נספח בינוי

תכנית מס' 101-1377753

התחדשות עירונית
הפלמ"ח 49, 51
והשיירות2

גיליון	1	מתוך	1
תחולה	מנחה		
תיאור	נספח בינוי		
תאריך עריכת הנספח			
קנ"מ	As indicated		

תרשימים נוספים	קנ"מ

מקרא

- גבול התכנית
- קו בניין
- קו בניין תחתי
- מסחר
- מגורים
- ציבורי

עורך ראשי	שם: ארז קלפר ת"ז: 065679078

KLAPPER ARCHITECTS

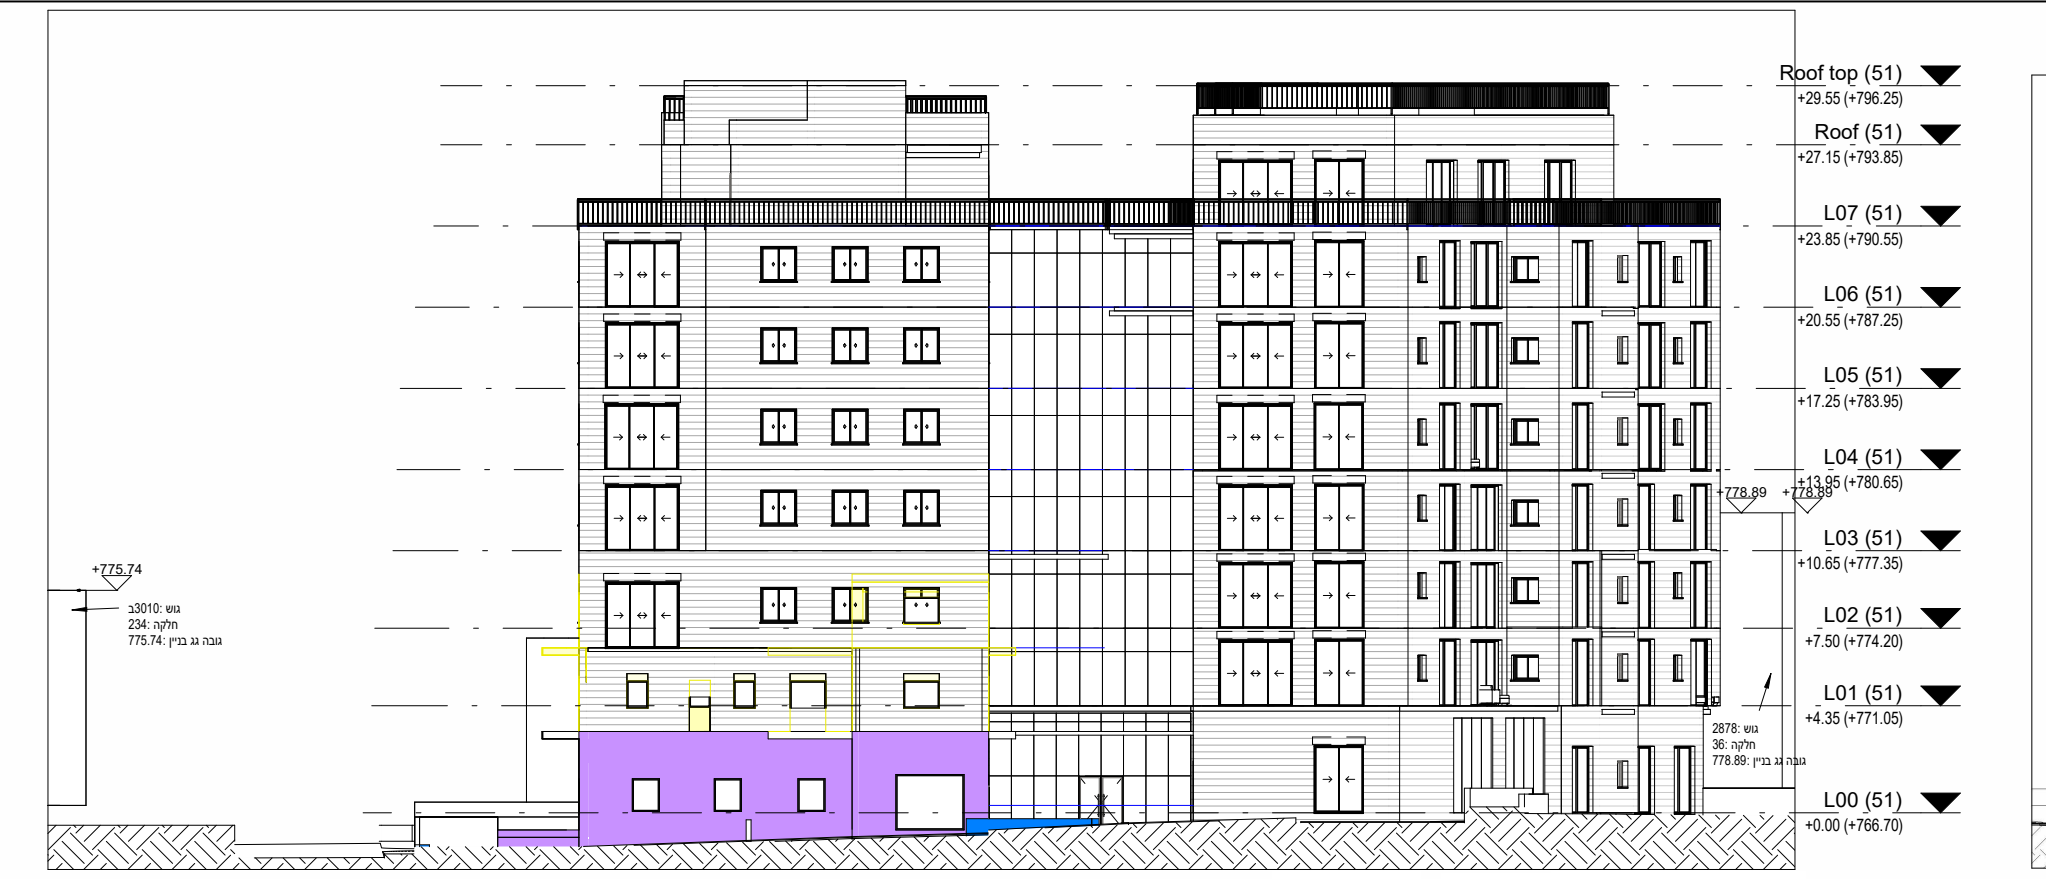
חזית צפונית2קנ"מ: 1 : 200

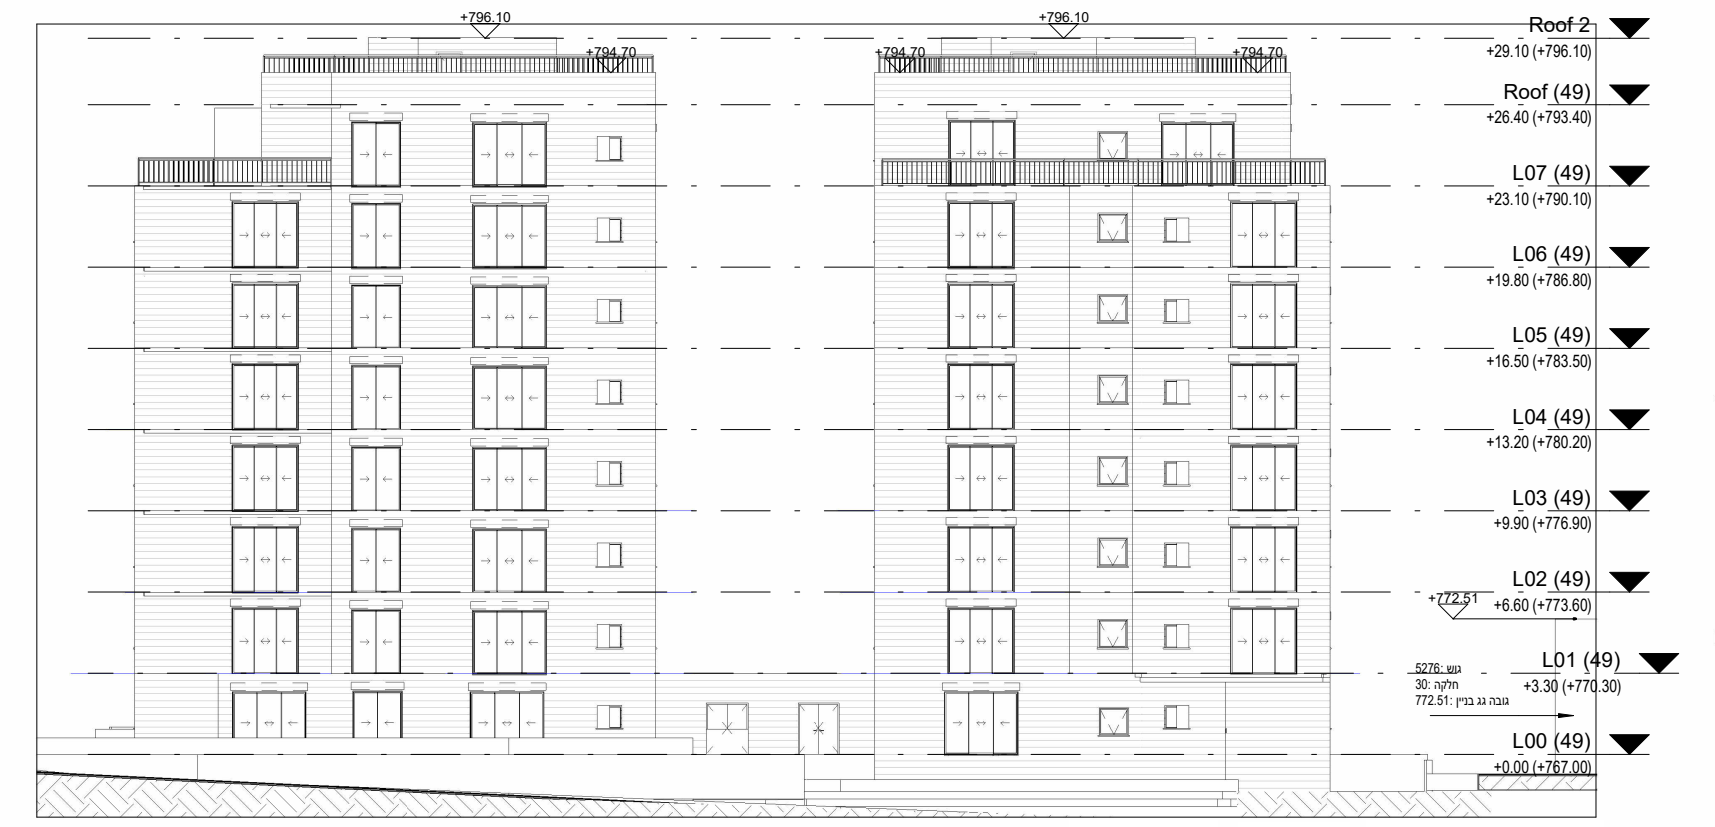
חזית דרומית קנ"מ: 1 : 200

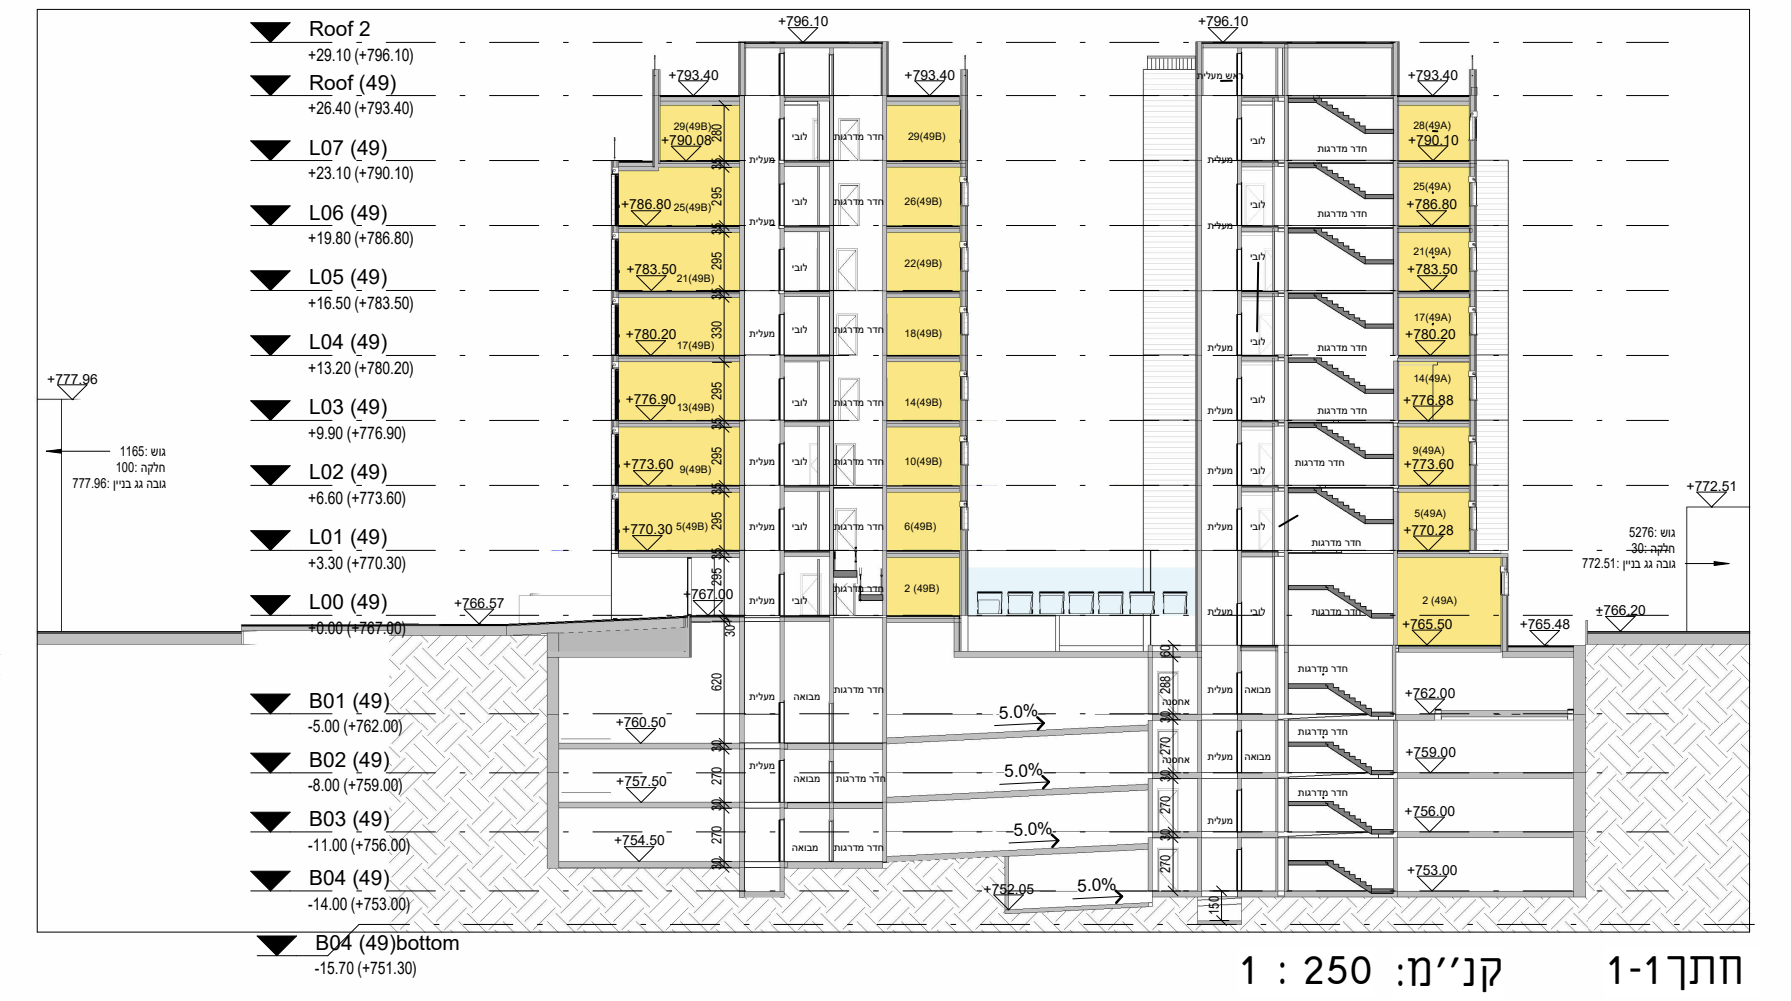
חתך1-1 קנ"מ: 1 : 250

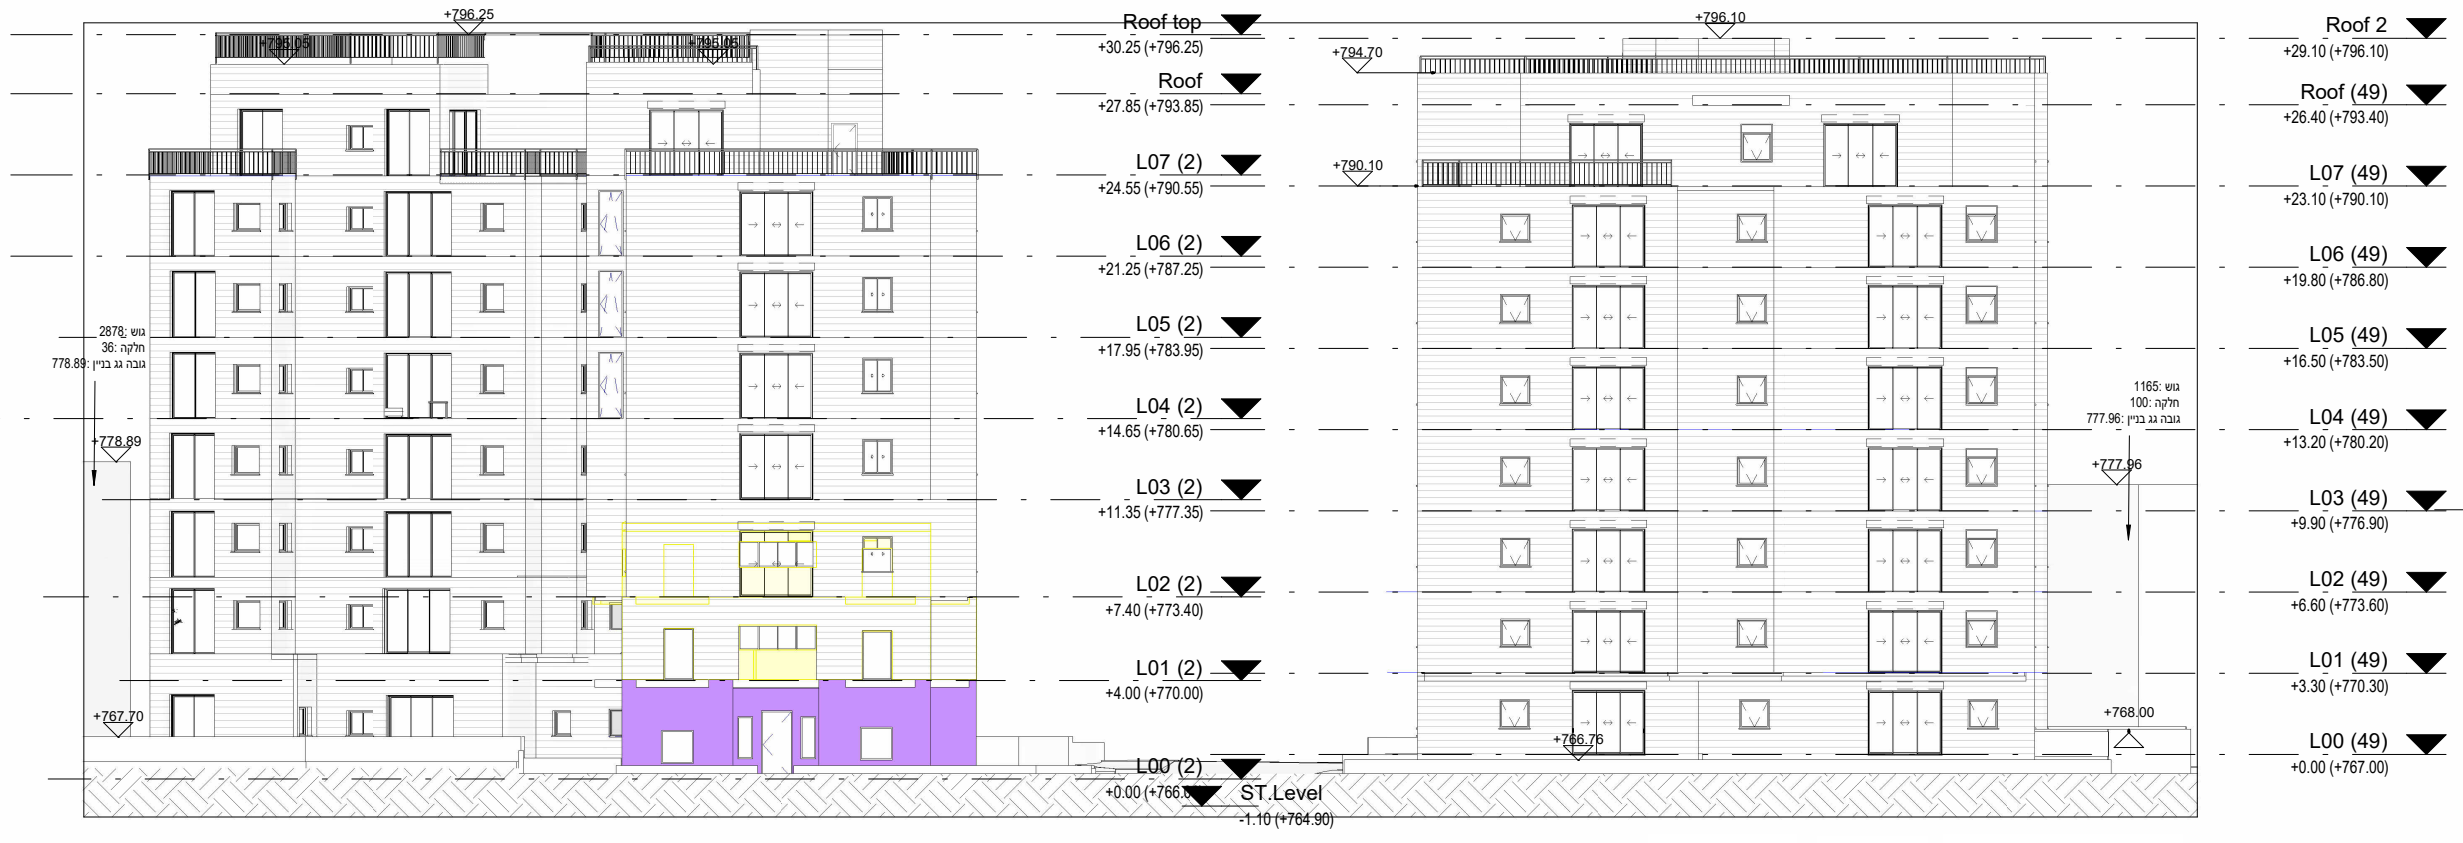
חזית מזרחית קנ"מ: 1 : 200

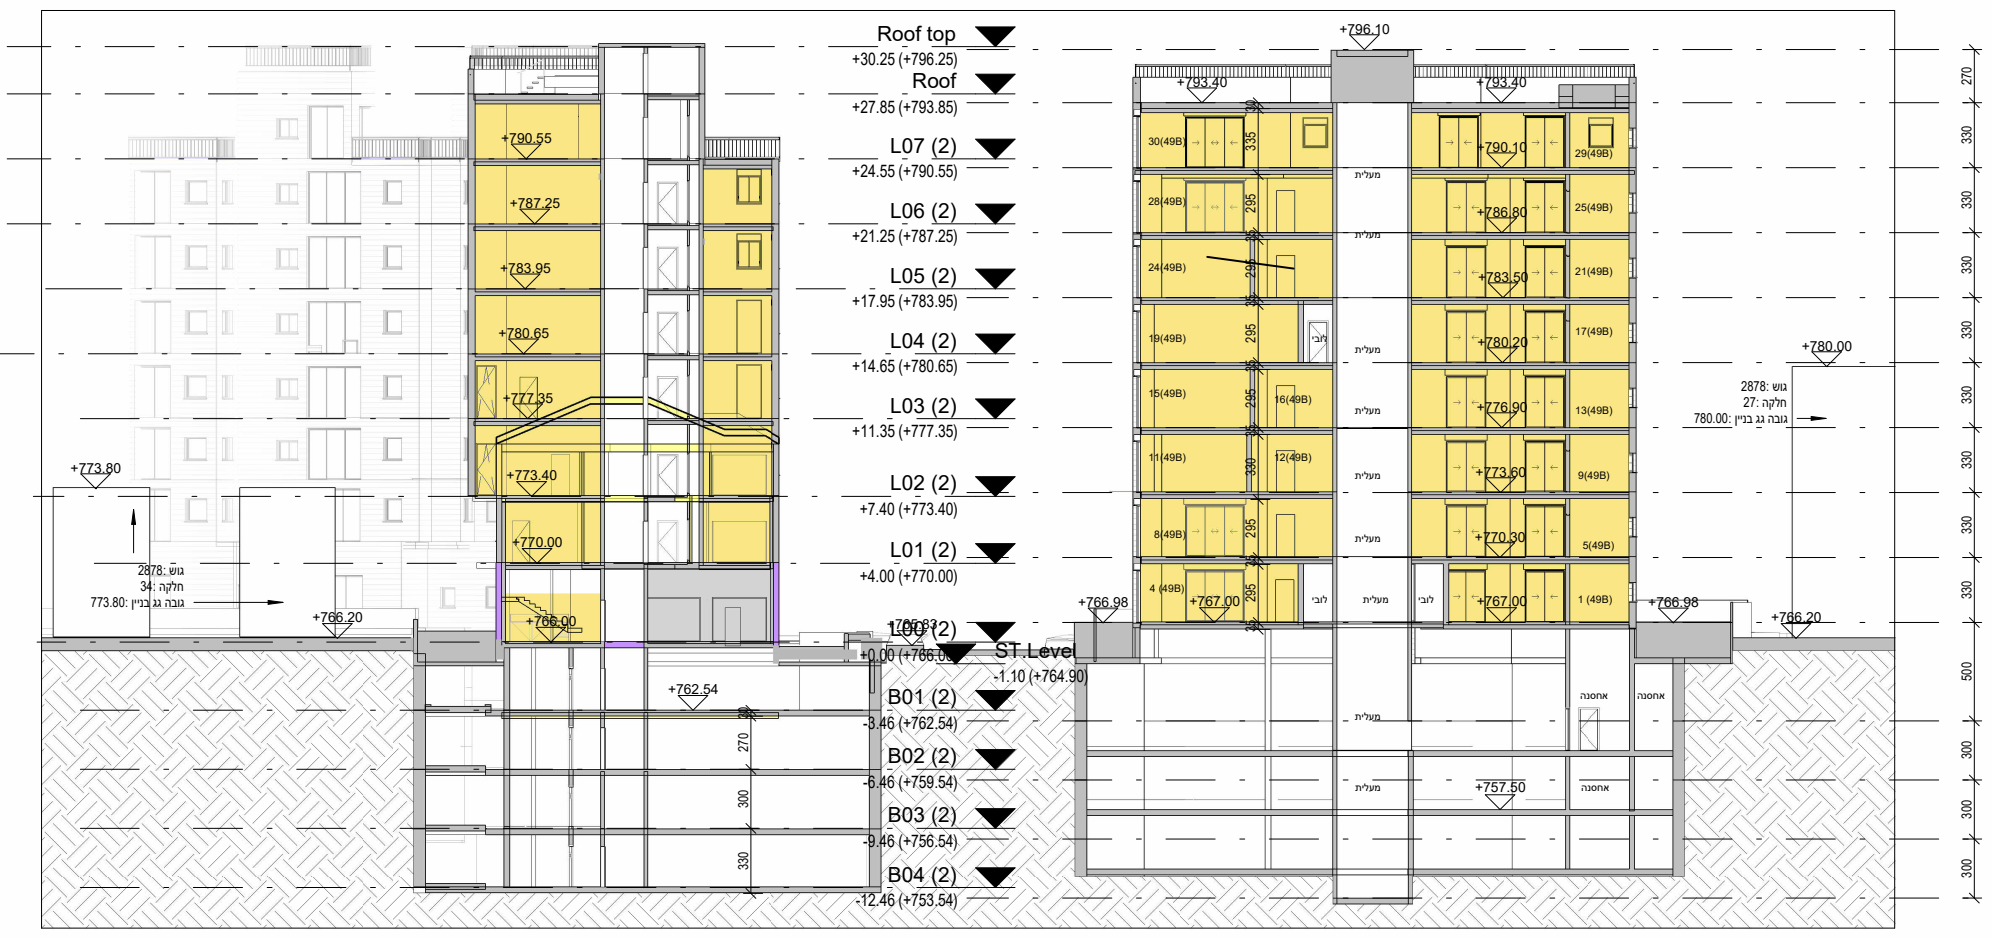
חתך2-2 קנ"מ: 1 : 250

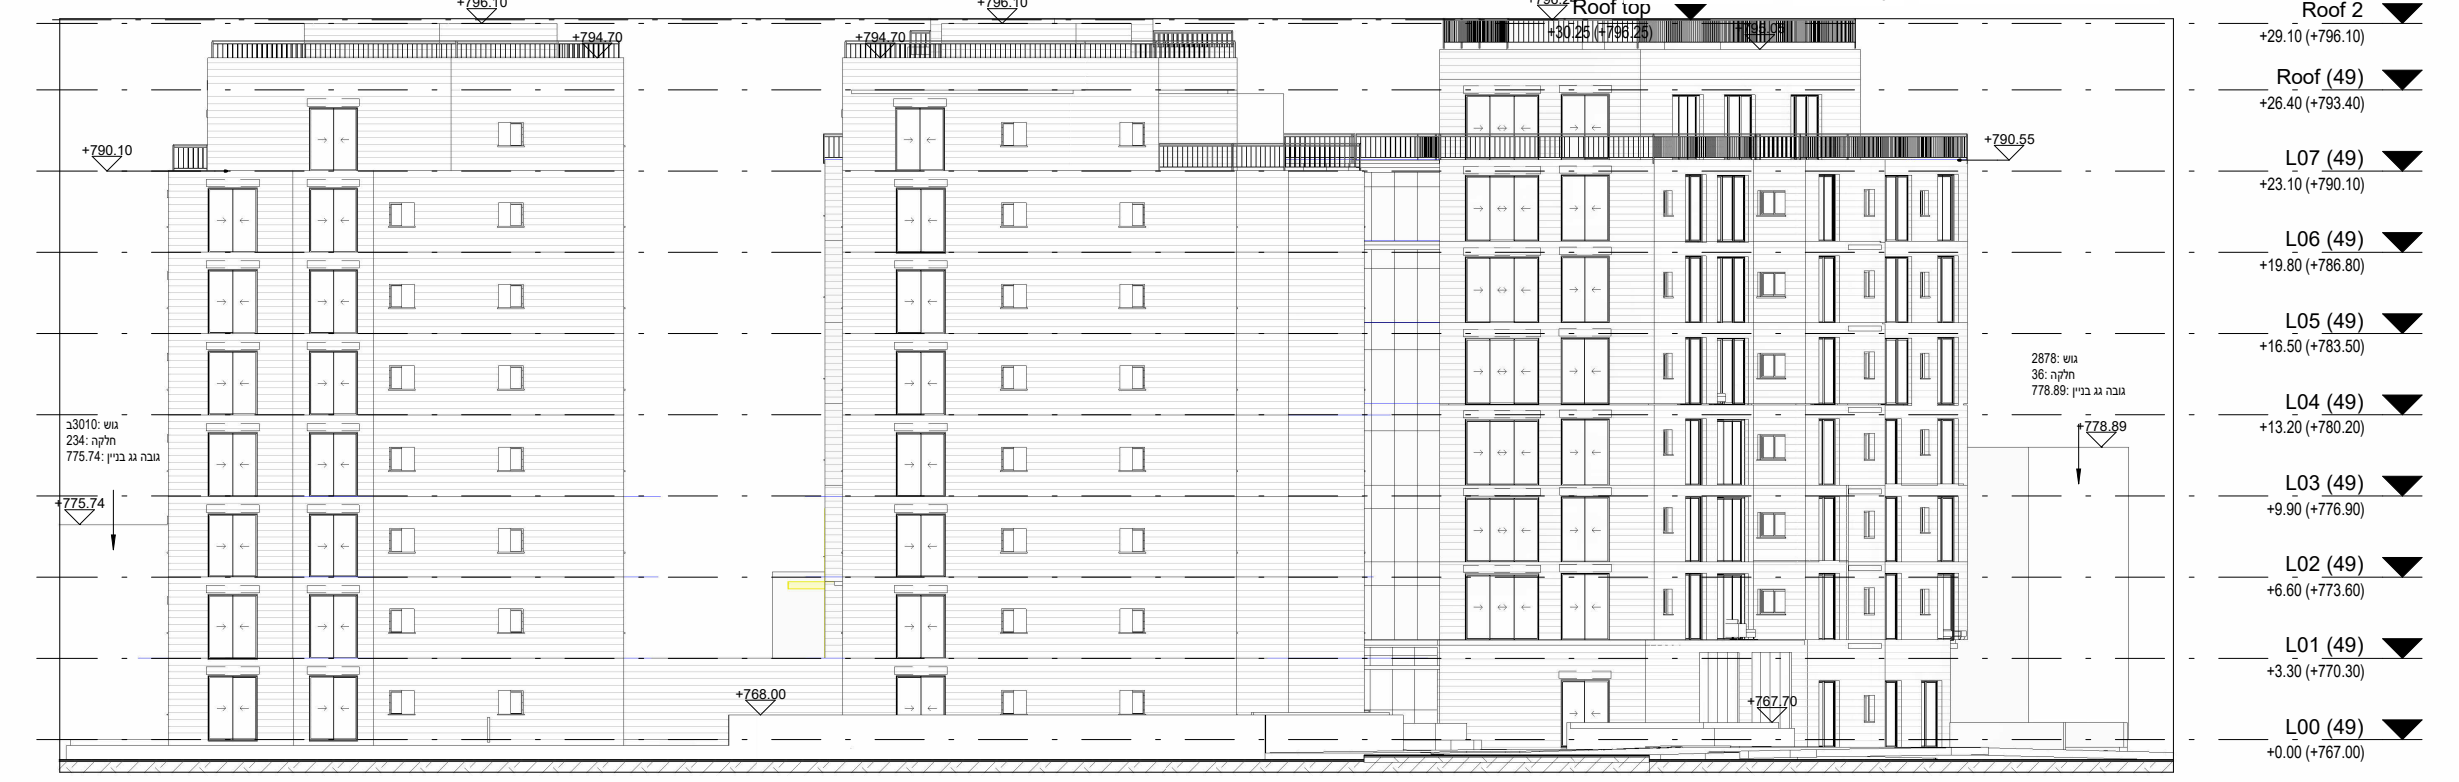
חזית צפונית קנ"מ: 1 : 200

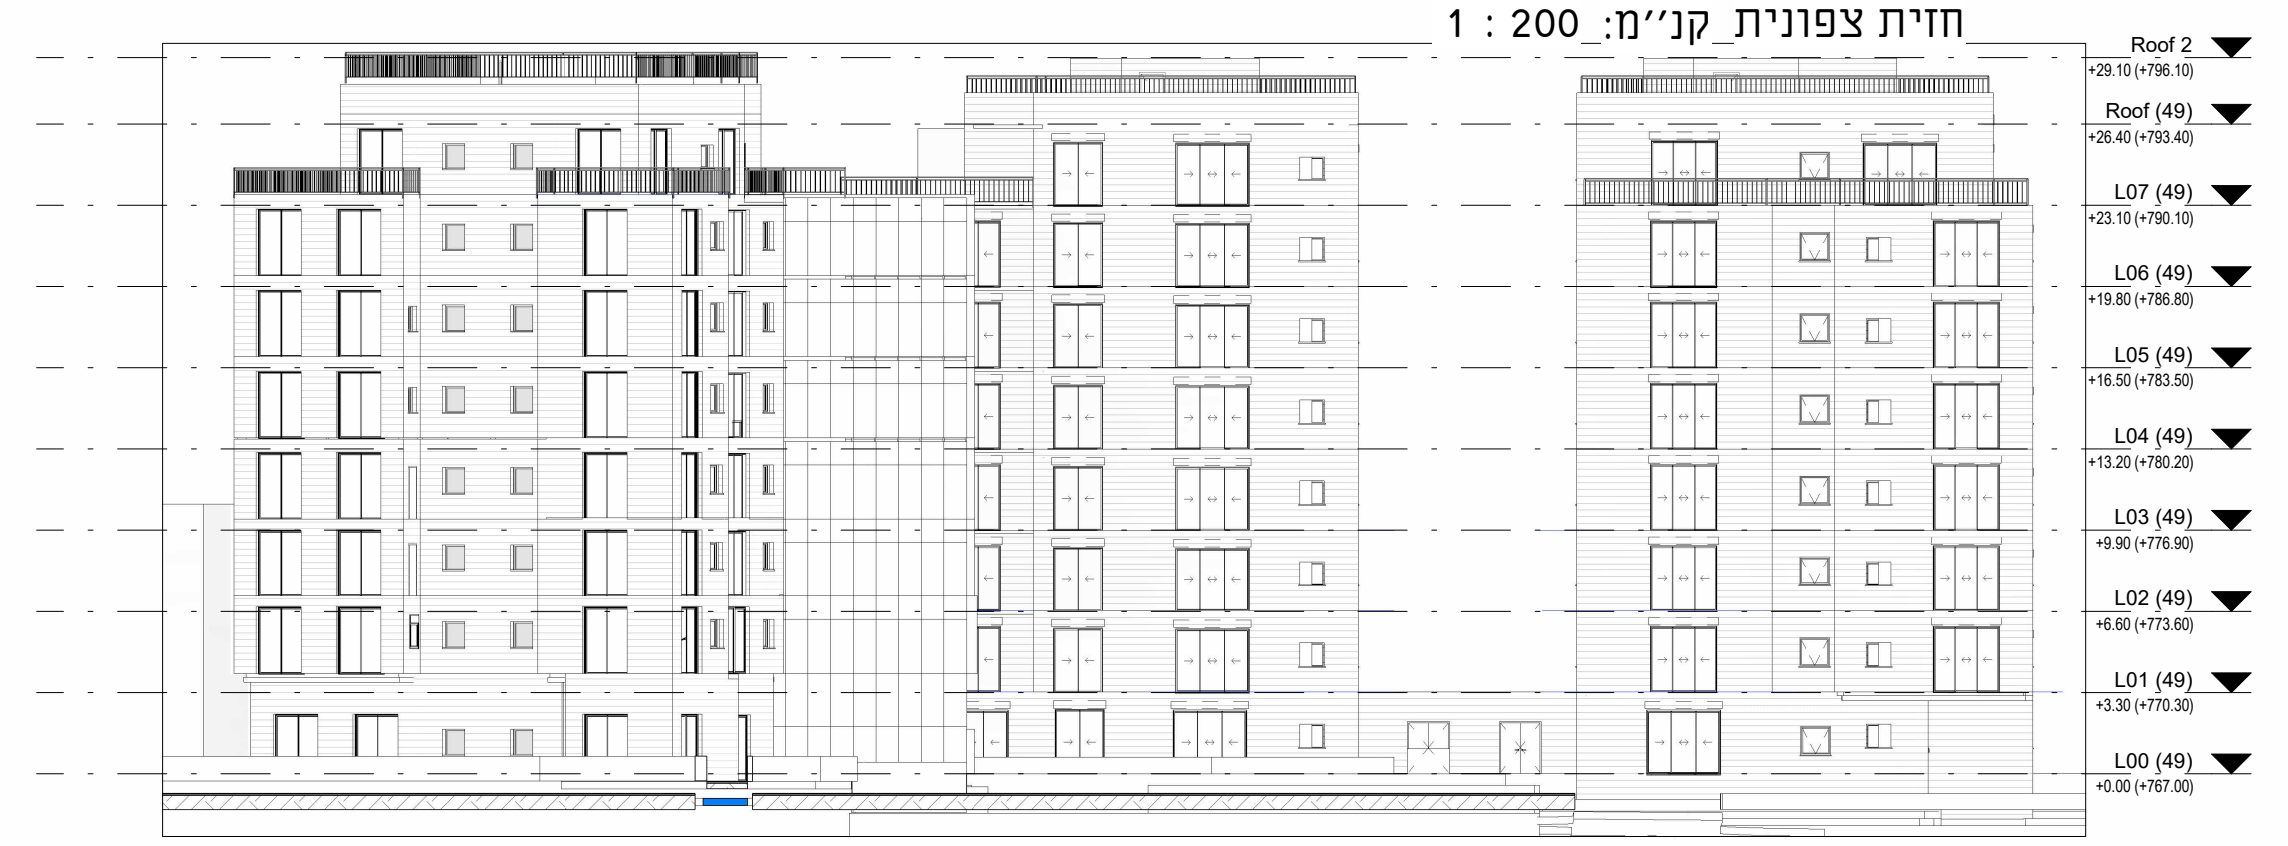
חזית דרומית2קנ"מ: 1 : 200

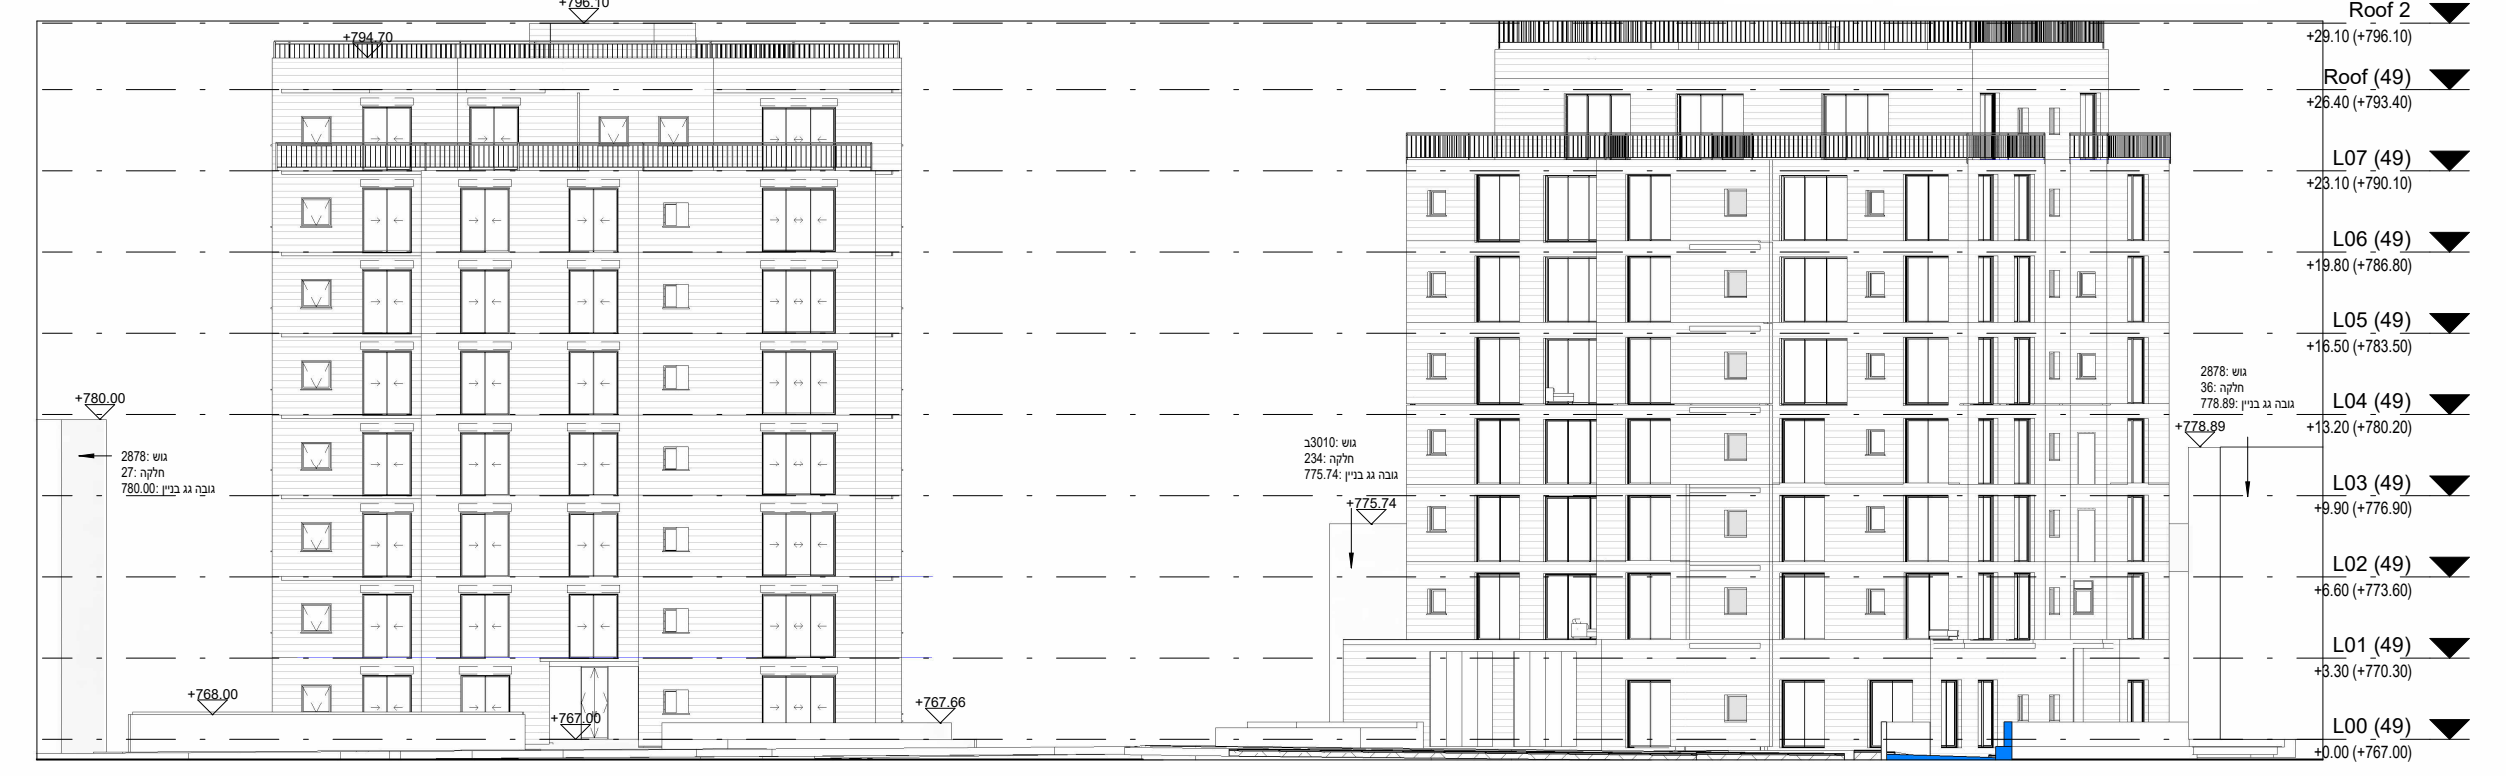

חזית מערביתקנ"מ: 1 : 200

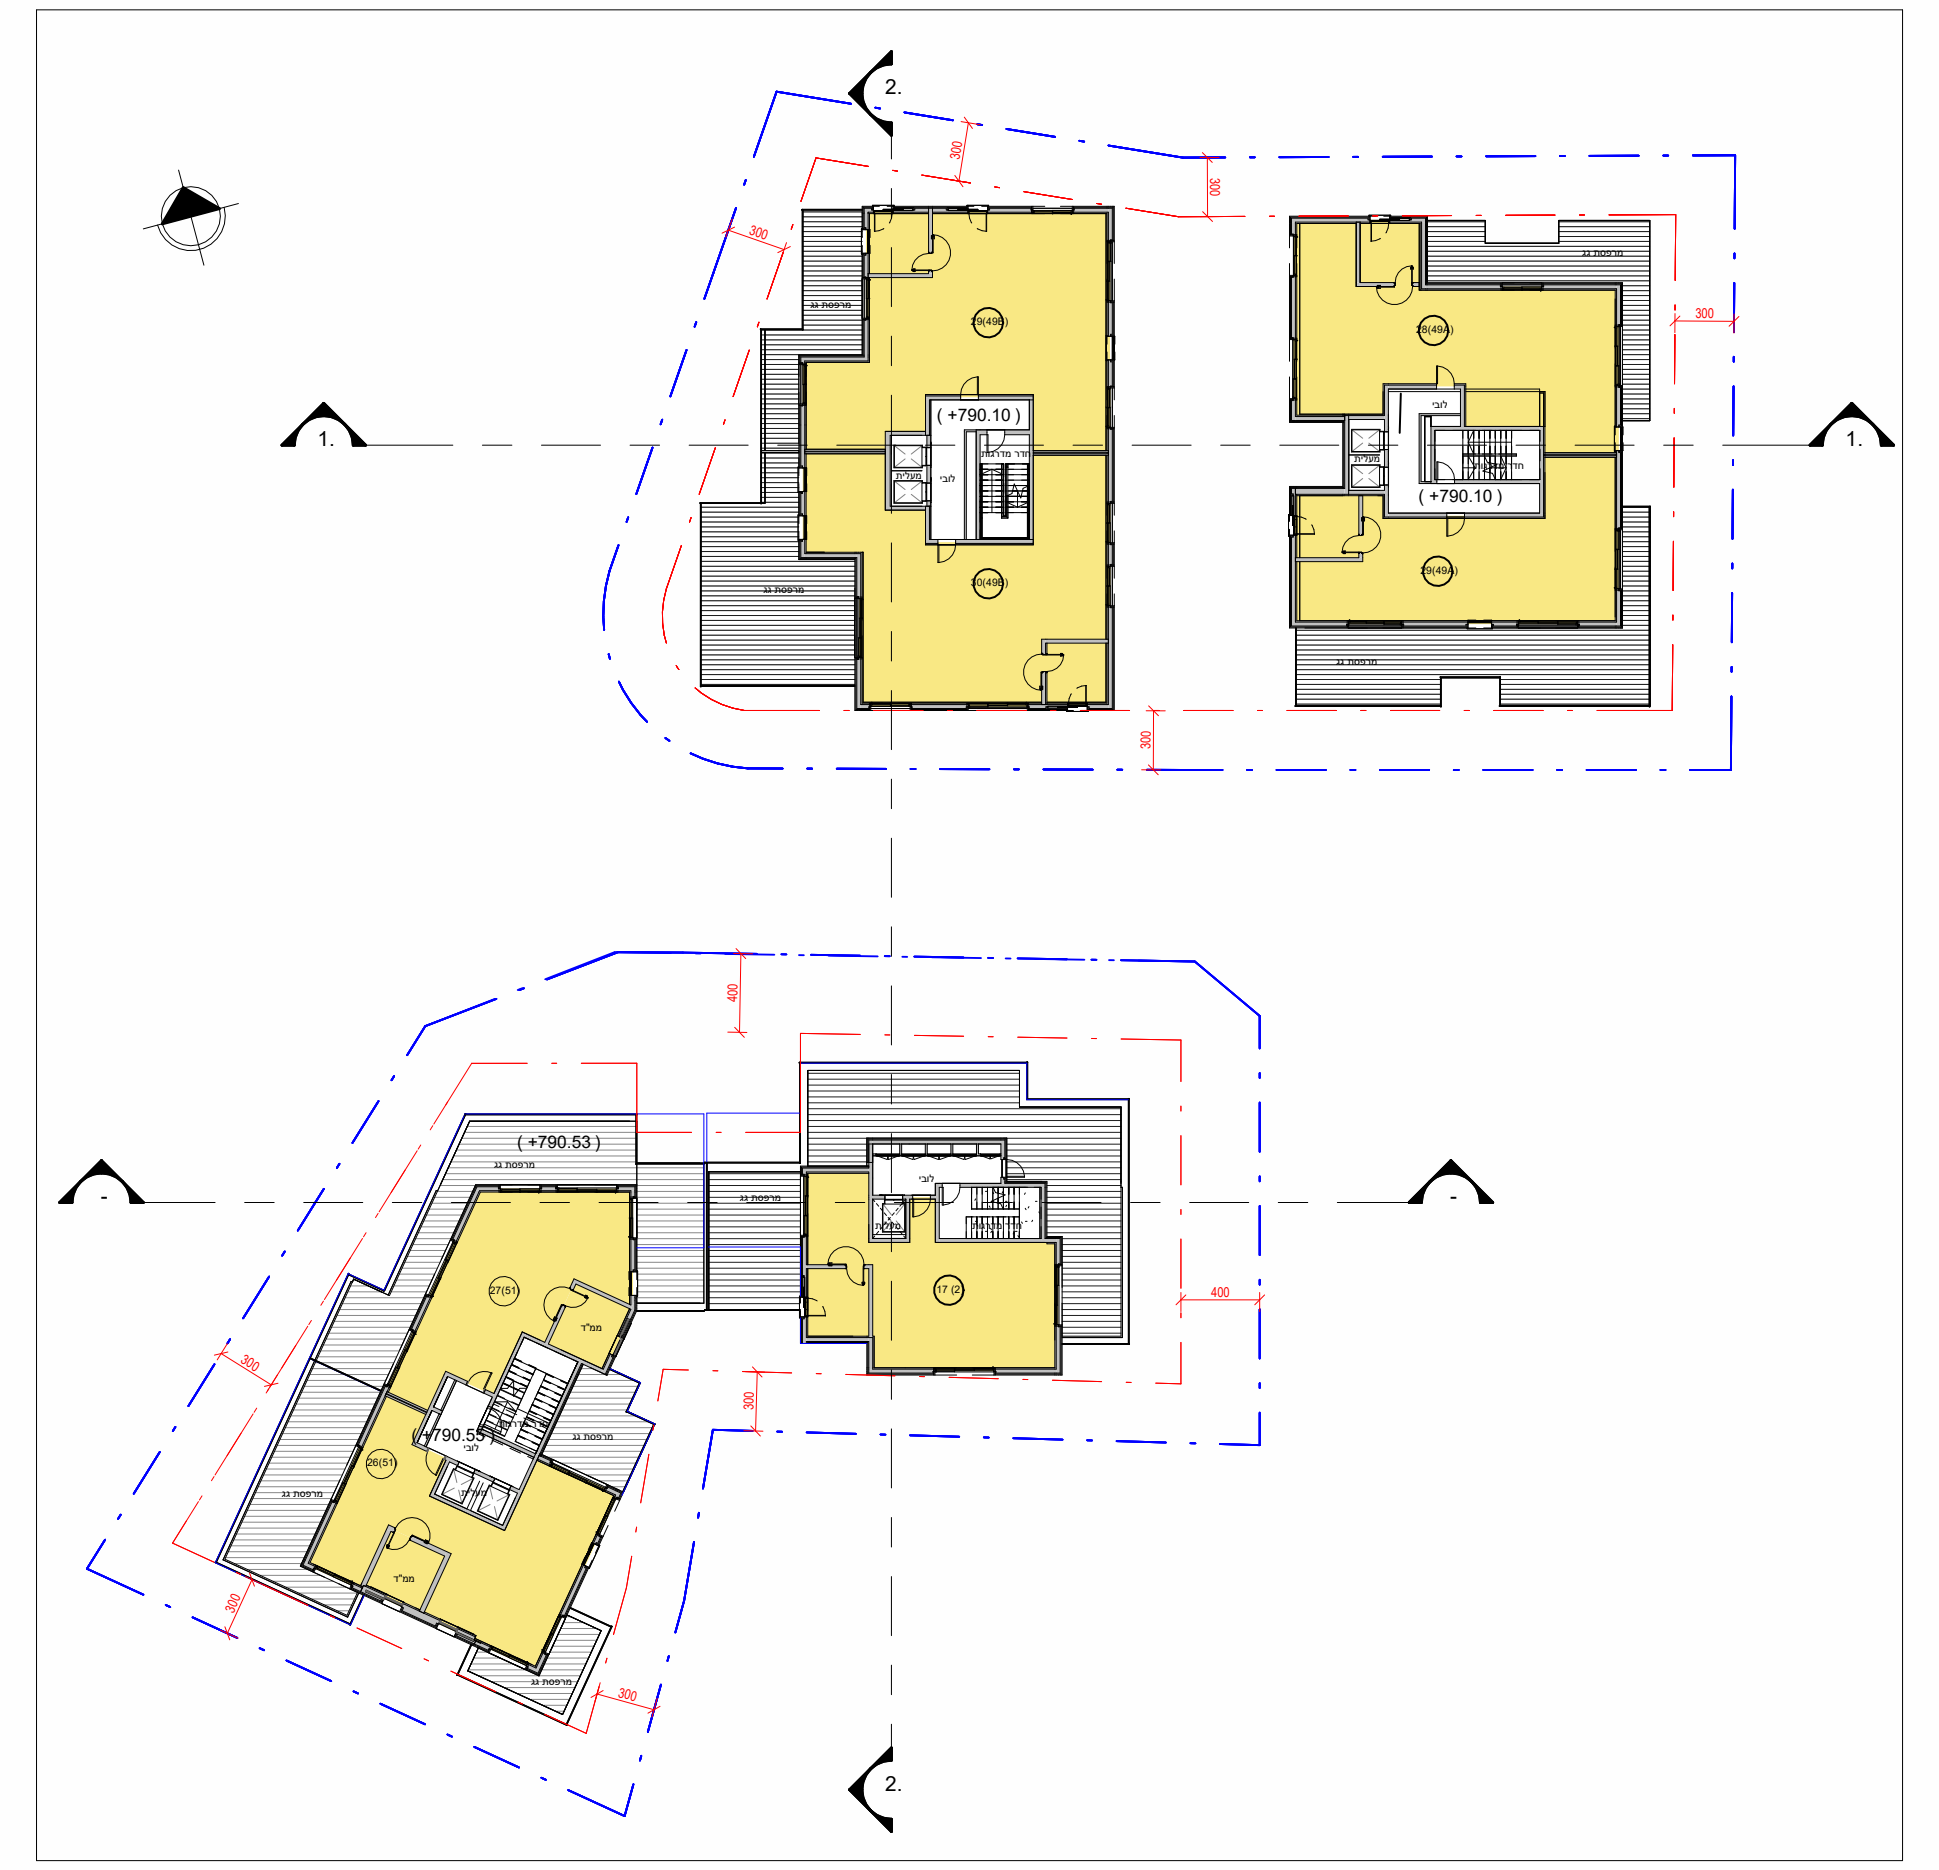
תכנית קומה7
מפלס:
קנ"מ: 1 : 250

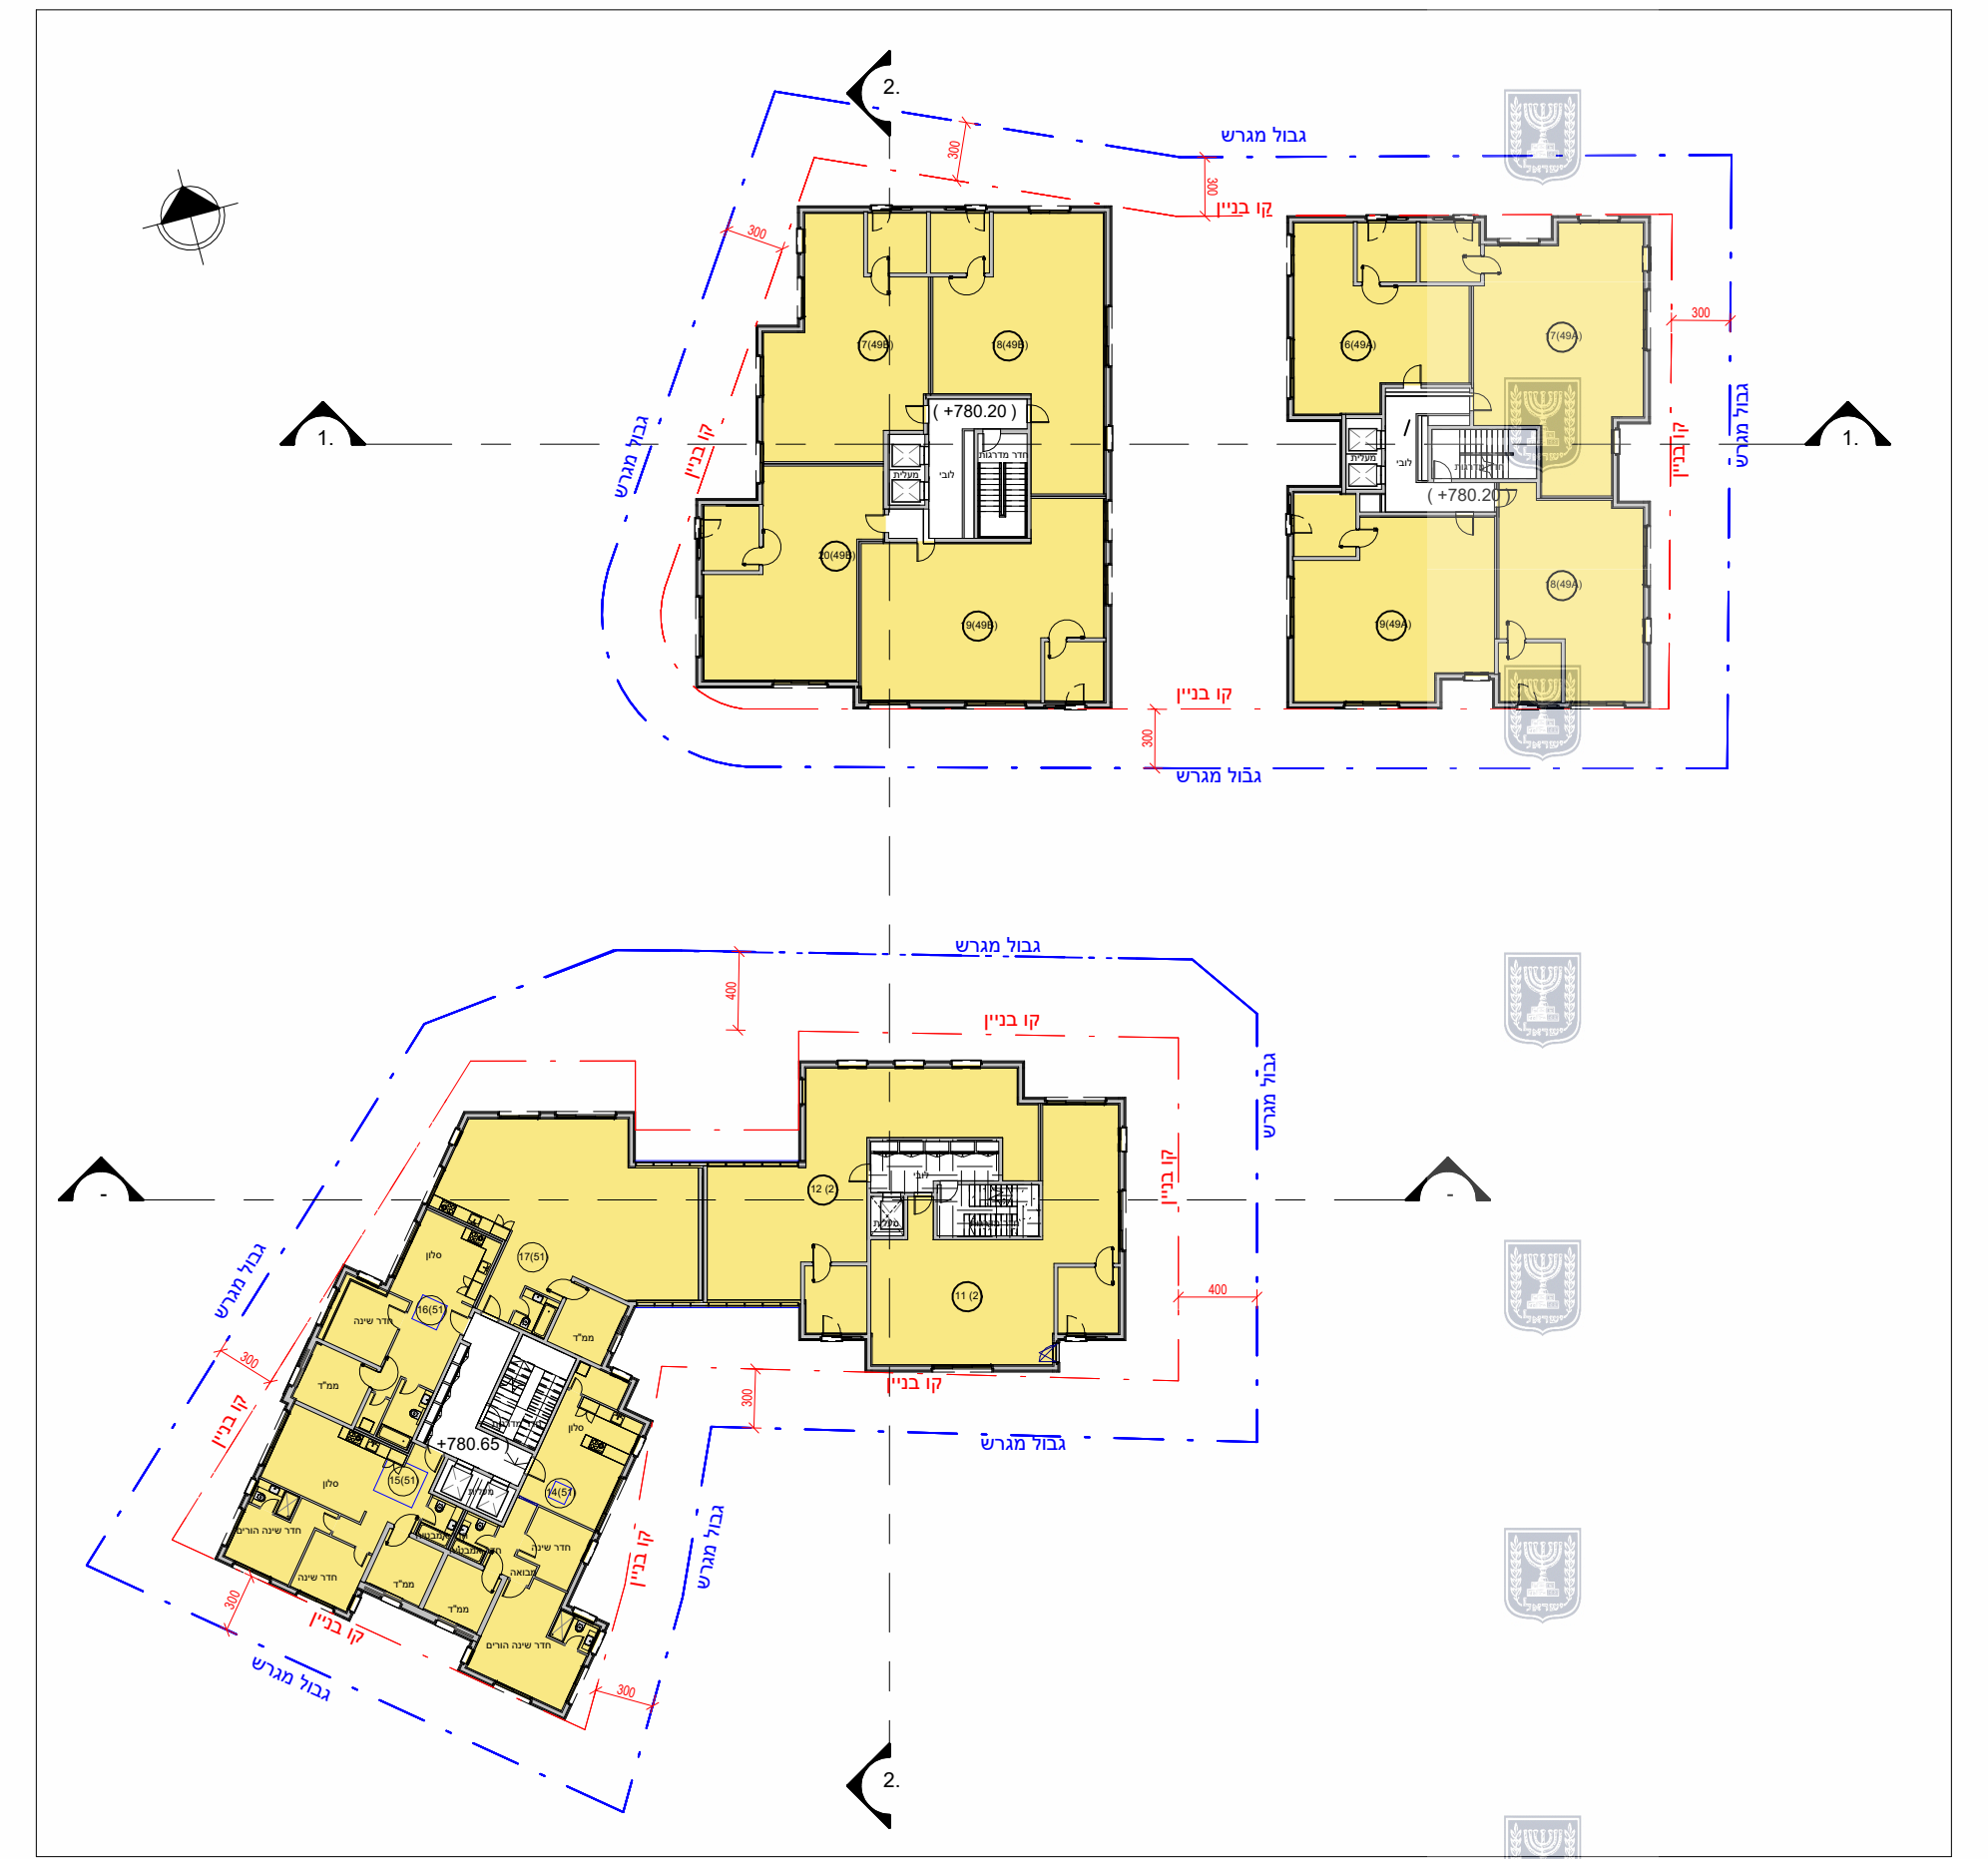
תכנית קומה4-5
מפלס:
קנ"מ: 1 : 250

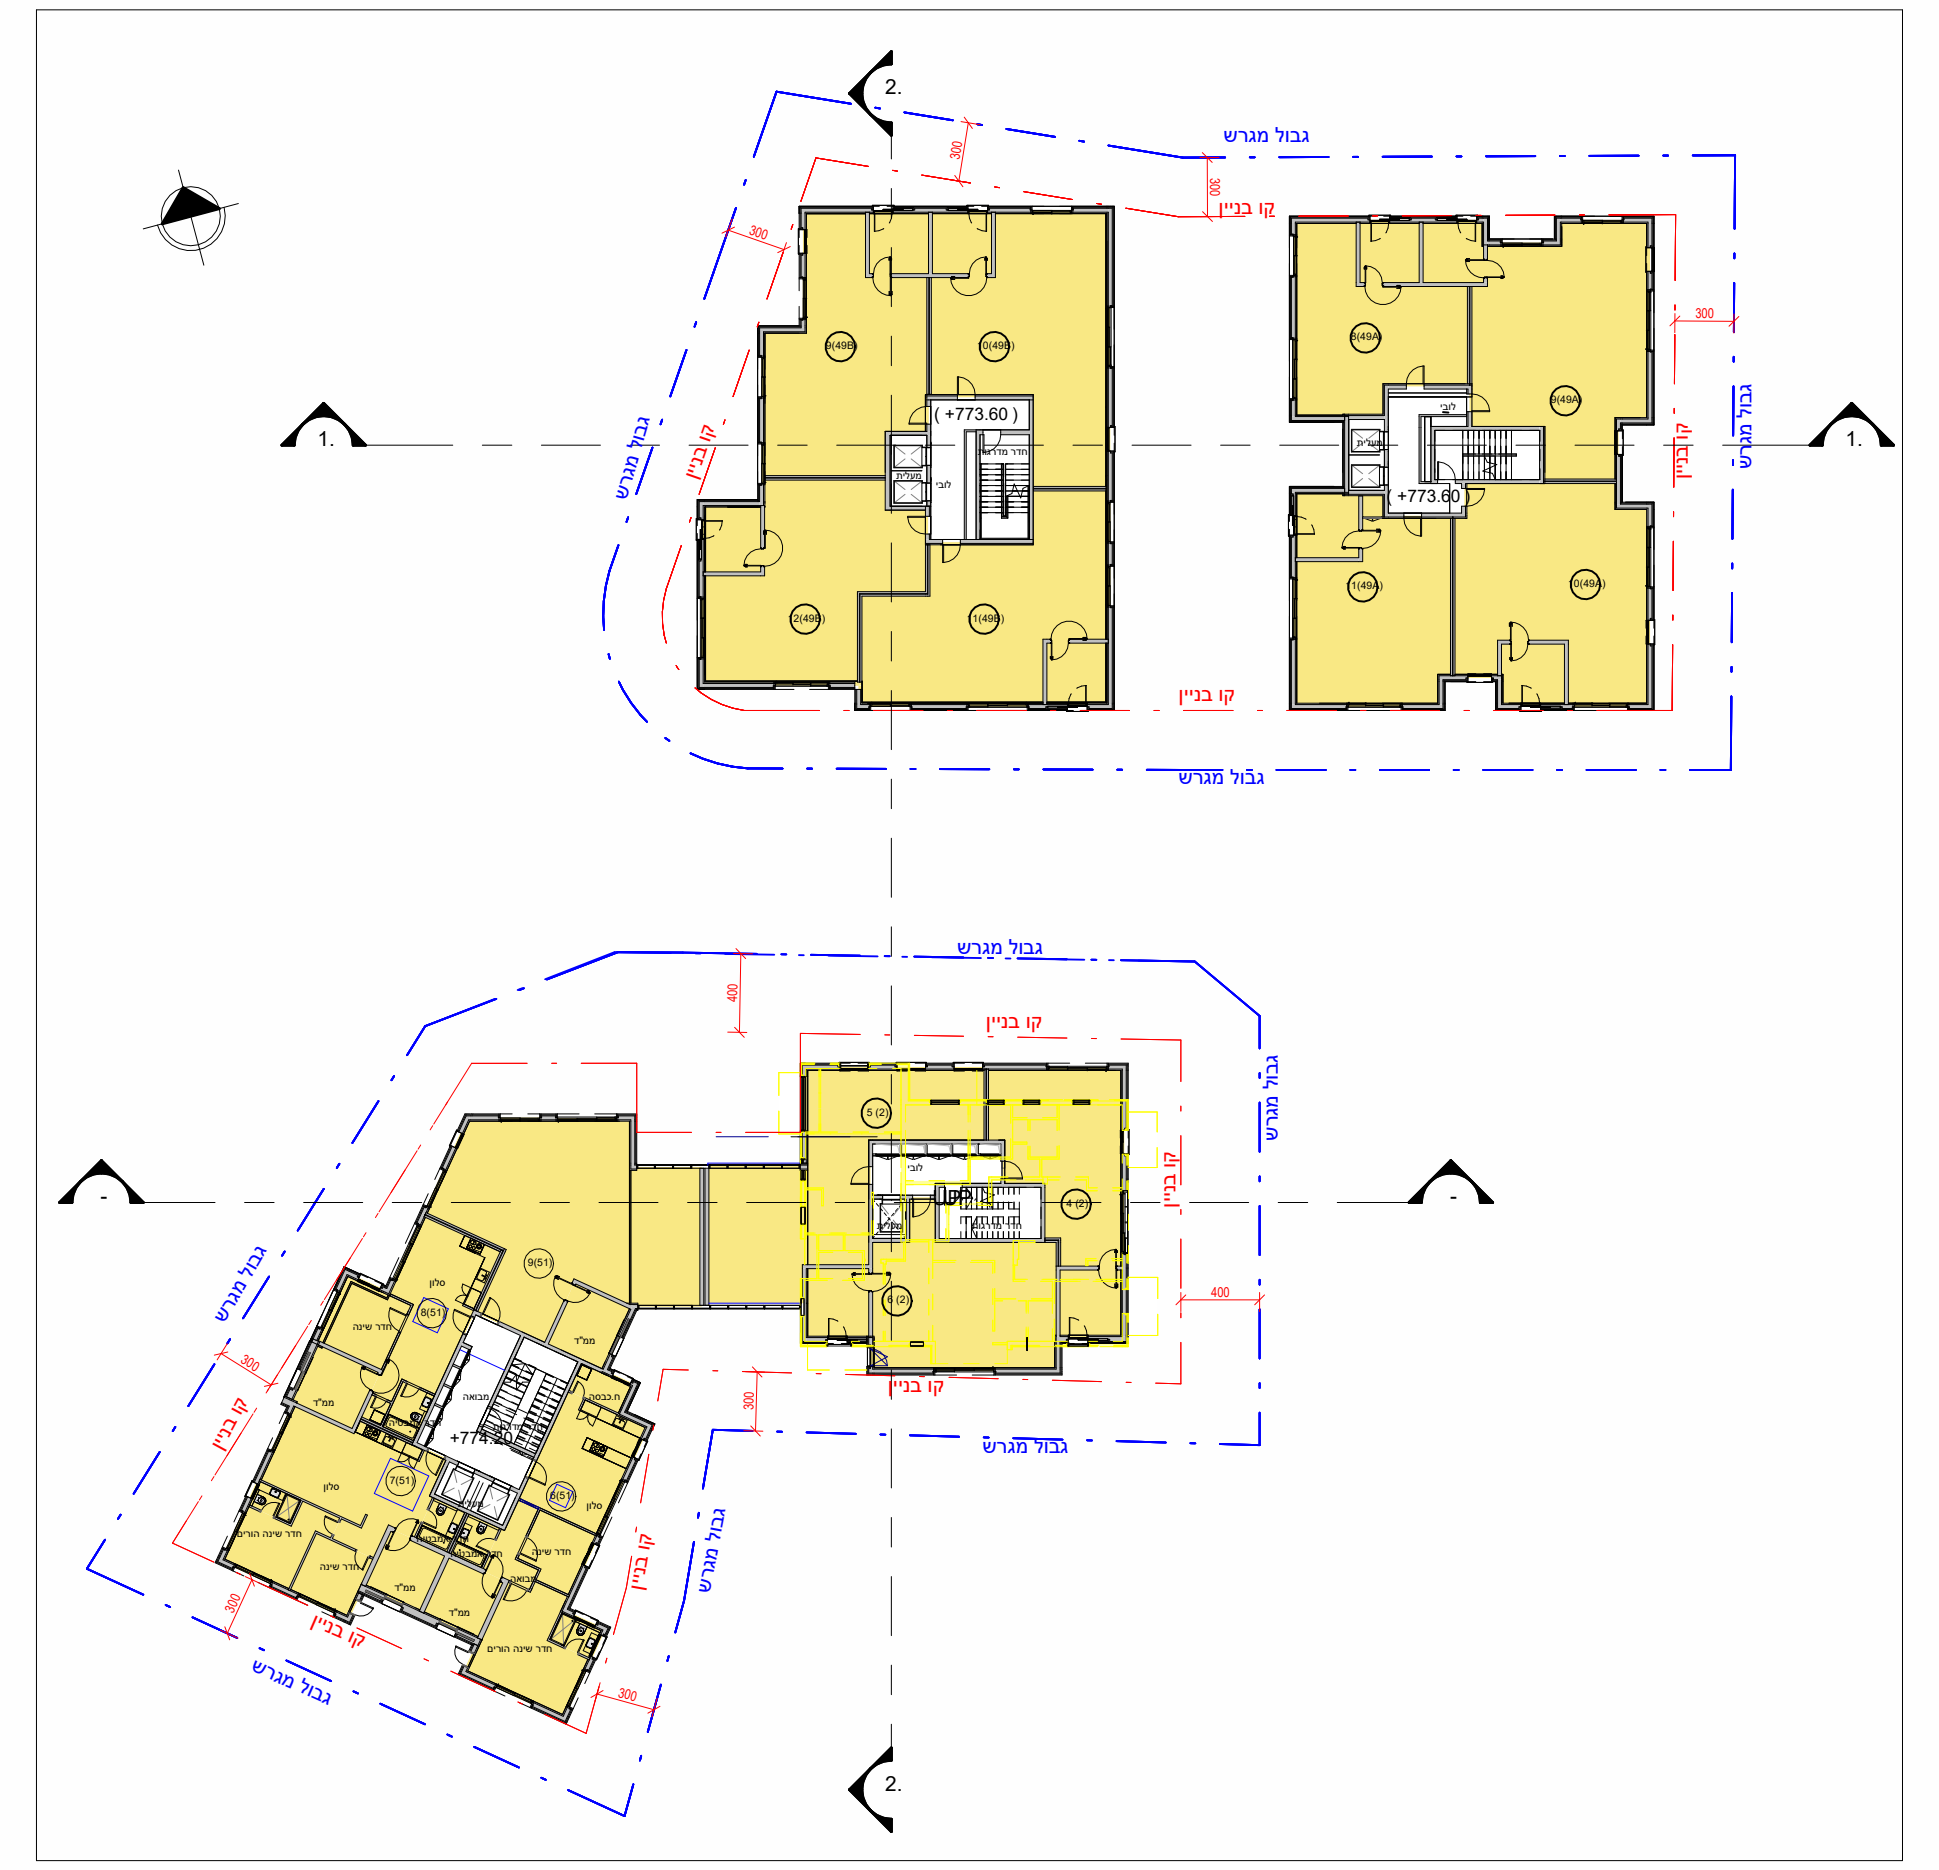
תכנית קומה2
מפלס:
קנ"מ: 1 : 250

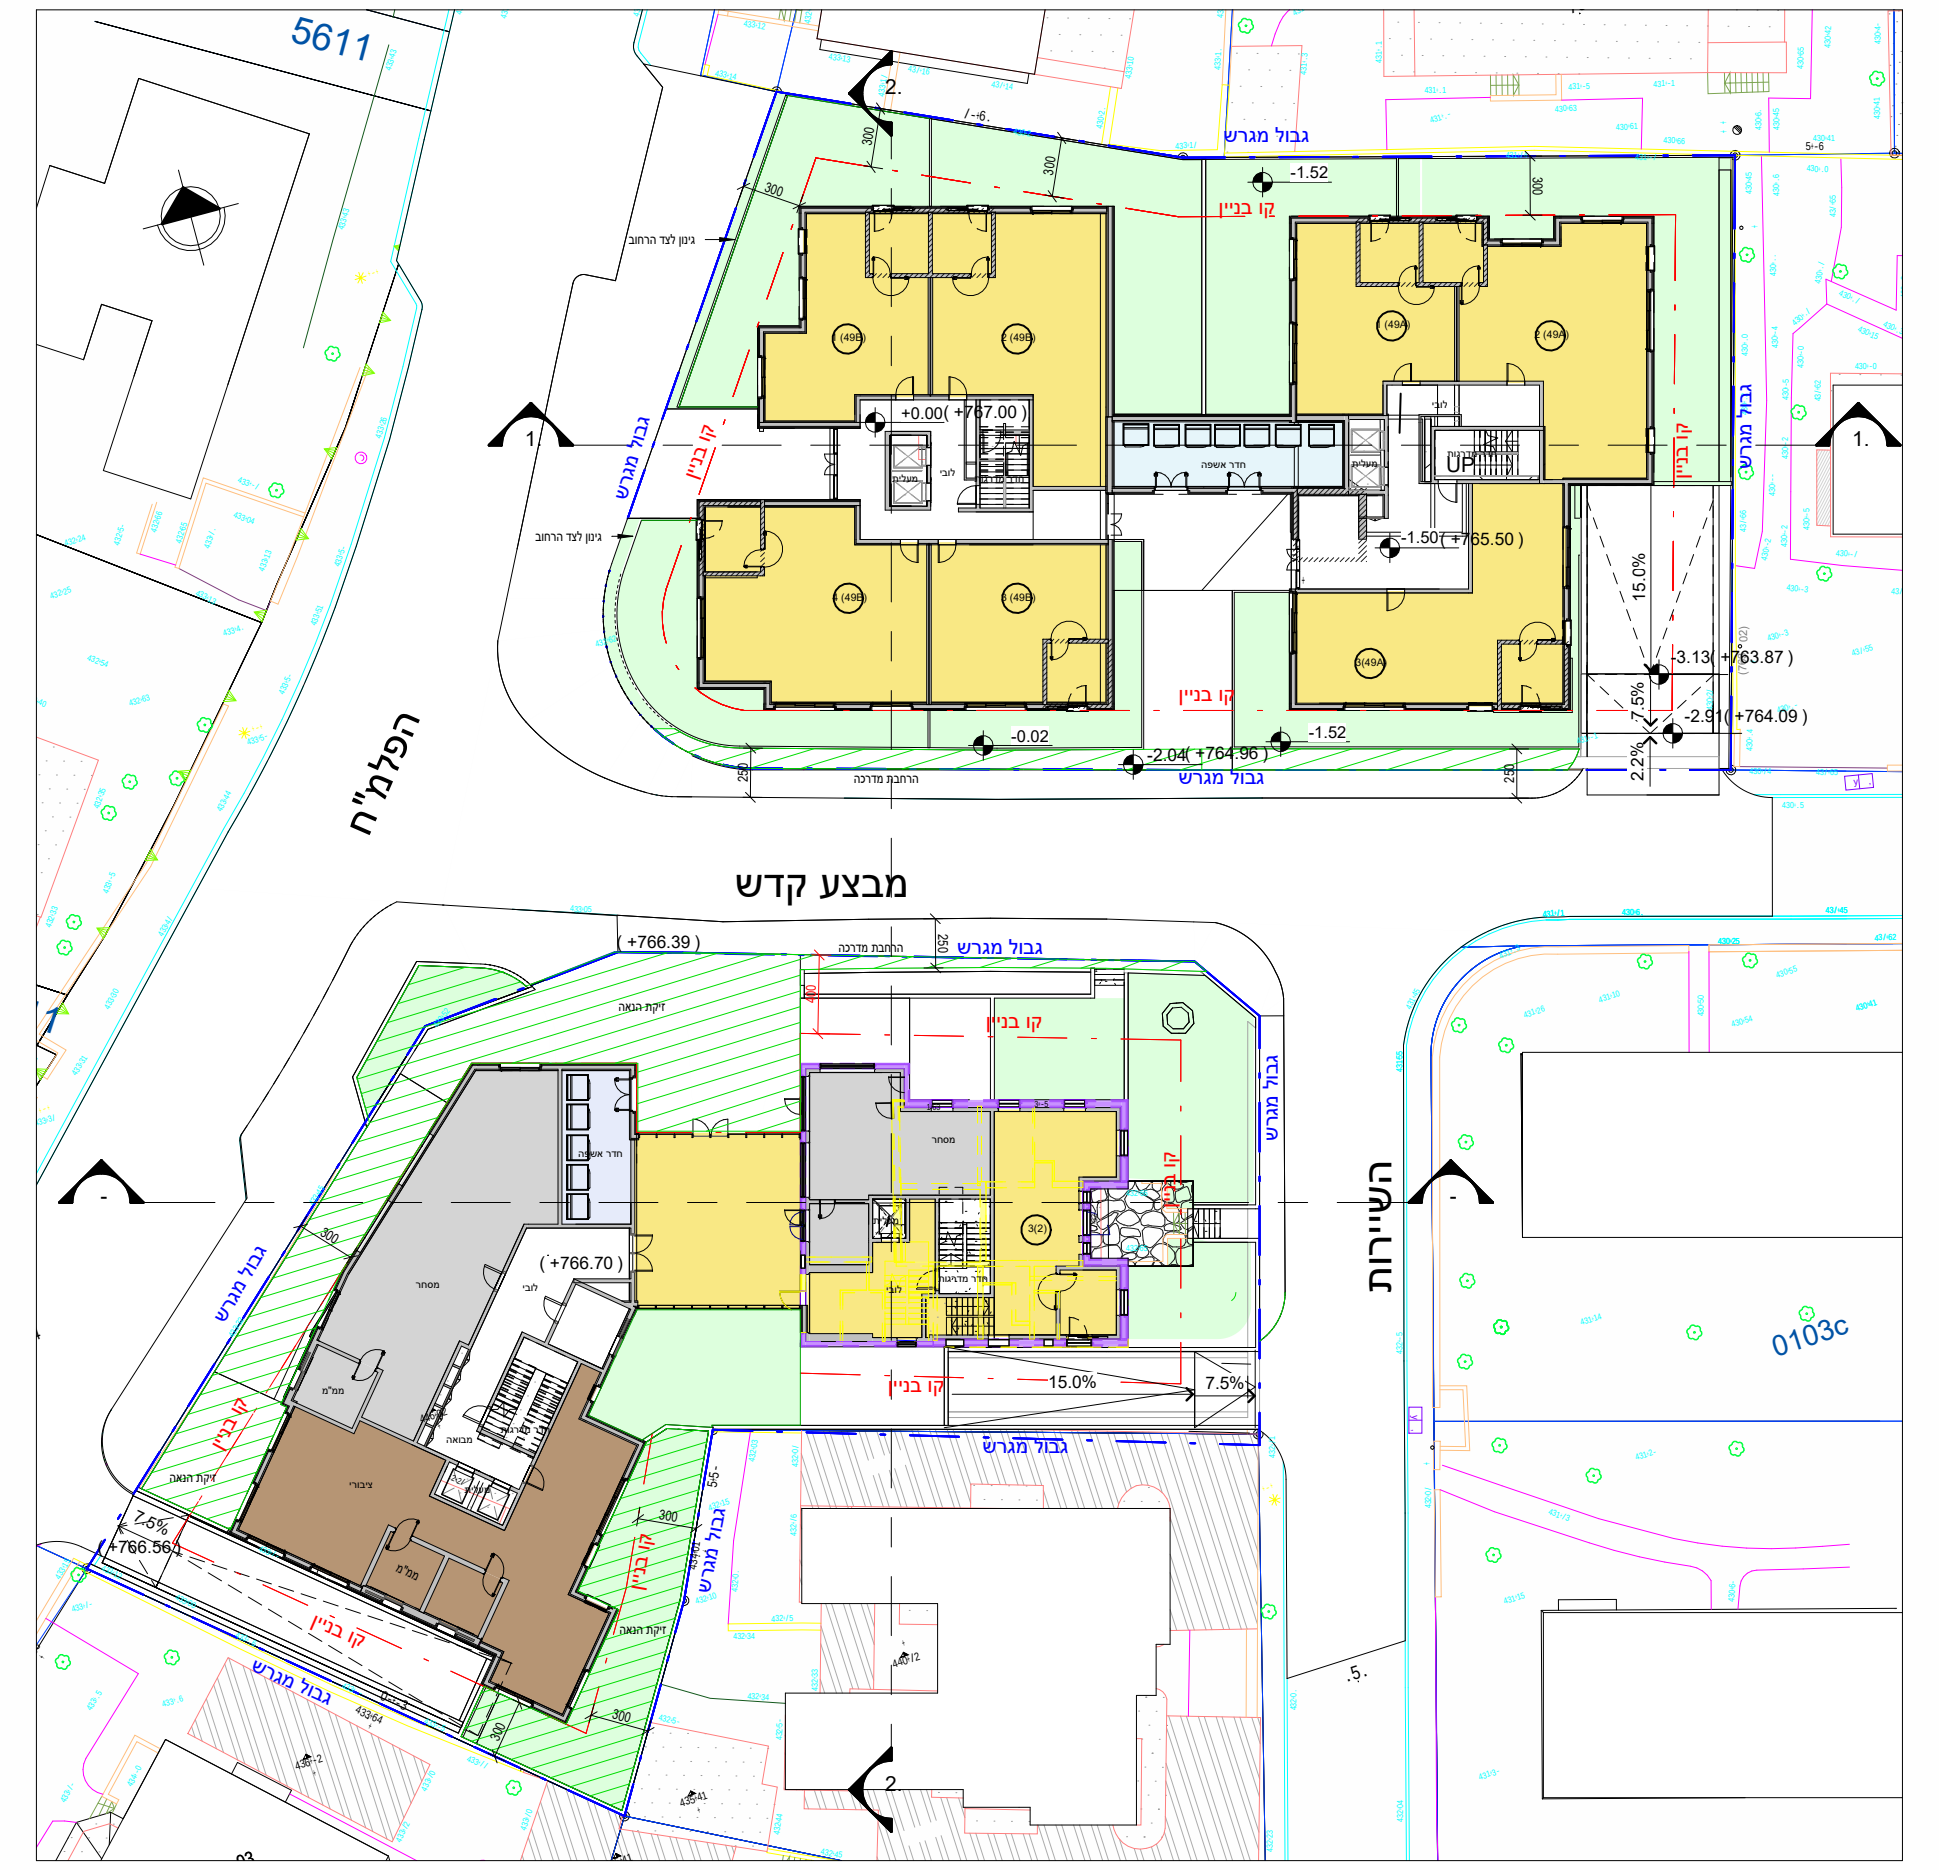
תכנית קומת קרקע
מפלס: +766.12, +766.70, +767.00
קנ"מ: 1 : 250

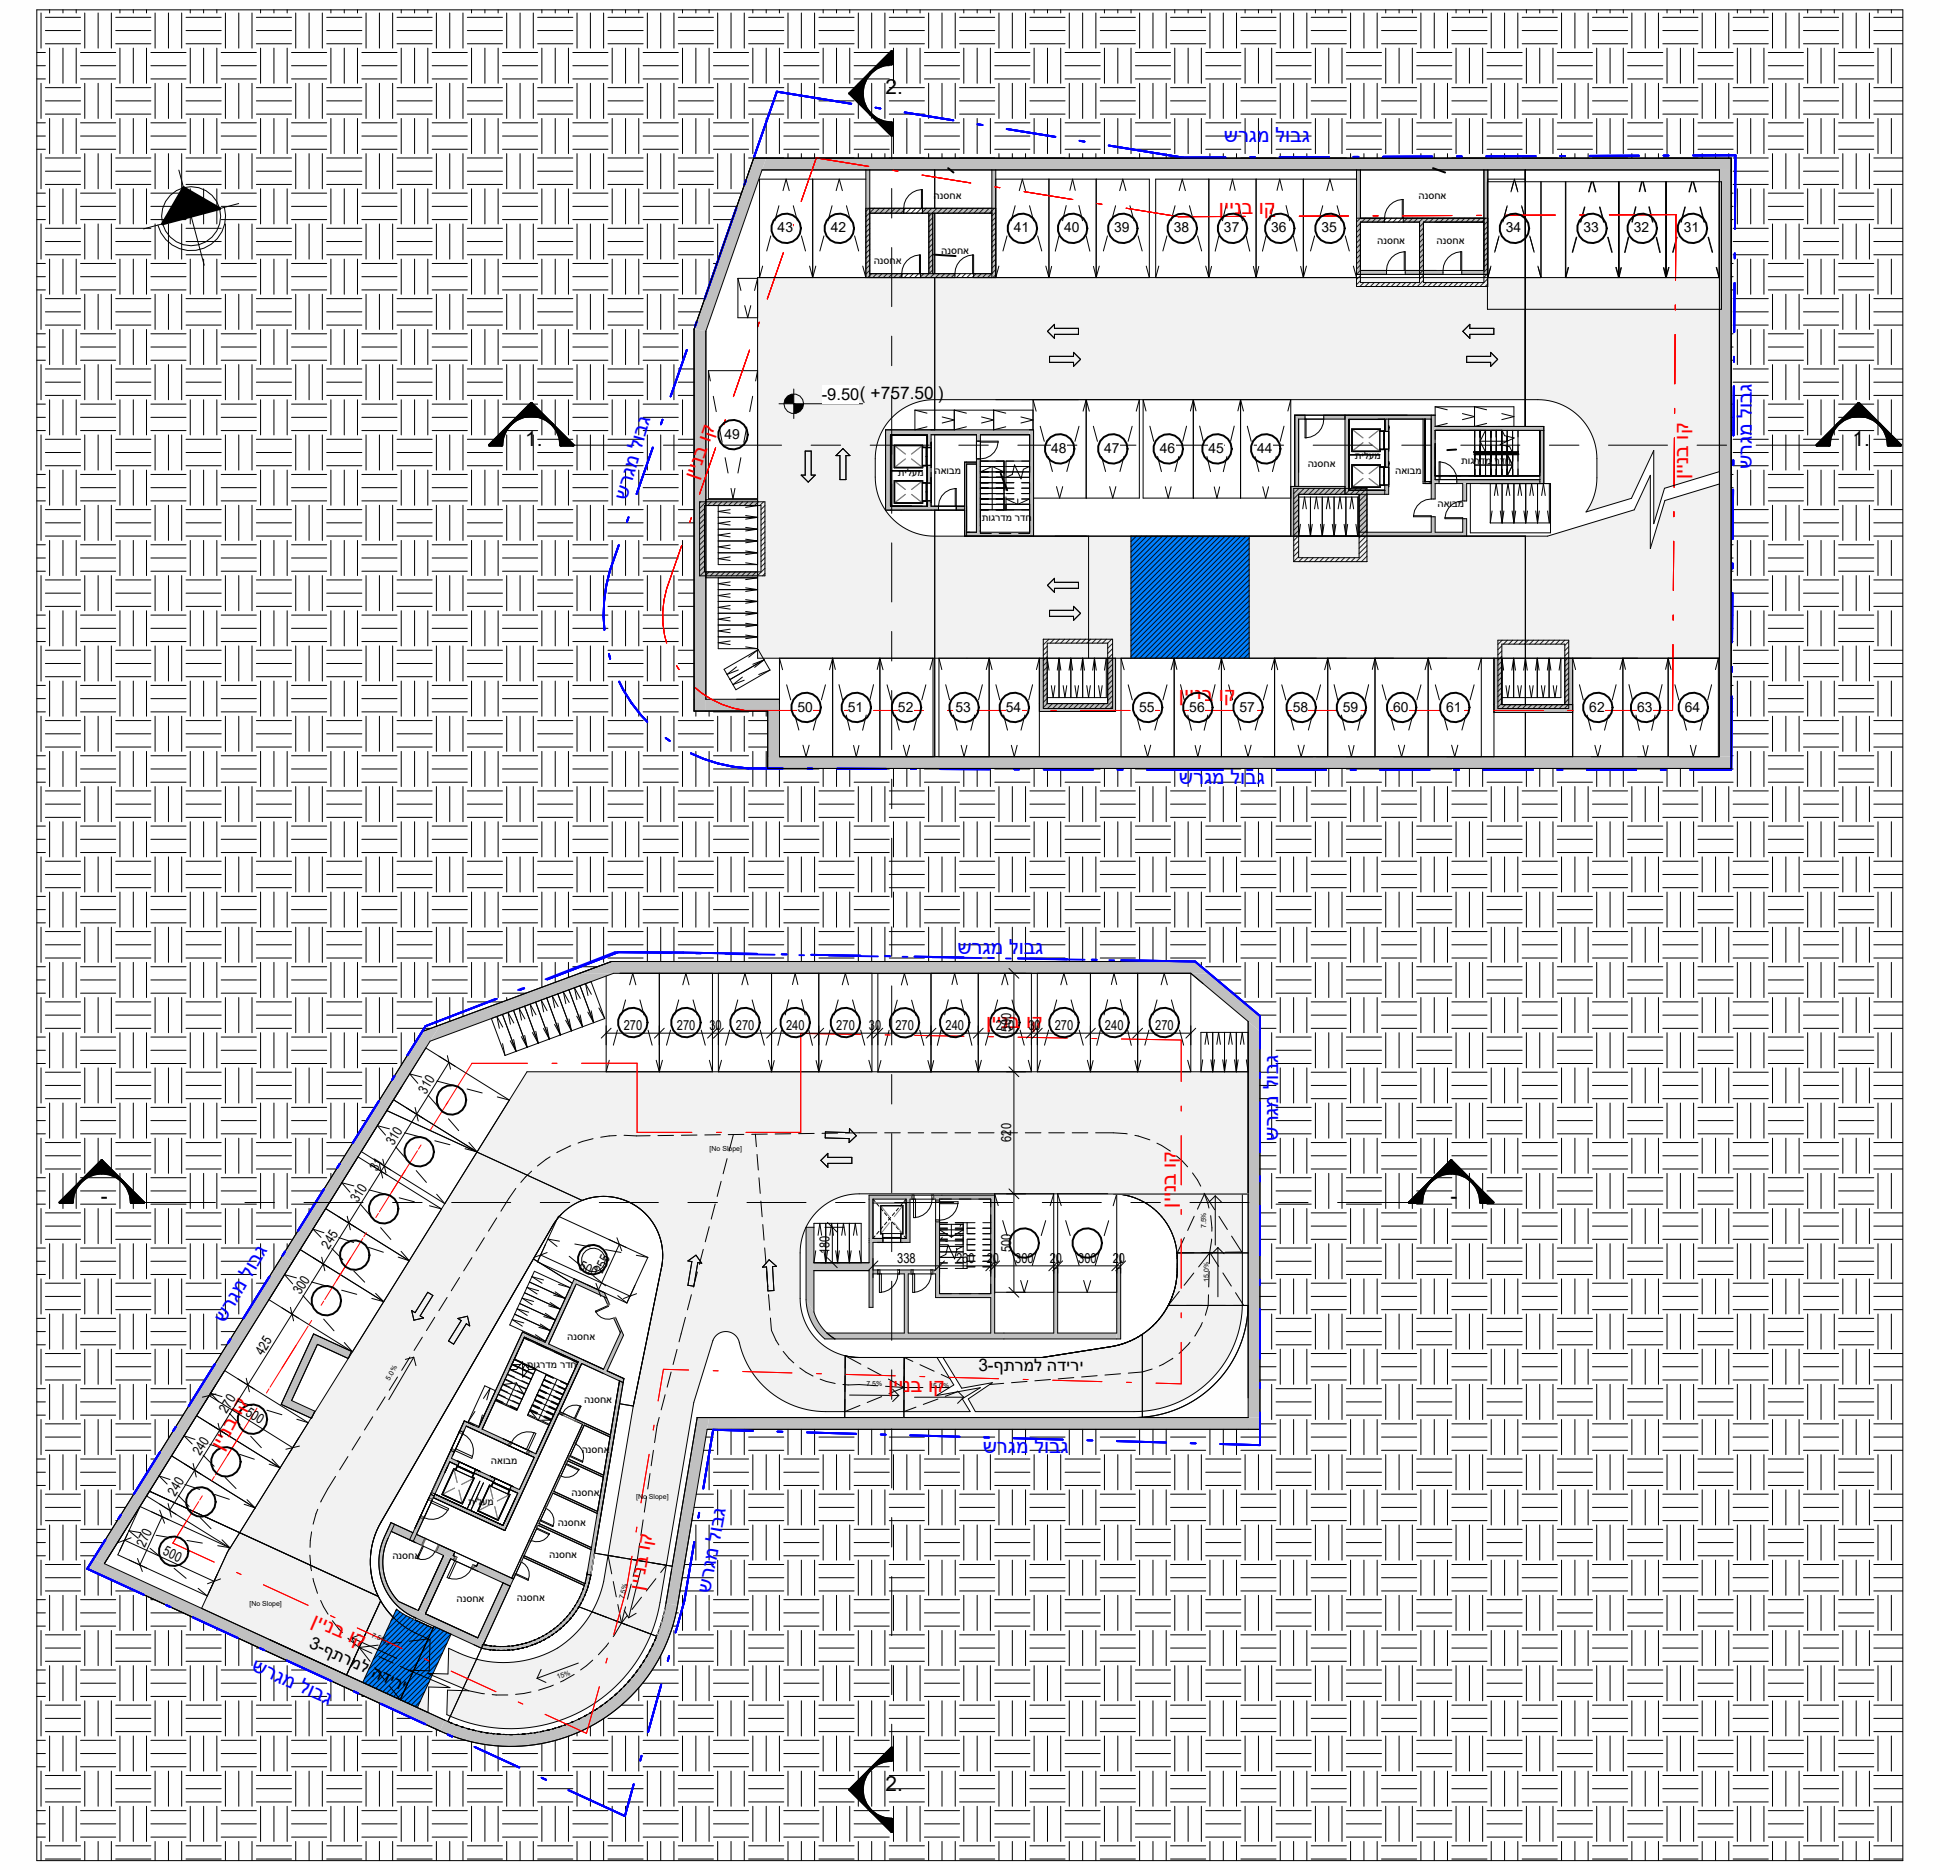
תכנית מרתף-2
מפלס: +757.47, +759.54
קנ"מ: 1 : 250

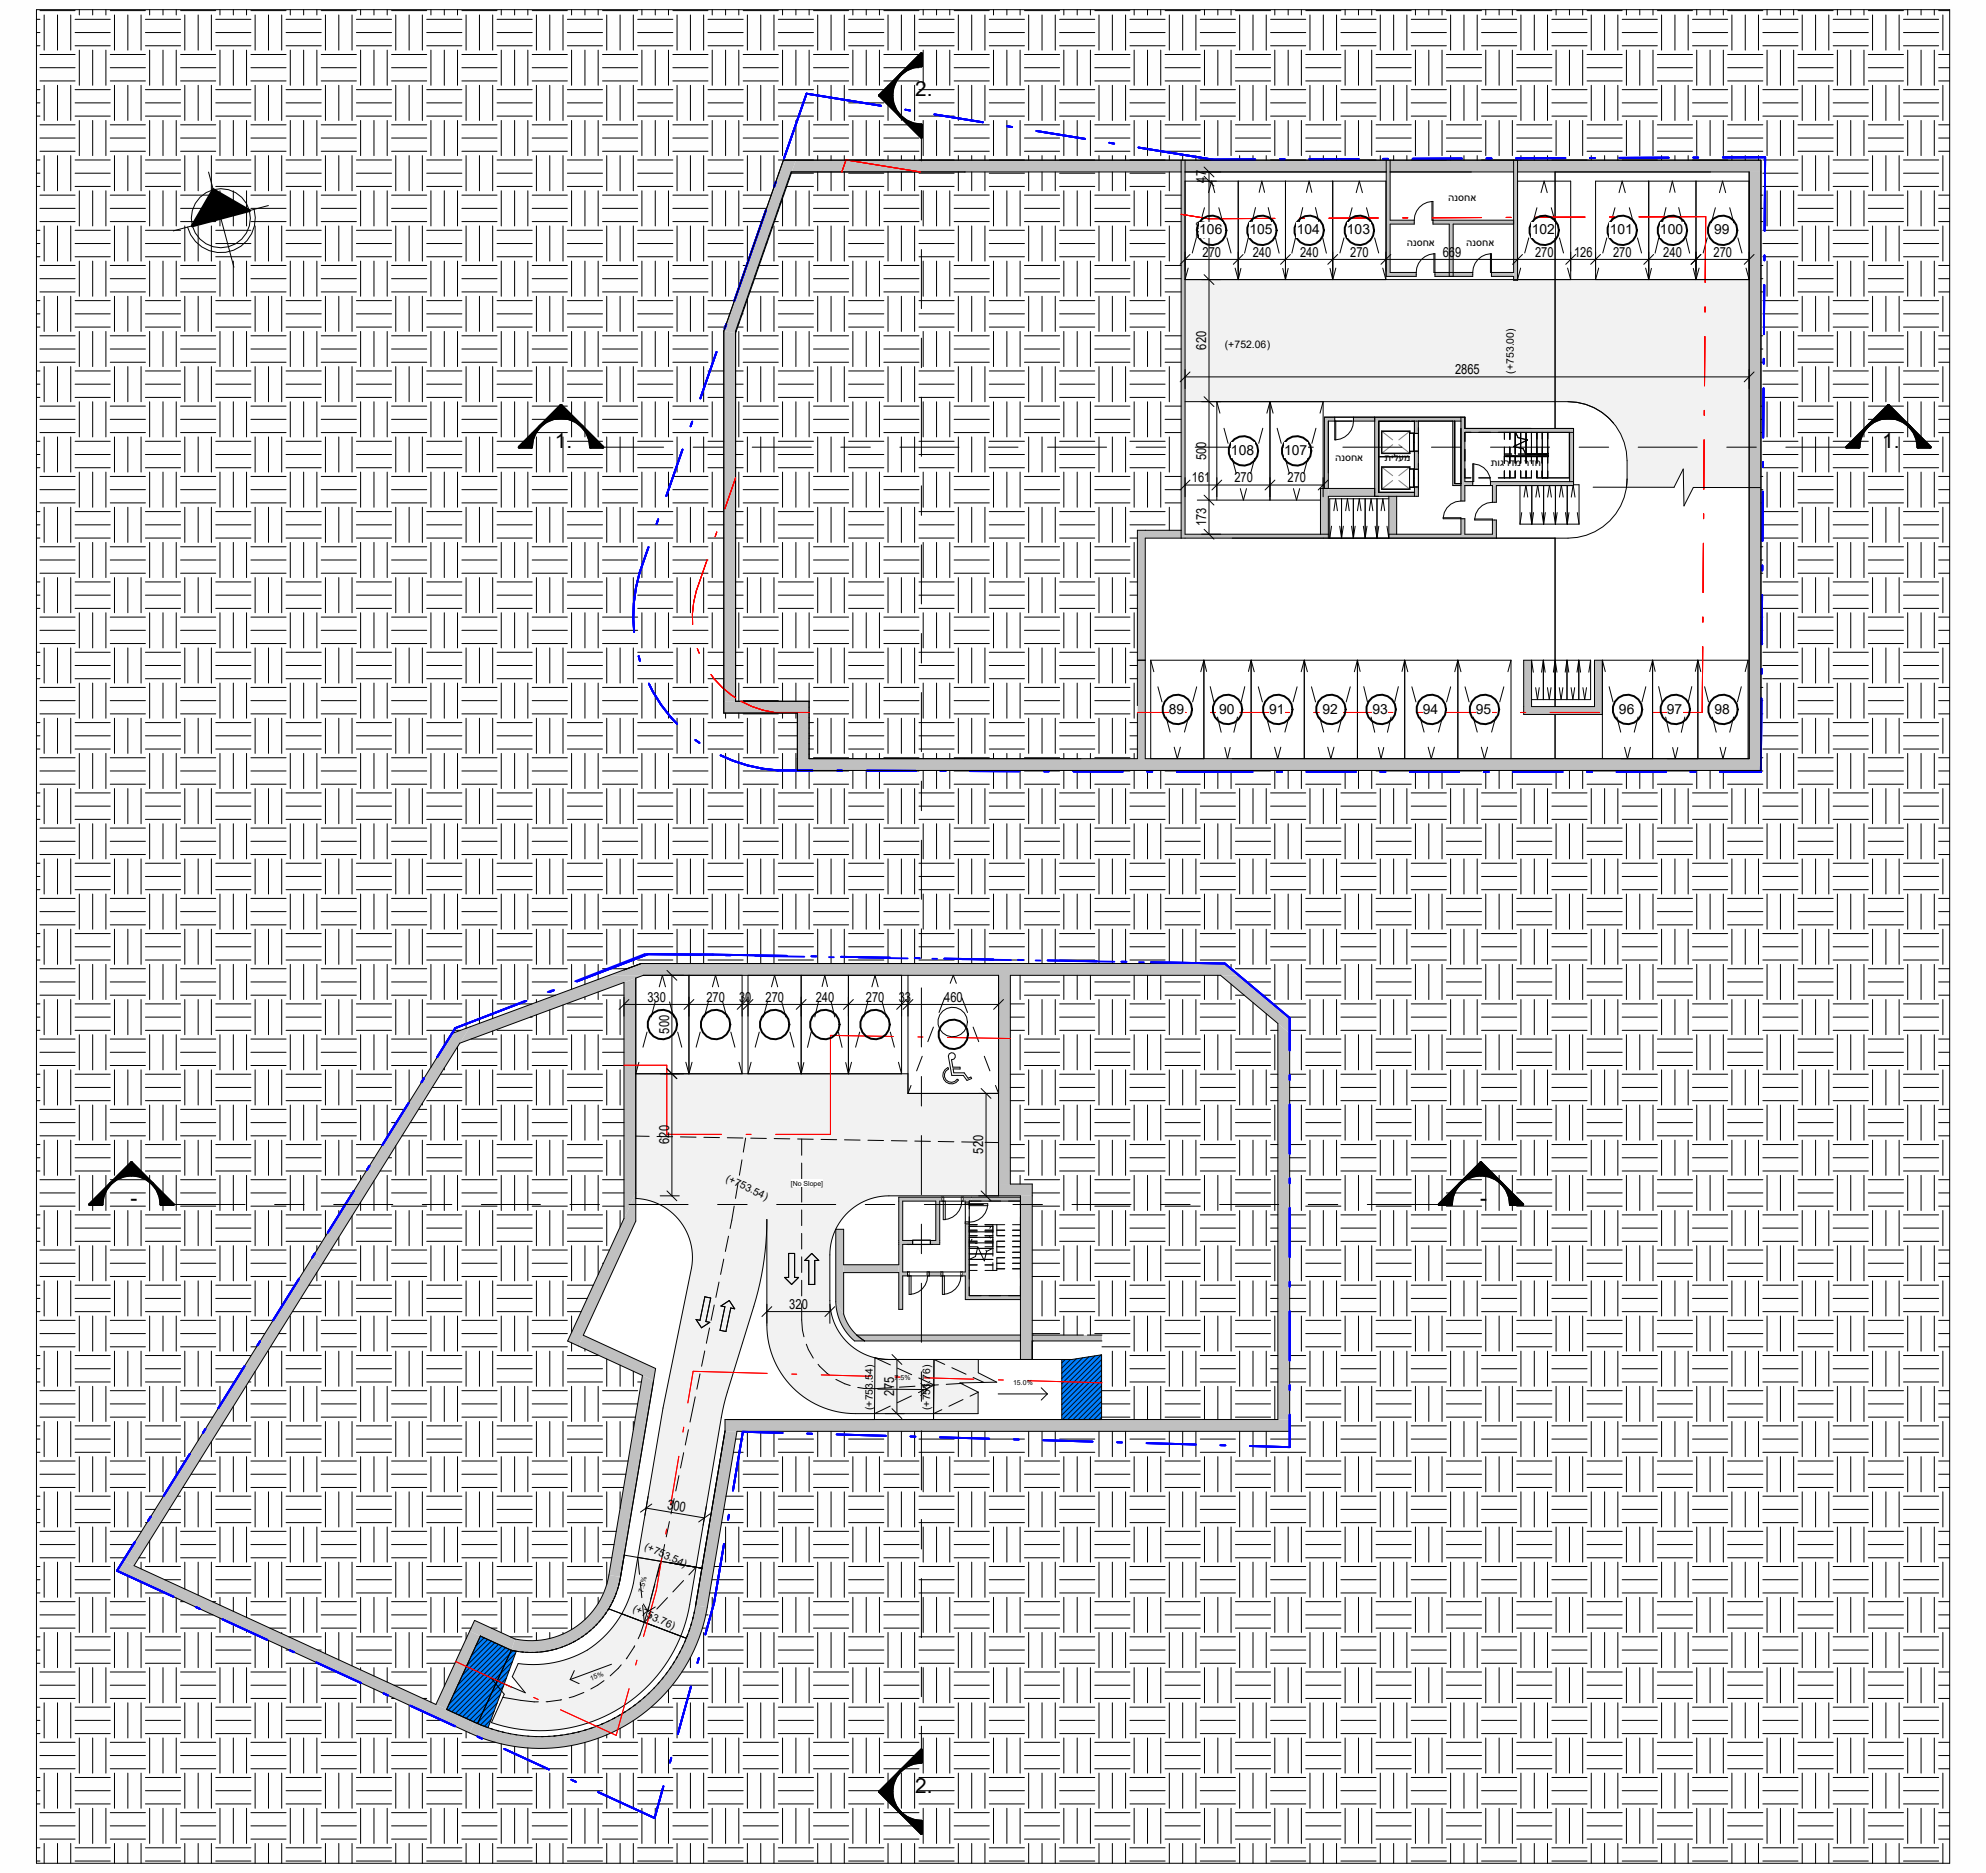
תכנית מרתף-4
מפלס: +752.06,+75.54
קנ"מ: 1 : 250

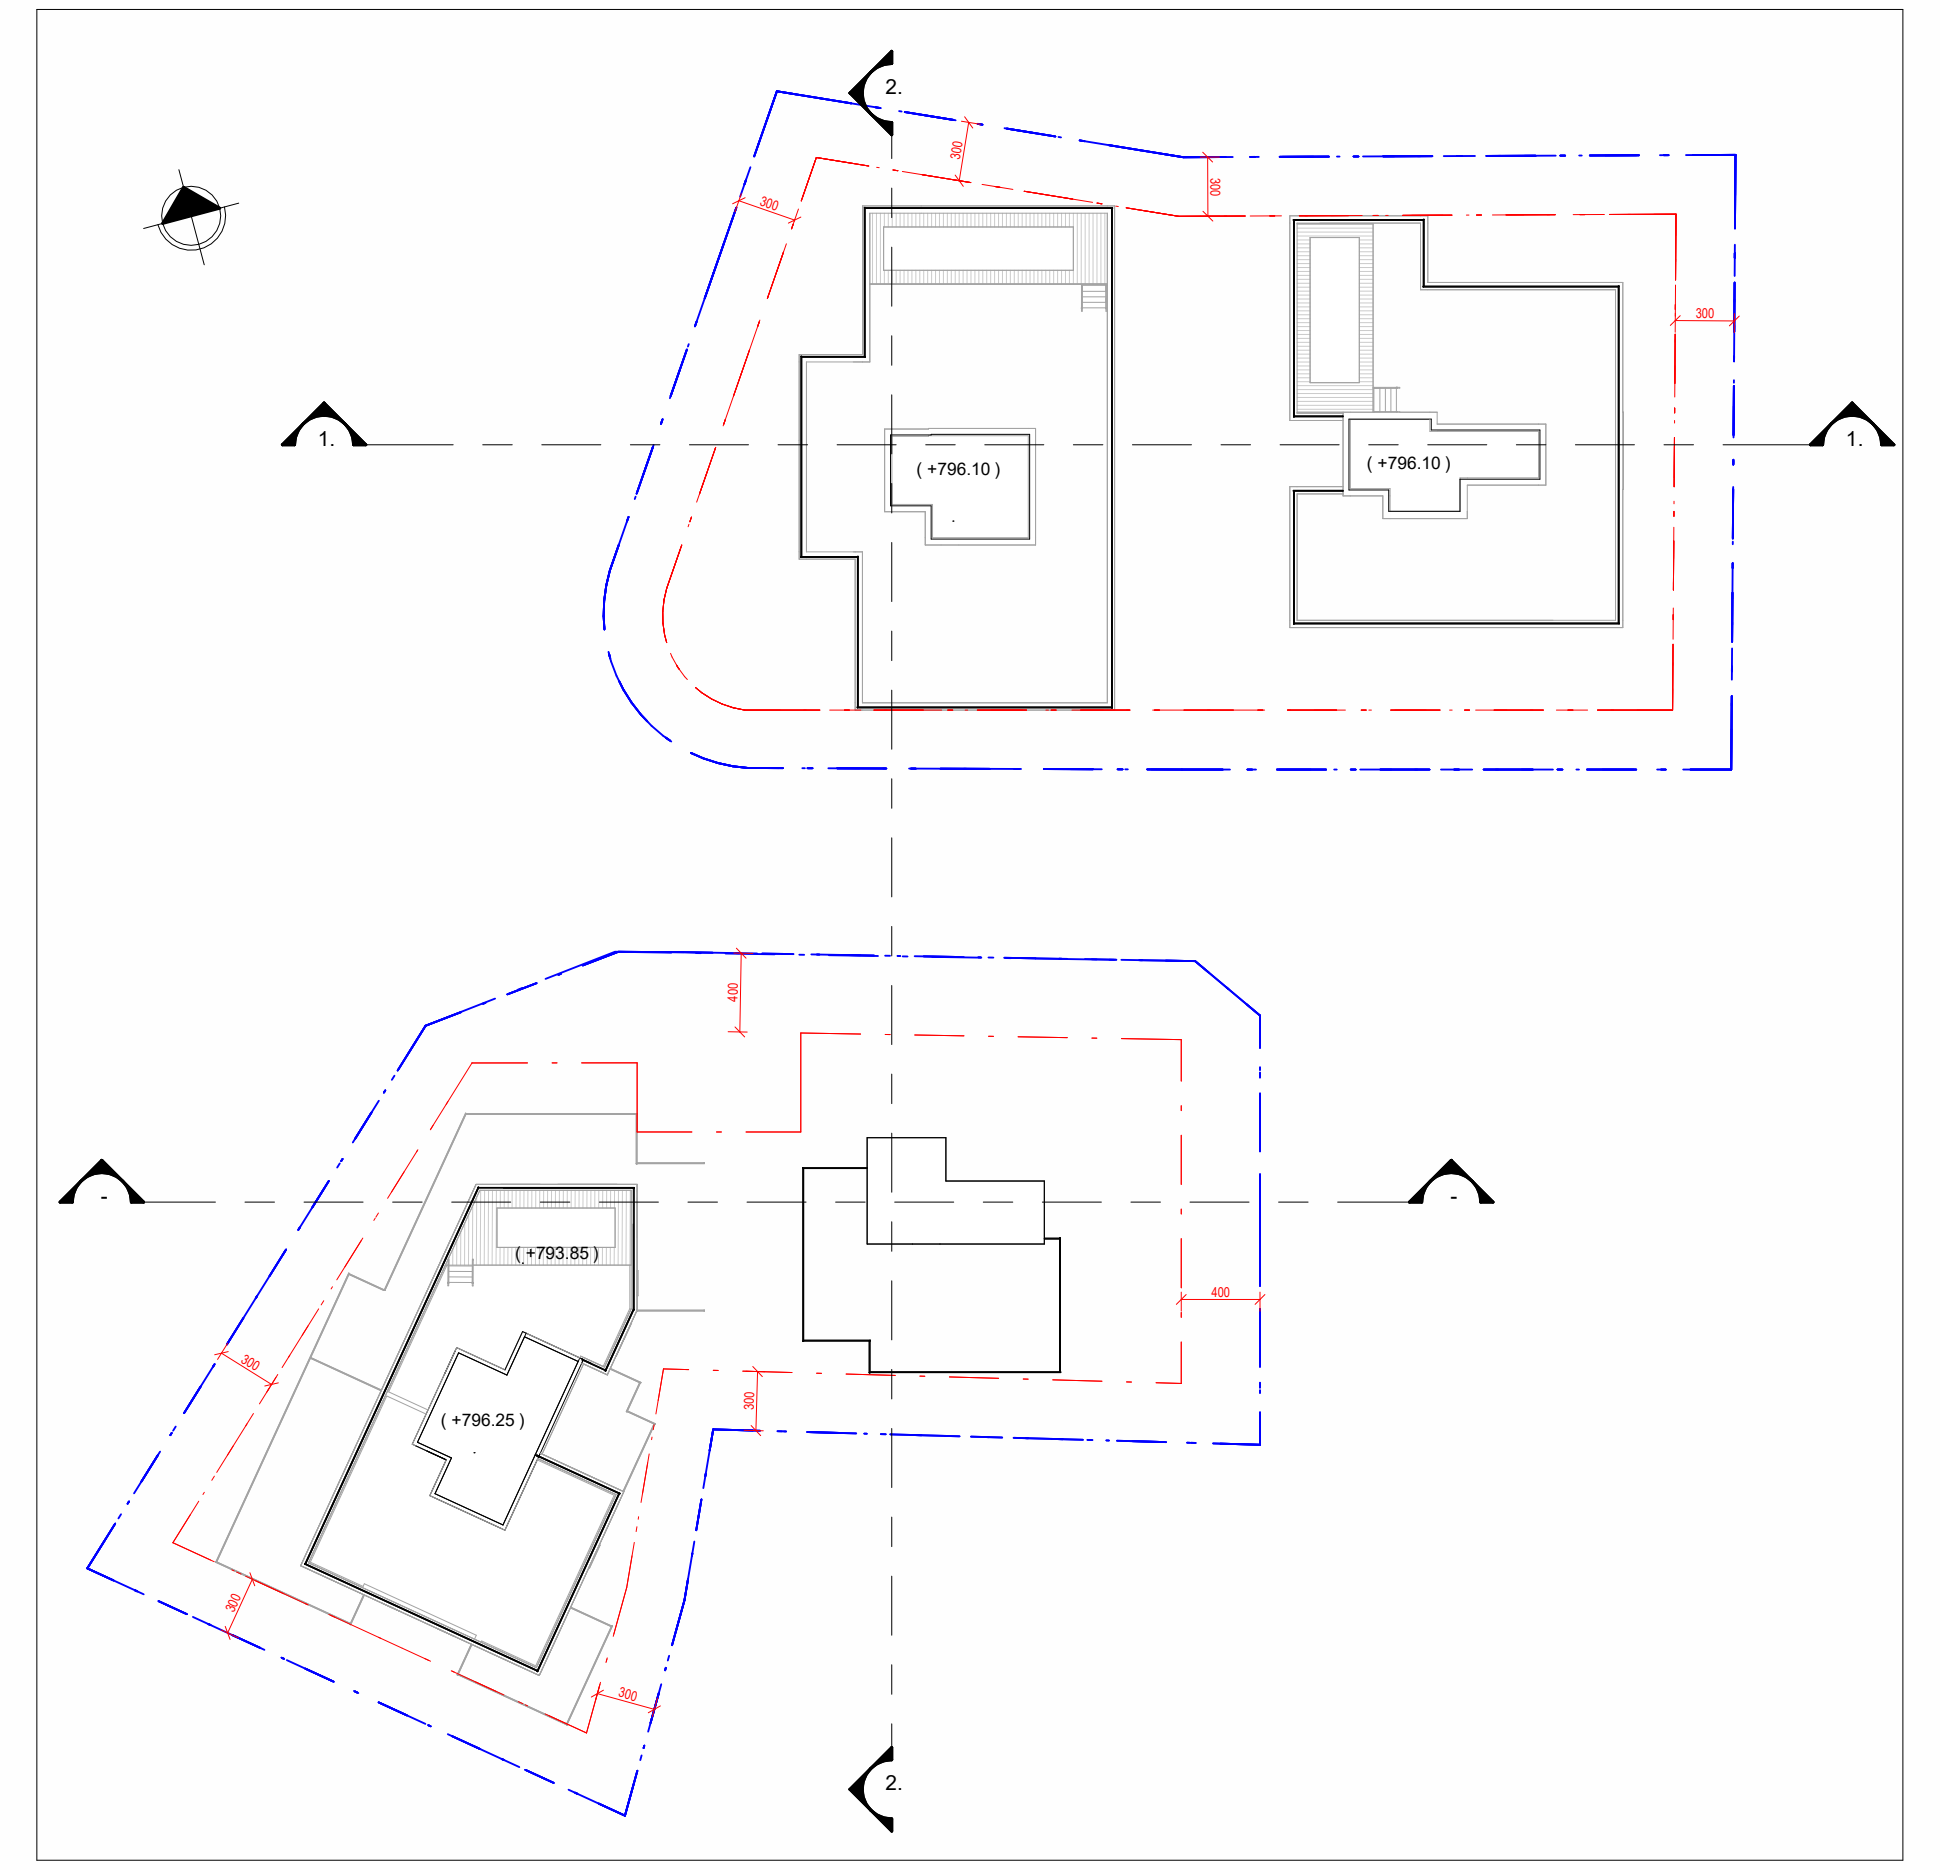
גג קומה
מפלס:
קנ"מ: 1 : 250

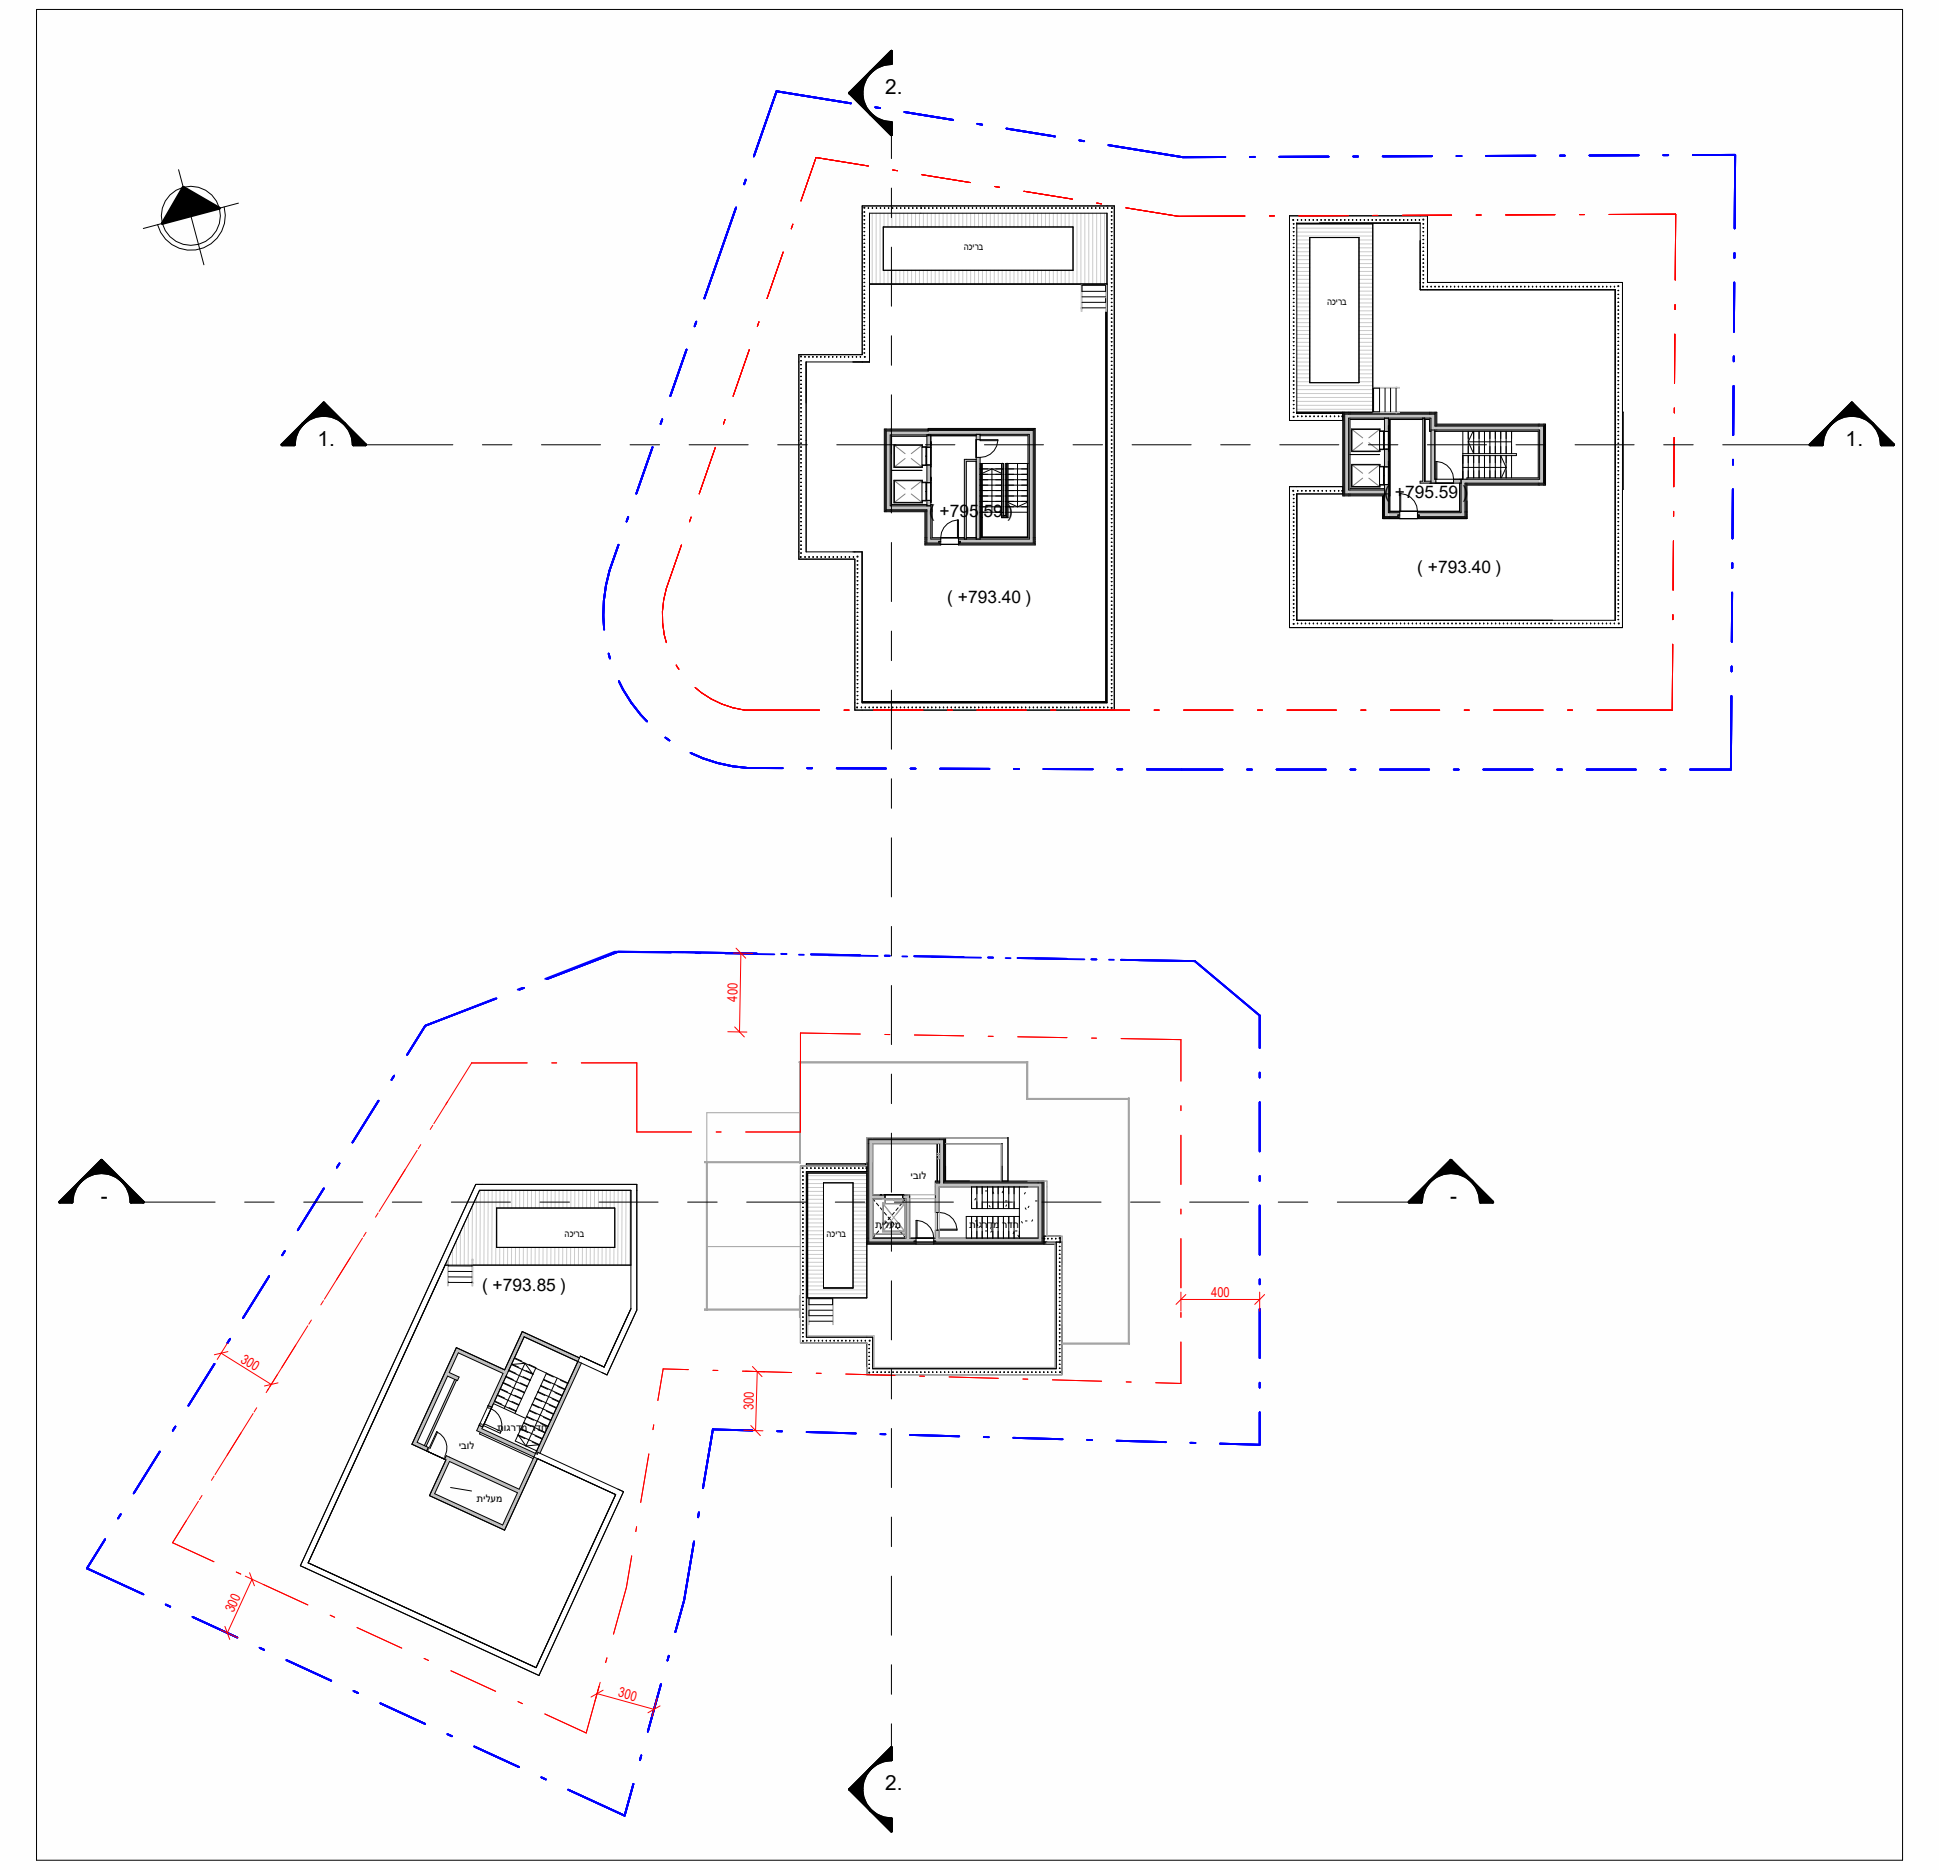
גג קומה
מפלס:
קנ"מ: 1 : 250

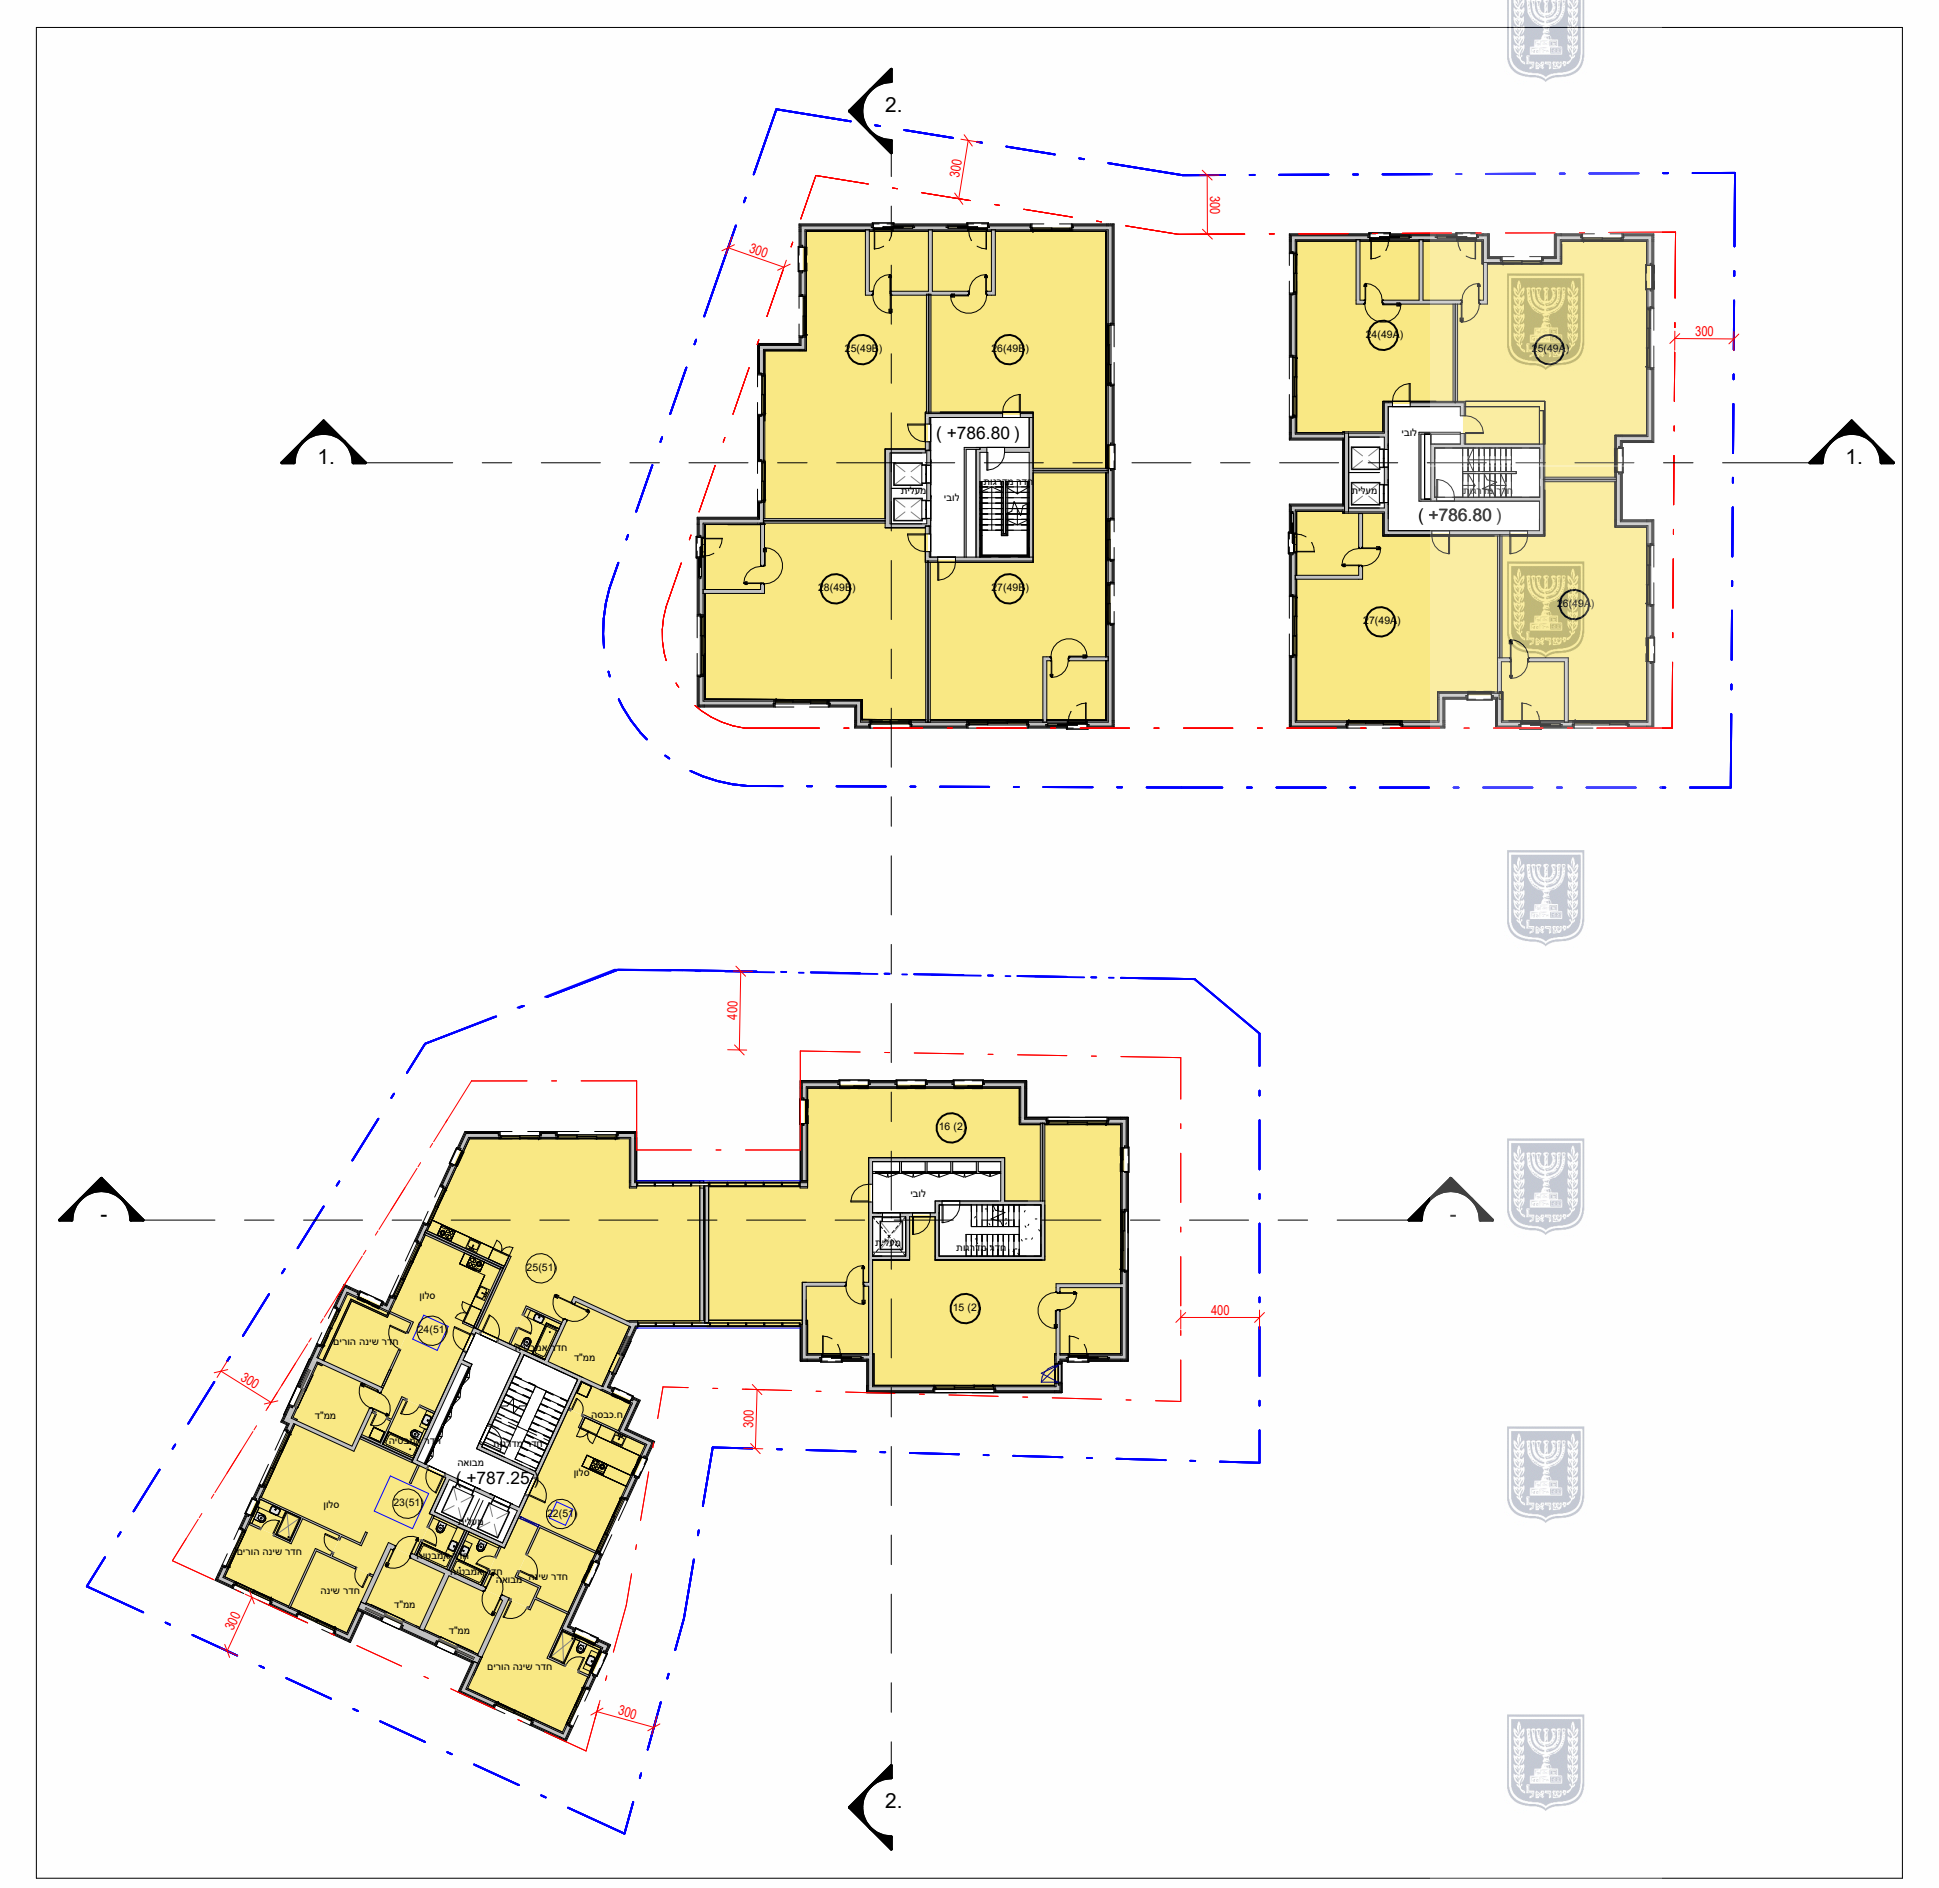
תכנית קומה6
מפלס:
קנ"מ: 1 : 250

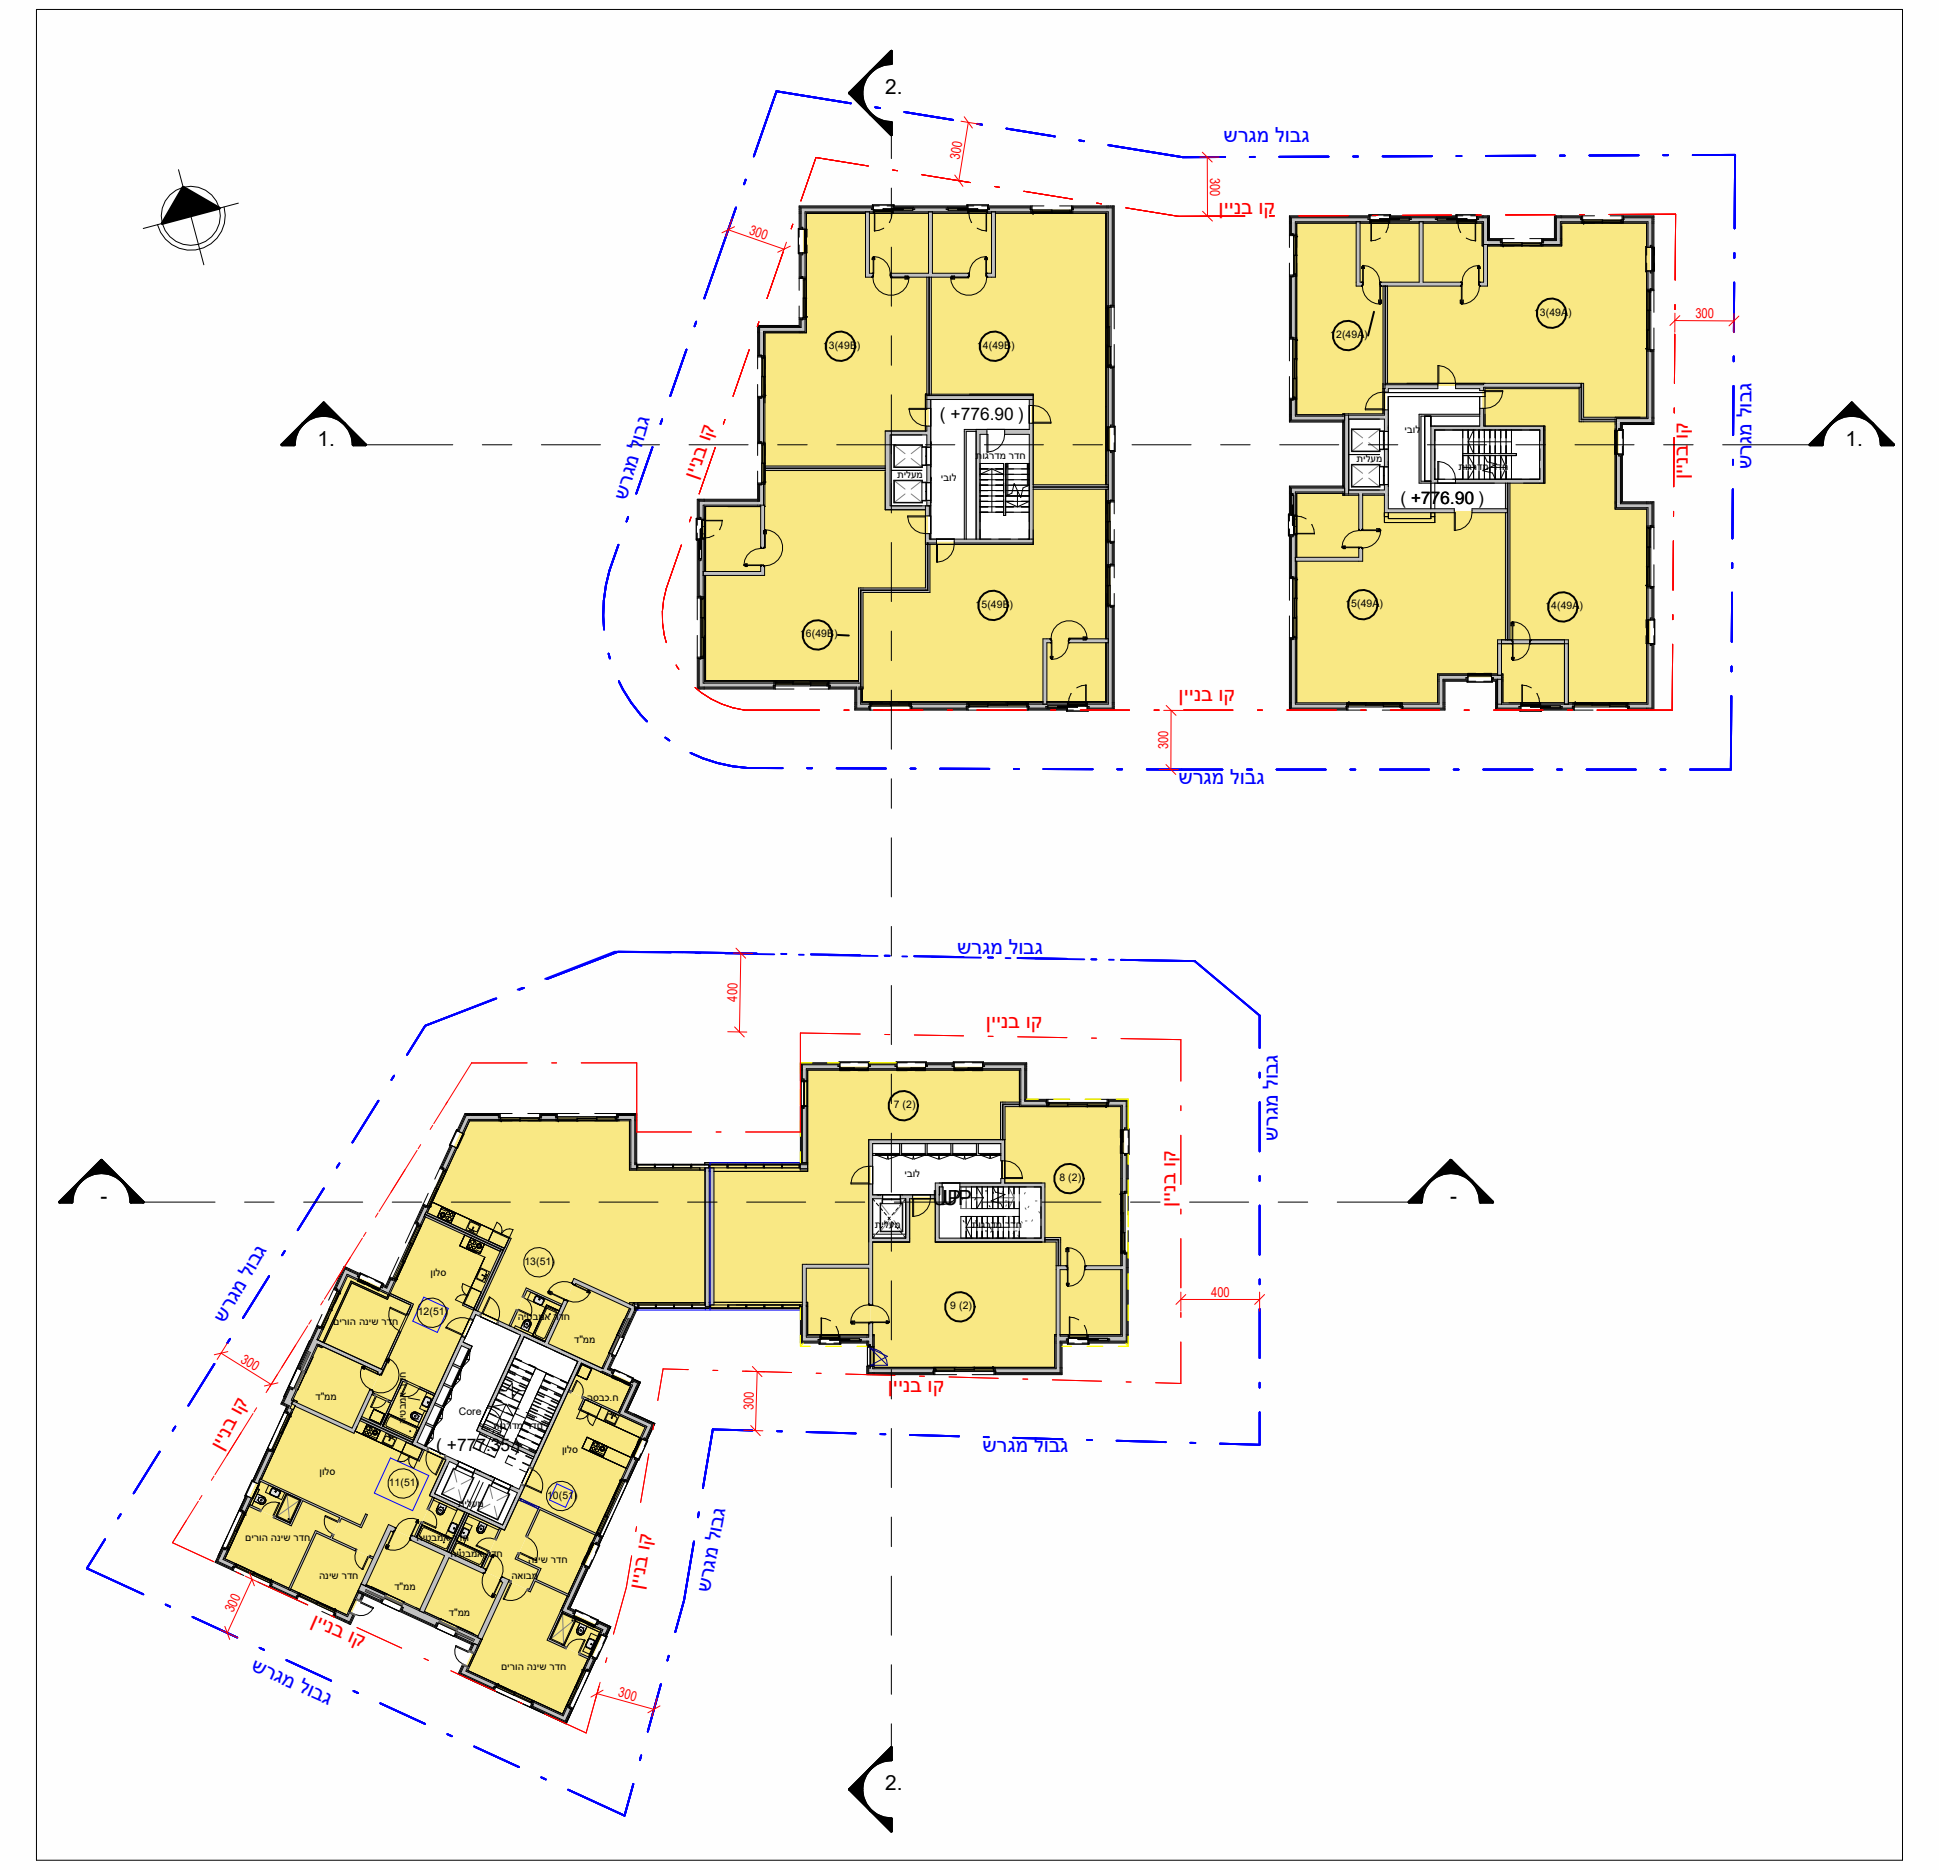
תכנית קומה3
מפלס:
קנ"מ: 1 : 250

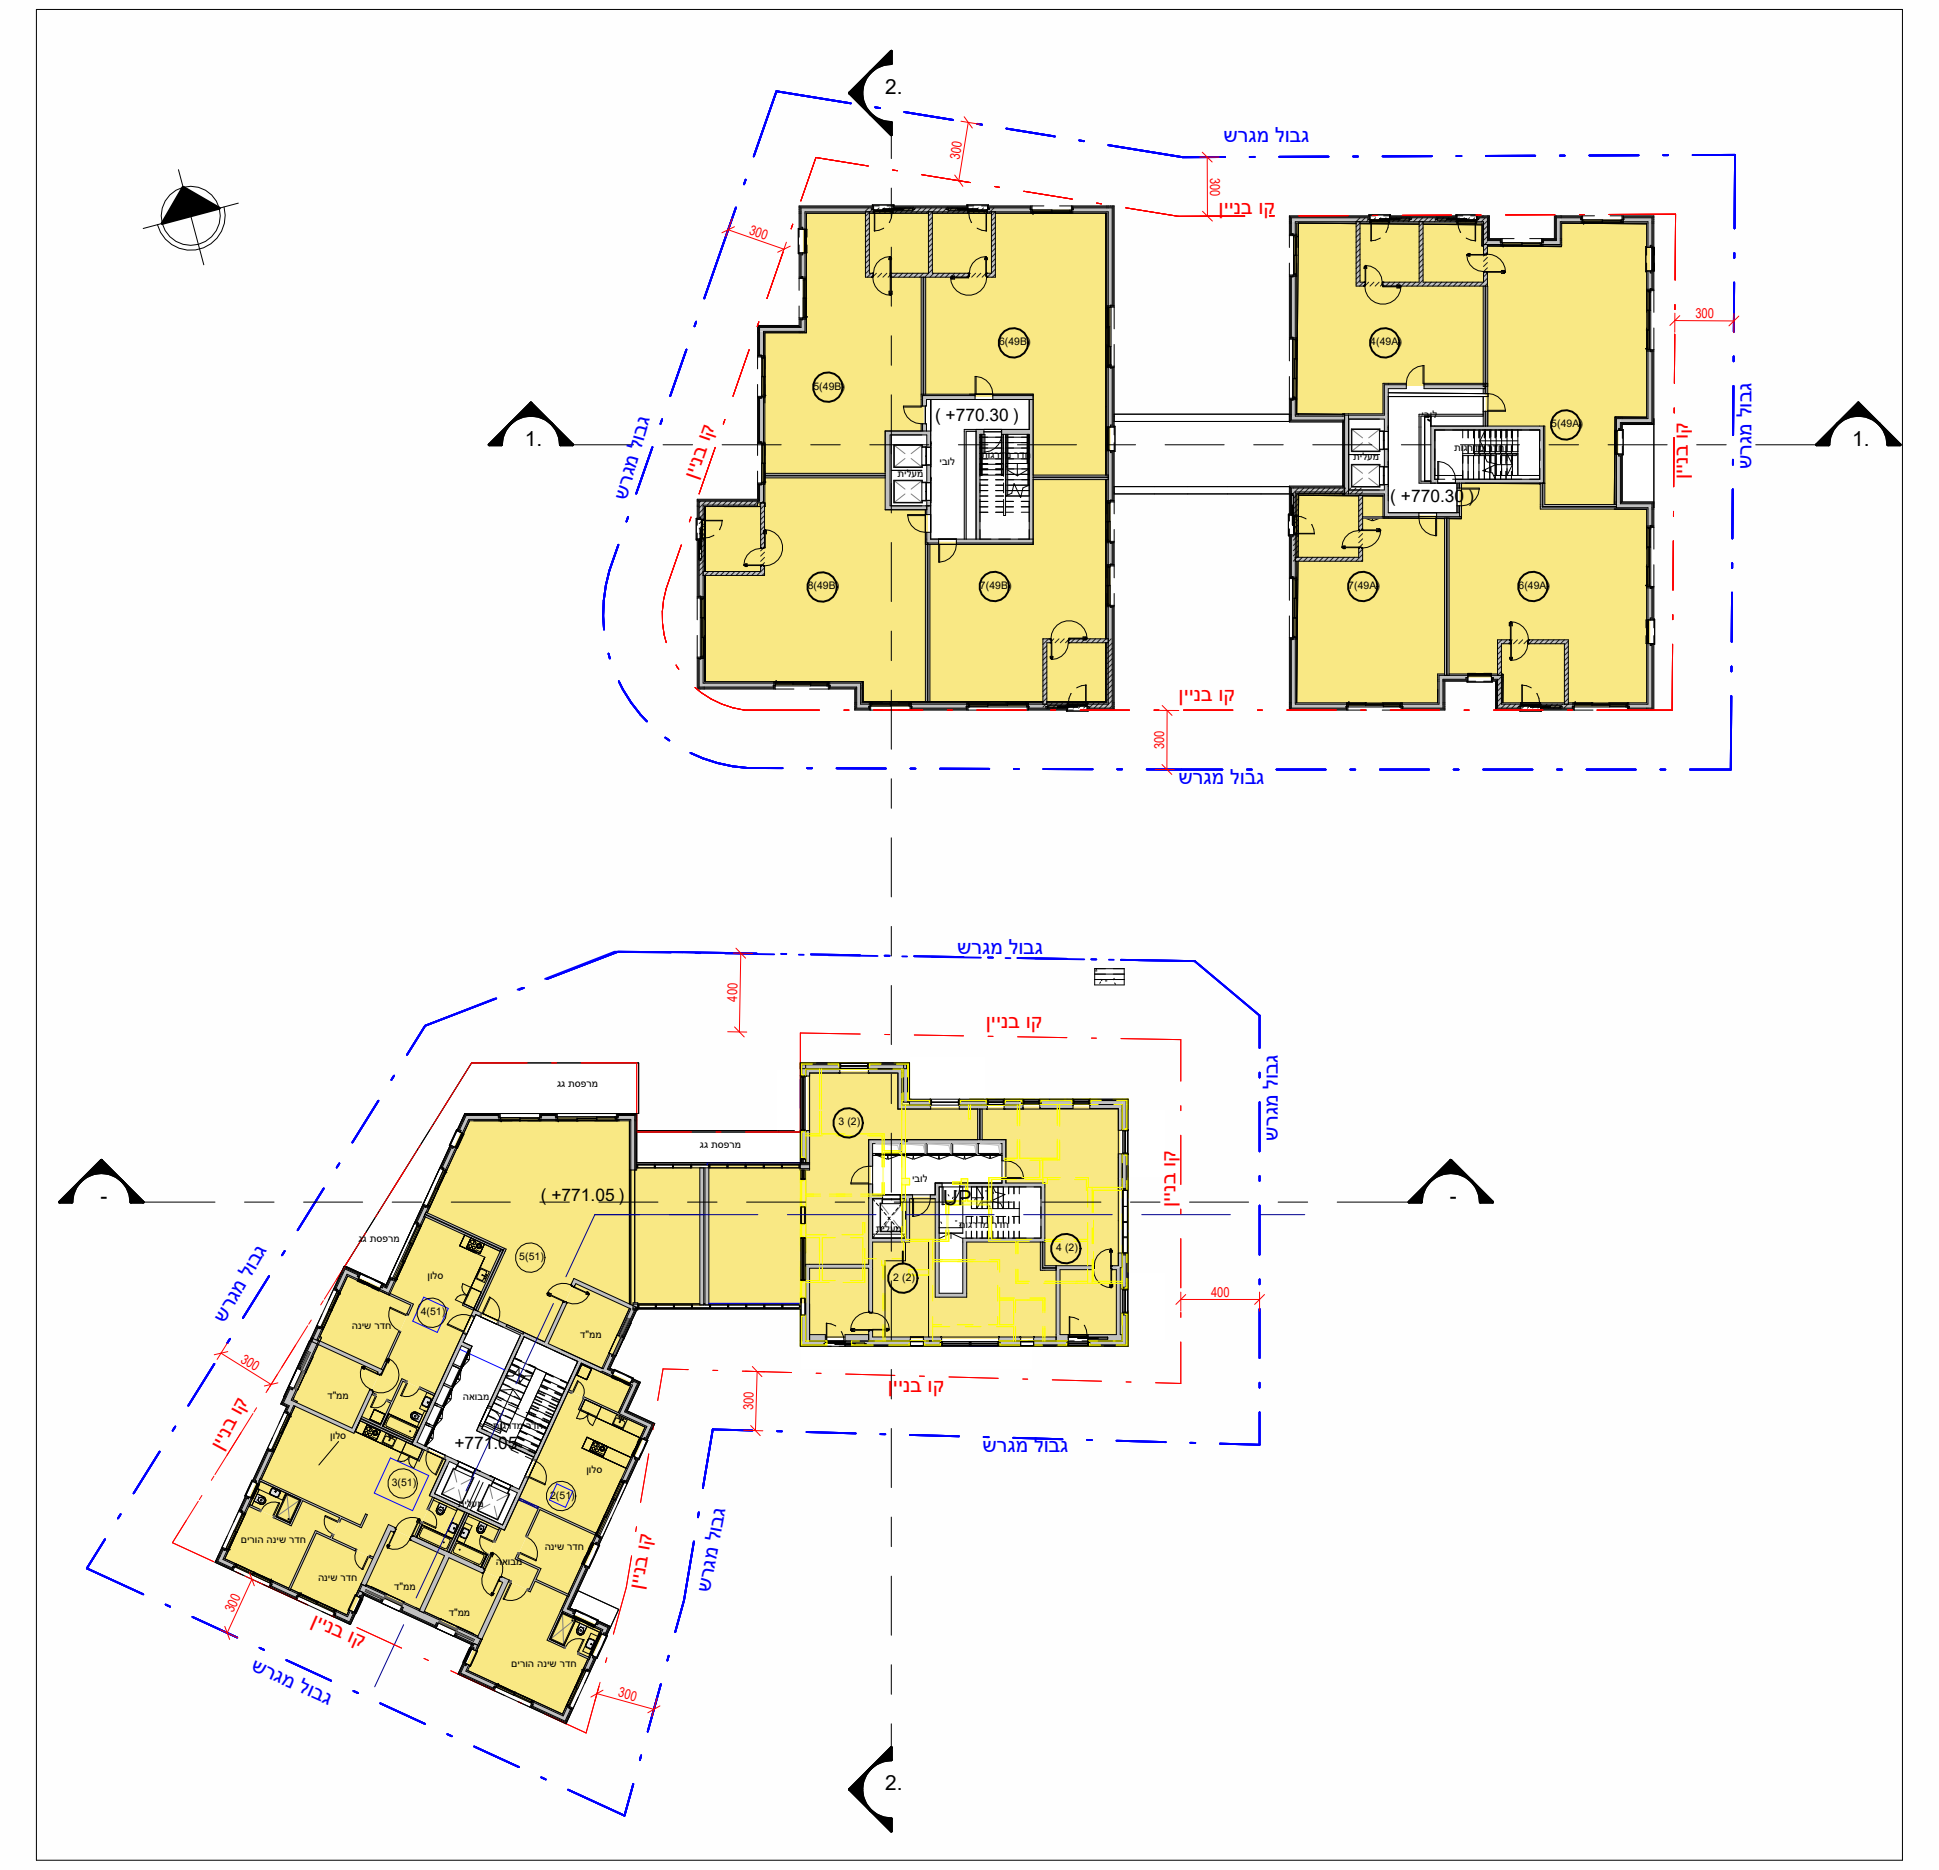
תכנית קומה1
מפלס:
קנ"מ: 1 : 250

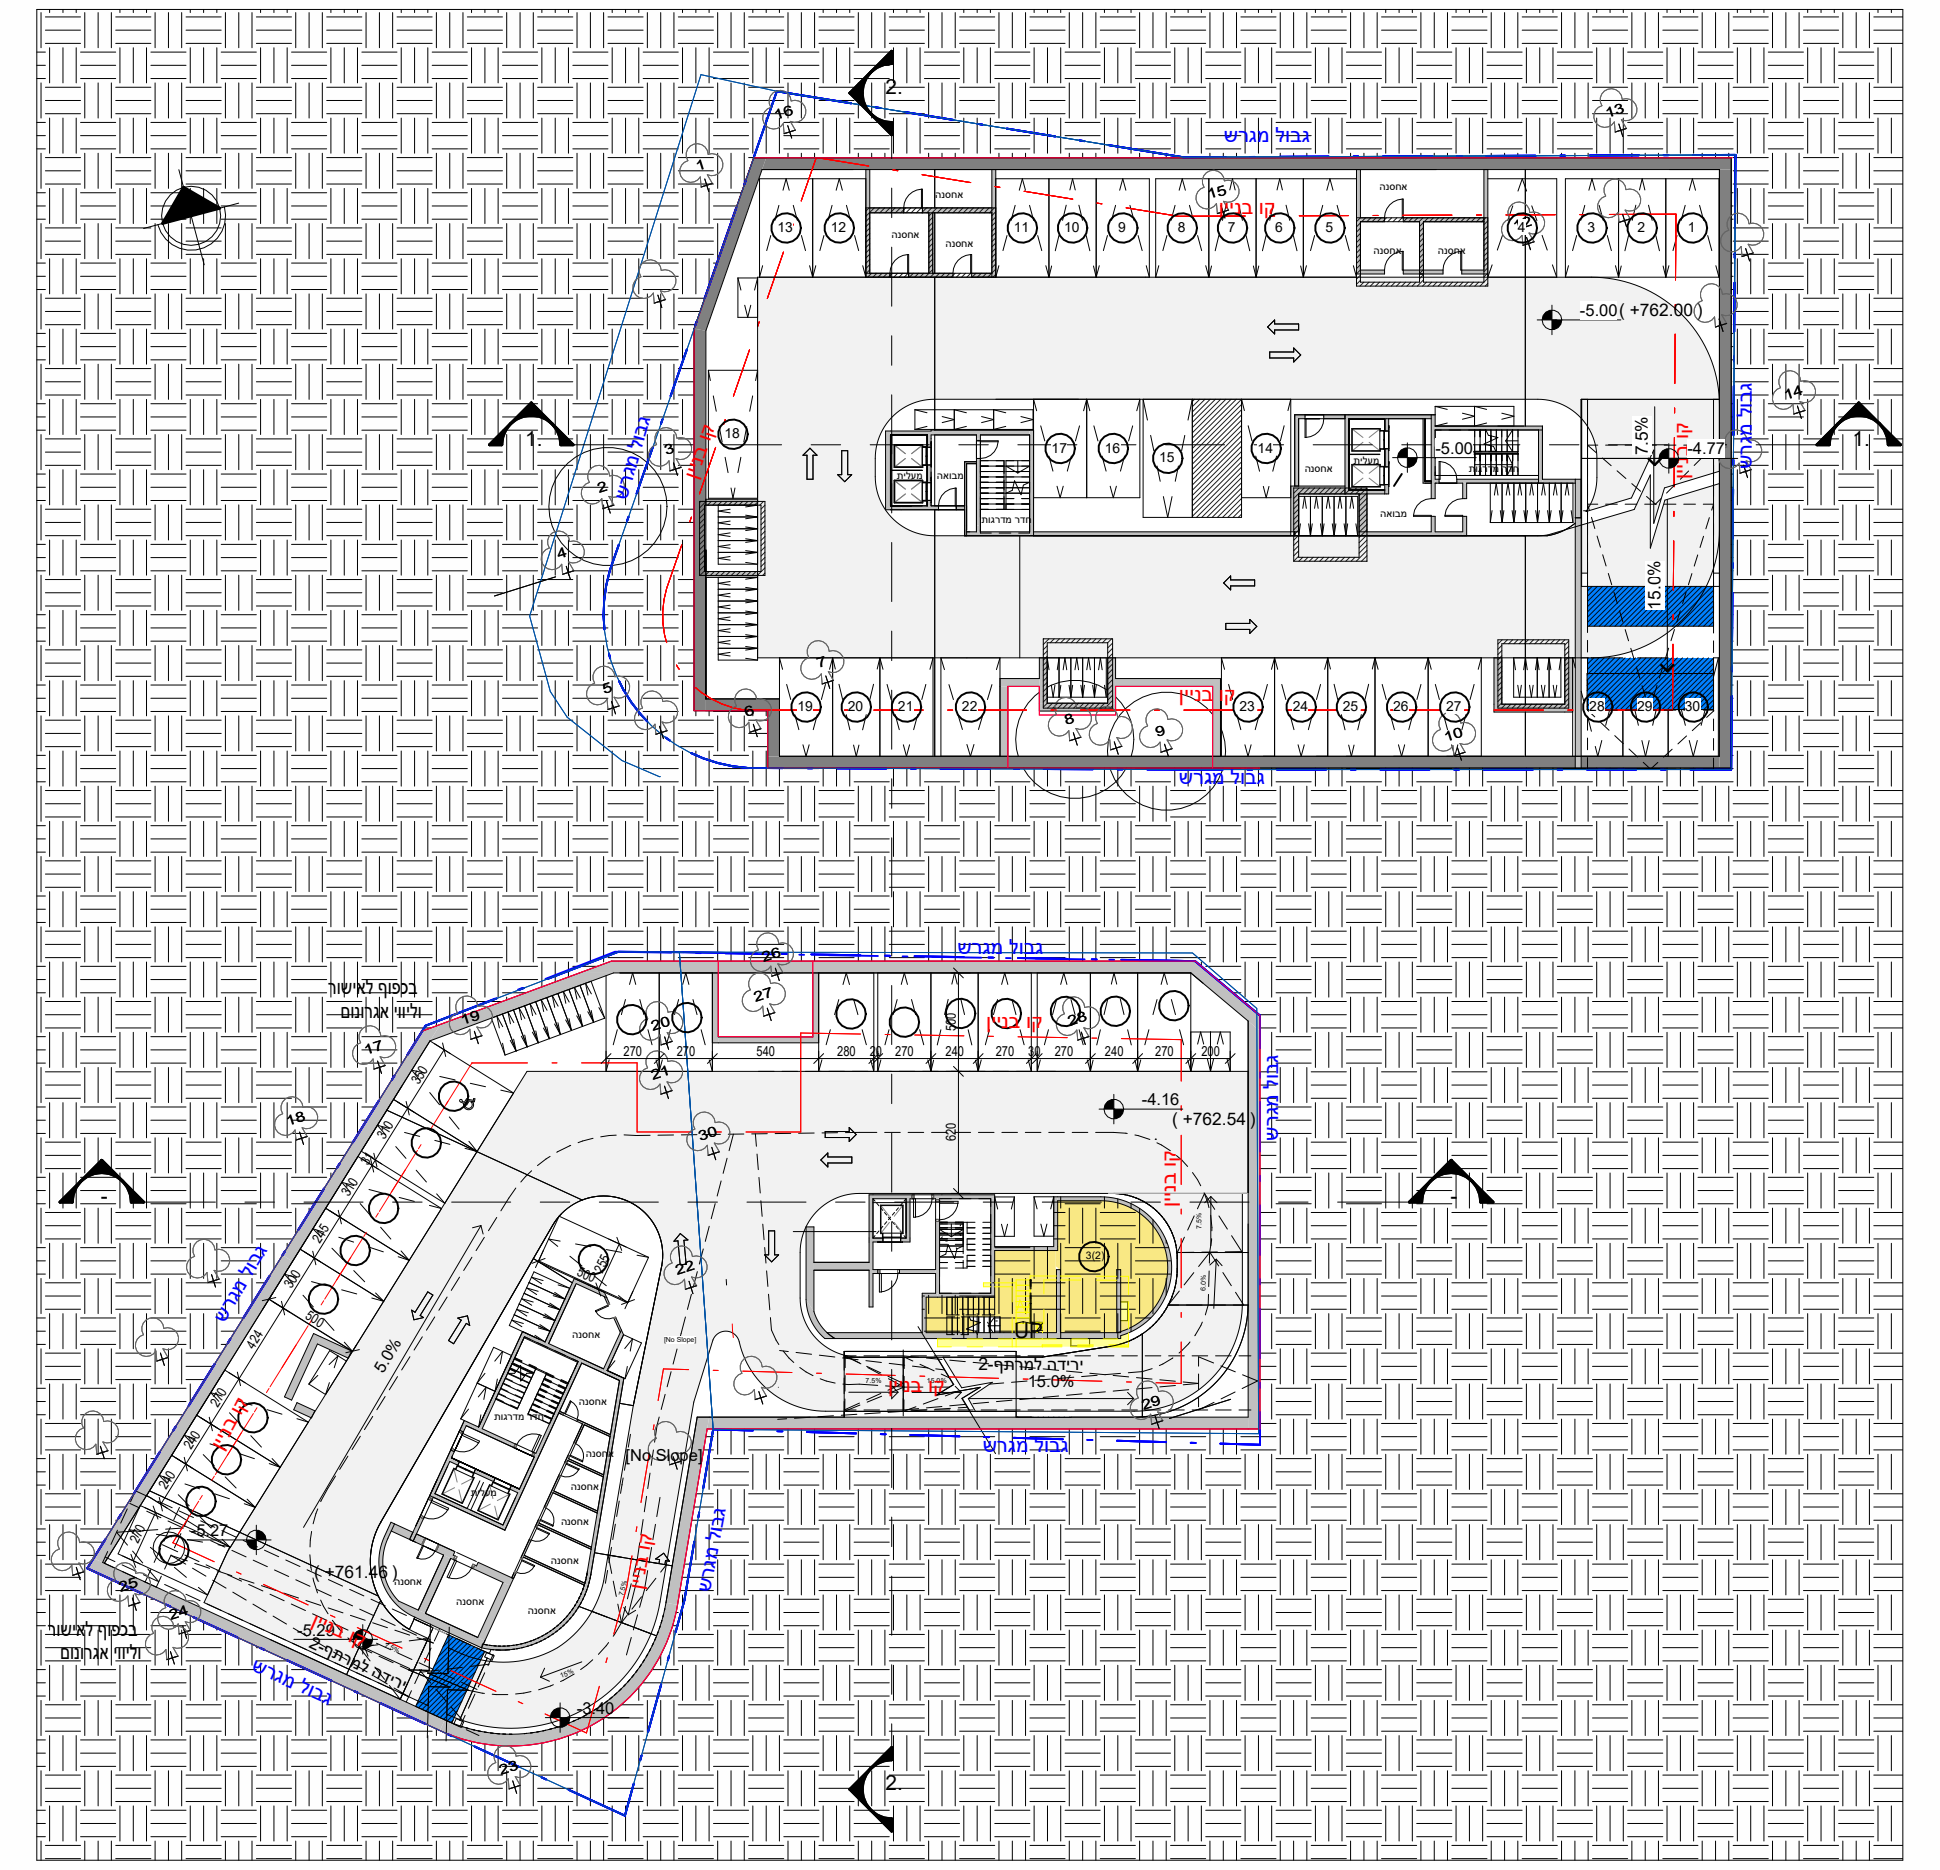
תכנית מרתף
מפלס: +762.00, +762.54
קנ"מ: 1 : 250

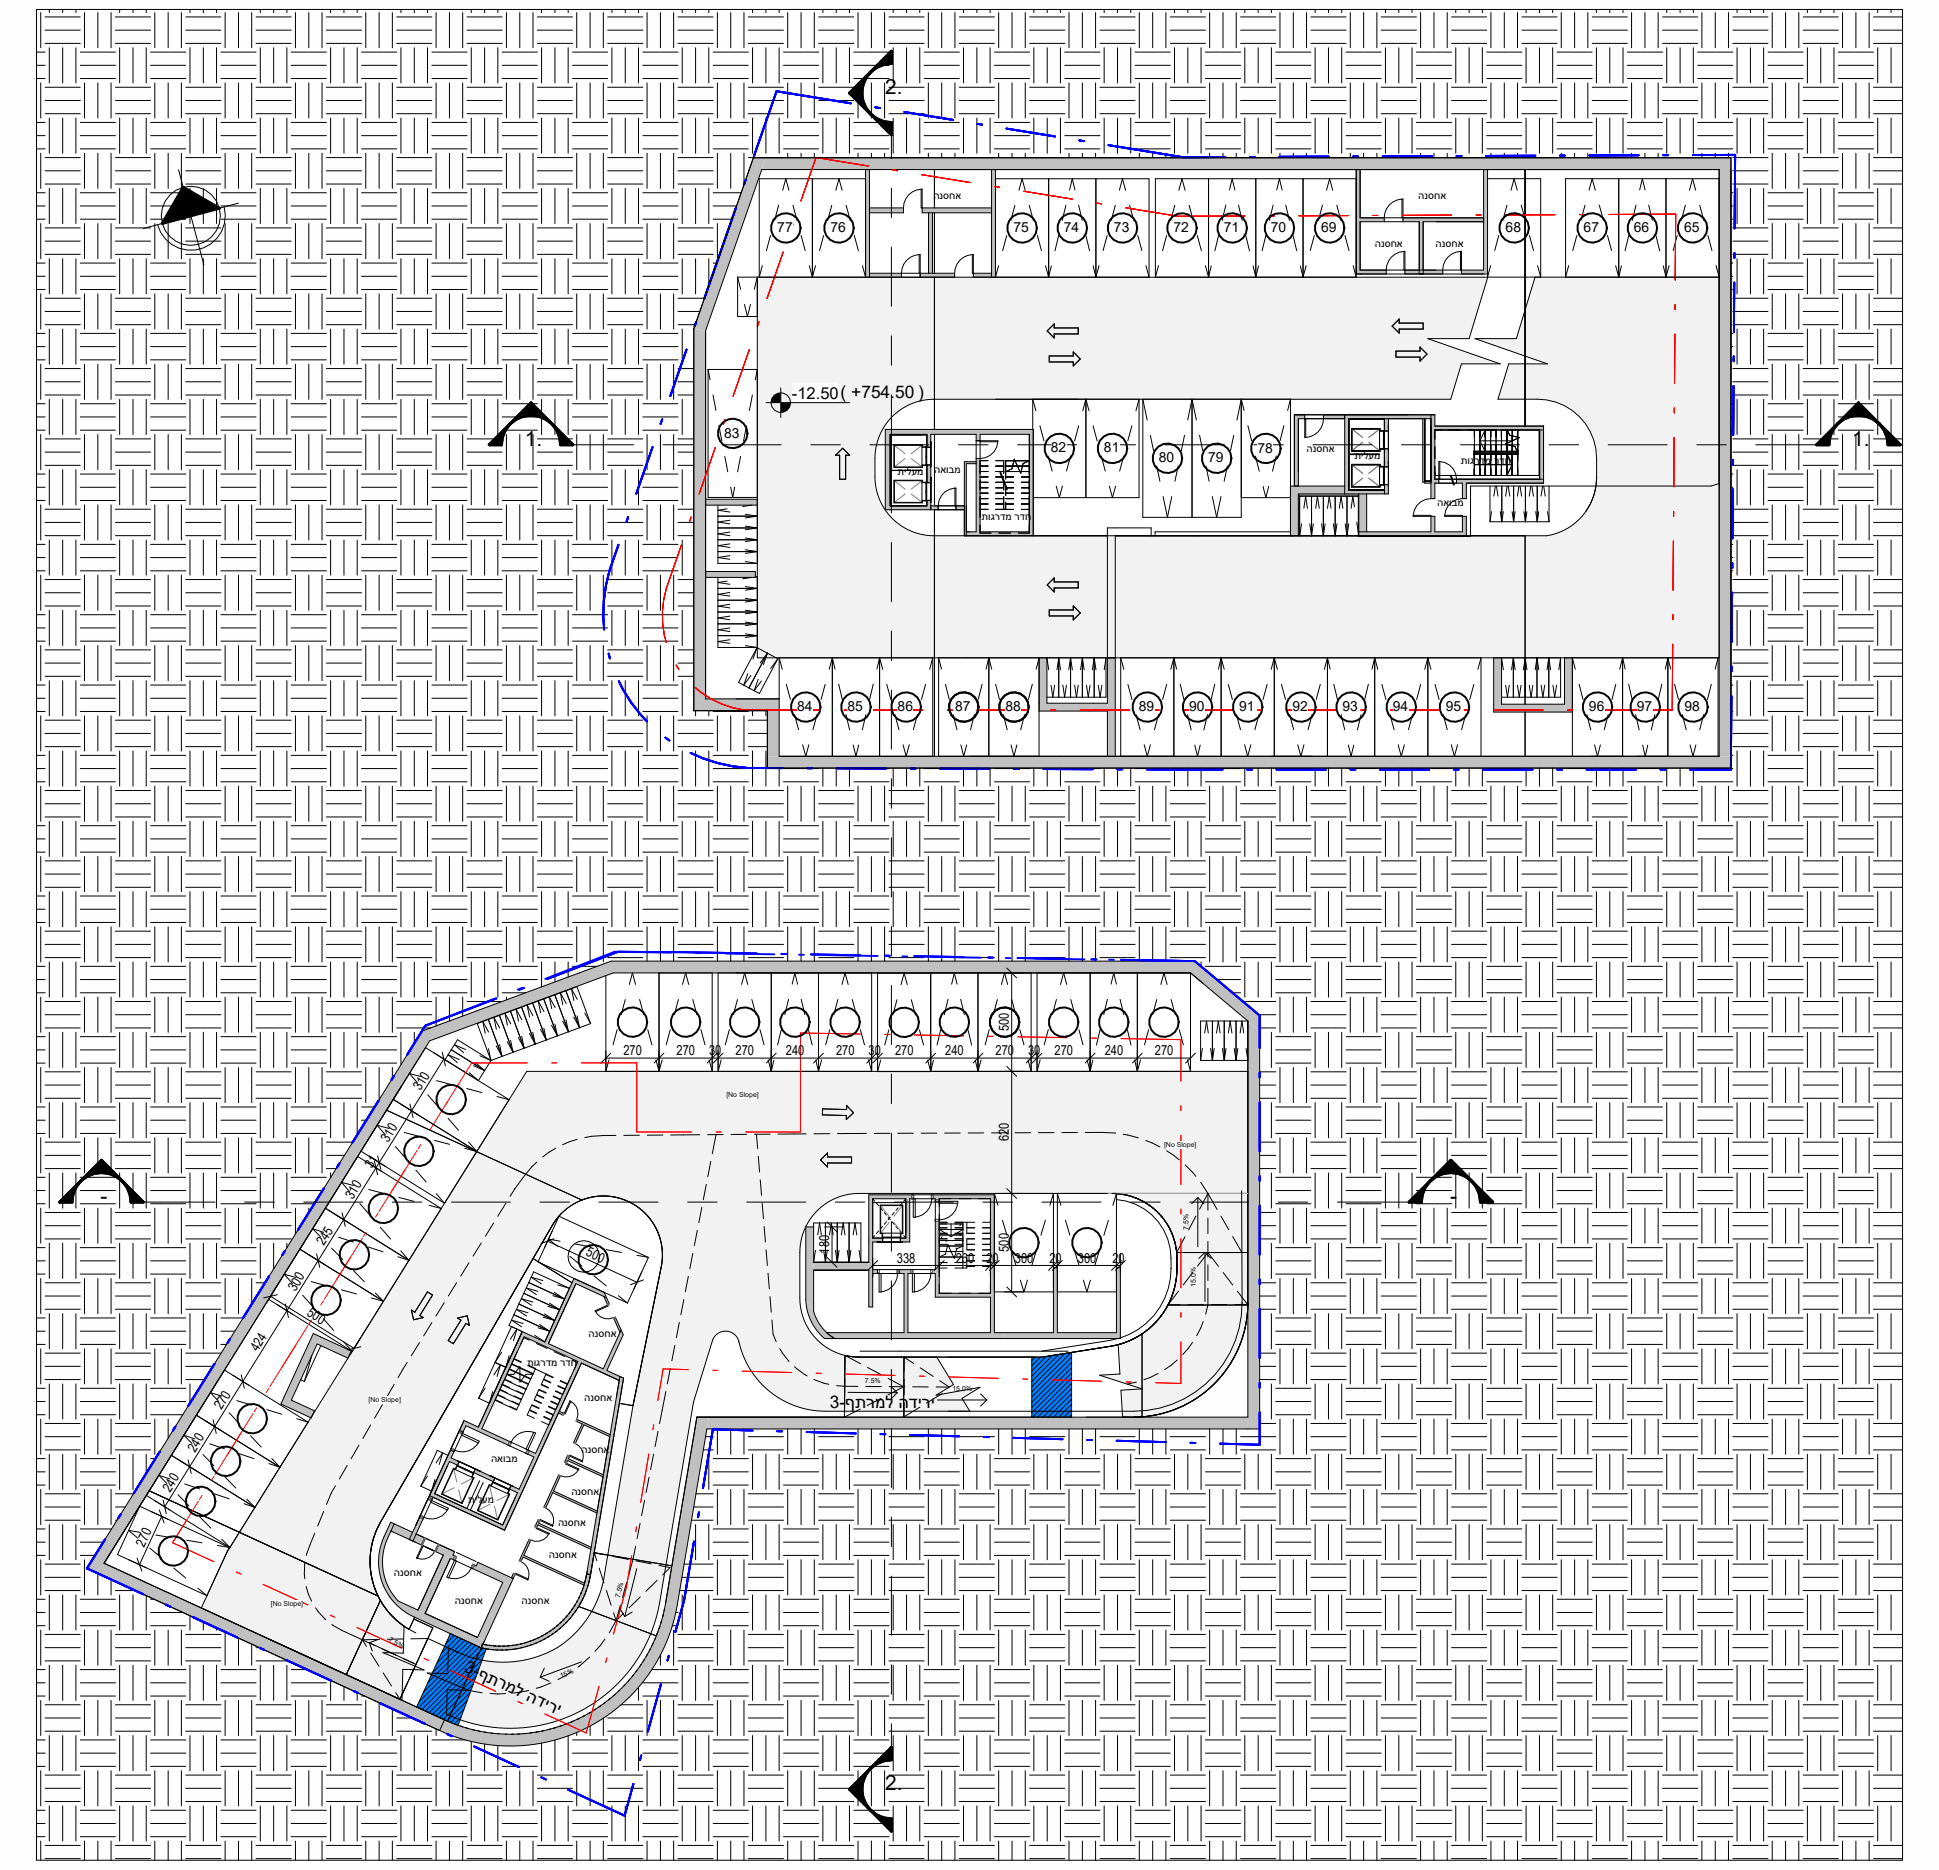
תכנית מרתף-3
מפלס: +756.54, +752.96
קנ"מ: 1 : 250