מינהל התכנון
חוק התכנון והבניה, התשכ"ה - 1965
מחוז ירושלים
הוועדה המחוזית החליטה ביום :
28/08/2025
להפקיד את התכנית
15/09/2026
יו"ר הוועדה המחוזית   תאריך

תכנית 101-1377753 נספח נוף נספח פיתוח 30/06/2026 13:18:13

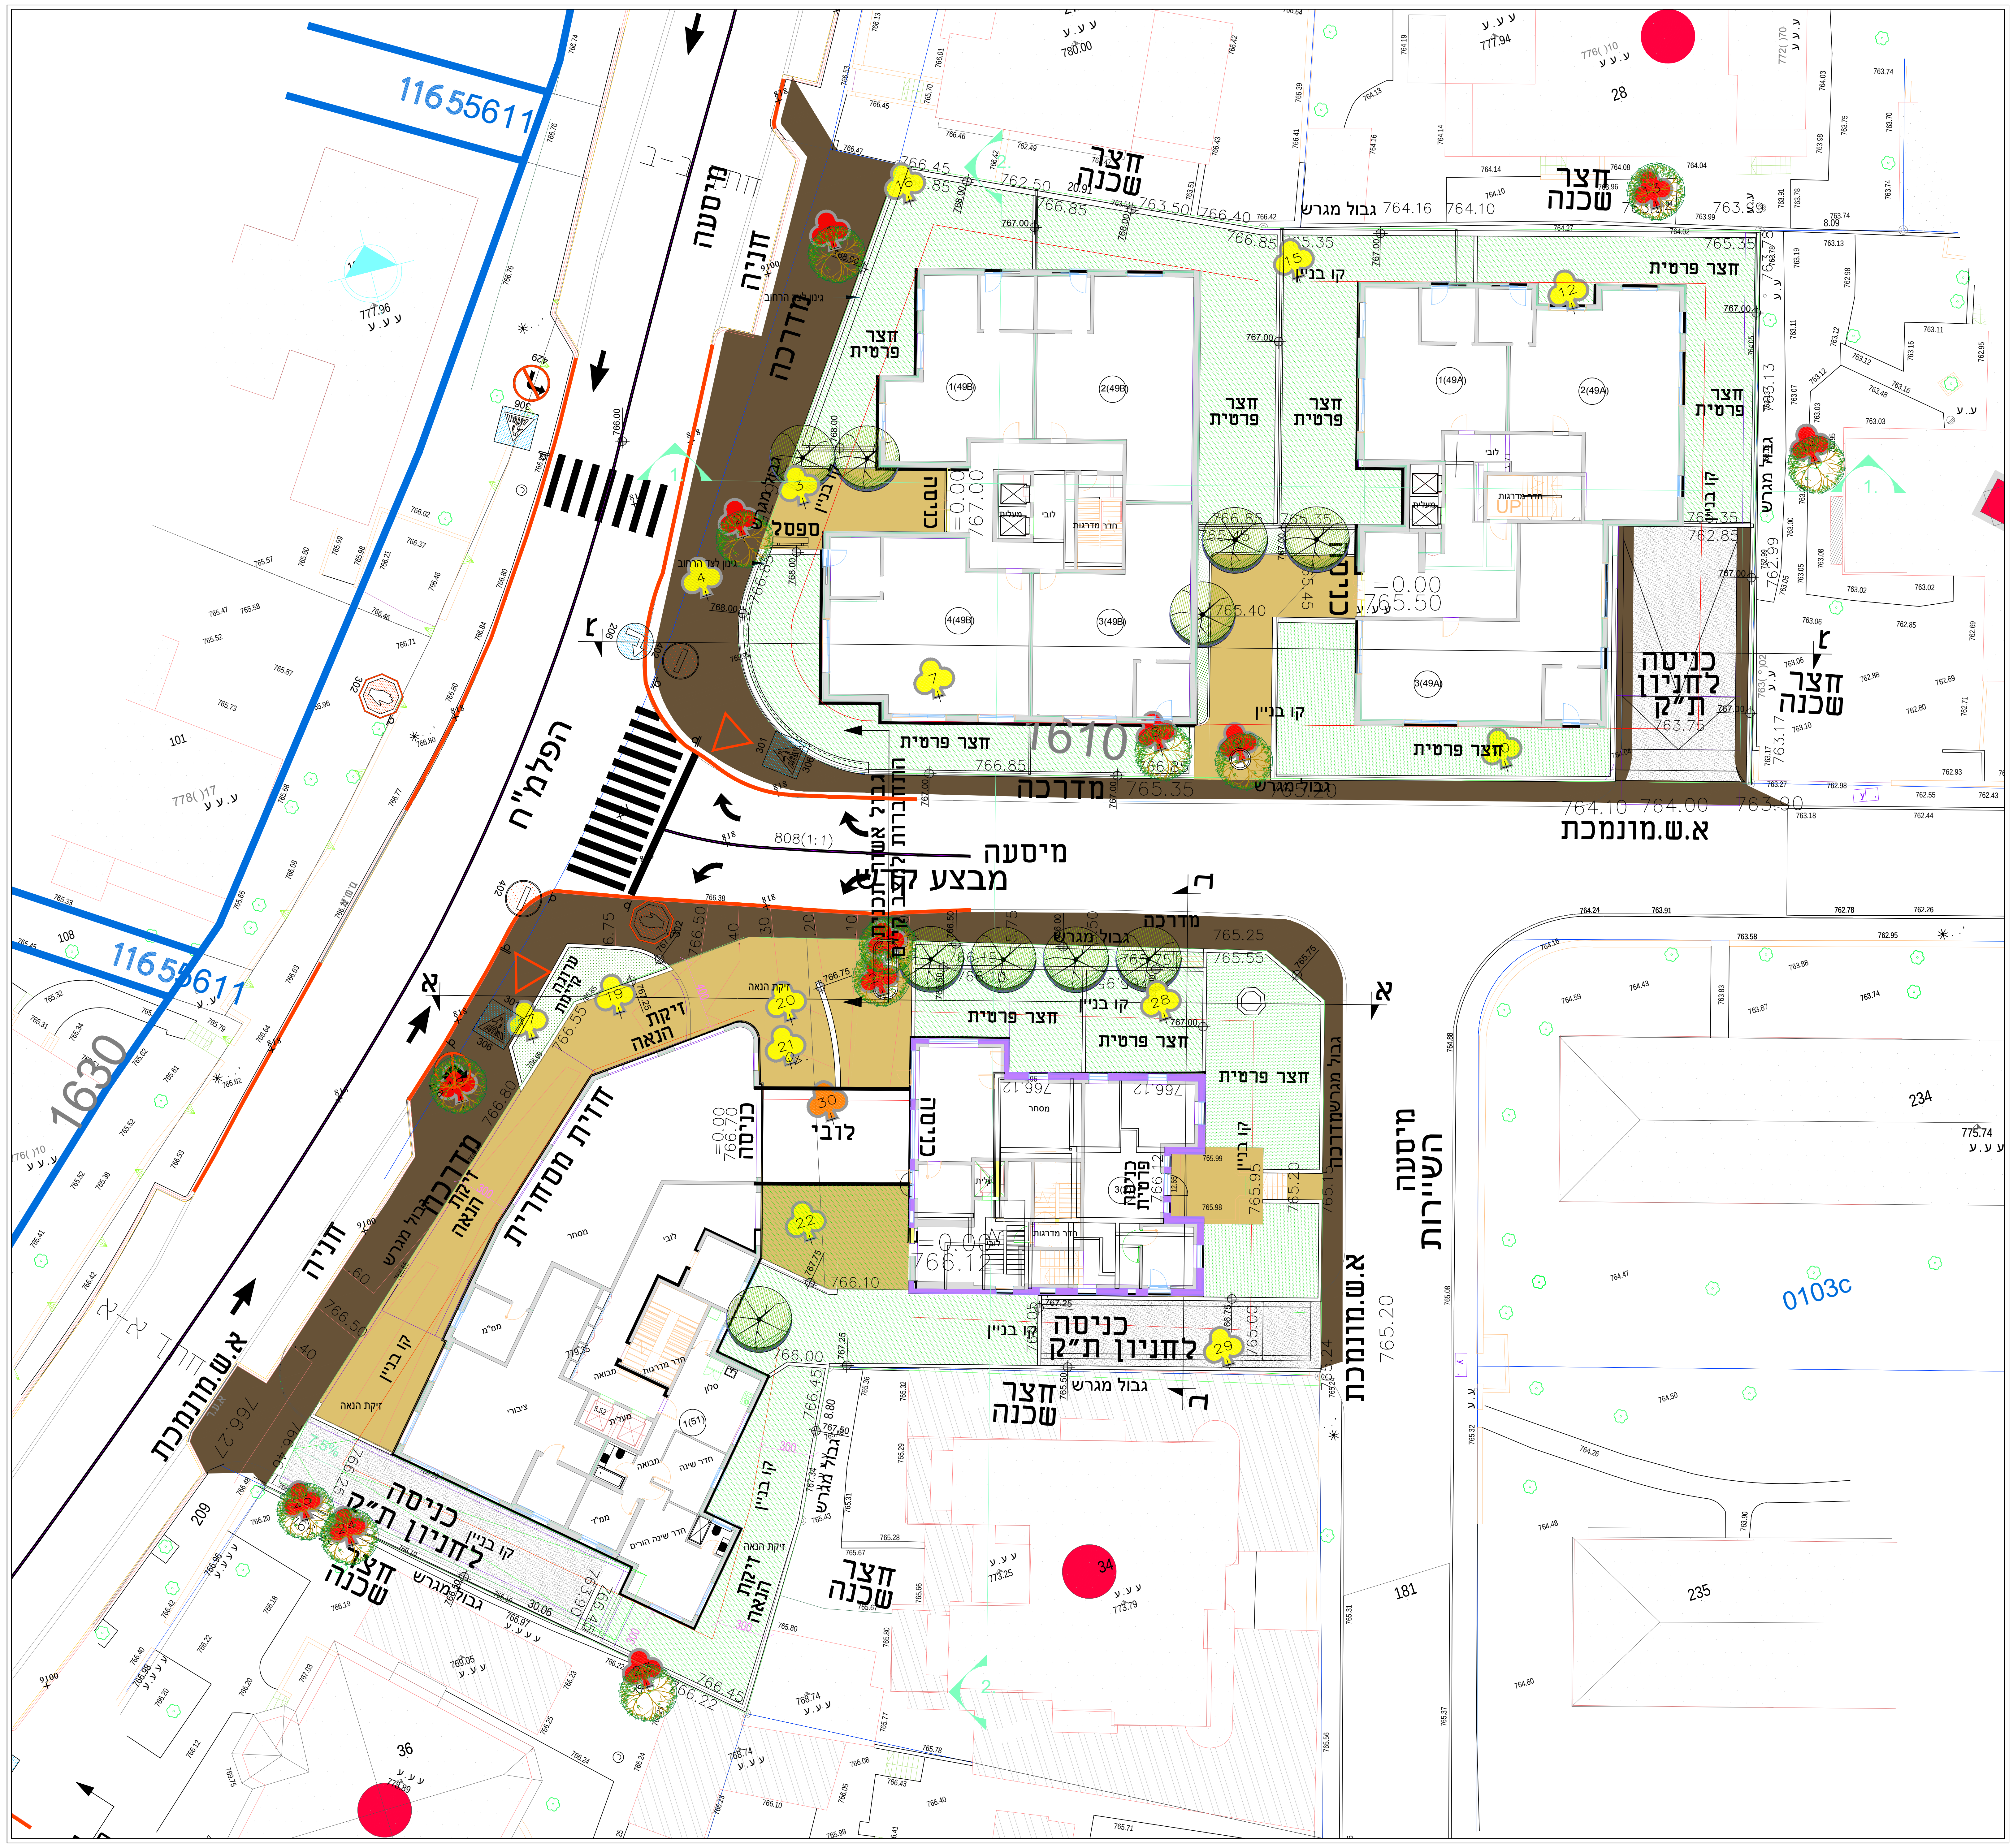
11655611
1630
1610
הפלמ"ח
מיסעה
חניה
מדרכה
חצר פרטית
חצר שכנה
ספסל
לובי
כניסה
כניסה לחניון ת"ק
קו בניין
גבול מגרש
א.ש.מונמכת
מיסעה השיירות
זיקת הנאה
חזית מסחרית
ערוגה קיימת
מבצע קדש
808(1:1)
0103c
28
36
101
108
181
209
234
235
1(49ח)
2(49ח)
3(49ח)
4(49ח)
1(49א)
2(49א)
3(49א)
=0.00
767.00
765.50
766.12
765.35
766.85
765.40
764.10
764.00
763.75
765.25
765.55
766.10
766.00
766.45
766.22
764.16
763.50
766.40
762.85

שם הנספח

נספח לתכנית מס'	101-1377753
שם התכנית	התחדשות עירונית הפלמ"ח 51,49 והשיירות 2
גליון 1 מתוך 2	
תחולה	נספח נופי
תיאור	תכנית פיתוח
תאריך עריכת הנספח	30/06/2026
קנ"מ	1:125

תרשימים נוספים	קנ"מ
שם תרשים	
שם תרשים	
שם תרשים	

שמות וחתימות:

עורך הנספח	שם:	יונתן ליכט
	תאגיד:	יונתן ליכט - אדריכל נוף

מקרא

עץ קיים לשימור	●
עץ לנטיעה	●
גינון פרטי	🟩
גינון ציבורי	▨
ריצוף בשטח נשותף	🟨
מרדכה	🟫
קיר מתוכנן	═
אבן שפה	═
מפלס 0.0	=0.00 766.12
קוי גובה	6.25

גליון פיתוח
קנ"מ : 1:125
תאריך עידכון: 30.06.2026