מינהל התכנון
חוק התכנון והבניה, התשכ"ה - 1965
מחוז ירושלים
תכנית 101-1377753 נספח תנועה 06/08/2026 11:57:38
הוועדה המחוזית החליטה ביום :
28/08/2025
להפקיד את התכנית
15/09/2026
תאריך יו"ר הוועדה המחוזית

נספח תנועה
תכנית מס׳: 101-1377753
התחדשות עירונית הפלמ״ח 49, והשיירות 2

תחולה	
תאריך עריכת הנספח	31.07.2026
קנ״מ	1:250

שמות וחתימות:

עורך הנספח	שם: י.ג יעוץ הנדסי

מקרא:

גבול תכנית	▬
חניית אופנוע	🟥
חניית אופניים	🟩
אבן שפה קיים	─
מדרכה בחניון	━

תרשים סביבה:

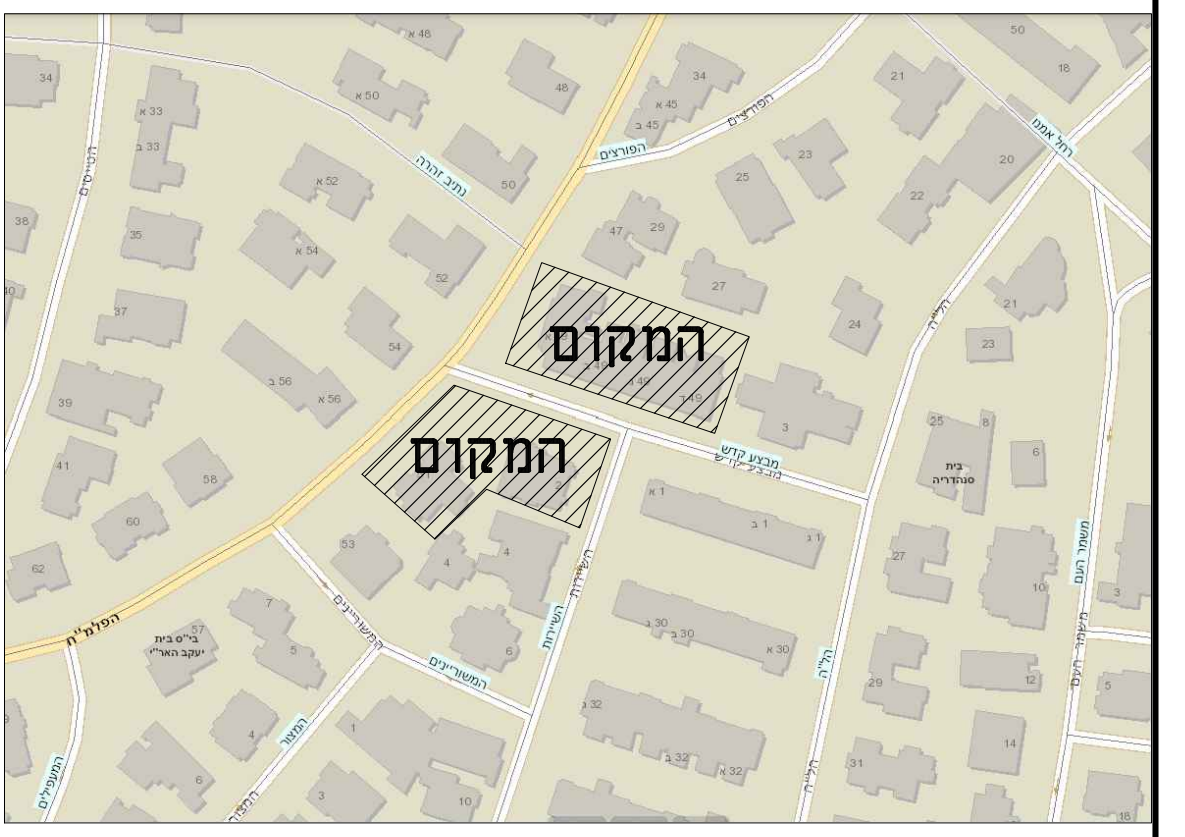

י.ג <<<
תכנון תנועה וכבישים
077-9103157 052-4155774
יואל משה סלומון 9, ירושלים
office@ygyg.co.il
www.ygyg.co.il

קומת קרקע

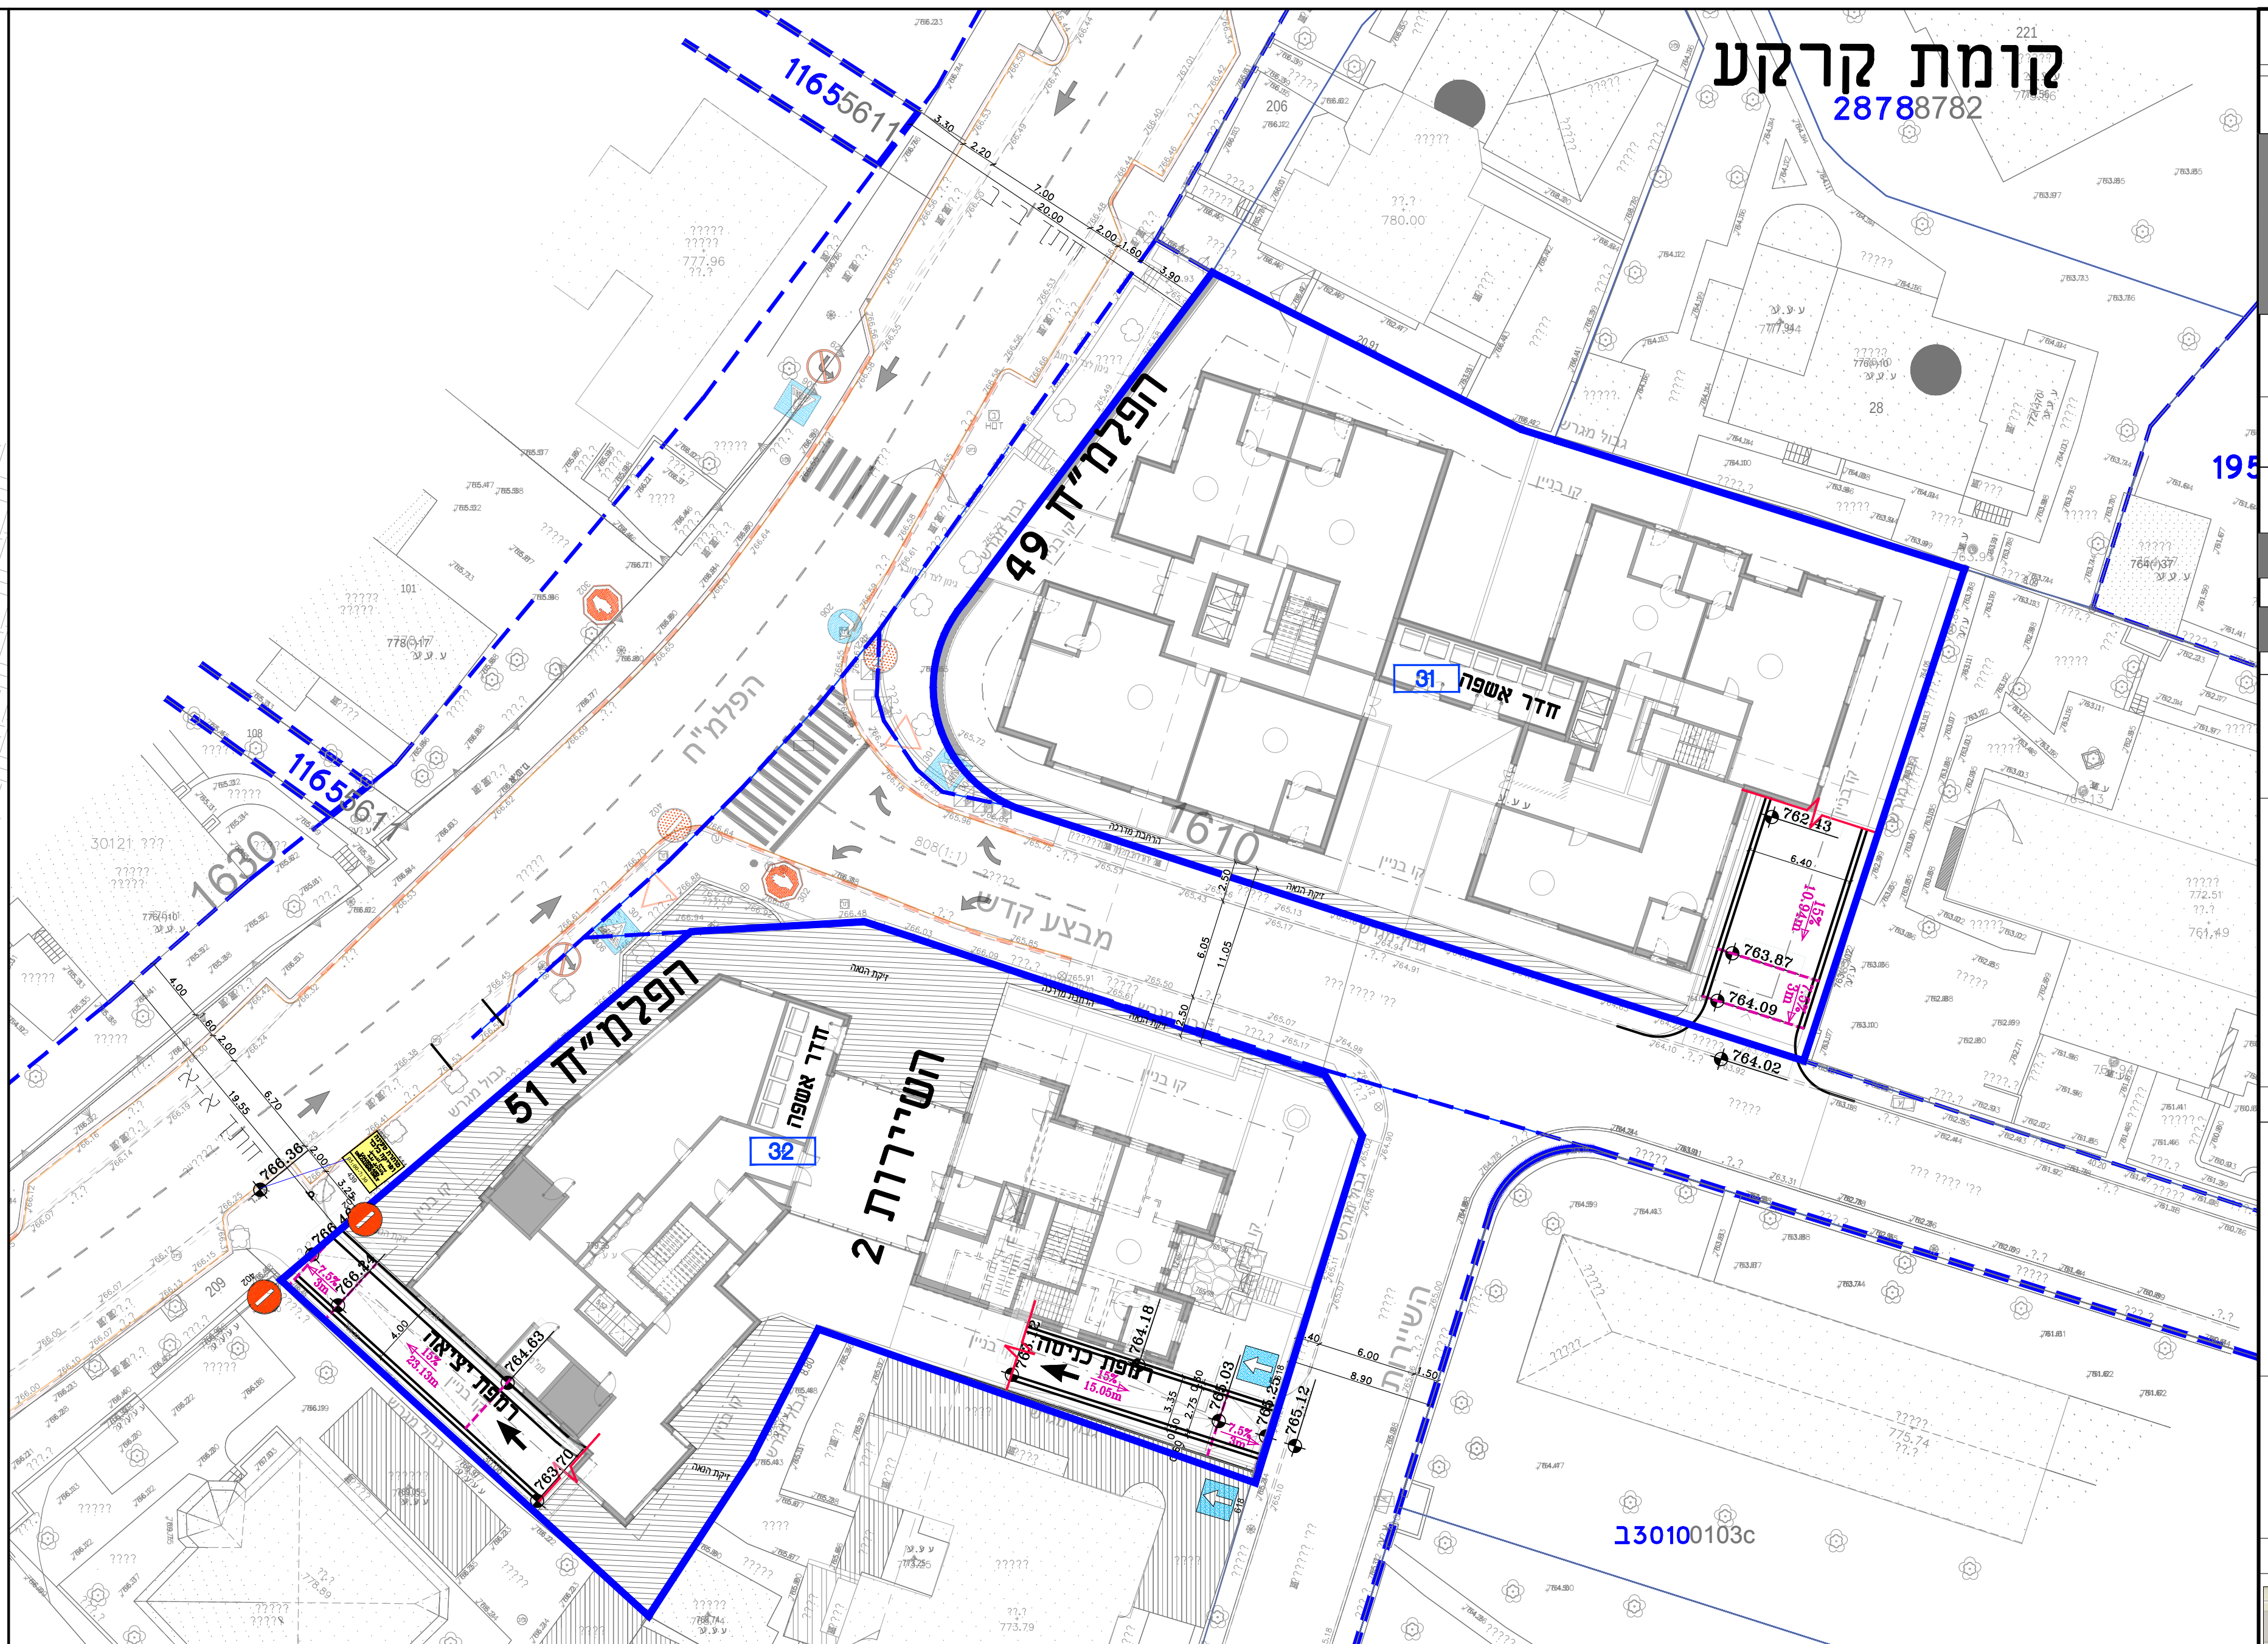

קומה -2

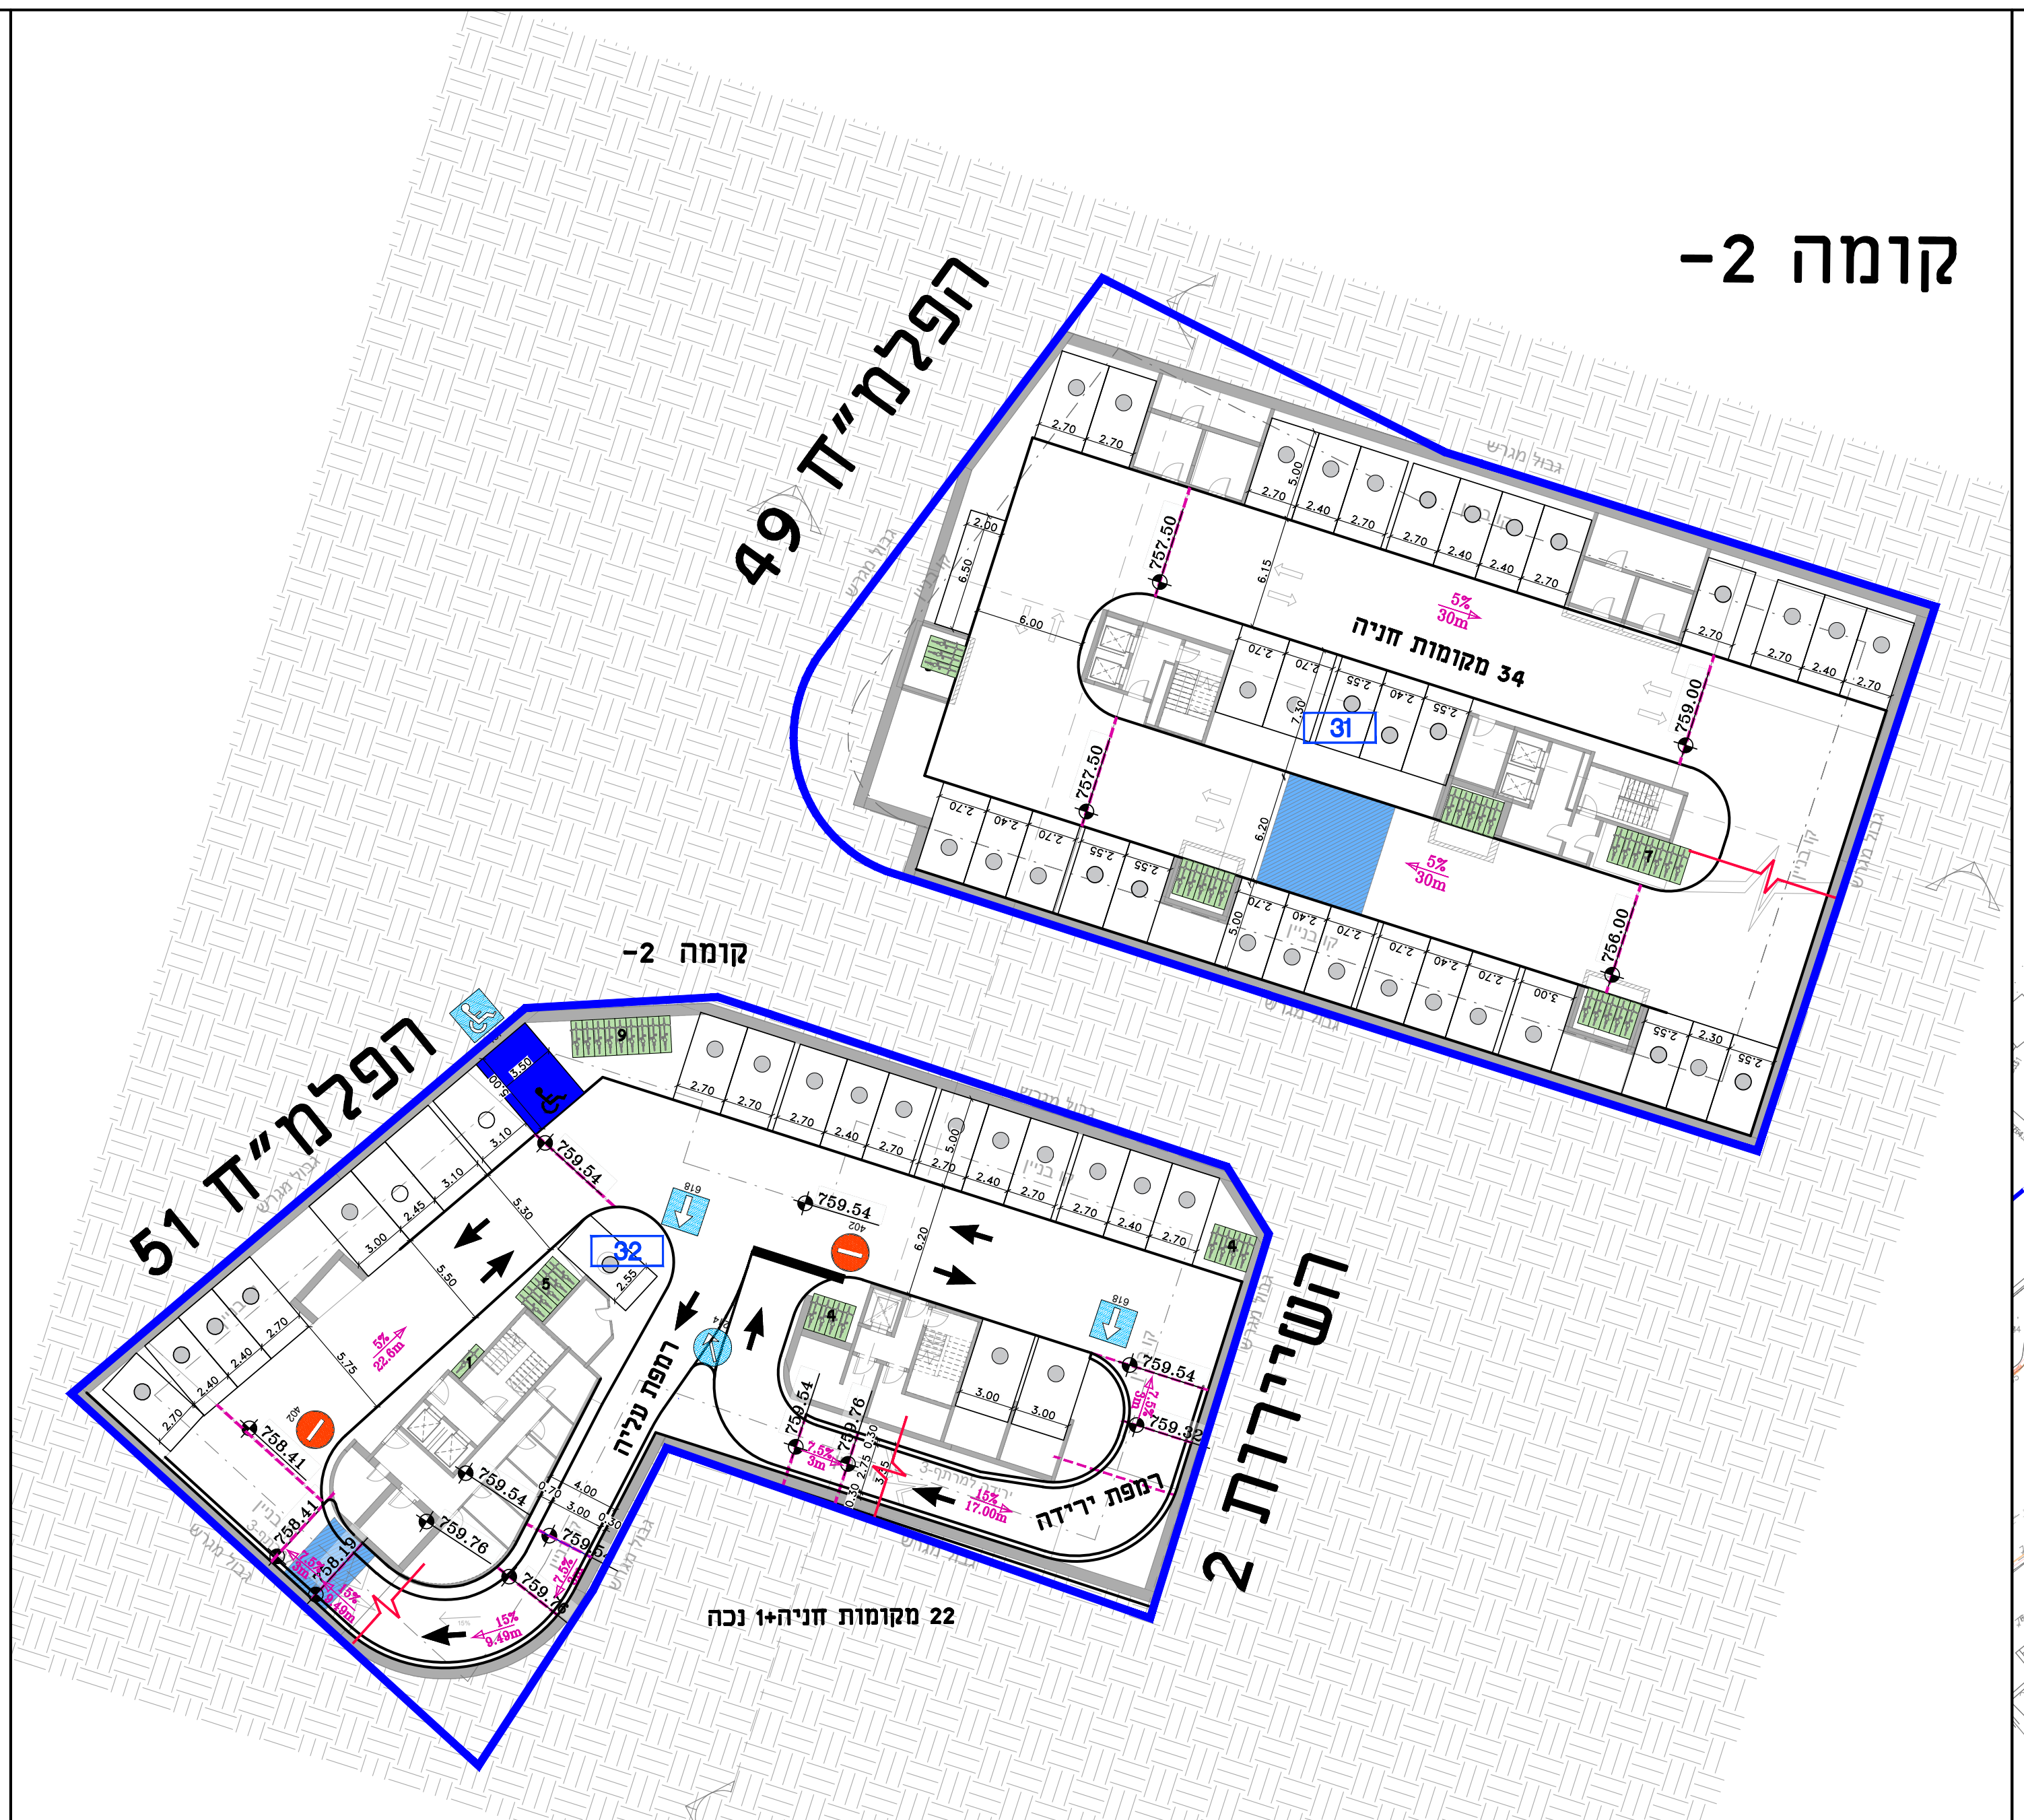

קומה -4

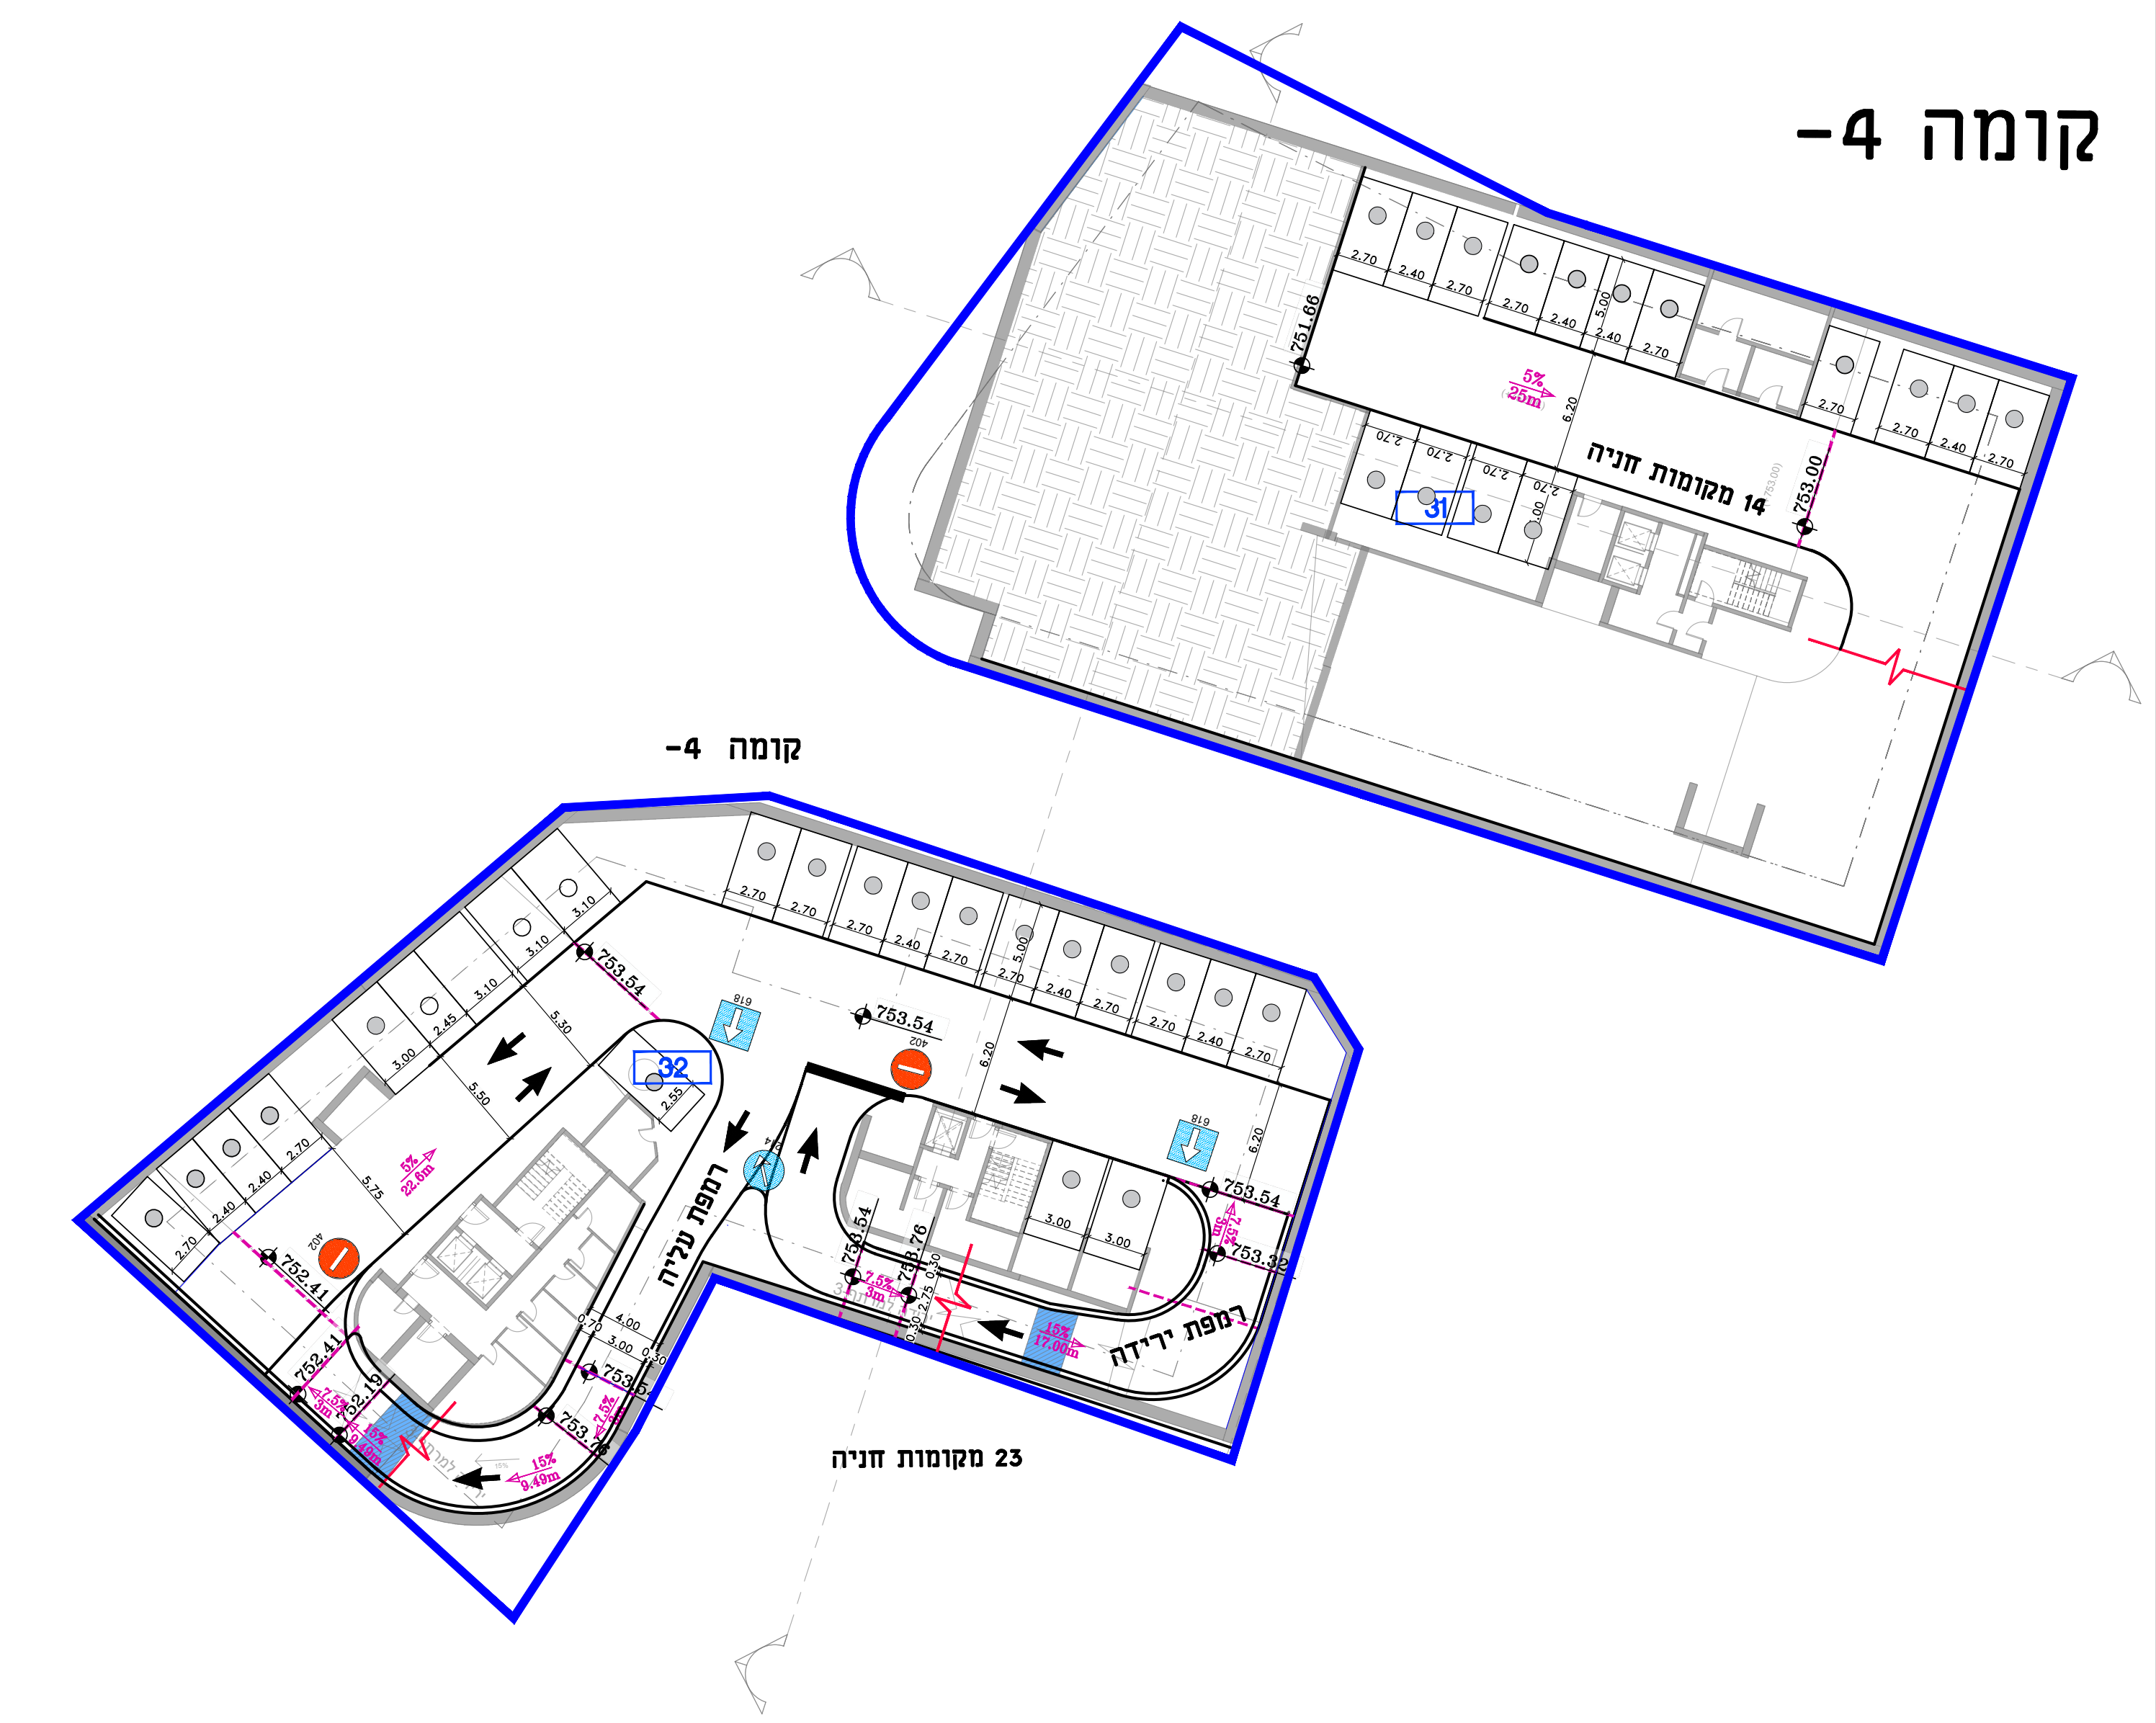

חתכים טיפוסיים
קנ״מ 1:100

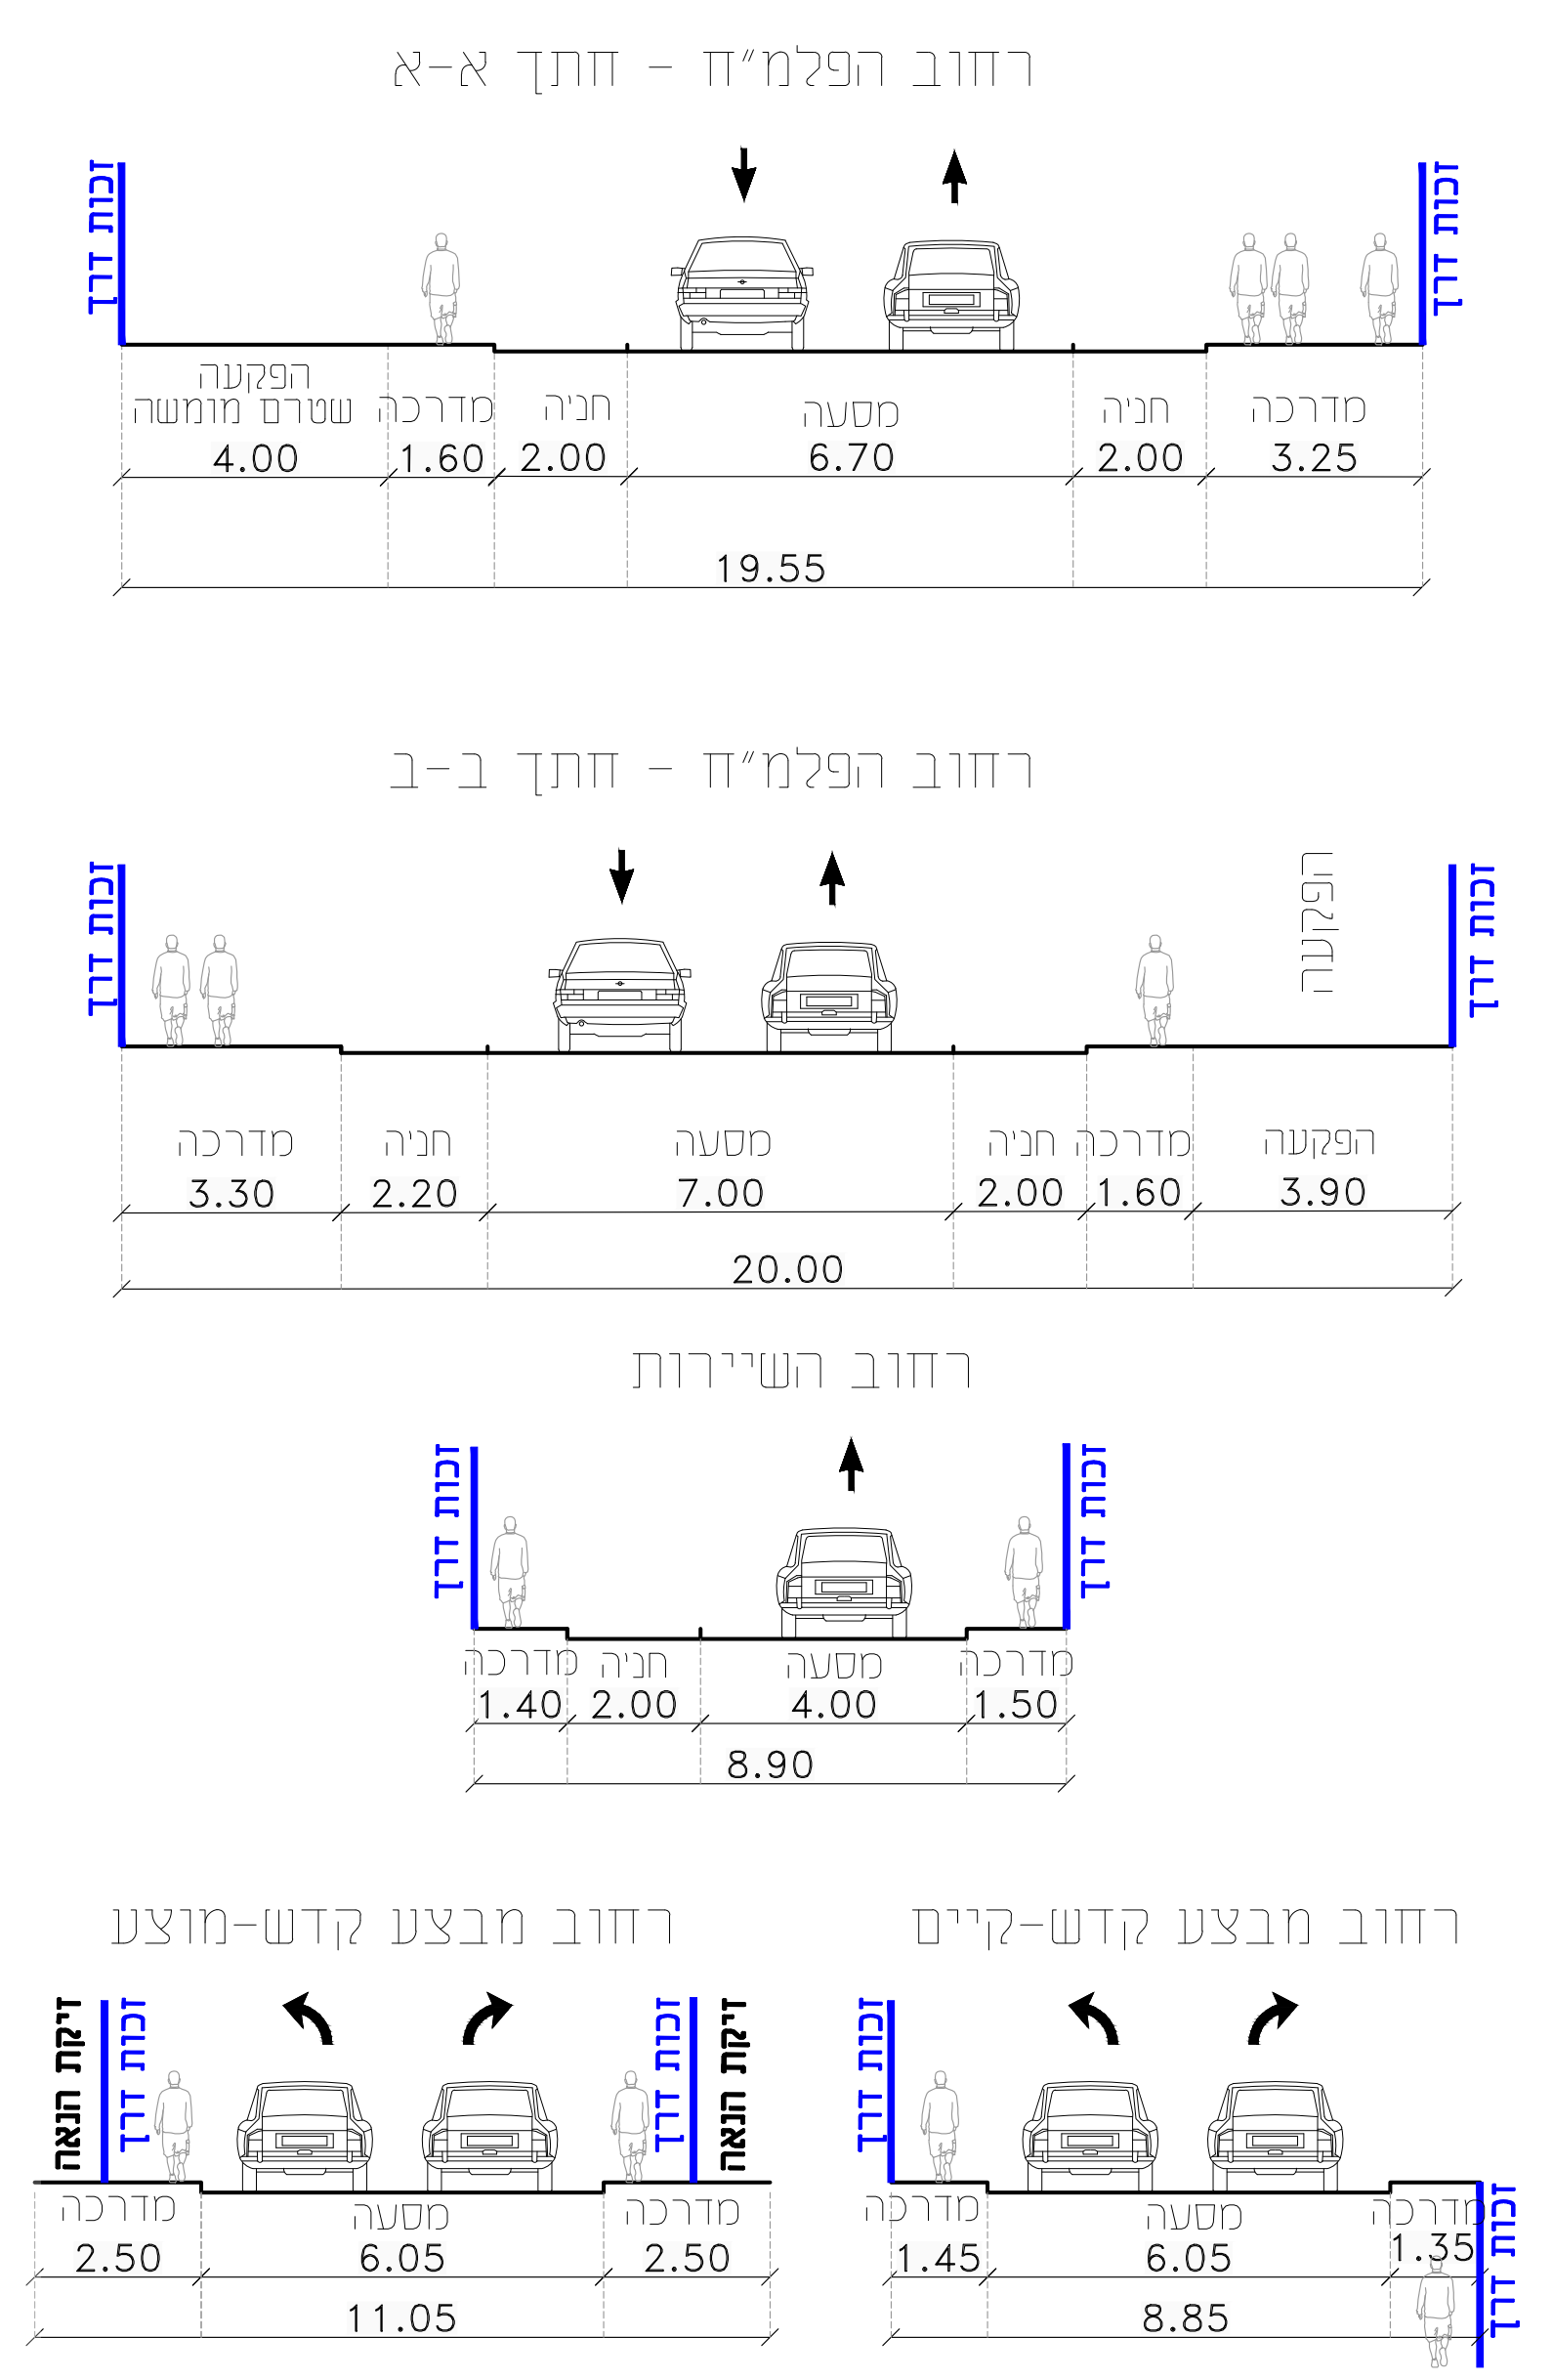

קומה -1

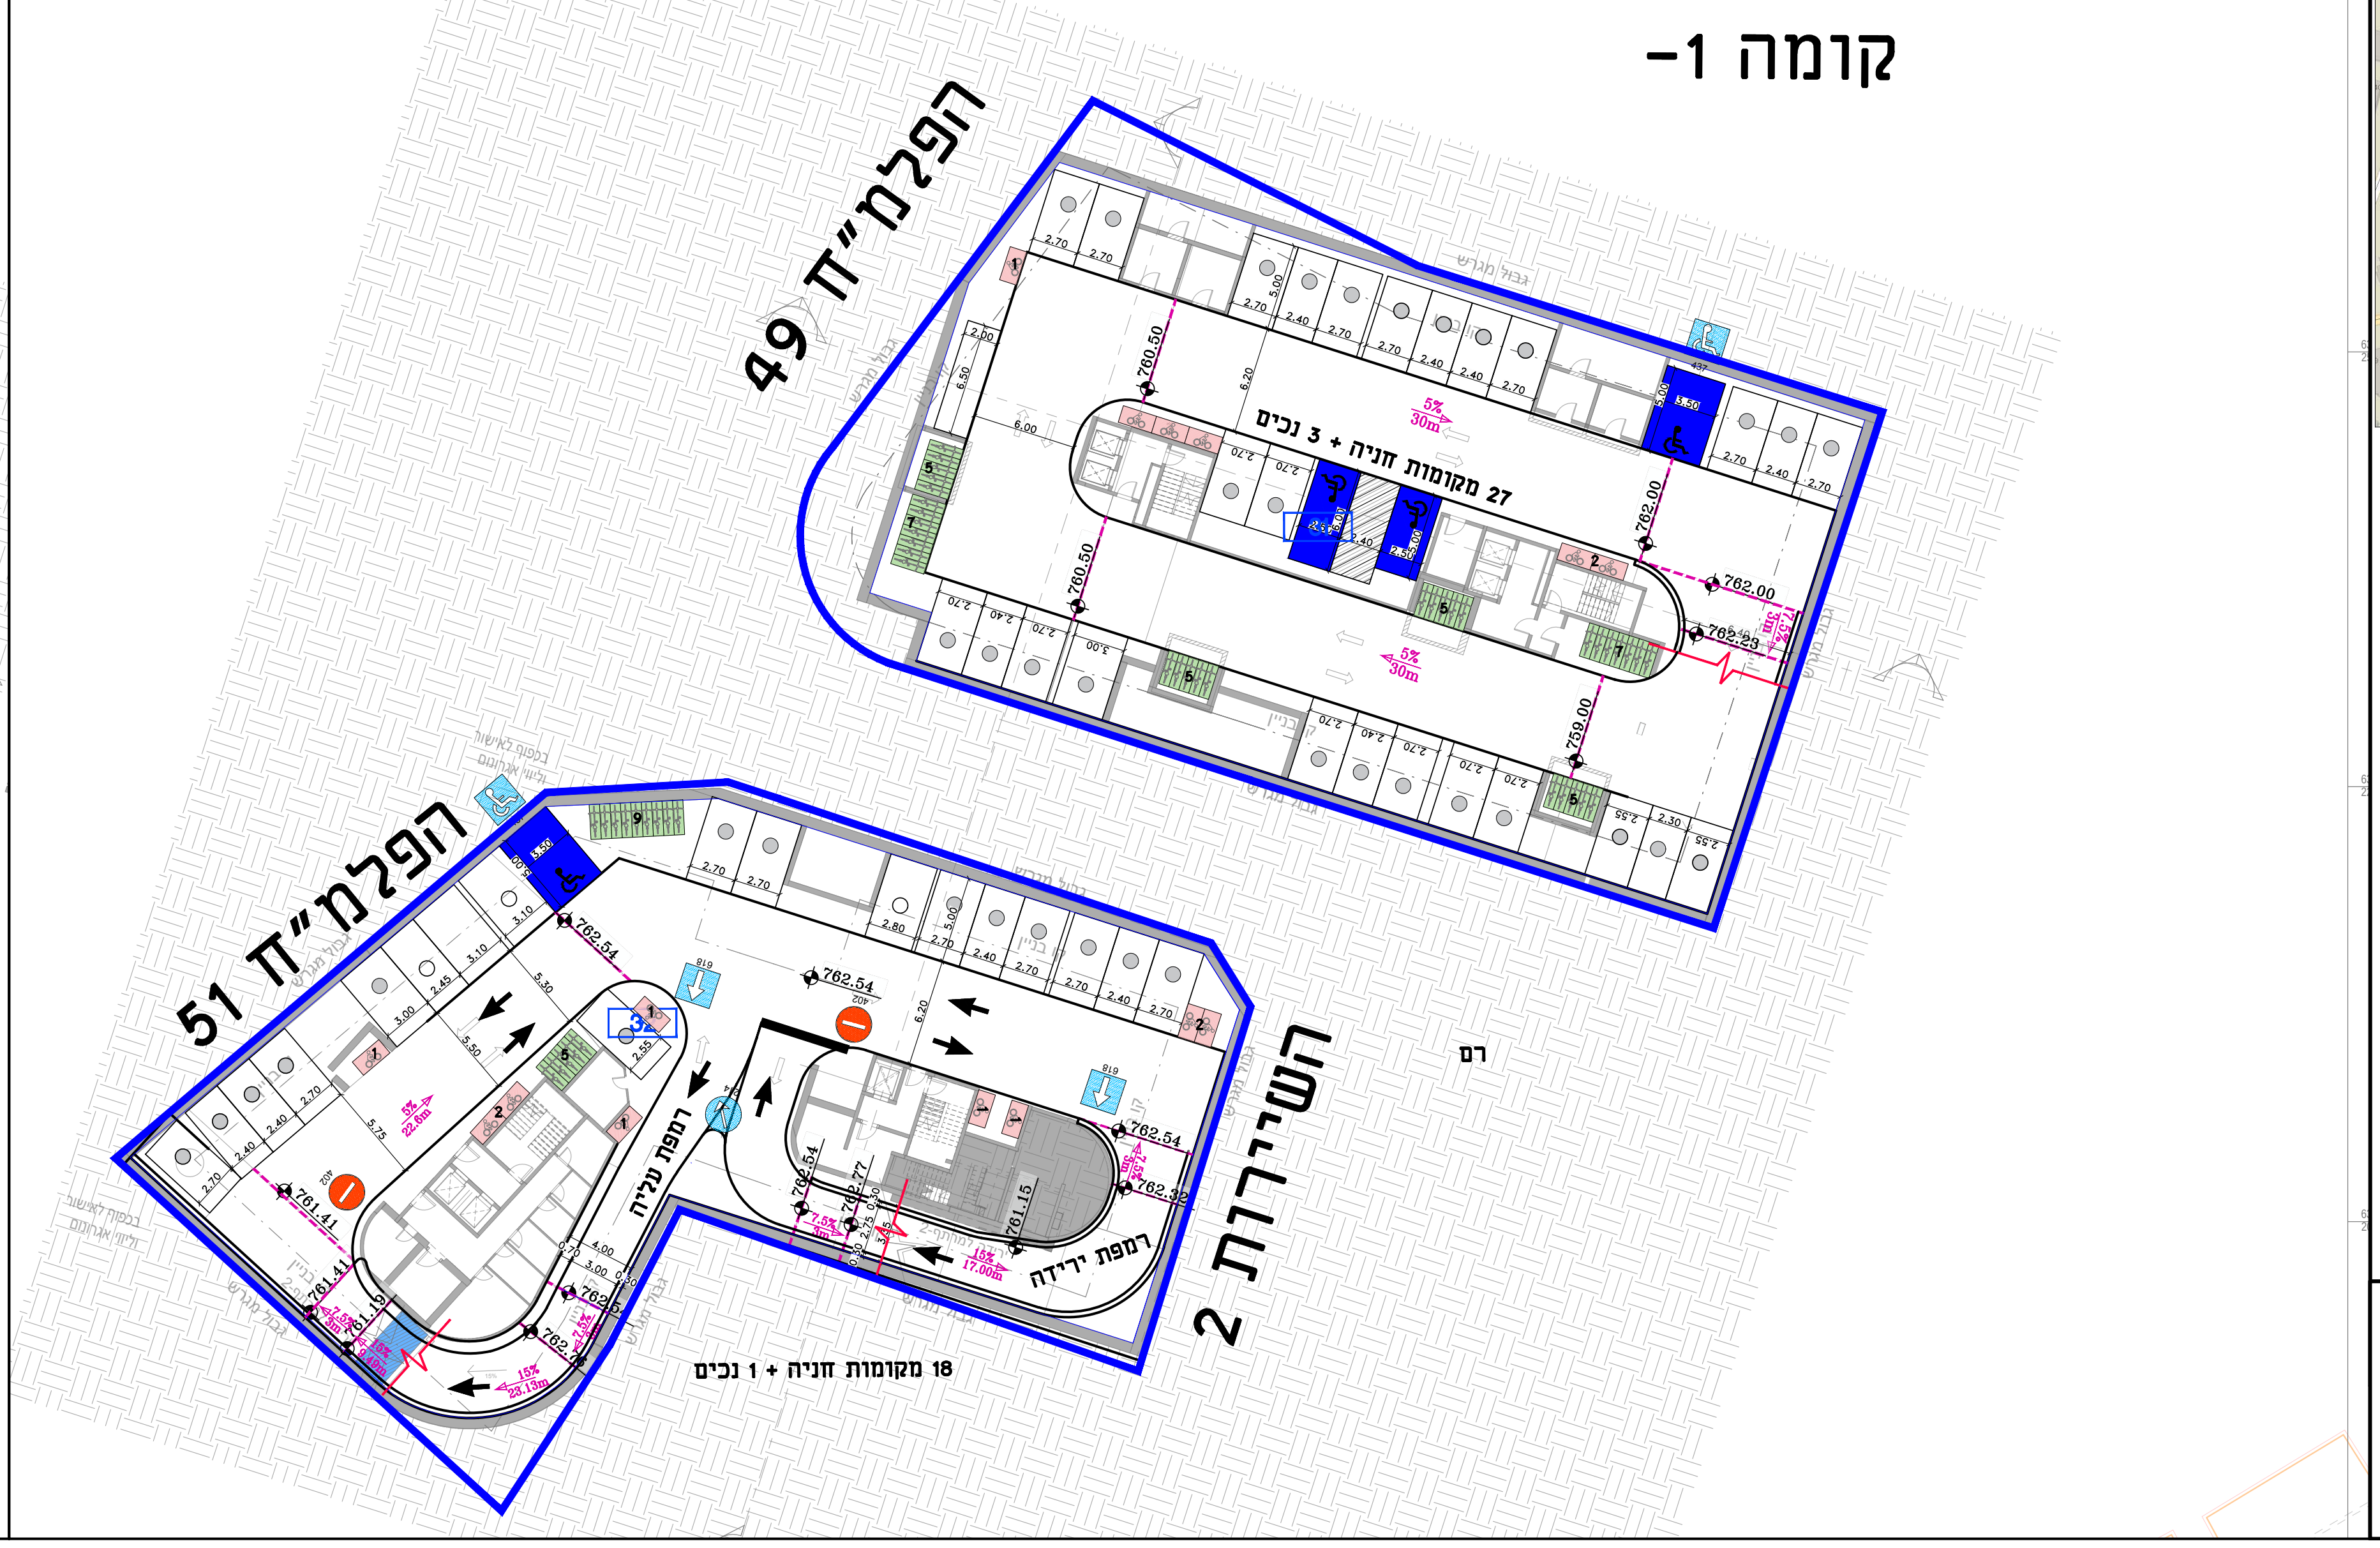

קומה -3

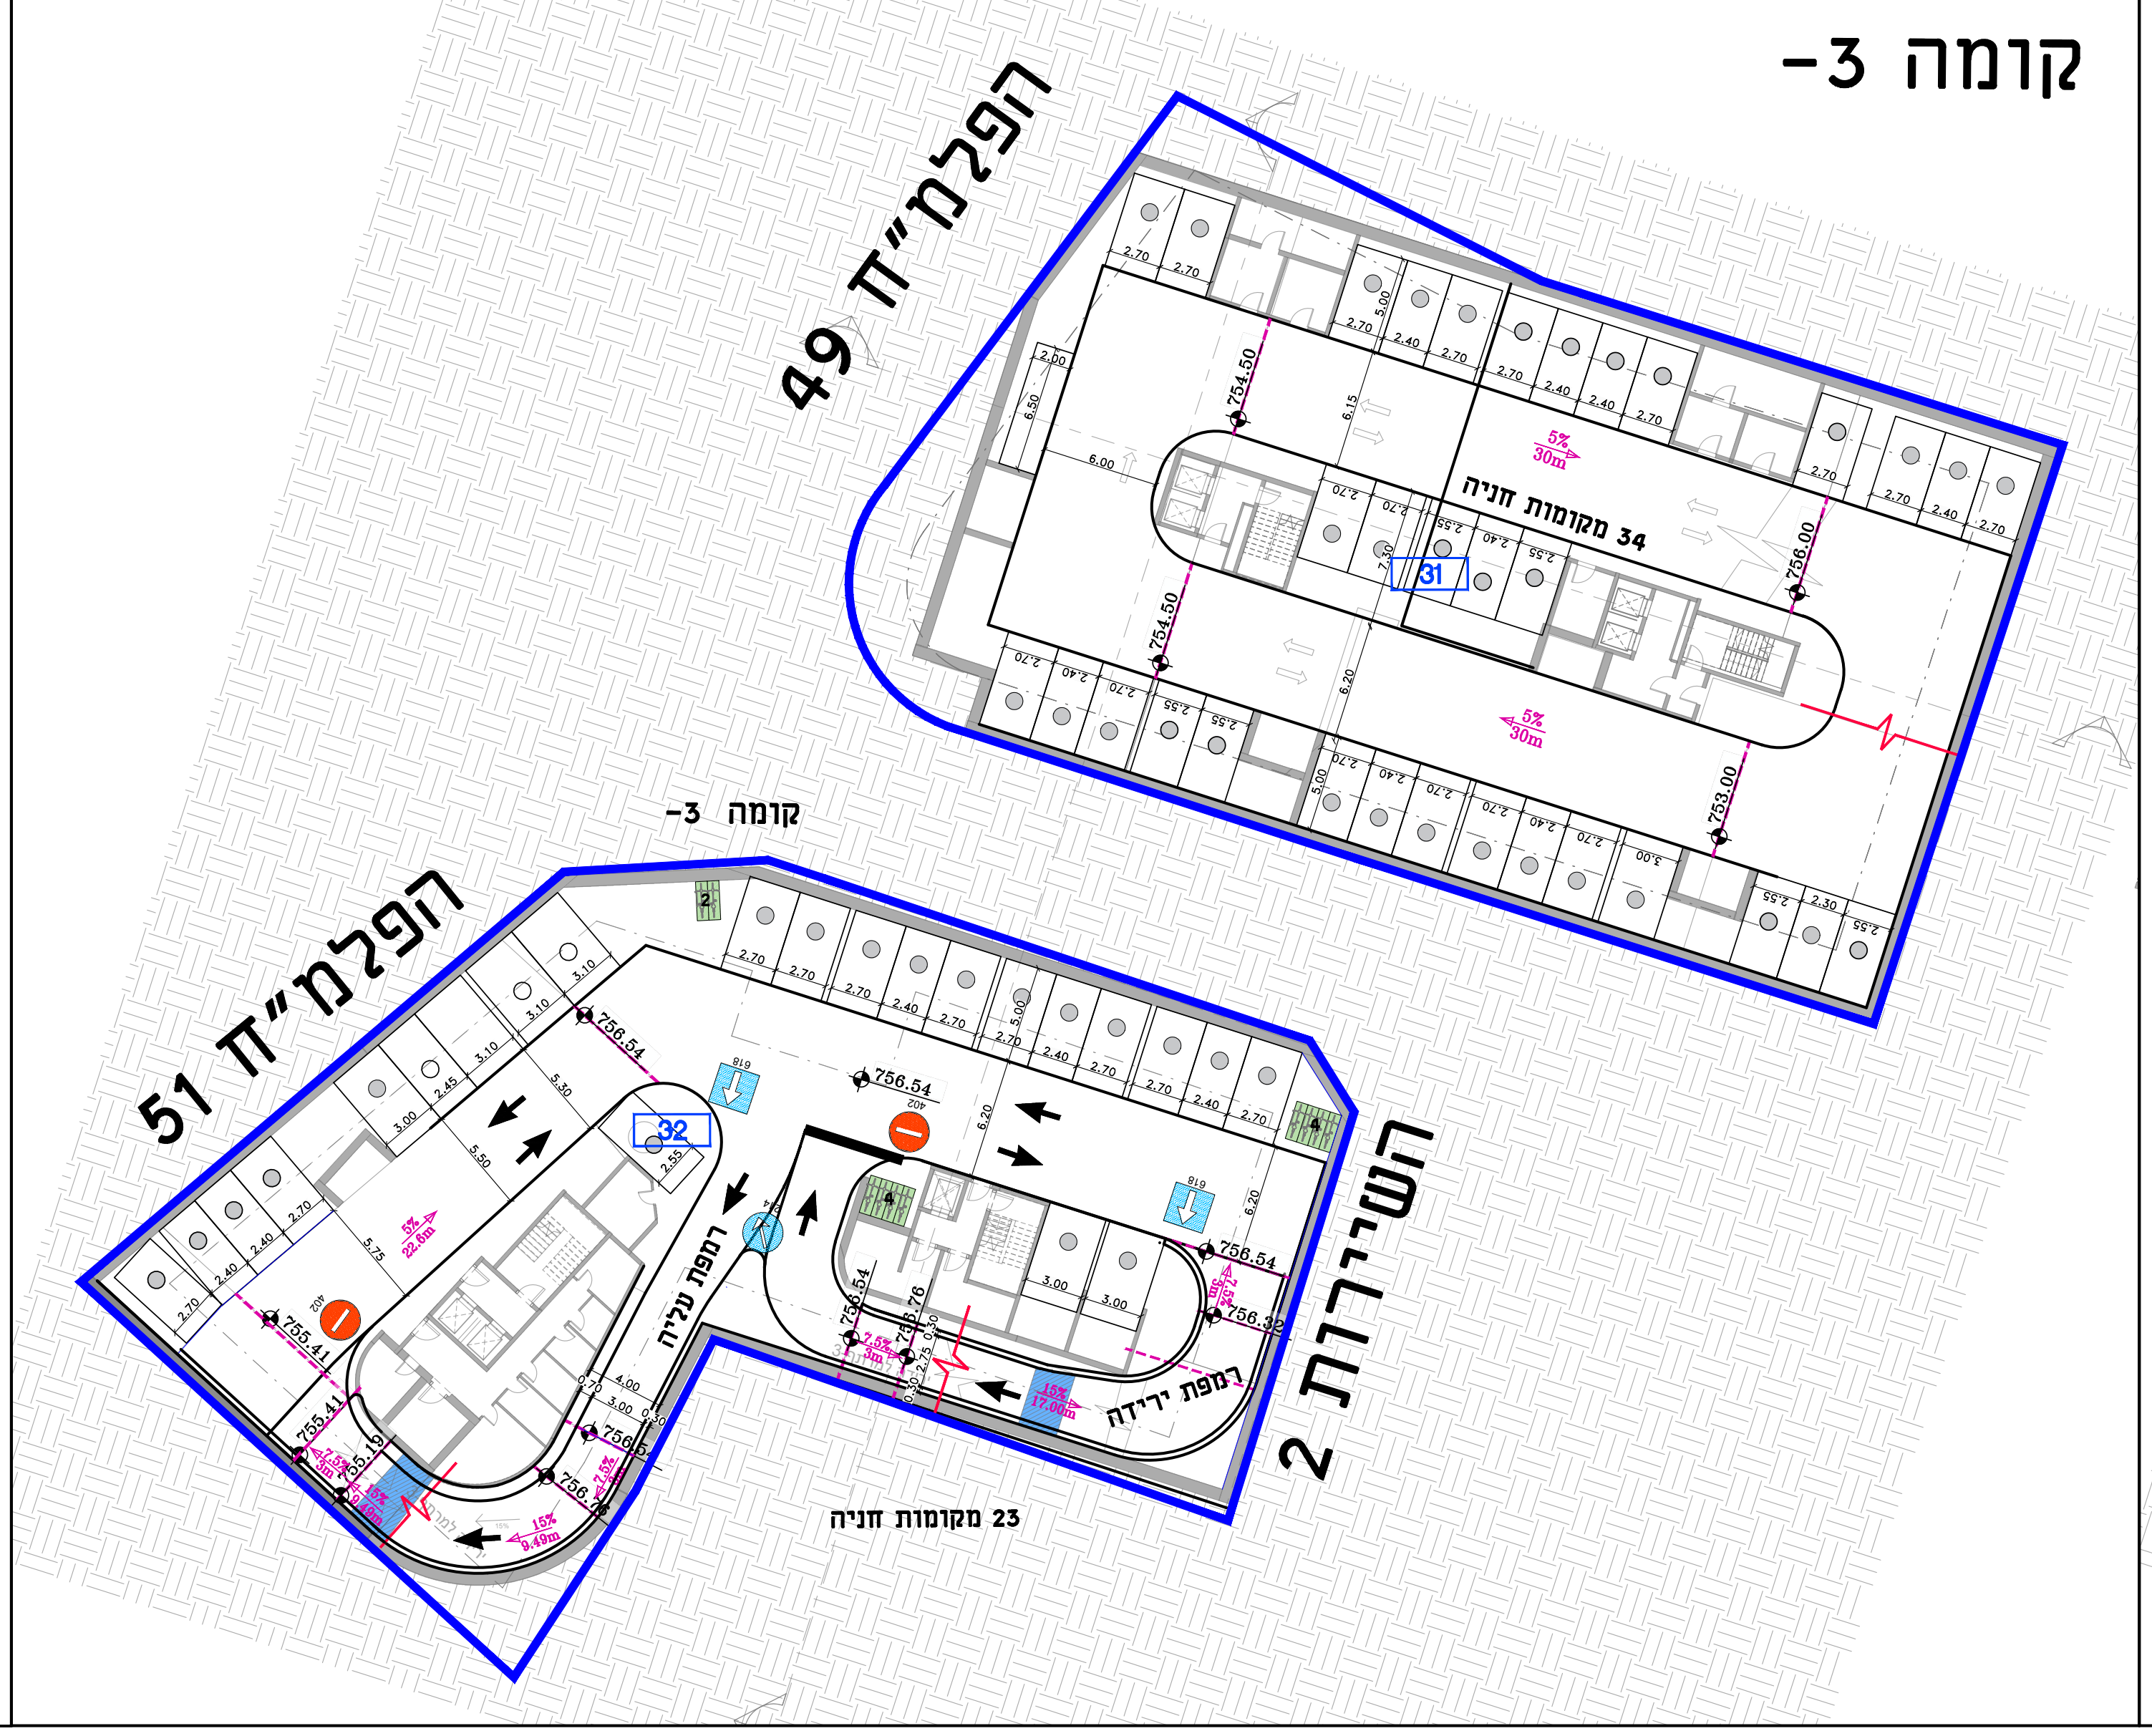

קומה -5

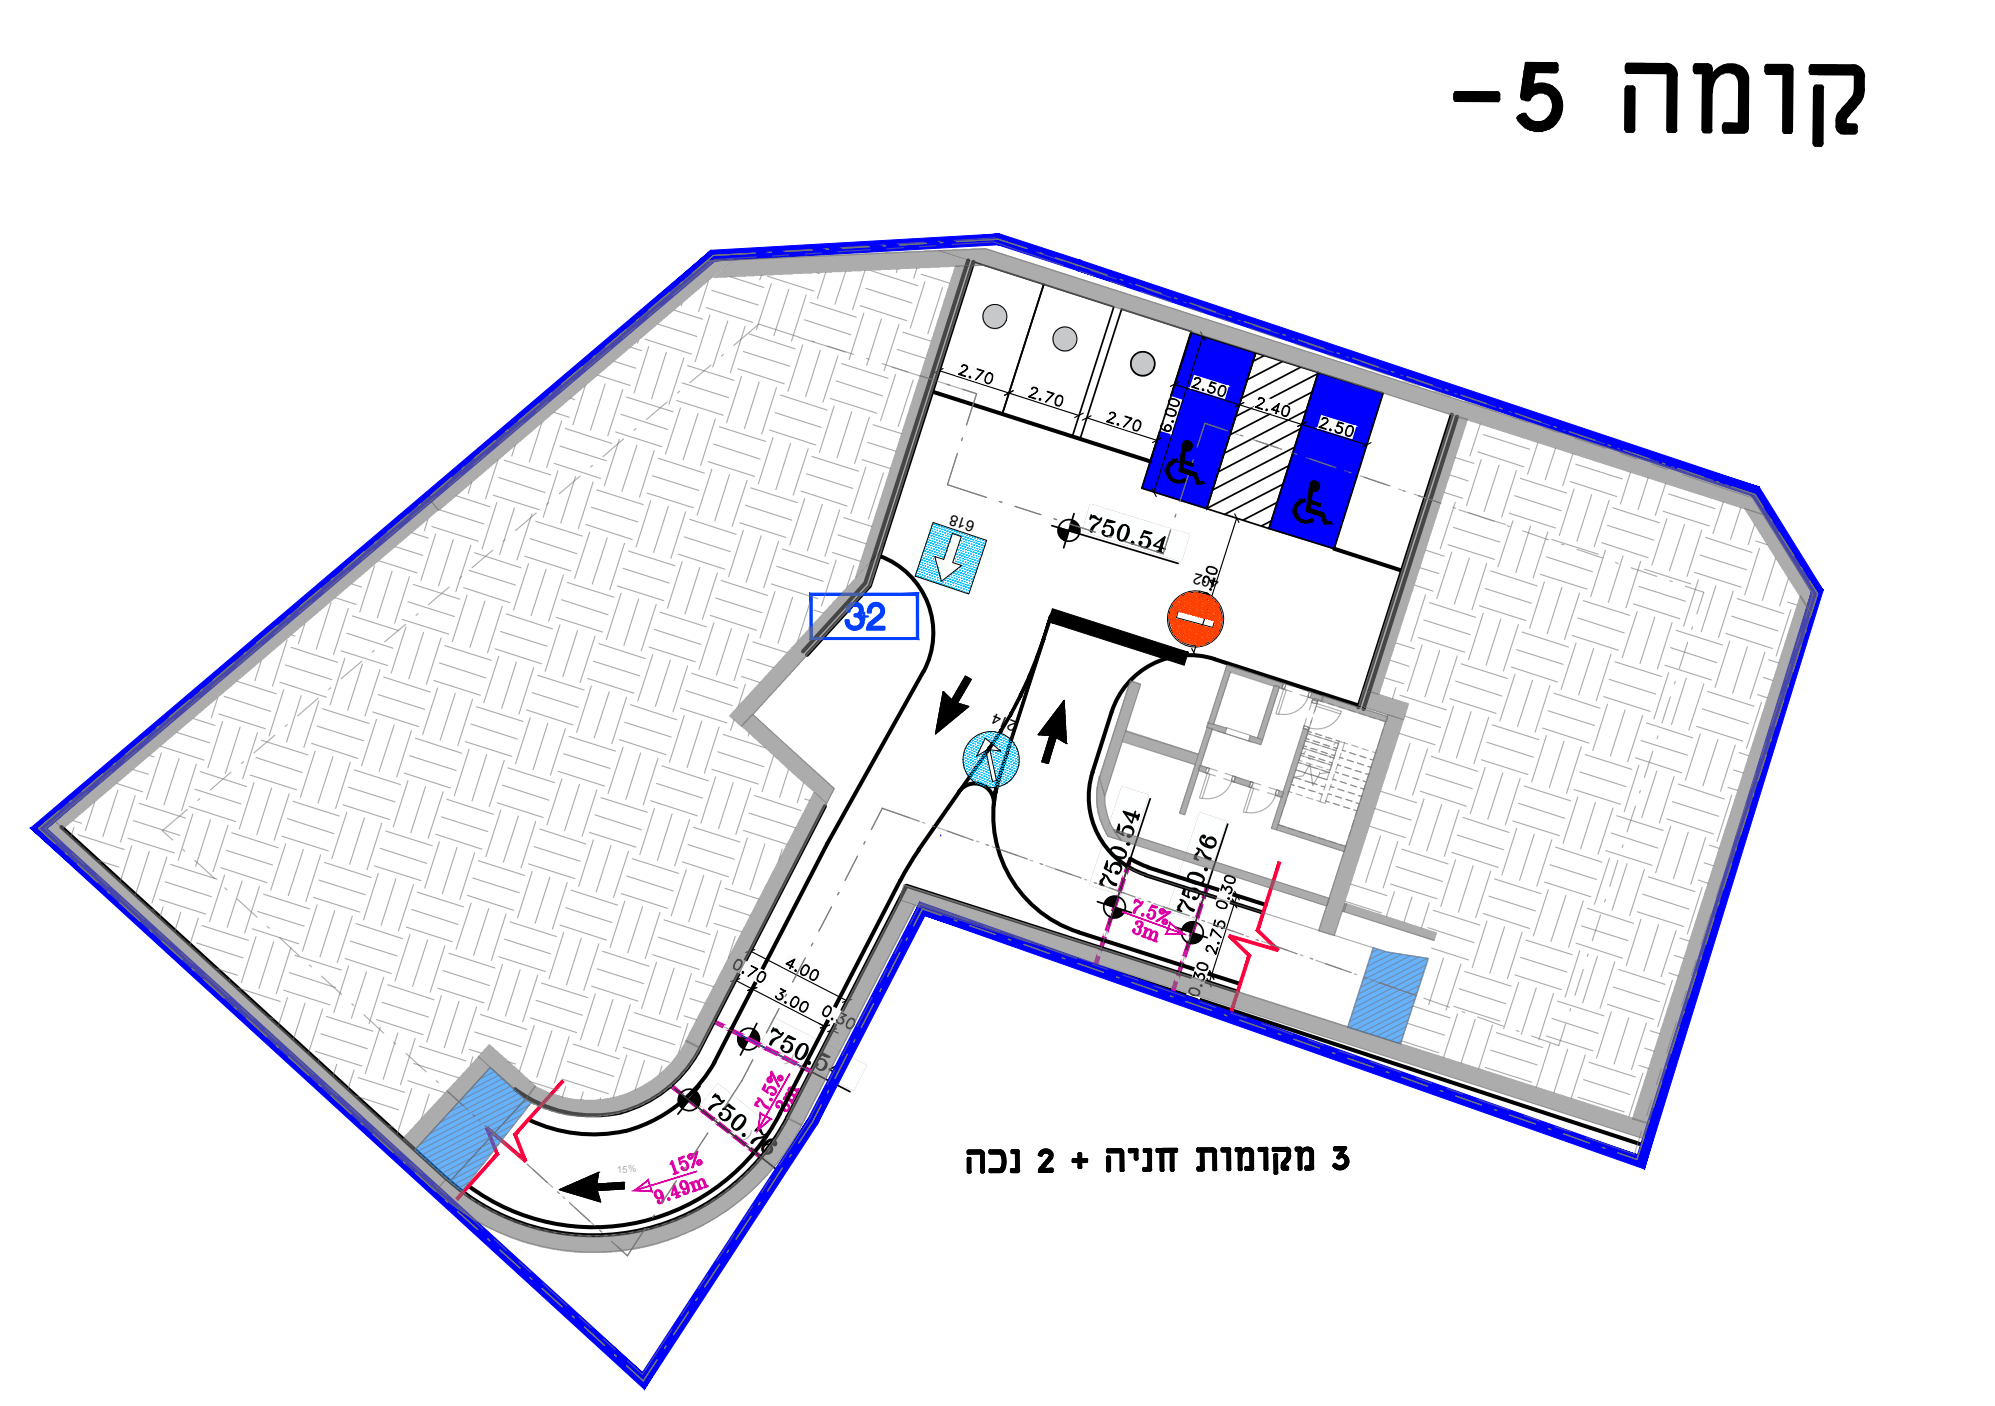

תקן חניה (1)

כתובת/חלקות	יעוד	כמות	רכב פרטי תקן	רכב פרטי דרוש	חניה נגישה תקן	חניה נגישה דרוש	אופנועים תקן	אופנועים דרוש (2)	אופניים תקן	אופניים דרוש (2)
הפלמ"ח 49 (חלקה 31)	מגורים עד 95 מ"ר	16	1:1	16	בין 101-150	3	1:10	6	1:1	60
	מגורים מעל 95 מ"ר	44	2:1	88						
	אורחים	59	10:1	6			-			
	סה"כ			110		3		6		60

הערות:
(1) ע"פ תקן חניה 5166,5166ב - תקן גבוה.
(2) ע"פ תקן חניה ארצי 2016.

מאזן חניה

	רכב פרטי	נכים	אופנועים	אופניים
דרוש	110	3	6	60
מוצע	110	3	6	60
עודף/חסר	0	0	0	0

כתובת/חלקות	יעוד	כמות	רכב פרטי תקן	רכב פרטי דרוש	חניה נגישה תקן	חניה נגישה דרוש	אופנועים תקן	אופנועים דרוש (2)	אופניים תקן	אופניים דרוש (2)
הפלמ"ח 51 השיירות 2 (חלקה 32)	מגורים עד 95 מ"ר	21	1:1	21	בין 31-75	2	1:10	5	1:1	45
	מגורים מעל 95 מ"ר	24	2:1	48						
	אורחים	45	10:1	5			-			
	מבנה ציבור	164	1:50	4	בין 11-25	2	1:100	2	1:500	1
	מסחר	262	1:25	11			1:200	2	1:300	1
	סה"כ			89		4		9		47

הערות:
(1) ע"פ תקן חניה 5166,5166ב - תקן גבוה.
(2) ע"פ תקן חניה ארצי 2016.

מאזן חניה

	רכב פרטי	נכים	אופנועים	אופניים
דרוש	89	4	9	47
מוצע	89	4	9	47
עודף/חסר	0	0	0	0