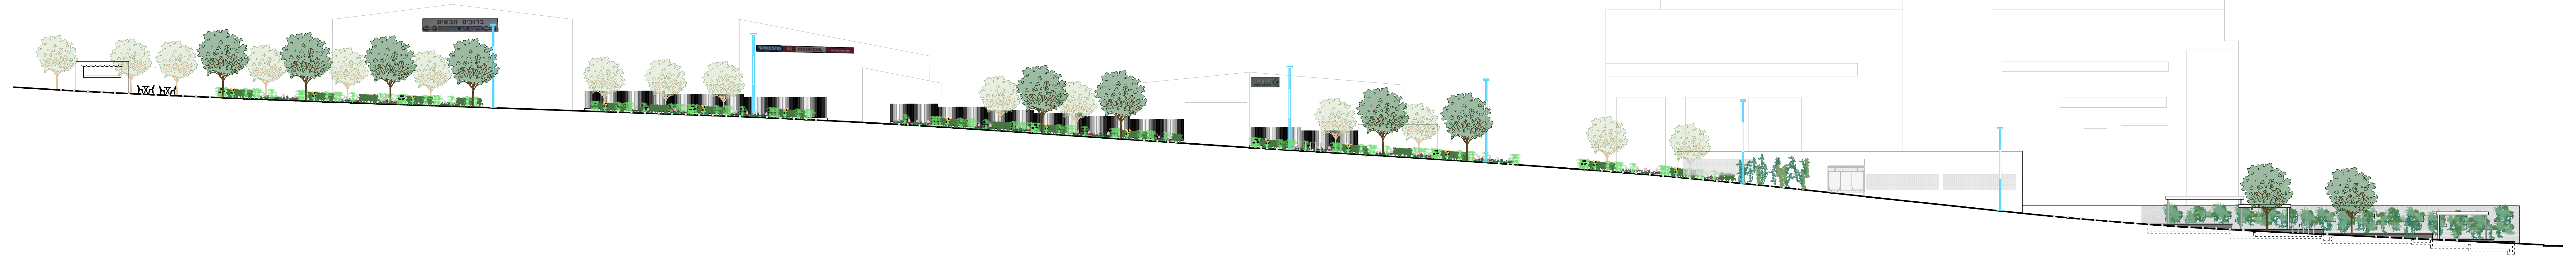

חתך דרומי
קנ"מ: 1:250

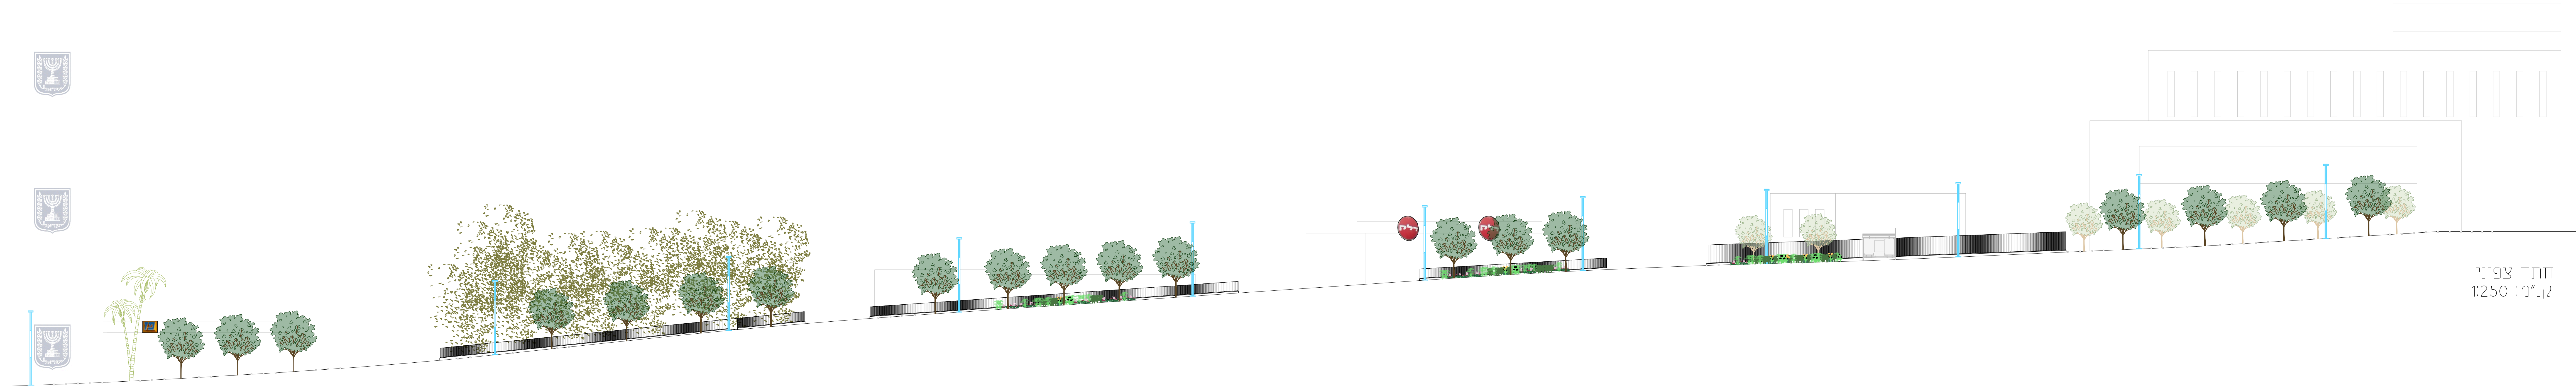

חתך צפוני
קנ"מ: 1:250

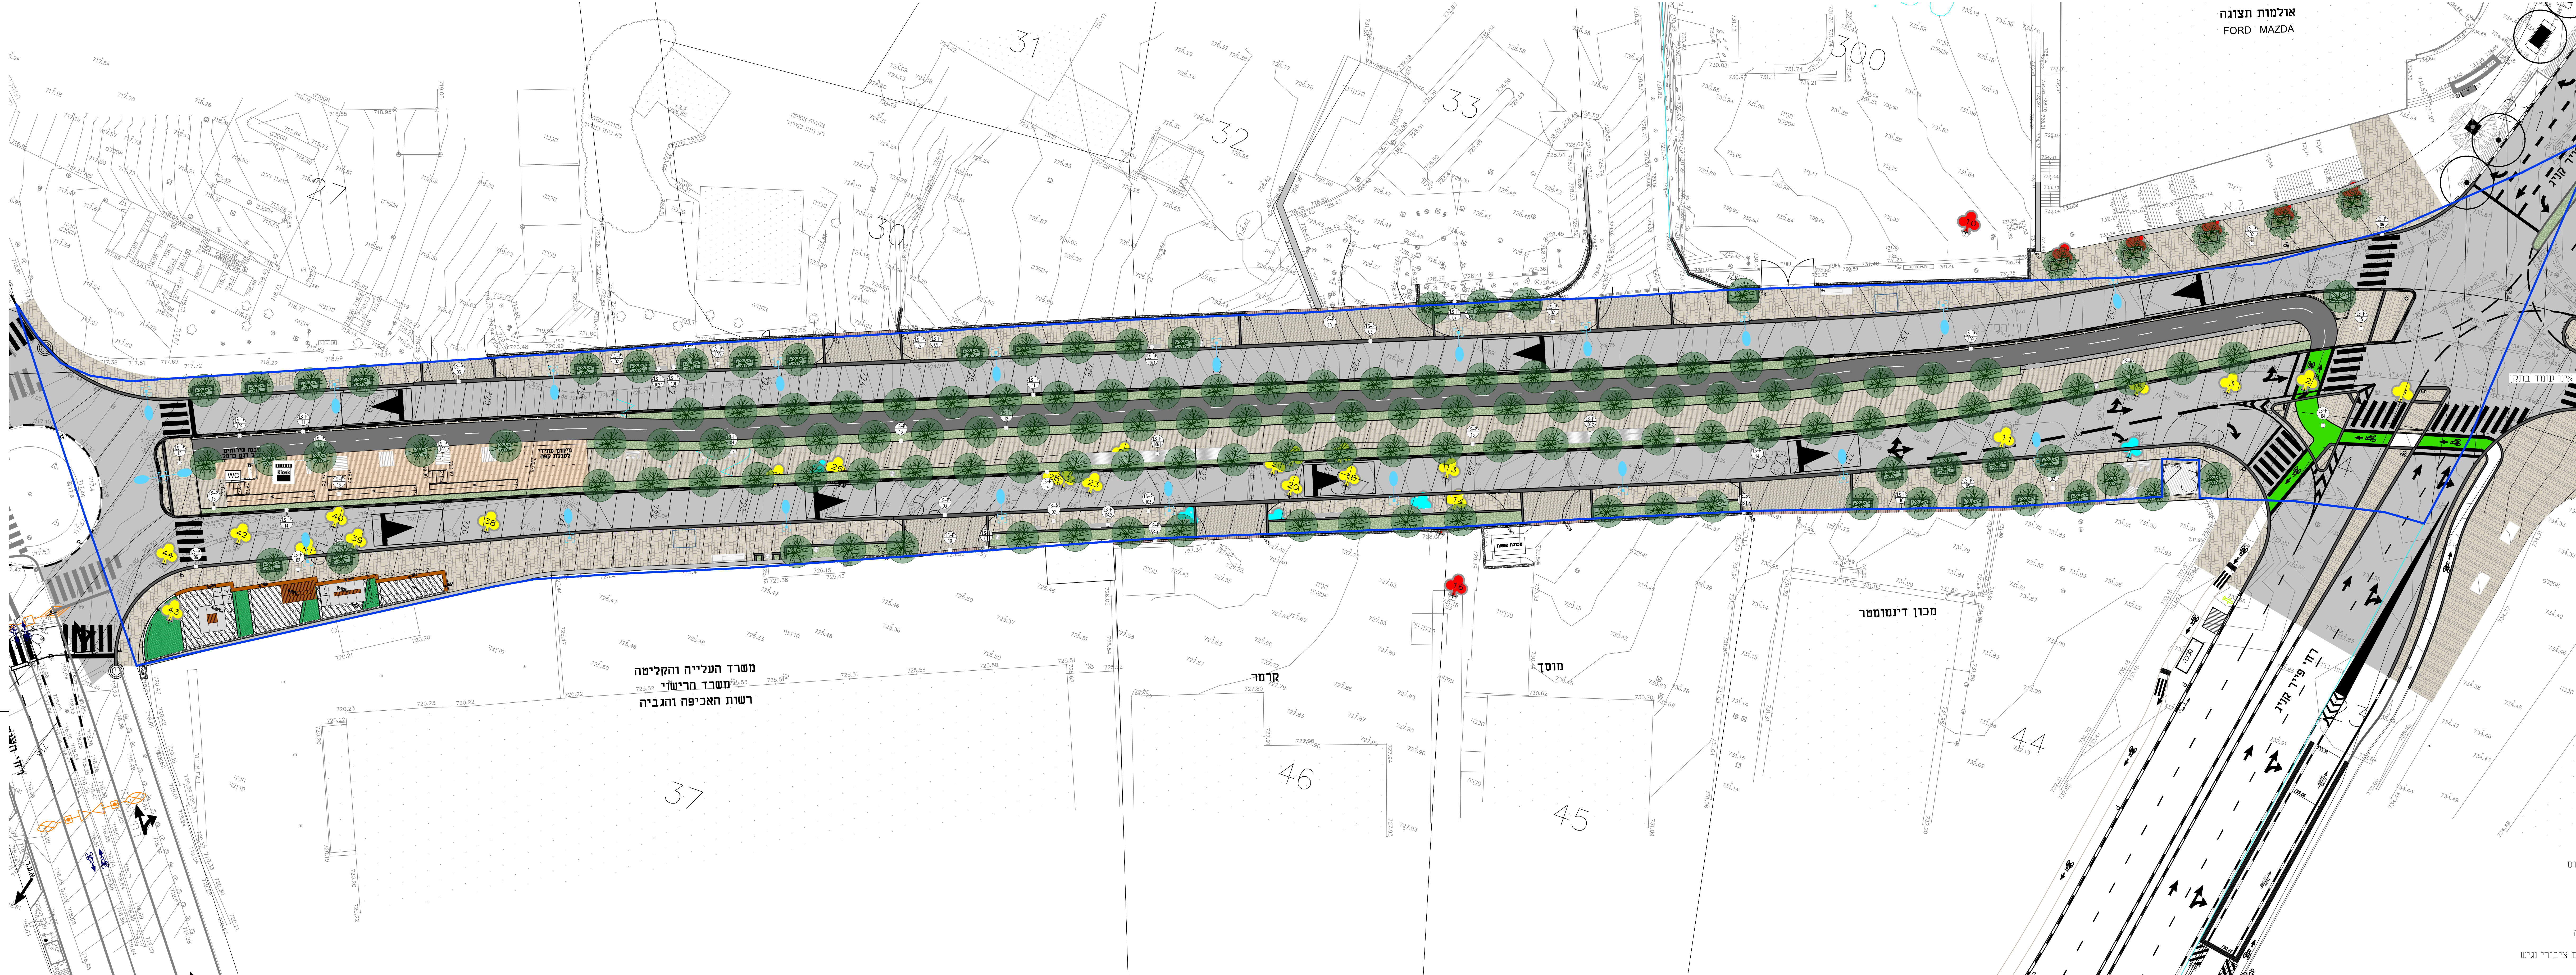

מקרא:

●	עצים לכריתה
●	עצים לשימור
●	עץ שנמדד אך אינו קיים או אינו עומד בתקן
—	גבול תכנית
○	עץ מתוכנן
▨	קיר קיים
▨	קיר מתוכנן
▨	מדרגות אקר דק
▨	ריצוף אבן משתלבת
▨	ריצוף אקר-דק
■	שביל אופניים
▨	אספלט כביש
🟩	גינון
🟩	דשא
═	אבן שפה
●	עץ קיים
▨	שולחן קק"ל
▨	ספסל רחוב
▨	ספסל בשדרה
▨	שולחן בר
○	אשפתון
▨	ברזיה
¦	חניה לאופנים
▨	תחנת אוטובוס
●	עמוד מחסום לתחנת אוטובוס
□	עמוד מחסום
●	גוף תאורה לפי יועץ
Kiosk	חלופות למיקום קיוסק / קפה
WC	חלופות למיקום תא שירותים ציבורי נגיש

נספח נוף

נספח לתכנית מס' 101-1409366

הרחבת רחוב הסדנא - תלפיות

גליון 1 מתוך 1

תחולה	מנחה
תיאור	תכנית פיתוח
תאריך עריכת הנספח	20.04.2025
קנ"מ	1:250

שמות וחתימות:

עורך הנספח	שם: ורד סינגר יעקבי תאגיד: תפנית תכנון

תפנית - תכנון ובינוי ערים

Tafnit
Architects
תפנית
תכנון ובינוי ערים