חוק התכנון והבנייה, התשכ"ה - 1965
תכנית מתאר מקומית

מס תכנית 101-1451699

שם התכנית:

תכנית איחוד וחלוקה עבור מדרשיית הרטמן לבנות

נספח מס' 1 -בינוי

קנ"מ 1:200

מקרא נספח בינוי

גבול מגרש	━
הריסה	─
קו קרקע טבעי	- - - - - - -
עץ לשימור	♣
עץ לעקירה	♣
עץ לשתילה	✲
גינון	🟩

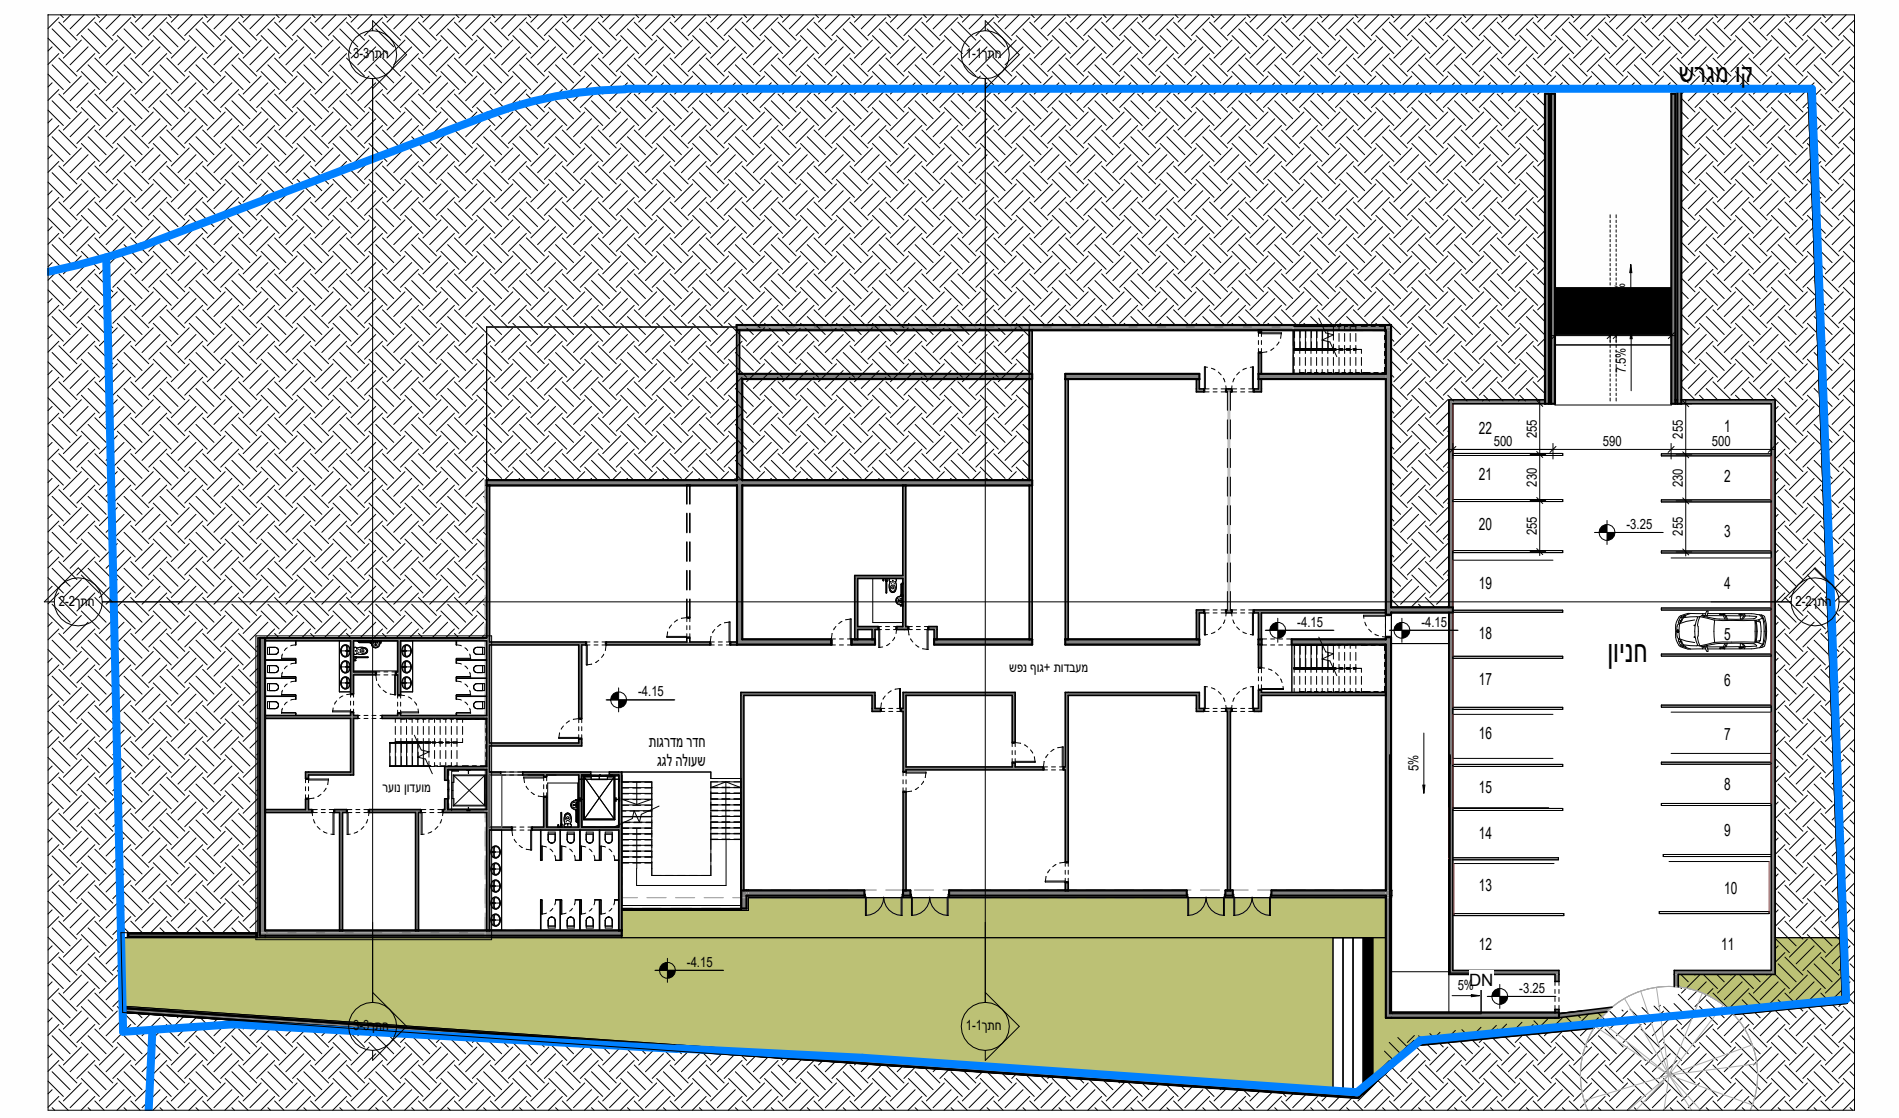

קומת מרתף-1
1 : 200

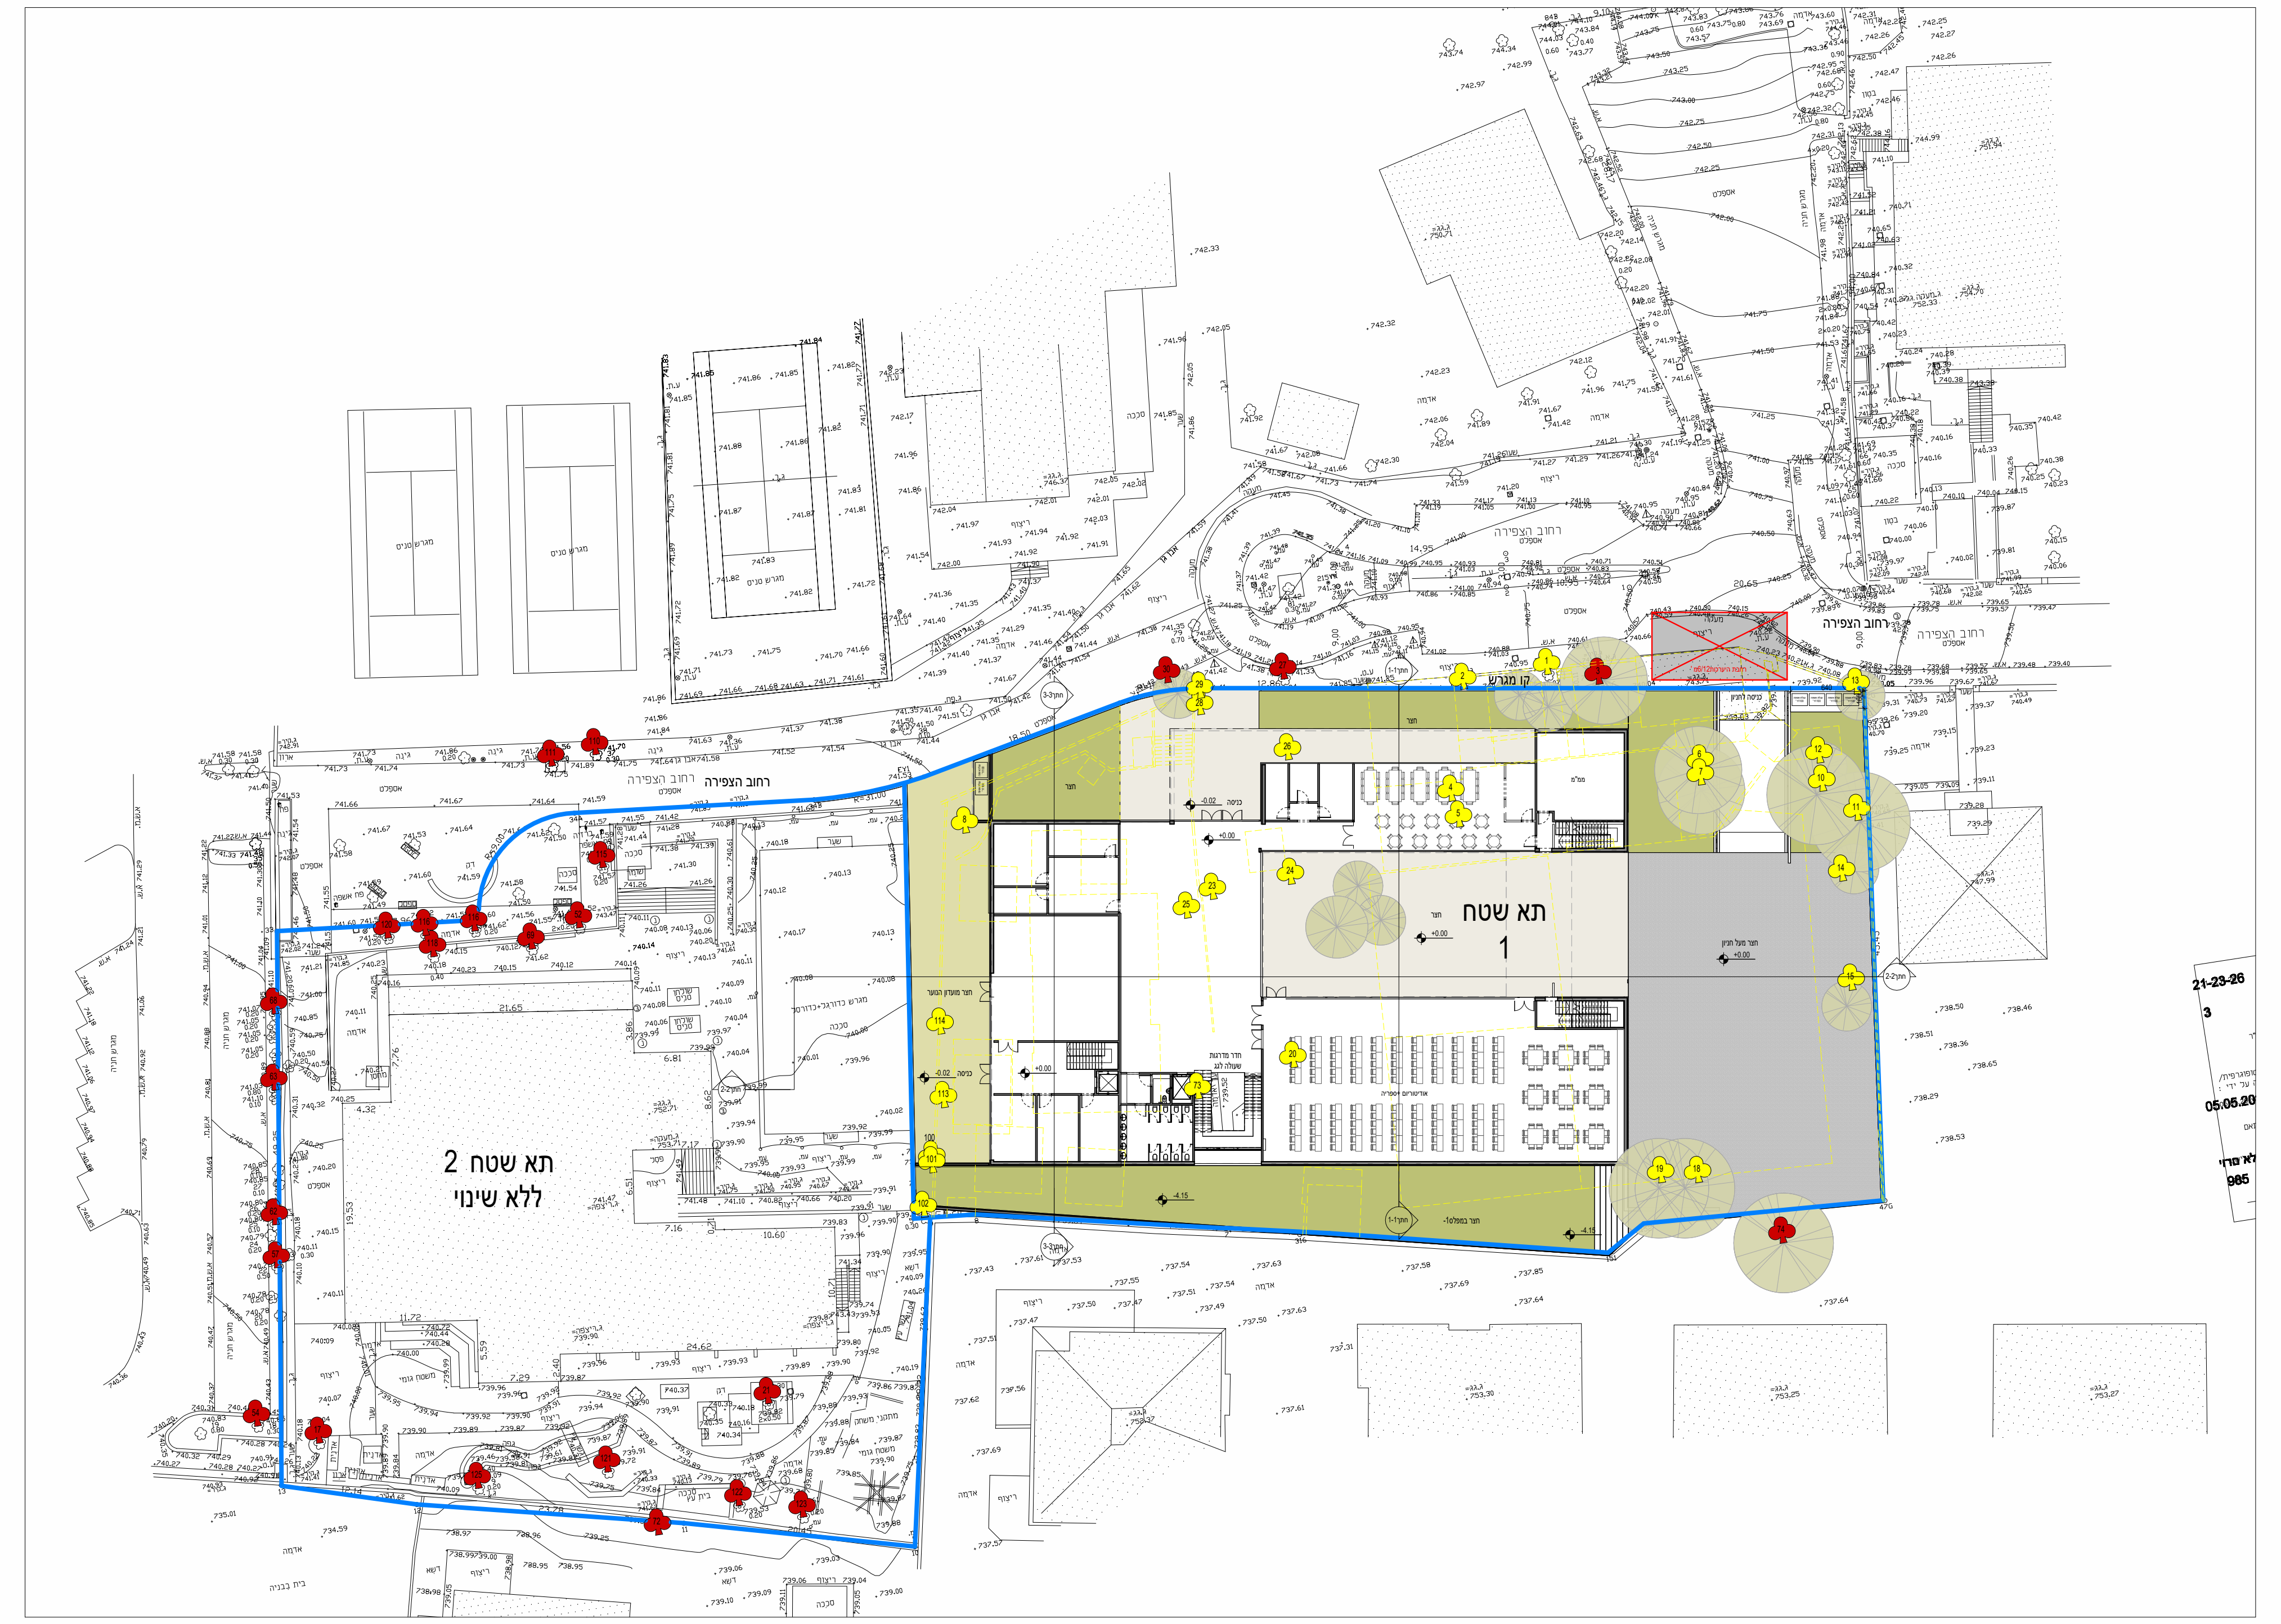

תכנית פיתוח וקרקע
1 : 200

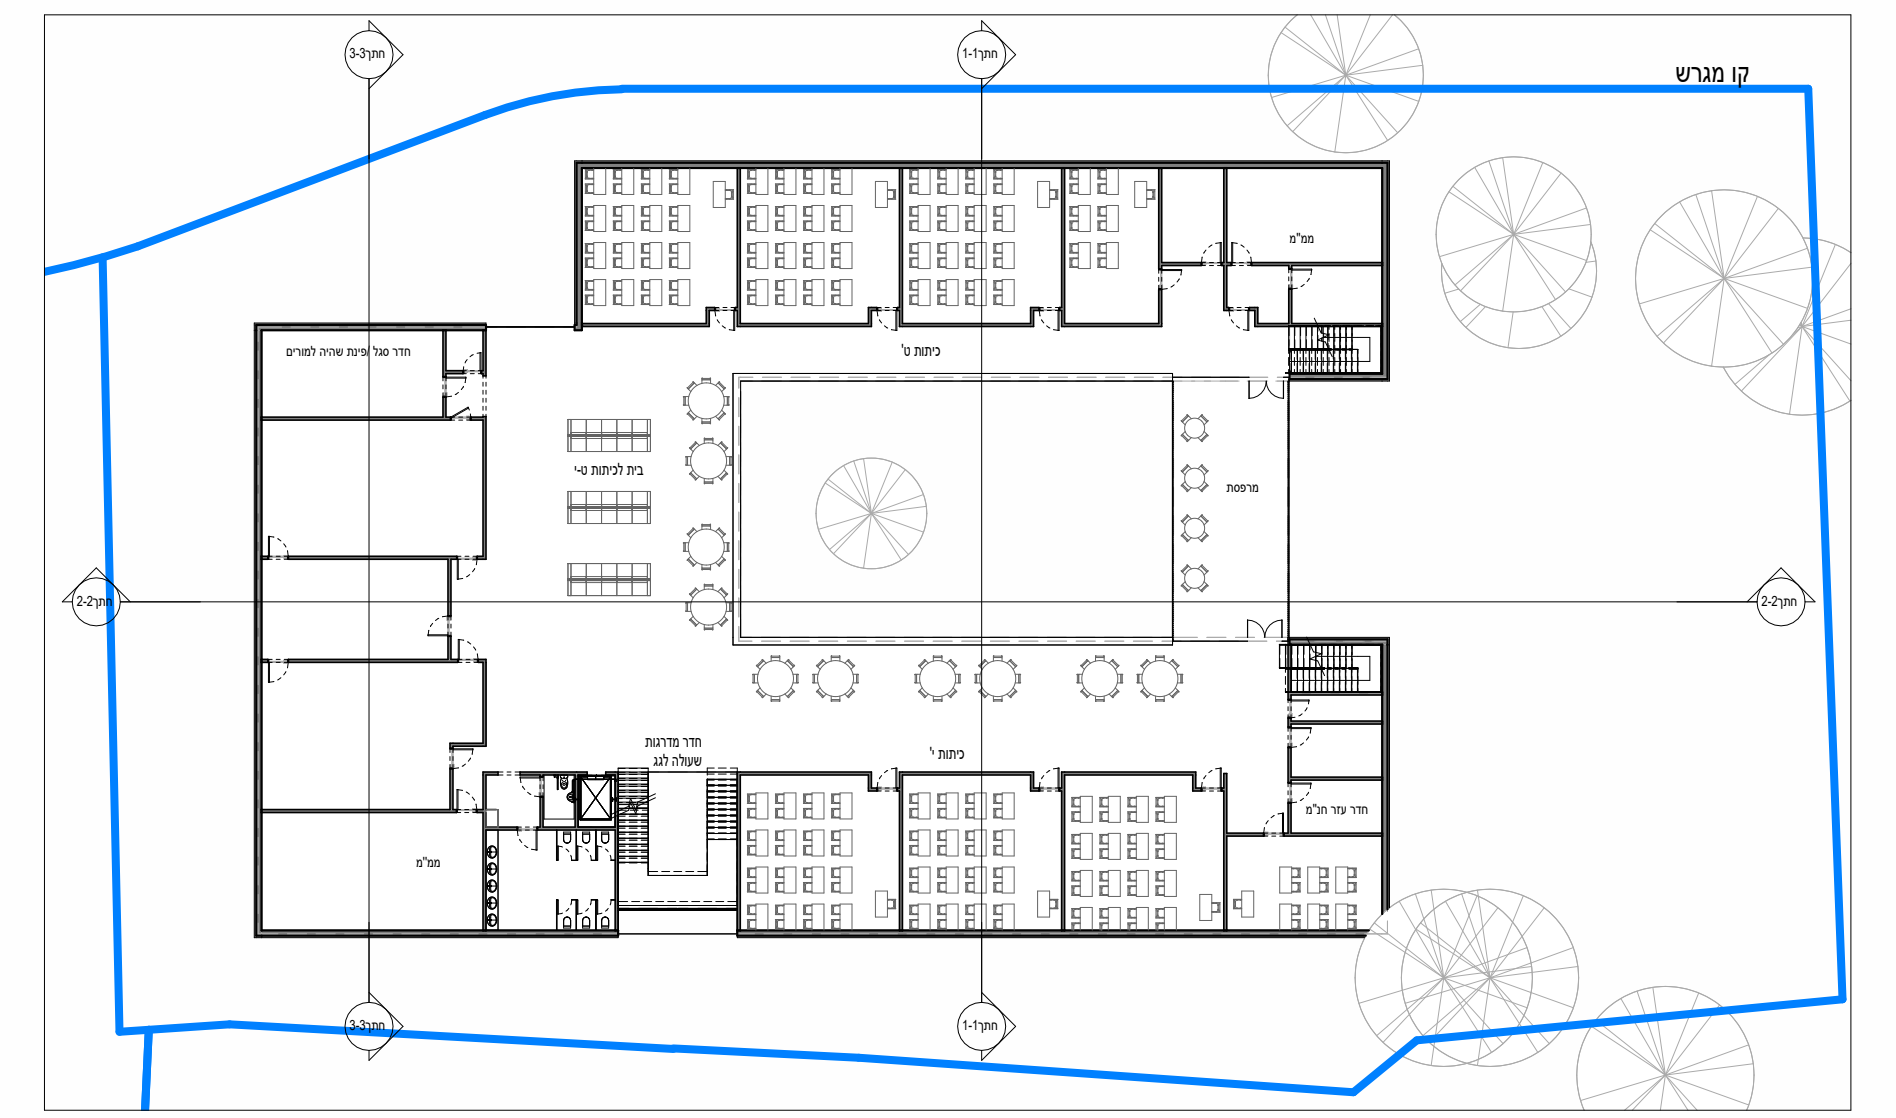
תכנית קומה שניה
1 : 200

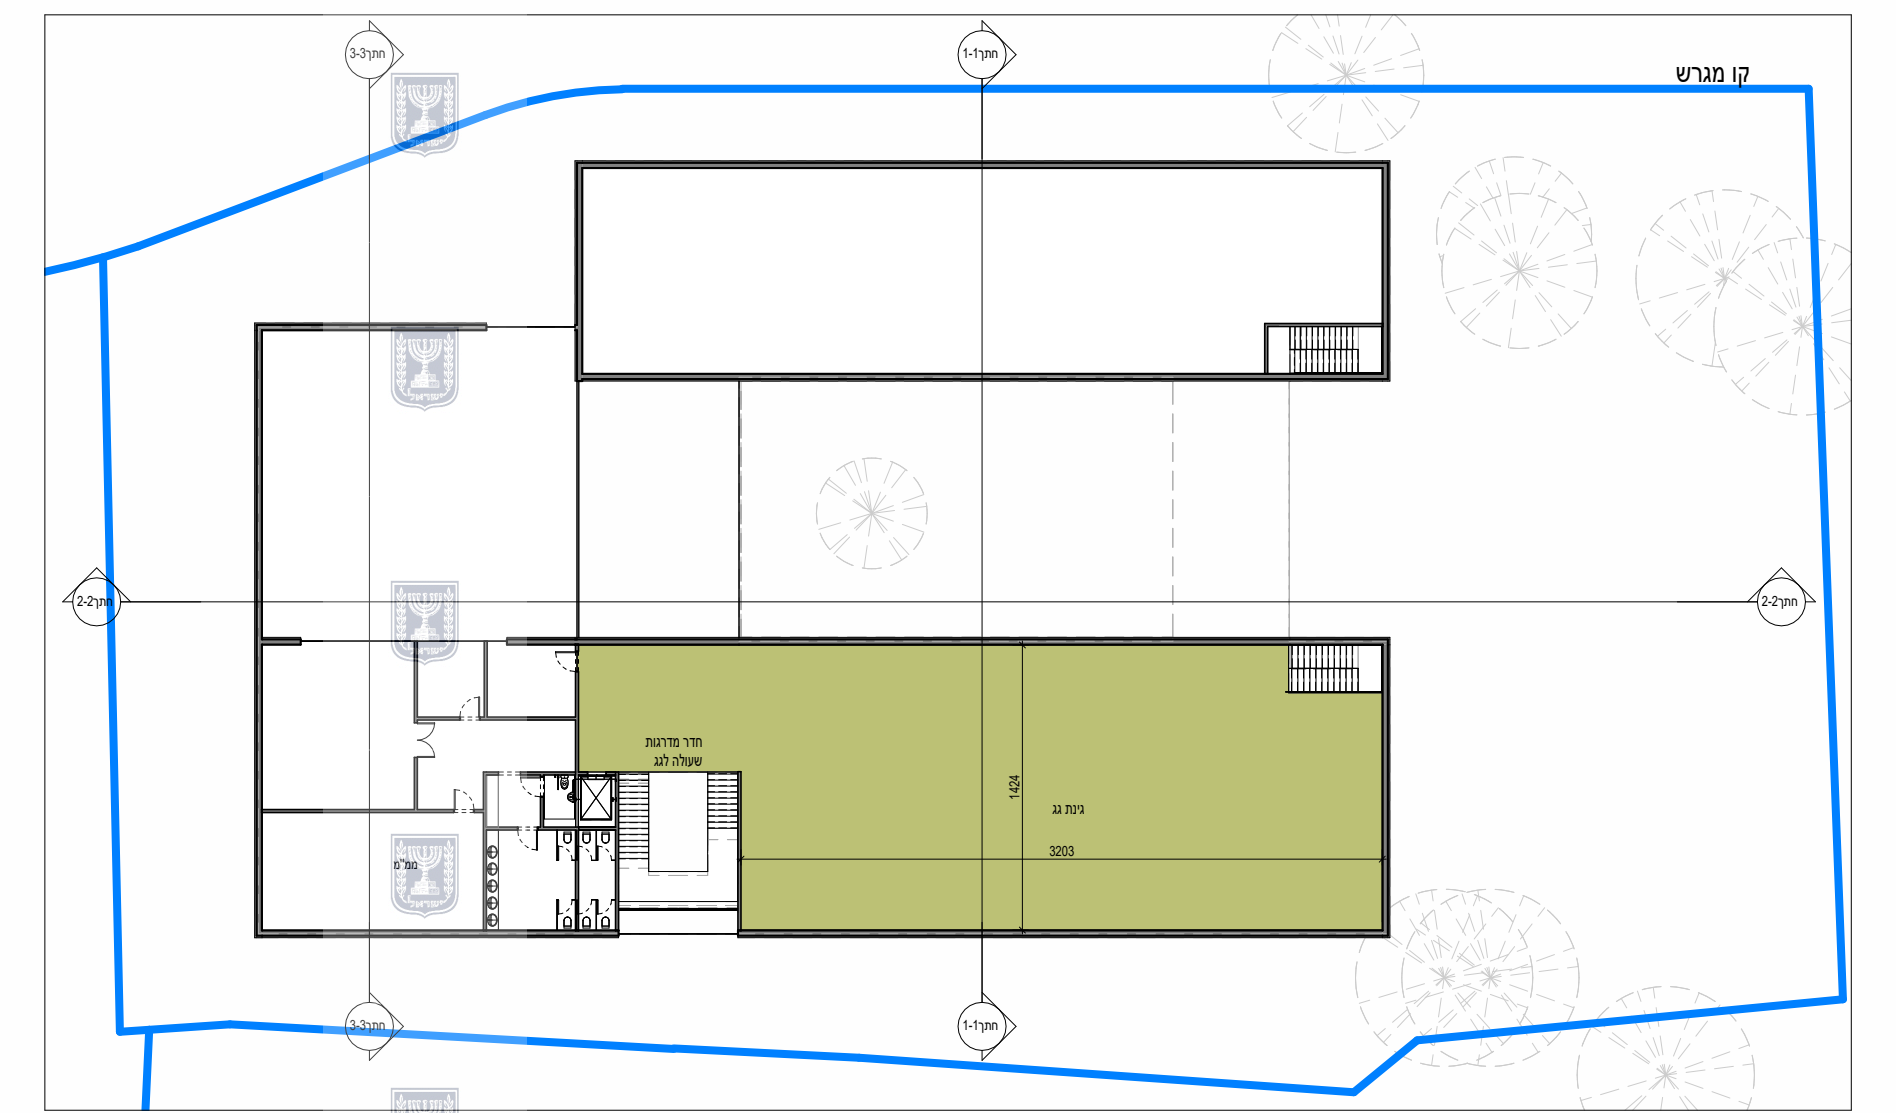
תכנית קומה רביעית
1 : 200

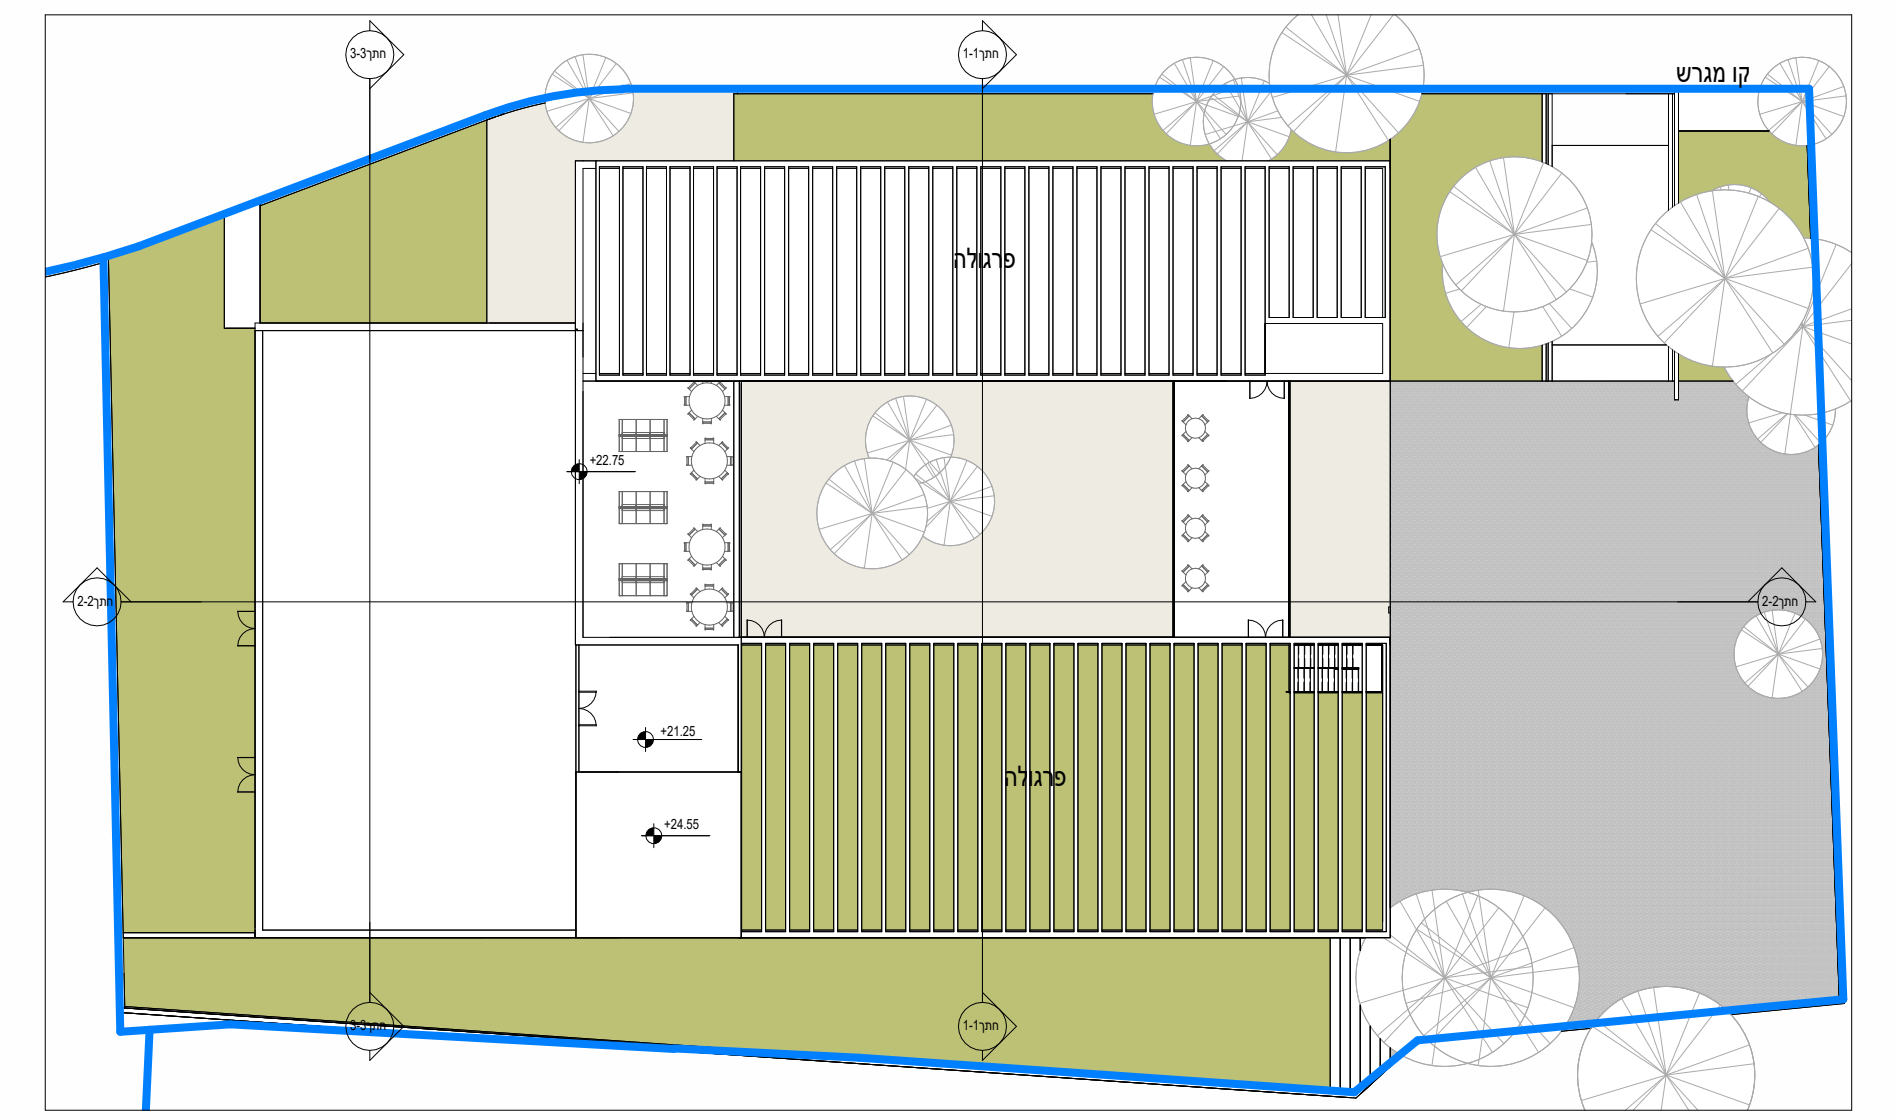
תכנית קומת גג
1 : 200

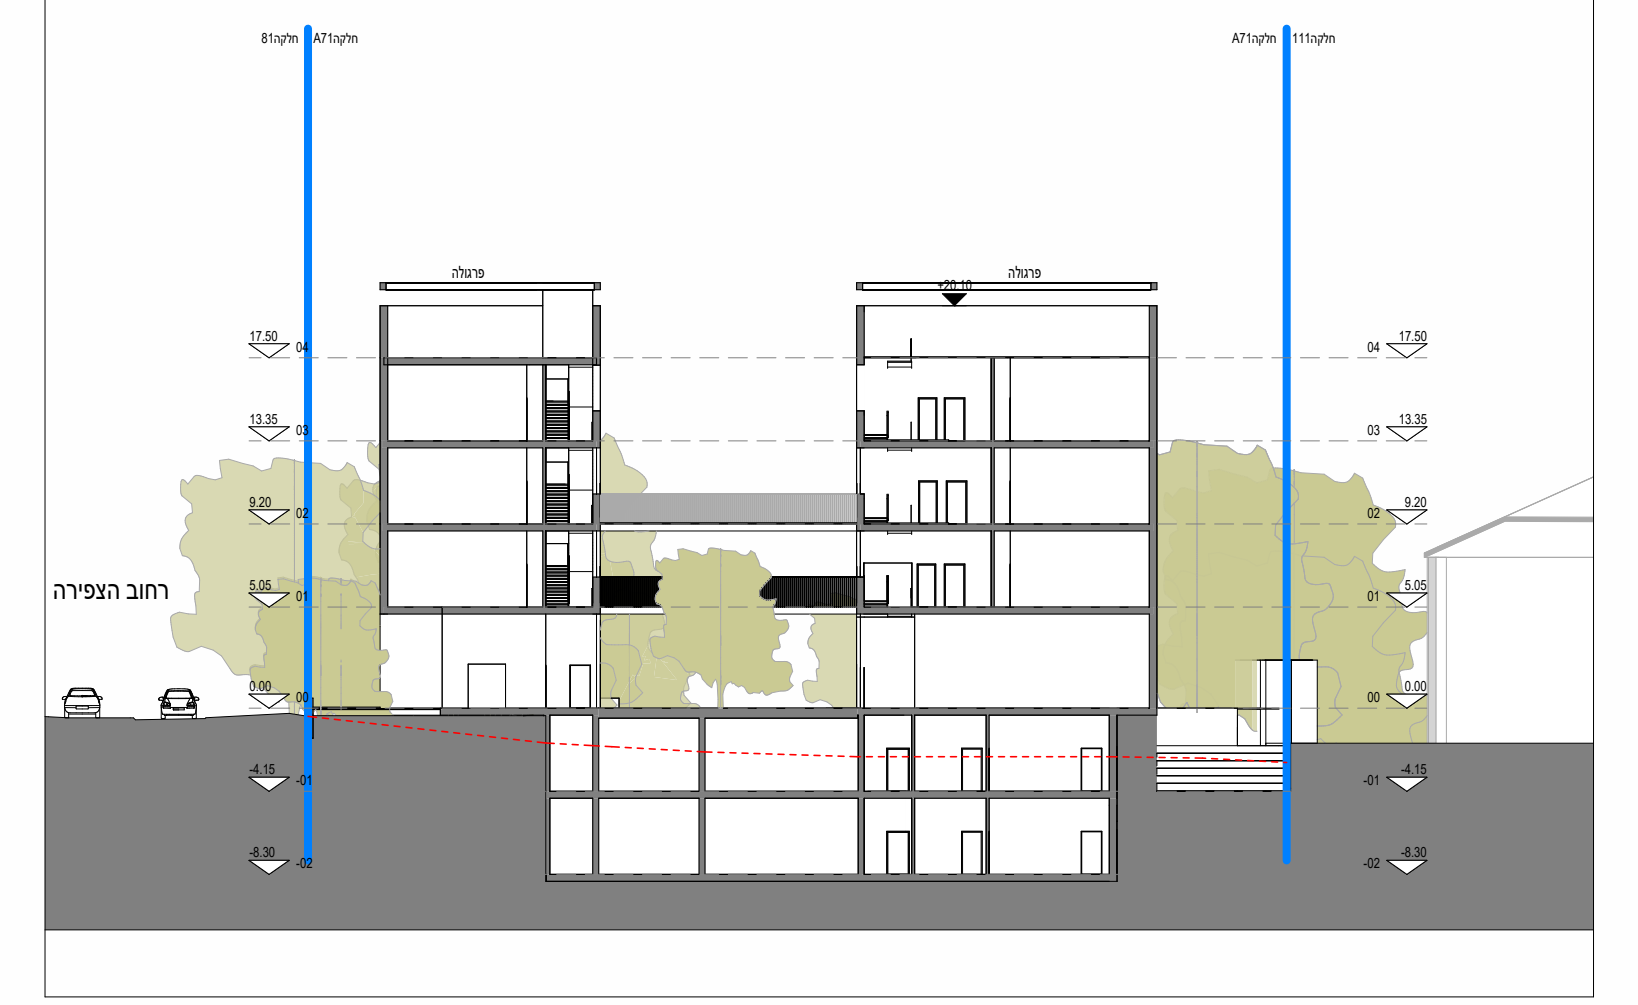
חתך1-1
1 : 200

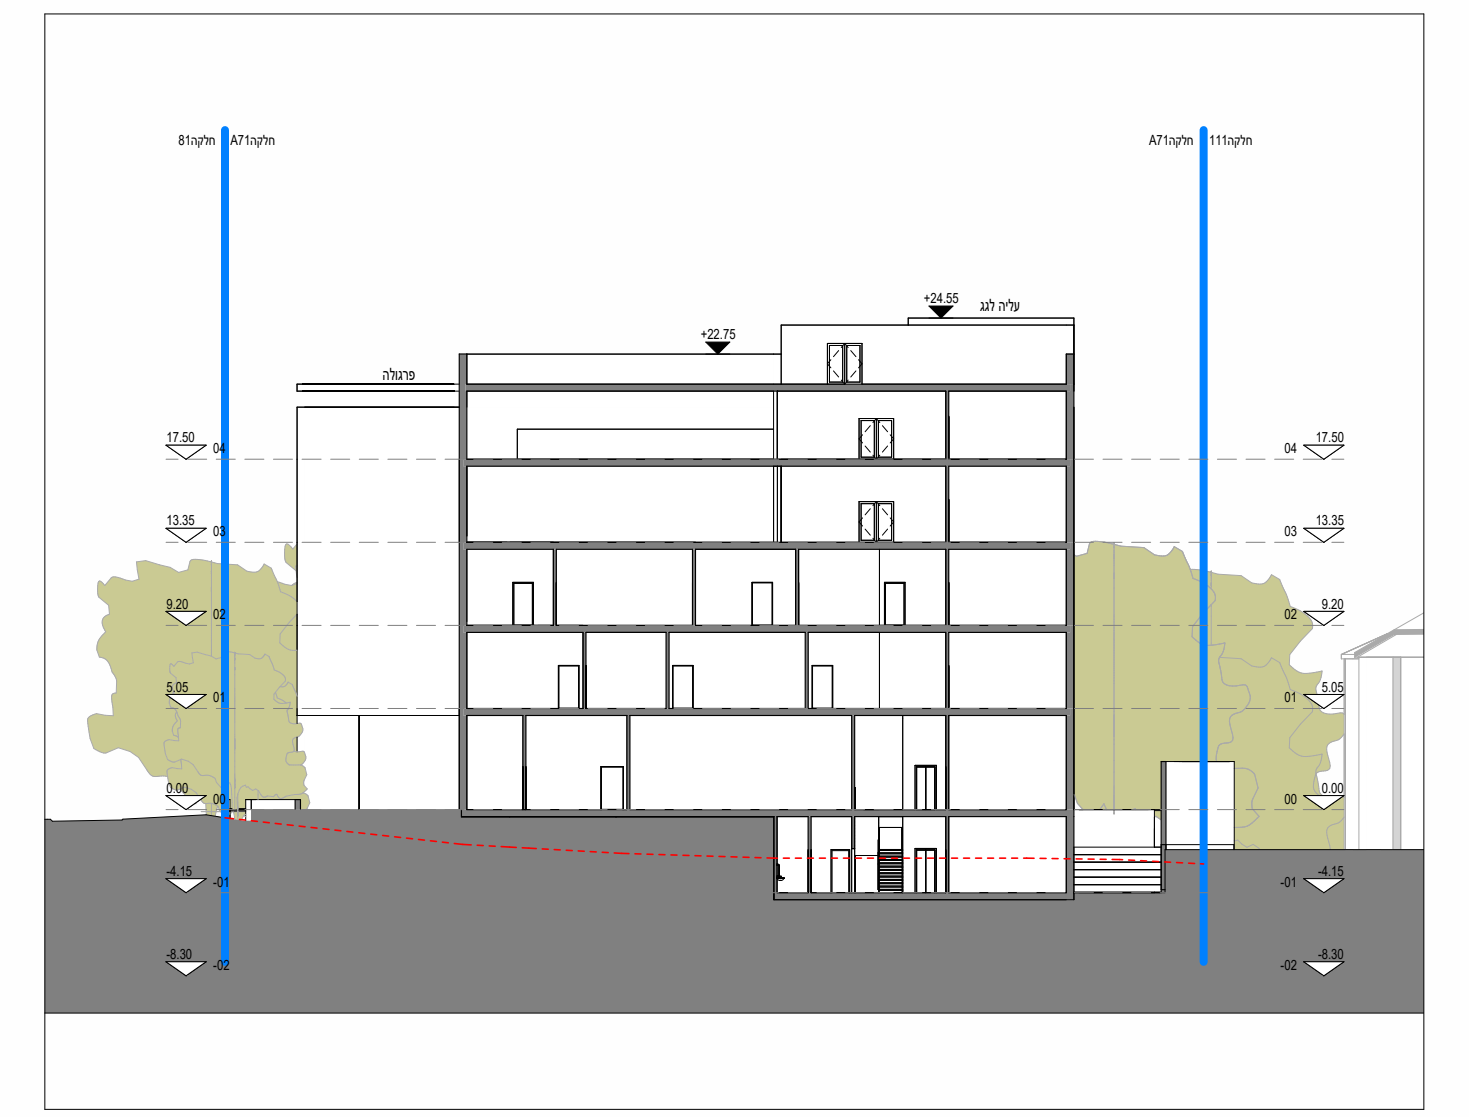
חתך3-3
1 : 200

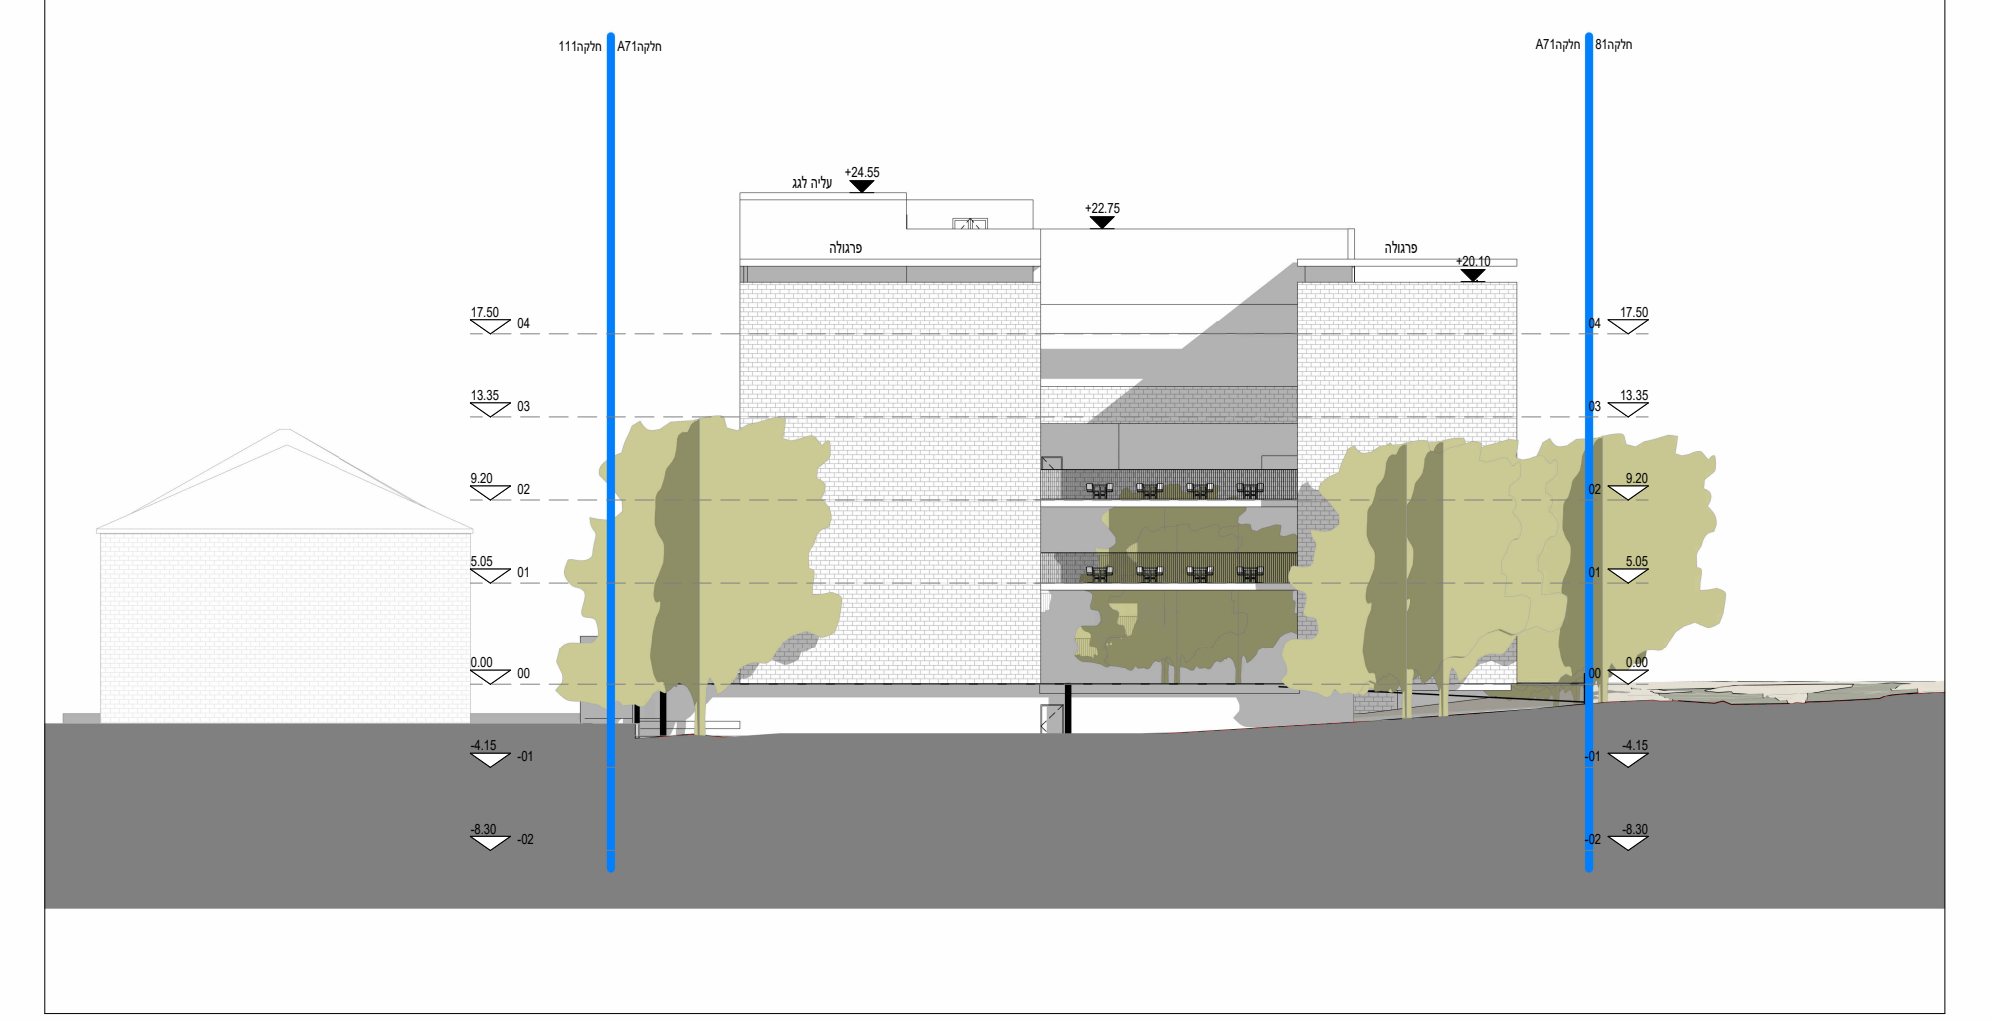
חזית נפחית מזרחית
1 : 200

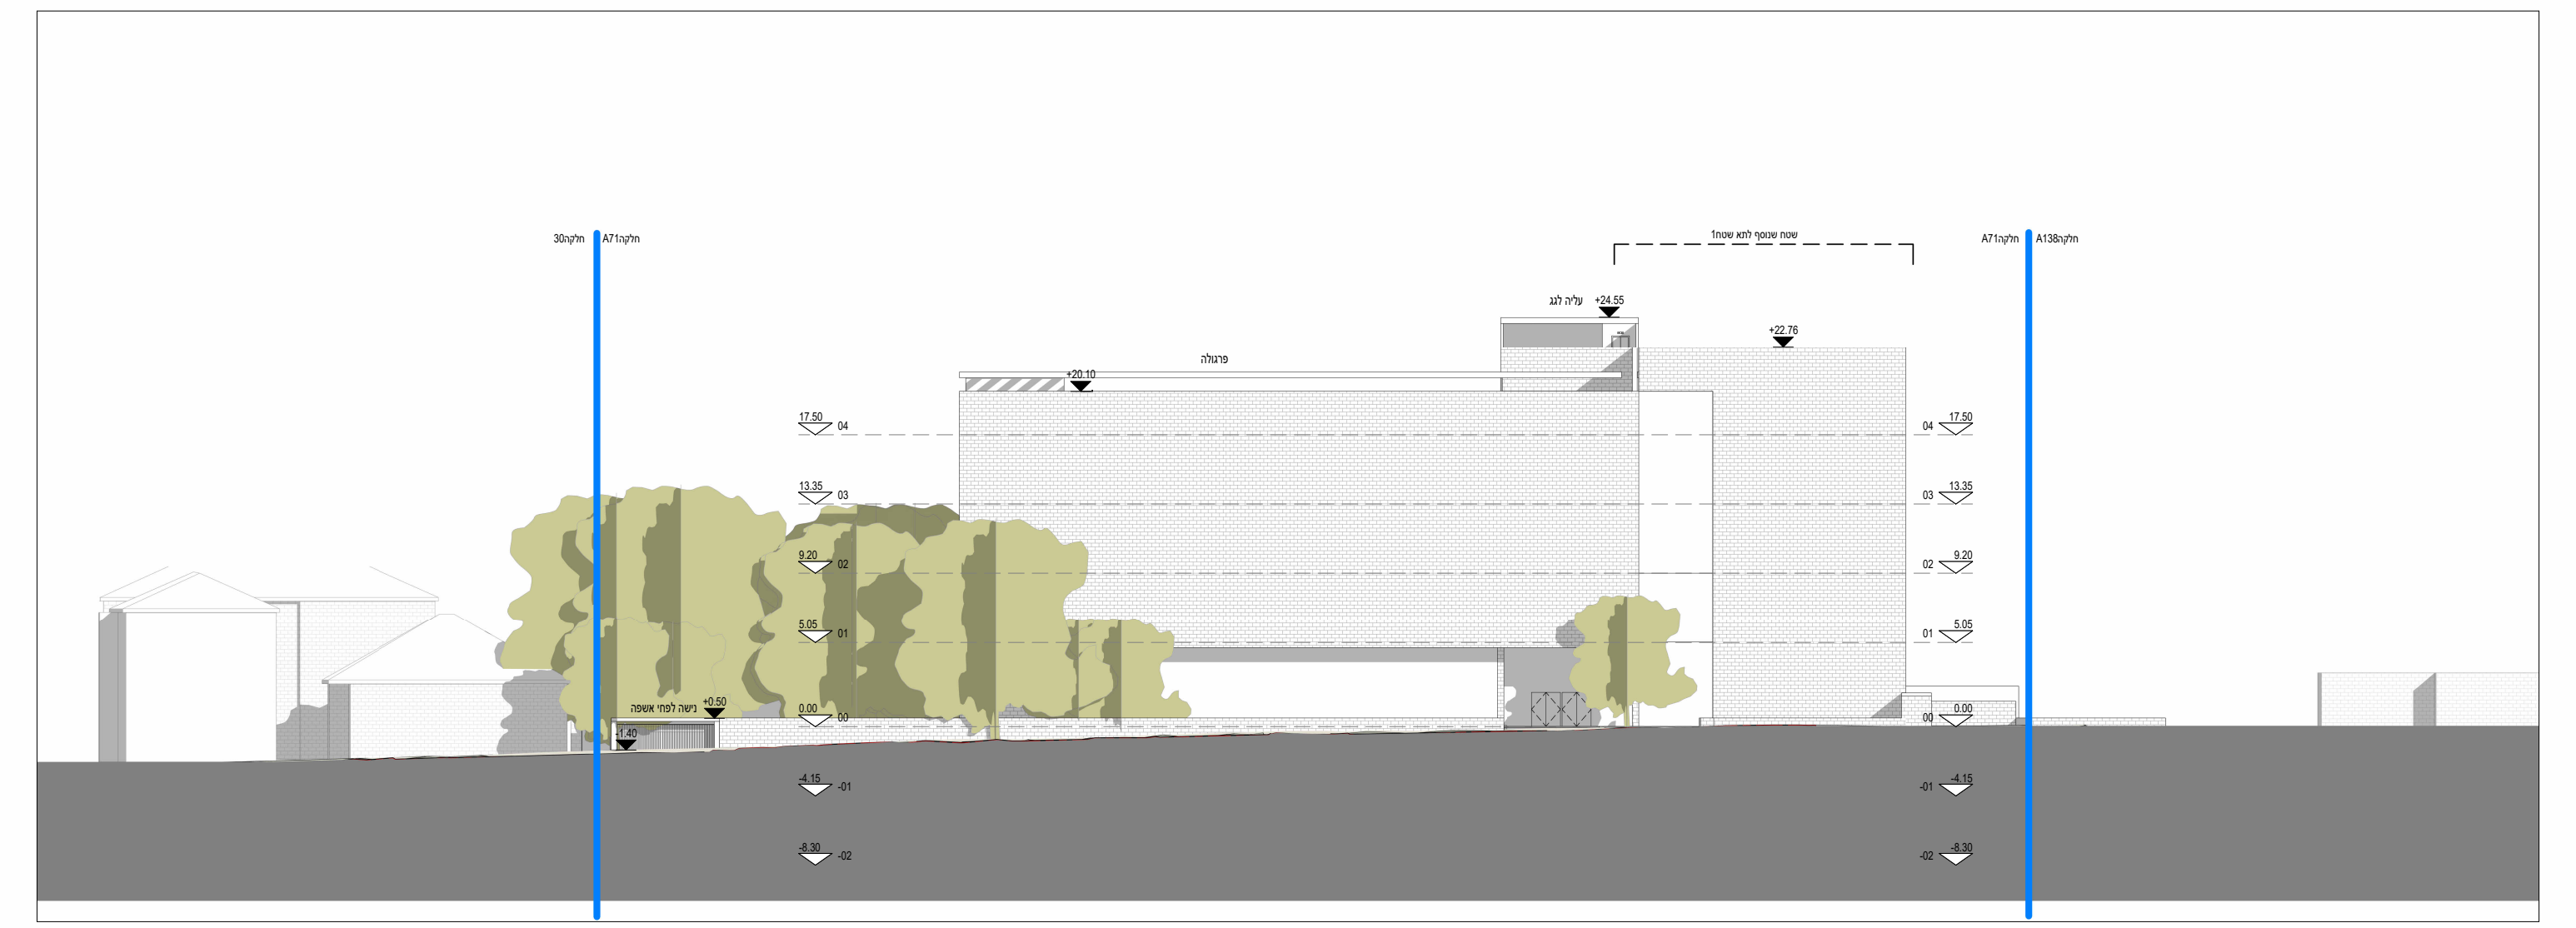
חזית נפחית צפונית
1 : 200

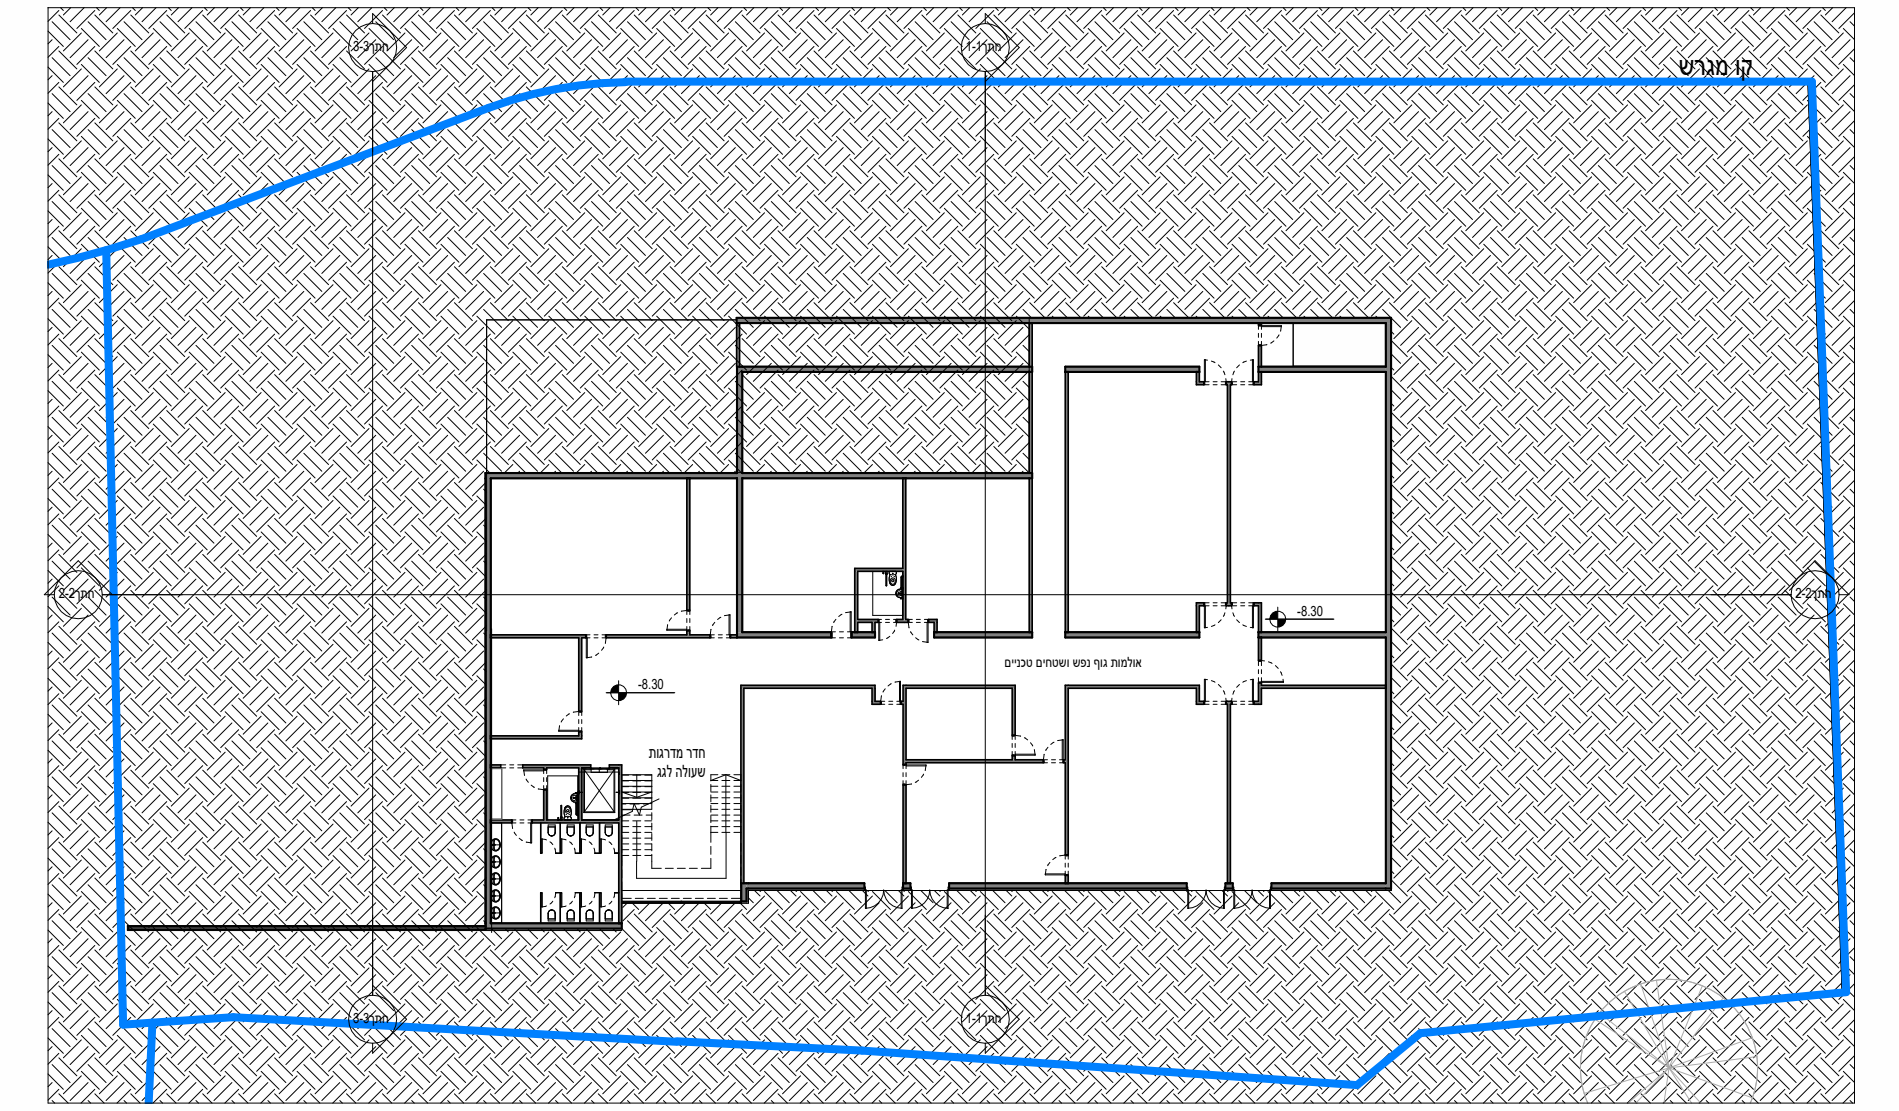
תכנית מרתף-2
1 : 200

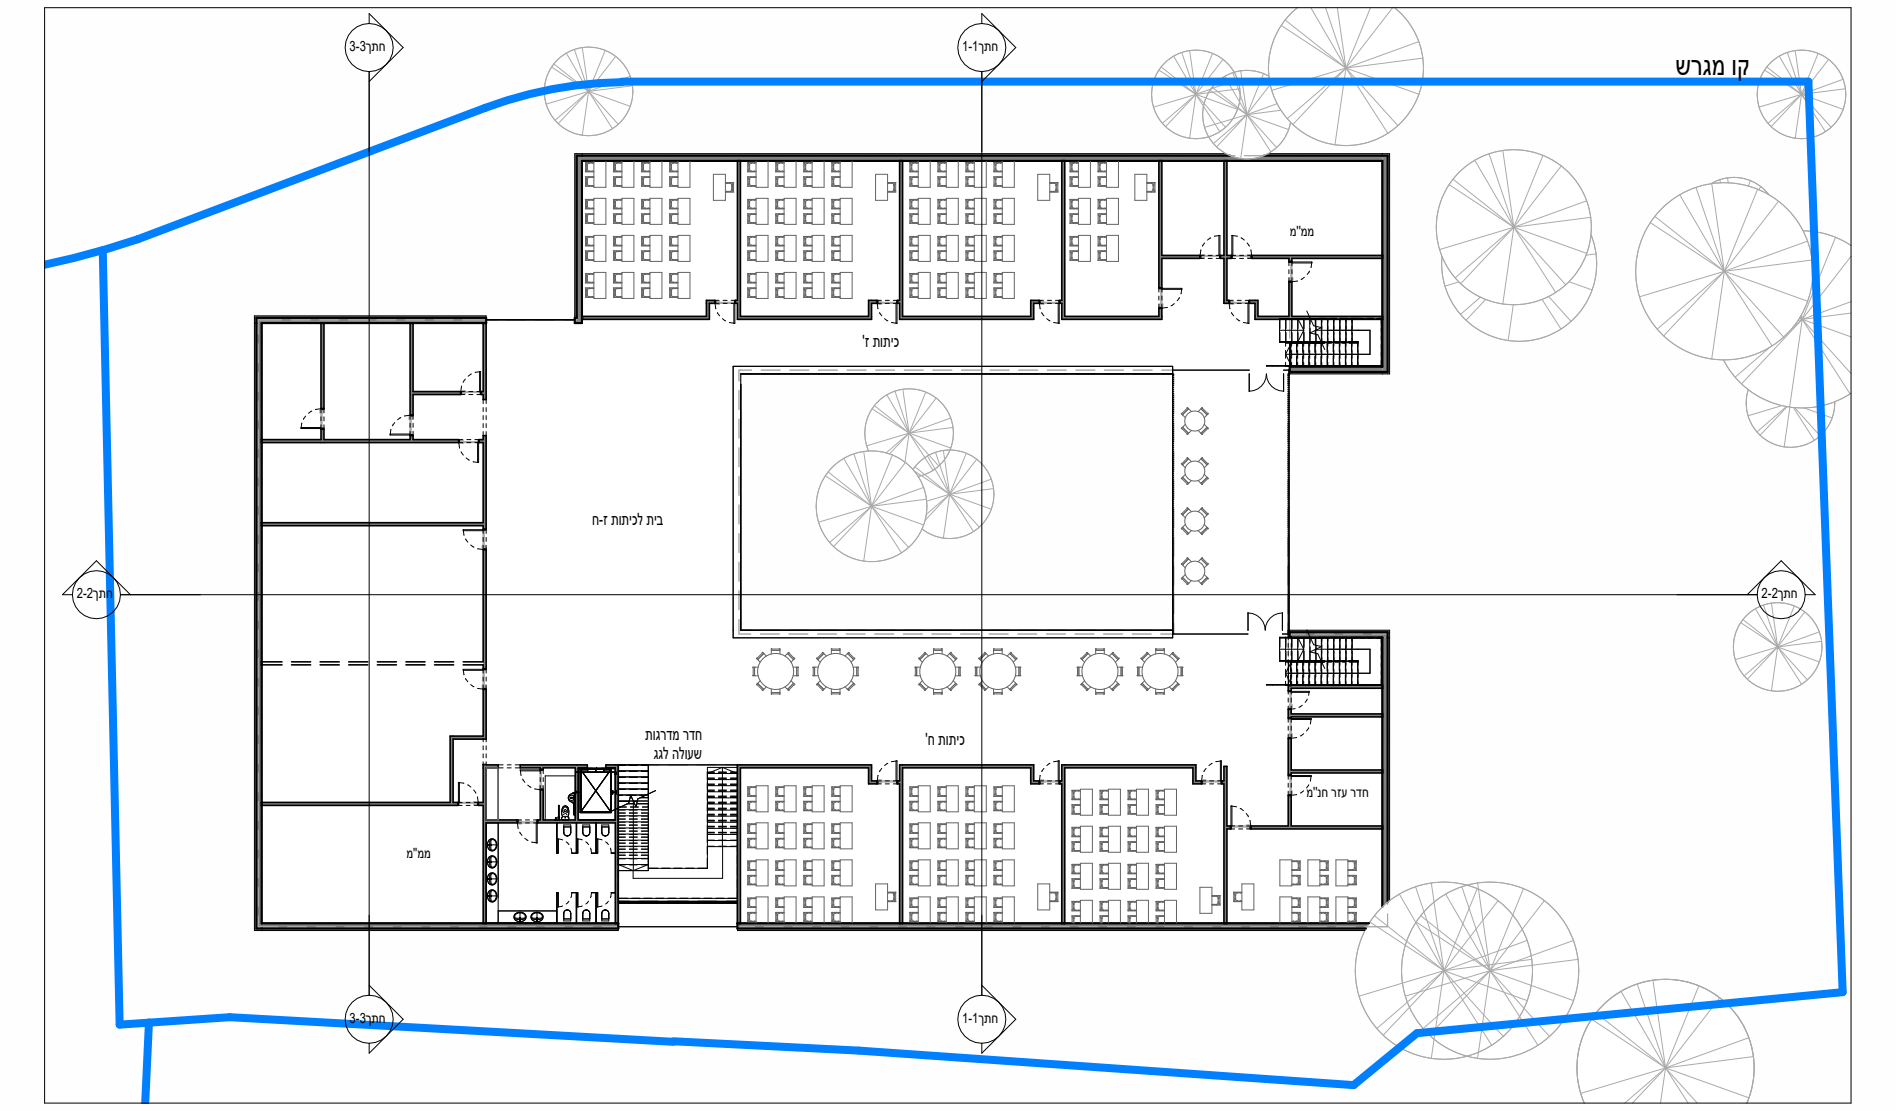
תכנית קומה ראשונה
1 : 200

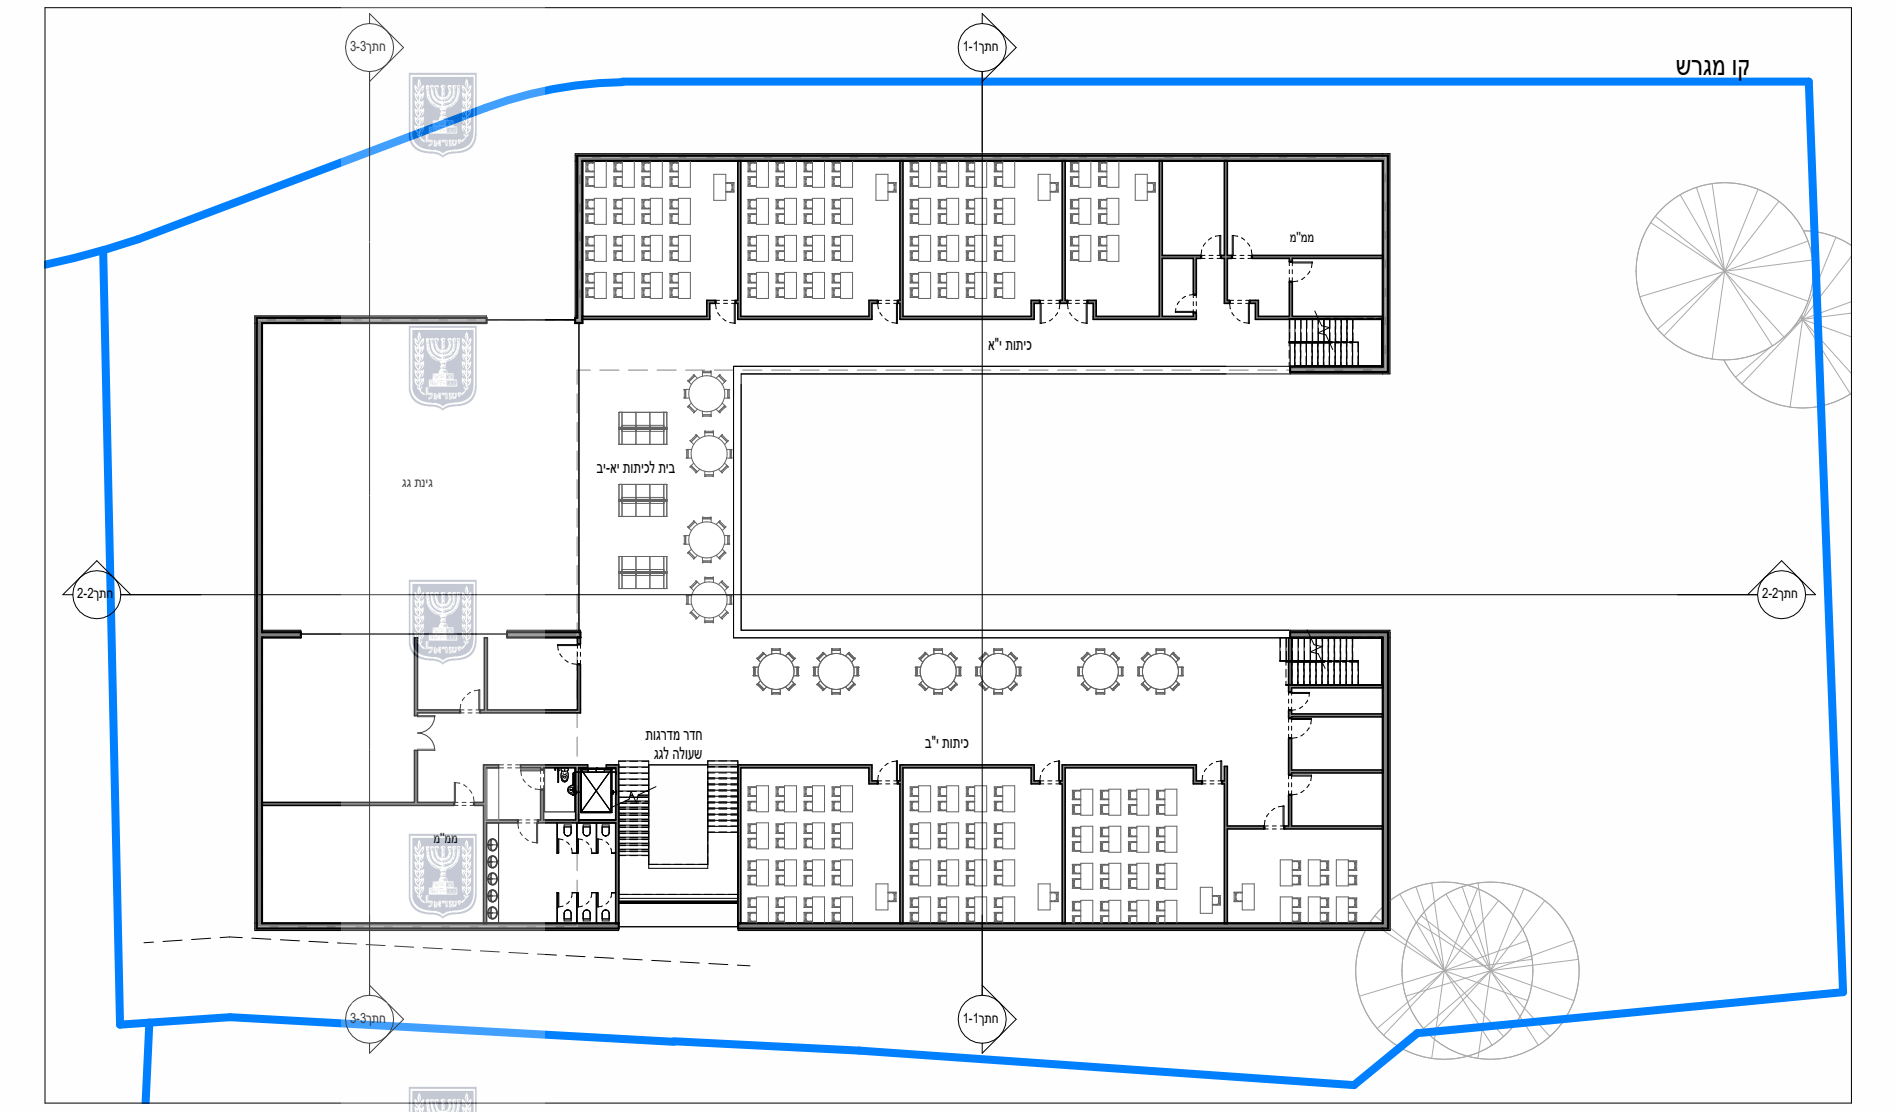
תכנית קומה שלישית
1 : 200

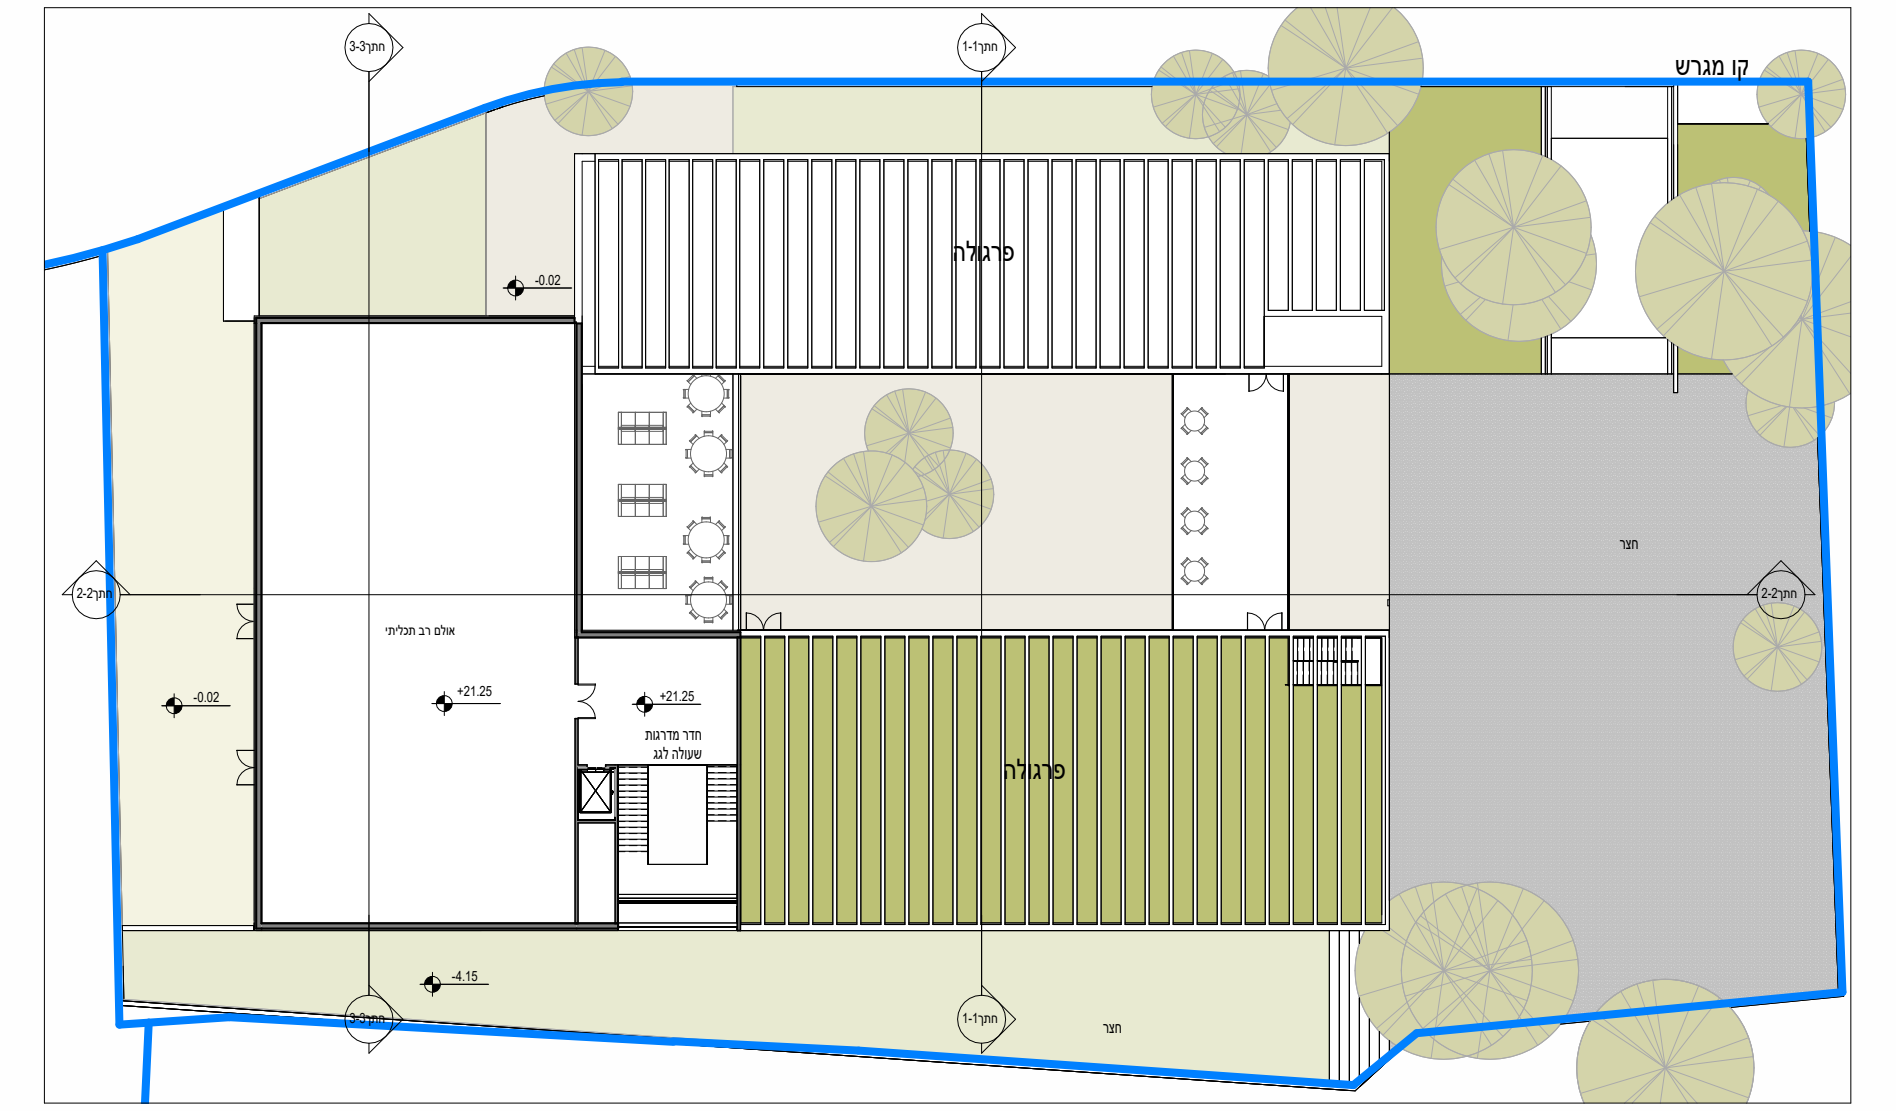
תכנית קומה חמישית
1 : 200

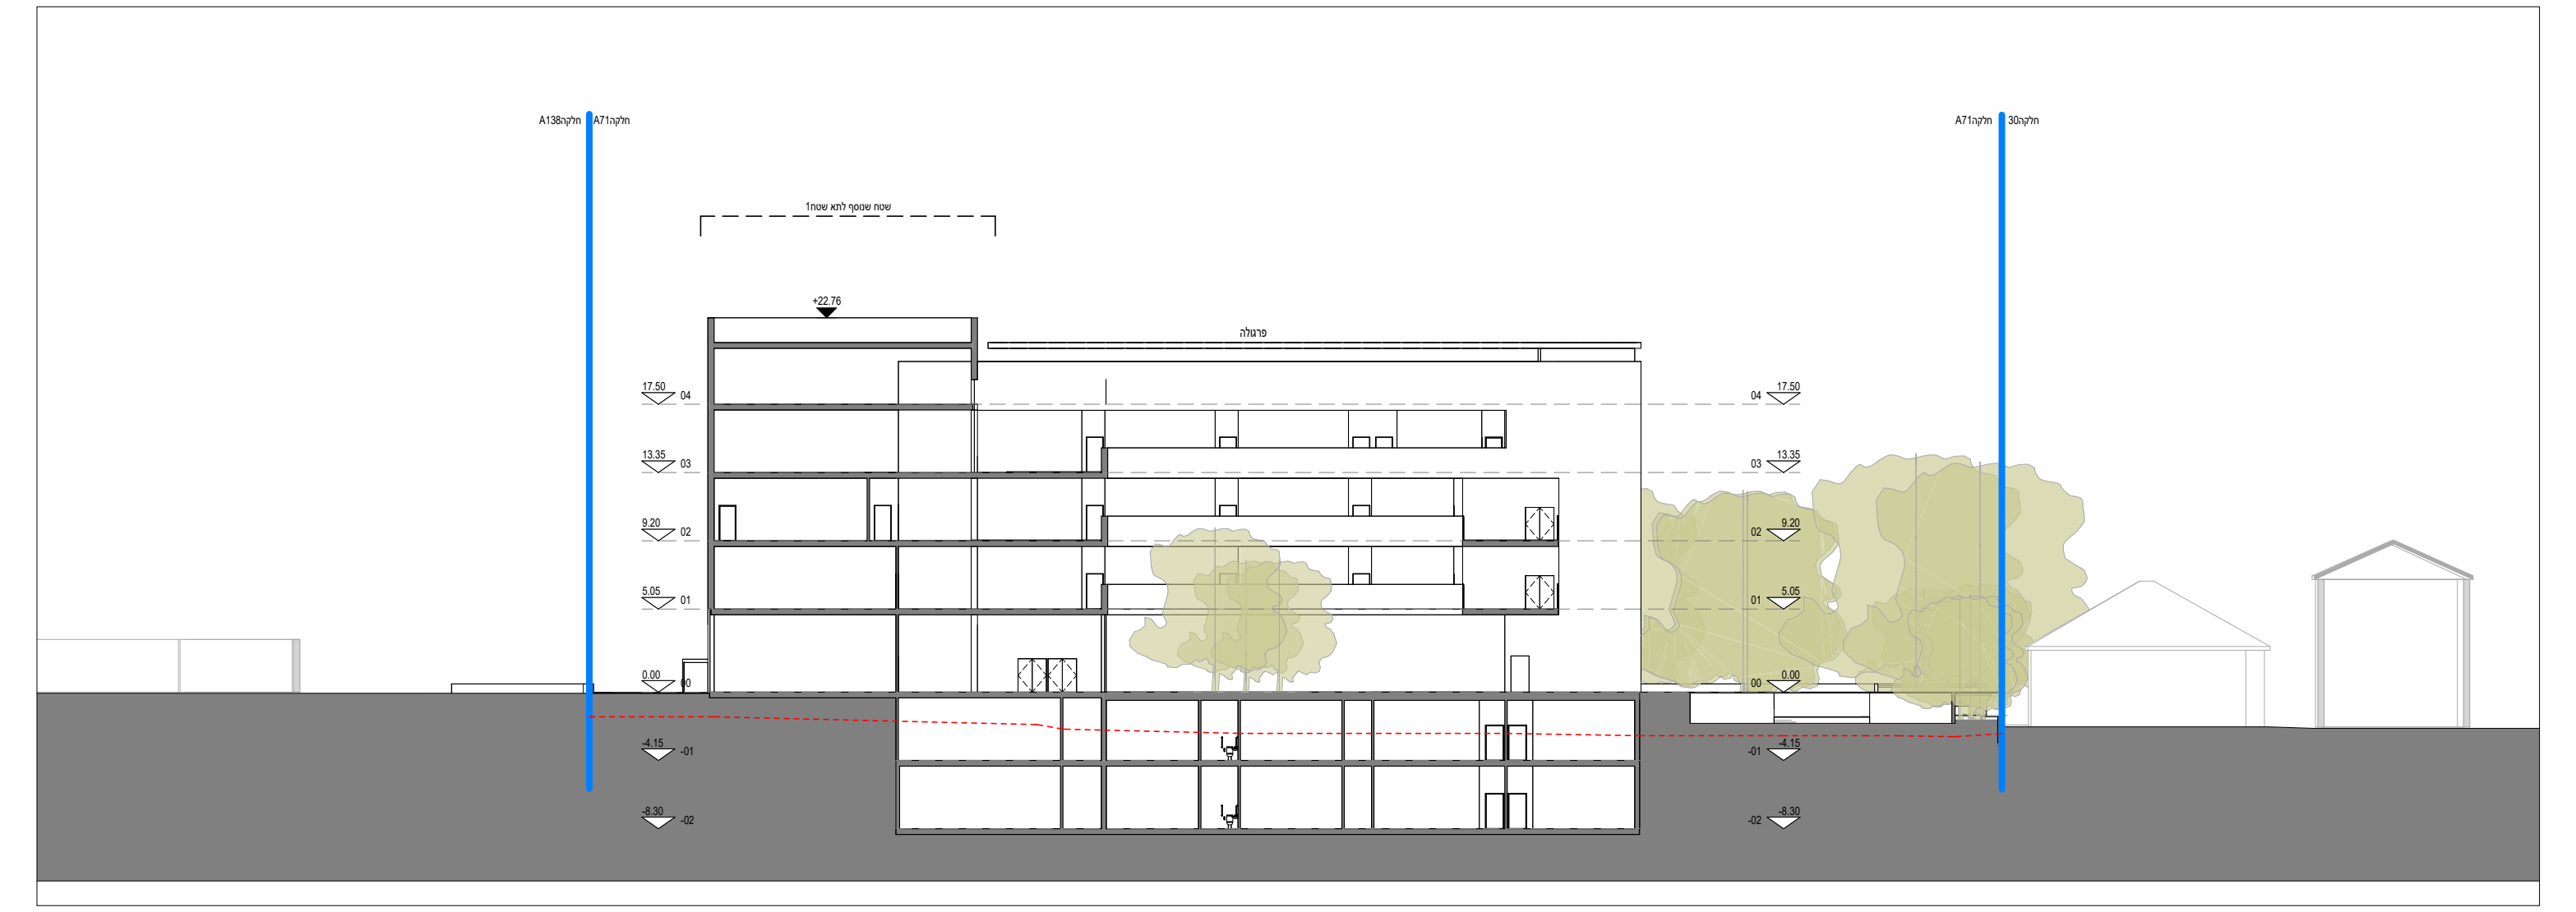
חתך2-2
1 : 200

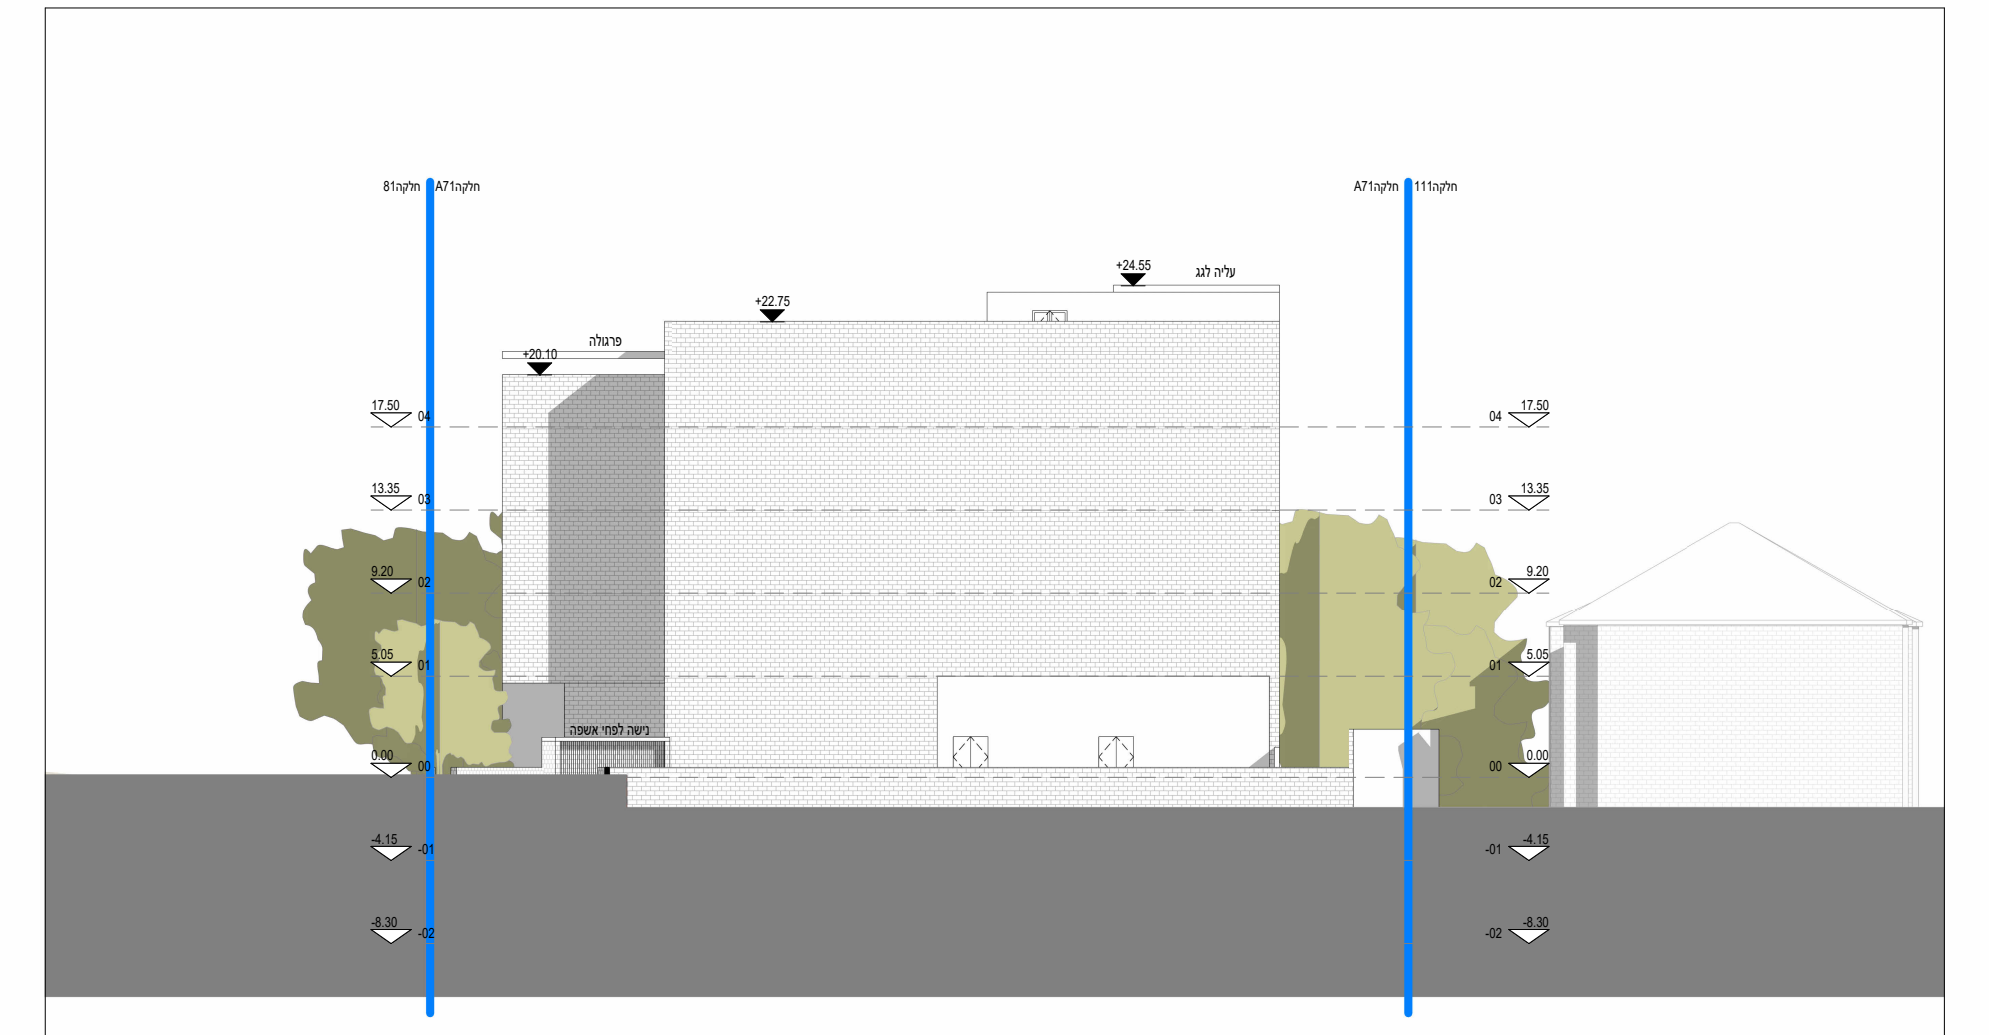
חזית נפחית מערבית
1 : 200

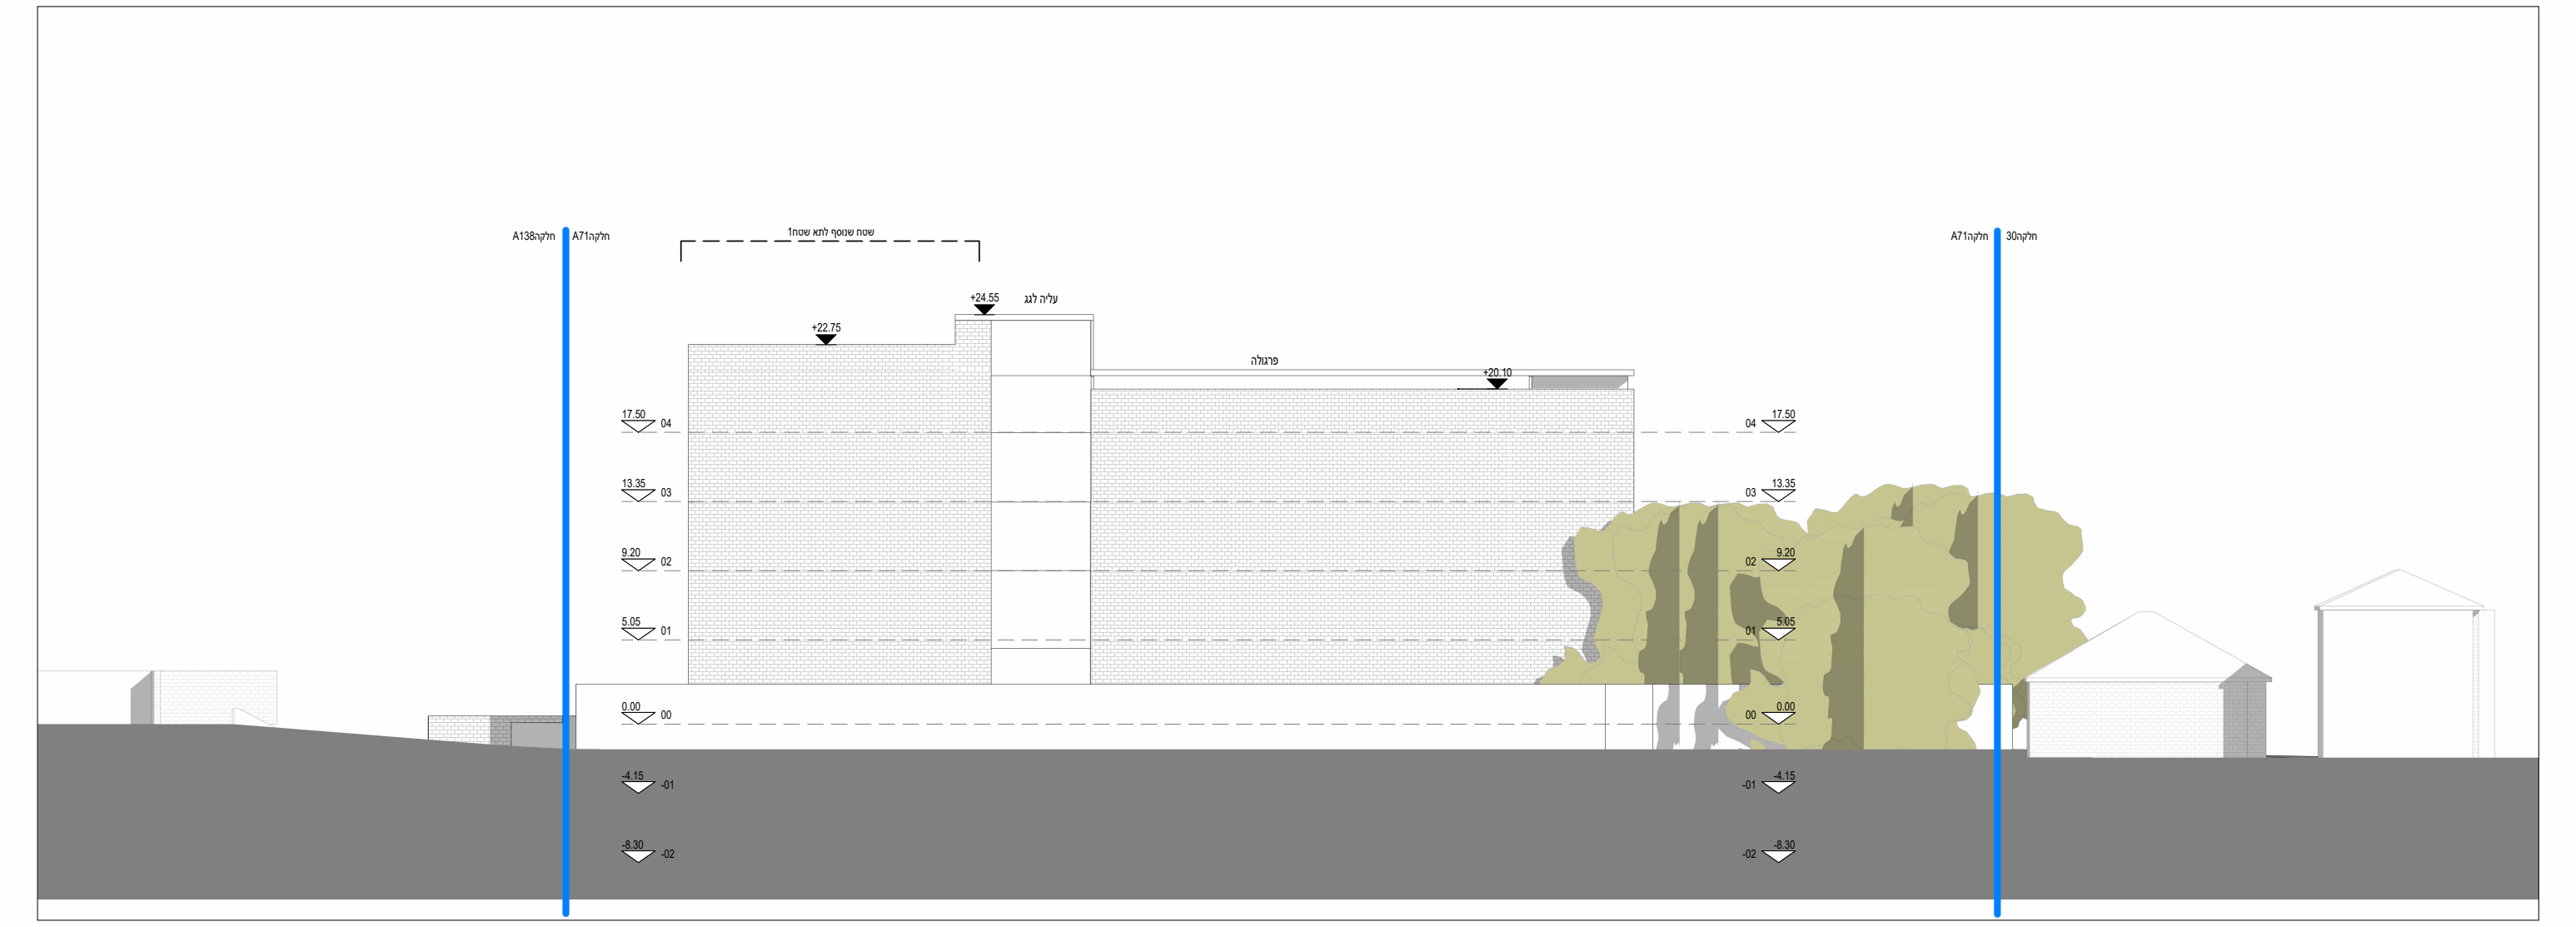
חזית נפחית דרומית
1 : 200

שמות וחתימות:

עורך התוכנית	שם: **שיפמן-נתן אדריכלים**	מס' רישיון: 88904
	כתובת: **יד חרוצים 6, ירושלים**	
	טלפון: 02-6740674	פקס: 02-6740675
	דוא"ל: info@gsna.co.il	
	תאריך: 15/06/2026	חתימה: