חוק התכנון והבניה, התשכ"ה - 1965
תכנית מפורטת

תכנית מס' 101-1451699

תכנית איחוד וחלוקה
עבור מדרשיית הרטמן לבנות

נספח איחוד וחלוקה

מחוז	ירושלים
מרחב תכנון מקומי	ירושלים
רשות מקומית	עיריית ירושלים
ישוב	ירושלים
שכונה	קטמון הישנה
רחוב	הצפירה
הוכן עבור	מוריה

טבלת גושים וחלקות

מס' גוש	חלק/כל הגוש	מספרי חלקות בשלמות	מספרי חלקות בחלק
30009	חלק	71, 138	---

מקרא

גבול תכנית	━
שטח לאיחוד וחלוקה חדשה	⬚
גבול גוש ומספרו	30009
גבול חלקה ומספרה	71
גבול תא שטח ומספרו	71A
להריסה	━

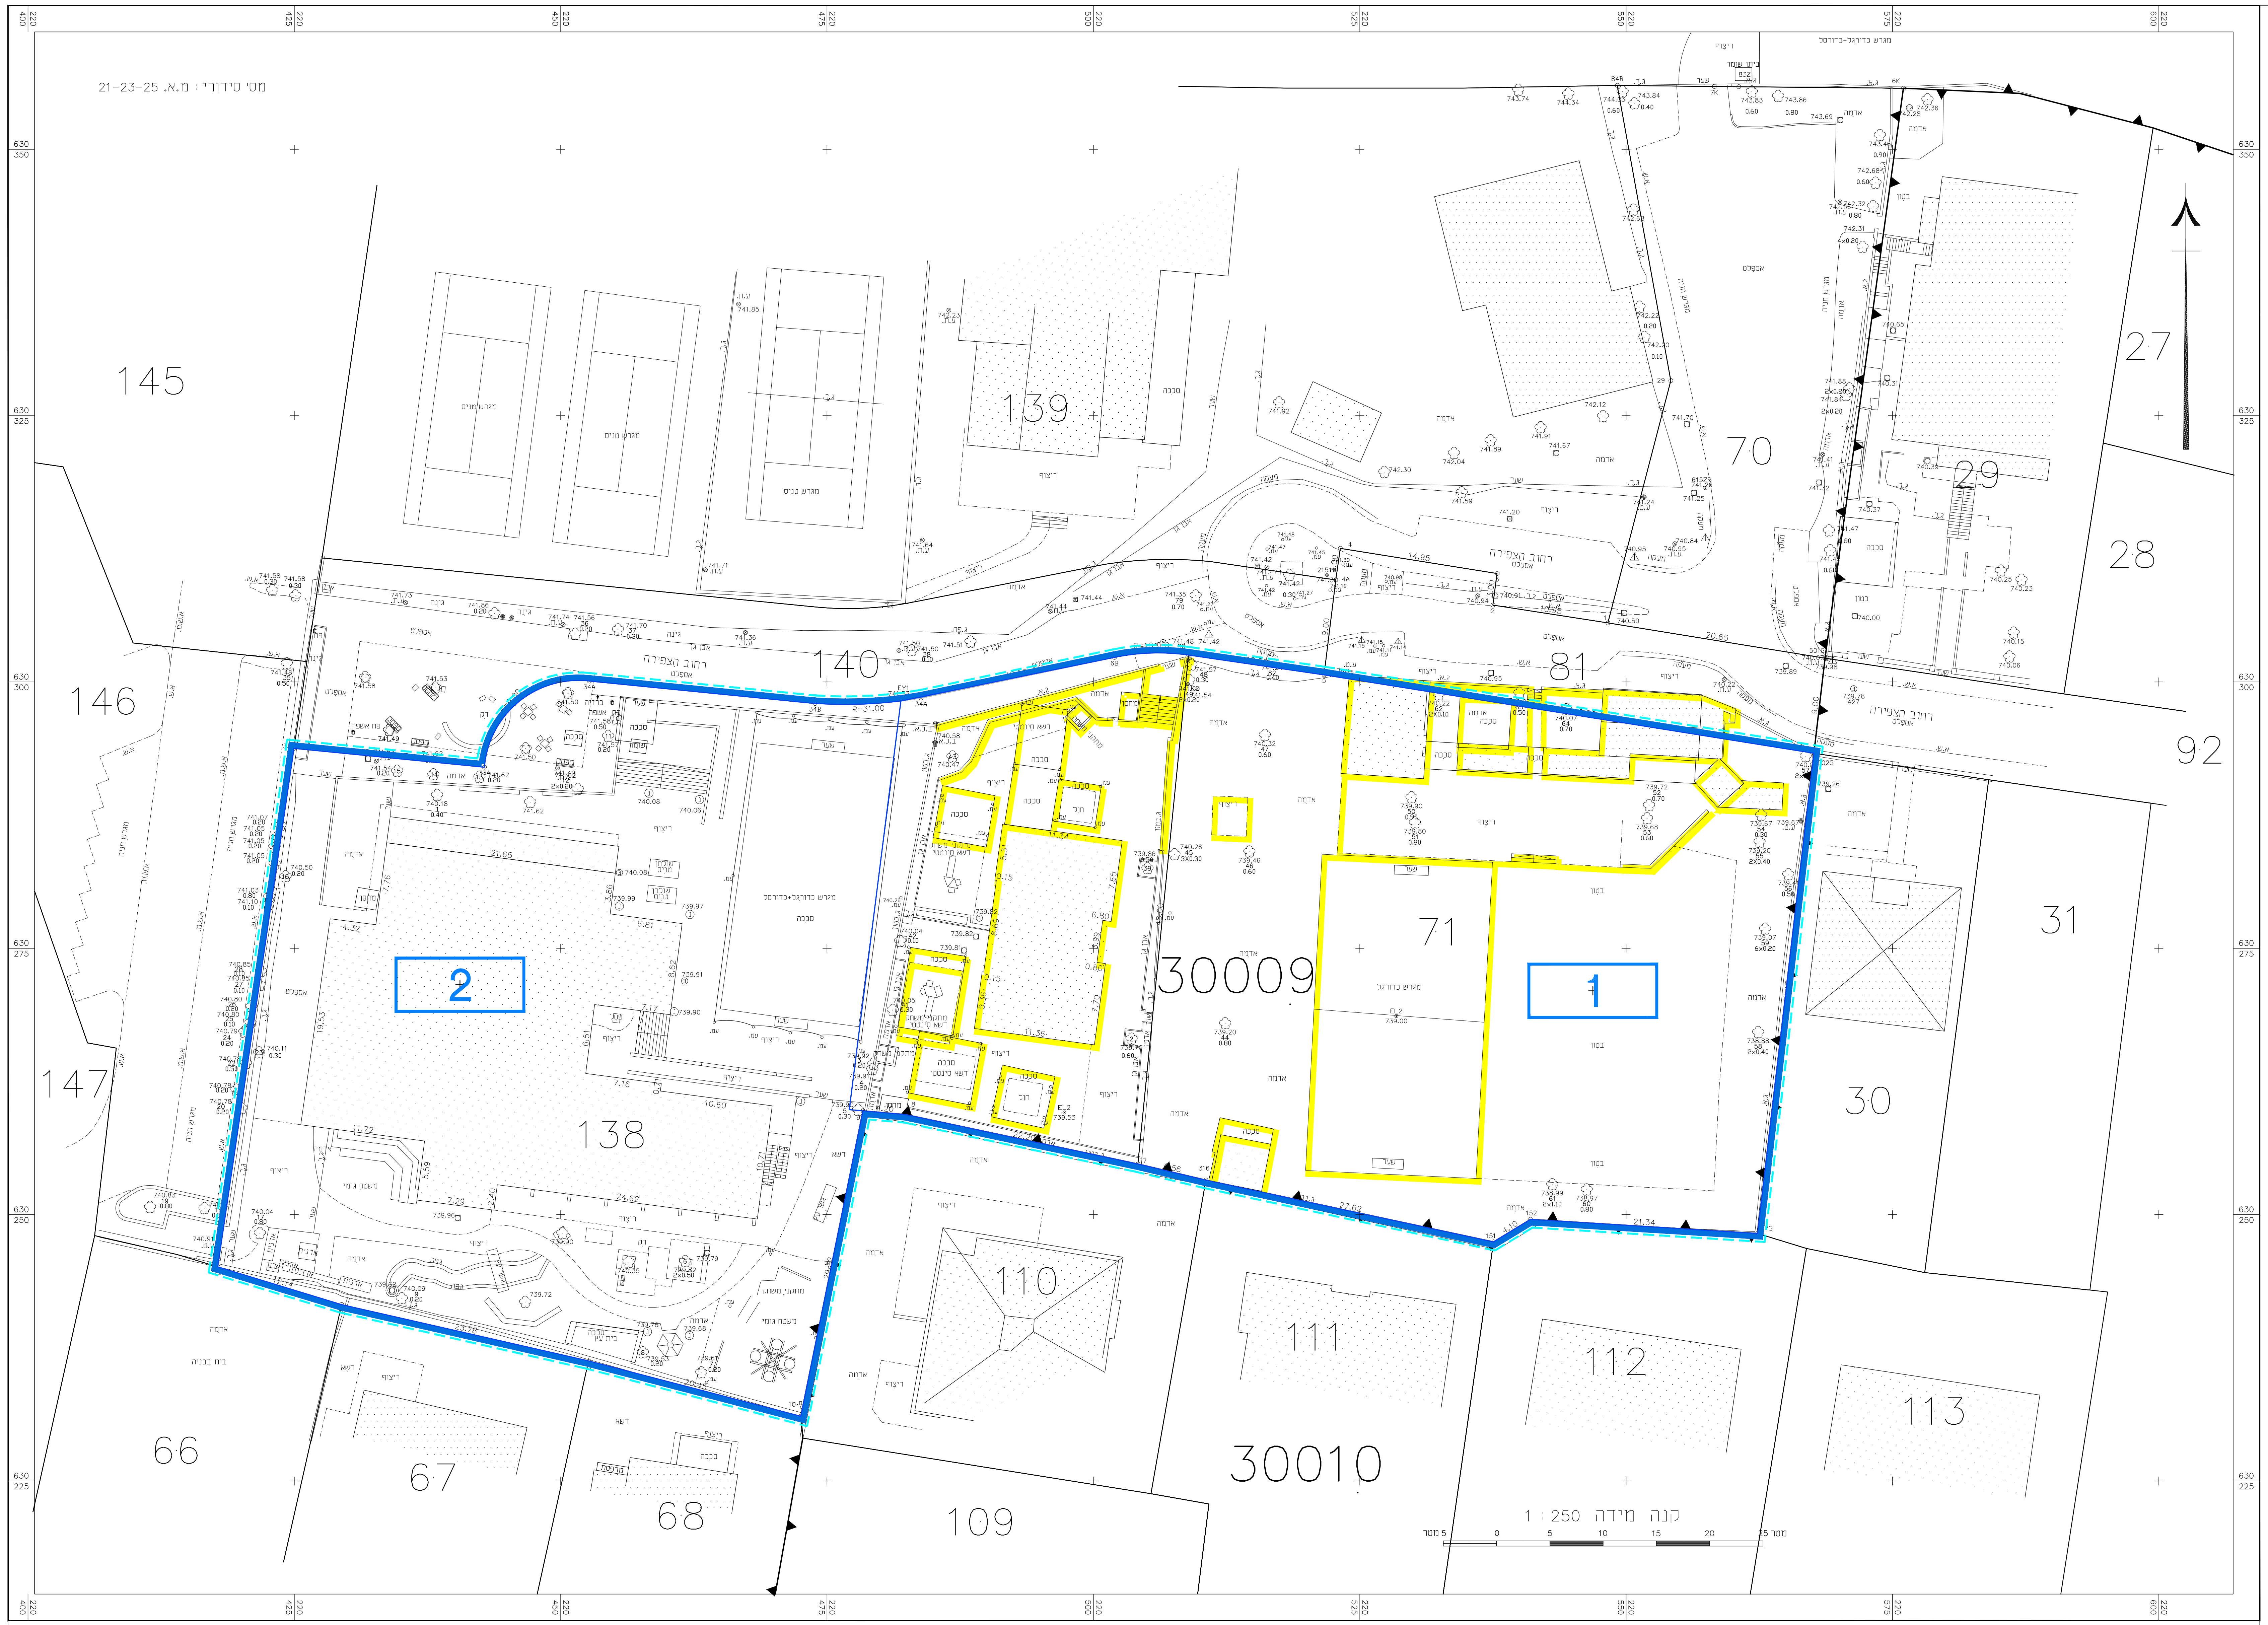

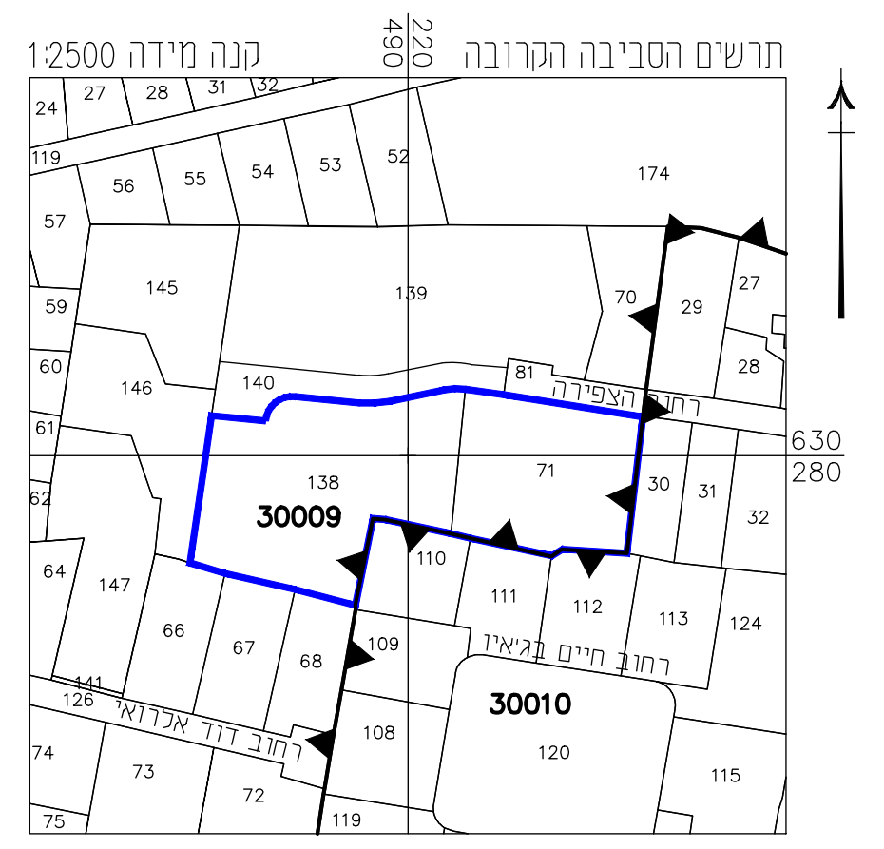

טבלת איחוד וחלוקה מחדש:

נתוני מקרקעין			נתוני מצב מאושר				מצב מוצע לפי הוראות תכנית מס' 101-1451699 זו				
מספר גוש	מספר חלקה	שטח רשום של החלקה	מס' תב"ע	מבנים ומוסדות ציבור לחינוך	שטח לבניני ציבור	סה"כ שטח מתוך החלקה	מספר תא שטח	מבנים ומוסדות ציבור	סה"כ הפרשות	סה"כ	הערות
		במ"ר		במ"ר	במ"ר	במ"ר		במ"ר	במ"ר	במ"ר	
30009	71	2835	101-0588897	2835		2835	1	4004	4004	4004	תא השטח המסומן במס' 1 יירשם על שם עיריית ירושלים
30009	138	4531	2878		4531	4531	2	3362	3362	3362	תא השטח המסומן במס' 2 יירשם על שם עיריית ירושלים
סה"כ		7366		2835	4531	7366	סה"כ	7366	7366	7366	

הערות:

1. סה"כ ההפרשות לצרכי ציבור בתחום האיחוד והחלוקה לפי תכנית מס' 101-1451699 זו, הם כ-7366 מ"ר שהם כ-100% משטח התוכנית לאיחוד וחלוקה.
2. אני, יורם אלישיב מודד מוסמך, חתום מטה, מאשר בזה כי חישוב השטחים , שבטבלת איחוד וחלוקה נכונים. בדקתי החישוב פלנימטרית ובשיטה דיגיטלית.

יורם אלישיב - מודד מוסמך
רשיון מס' 985
15.06.2026

מספר התוכנית: 21-23-25

רמת דיוק הקו הכחול והקדסטר: 3
1 = מדידה גרפית
2 = קו כחול (בלבד) ברמה אנליטית
3 = מדידה אנליטית מלאה ברמת תצ"ר

1. המדידה המקורית:
הריני מצהיר בזאת כי מדידת המפה הטופוגרפית/ המצבית המהווה רקע לתוכנית זו, נערכה על ידי :

ביום: 16.03.2025

והיא הוכנה לפי הוראות נוהל מבא"ת ובהתאם להוראות החוק ולתקנות המודדים שבתוקף.

שם המודד: יורם אלישיב

מספר רישיון: 985

חתימה: ________ **תאריך:** ________

הערות
1. הרשת והגבהים קשורים לרשת הארצית בנקי טריג מס' 1448K,1447K ו- 82M. הגבהים בהתאמה: 780.03 מ', 827.03 מ', 818.723 מ'.
2. גבולות החלקה 138 נלקחו מתצ"ר מס' אליפסה 225/1971 ברשת ישנה.
3. נקודות גבול K7, 83Z, 84B, 6K נלקחו מתצ"ר 1277/2013
4. נקודות גבול חלקות 81,71,70 יחשבו לפי פנקס שדה 15130
5. התמרה 50000.20, 500000.44 נעשתה על פי פינות בית ישנים
6. המדידה בוצעה כרקע לתב"ע ותואמת למיפרט מבא"ת 2006 (נובמבר 2010).

תאריך	פרטי מדידה ועדכונים	חתימה
15.06.2026	נספח איחוד וחלוקה	
27.03.2025	מפה מצבית טופוגרפית	

אלישיב מדידות והנדסה בע"מ
הנדסה אזרחית וגיאודטית,מדידות ומיפוי אוירי
רח' הרכבים 9, ירושלים טל. 02-6793012, פקס 02-6797852
E-MAIL : OFFICE@ELYASHIV1.CO.IL

שם שרטוט : מ.א. 21-23-25
מיקום המדידה : רחוב הצפירה 27

מייסד: מיכאל אלישיב ז"ל
רשיון מס' 196
מודד מוסמך ושמאי מקרקעין

יורם אלישיב - מודד מוסמך, רשיון מס' 985

אין להעתיק או להשתמש בתוכנית זו או בחלק ממנה ללא אישור בכתב מהמודד

לא לצרכי רישום