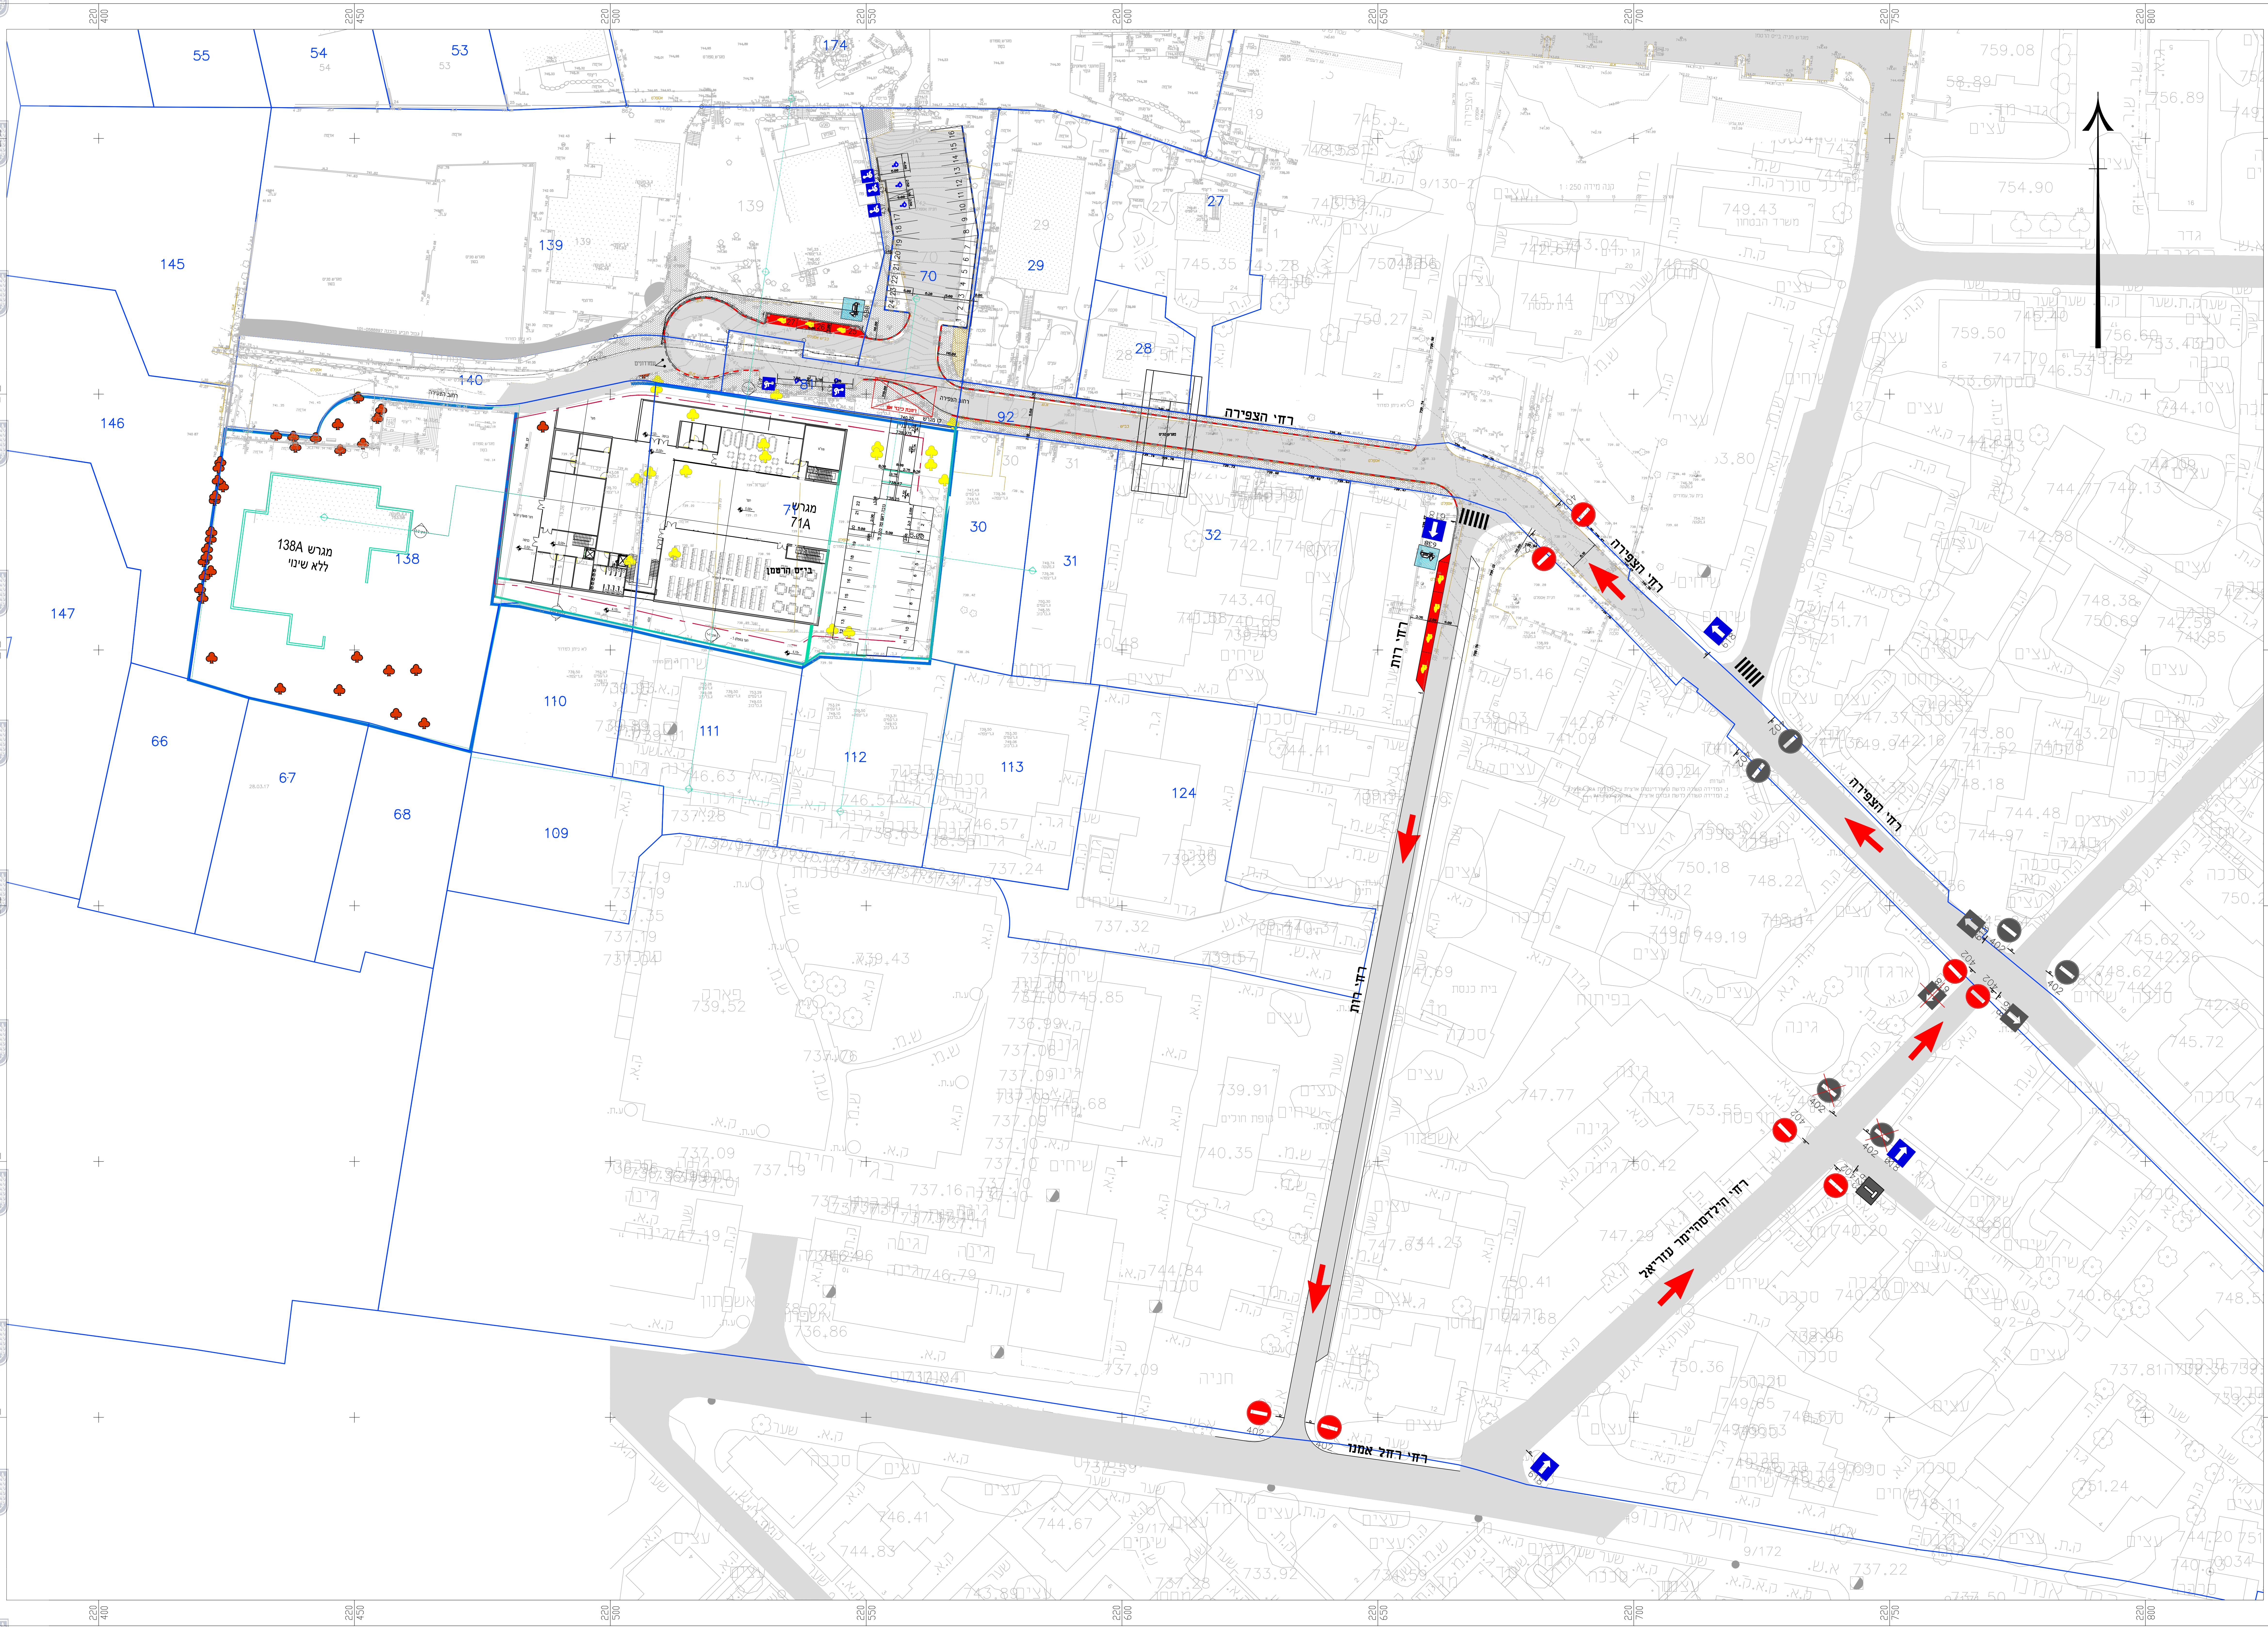
רח' הצפירה
רח' רות
רח' רחל אמנו
רח' הילדסהיימר עזריאל
מגרש 71A
בי"ס הרטמן
מגרש 138A
ללא שינוי
55
54
53
174
139
70
29
27
28
145
140
92
146
138
30
31
32
147
110
111
112
113
124
66
67
68
109

תכנית מספר	101-1451699

נספח תנועה
תכנית איחוד וחלוקה
עבור מדרשיית הרטמן לבנות

גליון 1 מתוך 1

קנ"מ	1:500
תאריך עדכון	23\06\2026

מקרא:

גבול תכנית	━
קו בניין	━ · ━ · ━
תוכנן ע"י אחרים	━
גבול תא שטח מתוכנן	━
מס' תא שטח	1
עץ לשימור	♣
עץ לעקירה	♣
מדרכה קיימת	▨
מדרכה מתוכננת	▨
אספלט קיים	☐

טבלת מאזן חניה

שימוש	רכב פרטי			אופניים	
	כיתות	תקן	דרוש	תקן	דרוש
בי"ס על יסודי	18	2:1	36	1:10 תלמידים	54
מועדון נוער	400	1:50	10	1:100	4
סה"כ דרוש			46		58
מתוכנן			46		58

תוכננו 7 עמדות הורדה לתלמידים ברח' הצפירה וברחוב רות.
חניות נכים 3 לרכב רגיל 2 לרכב גבוה

שטרן תנועה וכבישים בע"מ

טל: +972-2-6569010 • Tel: +972-2-6569010 פקס: +972-1532-6569010 • Fax: +972-1532-6569010
e-mail: office@ysterneng.com • web: www.ysterneng.com
כתובת: רחוב בית זכריה 1, אלעזר 9094200
Address: 1, Bet Zecharia st., Elazar 9094200

שמות וחתימות:

חתימה:

יוסף שטרן
מהנדס תנועה וכבישים
מ.ר. 112234