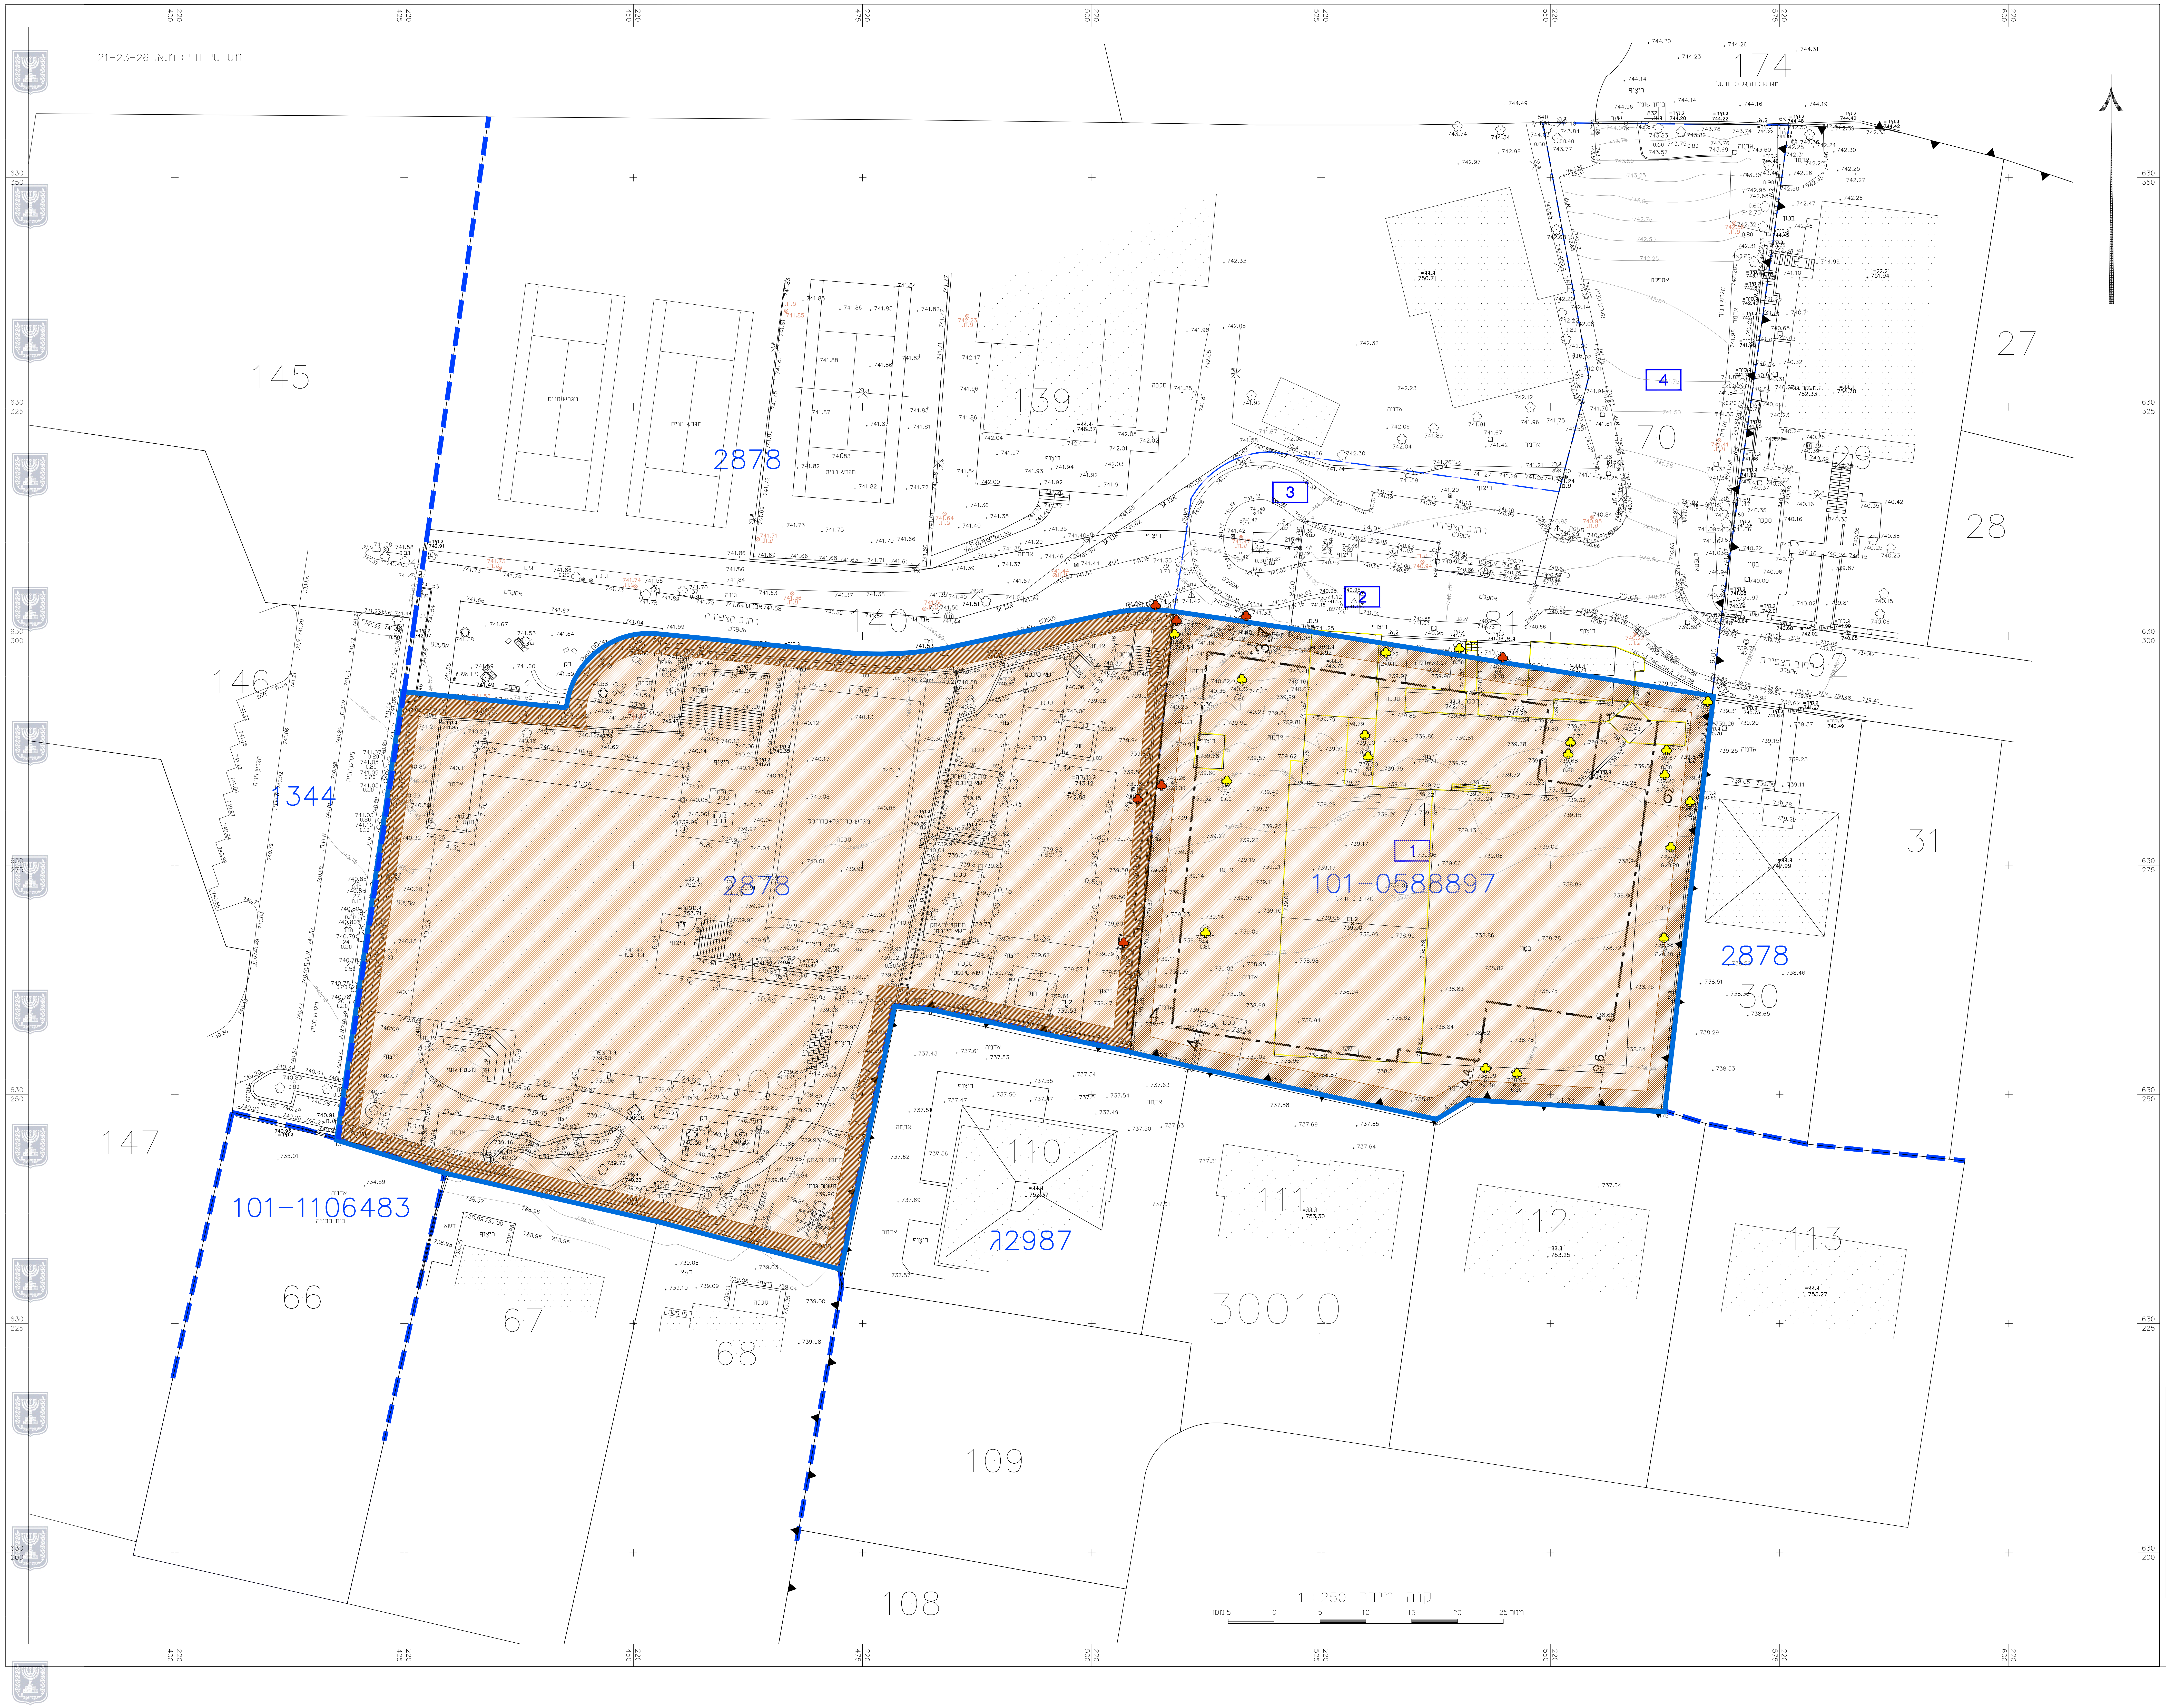

מקרא
מצב מאושר

גבול תכנית מוצעת	▭
גבול תכנית מאושרת ומספרה	2878
שטח לבניני ציבור	🟫
מבנים ומוסדות ציבור לחינוך	🟫
קו בנין	—·—
קו בנין תחתי (תת-קרקעי)	——
להריסה	——
עץ/עצים כריתה	♣
עץ/עצים לשימור	♣
בנין קיים	▨
גבול גוש קיים	▲▼
מספר גוש קיים	30009
גבול חלקה קיימת	——
מסי חלקה קיימת	138
גבול מגרש מאושר	— —
מסי מגרש מאושר	①
גבול תא שטח מאושר	——
מספר תא שטח	1
מספר הדרך קו בנין רוחב הדרך	⊗

חוק התכנון והבניה, התשכ"ה - 1965
תכנית מתאר מקומית

תכנית מס' 101-1451699

שם התכנית
תוכנית איחוד וחלוקה עבור
מדרשיית הרטמן לבנות

תשריט מצב מאושר גליון 1 מתוך 1

מחוז	ירושלים
מרחב תכנון מקומי	ירושלים
רשות מקומית	עירית ירושלים
ישוב	ירושלים
כתובת	רחוב הצפירה 27
הוכן עבור	מוריה
תאריך	18.03.2025

טבלת גושים וחלקות

מסי גוש	חלק/כל הגוש	מספרי חלקות בשלמות	מספרי חלקות בחלק
30009	חלק	71,138	

על פי תכניות מאושרות :
ג2987, 2878 1344
101-0588897 101-1106483

תרשים הסביבה

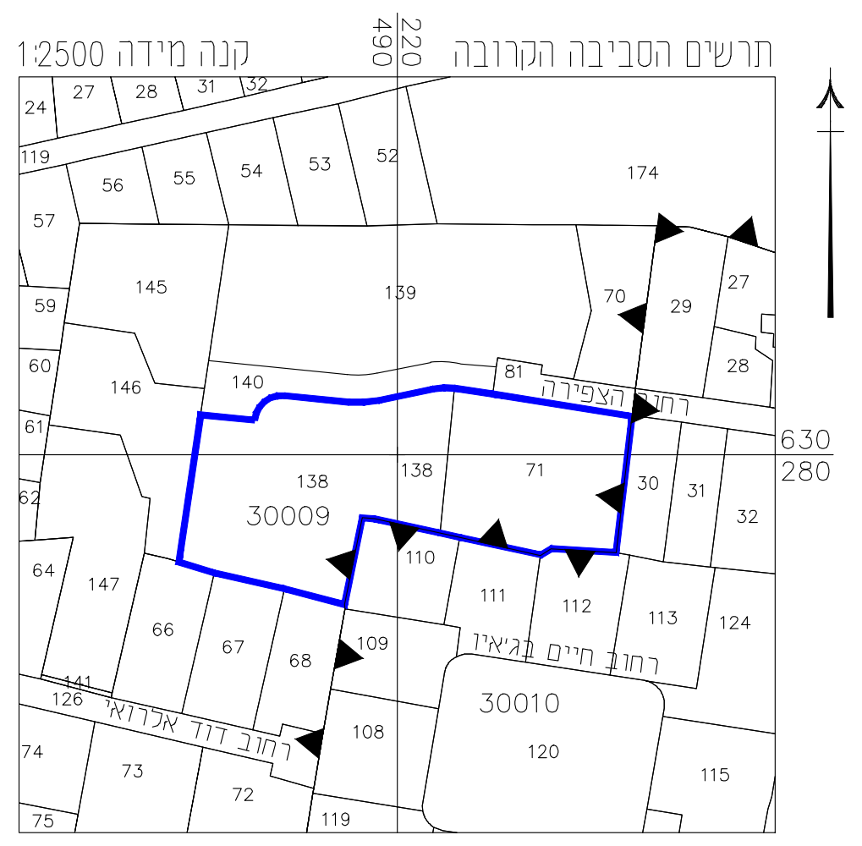

הערות
1. הרשת והגבהים קשורים לרשת הארצית בנקי טריג מסי 1447K,1448K ו- 82M.
הגבהים בהתאמה: 780.03 מ', 827.03 מ', 818.723 מ'.
2. גבולות החלקה 138 נלקחו מתצ"ר מסי אליפסה 225/1971 ברשת ישנה.
3. נקודות גבול 6K, 84B, 83Z, K7 נלקחו מתצ"ר 1277/2013
4. נקודות גבול חלקות 81,71,70 יחשבו לפי פנקס שדה 15130
5. התמרה 500000.44, 50000.20 נעשתה על פי פינות בית ישנים
6. המדידה בוצעה כרקע לתב"ע ותואמת למיפרט מבא"ת 2006 (נובמבר 2010).

מספר התוכנית: 21-23-26

רמת דיוק הקו הכחול והקדסטר: 3
1 = מדידה גרפית
2 = קו כחול (בלבד) ברמה אנליטית
3 = מדידה אנליטית מלאה ברמת תצ"ר

1. המדידה המקורית:
הריני מצהיר בזאת כי מדידת המפה הטופוגרפית/ המצבית המהווה רקע לתוכנית זו, נערכה על ידי :

ביום: 05.05.2026

והיא הוכנה לפי הוראות נוהל מבא"ת ובהתאם להוראות החוק ולתקנות המודדים שבתוקף.

שם המודד: יורם אלישיב

מספר רישיון: 985

חתימה: ____________ **תאריך:** ____________

תאריך	פרטי מדידה ועדכונים	חתימה
	תשריט מצב מאושר	
09.06.2026	מפה מצבית טופוגרפית	
27.03.2025	מפה מצבית טופוגרפית	

אלישיב מדידות והנדסה בע"מ
הנדסה אזרחית וגיאודטית,מדידות ומיפוי אוירי
רח' הרכבים 9, ירושלים טל. 02-6793012, פקס 02-6797852
E-MAIL : OFFICE@ELYASHIV1.CO.IL

שם שרטוט : מ.א. 21-23-26
מיקום המדידה : רחוב הצפירה 27

מייסד: מיכאל אלישיב ז"ל
רשיון מסי 196
מודד מוסמך ושמאי מקרקעין

יורם אלישיב - מודד מוסמך, רשיון מסי 985

אין להעתיק או להשתמש בתוכנית זו או בחלק ממנה ללא אישור בכתב מהמודד

לא לצרכי רישום