תוכנית
1:750

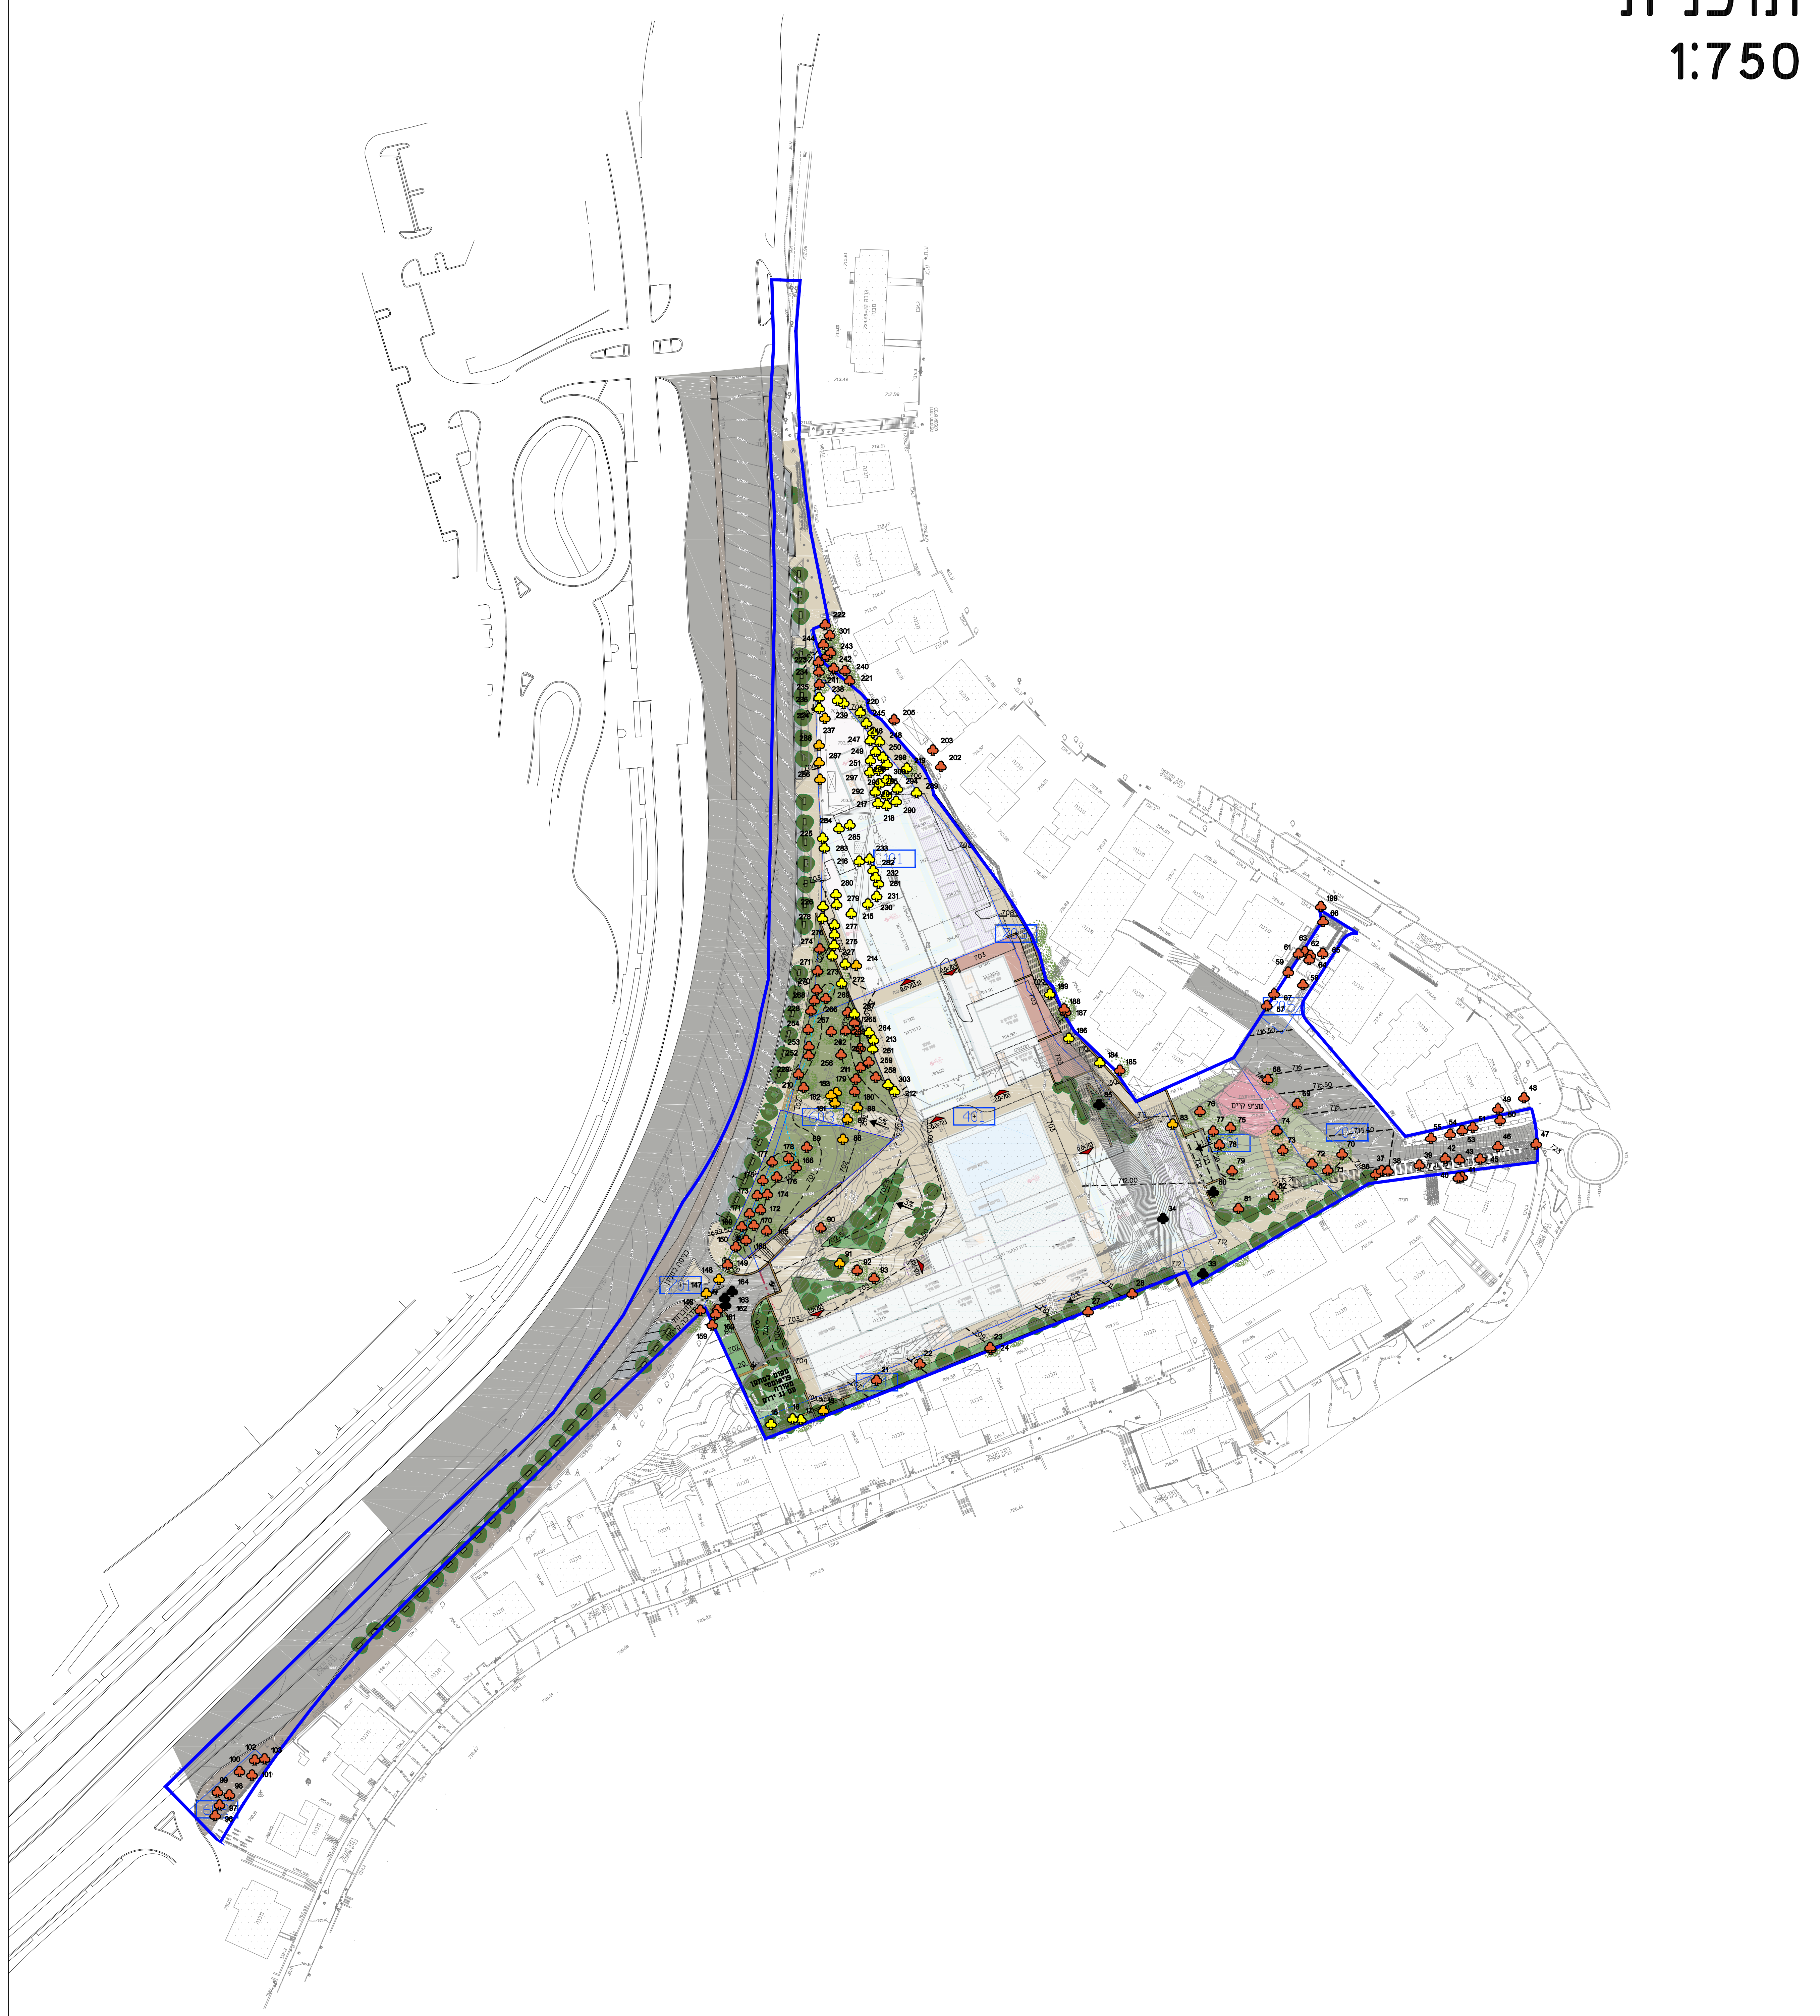

עקרונות מנחים לתכנון

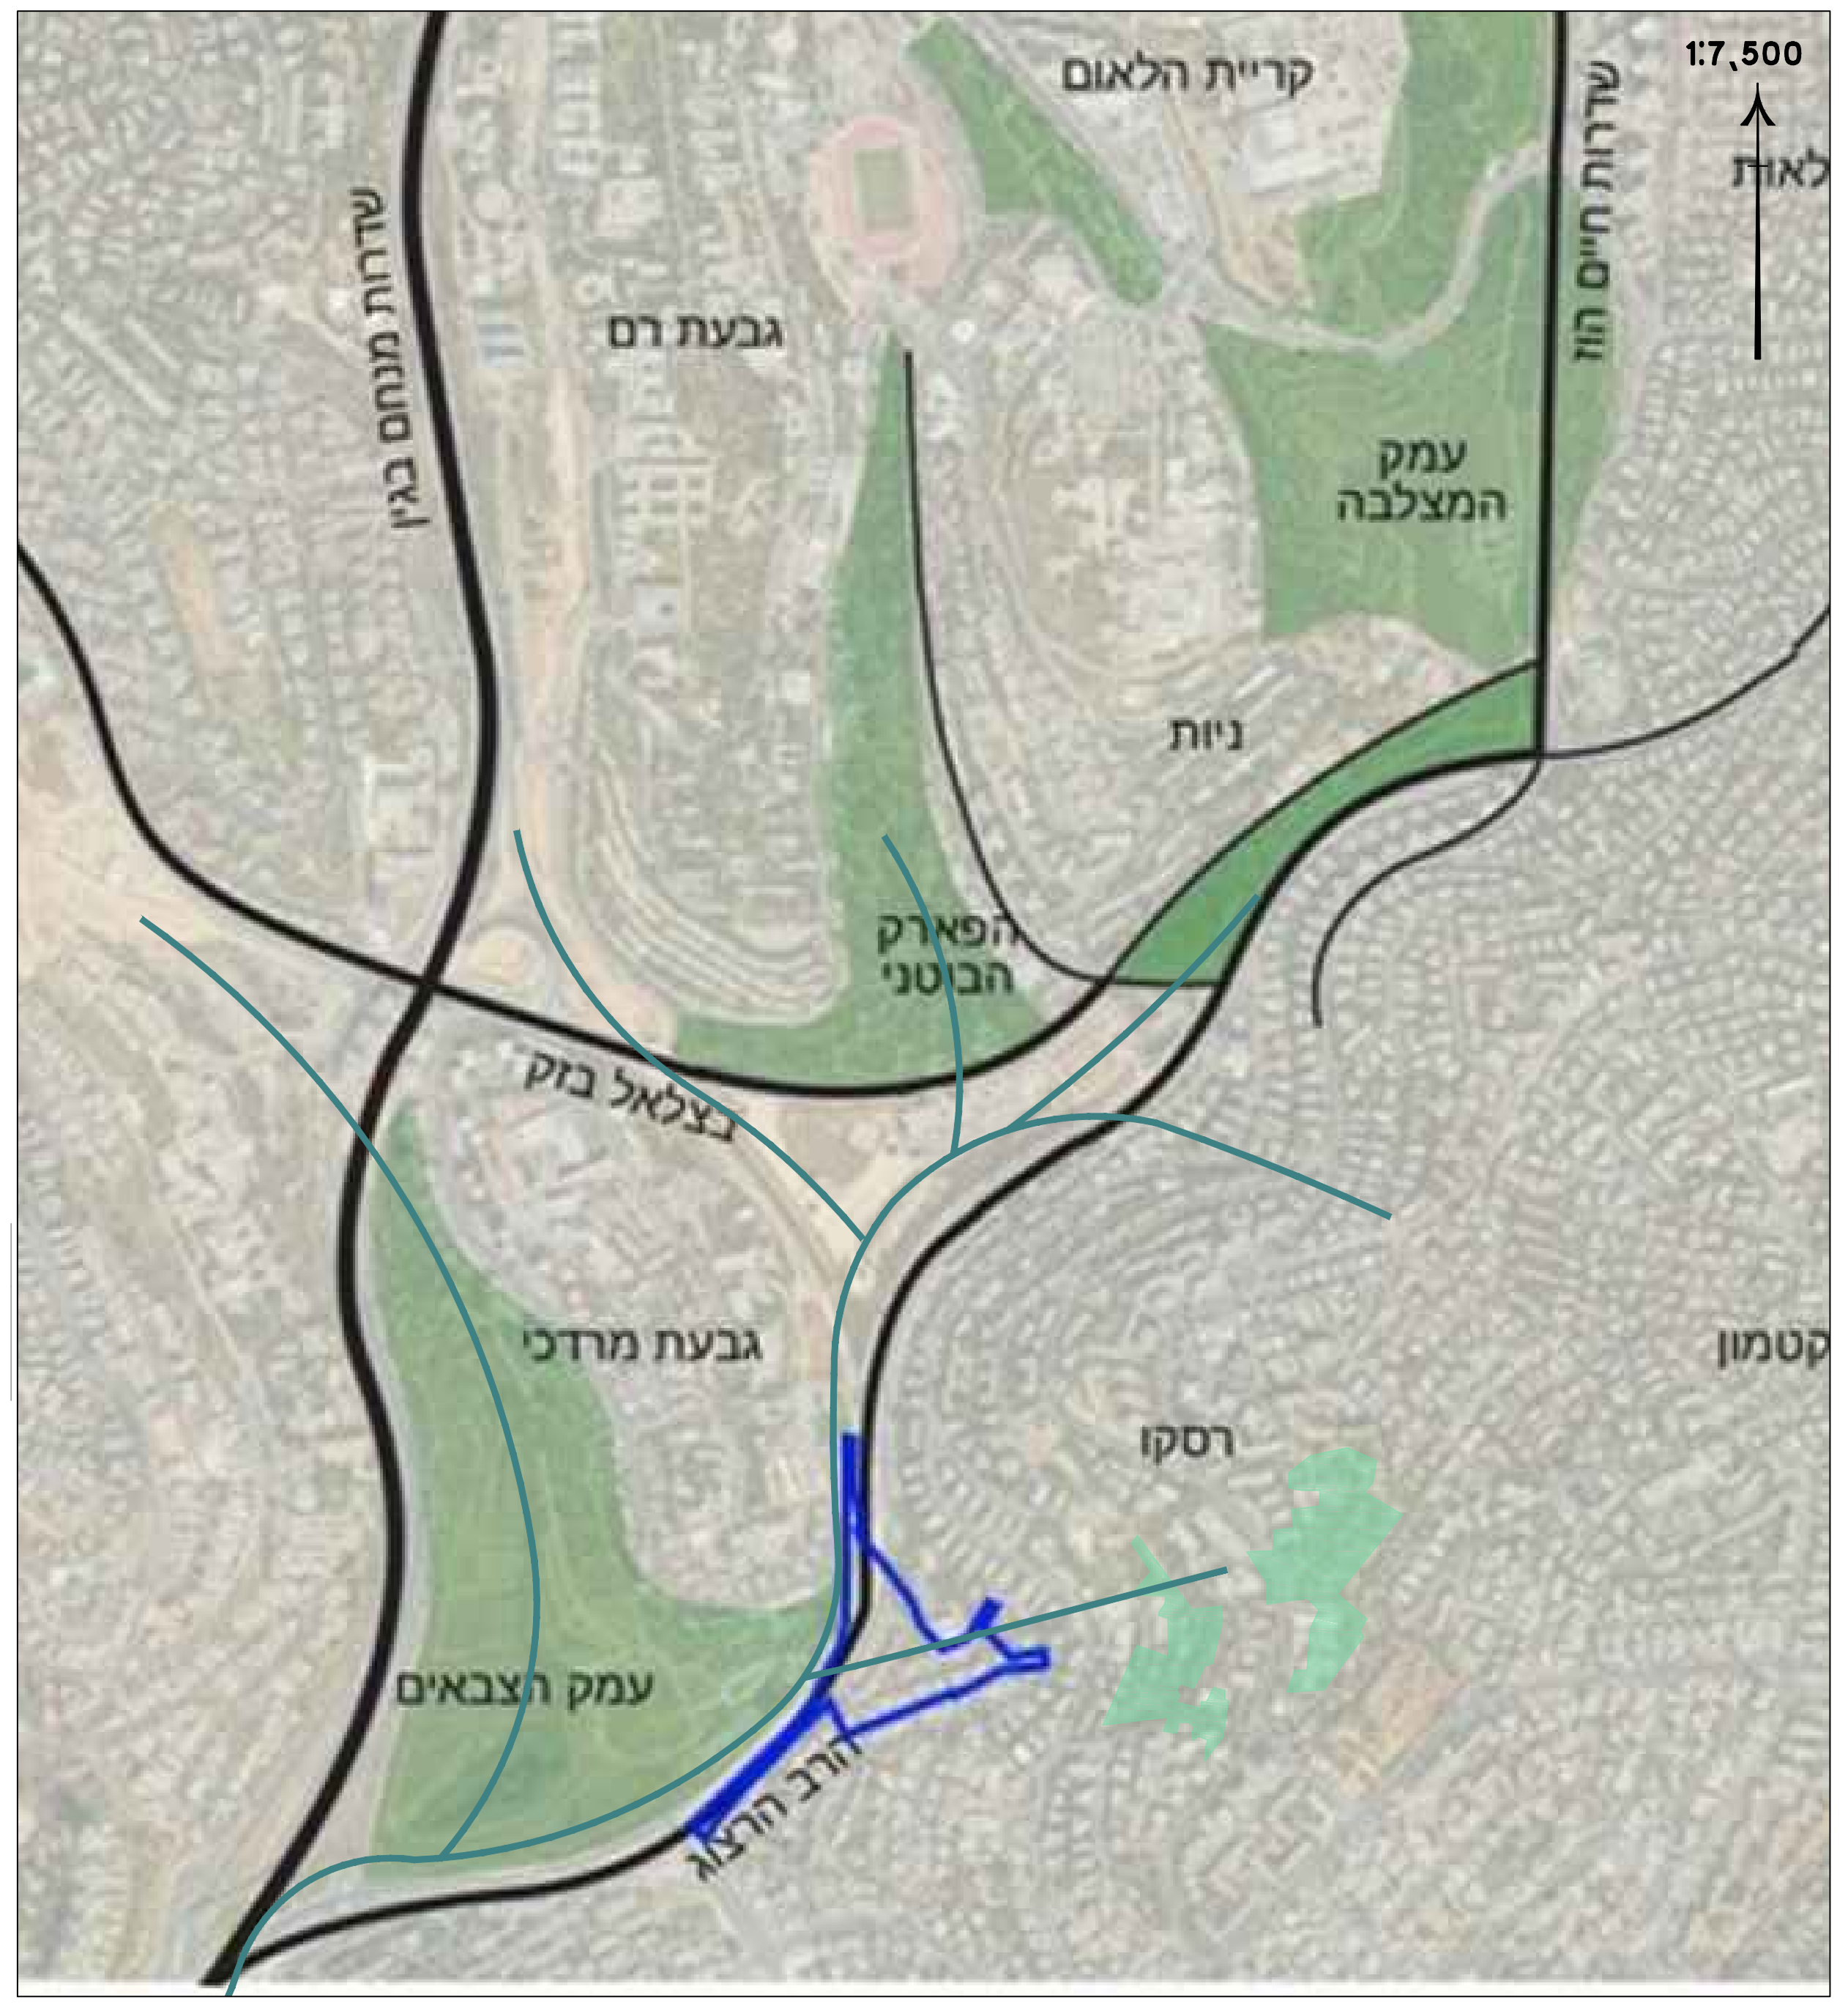

רצף שטחים פתוחים וניקוז

שטח התוכנית נמצא על ערוץ נחל רחביה הקושר בין השטחים הפתוחים הגדולים של מרכז העיר – גן סאקר, עמק המצלבה, הגן הבוטני ועמק הצבאים, המוגדרים כשטחי טבע עירוני ומנוקזים דרום מערבה לנחל רפאים.
את שטח התוכנית עצמה מנקז ערוצון קטן המתחבר למערכת הניקוז של עמק הצבאים.

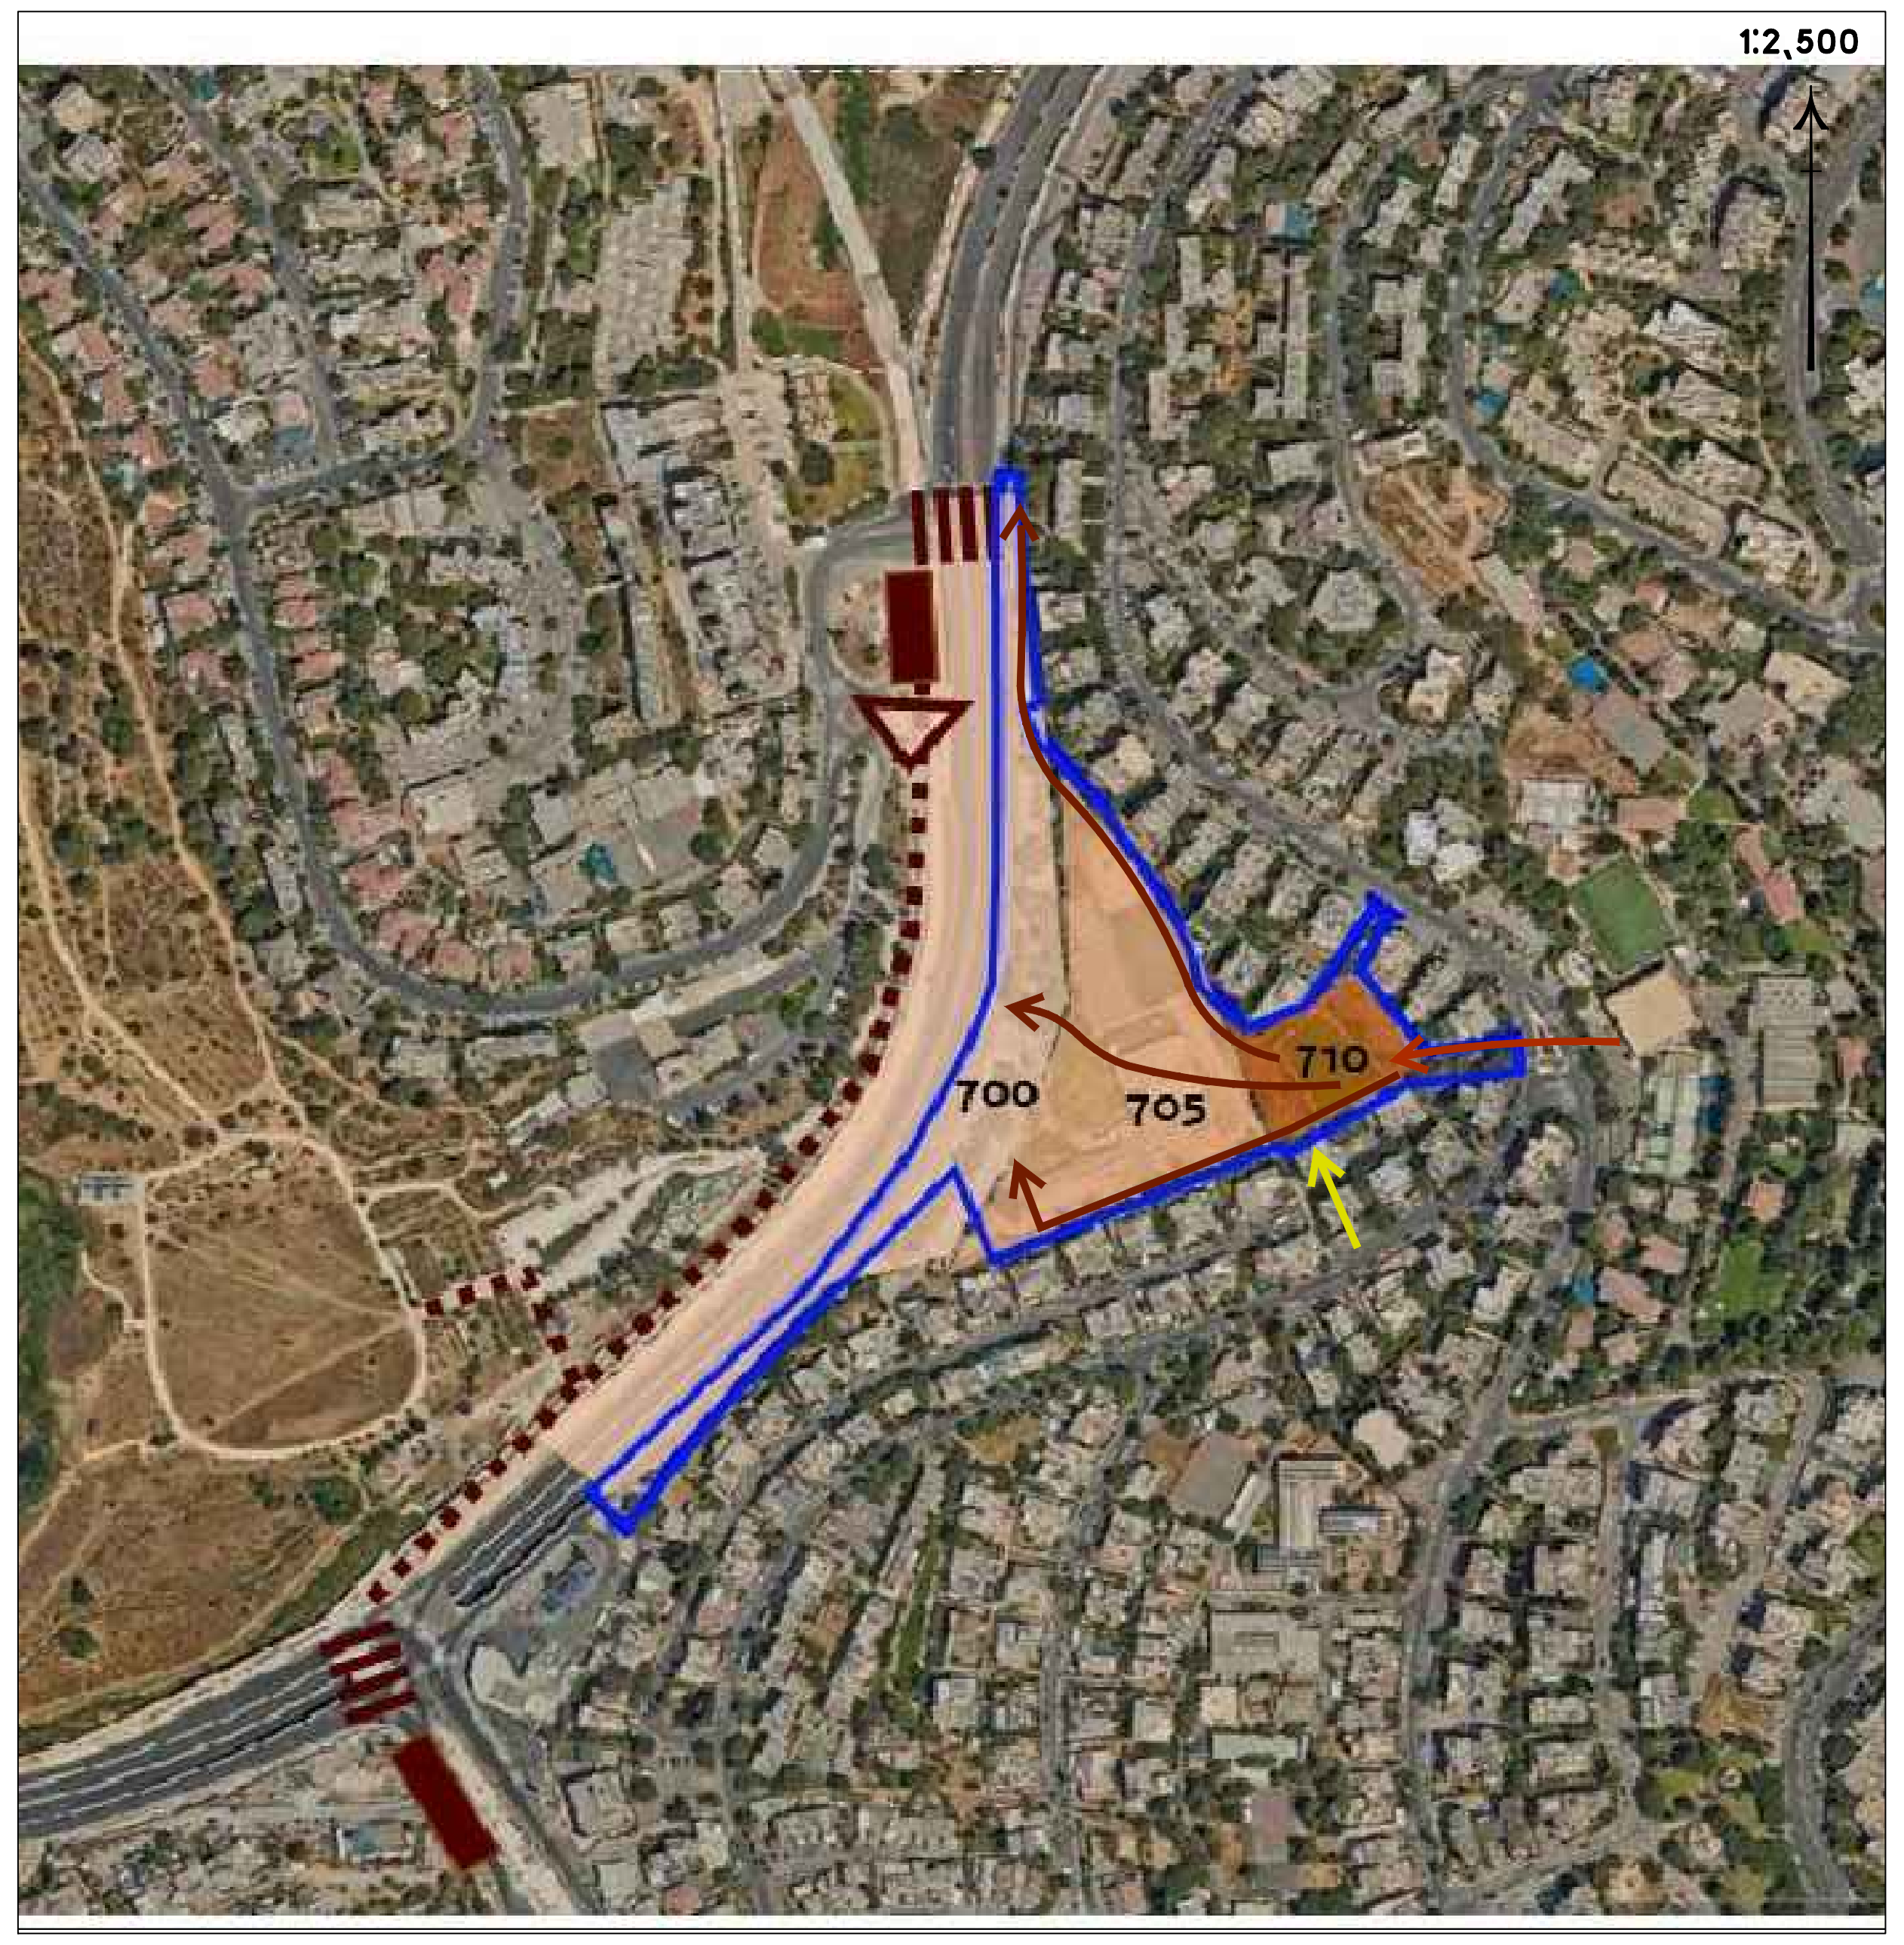

מורפולוגיה וקישוריות

שטח התוכנית מבונה בשלוש טרסות טופוגרפיות –
הראשונה – לאורך רחוב הרצוג, משמשת בעיקר כחניה,
השניה – מפלס בנין בית הנוער הקיים,
השלישית – שצ"פ קיים במפלס רחוב התקופה.

קישוריות המתחם אל השכונה הסובבת אותו היא מוגבלת בשל הפער הטופוגרפי המשמעותי.
מטרת הפרוייקט היא להנגיש ולחבר את המתחם אל השכונה ולייצר קישוריות חדשה מהשכונה לרחוב הרצוג, וממנו – לעמק הצבאים, והלאה למערכת הטיילות ושבילי האופניים התופרת את דרום מערב העיר.

←	הנגשת חיבור מרחוב התקופה
←	חיבורים חדשים לרחוב הרצוג
←	חיבורים קיימים

חוק התכנון והבנייה, התשכ"ה – 1965
תוכנית מפורטת
101-1158146

בית הנוער העברי

נספח נוף גליון **1** מתוך **2**

מחוז	ירושלים
מרחב תכנון מקומי	עיריית ירושלים
רשות מקומית	ירושלים
ישוב	ירושלים
תאריך	19/09/24
שם התרשים	קנ"מ
תוכנית	1:750
סכמות	משתנה

שמות וחתימות:		
עורך הנספח	שם:אדר' אור כהנא תאגיד: רחל וינר אדריכלות ונוף בע"מ	חתימה:

מקרא

▬	גבול תוכנית
4	תא שטח
☐	בינוי
▬ ▪▪ ▬	גבולות חניון תת"ק
0.0=703 ▼	כניסה למבנה
▨	מדרכה קיימת
▨	מסעה קיימת
▨	מסעה מרוצפת
▨	חניה מוצעת
699.50	קו גובה חדש
304.20	מפלס פיתוח
▬	קיר פיתוח
▦	נקז מי נגר
〰	ערוץ ניקוז מי נגר
▨	ריצוף ריפ ראפ בתוואי שביל
▨	שביל קיים
▨	שביל מוצע
▥	גשר
▨	חצר מבנ"צ
▨	משטח פעילות קיים
🟩	חורשה קיימת לשימור
🟩	שצ"פ קיים לשימור
🟩	גינון מוצע
🟩	גג ירוק
●	עץ קיים לשימור
●	עץ חדש בשטחי גינון
●	עץ חדש במדרכות
♣	עץ לעקירה לפי סקר עצים
♣	עץ להעתקה לפי סקר עצים
♣	עץ לשימור לפי סקר עצים

רחל וינר | אדריכלות ונוף בע"מ
Rachelle Wiener | Landscape & Architecture Ltd
Or Kahana אור כהנא | Moshe Rucham משה רוחם
רח' כספי 9 ירושלים, מיקוד 9355409 , טל: 02-5670080, פקס: 02-5670090, email: office@wisl.co.il
9 caspi st. Jerusalem, 9355409, tel: 02-5670080, fax: 02- 56700900, email: office@wisl.co.il

אוגוסט '24

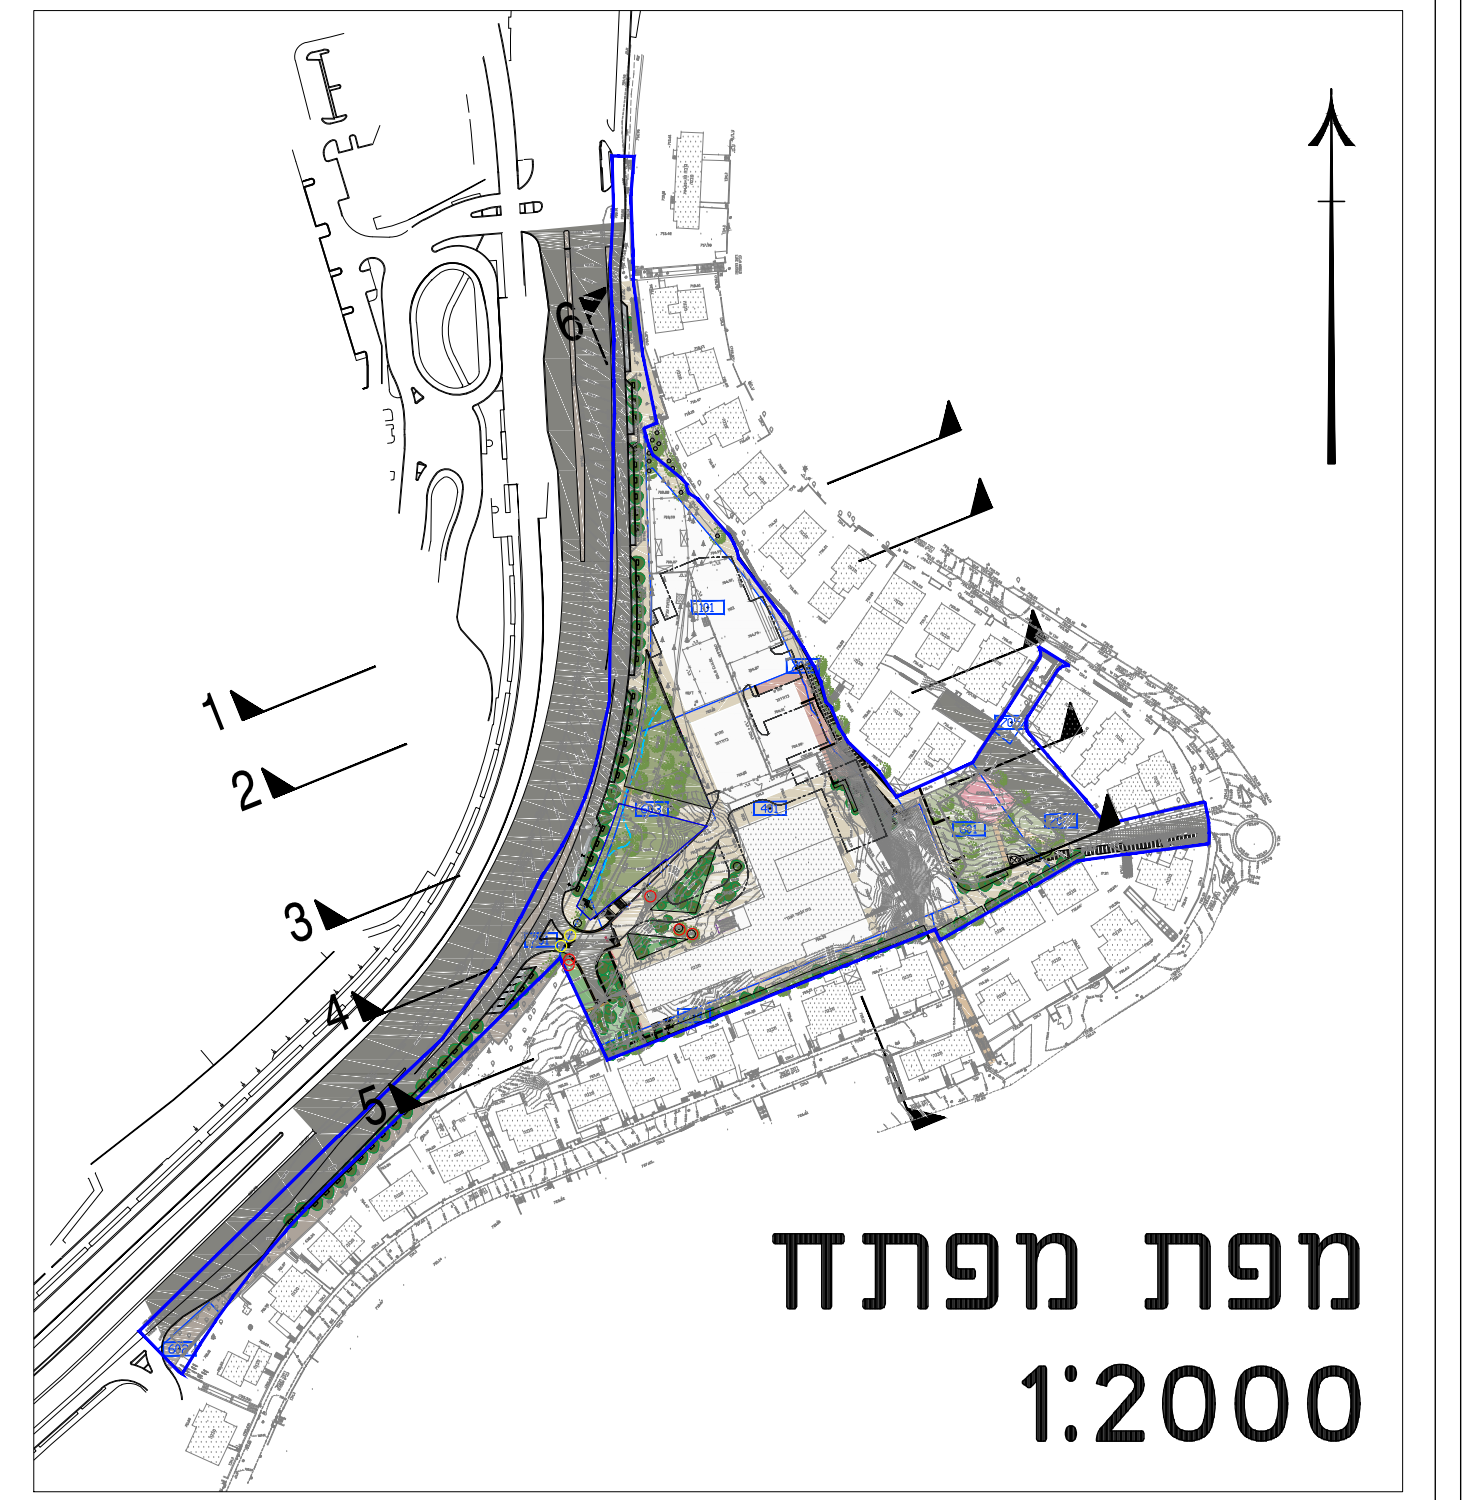

מפת מפתח
1:2000

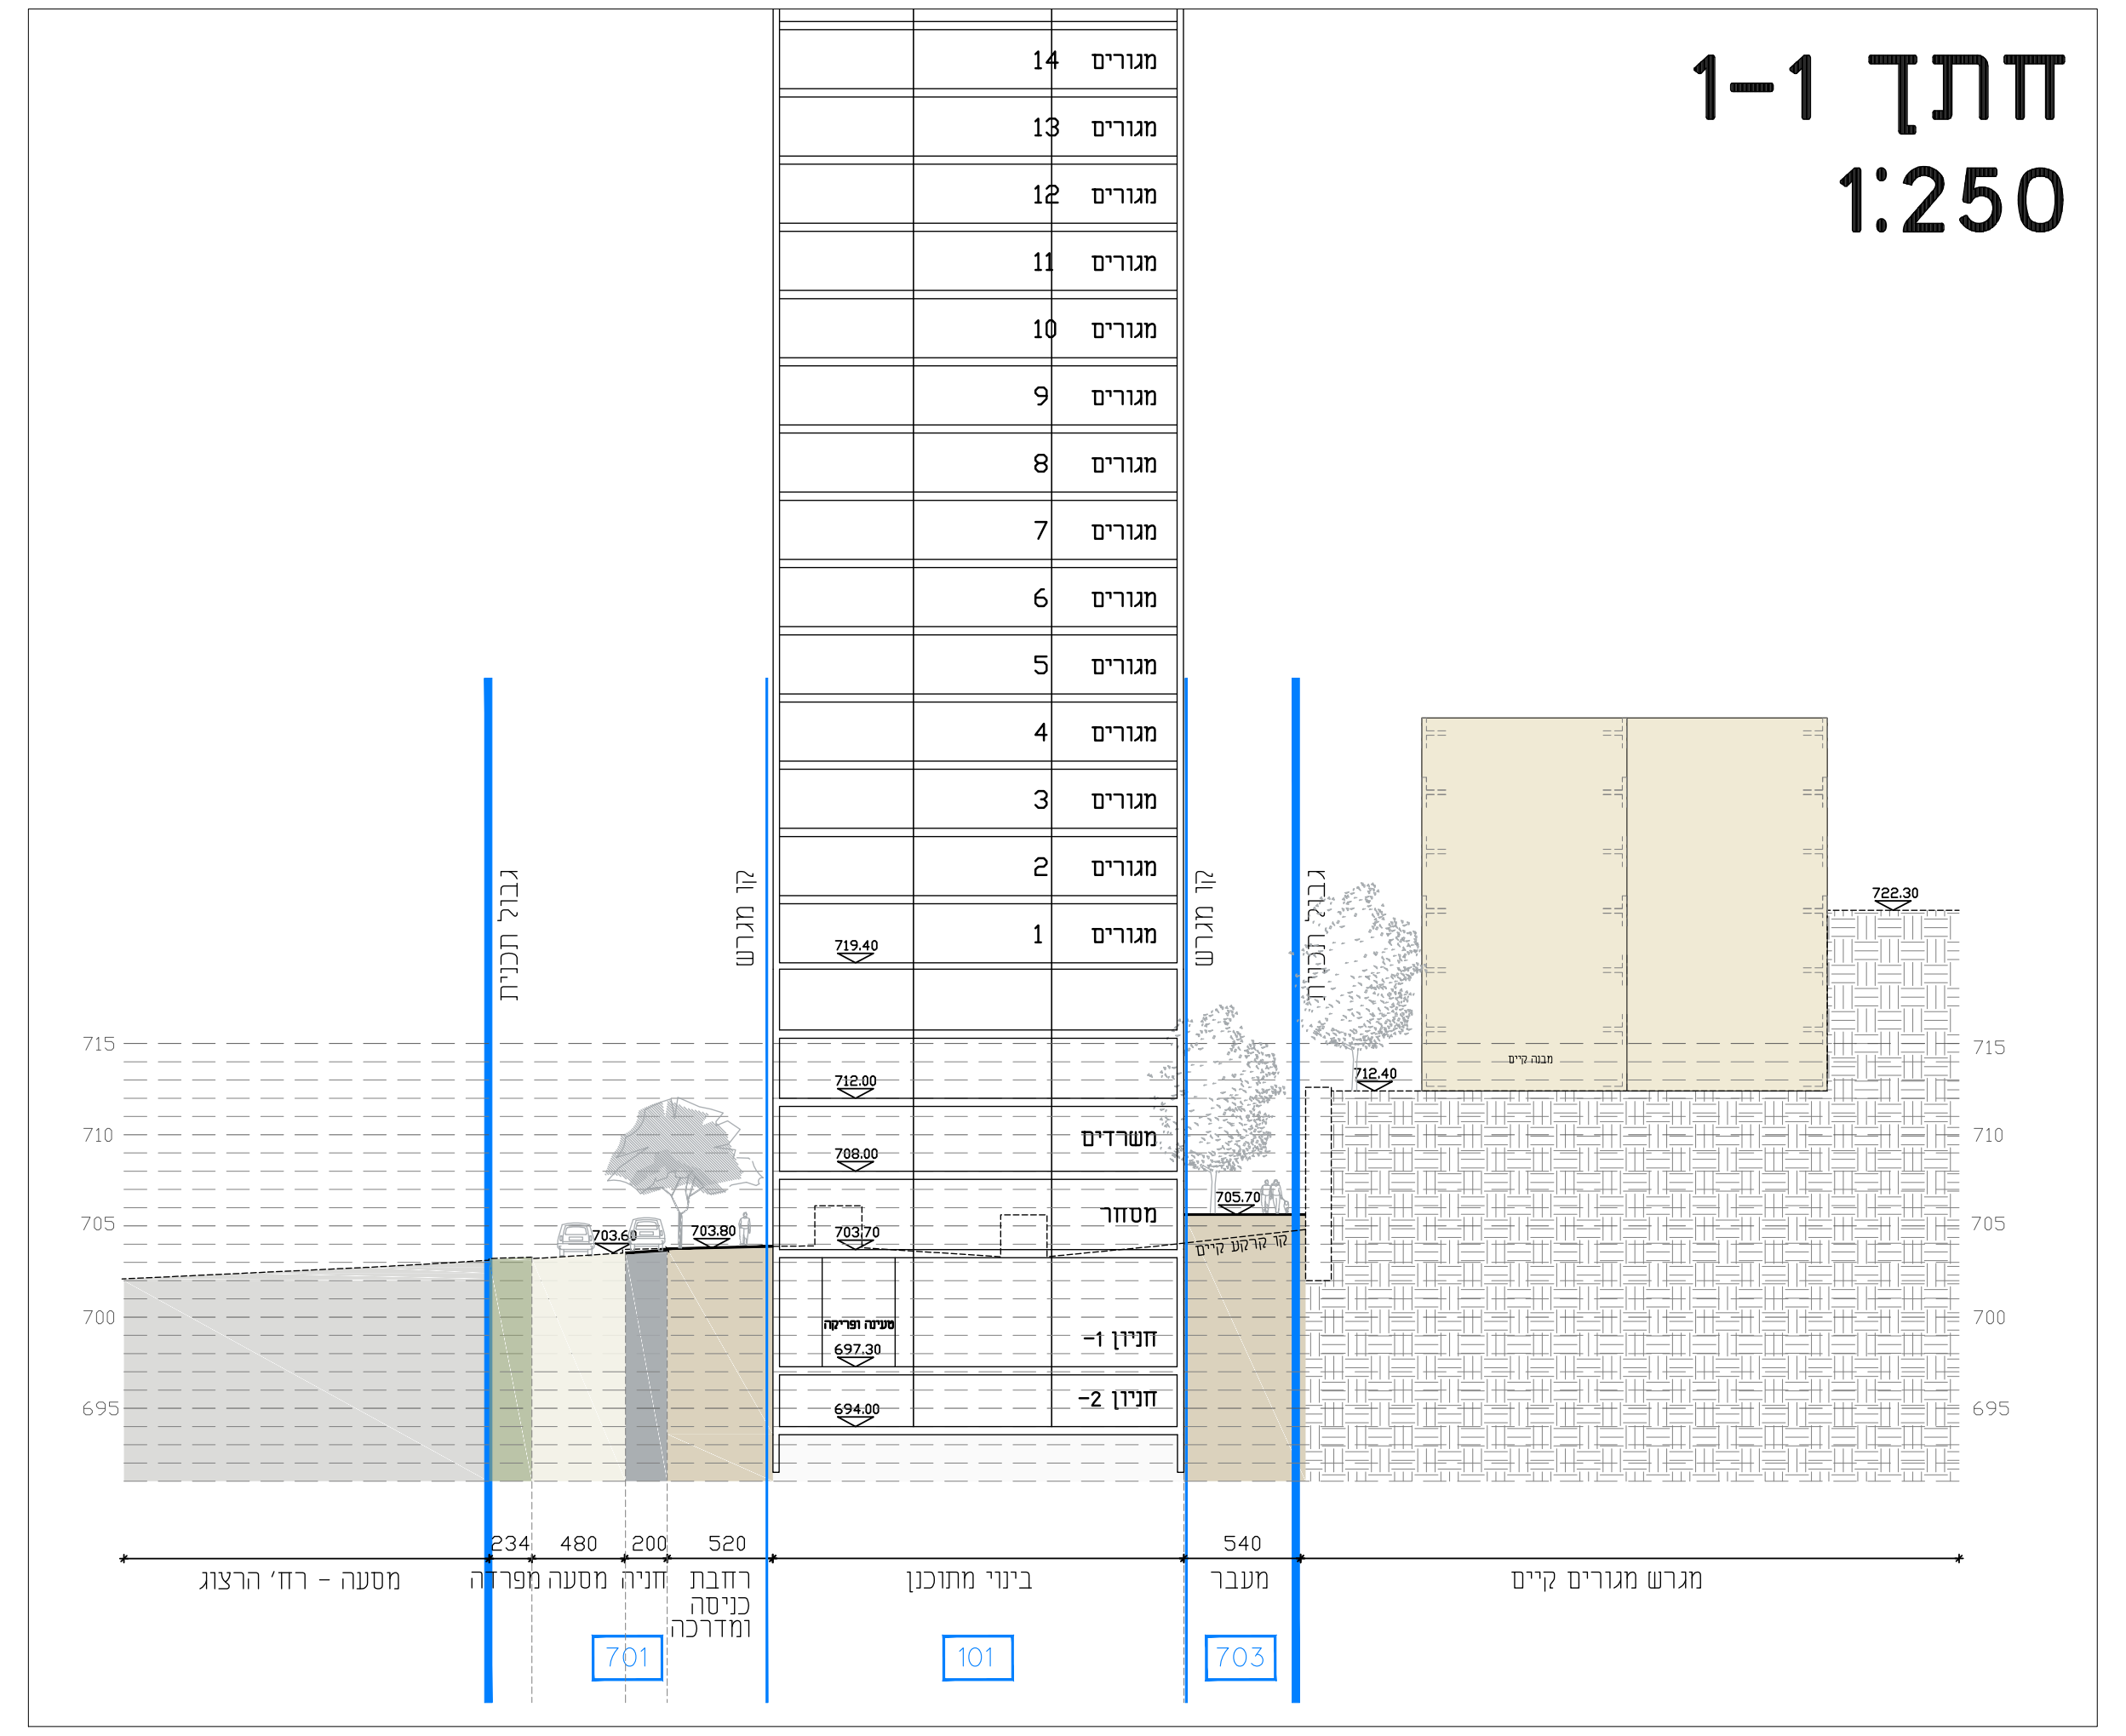

חתך 1-1
1:250

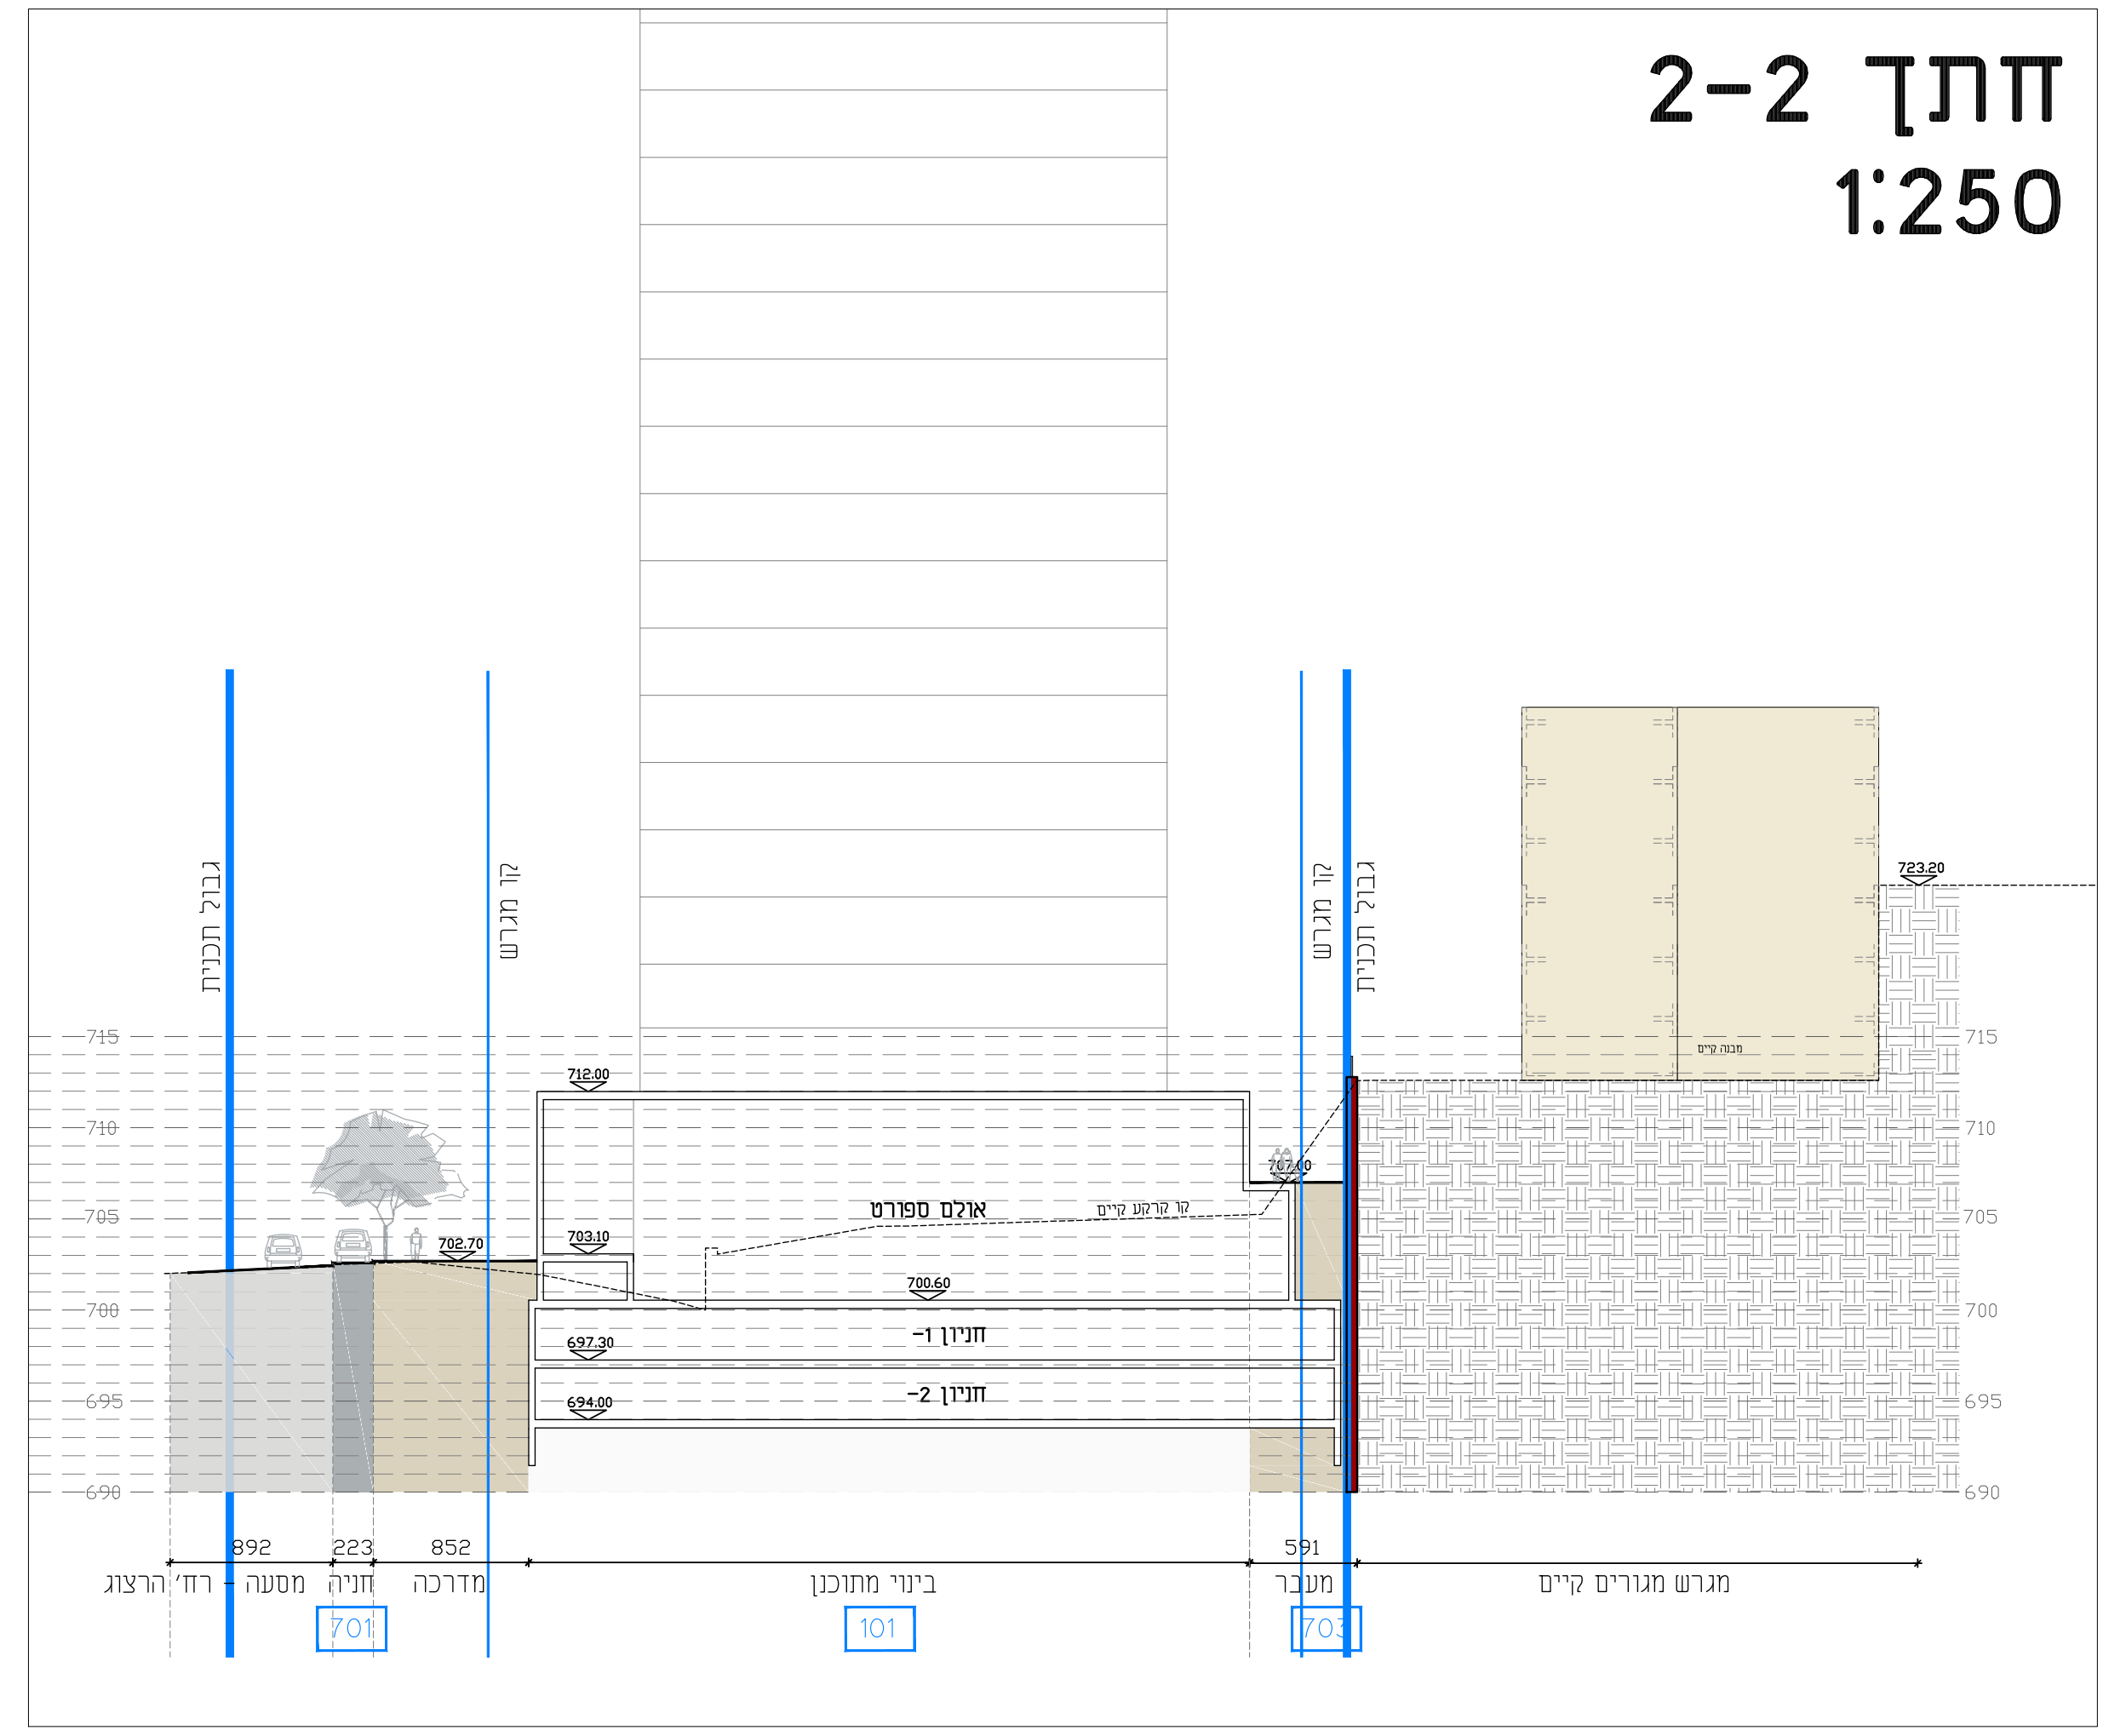

חתך 2-2
1:250

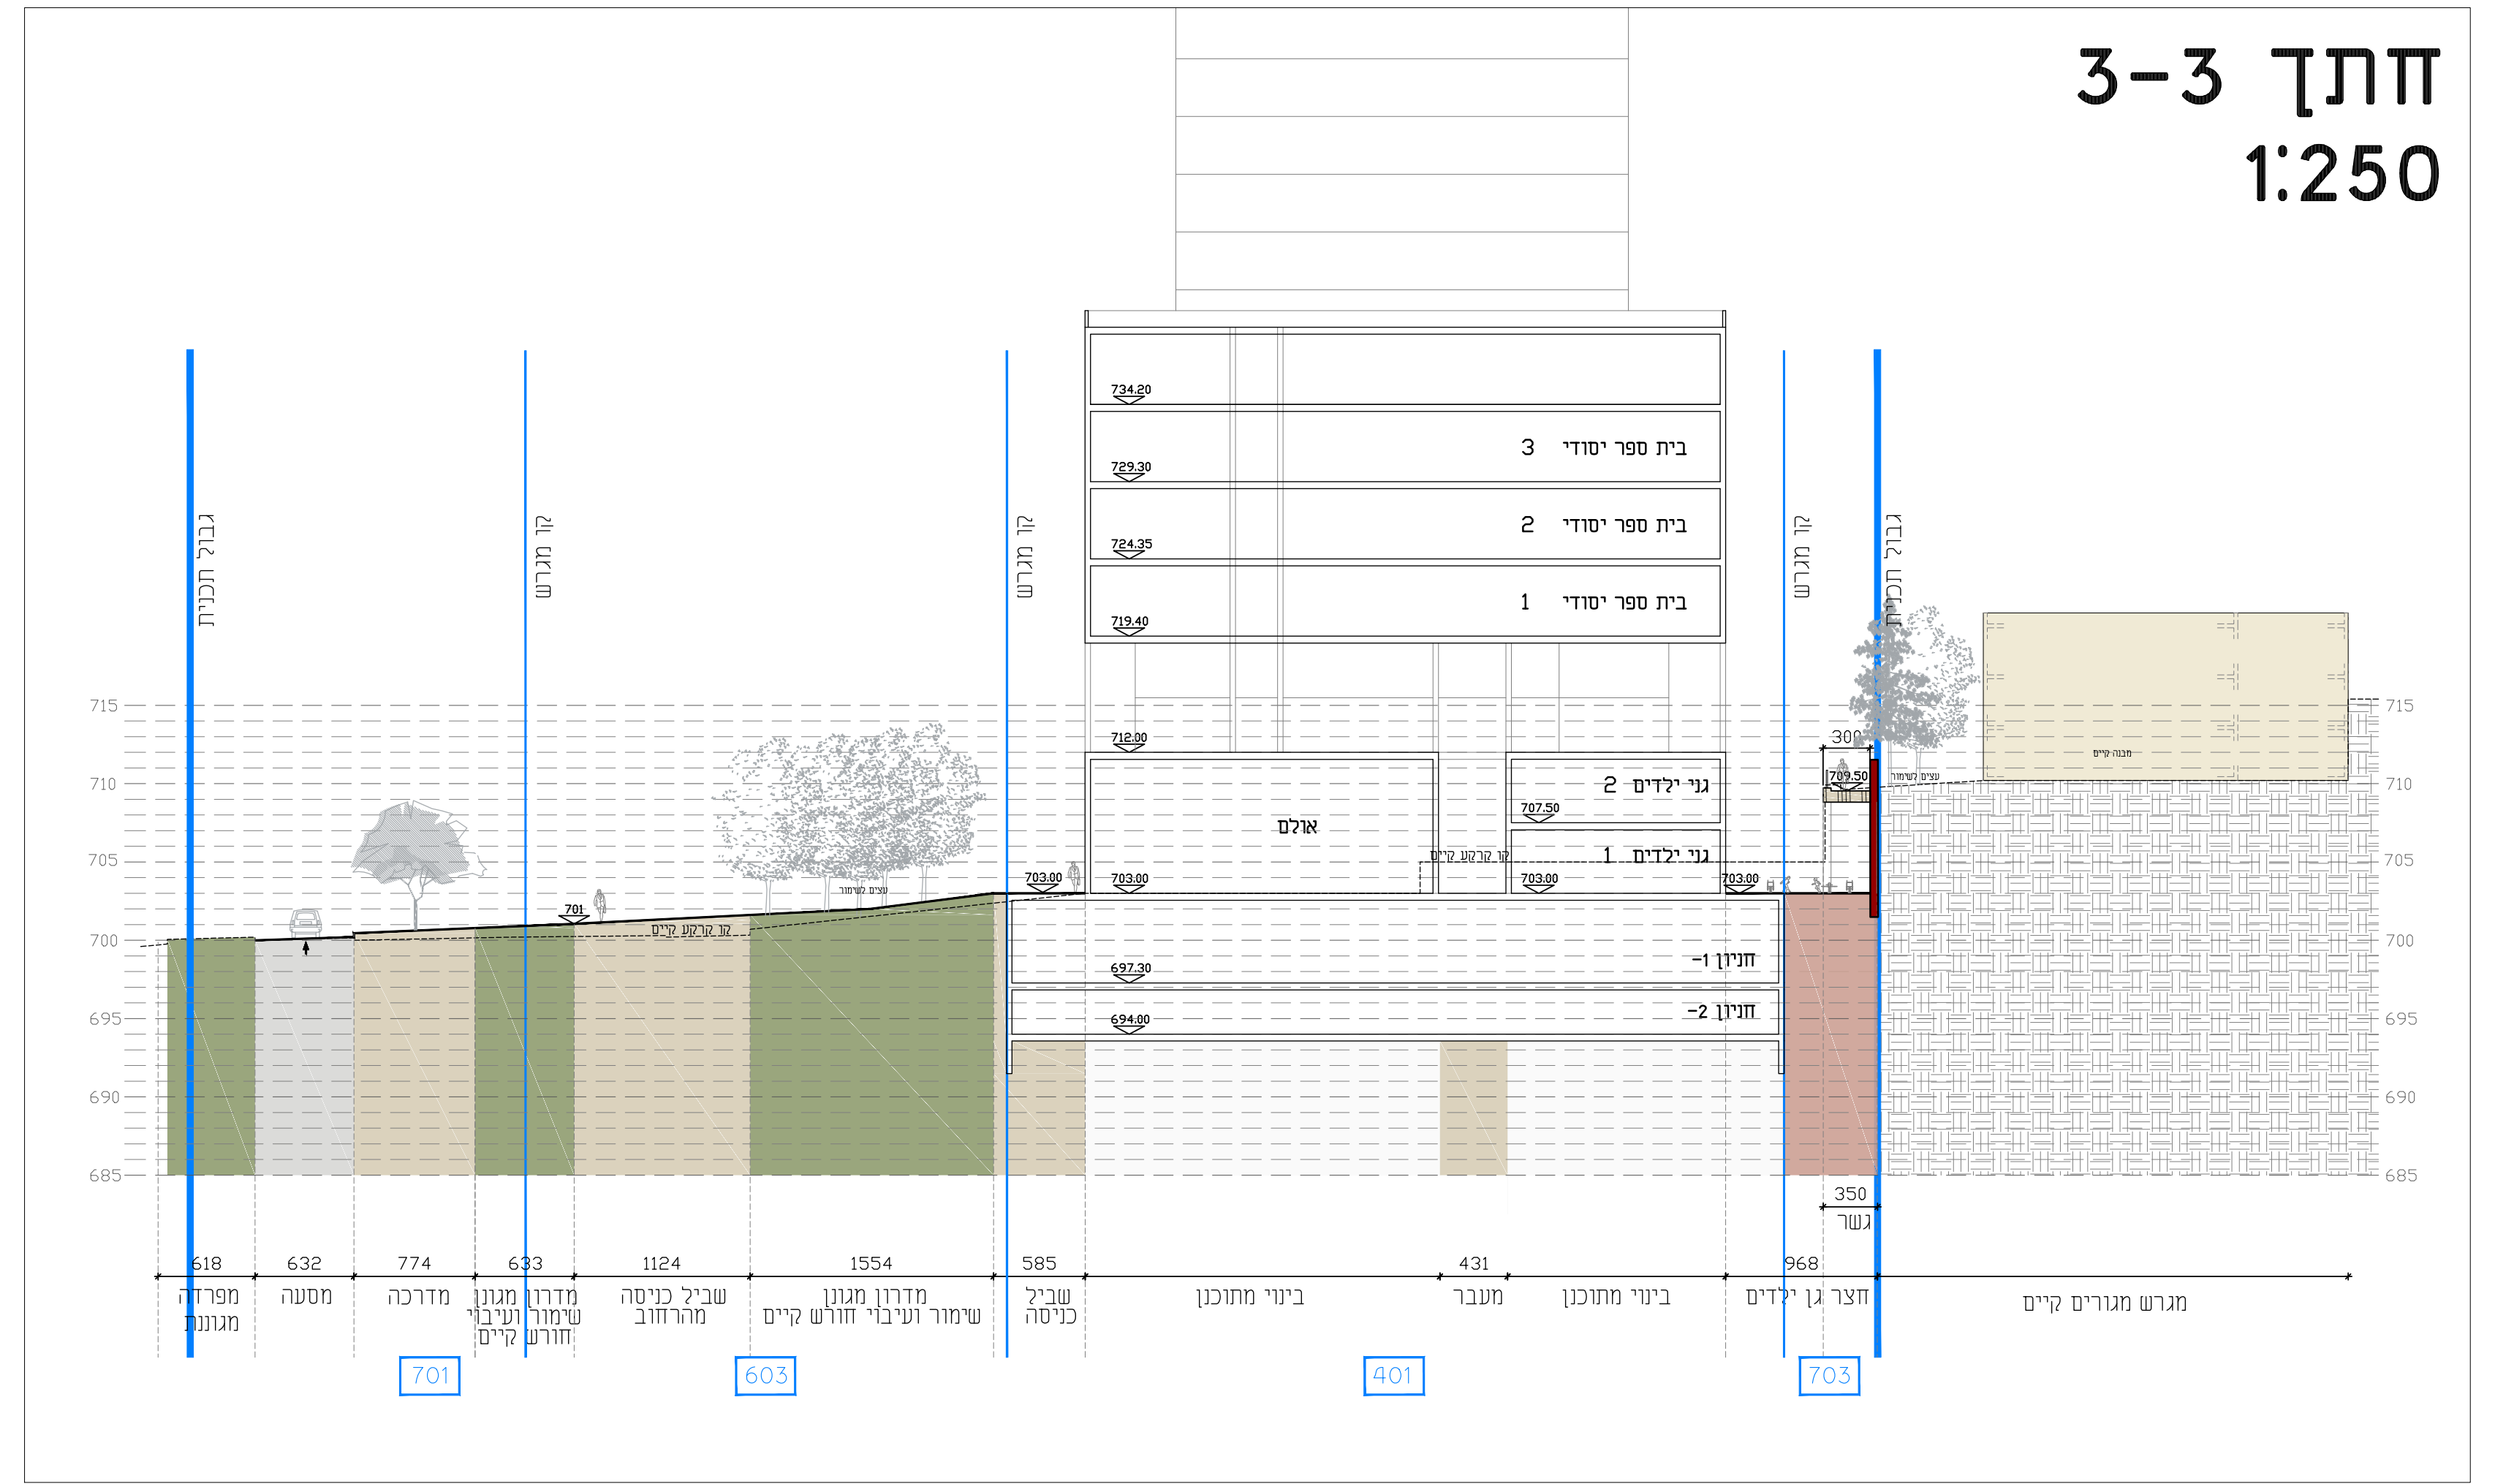

חתך 3-3
1:250

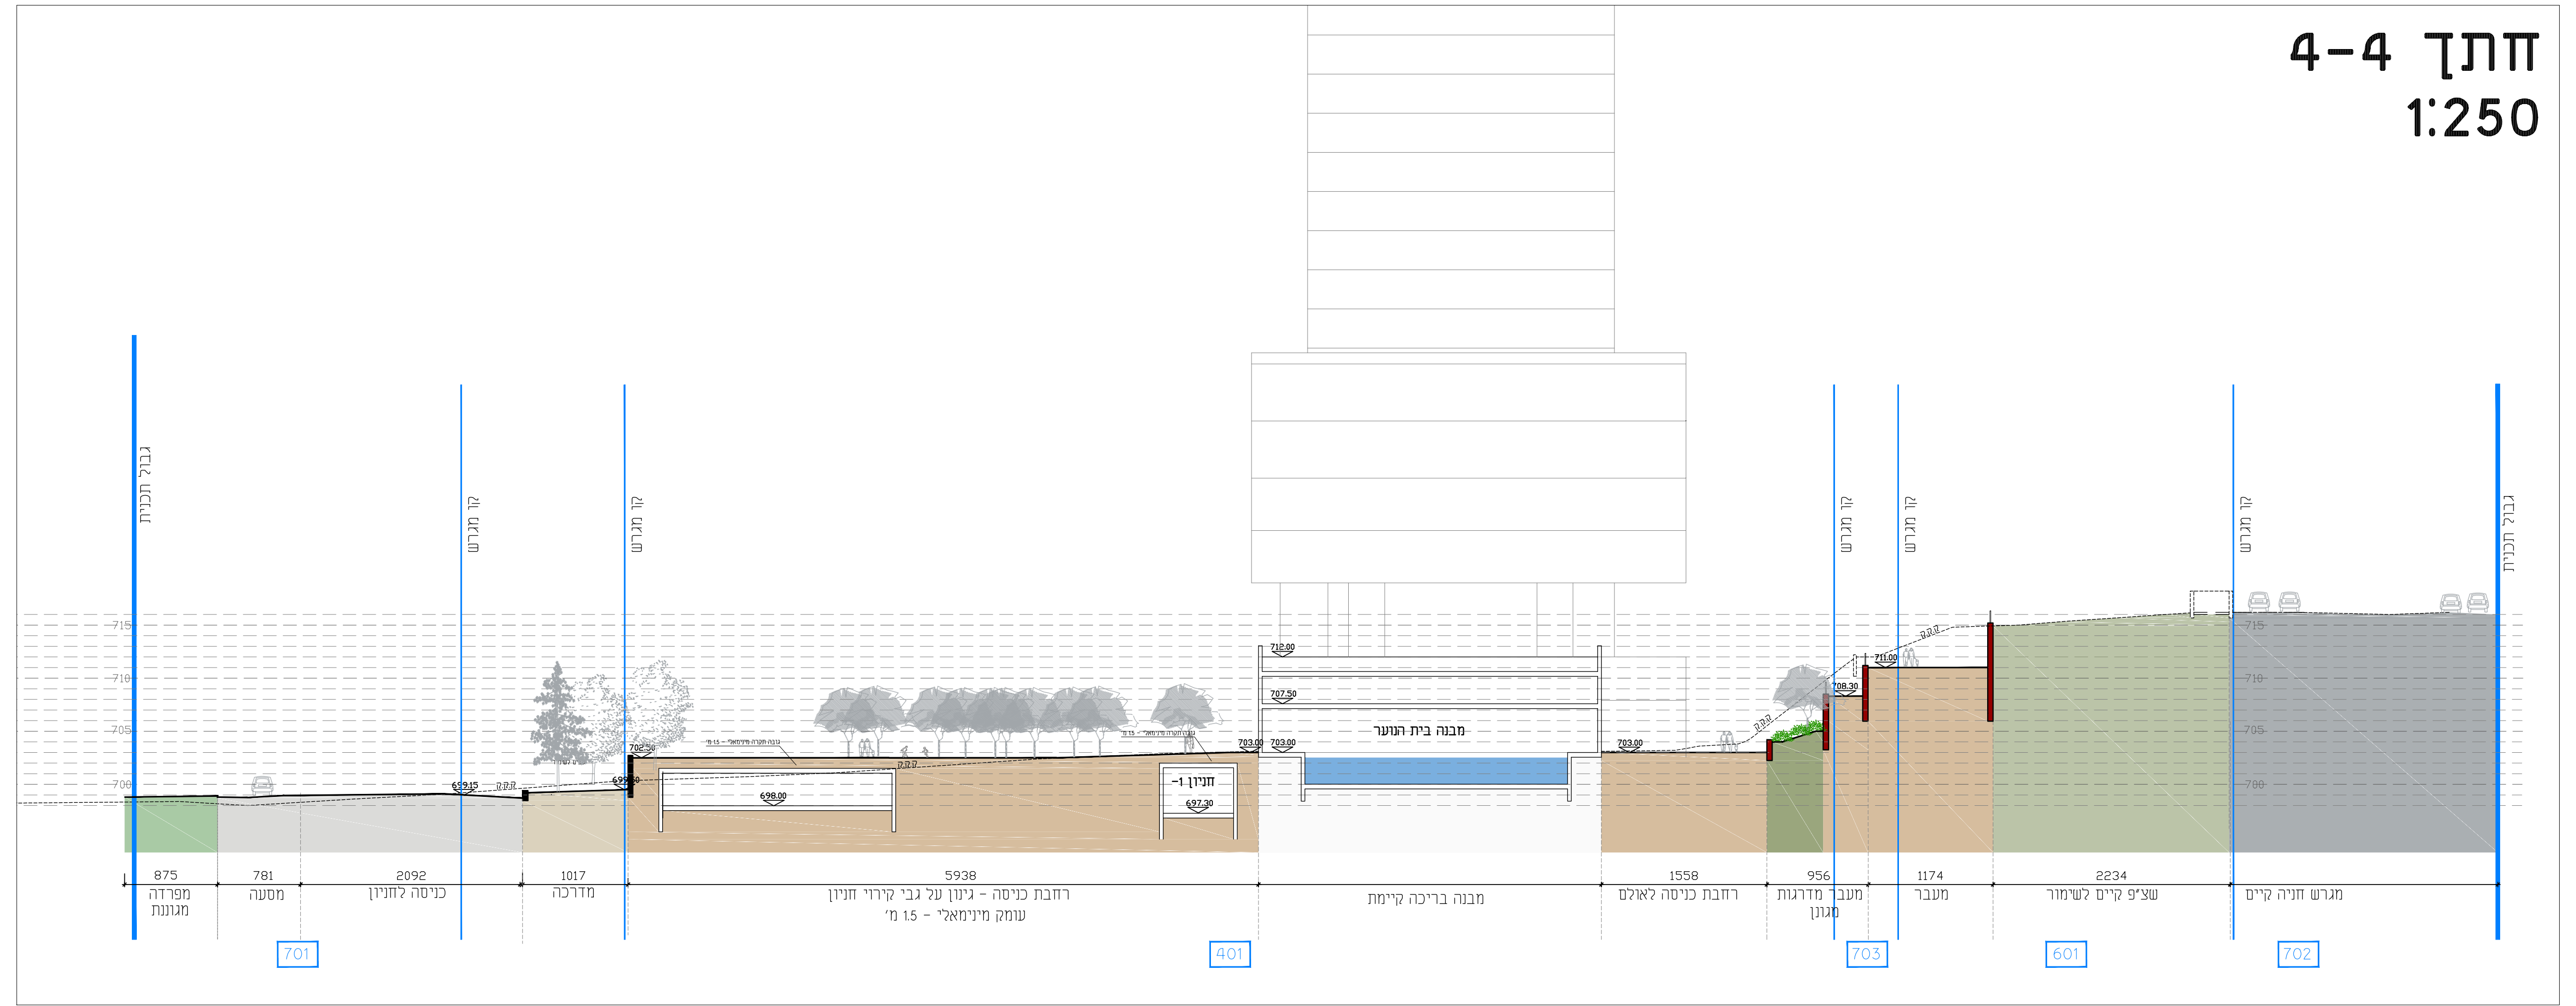

חתך 4-4
1:250

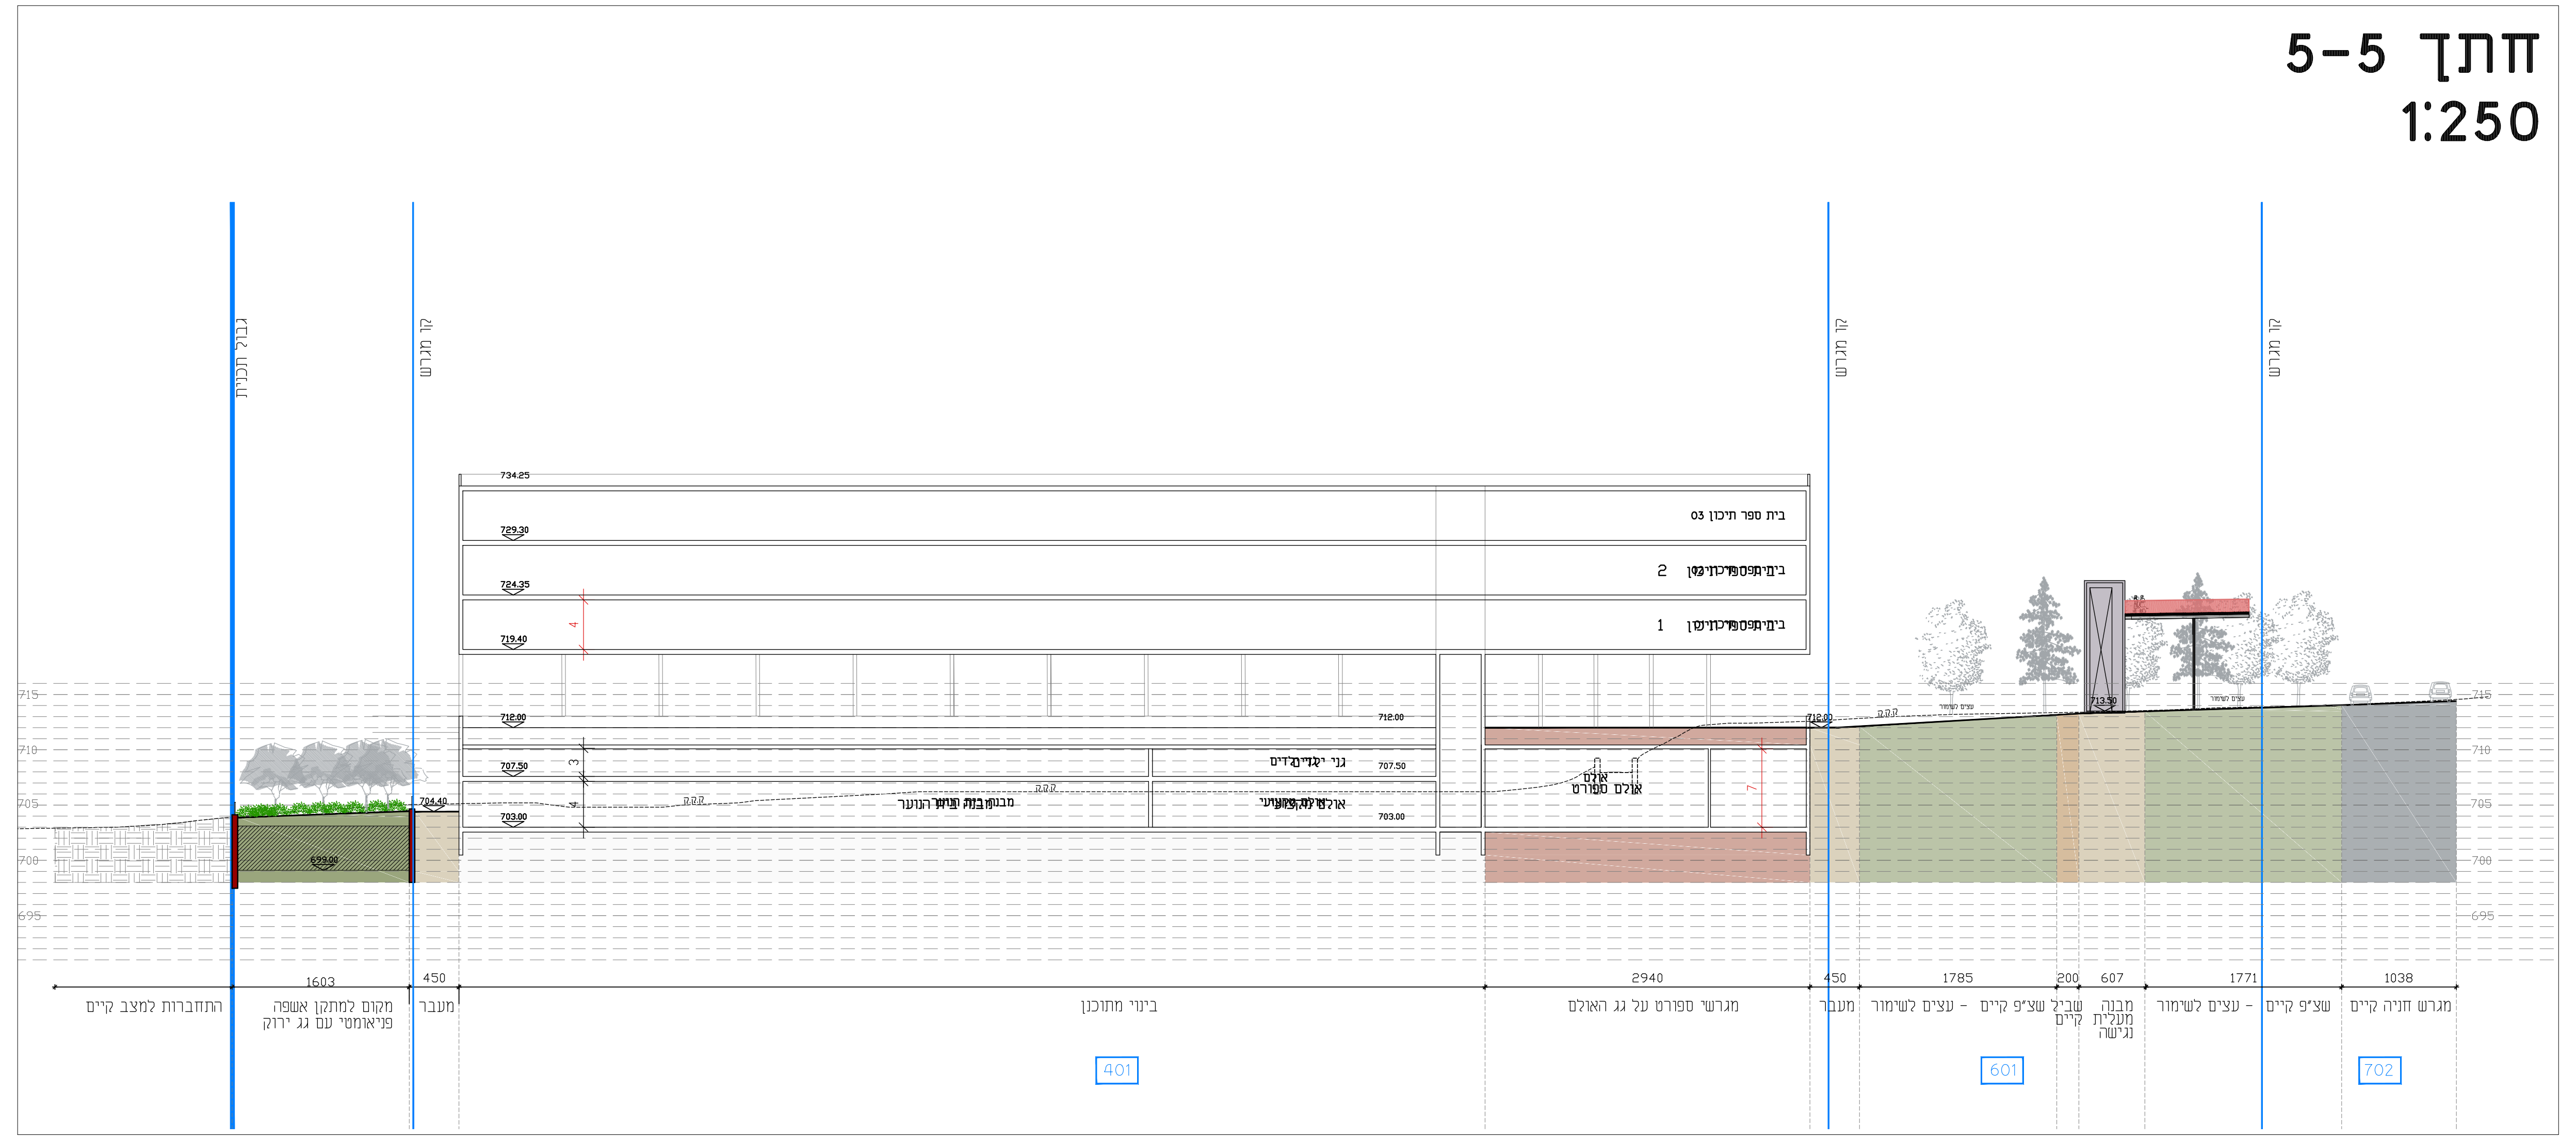

חתך 5-5
1:250

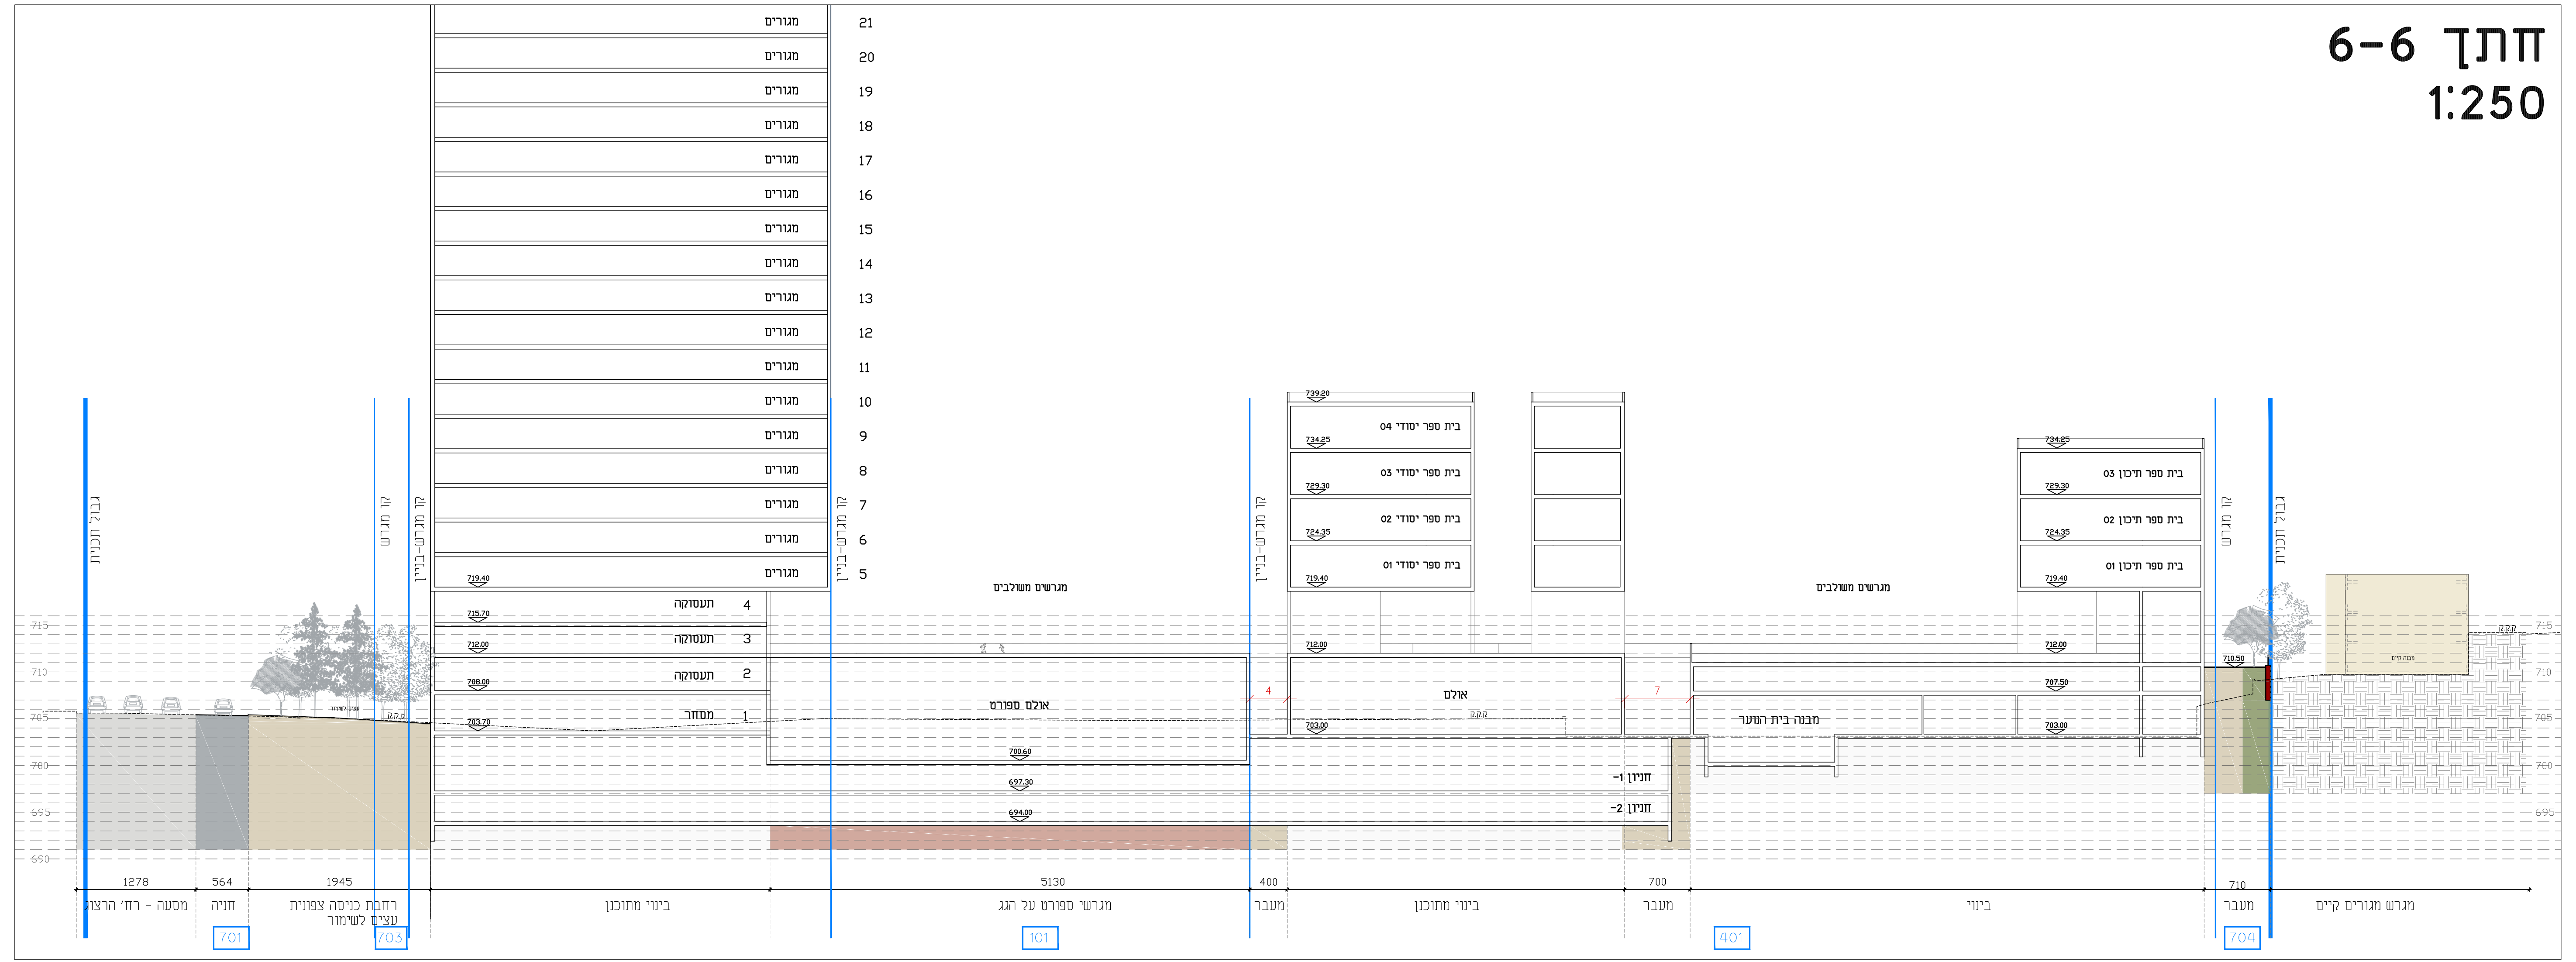

חתך 6-6
1:250

חוק התכנון והבנייה, התשכ"ה – 1965
תוכנית מפורטת

101-1158146

בית הנוער העברי

נספח נוף גליון **2** מתוך **2**

מחוז	ירושלים
מרחב תכנון מקומי	עיריית ירושלים
רשות מקומית	ירושלים
ישוב	ירושלים
תאריך	19/09/24

שם התרשים	קנ"מ
חתכים	1:250

שמות וחתימות:

עורך הנספח	שם:אדר' אור כהנא תאגיד: רחל וינר אדריכלות ונוף בע"מ	חתימה:

מקרא

▬	גבול תוכנית
4	תא שטח
☐	בינוי
▬▮▮▬	גבולות חניון תת"ק
0.0=703 ▼	כניסה למבנה
▨	מדרכה קיימת
▨	מסעה קיימת
▨	מסעה מרוצפת
▨	חניה מוצעת
699.50	קו גובה חדש
◐ 304.20	מפלס פיתוח
▬	קיר פיתוח
▦	נקז מי נגר
～	ערוץ ניקוז מי נגר
▨	ריצוף ריפ ראפ בתוואי שביל
▨	שביל קיים
▨	שביל מוצע
▥	גשר
▨	חצר מבנ"צ
▨	משטח פעילות קיים
▨	חורשה קיימת לשימור
▨	שצ"פ קיים לשימור
▨	גינון מוצע
▨	גג ירוק

רחל וינר | אדריכלות ונוף בע"מ
Rachelle Wiener | Landscape & Architecture Ltd
Or Kahana אור כהנא | Moshe Rucham משה רוחם

רח' כספי 9 ירושלים, מיקוד 9355409 , טל: 02-5670080, פקס: 02-5670090, email: office@wiel.co.il
9 caspi st. Jerusalem, 9355409, tel: 02-5670080, fax: 02- 56700900, email: office@wiel.co.il

ספטמבר '24