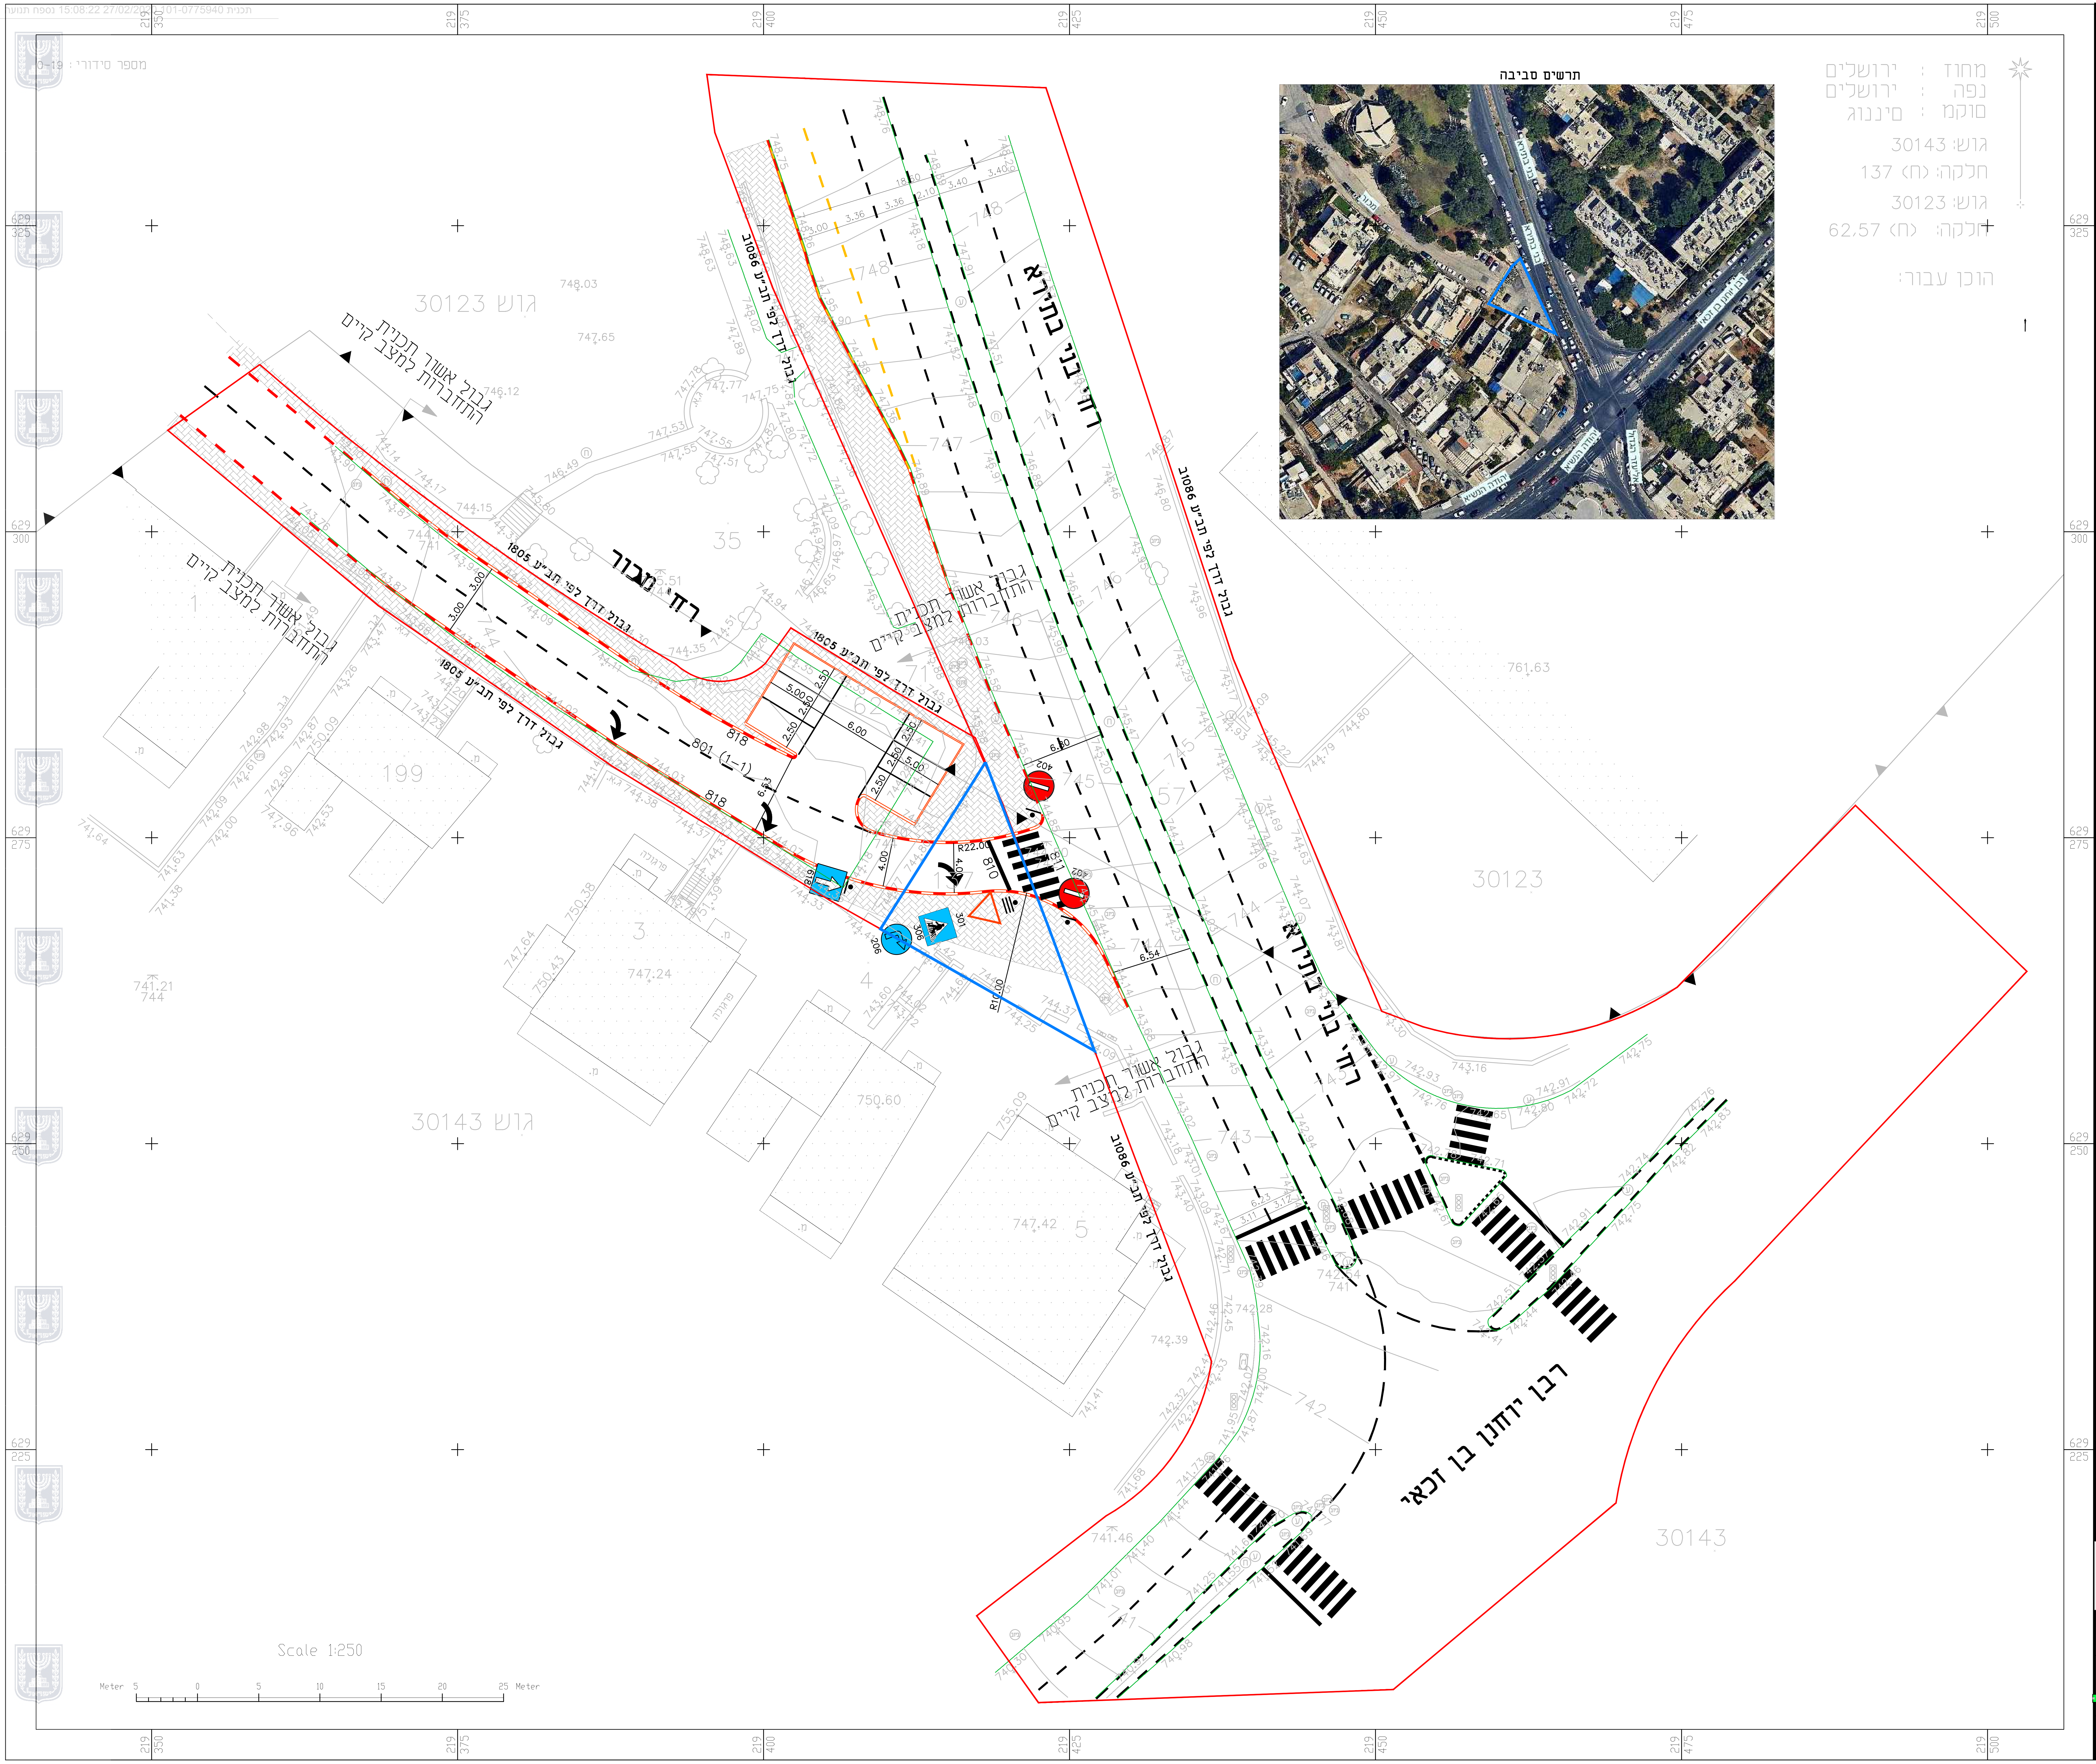

חוק התכנון והבנייה, התשכ"ה - 1965
תכנית מתאר מקומית

מס' 101-0775940

שם התכנית :
הארכת דרך, רחוב מכוור
בשכ' גוננים , ירושלים

נספח תנועה וחנייה

שם הנספח	קנ"מ
נספח מס' 1	1:200

תאריך 27\02\2020

מקרא

אבן שפה קיימת	- - - -
אבן שפה חדשה	═
גבול התכנית	━
גבול דרך מאושרת	━
גבול גוש	▼───▲
מס' גוש	30143
גבול חלקה קיימת	──
מס' חלקה קיימת	137

☑ לאישור ☐ למכרז ☐ לביצוע

המזמין: עיריית ירושליים

שם הפרוייקט: נספח תנועה
ירושלים - רח' מכוור

אינג' אשרף מסארוה-M.Sc
מהנדס תנועה מבוחה
מ"ר 107658

גליון מס'		תאריך:	קנה מידה:
2019/Jerusalem/Horakaniya/ASH-HW-000-Horakniya-101	תכנן: מהנדס אשרף מסארוה שרטוט:תקוא ראבוס אשר:	27/02/20	1:250

מסלול מהנדסים בע"מ
הנדסה אזרחית ומדידות
תנועה,כבישים ותשתיות

טייבה אזור תעשיה
מיקוד 40400 ת.ד. 3393
בית הכוכבים תחנת דלק גל
ashraf-m@zahav.net.il
טל: 09-7996525
פקס: 09-7996526
נייד: 052-4484874