מינהל התכנון
חוק התכנון והבניה, התשכ"ה - 1965
מחוז ירושלים
הוועדה המחוזית החליטה ביום :
12/06/2025
להפקיד את התכנית
19/08/2026

יו"ר הוועדה המחוזית תאריך

תכנית 101-1215656 14/06/2026 12:18:19 נספח חתכים נספח חתכים

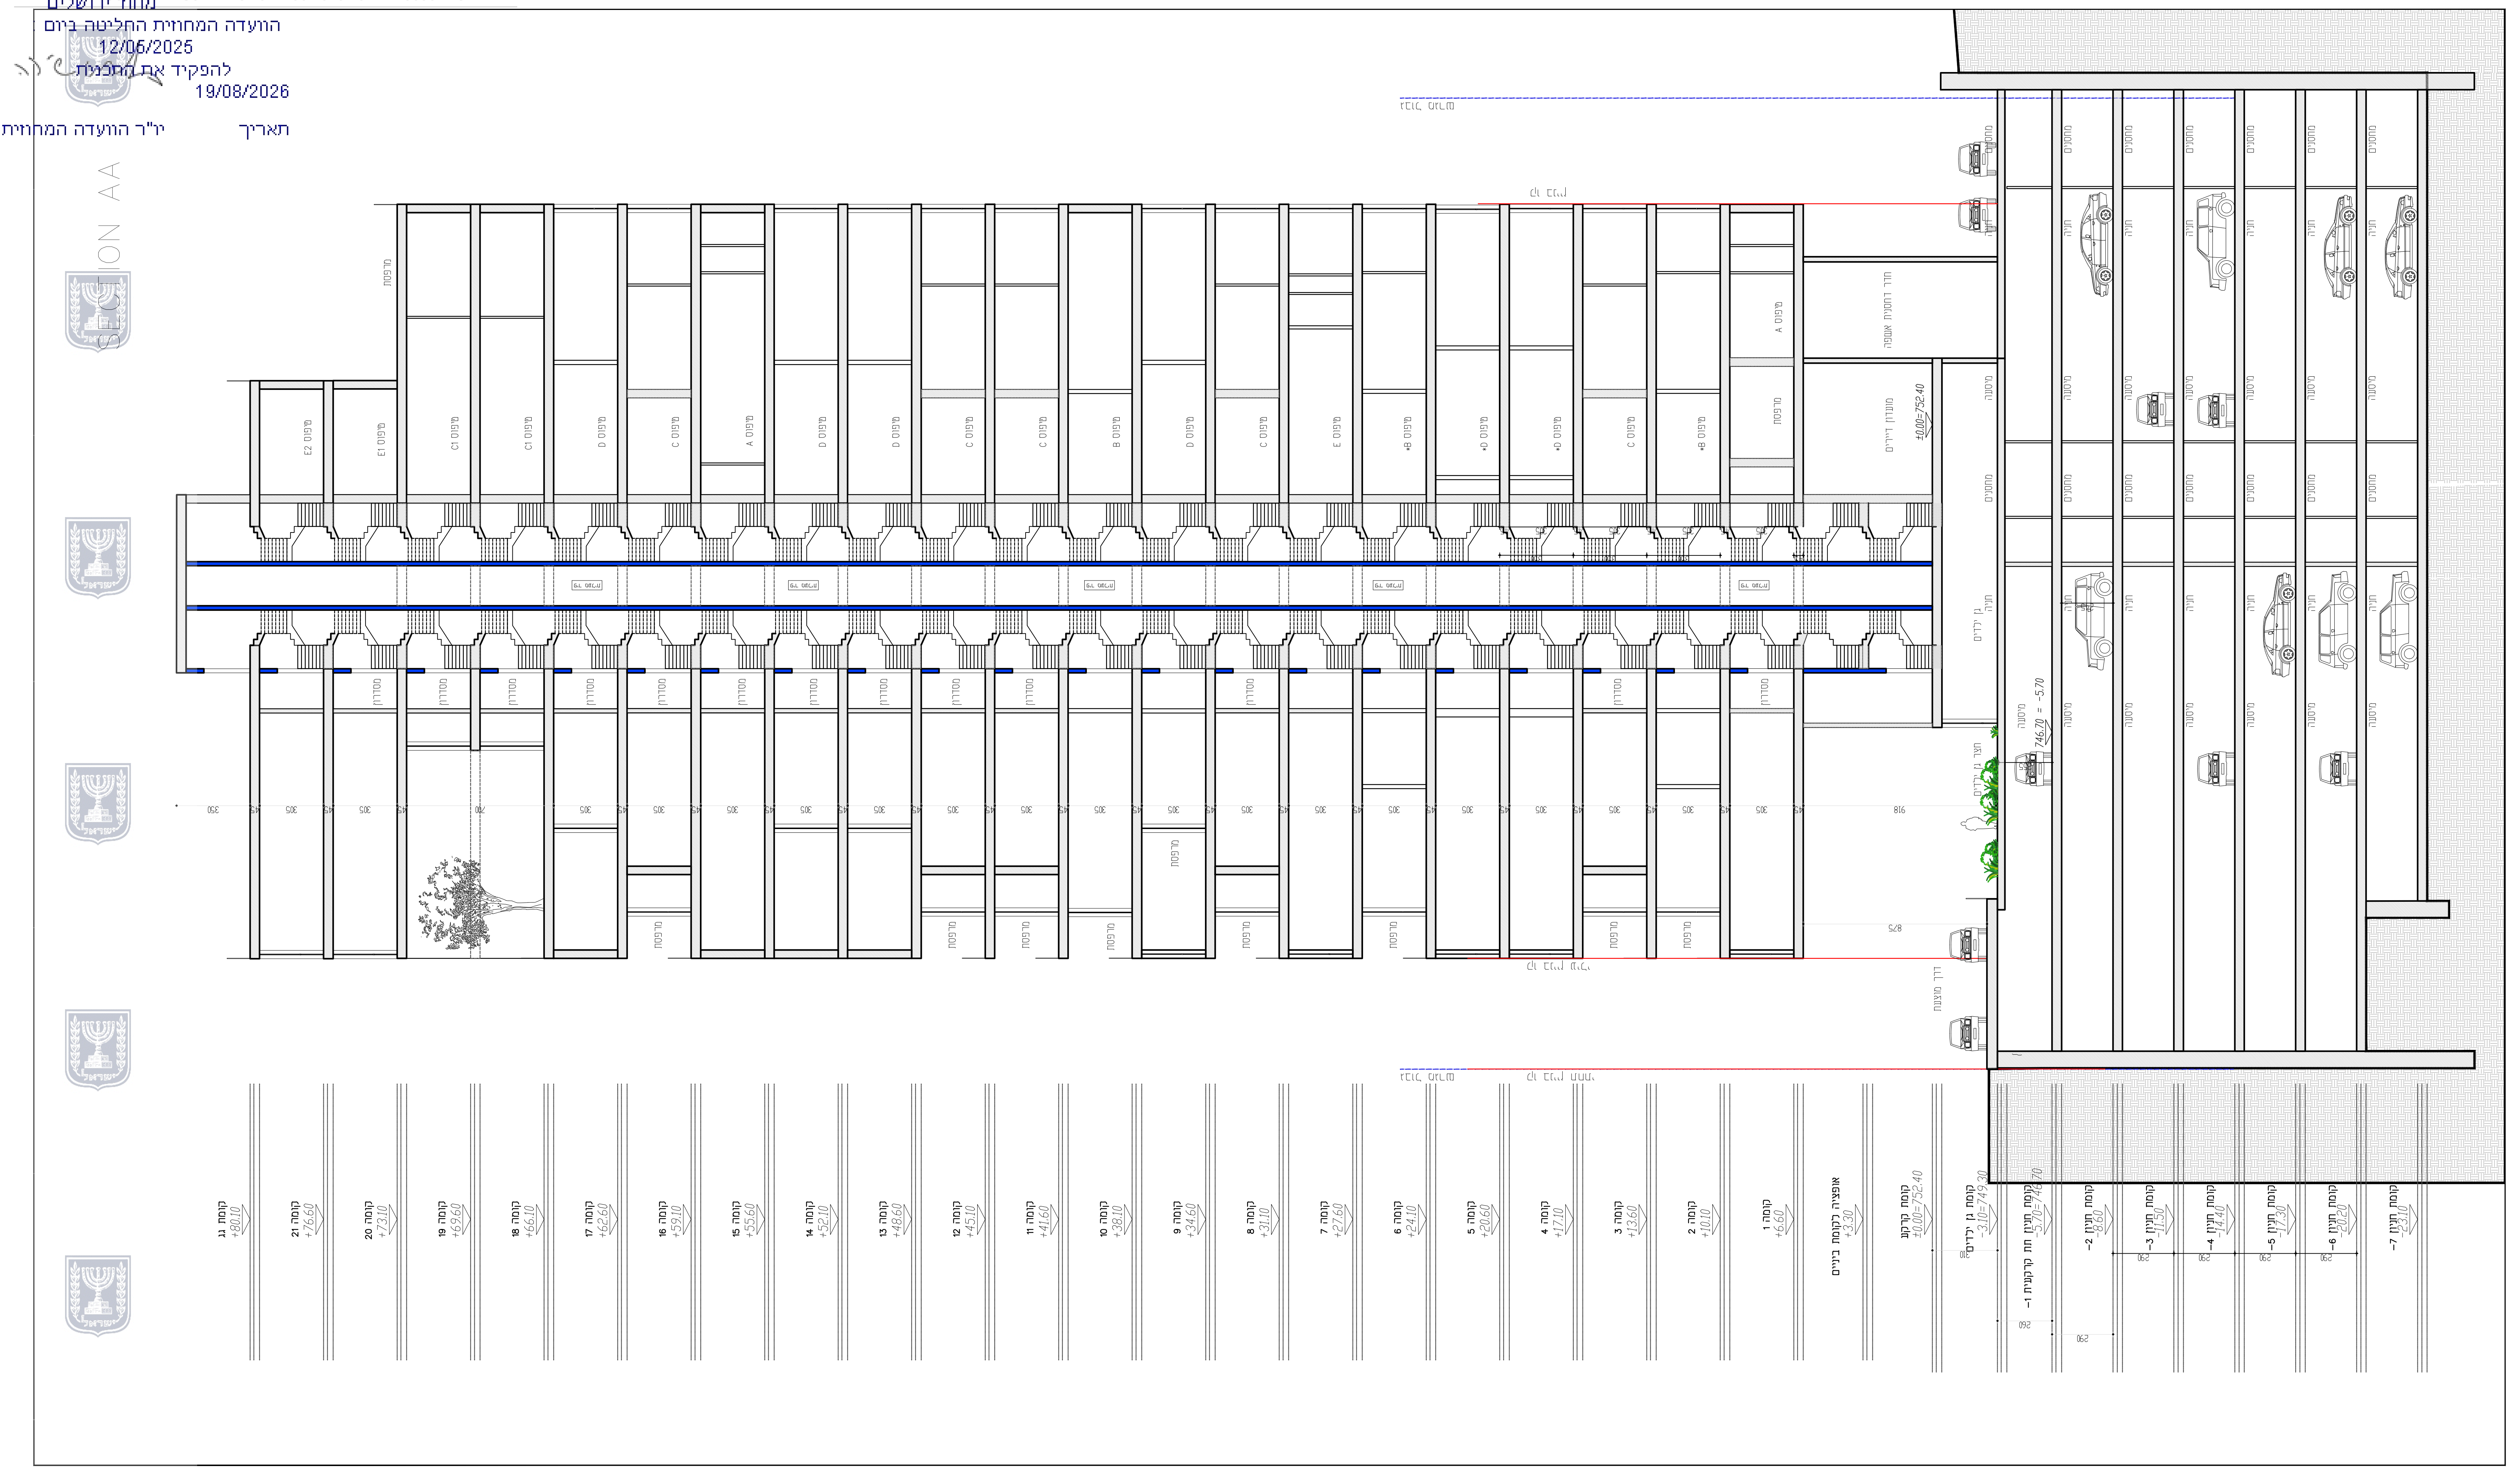
SECTION AA
1:200 ק.נ.מ.

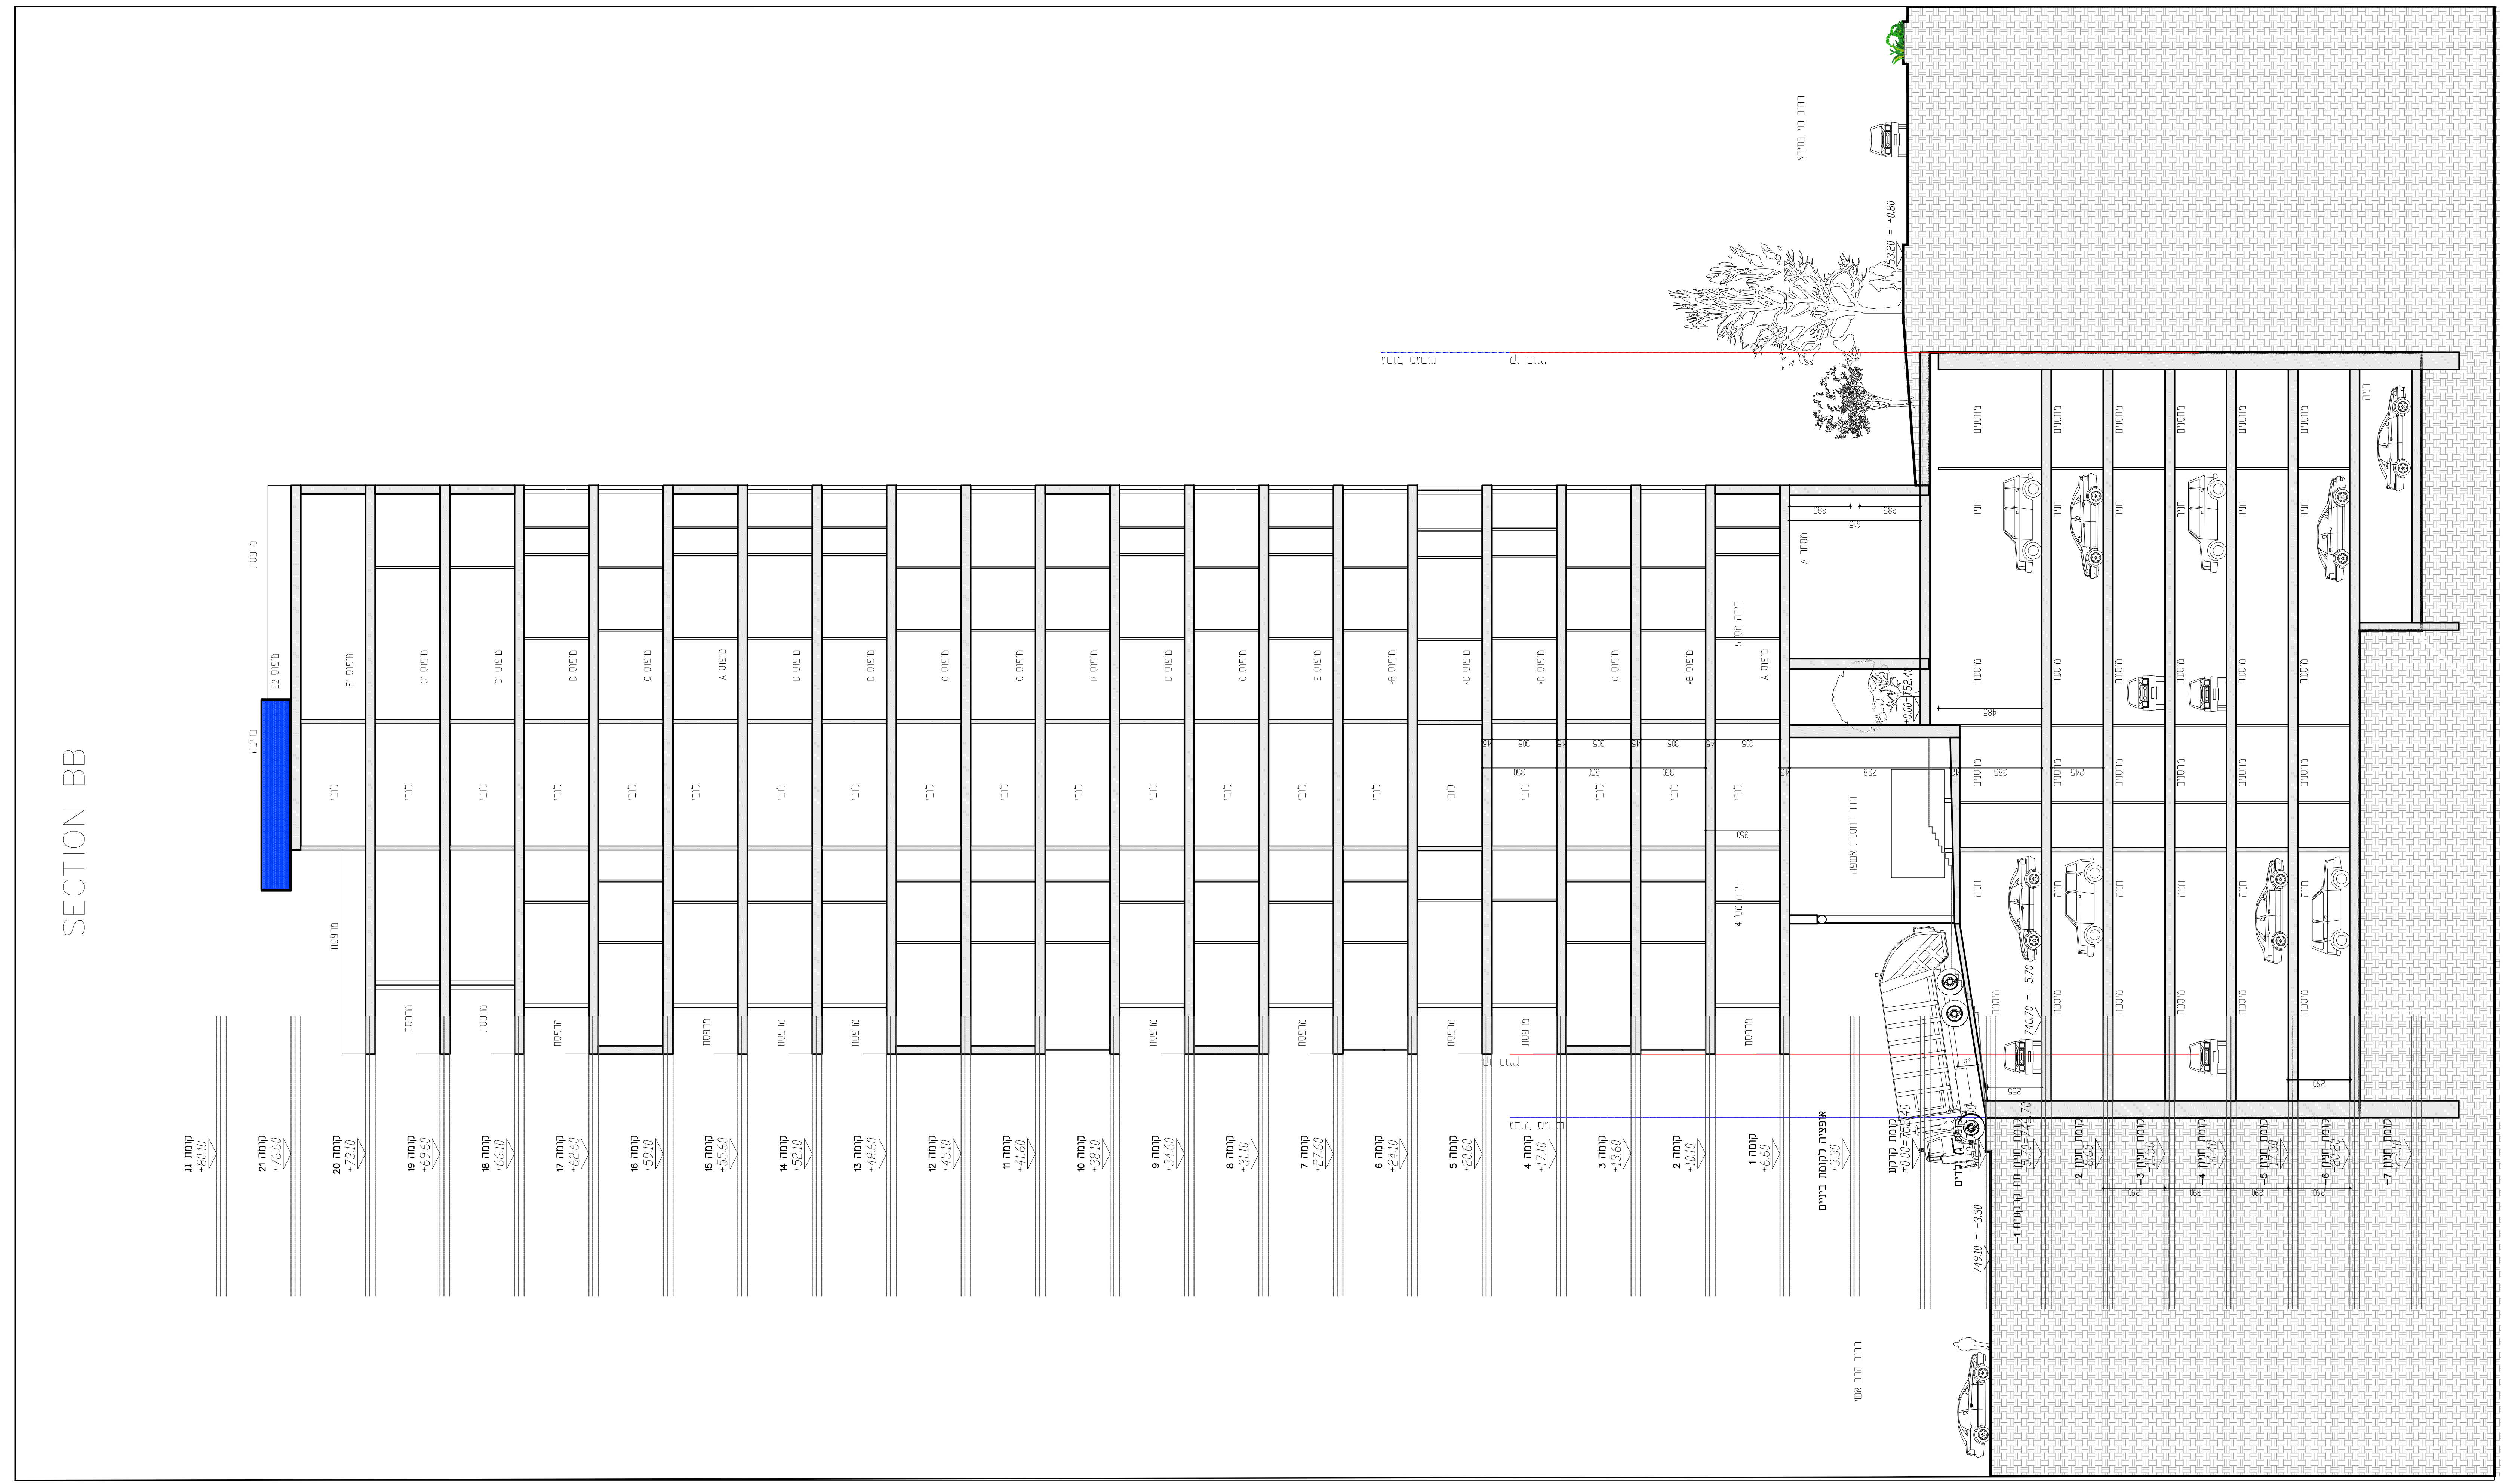
SECTION BB
1:200 ק.נ.מ.

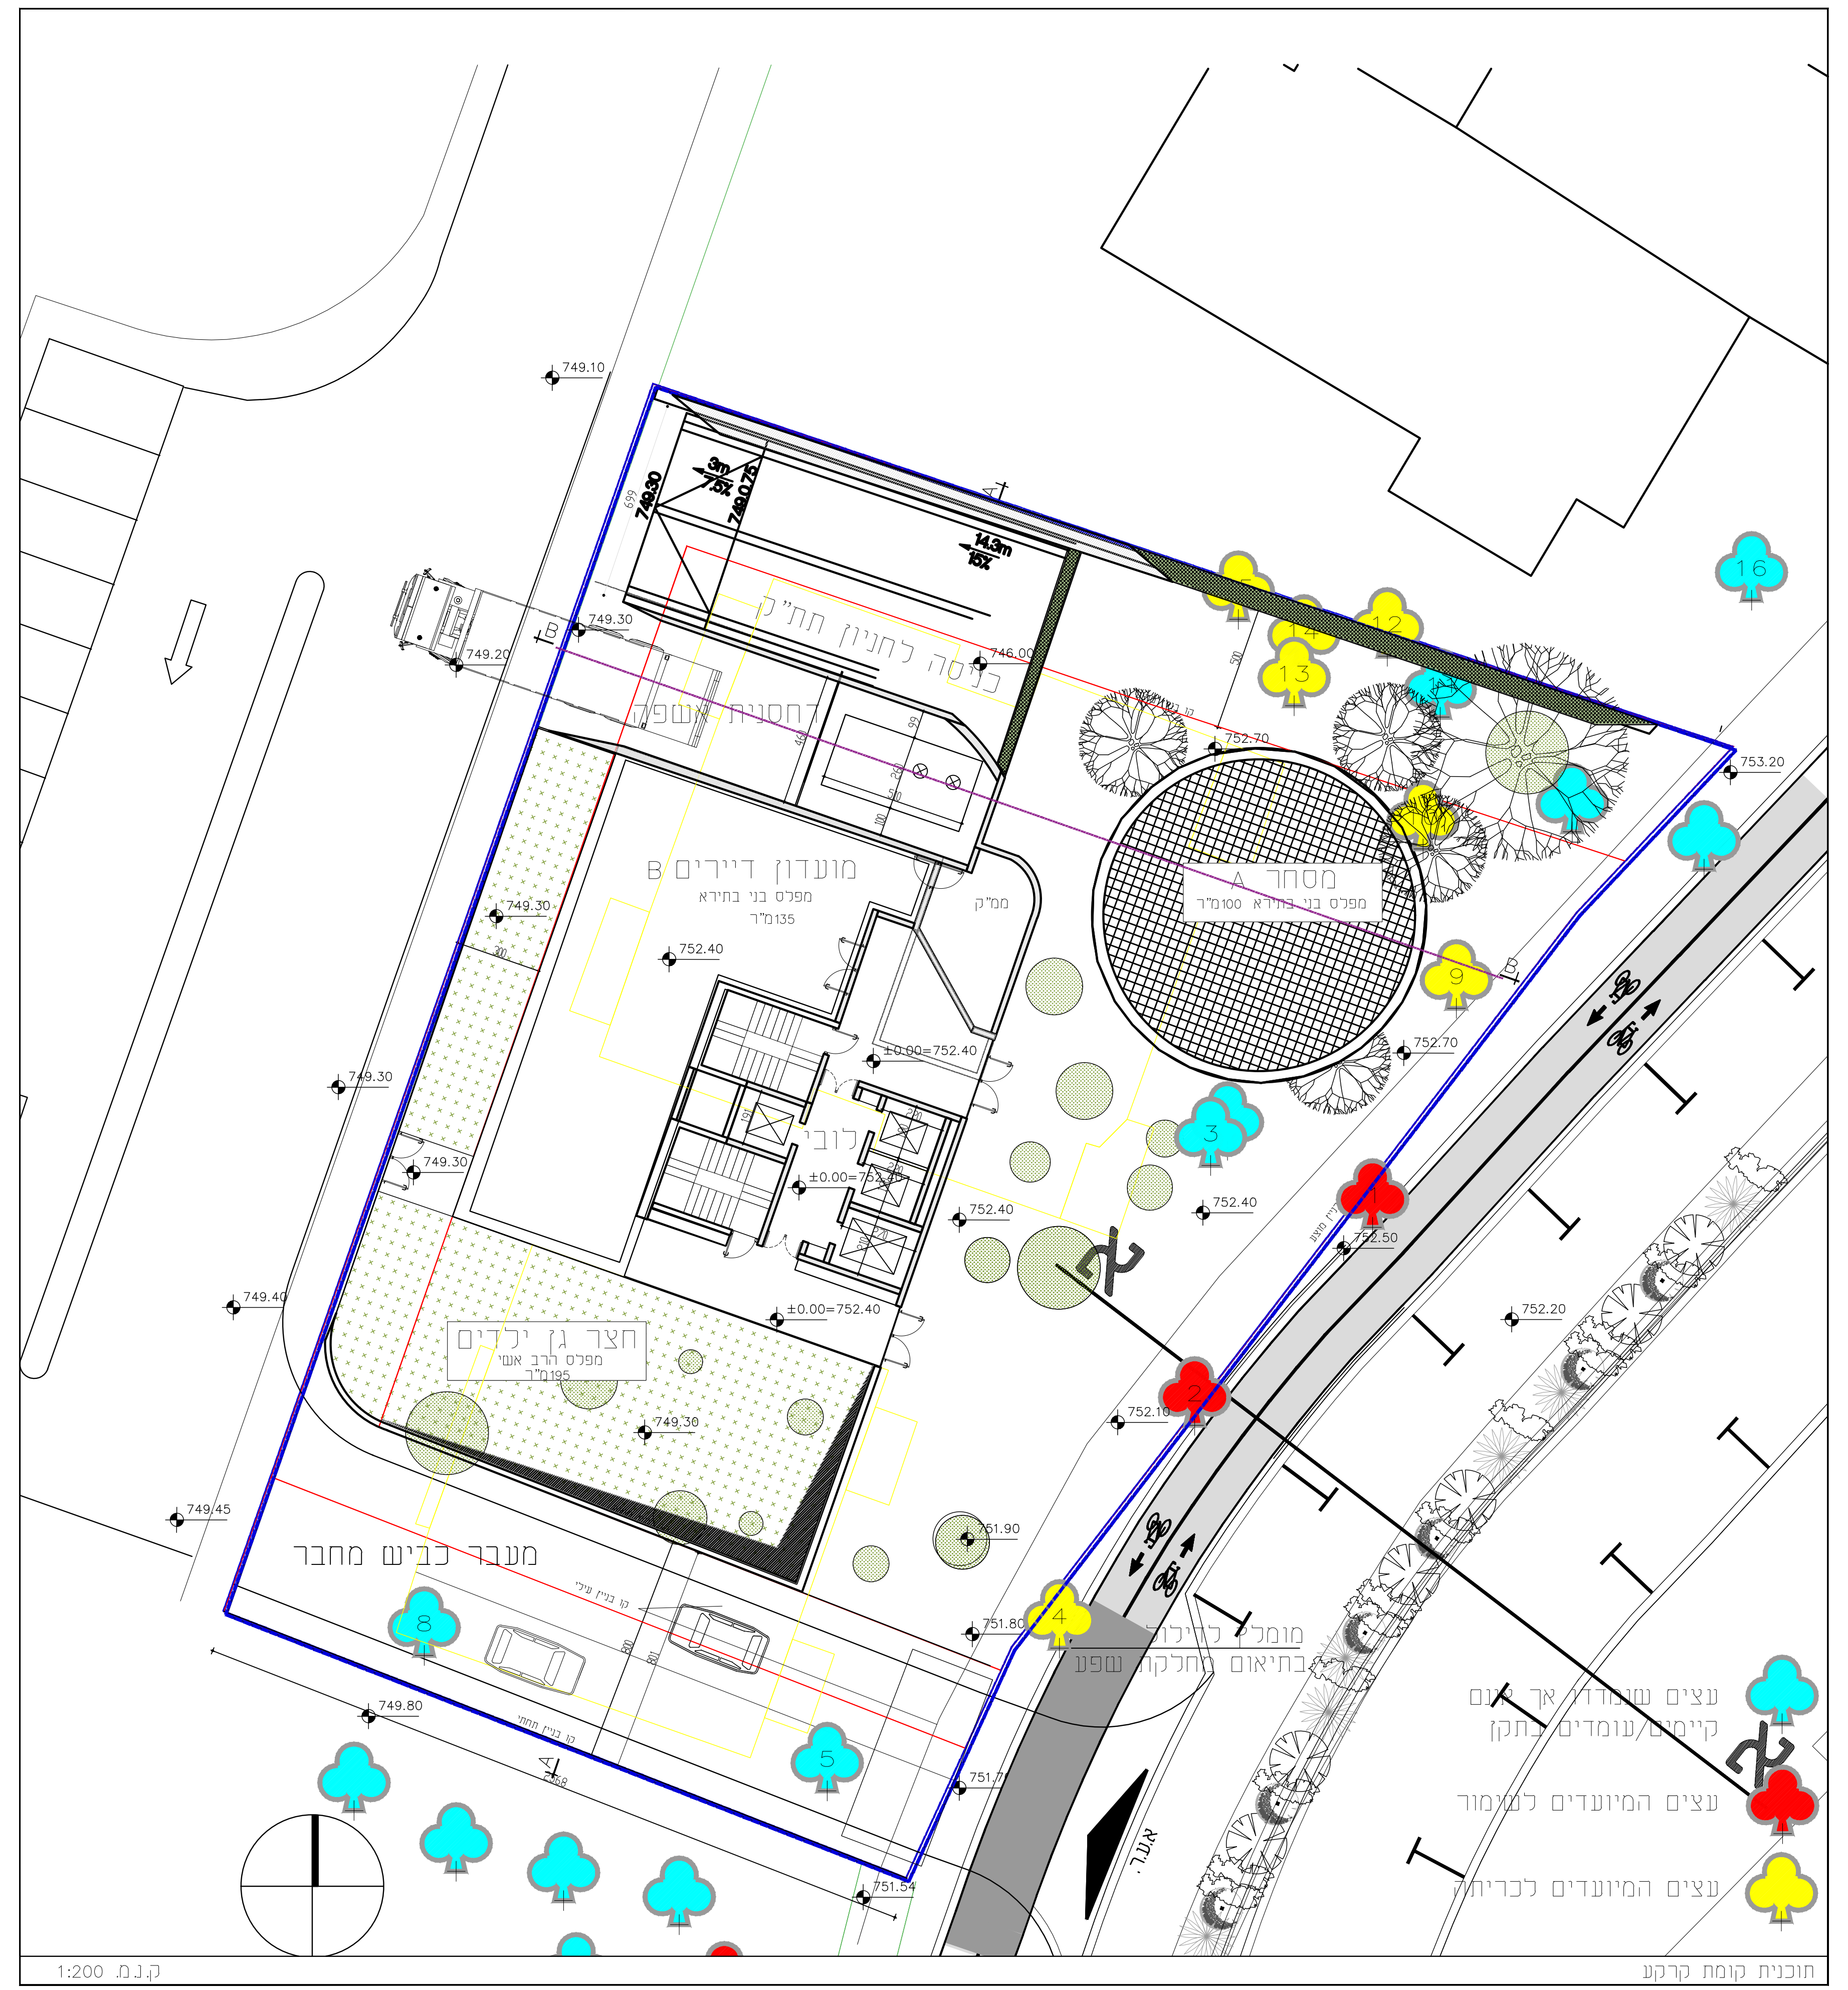
749.10
749.30
749.20
746.00
752.70
753.20
כניסה לחניון תת"ק
דחסנית אשפה
מועדון דיירים B
מפלס בני בתירא
135מ"ר
מסחר A
מפלס בני בתירא 100מ"ר
ממ"ק
752.40
±0.00=752.40
לובי
749.30
749.40
749.45
חצר גן ילדים
מפלס הרב אשי
195מ"ר
752.10
751.90
751.80
751.54
749.80
מעבר כביש מחבר
קו בניין עילי
קו בניין תחתי
מומלץ לגידול בתיאום מחלקת שפע
עצים שנמדדו אך אינם קיימים/עומדים בתקן
עצים המיועדים לשימור
עצים המיועדים לכריתה
א.ע.ר.
1:200 ק.נ.מ.
תוכנית קומת קרקע

תכנית מס'	101-1215656
בני בתירא 7-9 התחדשות עירונית	
נספח חתך	גליון 1 מתוך 1
תחולה	מנחה
תיאור	
תאריך	11.06.2026
תכניות, חתכים וחזיתות	קנ"מ 1:200

שמות וחתימות:		
עורך הנספח	שם: מיכל מאיר-יומא אדריכלים תאגיד:	חתימה:

מקרא

גבול מגרש	- - - - -
קו בניין תת"ק	— · — · —
קו בניין עילי	— — — —
מבנה לחריסה	———
עצים המיועדים לשימור	♣
עצים המיועדים לכריתה	♣
עצים שנמדדו אך אינם קיימים\עומדים בתקן	♣
סימון חתך רלוונטי	········