מינהל התכנון
חוק התכנון והבניה, התשכ"ה - 1965
תכנית 101-1386671 נספח תנועה נוסף 23/09/2026 11:01:15
מחוז ירושלים
הוועדה המחוזית החליטה ביום :
30/11/2025
להפקיד את התכנית
05/10/2026
יו"ר הוועדה המחוזית תאריך

קומת חניון -3

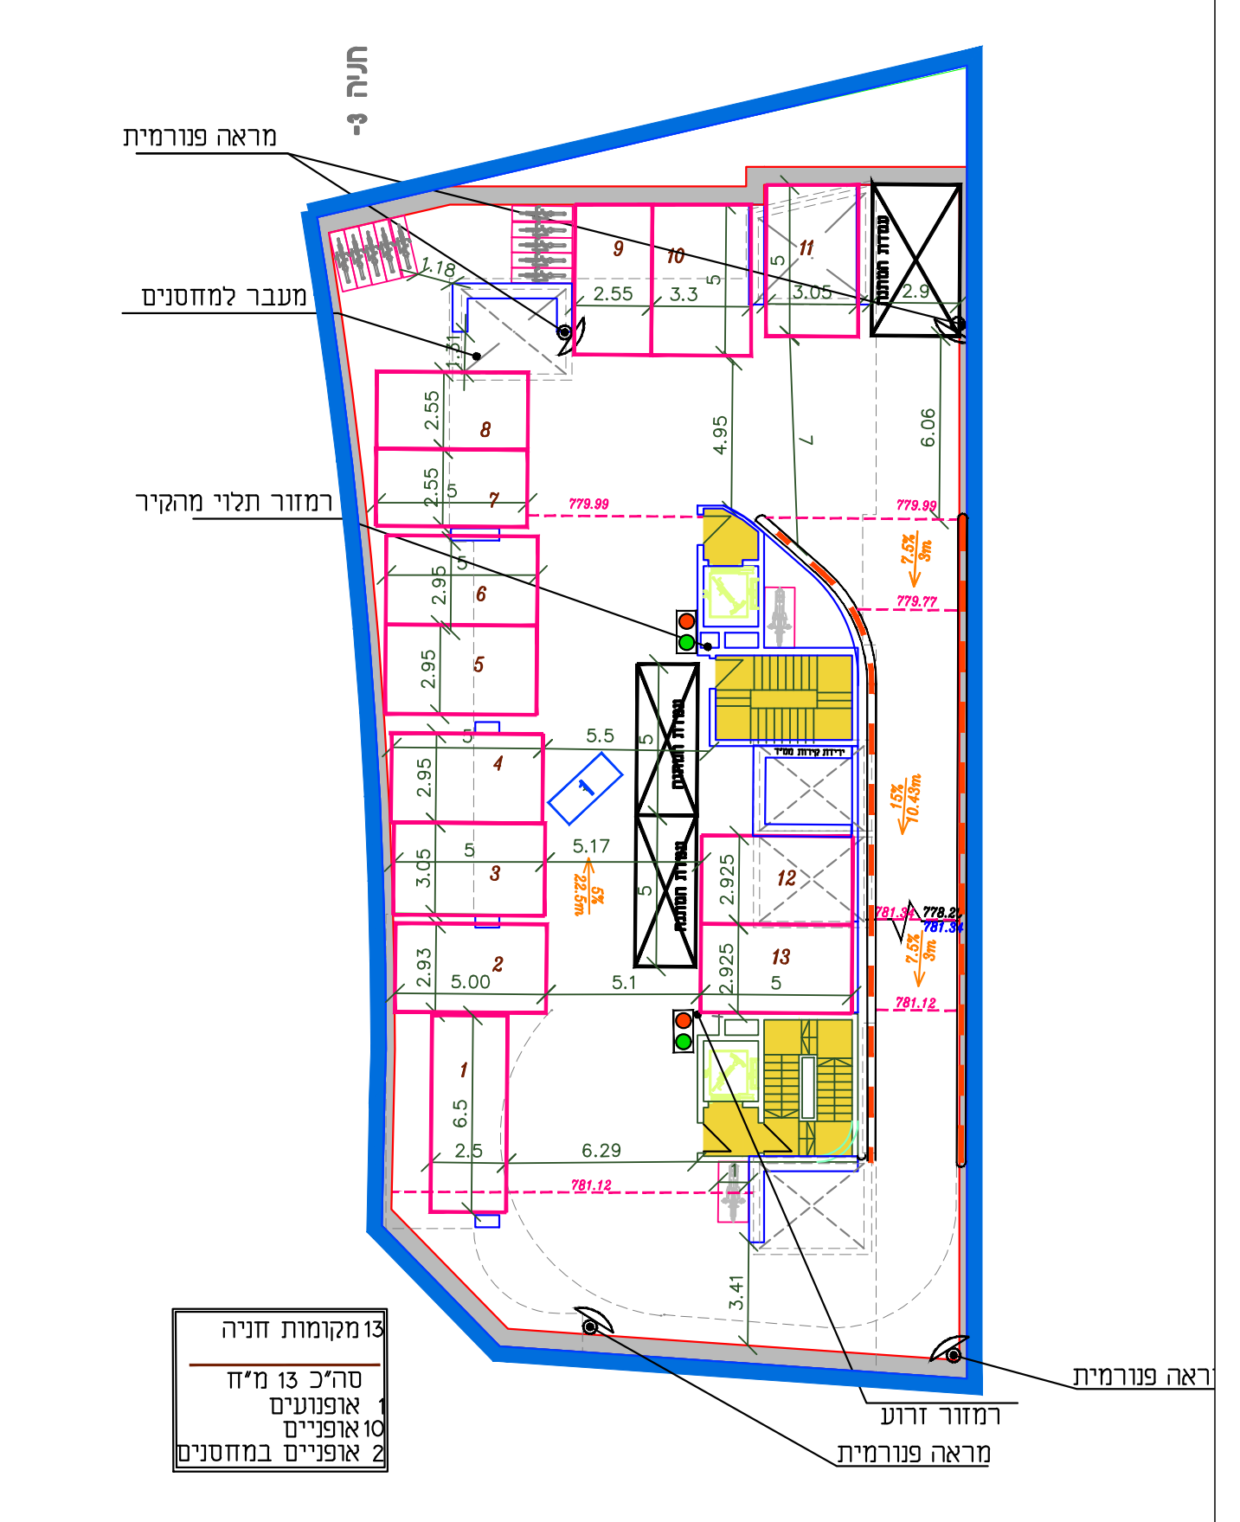

מראה פנורמית
רמזור זרוע
2.5
6.29
6.5
3.41
781.12

13 מקומות חניה
סה"כ 13 מ"ח
1 אופנועים
10 אופניים
2 אופניים במחסנים

קומת חניון -1

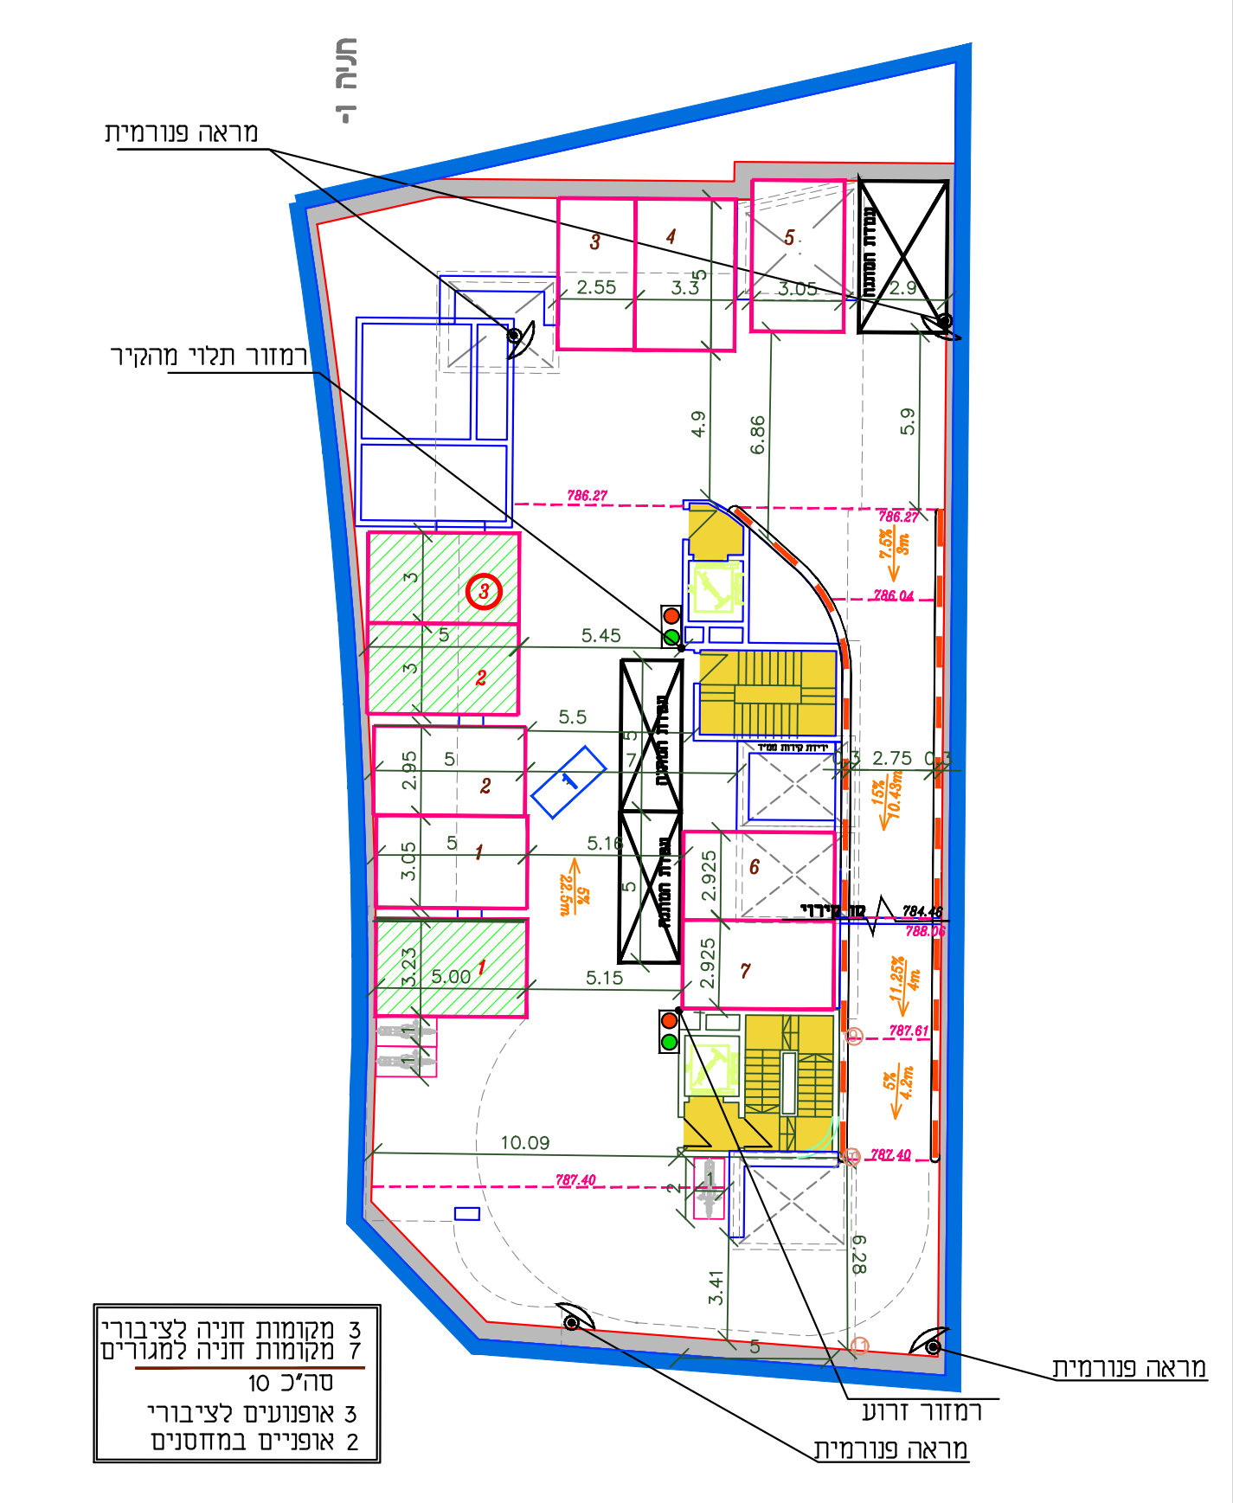

מראה פנורמית
רמזור זרוע
10.09
787.40
787.61
5%
4.2m
3.41
6.28
5

3 מקומות חניה לציבורי
7 מקומות חניה למגורים
סה"כ 10
3 אופנועים לציבורי
2 אופניים במחסנים

תמרון

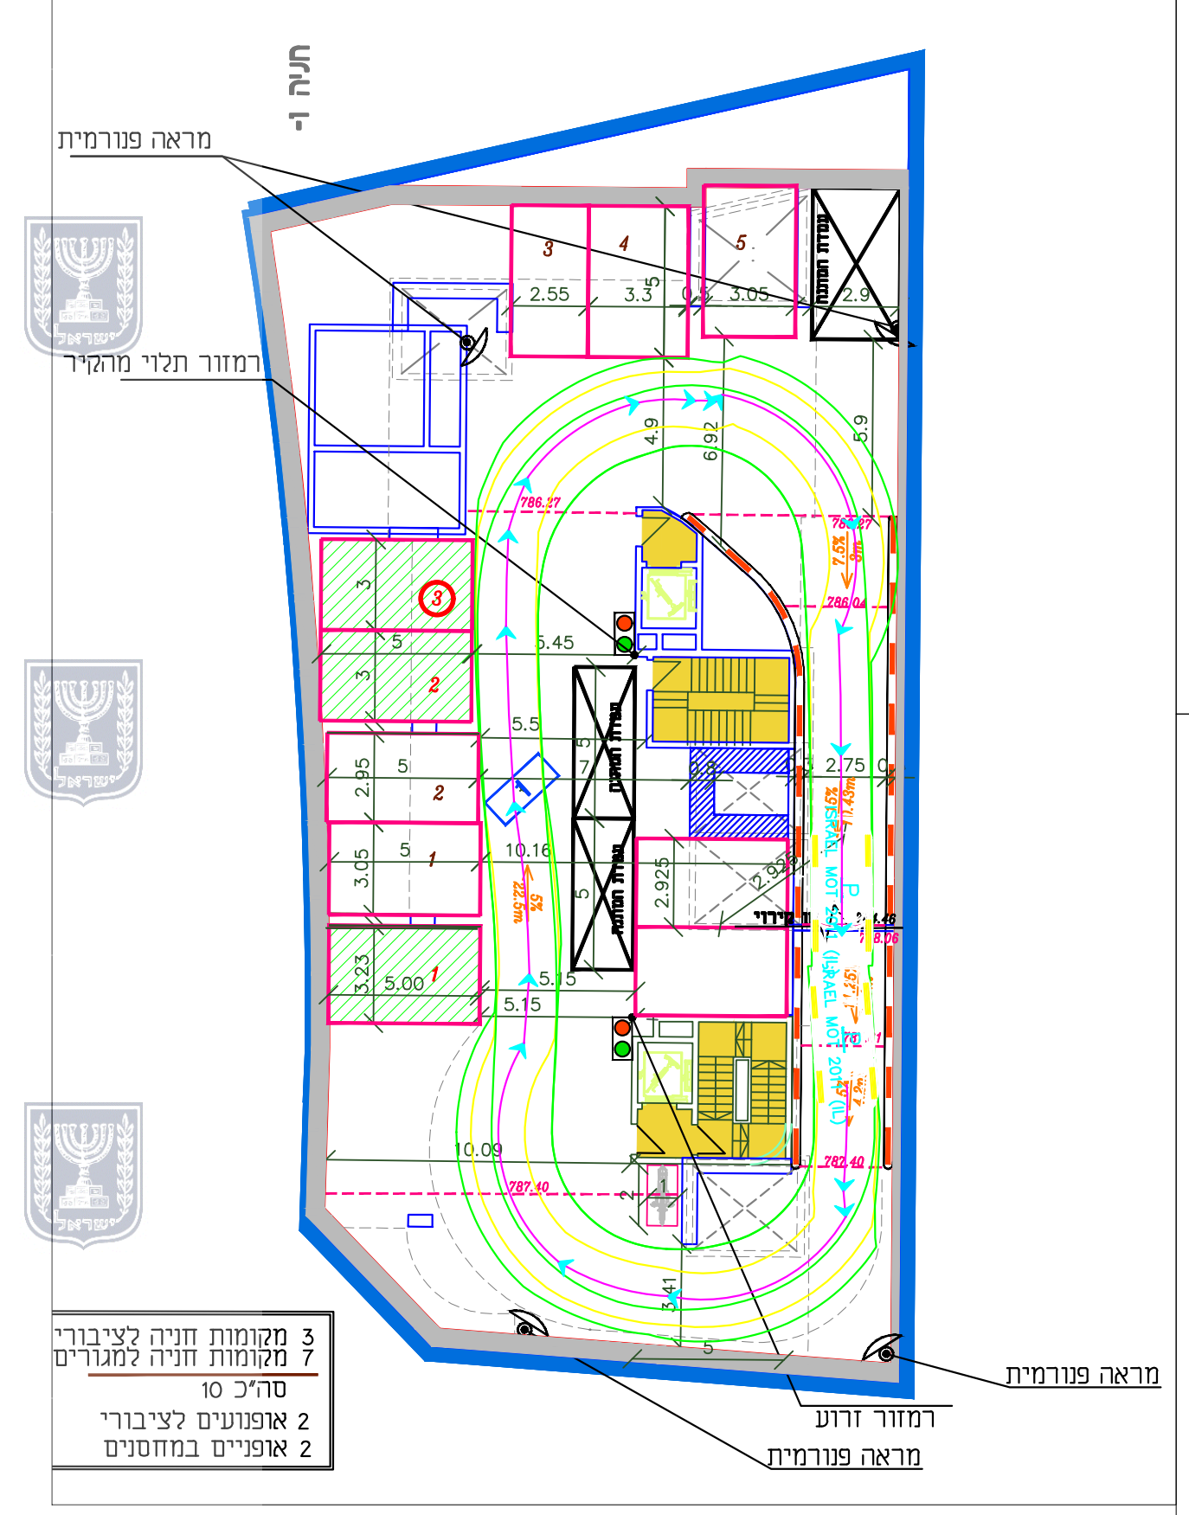

מראה פנורמית
רמזור זרוע
10.09
787.40
782.40
3.41
5

3 מקומות חניה לציבורי
7 מקומות חניה למגורים
סה"כ 10
2 אופנועים לציבורי
2 אופניים במחסנים

קומת חניון -4

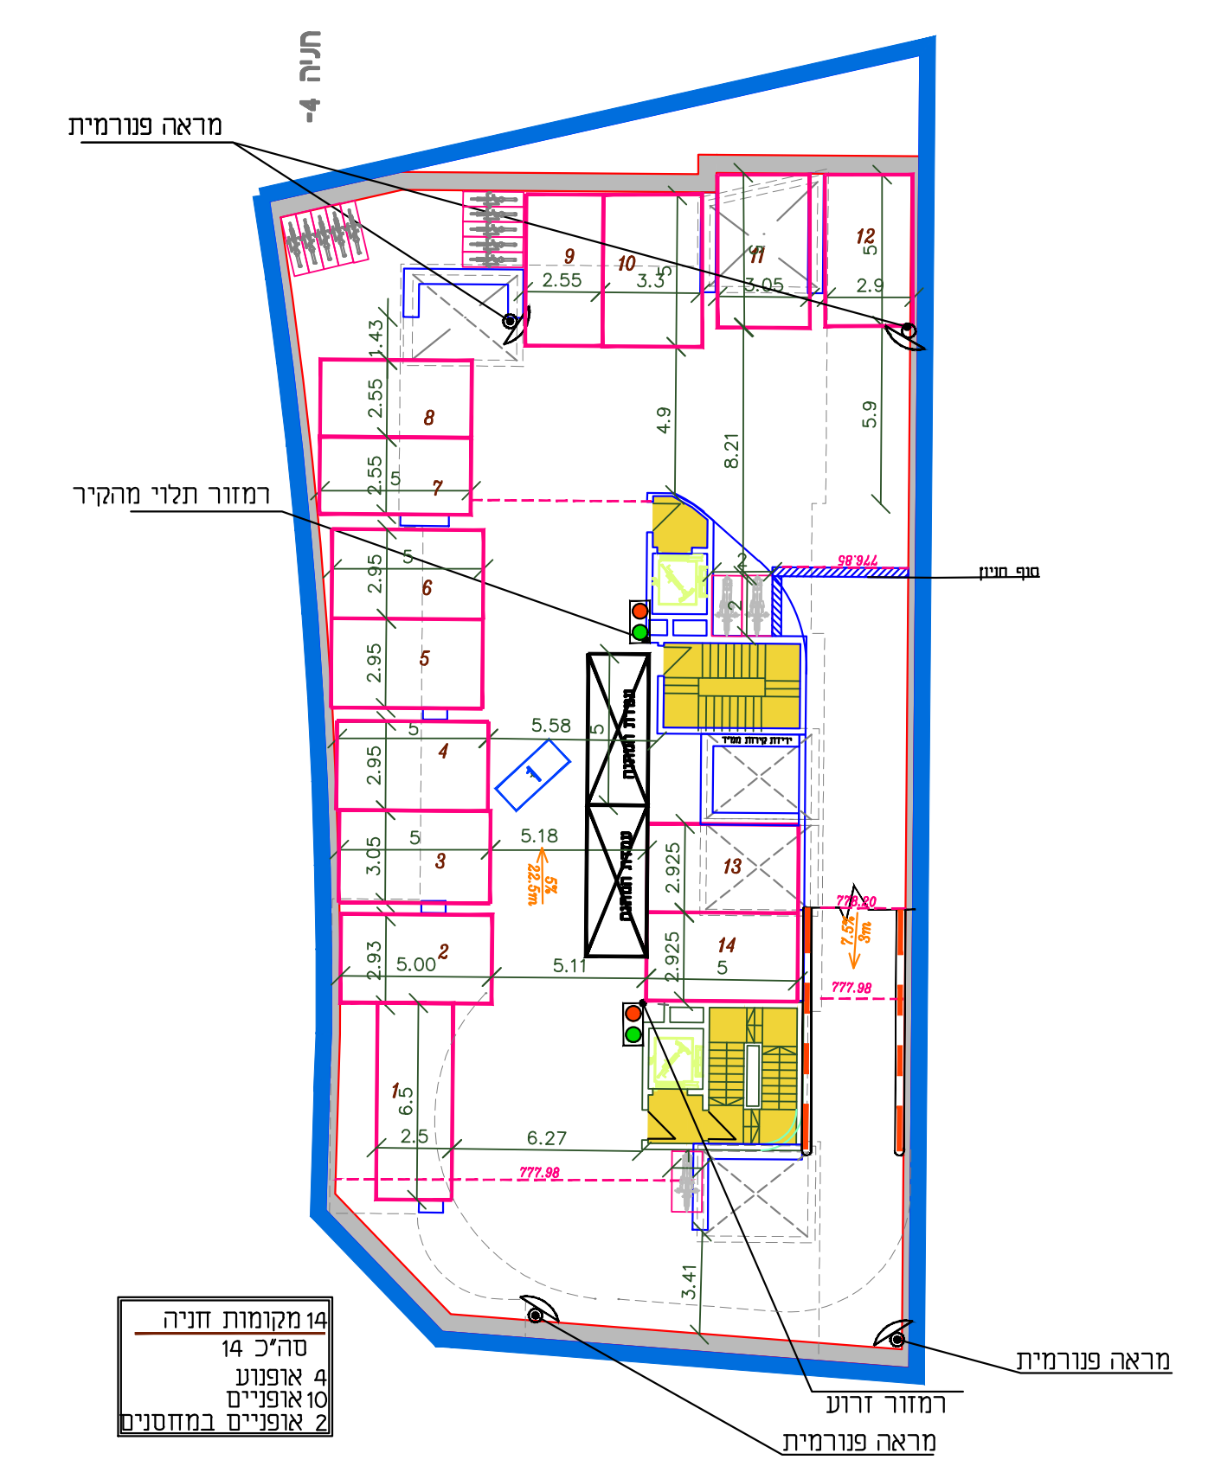

מראה פנורמית
רמזור זרוע
2.5
6.27
6.5
3.41
777.98

14 מקומות חניה
סה"כ 14
4 אופנוע
10 אופניים
2 אופניים במחסנים

קומת חניון -2

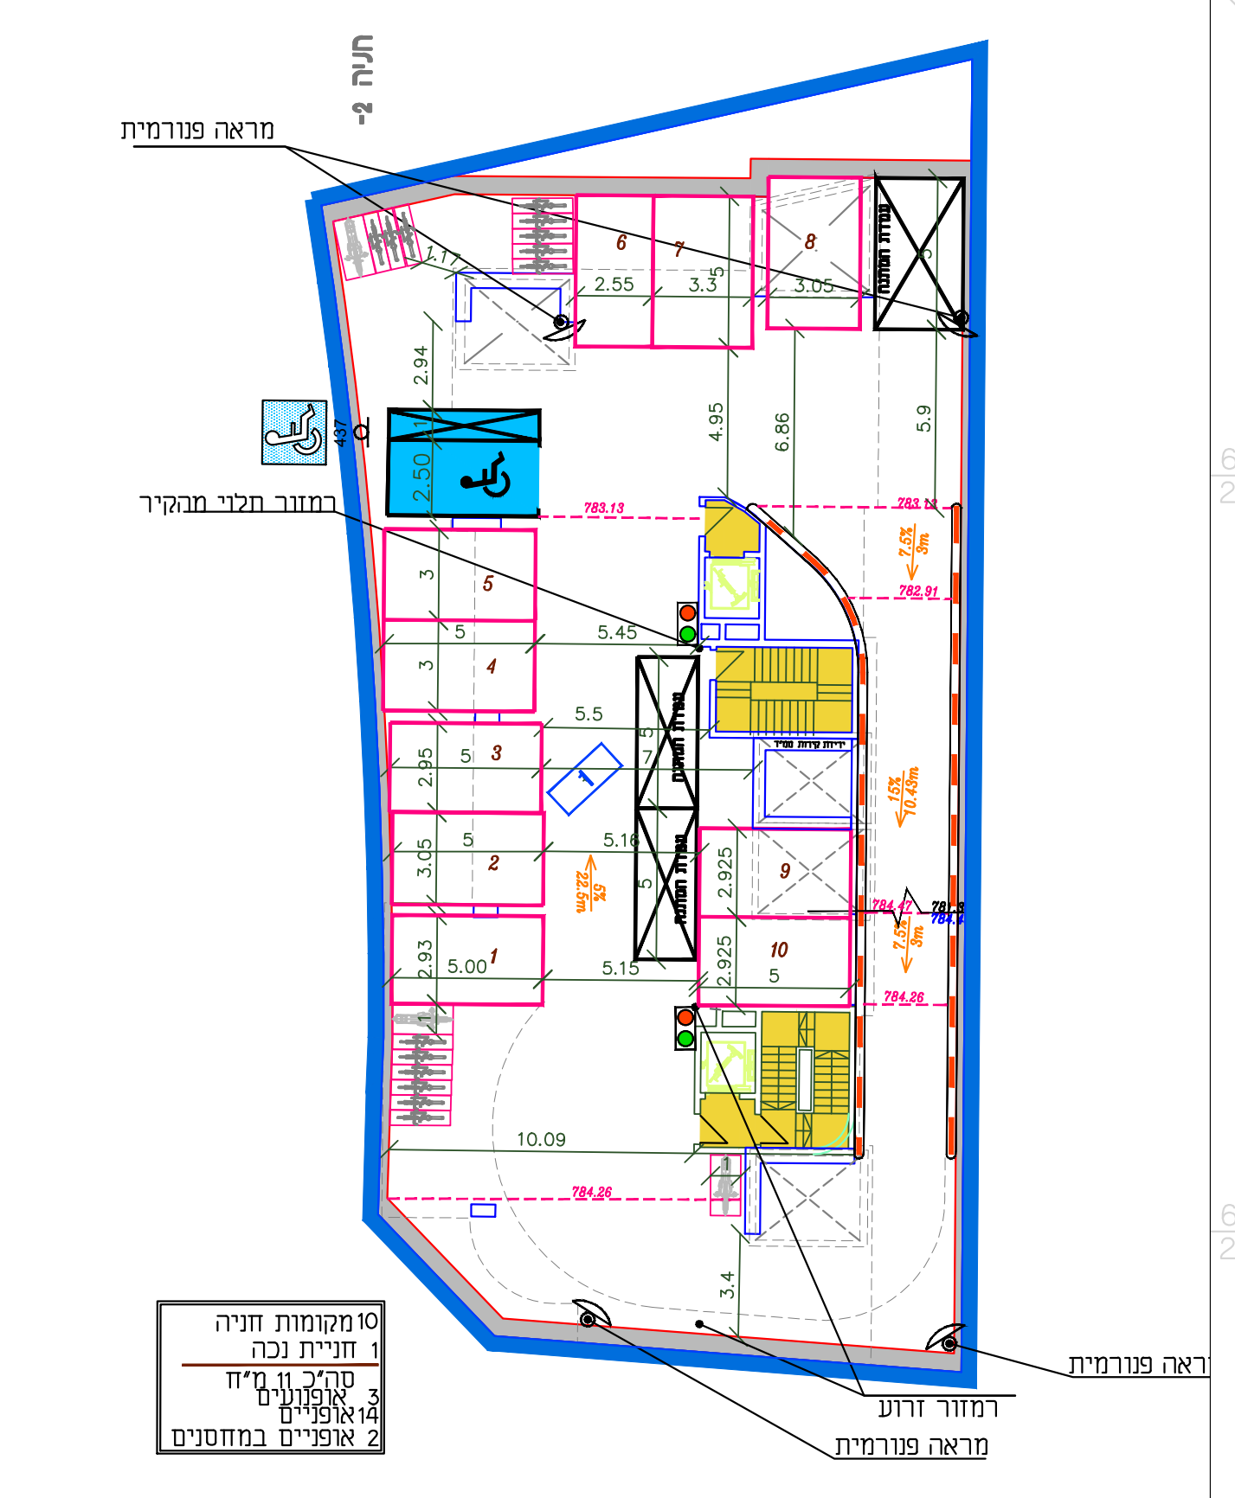

מראה פנורמית
רמזור זרוע
10.09
784.26
3.4

10 מקומות חניה
1 חניית נכה
סה"כ 11 מ"ח
3 אופנועים
14 אופניים
2 אופניים במחסנים

התחברות למצב קיים

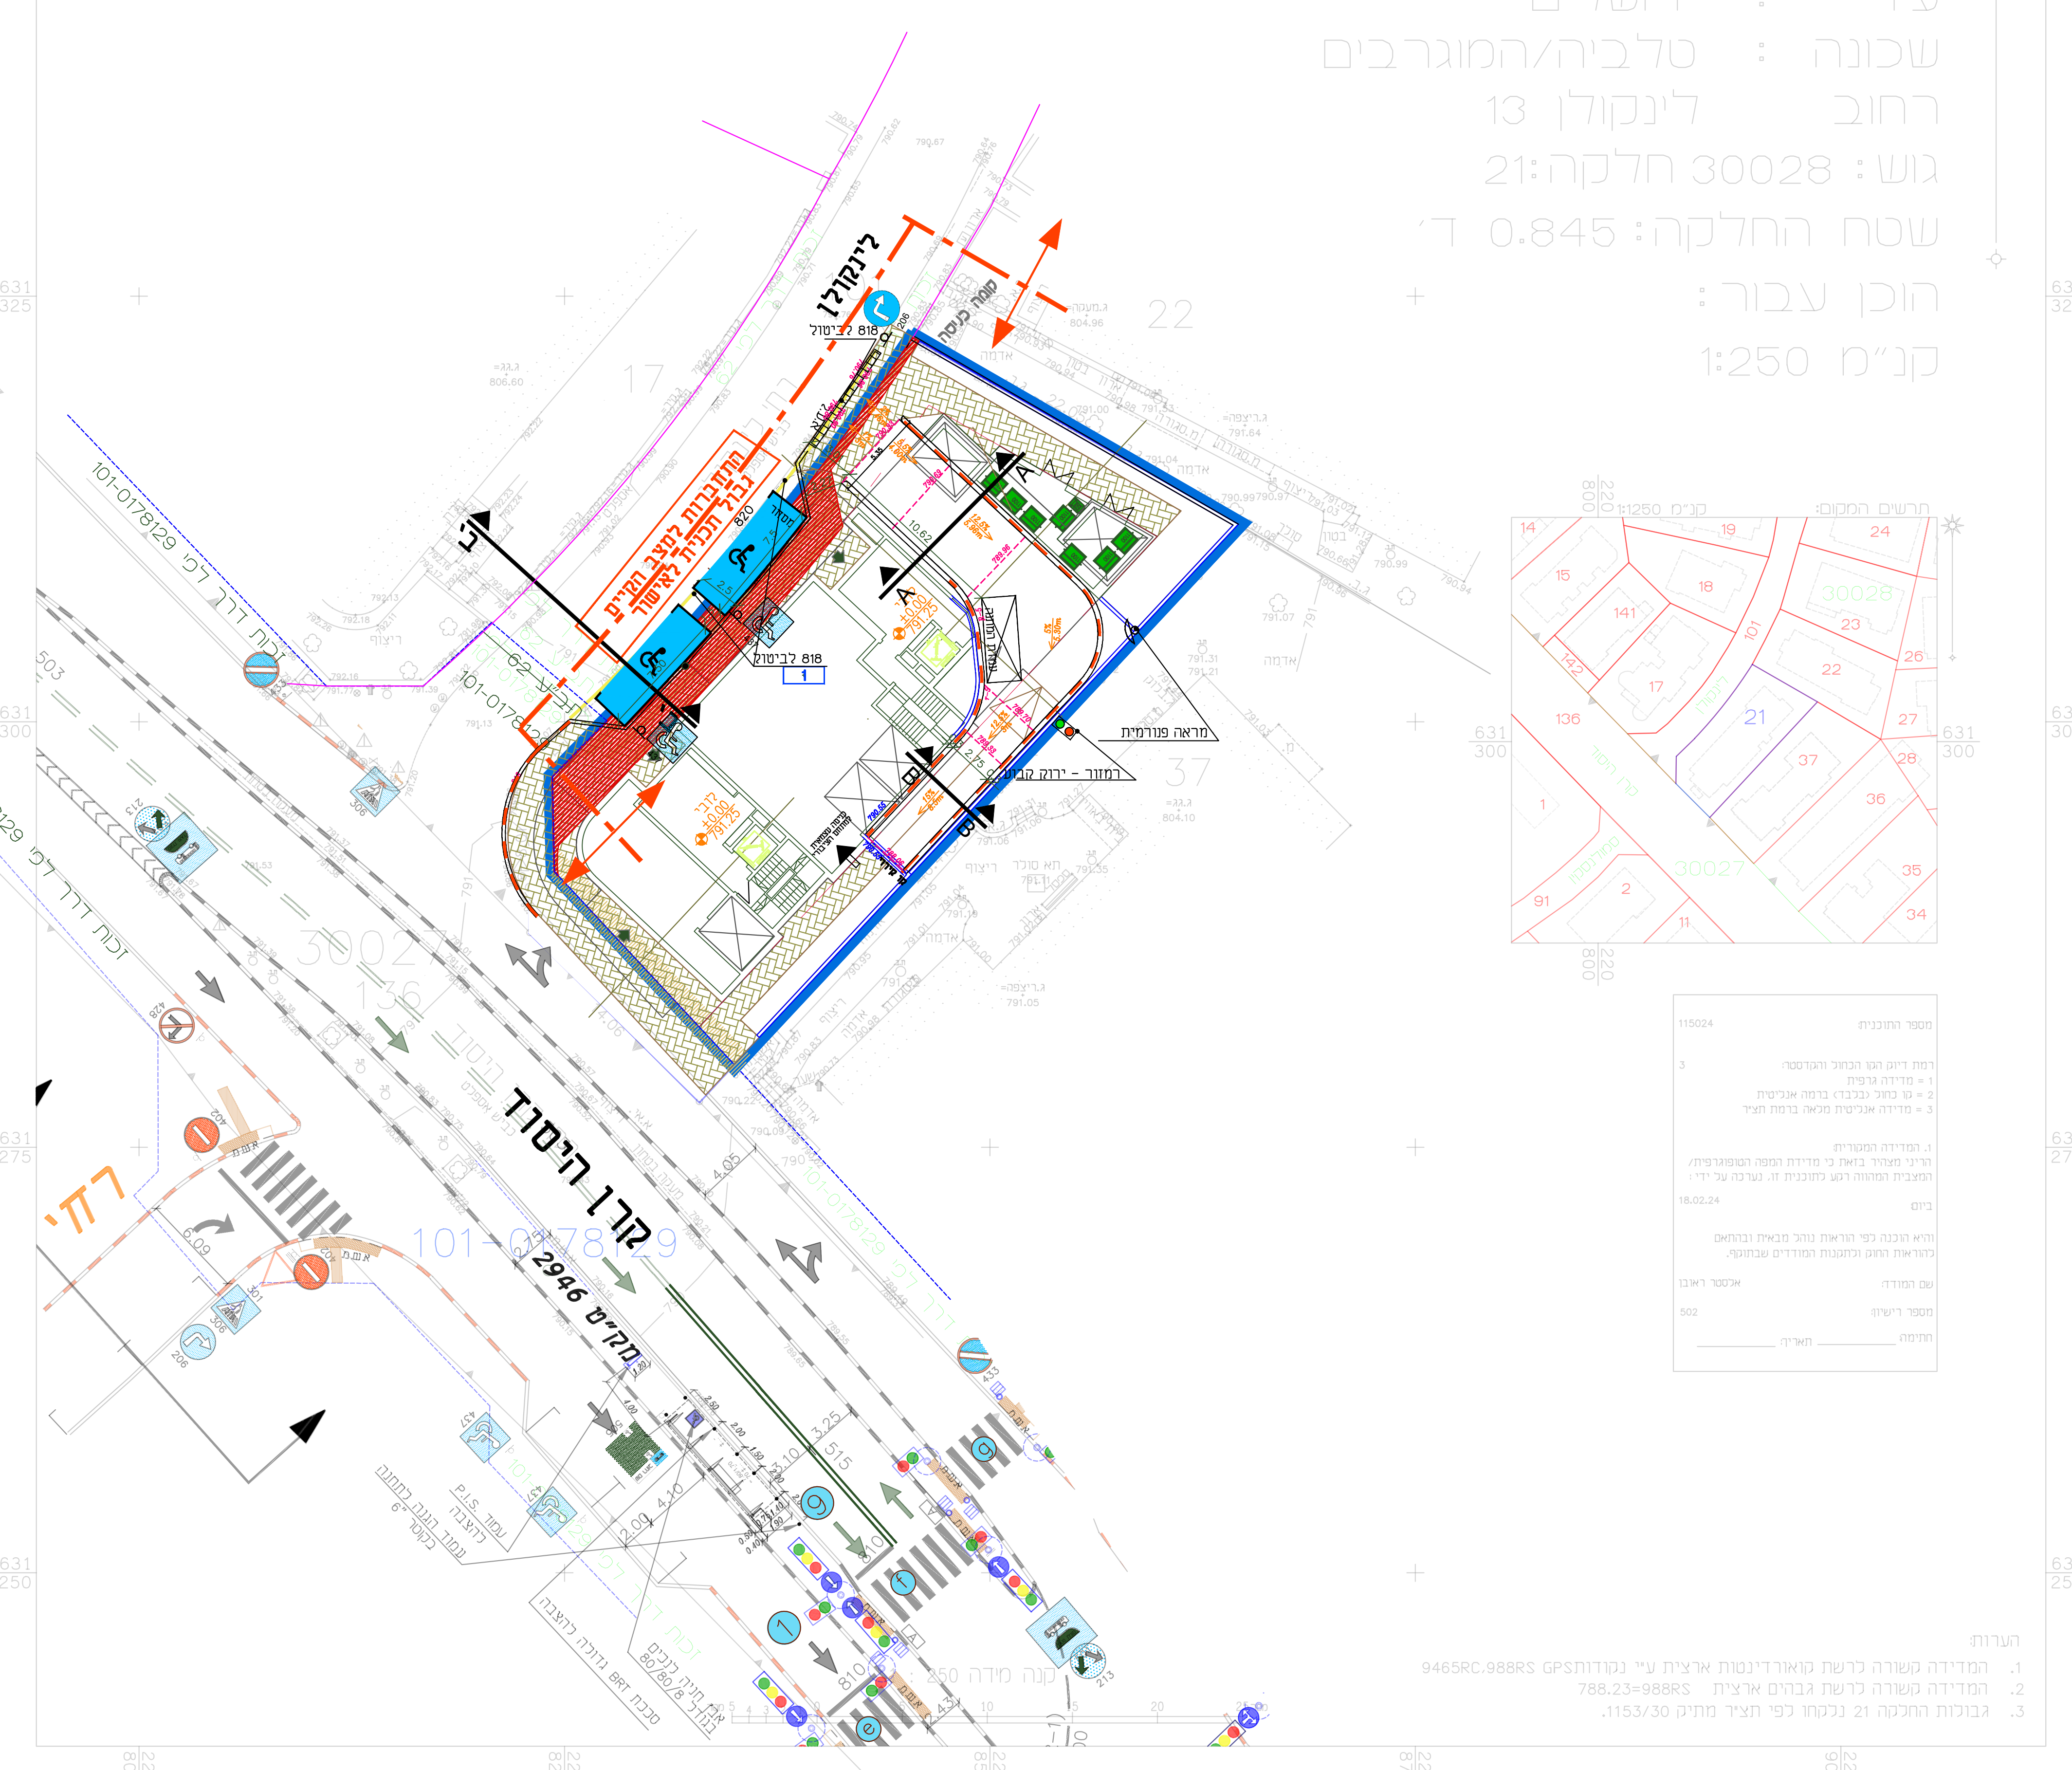

מחוז : ירושלים
נפה : ירושלים
עיר : ירושלים
שכונה : טלביה/המוגרבים
רחוב לינקולן 13
גוש : 30028 חלקה: 21
שטח החלקה: 0.845 ד'
הוכן עבור :
קנ"מ 1:250
לינקולן
קרן היסוד
רק"ל

התחברות למצב רק"ל

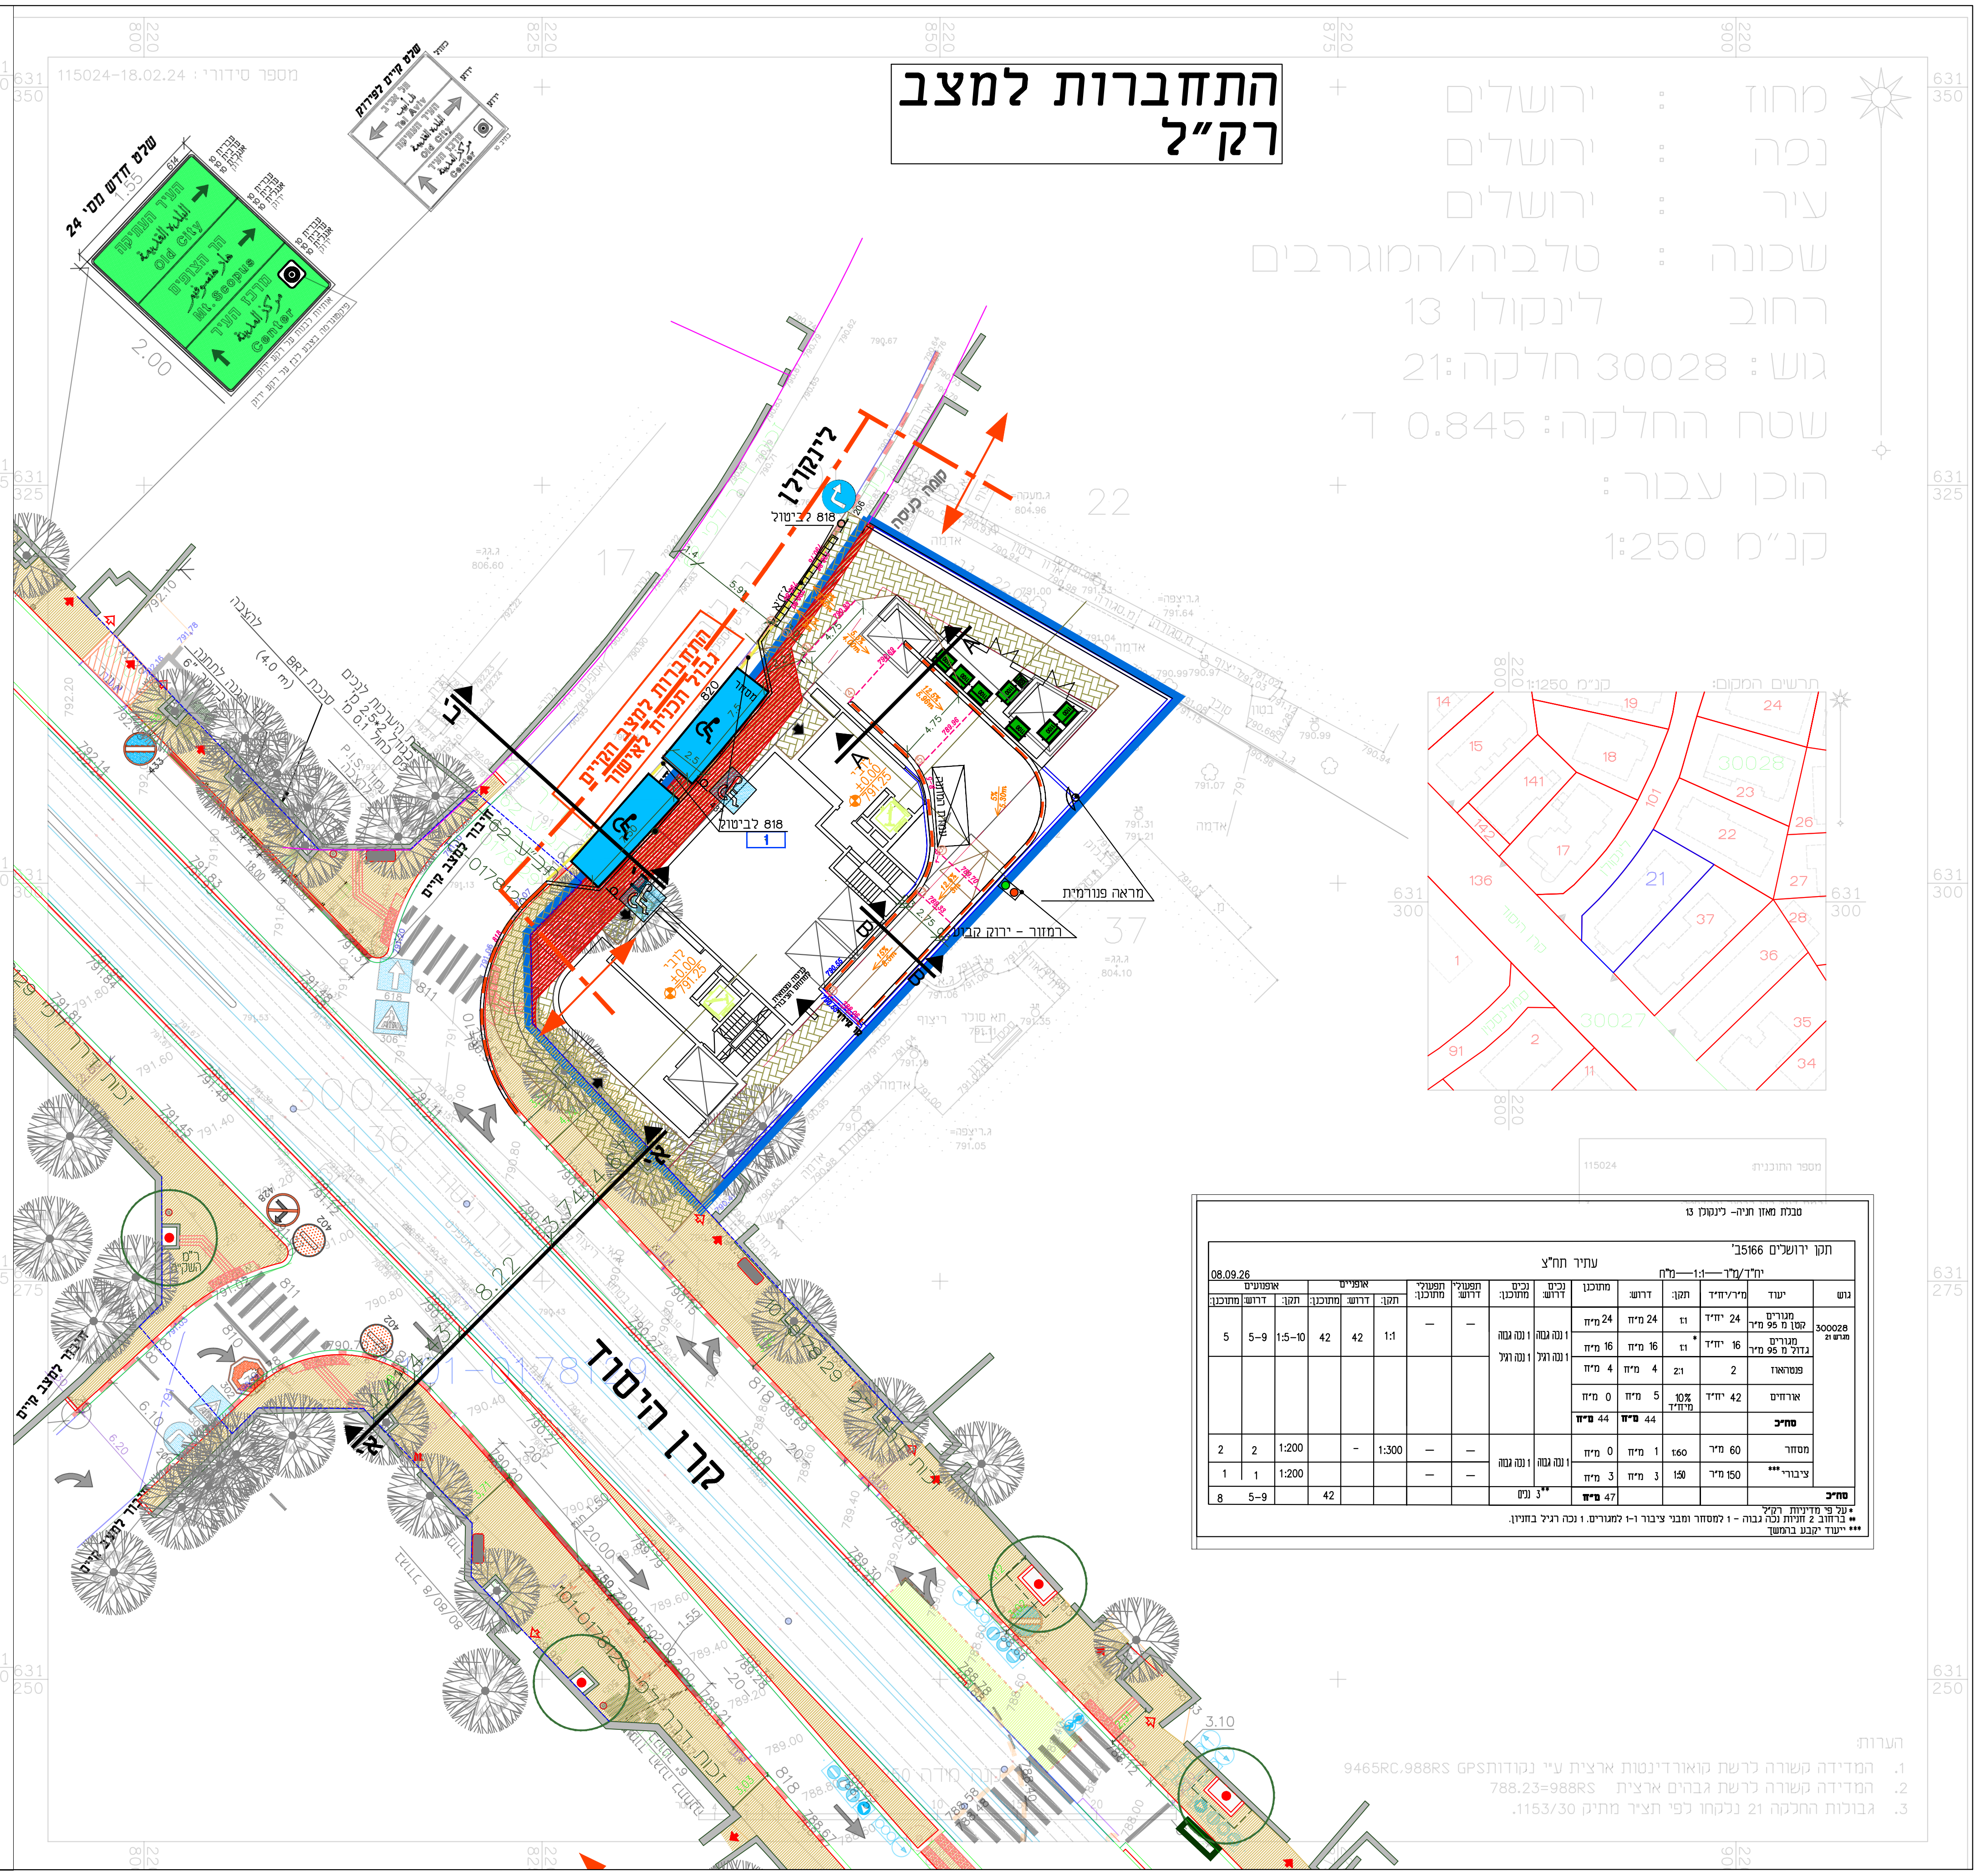

שלט חדש מס' 24
לינקולן
קרן היסוד
מחוז : ירושלים
נפה : ירושלים
עיר : ירושלים
שכונה : טלביה/המוגרבים
רחוב לינקולן 13
גוש : 30028 חלקה: 21
שטח החלקה: 0.845 ד'
הוכן עבור :
קנ"מ 1:250

טבלת מאזן חניה- לינקולן 13

תקן ירושלים 5166ב'
עתיר תח"צ
יח"ד/מ"ר—1:1—מ"ח
08.09.26

גוש	יעוד	מ"ר/יח"ד	תקן:	דרוש:	מתוכנן	נכים דרוש:	נכים מתוכנן:	תפעולי דרוש:	תפעולי מתוכנן:	אופניים תקן:	אופניים דרוש:	אופניים מתוכנן:	אופנועים תקן:	אופנועים דרוש:	אופנועים מתוכנן:
300028 מגרש 21	מגורים קטן מ 95 מ"ר	24 יח"ד	1:1	24 מ"ח	24 מ"ח	1 נכה גבוה 1 נכה רגיל	1 נכה גבוה 1 נכה רגיל	—	—	1:1	42	42	1:5-10	5-9	5
	מגורים גדול מ 95 מ"ר	16 יח"ד	*1:1	16 מ"ח	16 מ"ח										
	פנטהאוז	2	2:1	4 מ"ח	4 מ"ח										
	אורחים	42 יח"ד	10% מיח"ד	5 מ"ח	0 מ"ח										
	סה"כ			**44 מ"ח**	**44 מ"ח**										
	מסחר	60 מ"ר	1:60	1 מ"ח	0 מ"ח	1 נכה גבוה	1 נכה גבוה	—	—	1:300	-		1:200	2	2
	ציבורי***	150 מ"ר	1:50	3 מ"ח	3 מ"ח			—	—				1:200	1	1
סה"כ					**47 מ"ח**	3** נכים						42		5-9	8

* על פי מדיניות רקי"ל
** ברחוב 2 חניות נכה גבוה - 1 למסחר ומבני ציבור ו-1 למגורים. 1 נכה רגיל בחניון.
*** ייעוד יקבע בהמשך

חתך ב' - ב'

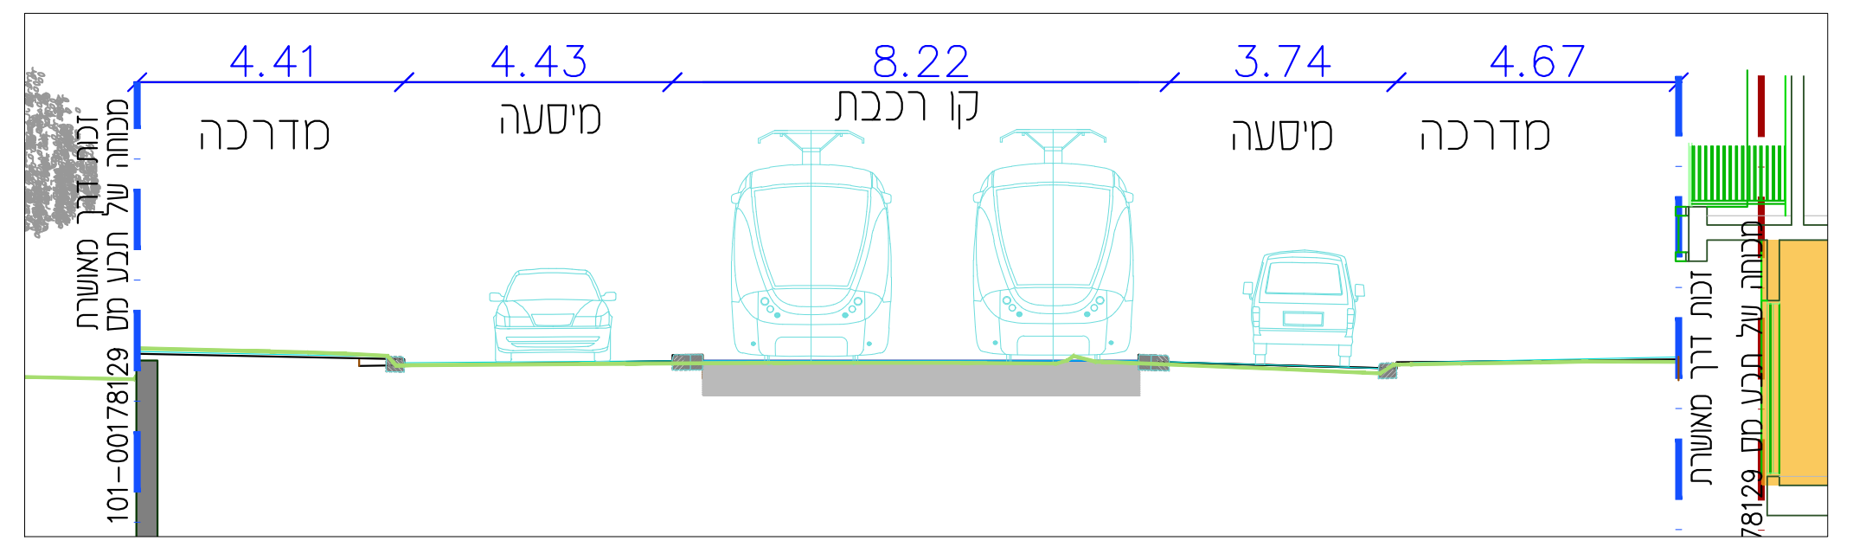

4.41
4.43
8.22
3.74
4.67
מדרכה
מיסעה
קו רכבת
מיסעה
מדרכה
זכות דרך מאושרת
מכוח של תבע מס 101-00178129

חתך א' א' רחוב קרן היסוד
חתך A–A
חתך רוחב רמפה חד סטרית
חתך B–B

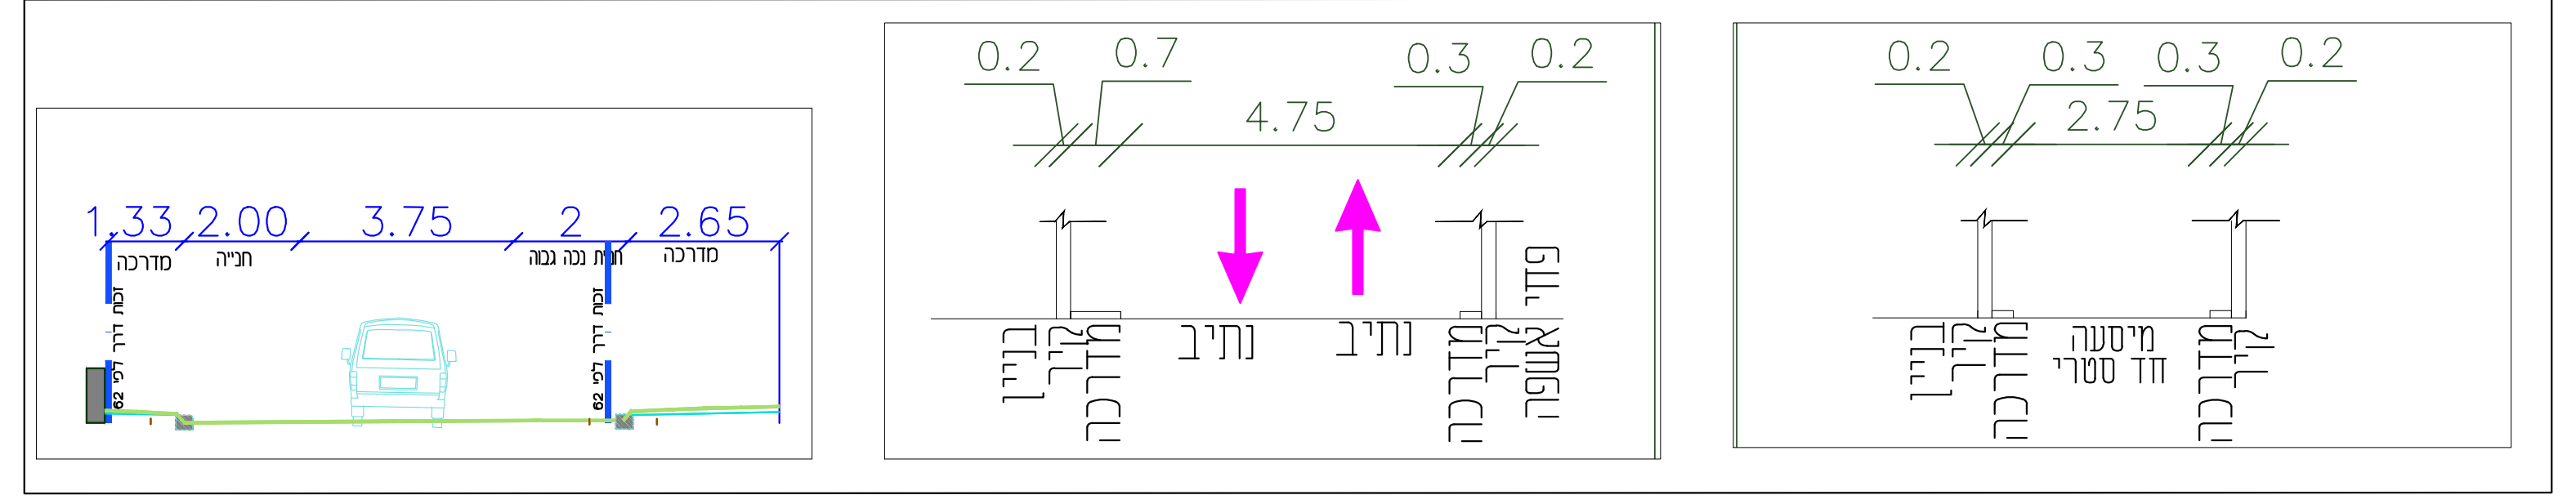

1.33
2.00
3.75
2
2.65
מדרכה
חנייה
מדרכה
0.2
0.7
4.75
0.3
0.2
בניין
קיר
מדרכה
נתיב
נתיב
מדרכה
קיר
פודי אשפה
0.2
0.3
2.75
0.3
0.2
בניין
קיר
מדרכה
מיסעה חד סטרי
קיר
מדרכה

חתך אורך קנ"מ 1:125
אורך הרמפה ברוחב חד סטרי מתפקדת דו סטרי

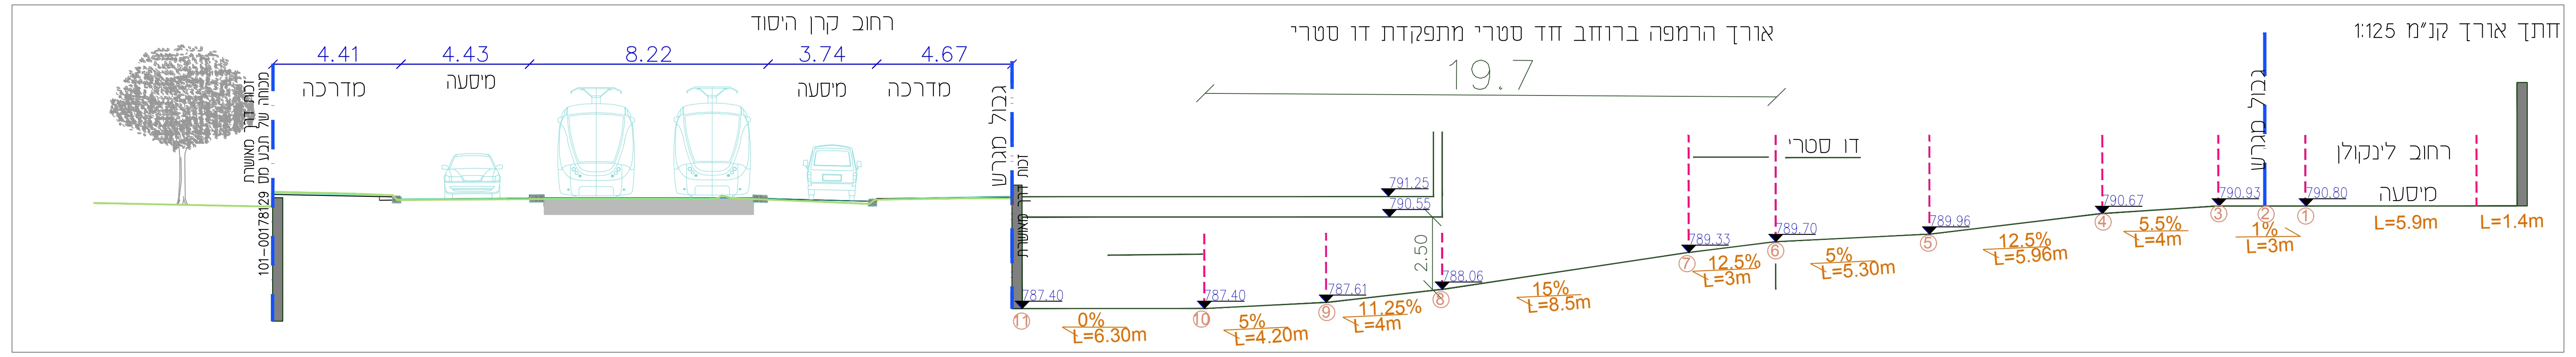

רחוב קרן היסוד
4.41
4.43
8.22
3.74
4.67
מדרכה
מיסעה
מיסעה
מדרכה
גבול מגרש
זכות דרך מאושרת
19.7
דו סטרי
גבול מגרש
רחוב לינקולן
מיסעה
791.25
790.55
2.50
787.40
787.40
787.61
788.06
789.33
789.70
789.96
790.67
790.93
790.80
0%
L=6.30m
5%
L=4.20m
11.25%
L=4m
15%
L=8.5m
12.5%
L=3m
5%
L=5.30m
12.5%
L=5.96m
5.5%
L=4m
1%
L=3m
L=5.9m
L=1.4m

תכנית מס' 101-1386671

לינקולן 13

מחוז	
מרחב תכנון מקומי	
	ירושלים
קנה מידה	**1:250**

תרשים סביבה ללא קנ"מ

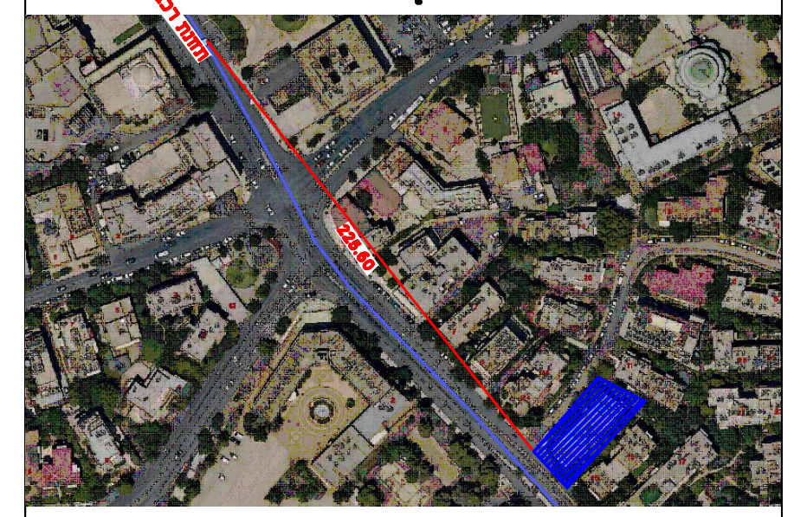

תחנת רכבת
225.60

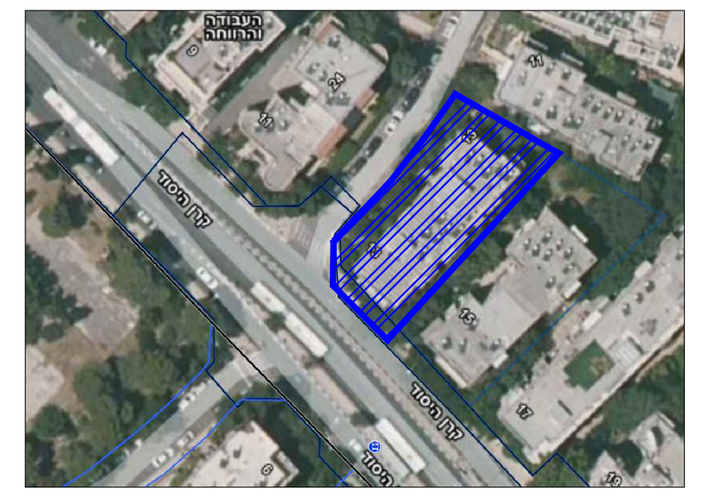

מקרא:

גבול מגרש	▬
קו זכות הדרך	▬
קו בניין	- - -
מדרכה	🟧
אספלט	▩
חניה מתוכננת	▭
חניית אופנוע	▭
זיקת הנאה	▨
חניות ציבוריות	🟩

רוזטה – לא קיימת רוזטה על פי מידע מהמודד ומהתשריט

שמות

עורך הנספח

אלבוחר משה
מהנדס רישיון 00114972

טלפון : 02-6795581
פקס : 02-6795571
office@albocher-eng.co.il

מהדורה: 01 **24.8.2026**

משה אלבוחר שירותי הנדסה בע"מ
תכנון תנועה וכבישים
דוא"ל: Office@albocher-eng.co.il