מינהל התכנון
חוק התכנון והבניה, התשכ"ה - 1965
מחוז ירושלים
הוועדה המחוזית החליטה ביום :
30/10/2023
להפקיד את התכנית
14/10/2026
יו"ר הוועדה המחוזית תאריך

תכנית 101-1095330 נספח ביוב וניקוז נספח ניקוז וניהול נגר עילי 15:36:50 04/01/2026

נספח ניקוז וניהול נגר עילי

תכנית מס' 101-1095330

שם התכנית
מתחם רג'ואן - הסדנא-פייר קניג
ירושלים

גליון 1 מתוך 1

מנחה

תאריך עריכת הנספח 03/11/2024

קנ"מ 1:250

שמות וחתימות
עורך הנספח שם: מרפיר פרויקטים
תאגיד:

גוש	סוג הגוש	חלקה	מגרש
30140	מוסדר	8	

שטח התכנית 13,337 מ"ר נ.צ : 220391/628562

רשימת תכניות חלות :

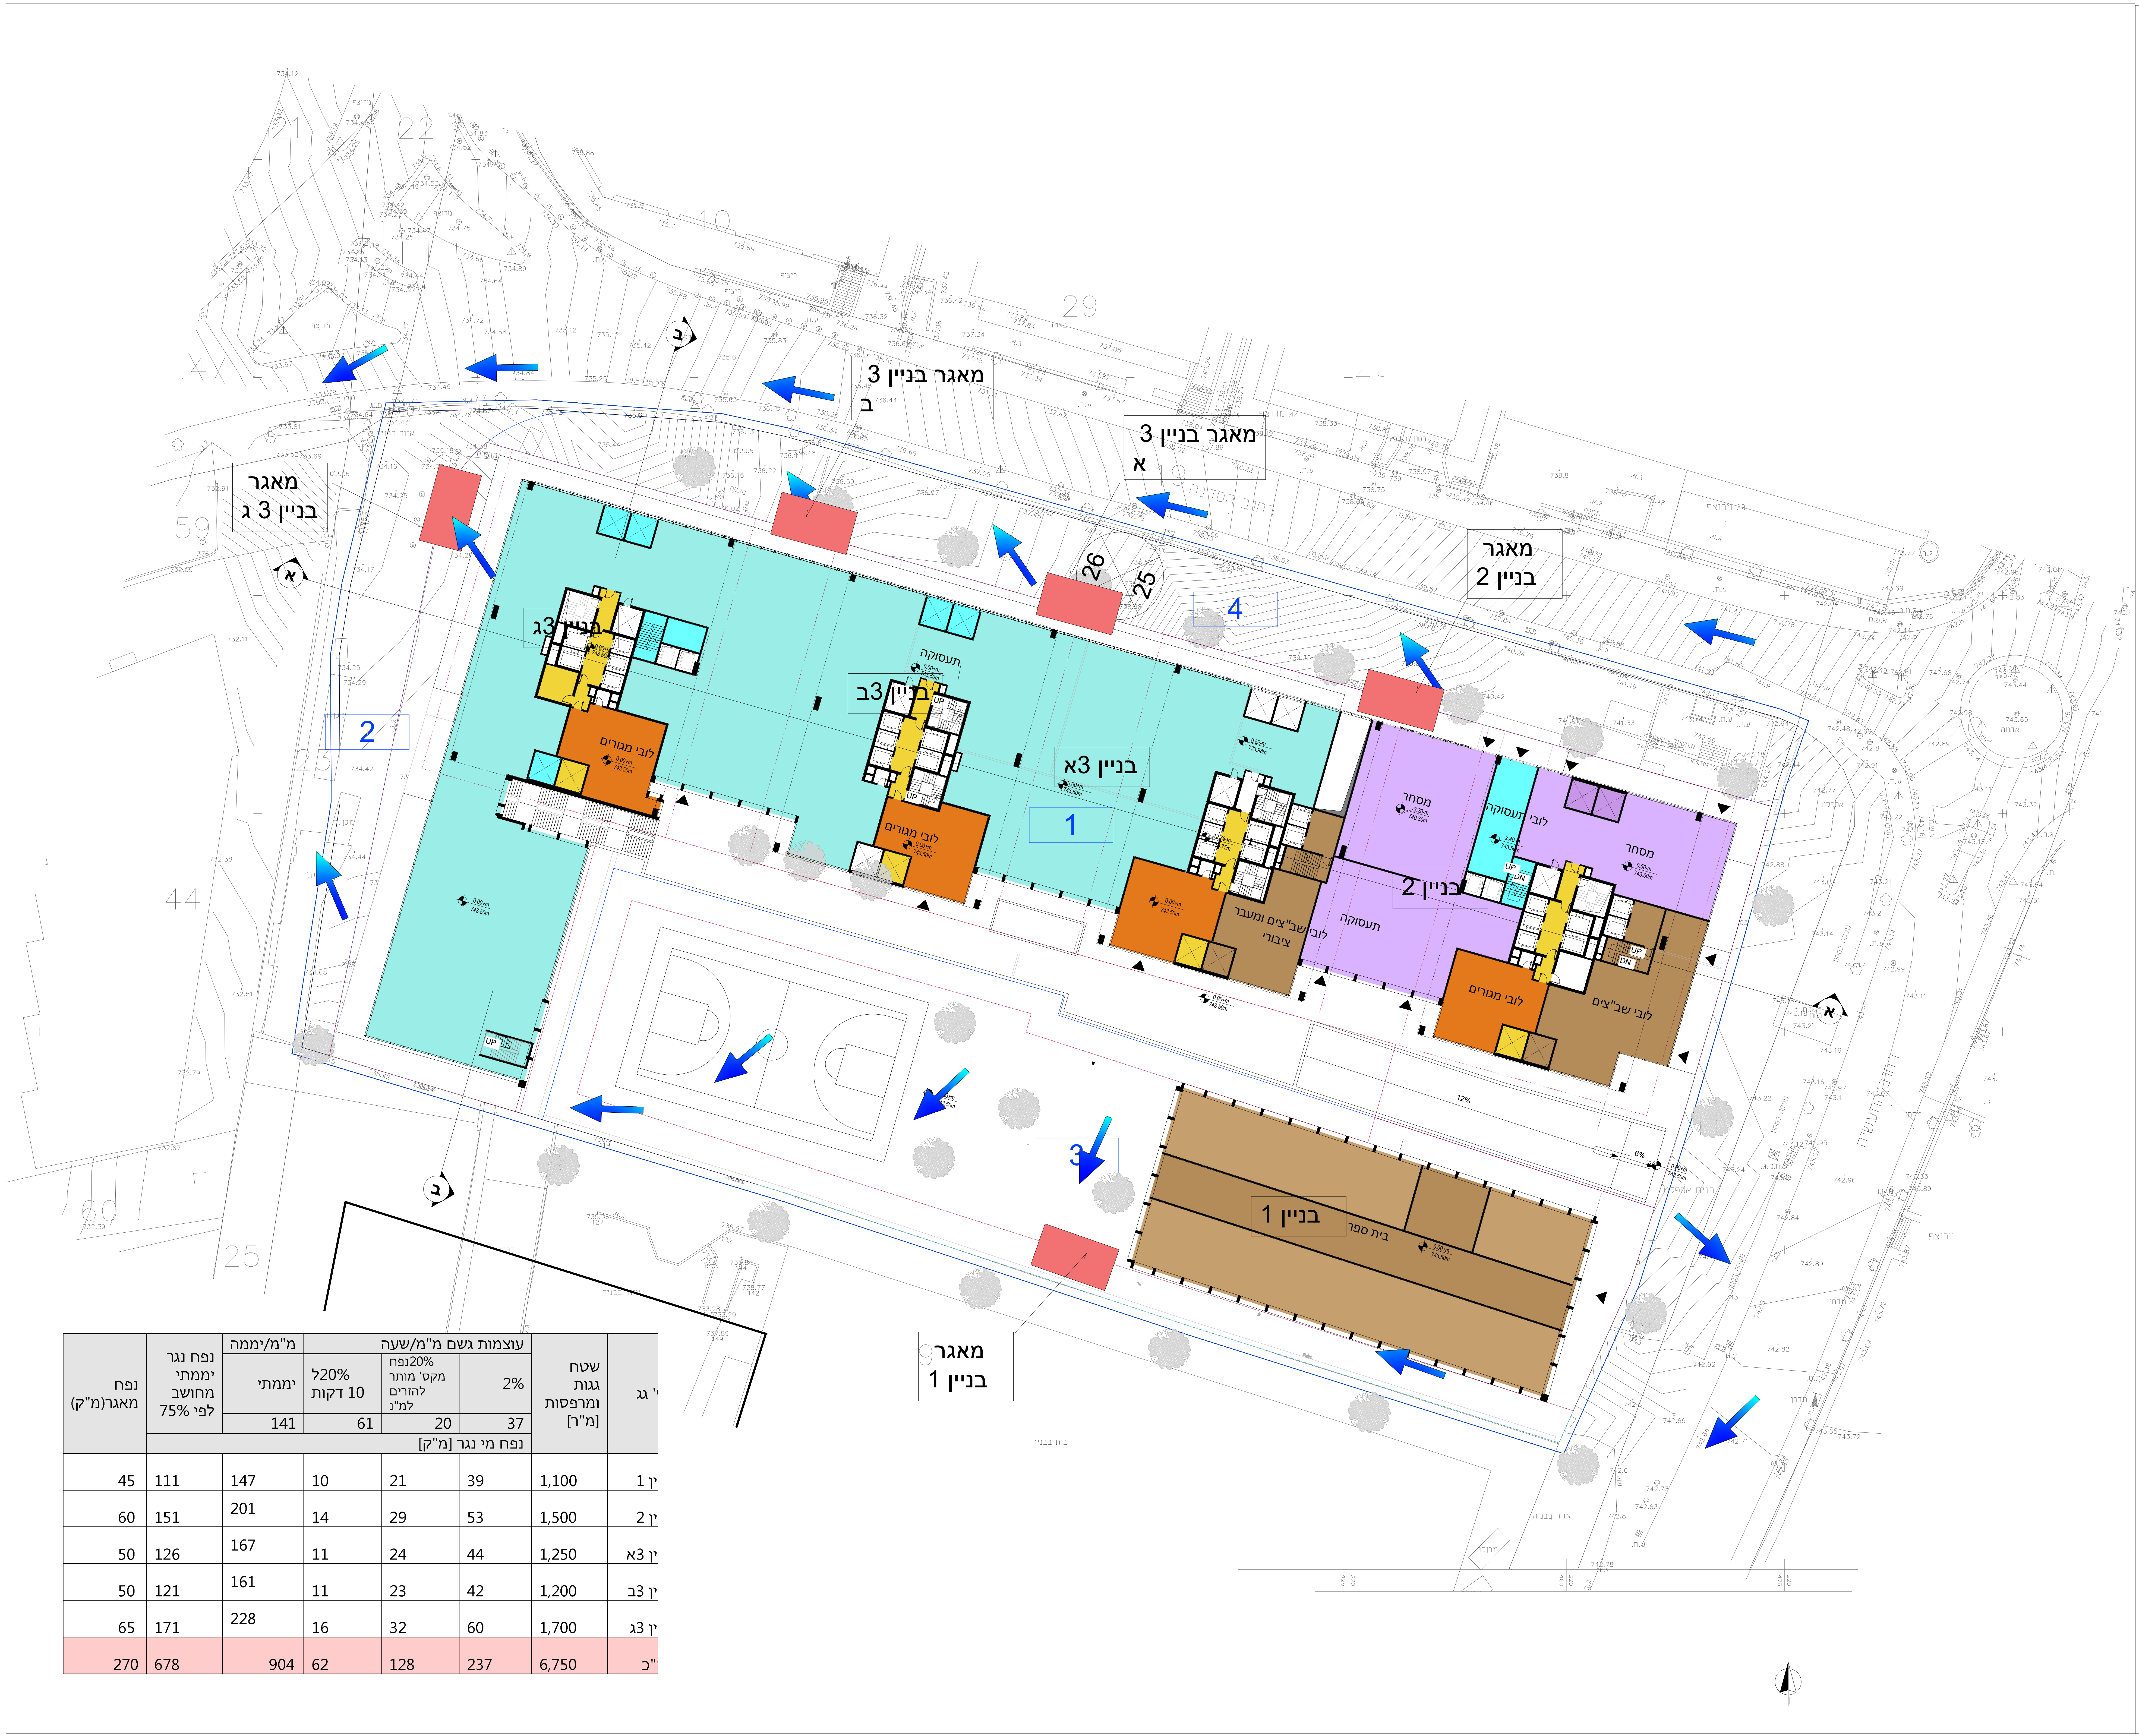
מאגר בניין 3 ב
מאגר בניין 3 א
מאגר בניין 3 ג
מאגר בניין 2
מאגר בניין 1
בניין 3ג
בניין 3ב
בניין 3א
בניין 2
בניין 1
תעסוקה
לובי מגורים
מסחר
לובי
לובי שב"צים
לובי שב"צים ומעבר ציבורי
בית ספר
1
2
3
4
א
ב
UP
DN
12%
6%

' גג	שטח גגות ומרפסות [מ"ר]	עוצמות גשם מ"מ/שעה			מ"מ/יממה	נפח נגר יממתי מחושב לפי 75%	נפח מאגר(מ"ק)
		2%	20%נפח מקס' מותר להזרים למ"נ	20%ל 10 דקות	יממתי		
		37	20	61	141		
		נפח מי נגר [מ"ק]					
ין 1	1,100	39	21	10	147	111	45
ין 2	1,500	53	29	14	201	151	60
ין 3א	1,250	44	24	11	167	126	50
ין 3ב	1,200	42	23	11	161	121	50
ין 3ג	1,700	60	32	16	228	171	65
"כ	6,750	237	128	62	904	678	270

מקרא

←	כיוון זרימה
▬	גבול מגרש
🟥	מאגר תת קרקעי

מרפיר פרויקטים
בית לחוות דעת הידרולוגיות