מינהל התכנון
חוק התכנון והבניה, התשכ"ה - 1965
מחוז ירושלים
הוועדה המחוזית החליטה ביום :
30/10/2023
להפקיד את התכנית
14/10/2026
תאריך יו"ר הוועדה המחוזית

תכנית 101-1095330 29/12/2025 16:16:47 נספח תנועה נספח תנועה

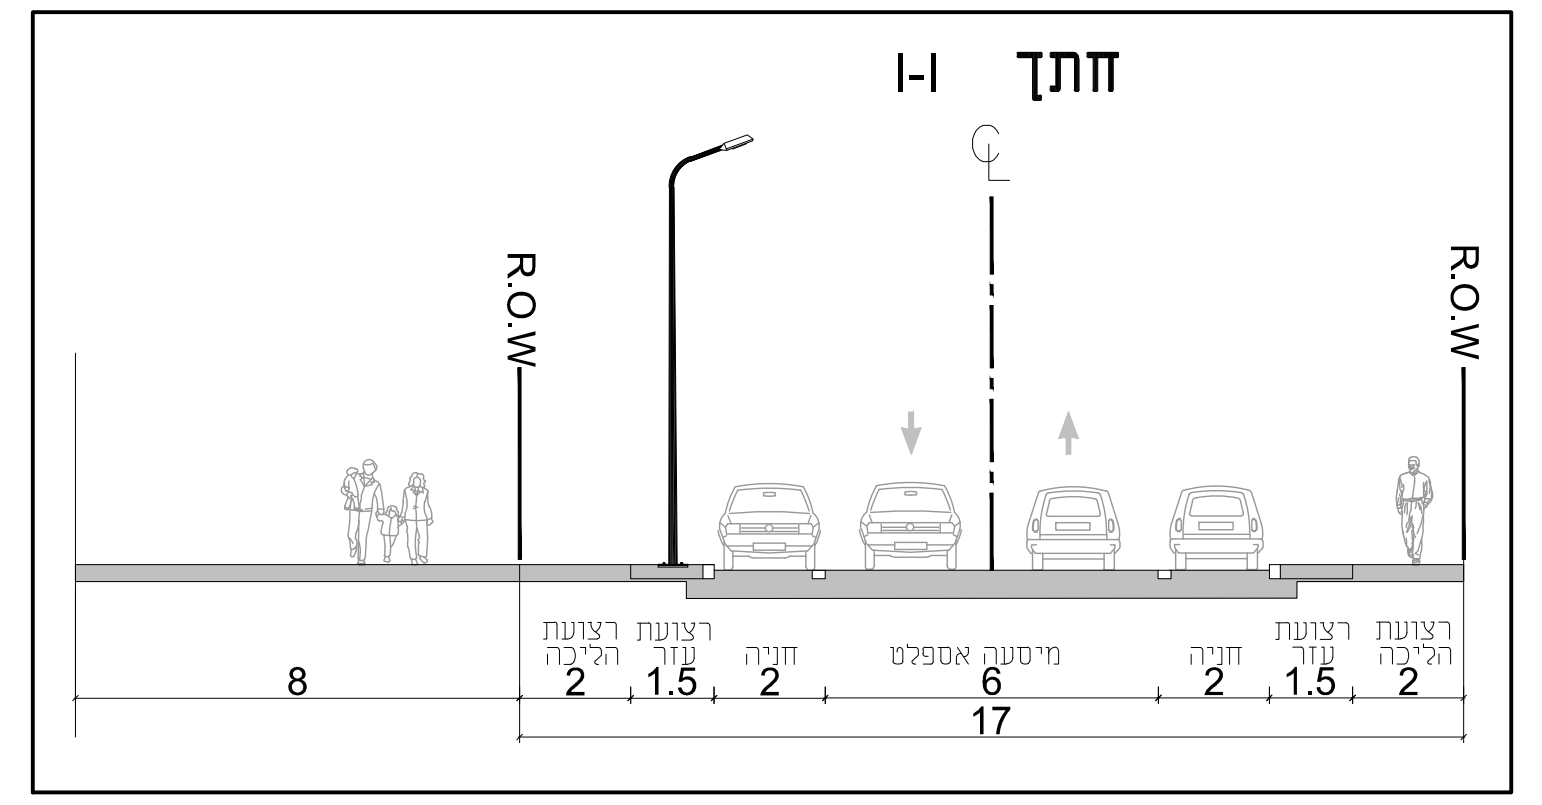

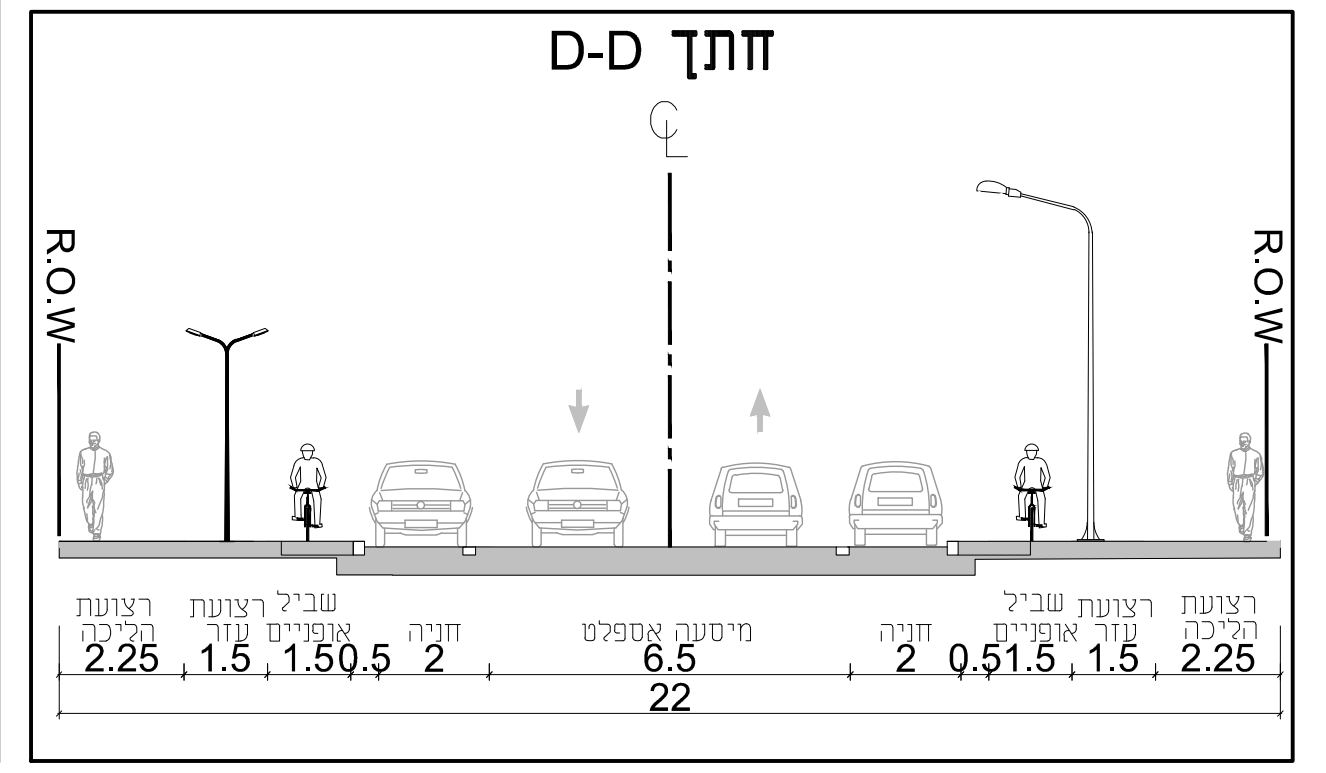

טבלת מאזן חניה לתכנית מס' 101-1095330 מתחם רג'ואן - הסדנא- פייר קינג
ע"פ הוראות תקן החניה של תכנית מס' 5166

דרישת חניה- אזור עתיר תח"צ

שימוש קרקע		תא שטח	יח"ד/ חדרים	שטח עיקרי	רכב פרטי		רכב תפעולי		אופנועים		אופניים	
			[יח']	[מ"ר]	תקן	תאי חניה	תקן	תאי חניה	תקן	תאי חניה	תקן	תאי חניה
מגורים	יחידות דיור עד 95 מ"ר	1	246		1: 1	246	-	-	1: 5-10	152-76	1: 1	636
	יחידות דיור מעל 95 מ"ר		390		1: 1	390	-	-				
	חניה לאורחים				כמות נדרשת 10 %	64						
סה"כ						700				152-76		636
תעסוקה (משרדים)		1	-	17500	1: 280	63	-	-	1: 200	88	1: 250	70
מסחר		1	-	2500	עד 2000 מ"ר: 1: 60 מ-2000 עד 10,000 מ"ר: 1: 100	38	עד 2000 מ"ר: 1: 500 (1000 מ"ר) 1: 1,000	5	1: 200	13	1: 300	8
מוסדות ציבור	אשכול מעונות יום. 3 כיתות+ חצר צמודה לכל כיתה(305 מ"ר)	1	3	441	1לכל כיתה+ מפרץ הורד	3			ל-100 מ"ר	4	ל 10 תלמידים	9
	גני ילדים. 4 כיתות+ חצר צמודה לכל כיתה (175 מ"ר)		4	305	1לכל כיתה+ מפרץ הורד	4			ל-100 מ"ר	3	ל 10 תלמידים	12
	שני בתיי כנסת			800	1לכל 50 מ"ר	16			ל-100 מ"ר	8	ל-500 מ"ר	1
	מתנ"ס			450	1לכל 50מ"ר ובנוסף 1לכל 10מ"ר אולם כינוסים	9			ל-100 מ"ר	5	ל-100 מ"ר	3
	תחנת לבריאות משפחה			300	2לכל חדר או 1 לכל 20 מ"ר	15			ל-100 מ"ר	3	ל-300 מ"ר	1
	מרכז לגיל רך			984	2לכל חדר או 1 לכל 20 מ"ר	49			ל-100 מ"ר	10	ל-500 מ"ר	1
						190		5		133		105
סה"כ						890				265-198		741

היצע חניה

	חניה פרטית	חניה נגישה	רכב תפעולי	אופנועים	אופניים
סה"כ מוצע	890	6 לרכב גבוה 12 לרכב רגיל	5	205	105 1

1. 636 חניות אופניים ממוקמות במחסני דירות מגורים

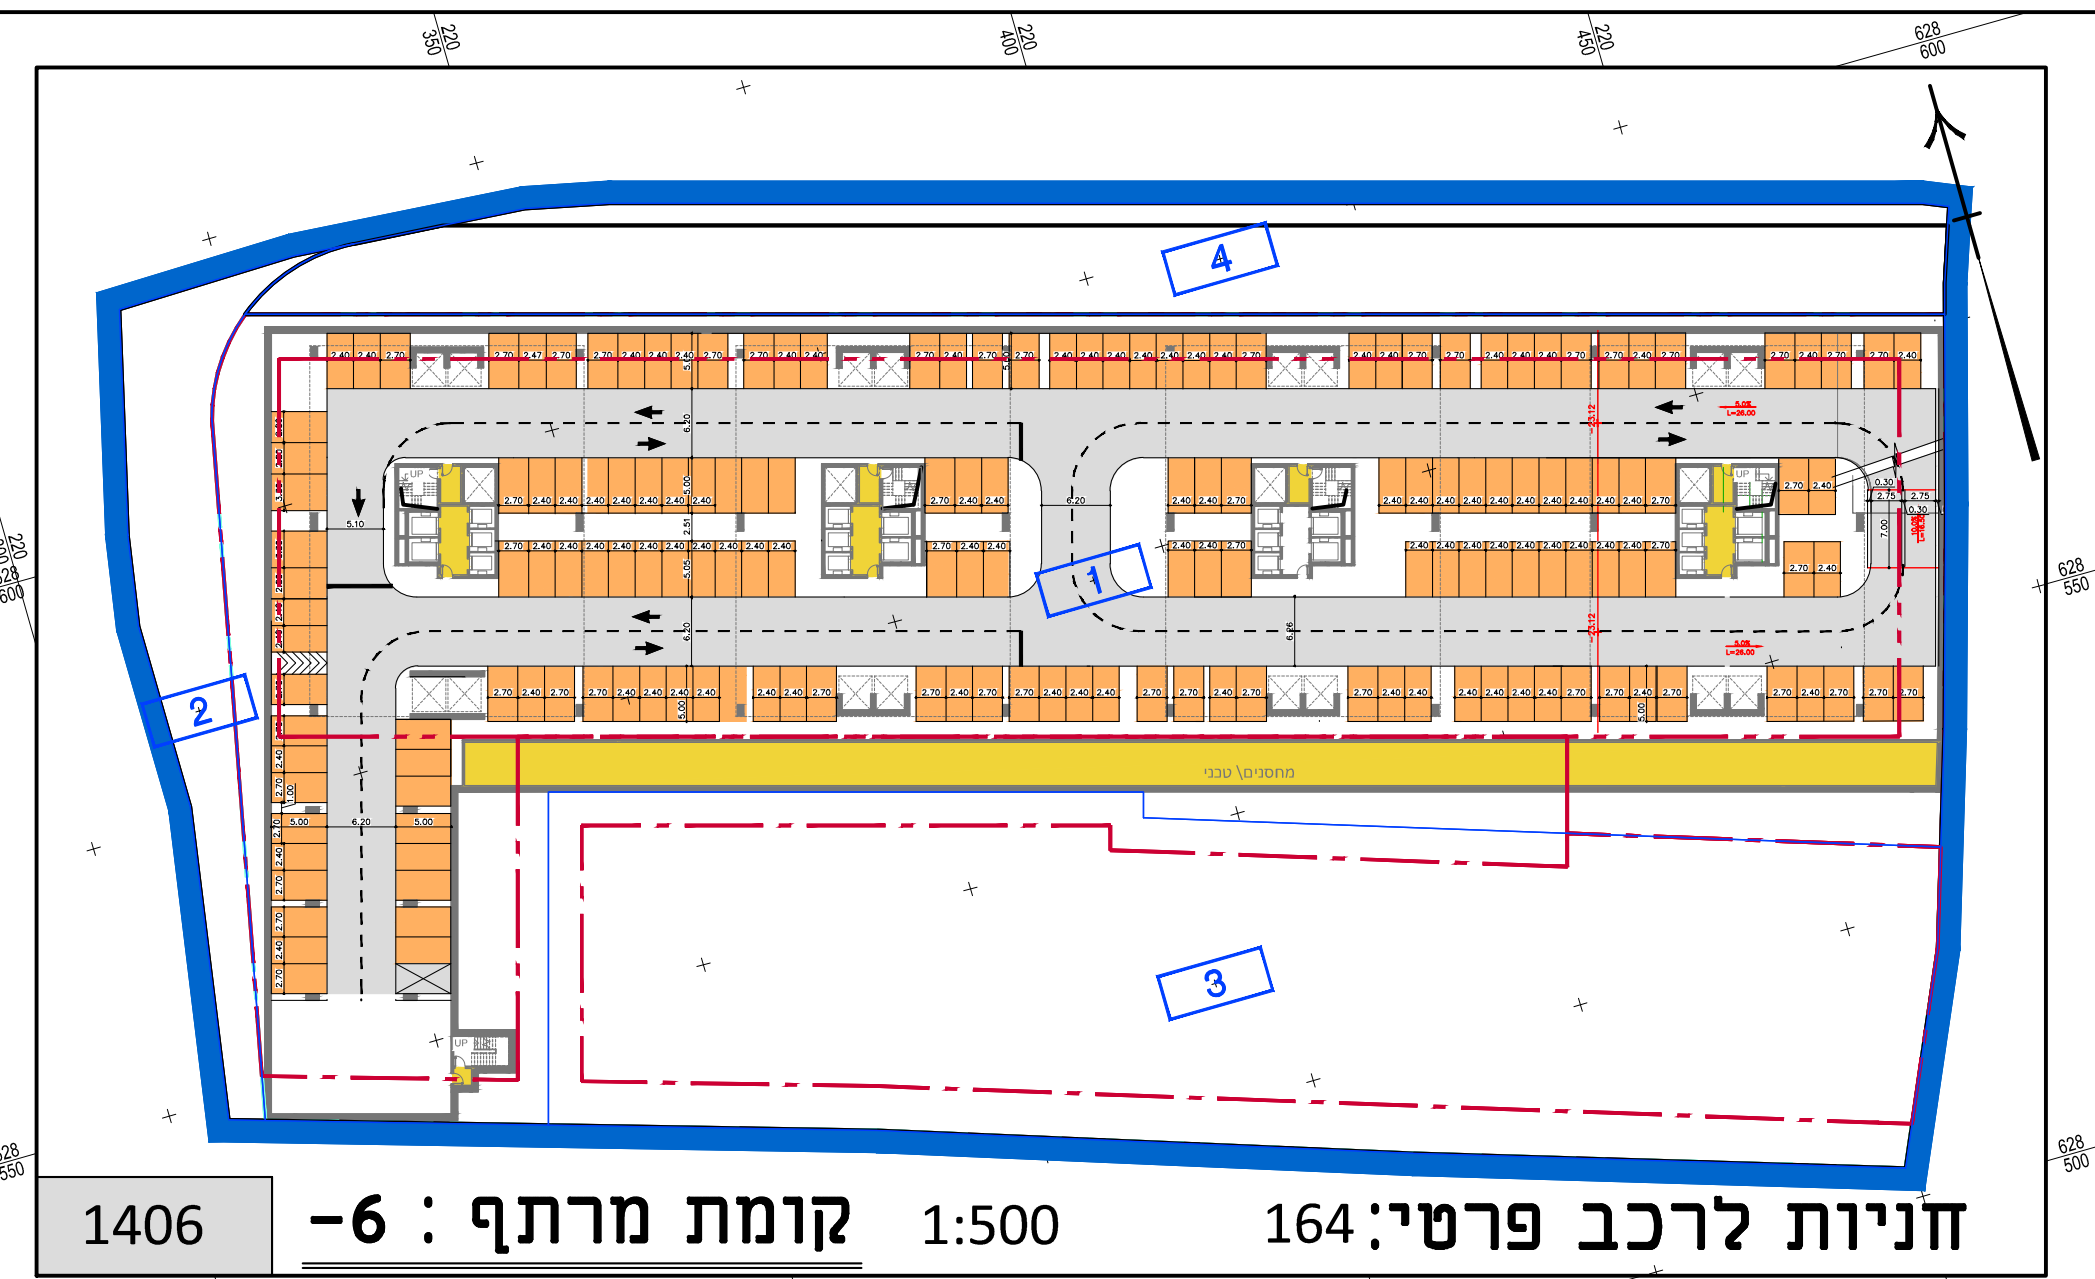

1406 קומת מרתף : -6 1:500 חניות לרכב פרטי: 164

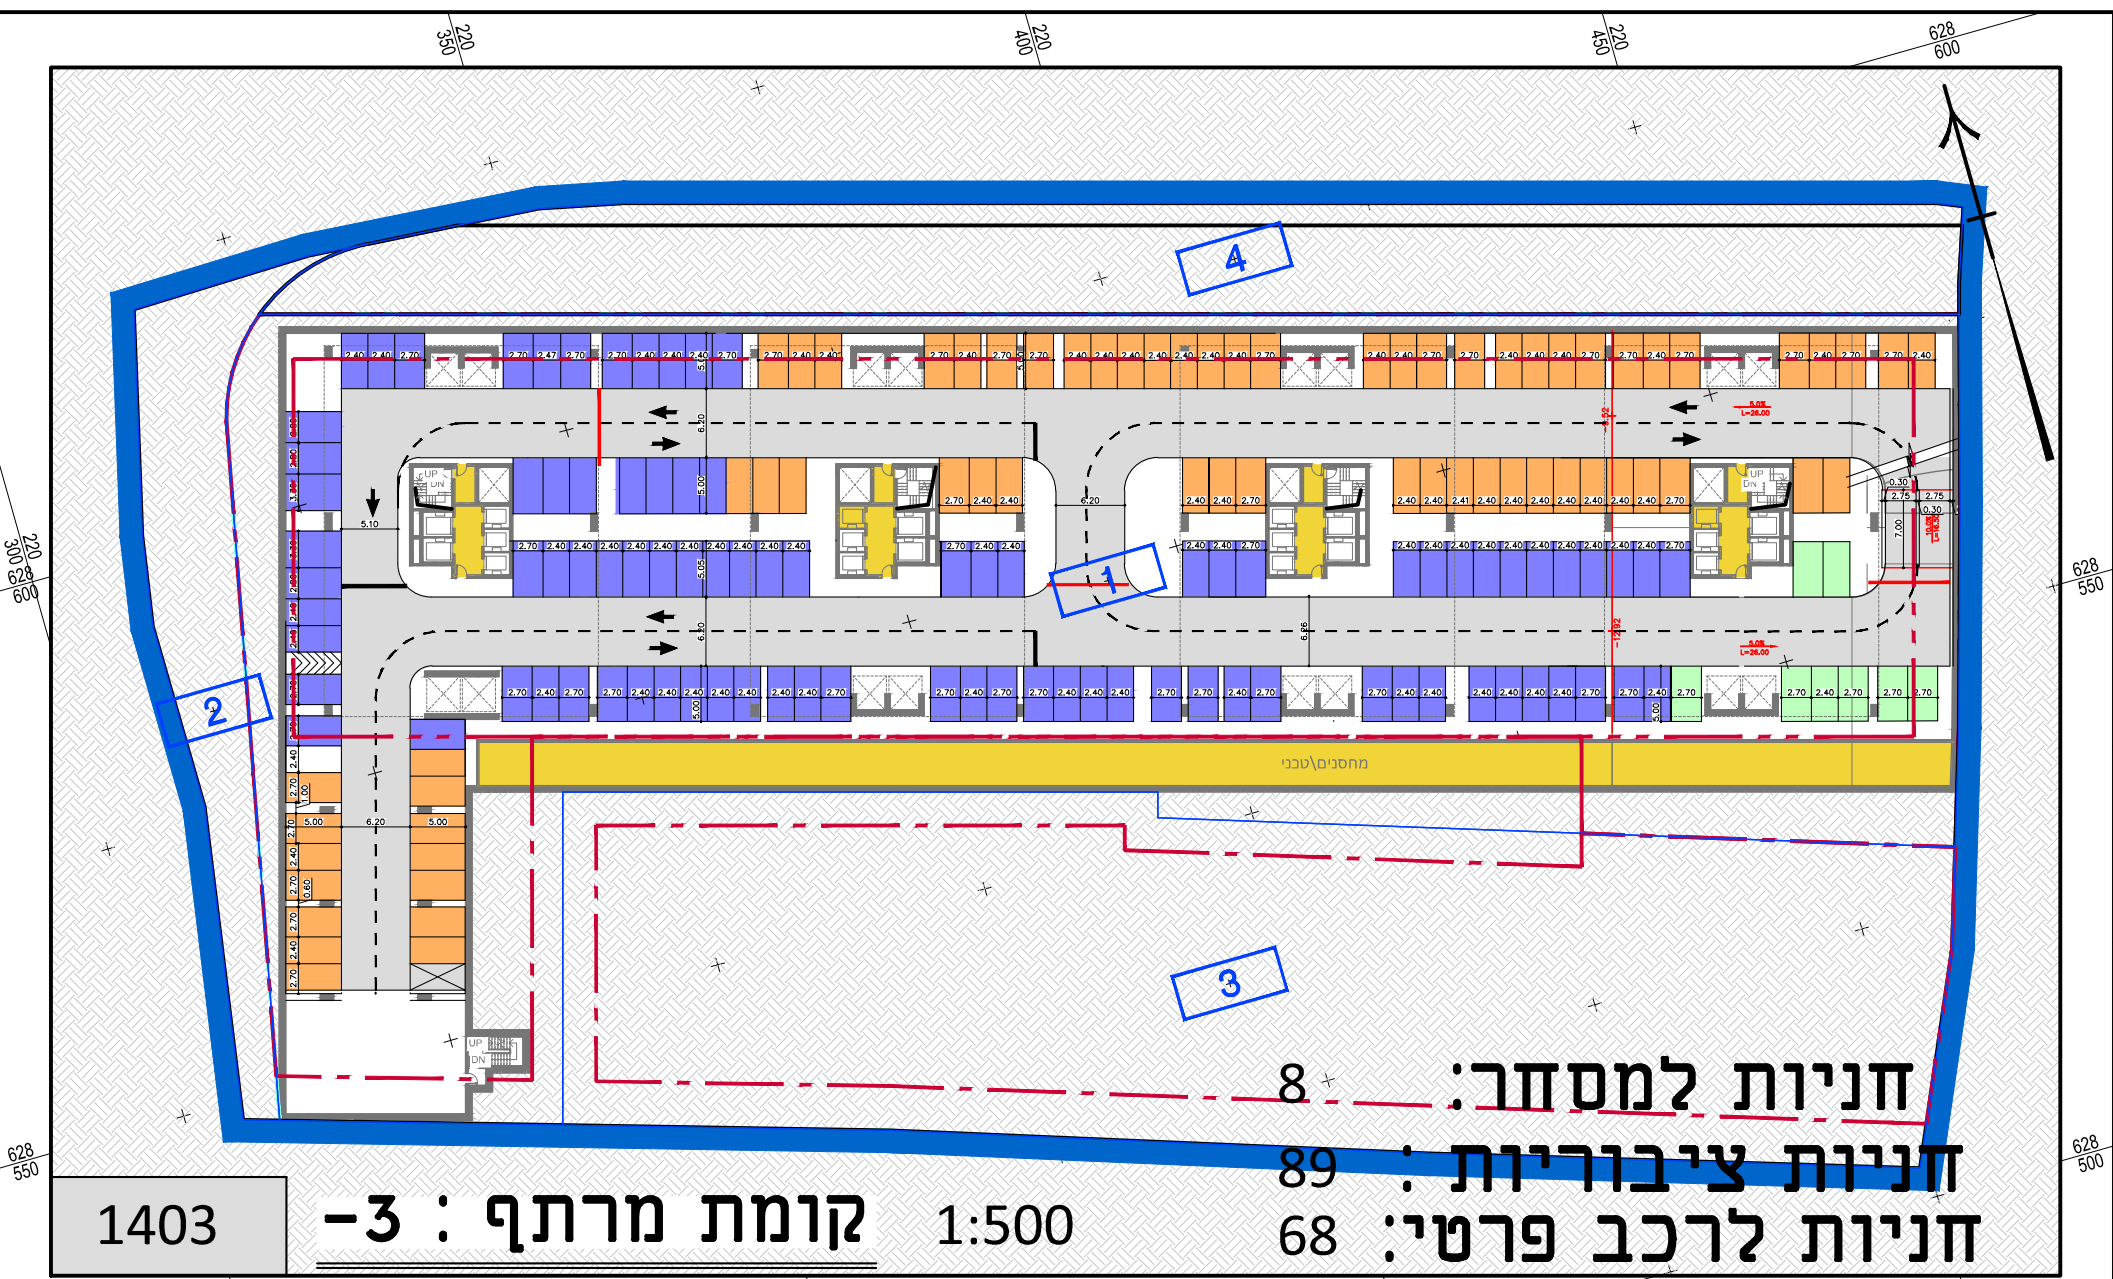

חניות למסחר: 8
חניות ציבוריות : 89
חניות לרכב פרטי: 68
1403 קומת מרתף : -3 1:500

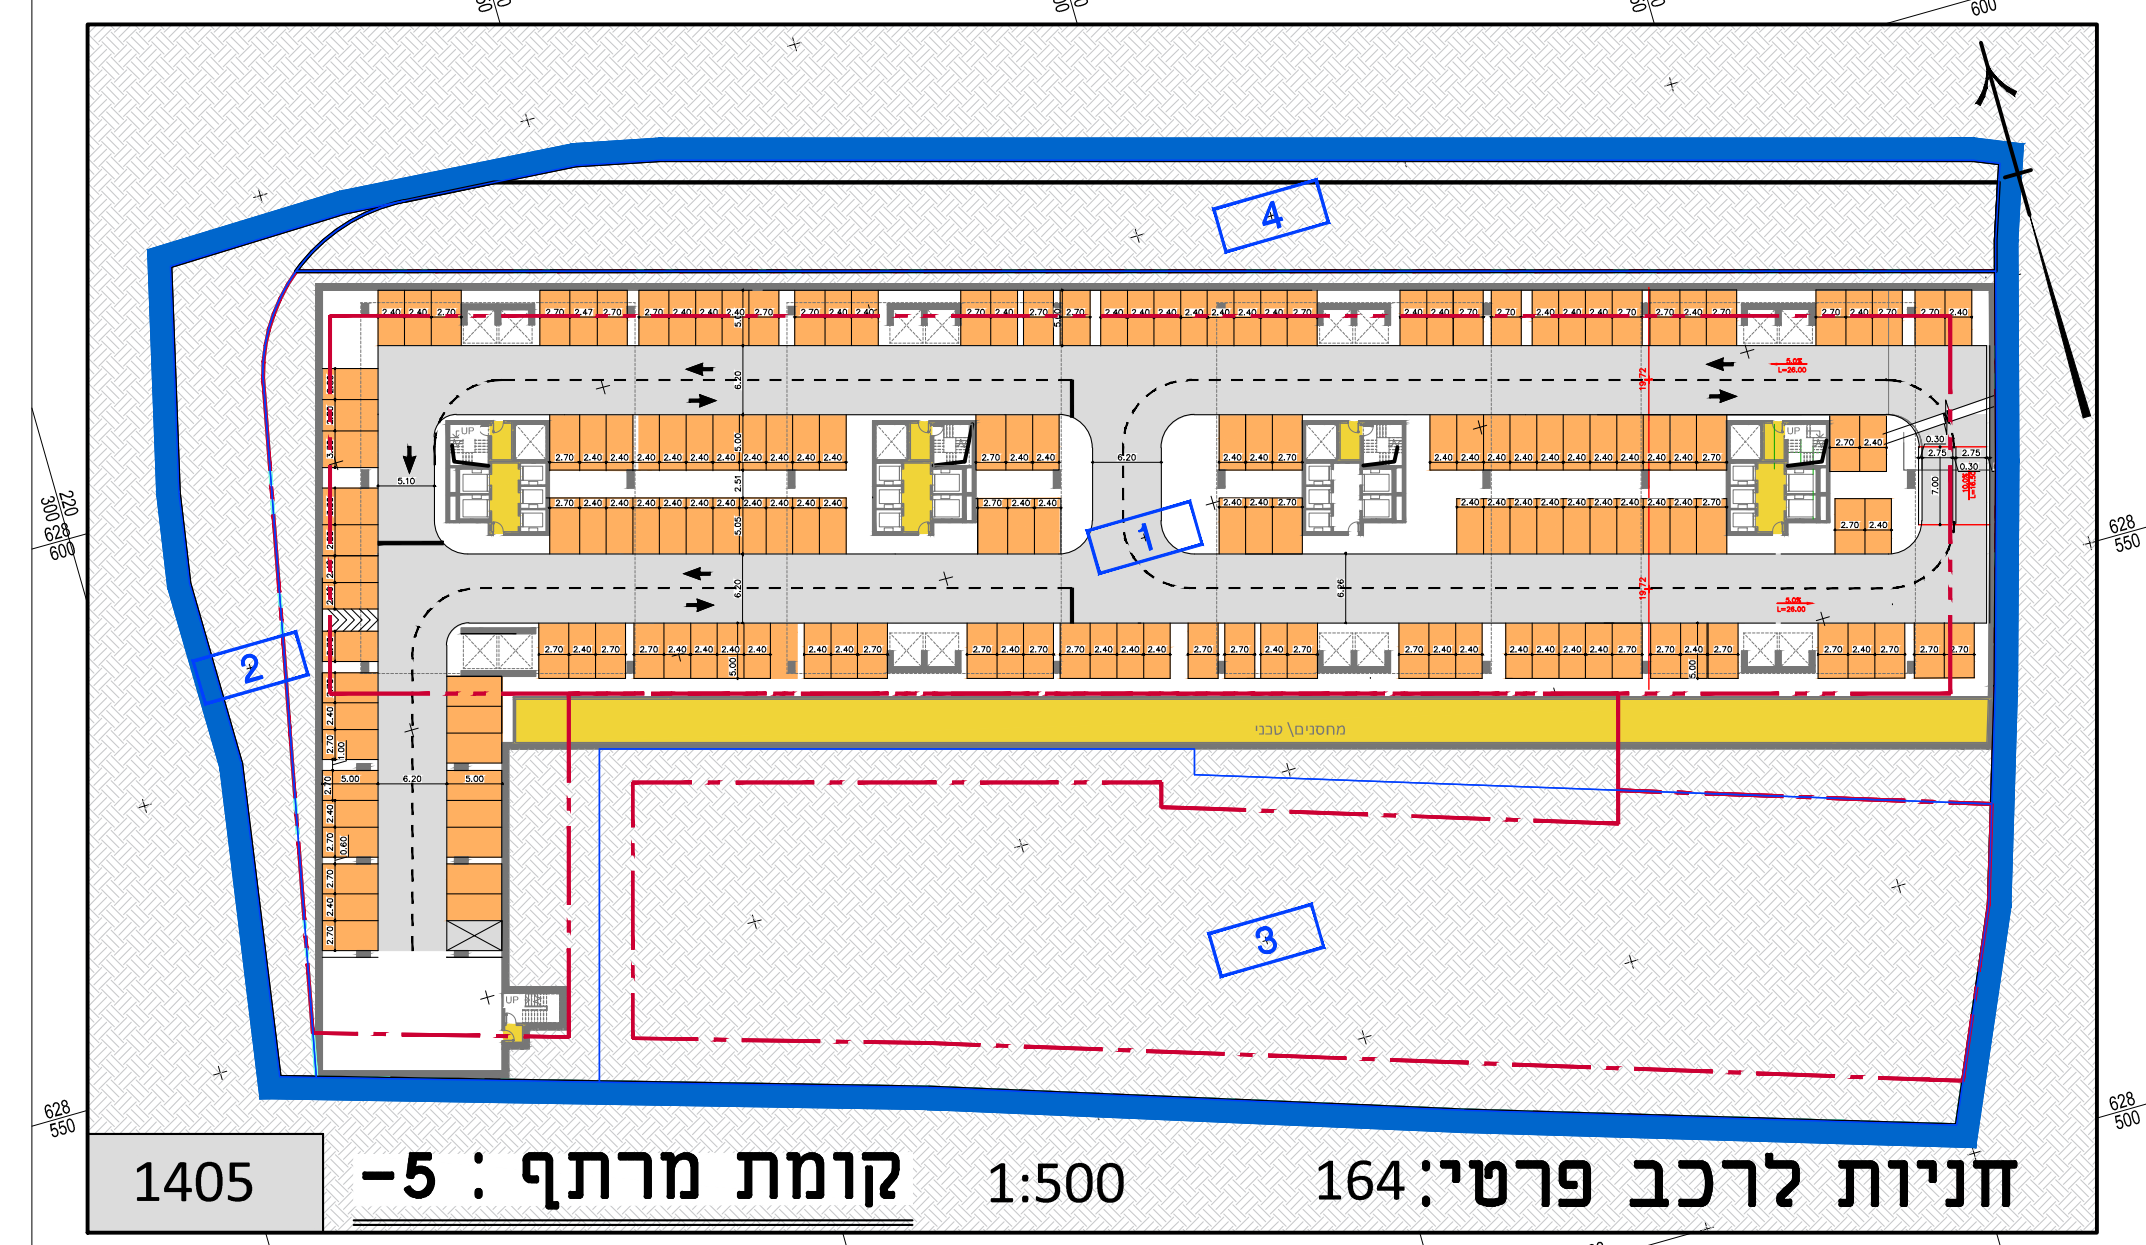

1405 קומת מרתף : -5 1:500 חניות לרכב פרטי: 164

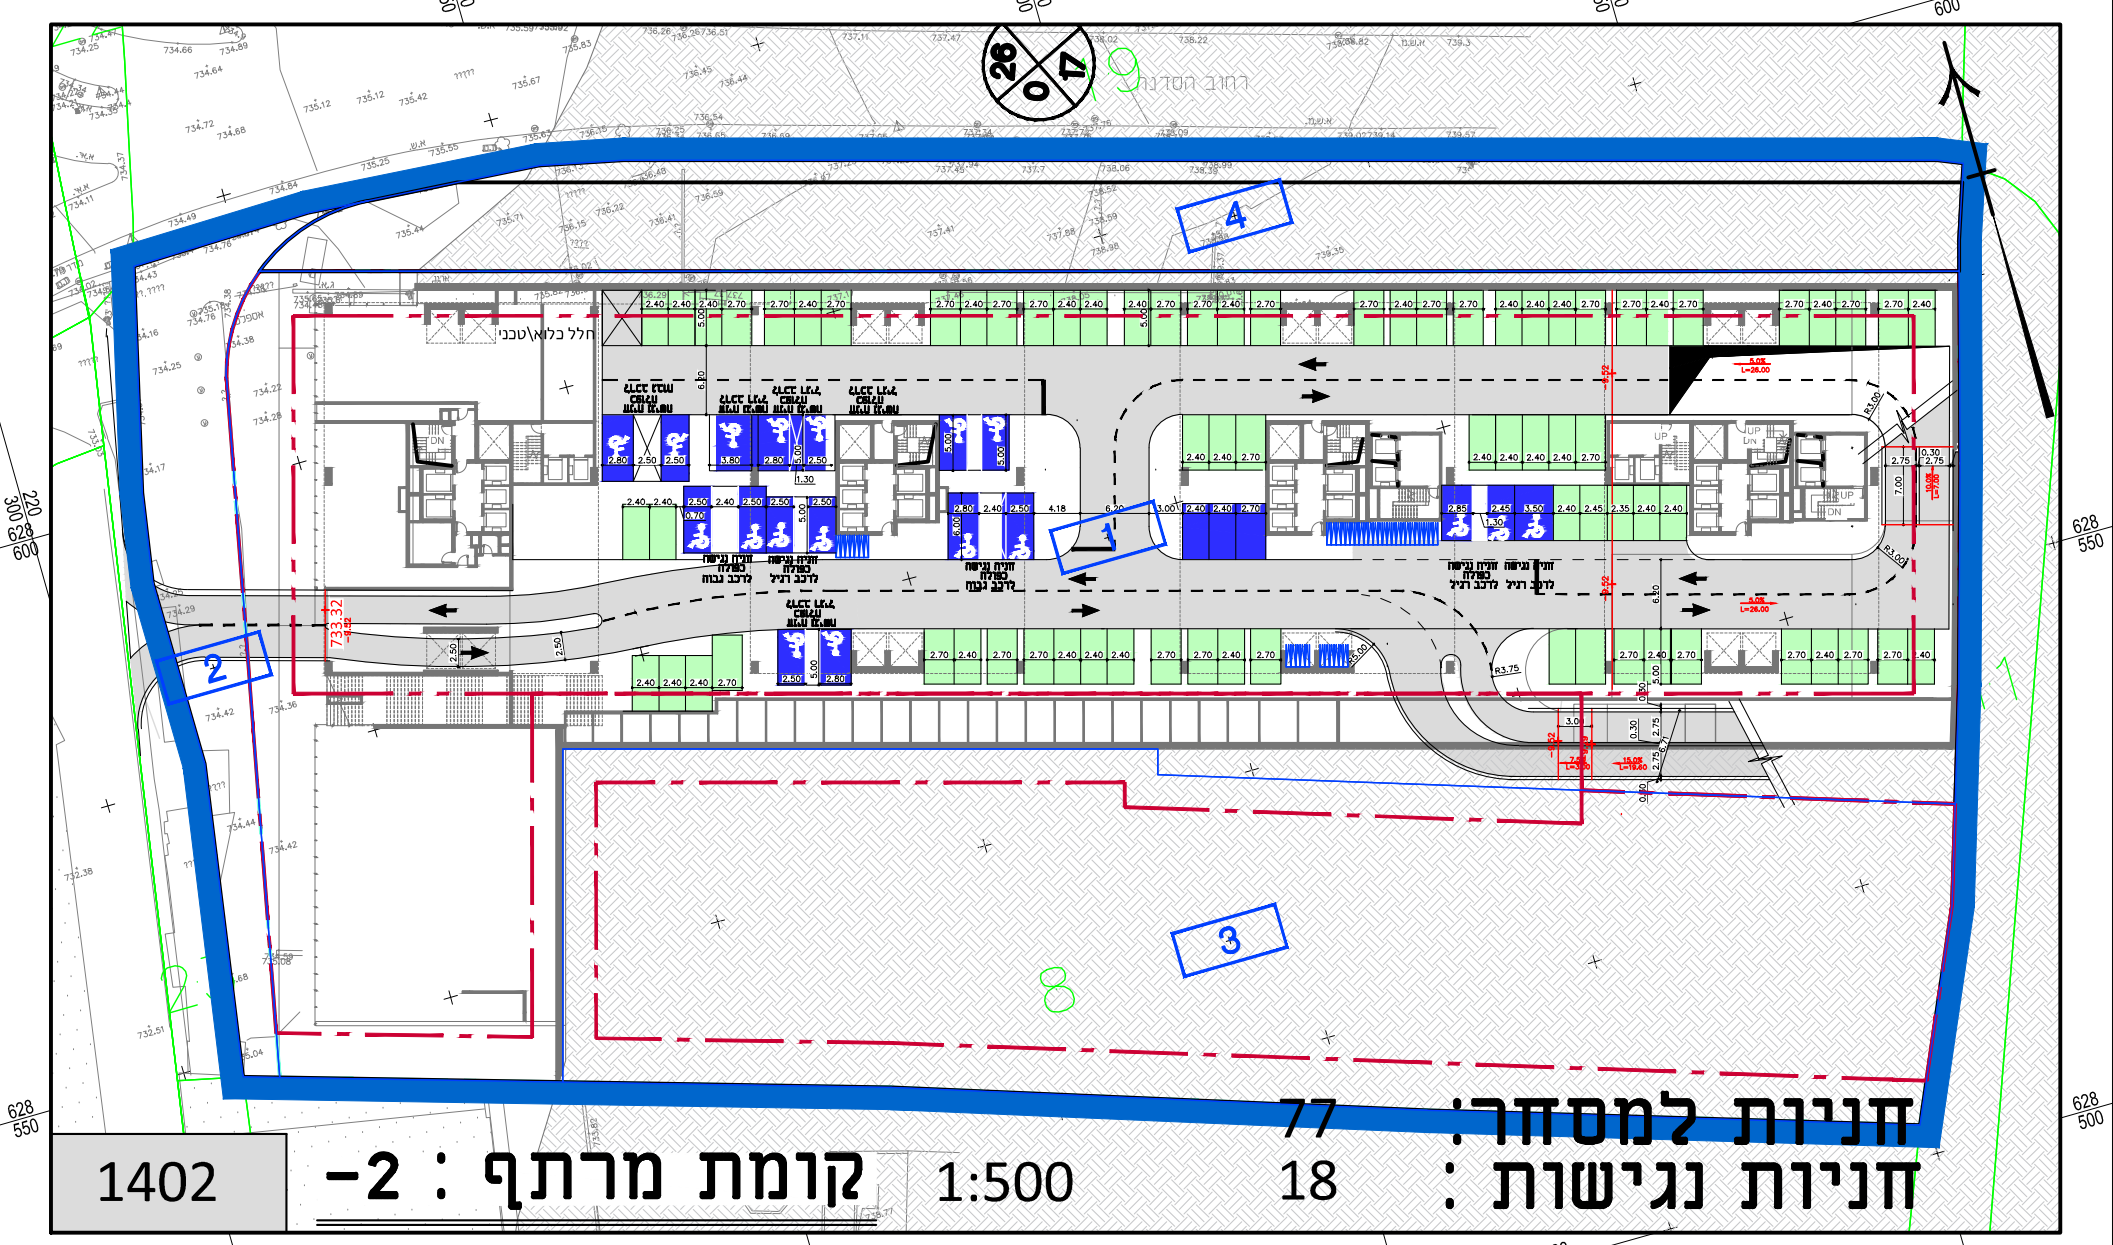

חניות למסחר: 77
חניות נגישות : 18
1402 קומת מרתף : -2 1:500

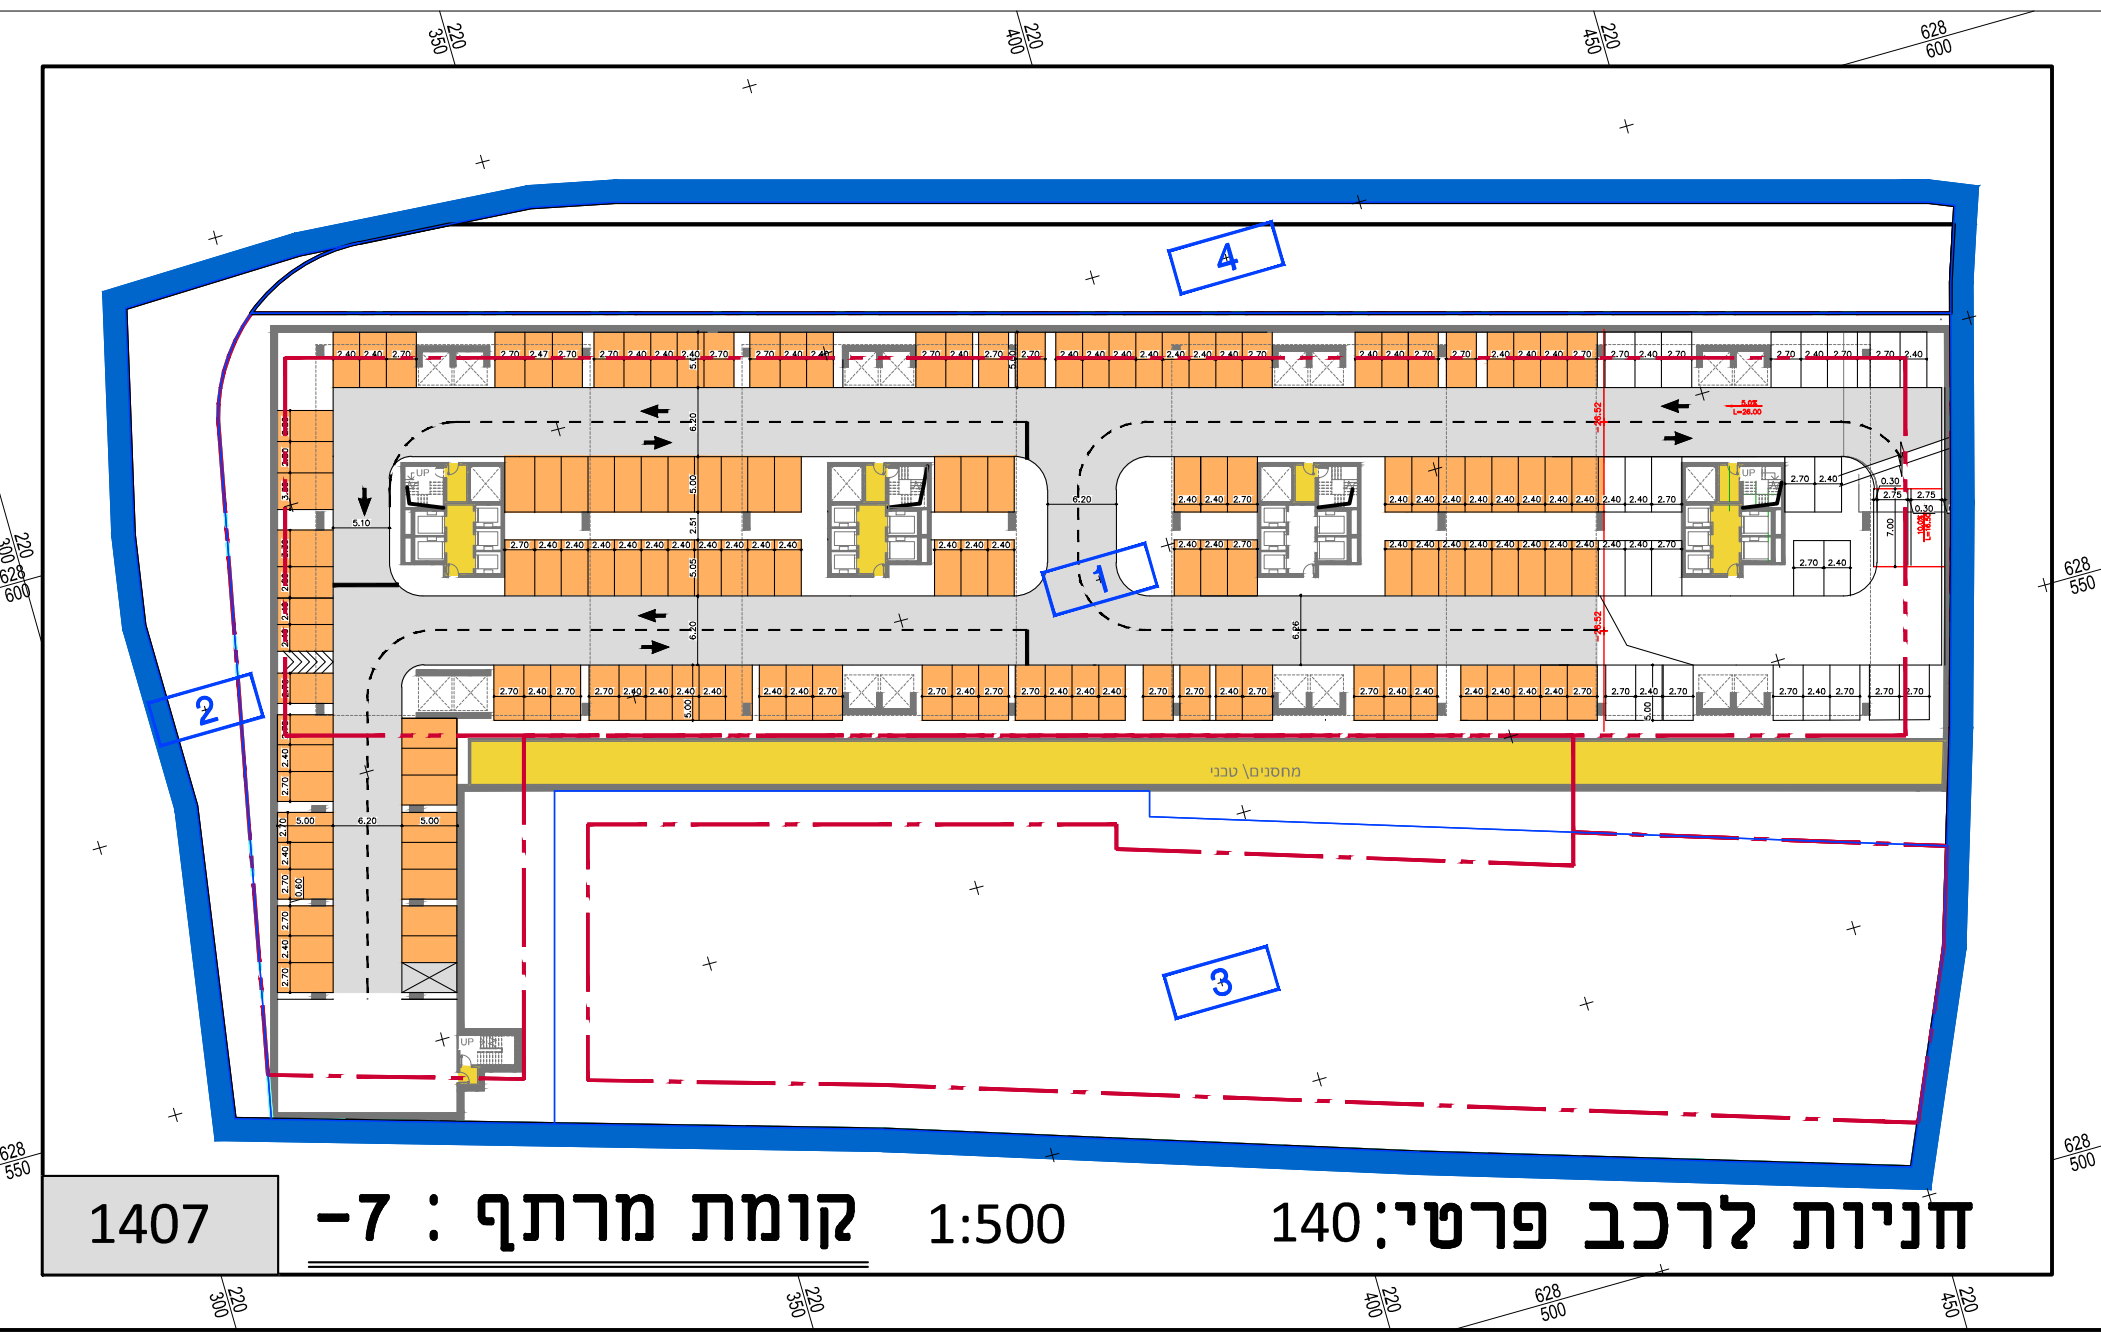

1407 קומת מרתף : -7 1:500 חניות לרכב פרטי: 140

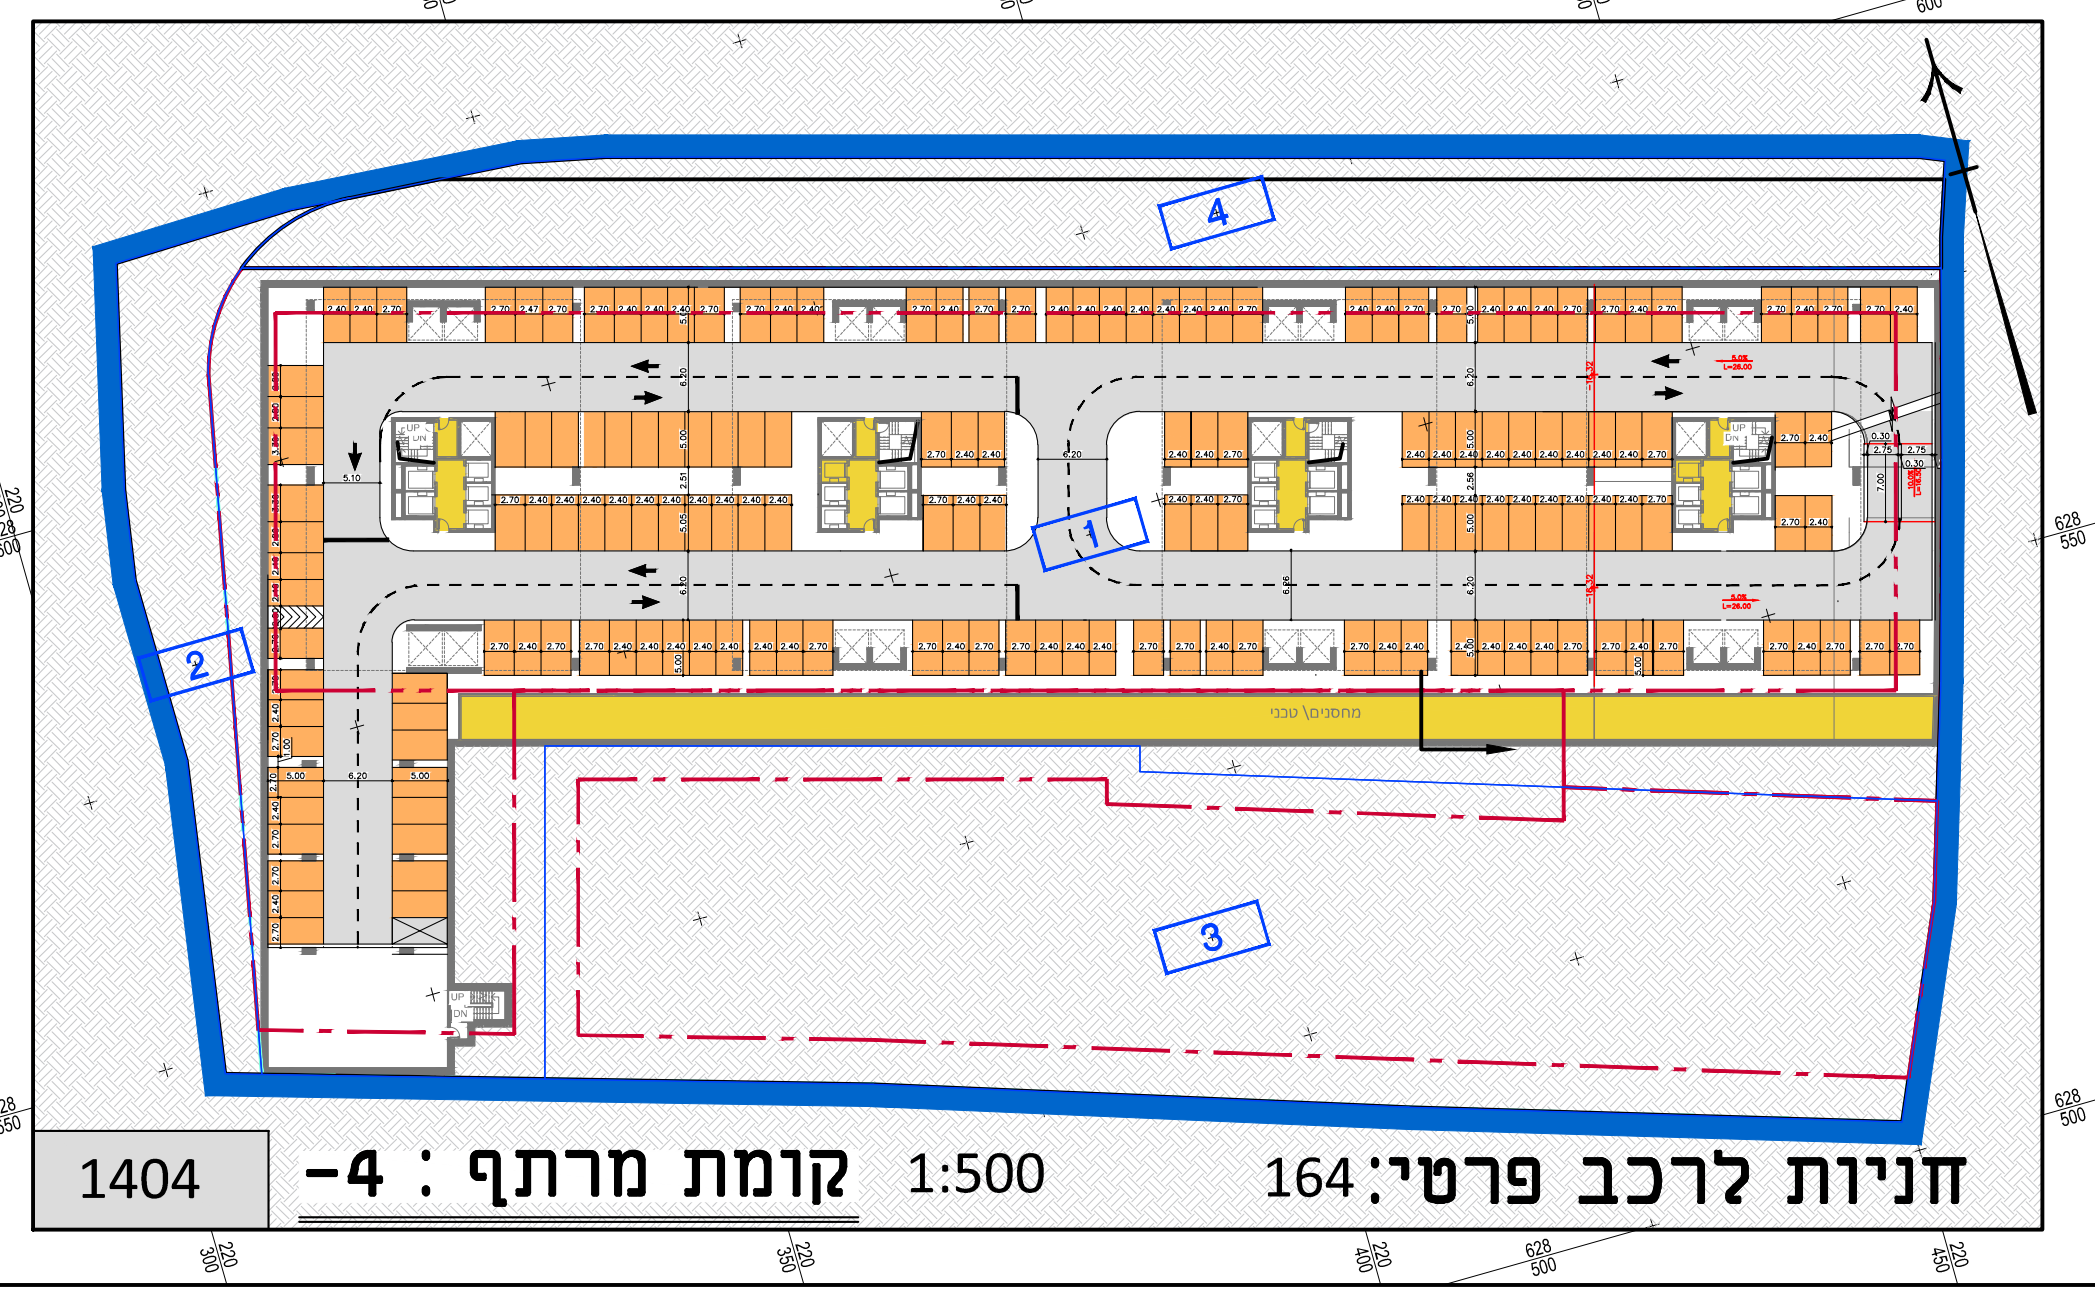

1404 קומת מרתף : -4 1:500 חניות לרכב פרטי: 164

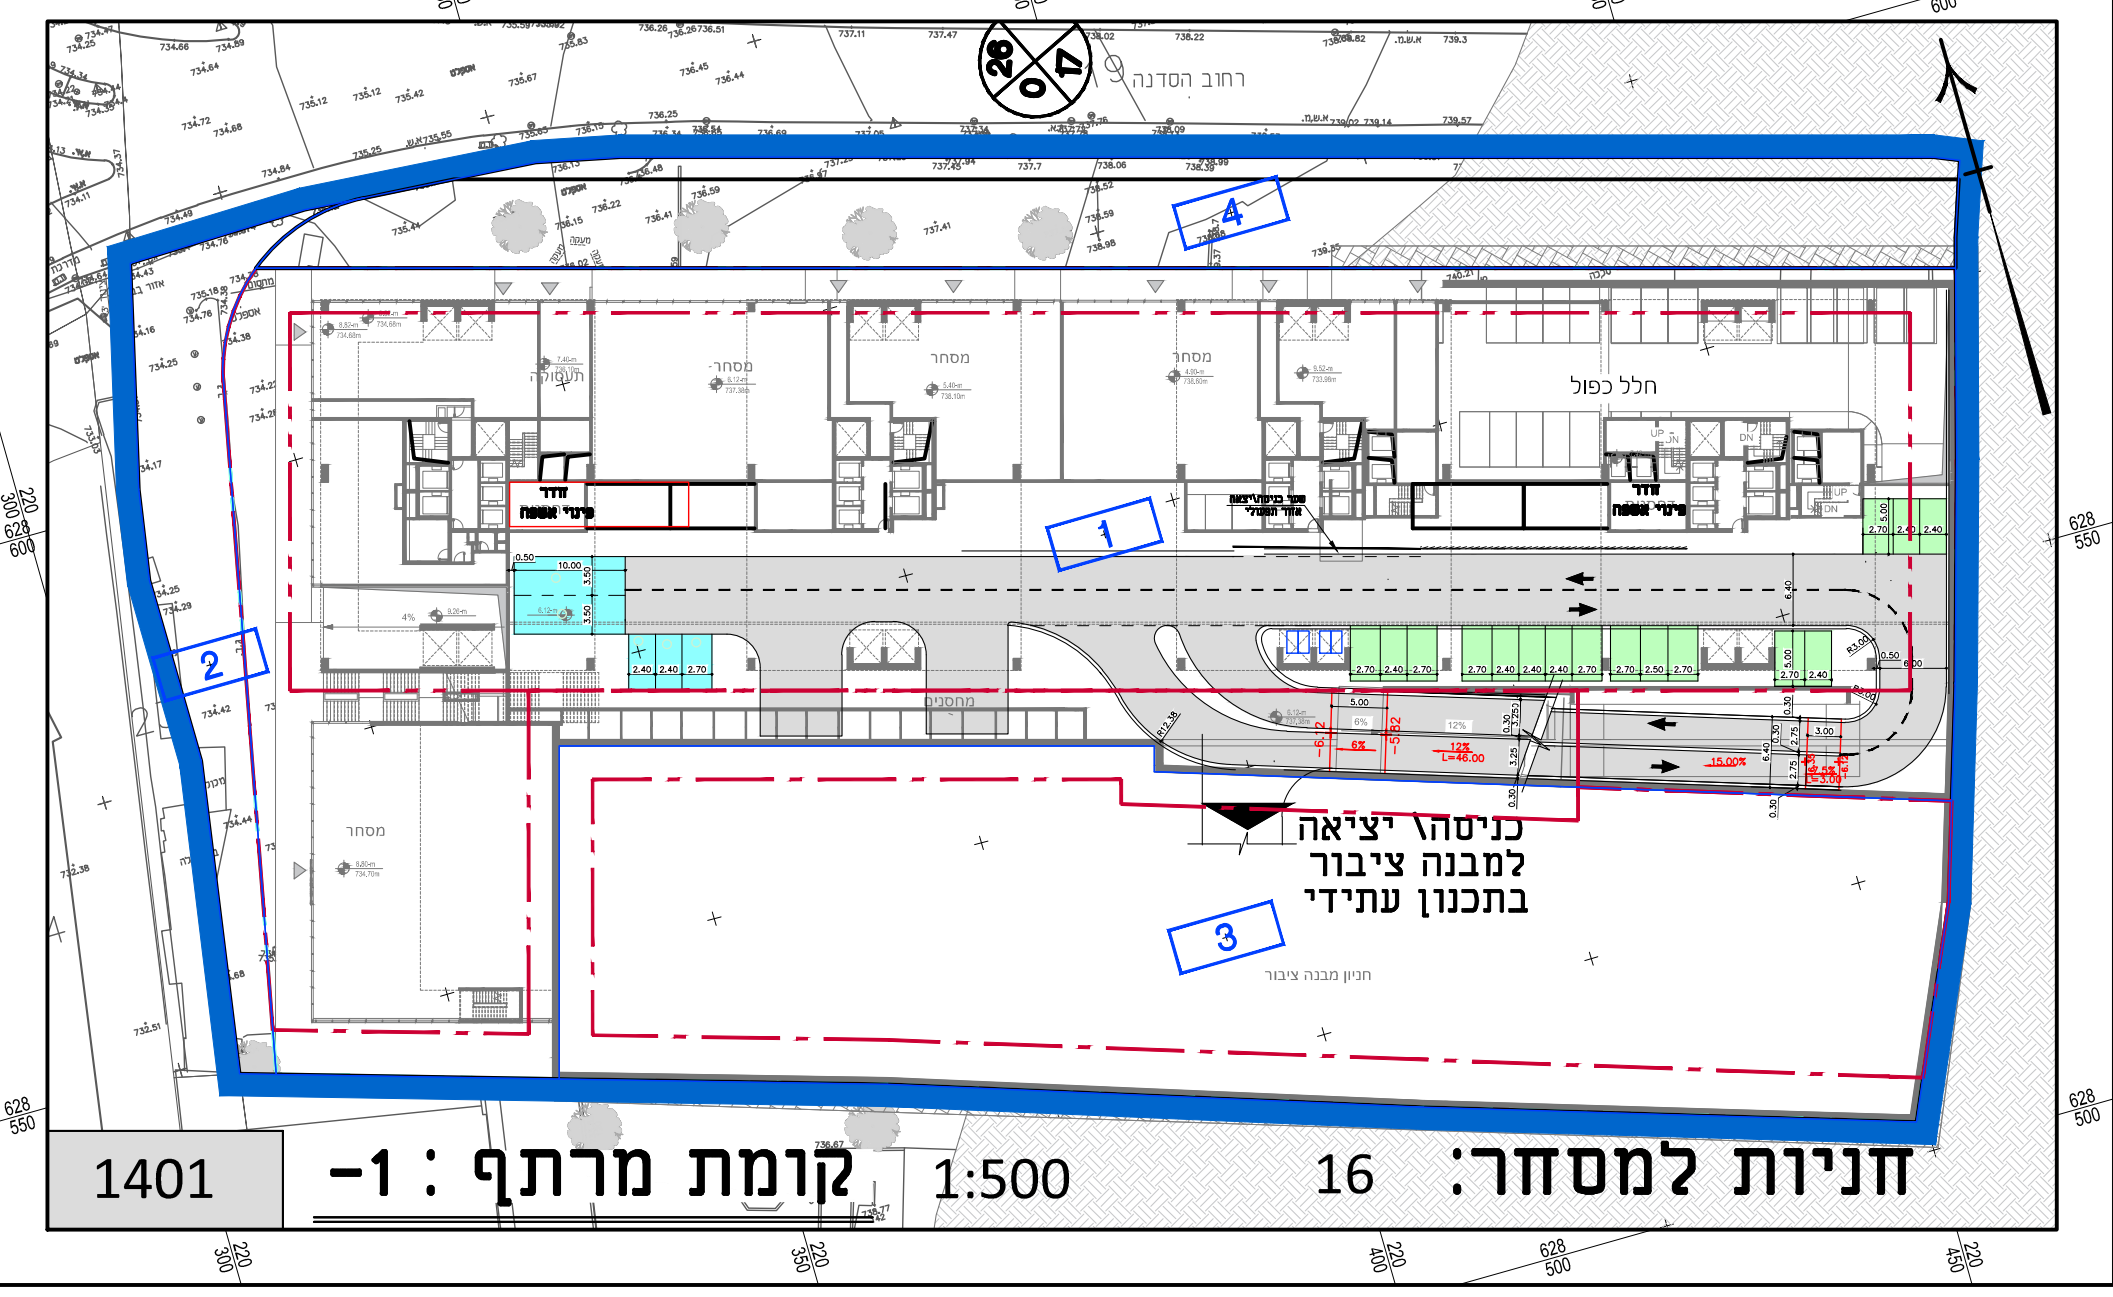

כניסה\ יציאה
למבנה ציבור
בתכנון עתידי

1401 קומת מרתף : -1 1:500 חניות למסחר: 16

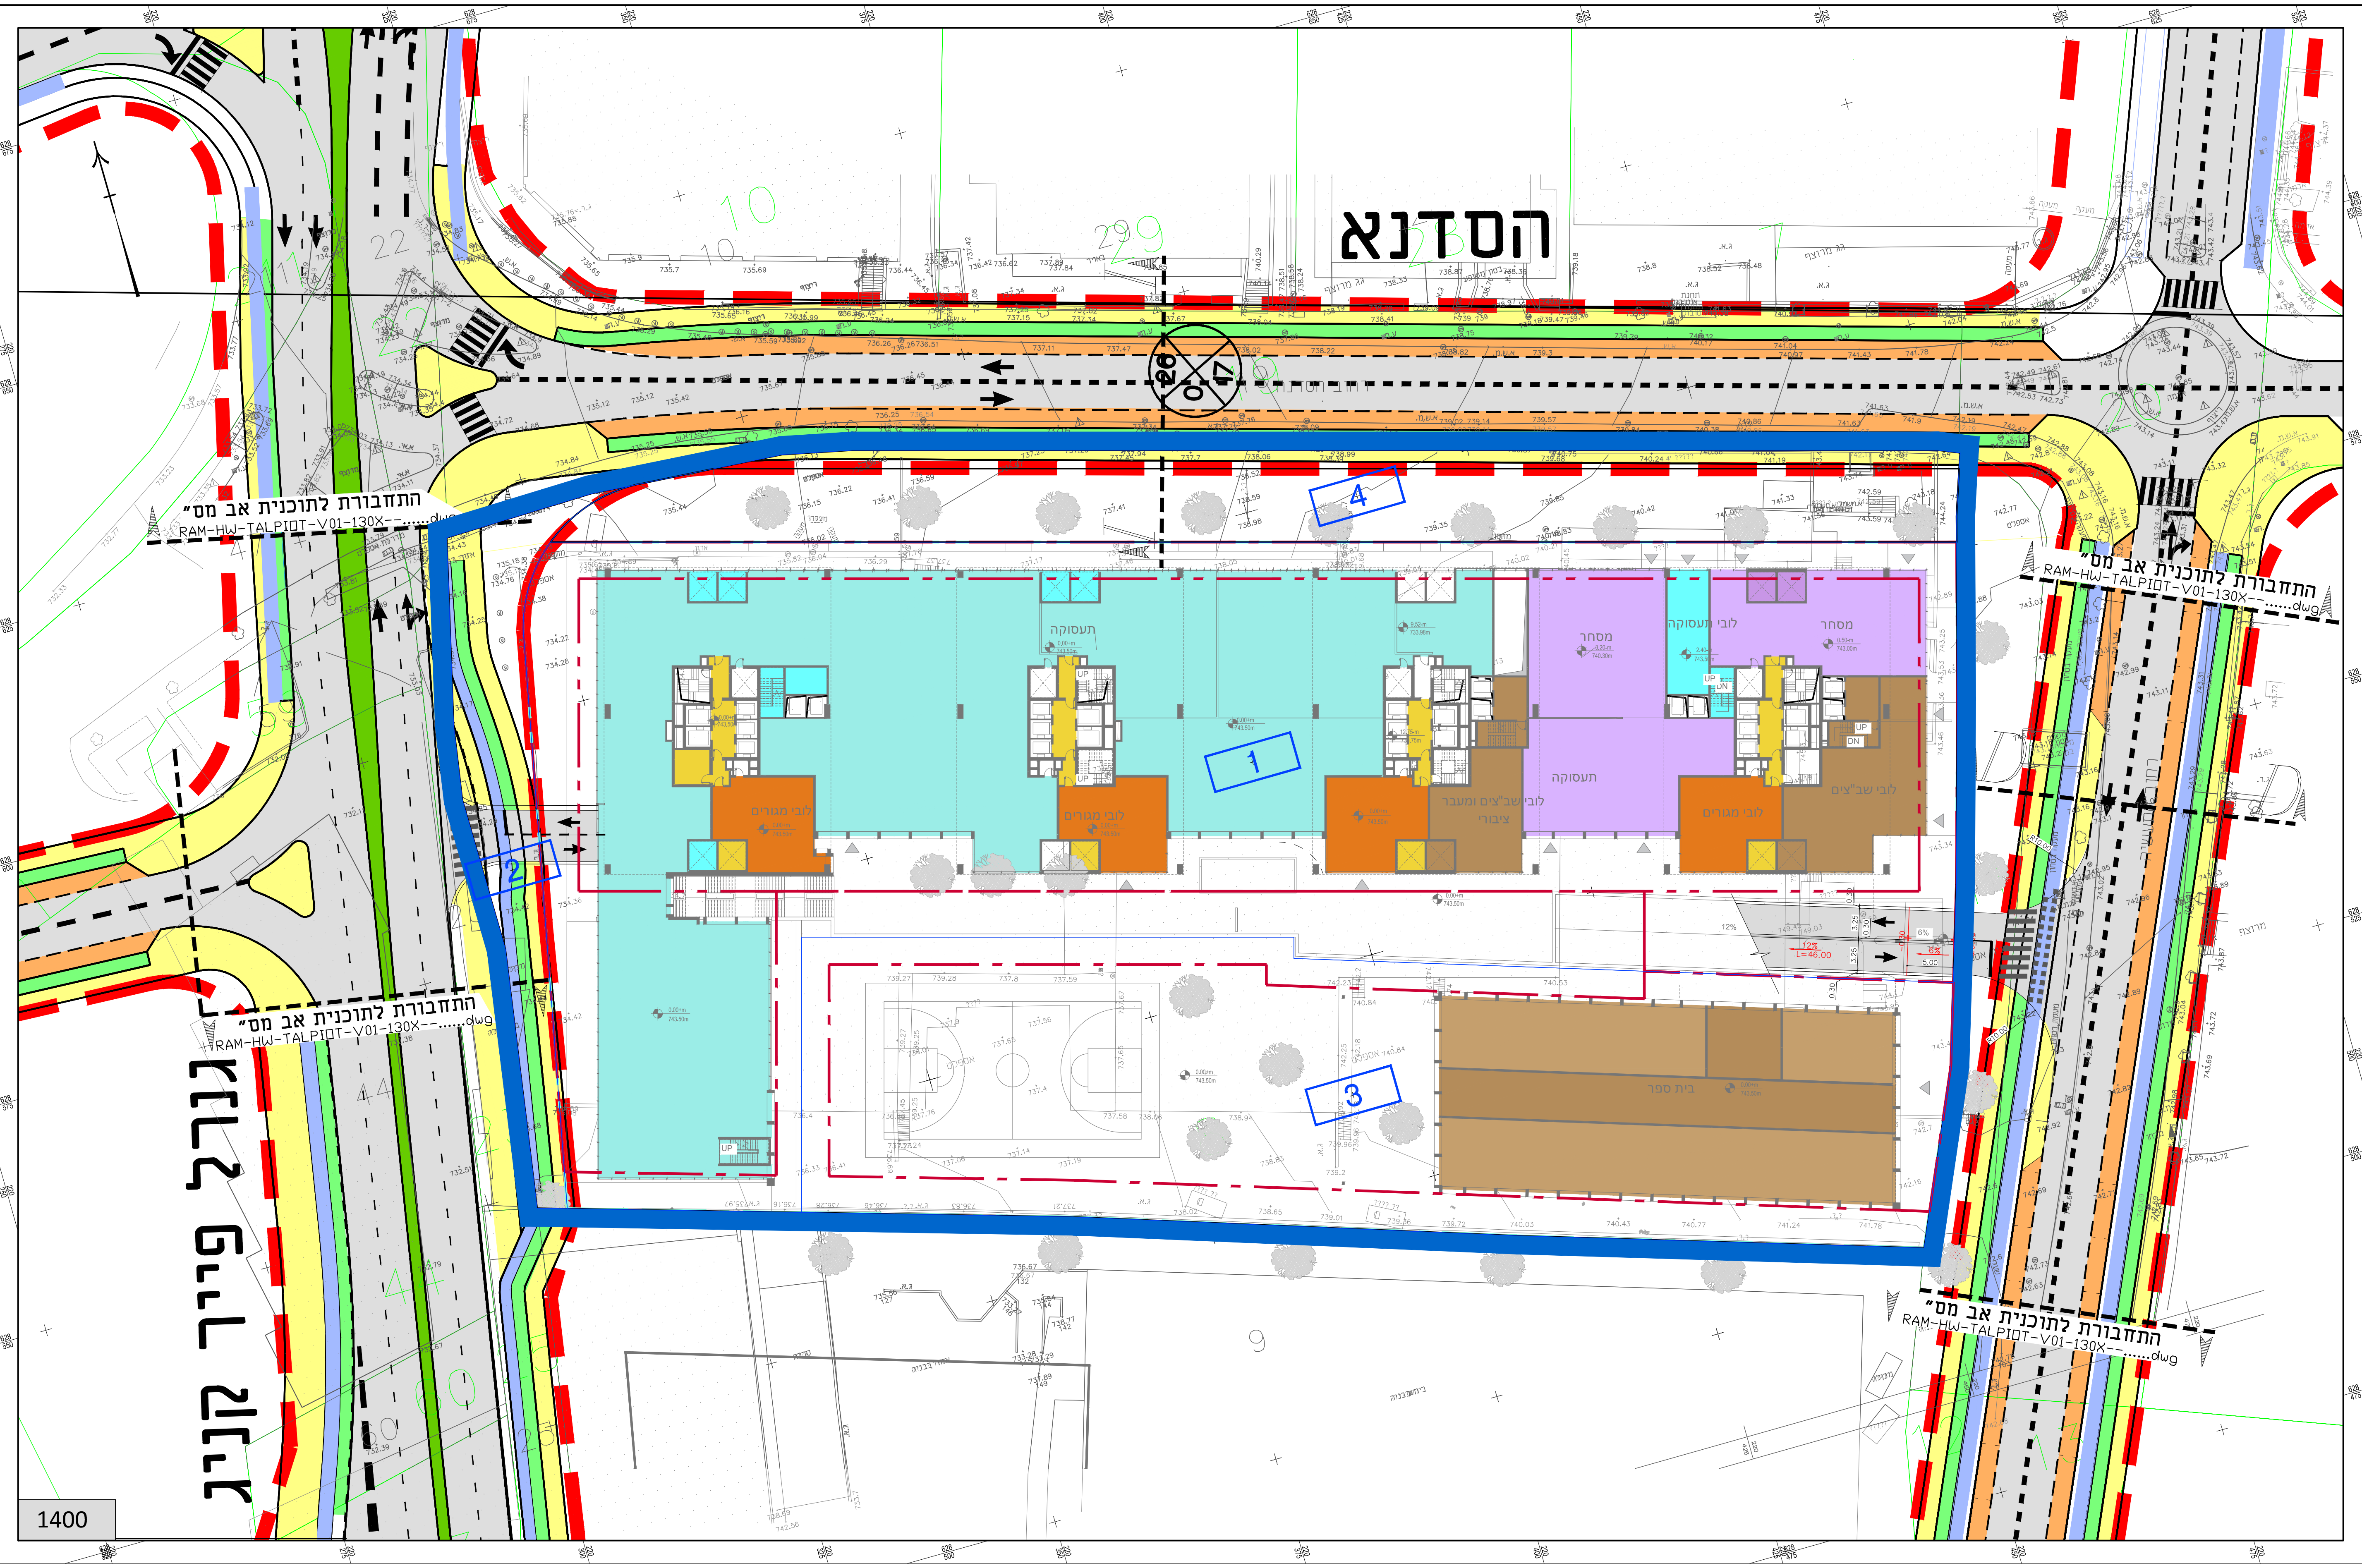
הסדנא
פייר קניג
26
0
17
1
2
3
4
מרוצף
התחברות לתוכנית אב מס"
RAM-HW-TALPIOT-V01-130X--......dwg
התחברות לתוכנית אב מס"
RAM-HW-TALPIOT-V01-130X--......dwg
התחברות לתוכנית אב מס"
RAM-HW-TALPIOT-V01-130X--......dwg
התחברות לתוכנית אב מס"
RAM-HW-TALPIOT-V01-130X--......dwg
1400

תוכנית העמדה
1:250

נספח תנועה

נספח לתכנית מס' 101-1095330

מתחם רג'ואן- הסדנא- פייר קינג
נספח מס' 2

גליון 1 מתוך 1

תחולה	מנחה
תיאור	
תאריך עריכת הנספח	28/12/2025

קנ"מ	לפי מסומן
תרשימים נוספים	קנ"מ

שמות וחתימות:

עורך הנספח
שם: רן זילברשטיין
חותימה:
תאגיד:
לוי | שטרק | זילברשטיין מהנדסים יועצים בע"מ
תכנון בהנדסה אזרחית, דרכים, תנועה ותמרורים
אברהם לוי, יוסי שטרק, רן זילברשטיין
ראשי: רח' יפו 145 א', חיפה, ת.ד. 9833 חיפה 3109702,
טל. 04-8553655, פקס. 04-8553654
סניף תל-אביב: רח' יגאל אלון 65, 6744316,
טל. 03-3733500, פקס. 04-8553654
www.levyshtark.co.il e-mail: office@levyshtark.co.il

מקרא:

מקרא

גבול תוכנית	🟦
זכות דרך	▬ ▬ ▬
גבול תוכנית מאושרת	▬
גוש/ חילקה	▬
קוו בניין	▬ ▪ ▬
קוו בניין תחתי	▬ ▪ ▬
שער כניבה/ יציאה	▬ ▪ ▬
שביל אופניים	🟦
חניה לרכב תיפעולי	🟦
חניה לרכב פרטי	🟧
חניות מסחר/ תעסוקה	🟩
חניות למוסדות ציבור	🟪
חניה נגישות	🟦
מדרכה מתוכננת	🟨
חניה אופנועים	☐
חניה כפולה לאופניים	▨

V-RDJAN-PD-140X (2739).dwg