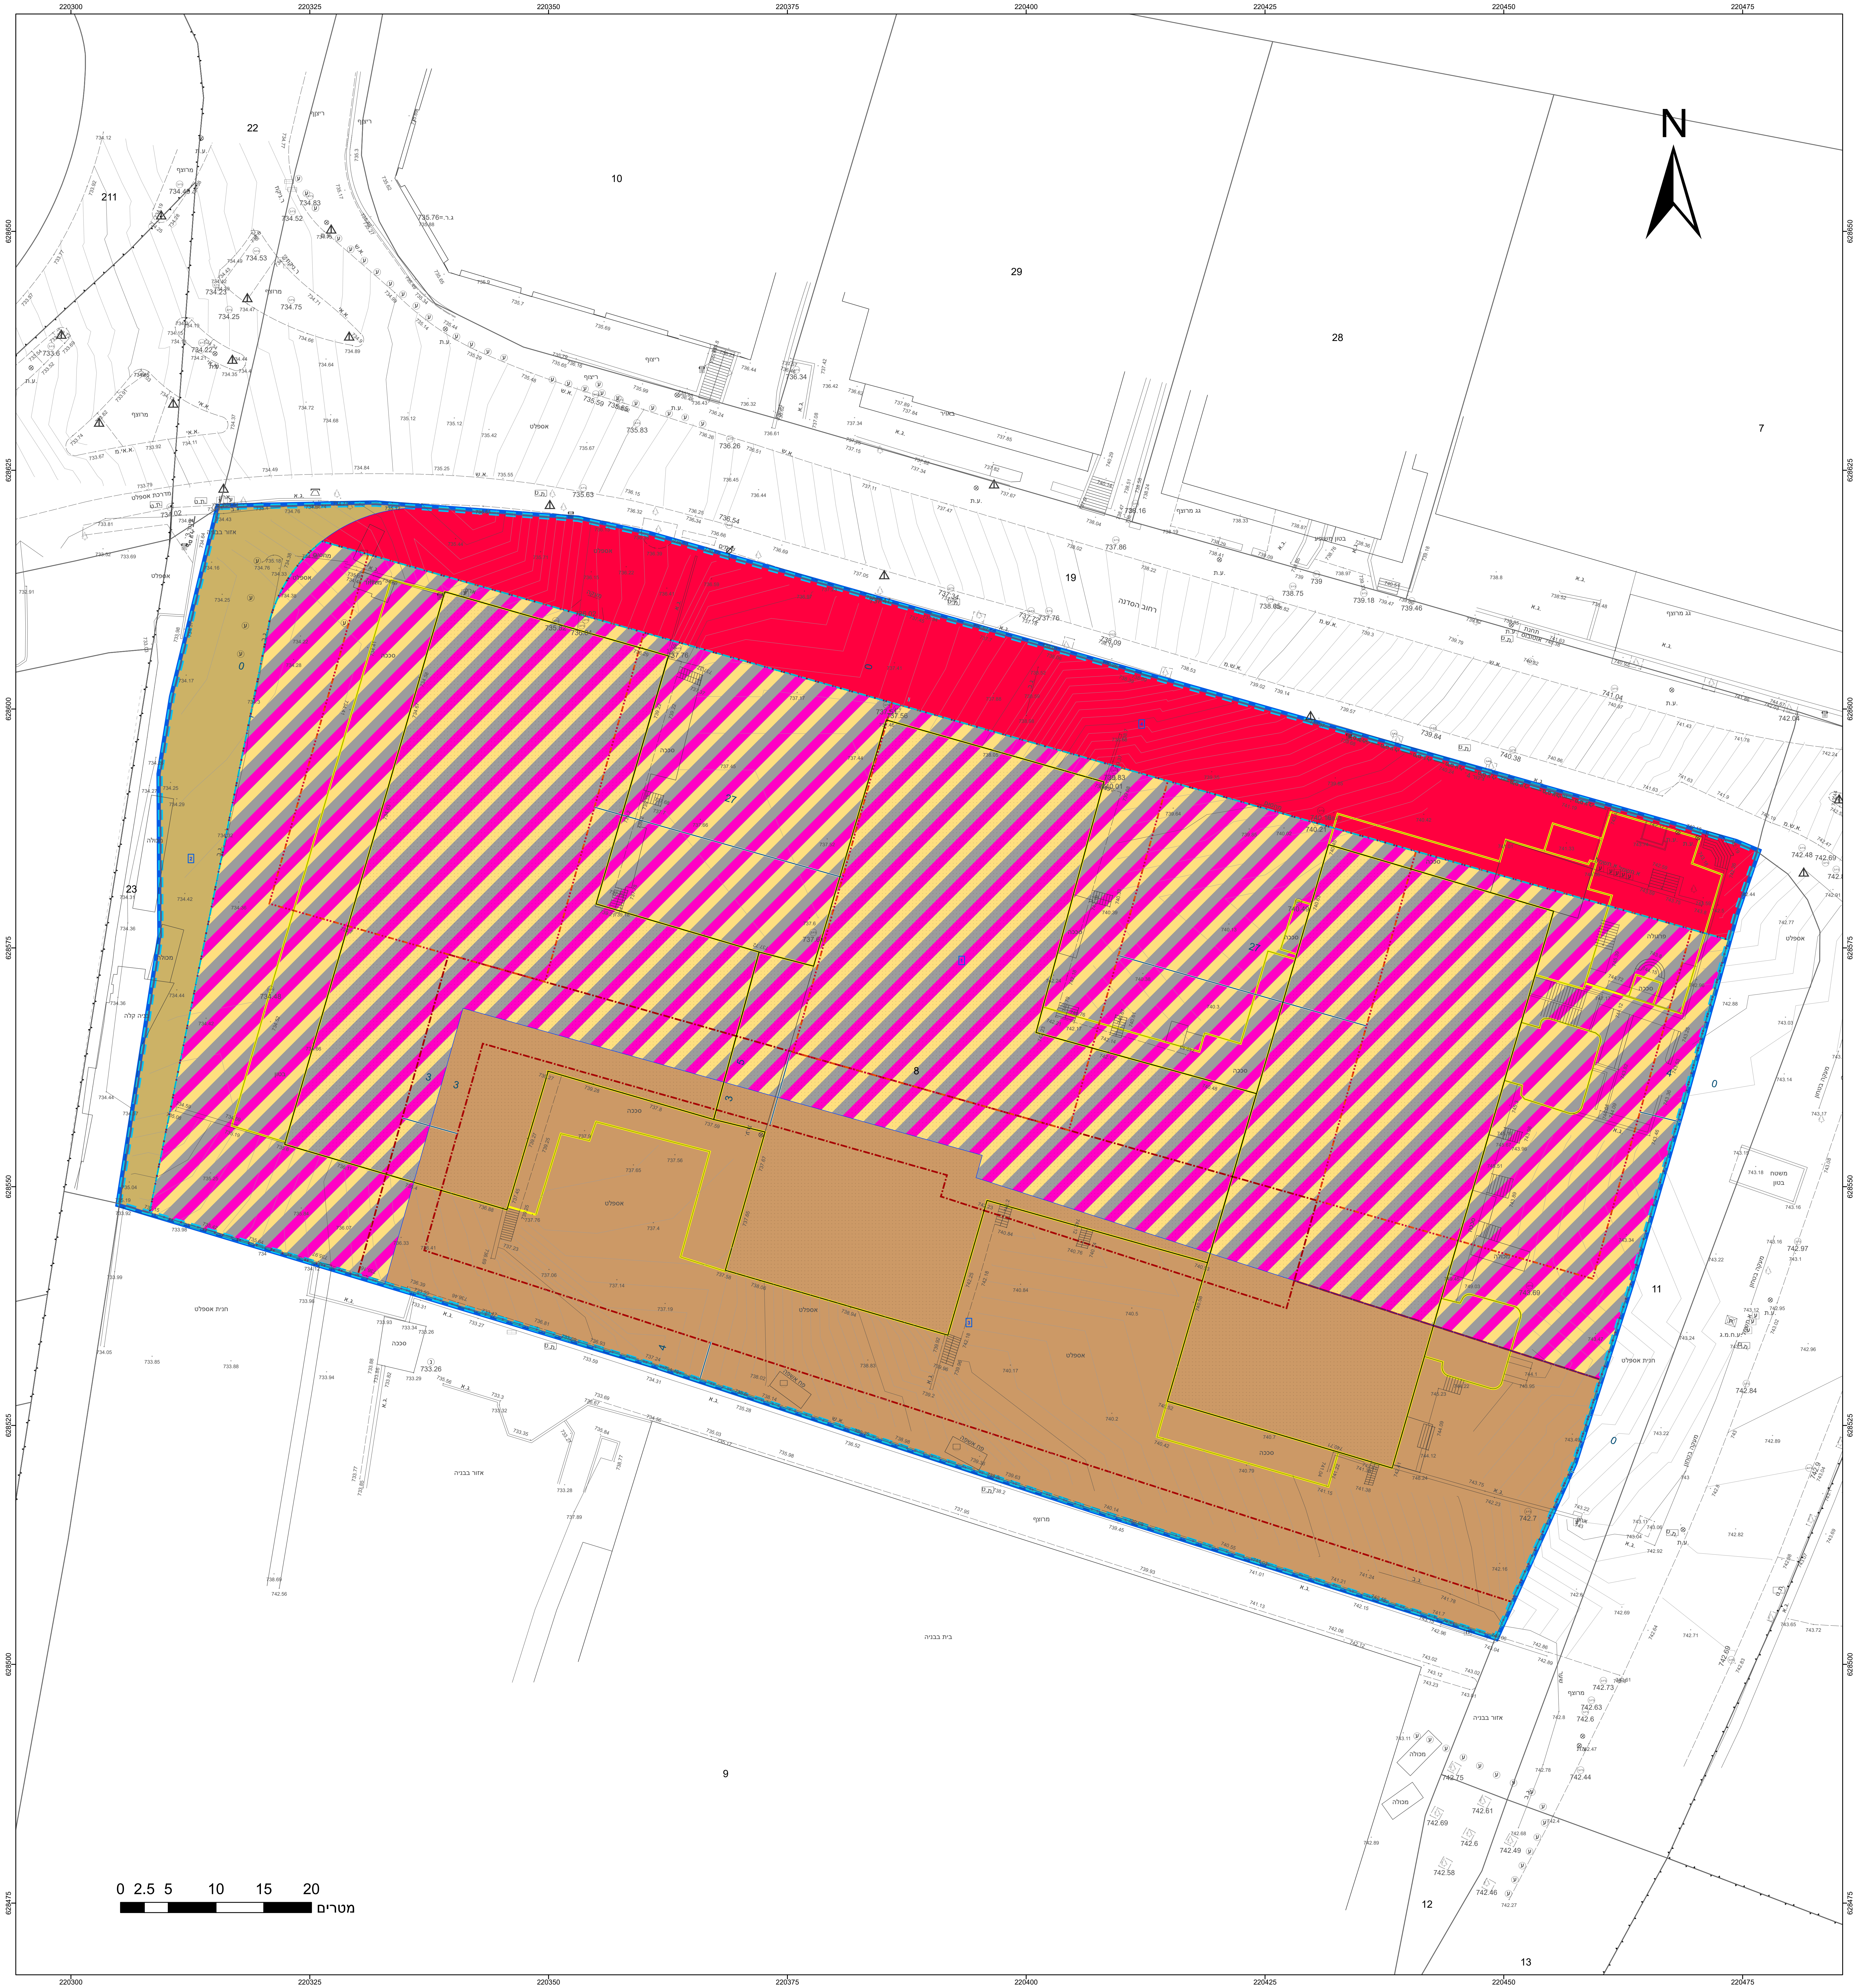

מקרא

▭	גבול תכנית
140	תא שטח ומספרו
גוש 1234	גבול גוש ומספרו
5	גבול חלקה ומספרה
1 2 3 4	רוזטת דרך: מספר הדרך, קוי בנין, רוחב הדרך
🟫	מבנים ומוסדות ציבור
🟨	דרך מאושרת
🟥	דרך מוצעת
▨	מגורים, מסחר ותעסוקה
⬚	שטח לאיחוד וחלוקה חדשה
-·-·-	קו-בנין
-··-··	קו בנין עילי
-·-·-	קו בנין תחתי/תת קרקעי
—	להריסה
—	מידות

חוק התכנון והבניה, התשכ"ה - 1965
תכנית מתאר מקומית

מס' 101-1095330

מתחם רג'ואן - הסדנא-פייר קניג

תשריט מצב מוצע — **גיליון 1 מתוך 1**

מחוז	**ירושלים**
מרחב תכנון מקומי	**ירושלים**
רשות מקומית	
ישוב	
תכנית בסמכות	מחוזית
איחוד וחלוקה	איחוד ו/או חלוקה ללא הסכמת כל הבעלים בכל תחום התכנית/בחלק מתחום התכנית
היתרים או הרשאות	תכנית שמכוחה ניתן להוציא היתרים או הרשאות
מונה תדפיס התשריט	13
מועד הפקה	09/04/2025 18:50
שטח התכנית	13.337 דונם
קנה מידה	1:250

אישורים בתכנית מס' 101-1095330

תרשים התמצאות - קנ"מ 1:5500

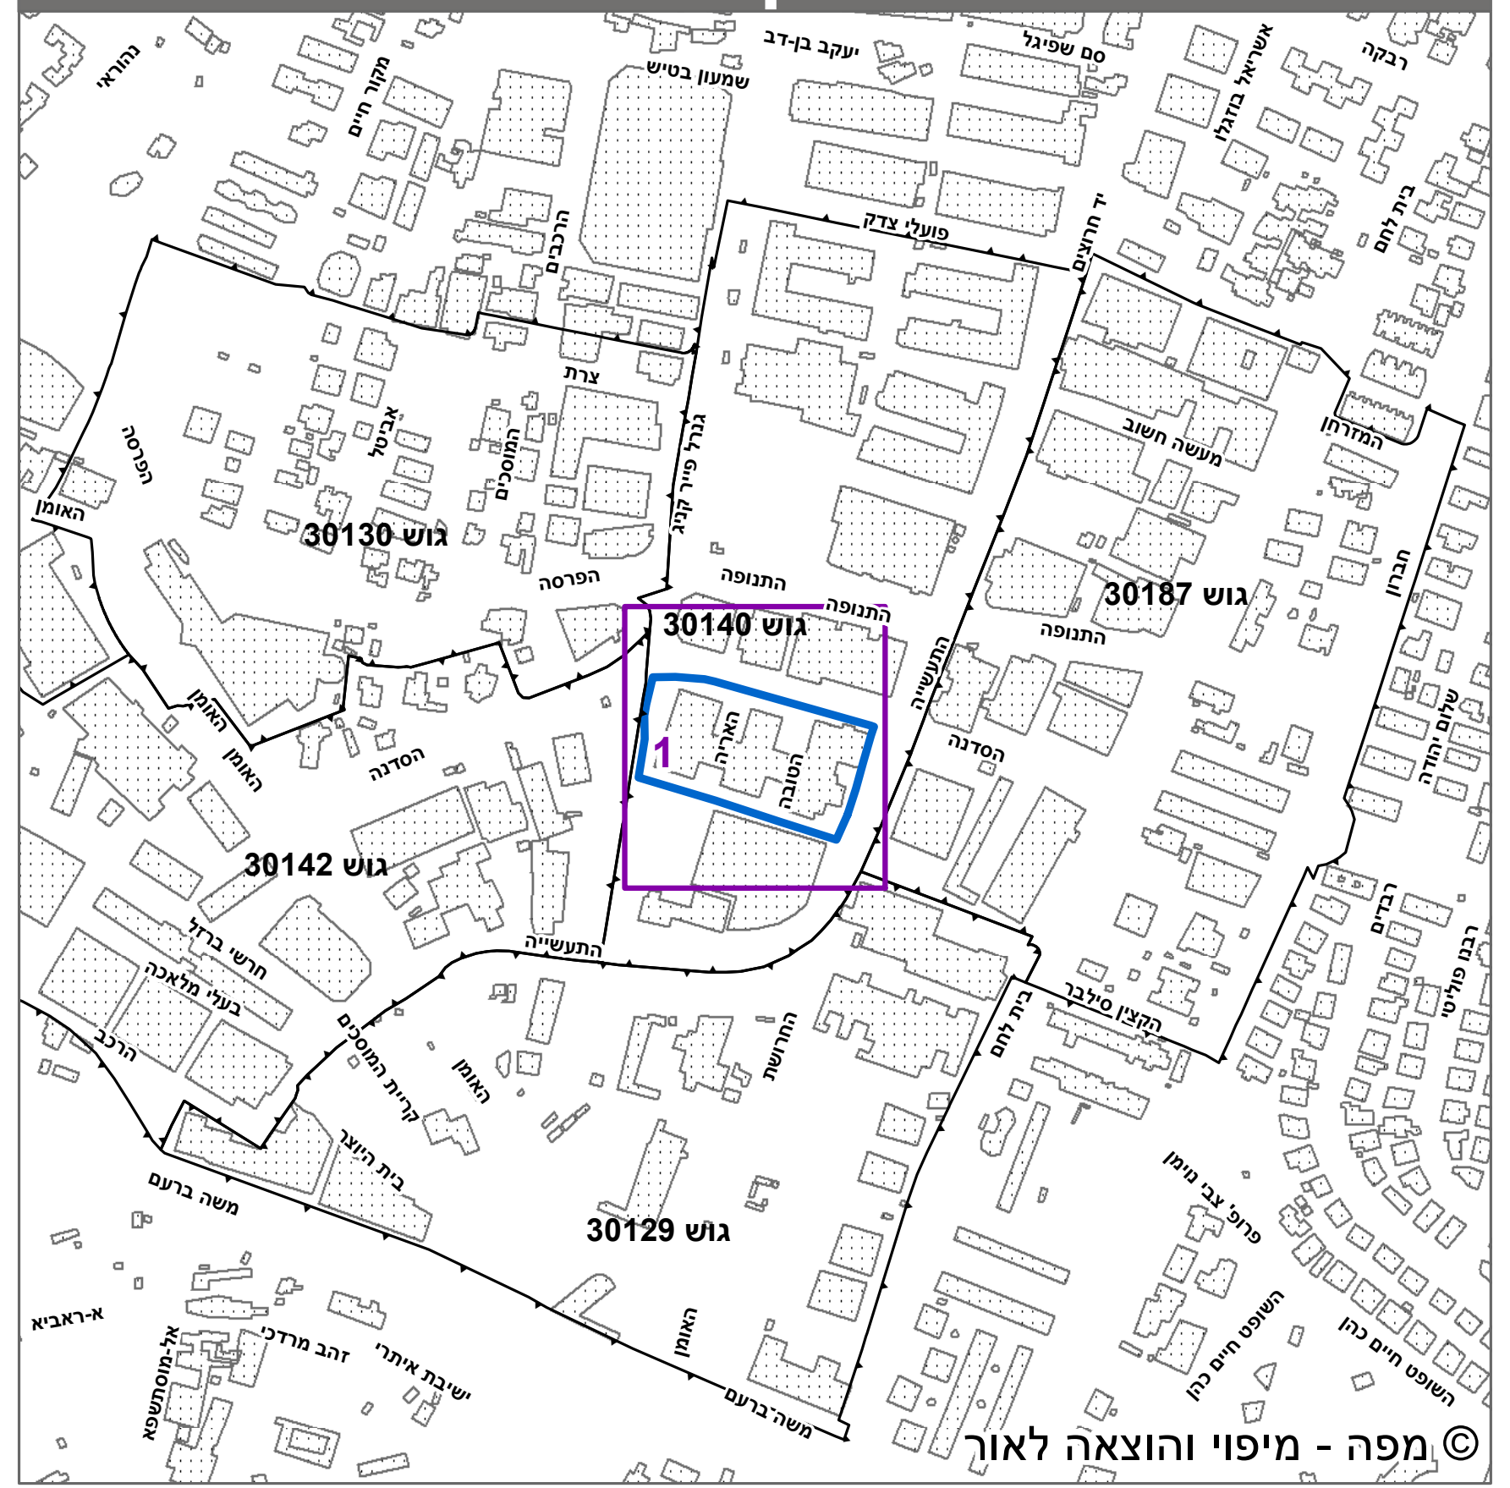

© מפה - מיפוי והוצאה לאור

שנת צילום אויר: 2023

תרשים סביבה - קנ"מ 1:1300

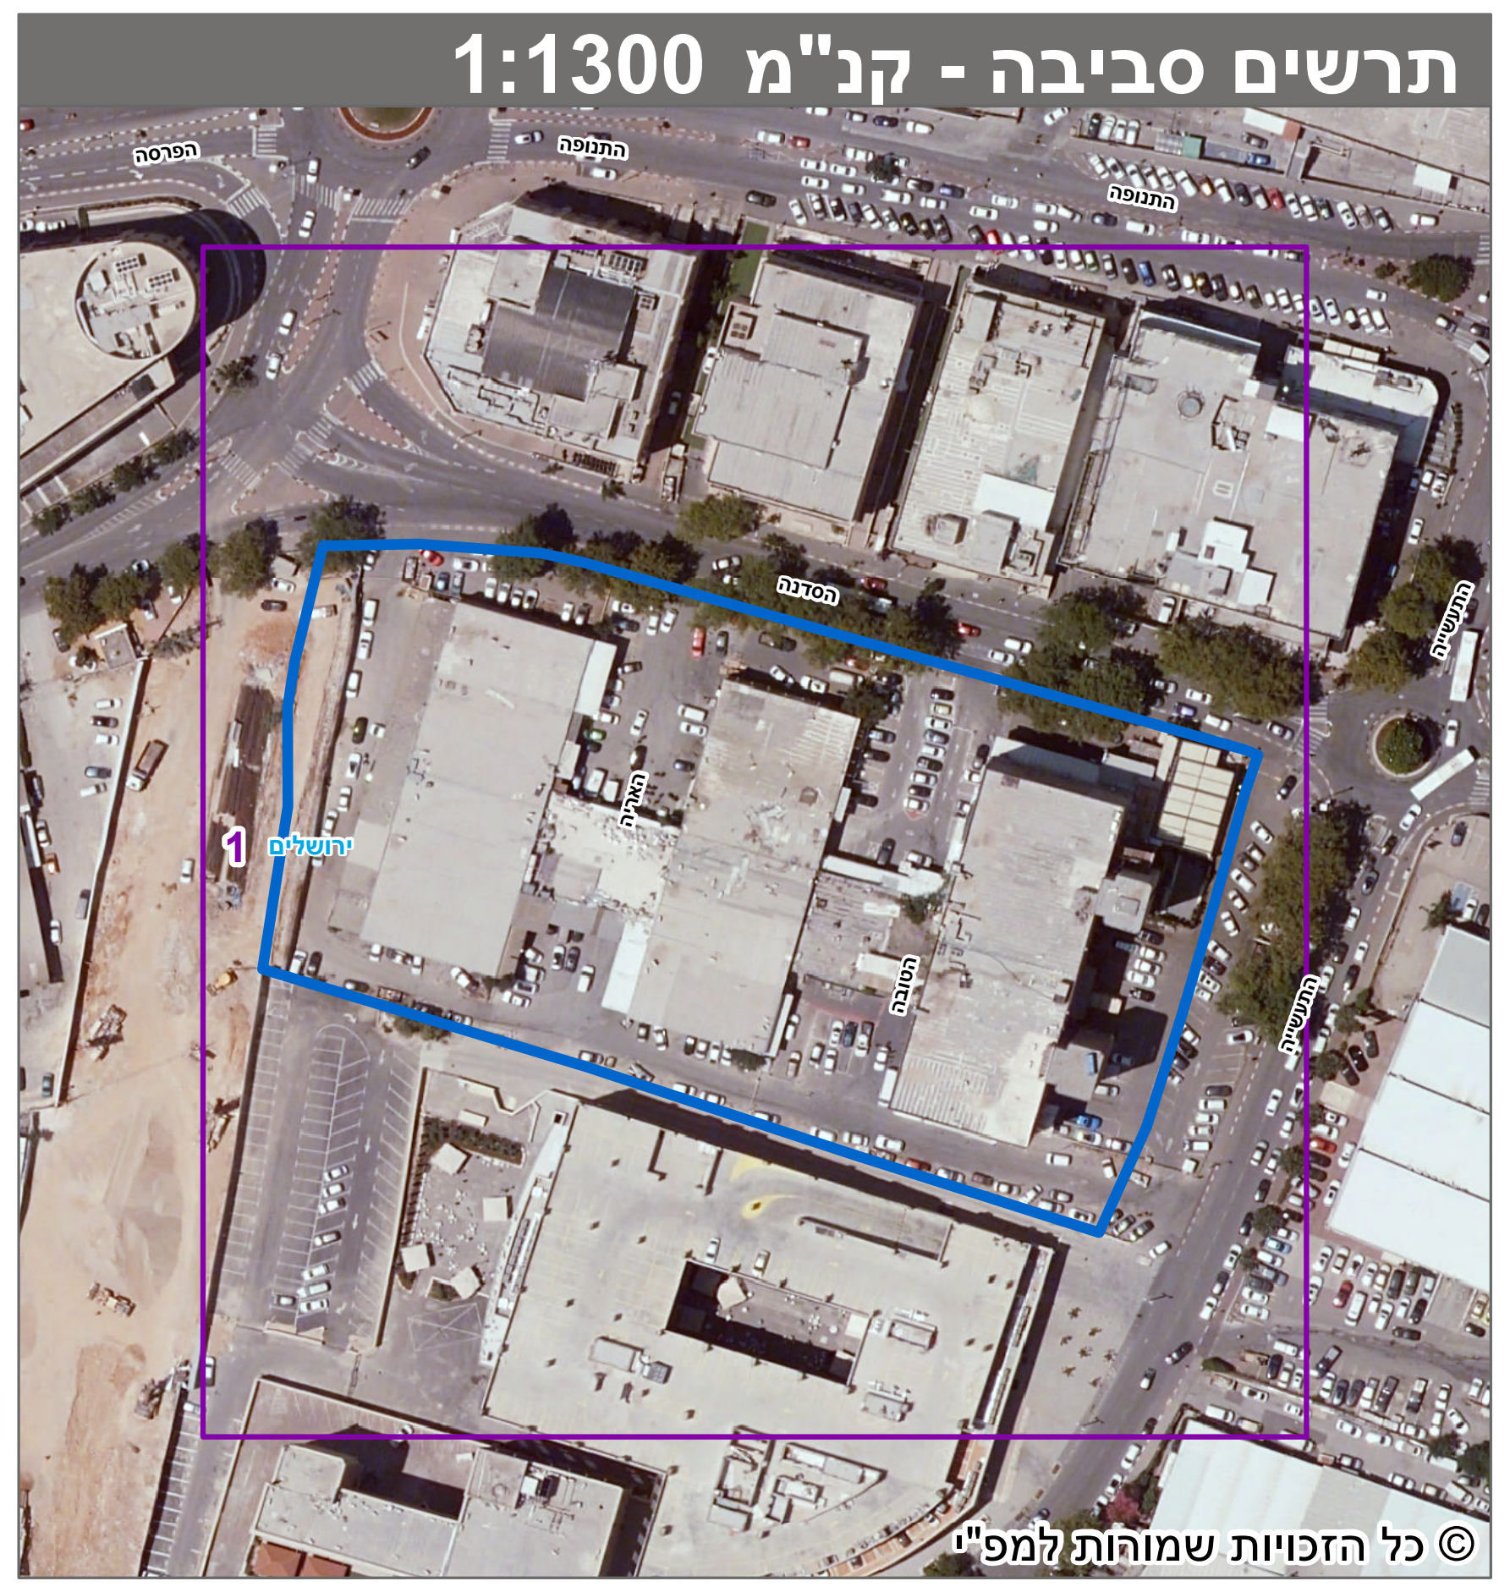

© כל הזכויות שמורות למפ"י

שמות*

מגיש התכנית	**אמיר רג'ואן** תאגיד: **אמינפה חברה אמריקאית לפיתוח שטחי תעשיה בע"מ**
עורך ראשי	**בועז ביטמן** תאגיד: **ביטמן בן צור אדריכלים**

טבלת גושים וחלקות*

מספר גוש	חלק/ כל הגוש	מספרי חלקות בשלמותן	מספרי חלקות בחלקיותן
30140	חלק	8	

מסמך ממוחשב חתום דיגיטלית ומאושר על ידי גורם מאשר

comsign

* הרשימה המלאה מפורטת בהוראות התכנית / בהודעה שפורסמה בעיתונות וברשומות

הריני מצהיר בזאת כי המפה הטופוגרפית/המצבית המהווה רקע לתכנית זו, נערכה על ידי ביום 21.02.2023 והיא הוכנה לפי הוראות נוהל מבא"ת ובהתאם להוראות החוק ולתקנות המודדים שבתוקף.
דיוק הקו הכחול והקדסטר: מדידה אנליטית מלאה ברמת תצ"ר

שם המודד	מספר רשיון	חתימה	תאריך
אהוד קראוס	1363		