חוק התכנון והבנייה, התשכ"ה - 1965
תוכנית מפורטת

101-1158146

בית הנוער העברי

נספח בינוי גליון 1 מתוך 1

מחוז	ירושלים
מרחב תכנון מקומי	עיריית ירושלים
רשות מקומית	ירושלים
ישוב	ירושלים
תאריך	23.09.2024
שם התרשים	**קנ"מ**
נספח בינוי	1:750

שמות וחתימות:

עורך התוכנית	שם: אדר' עדי אסיף תאגיד: גוטמן אסיף אדריכלים	חתימה:
עורך הנספח	שם: אדר' עדי אסיף תאגיד: גוטמן אסיף אדריכלים	חתימה: תאריך:

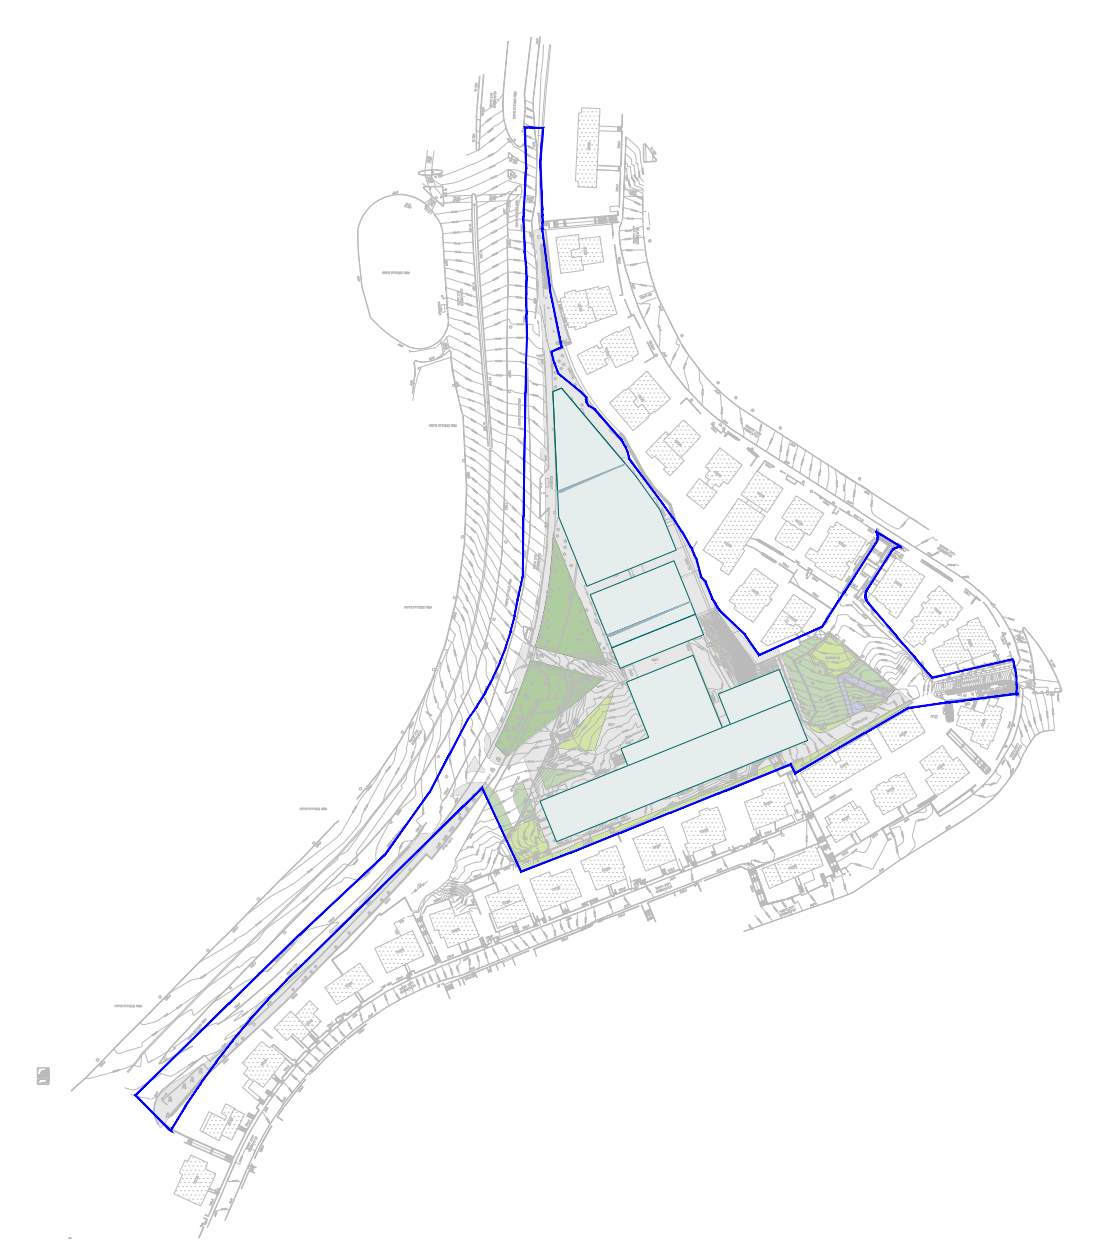

תכנית גגות 1:2500

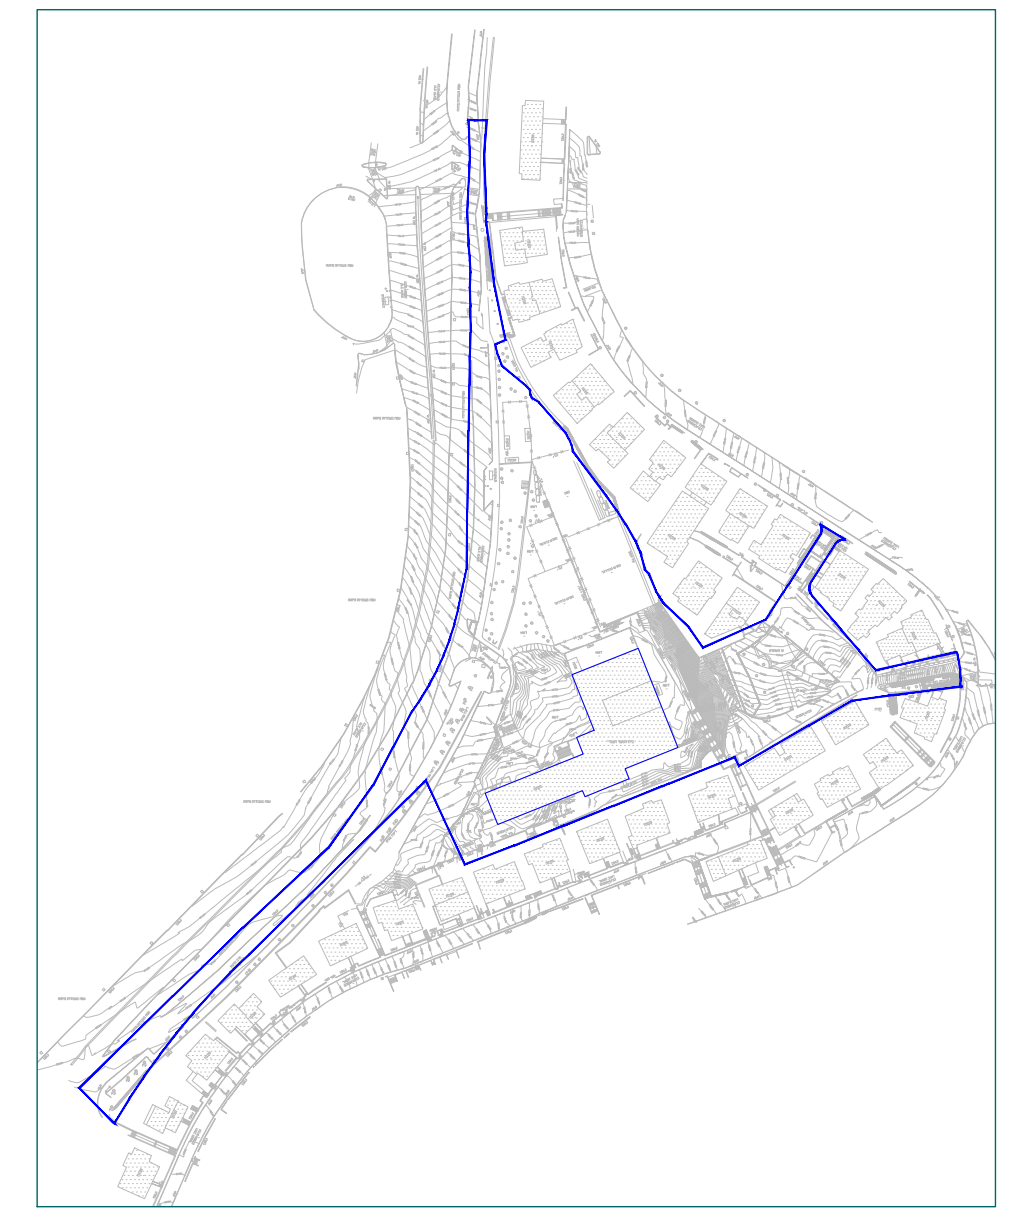

תכנית מדידה 1:2500

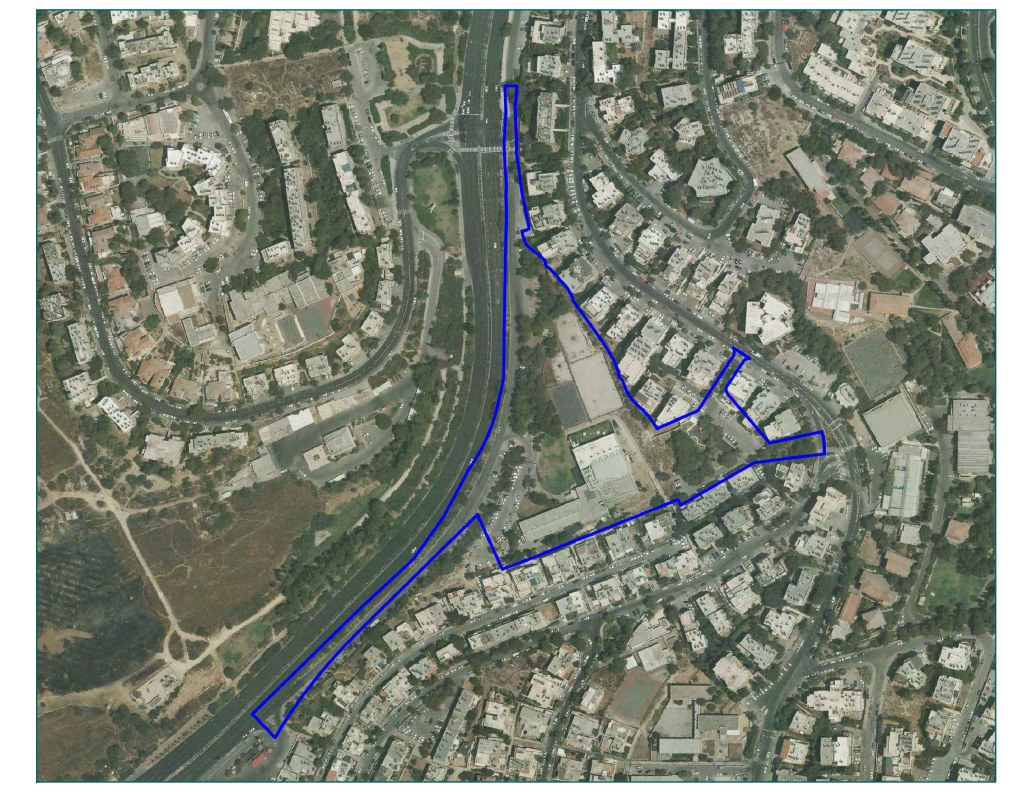

תרשים סביבה 1:3000

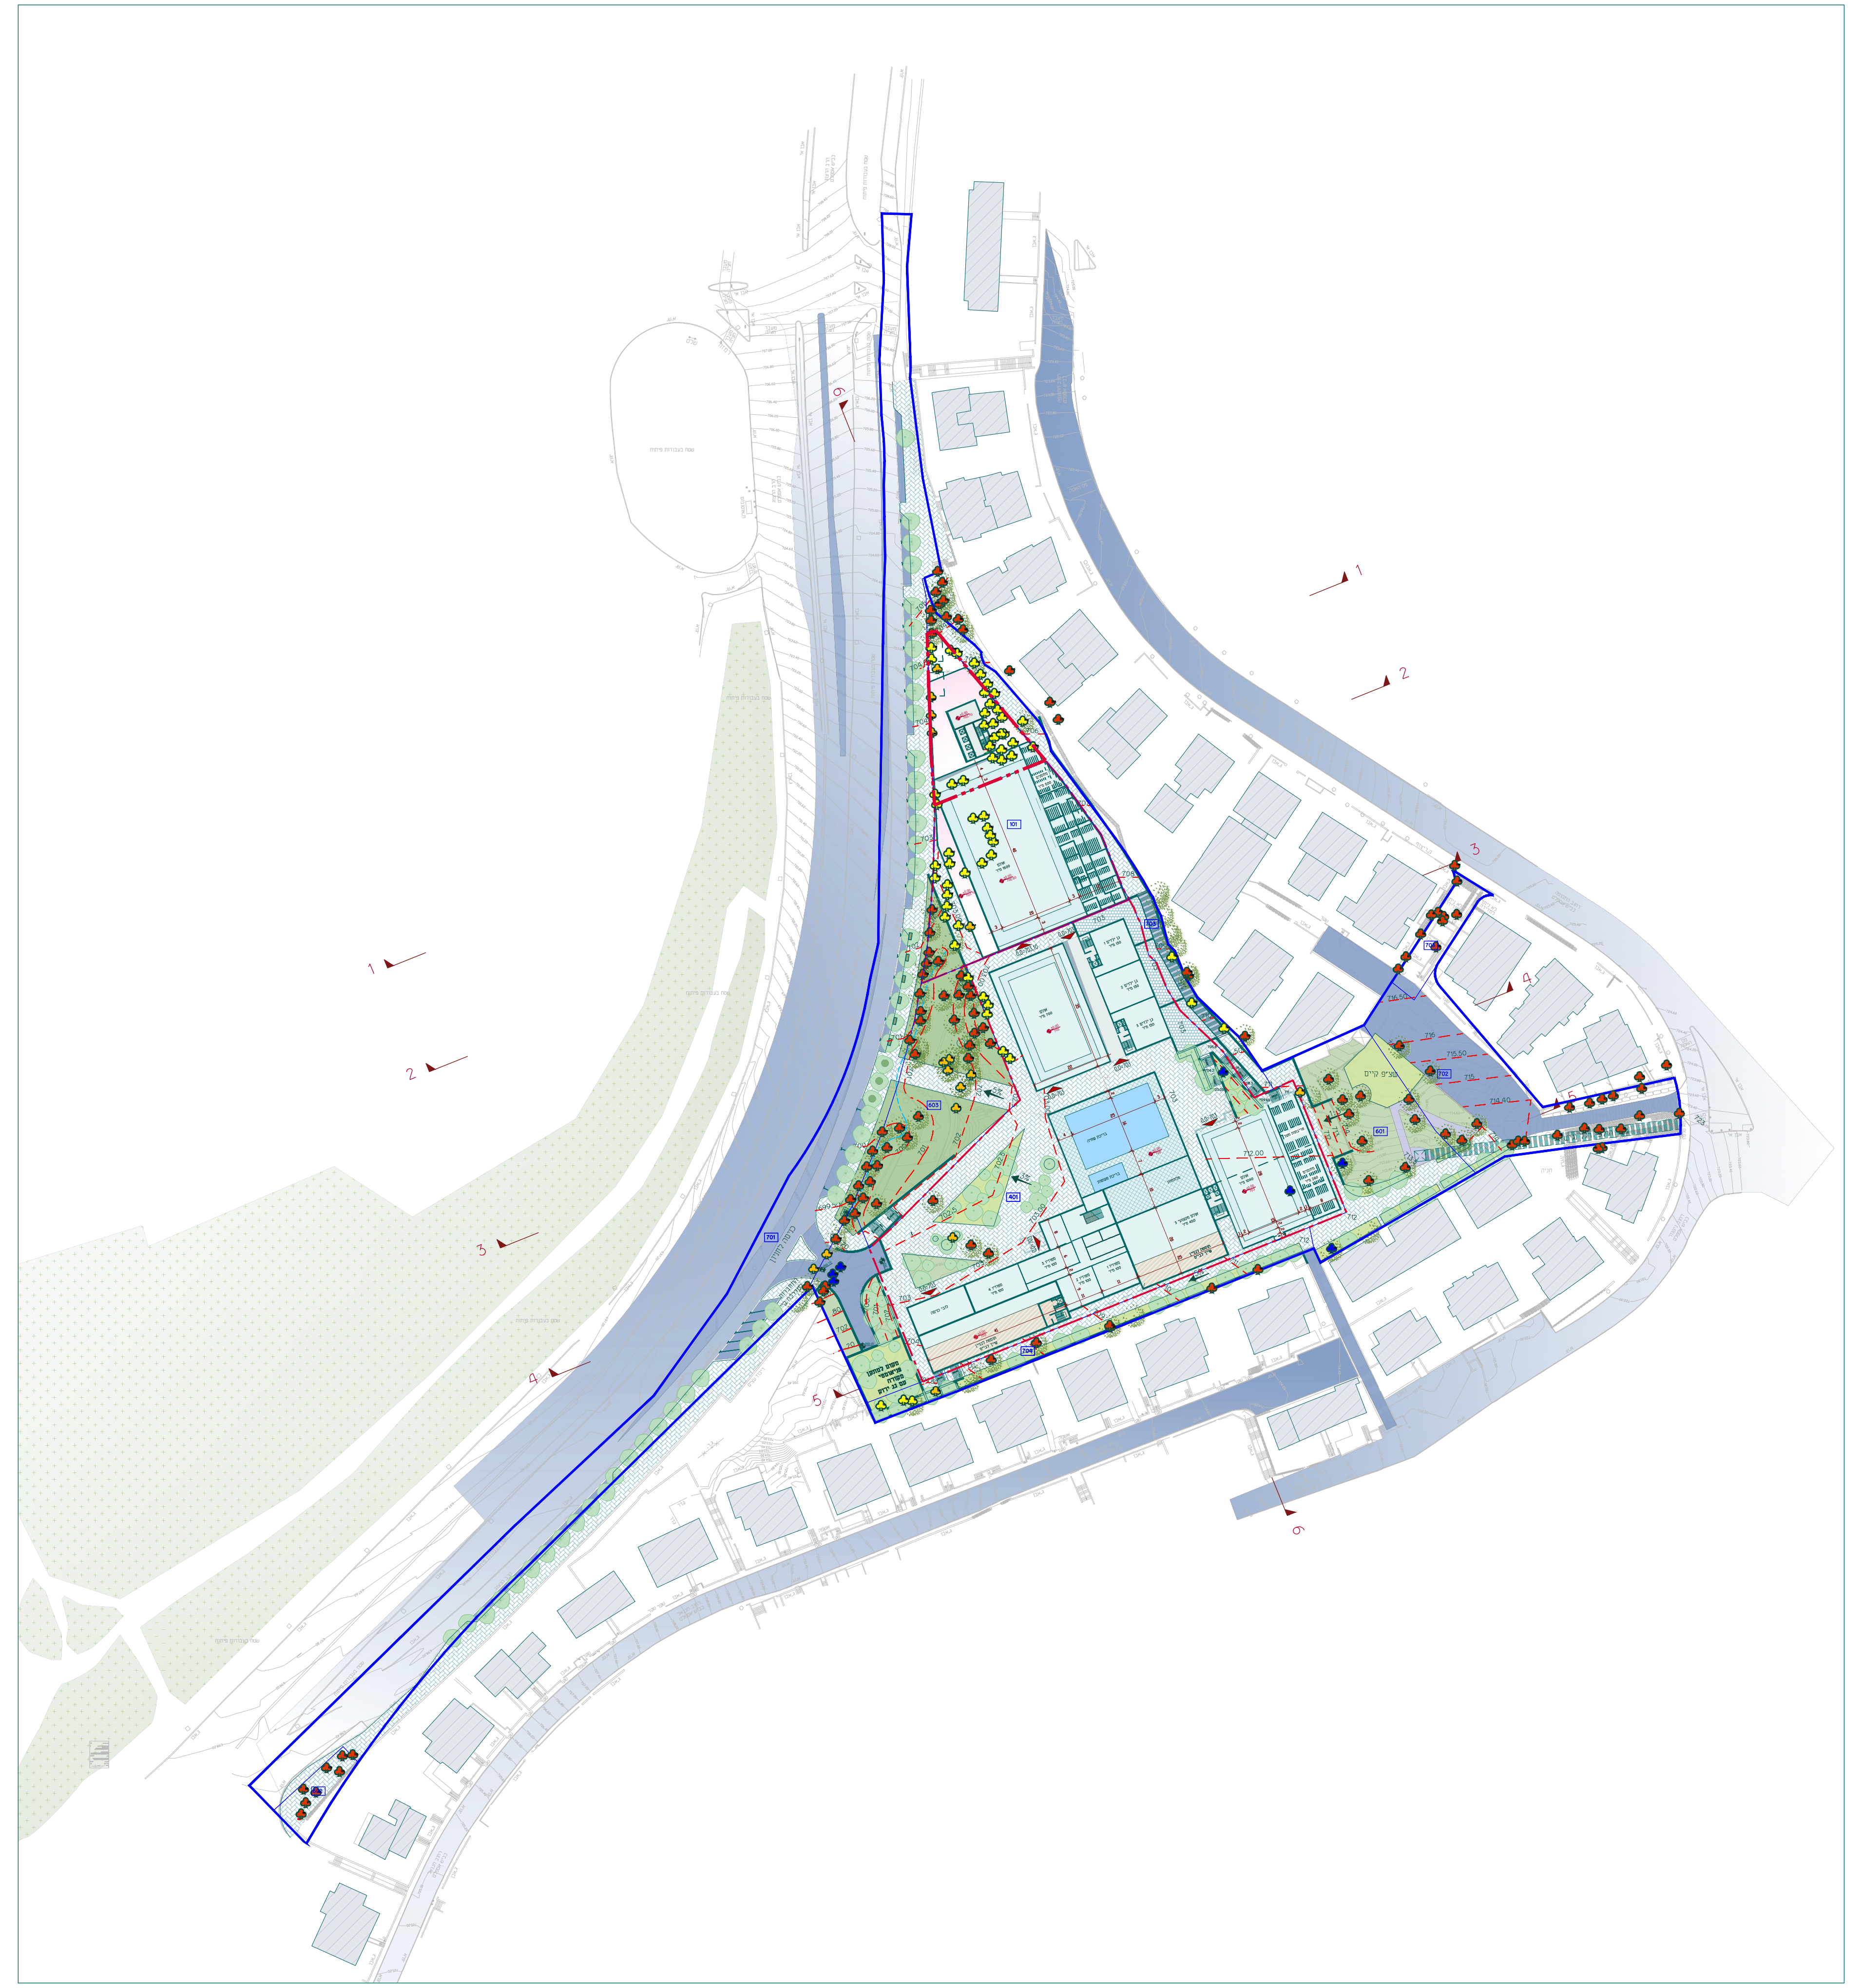

קומת הקרקע 1 : 750

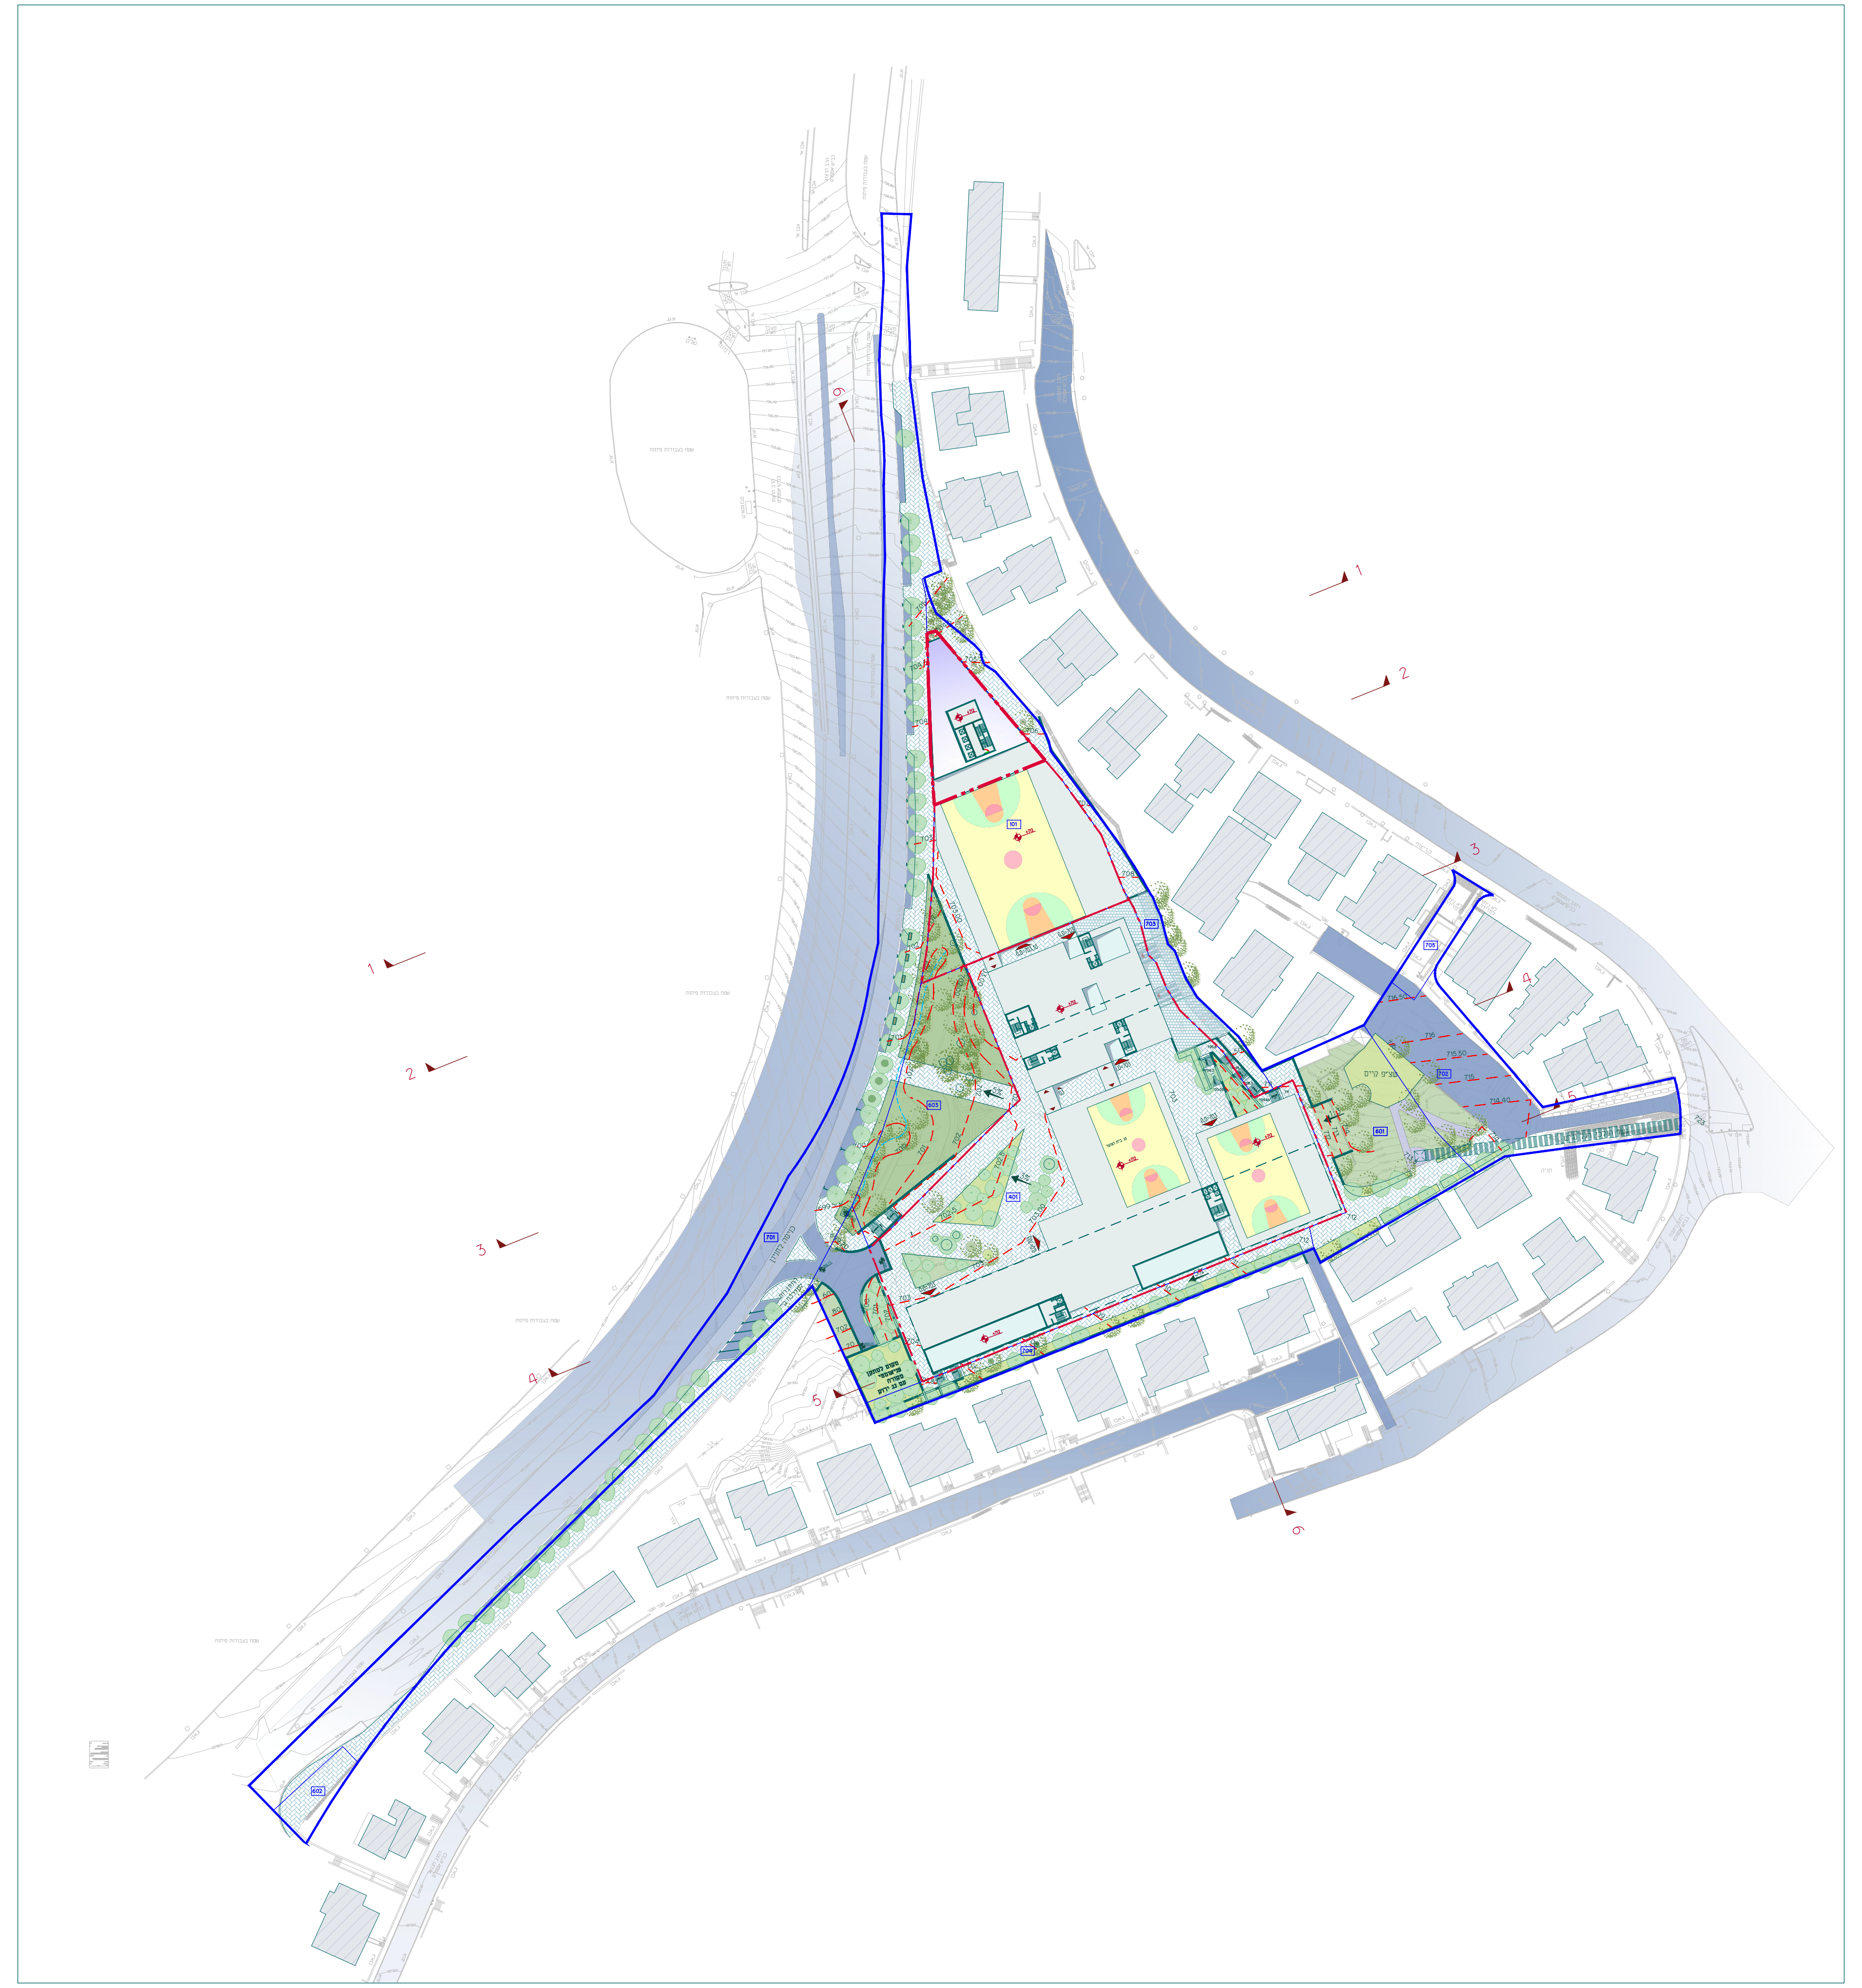

קומה מפולשת 1 : 750

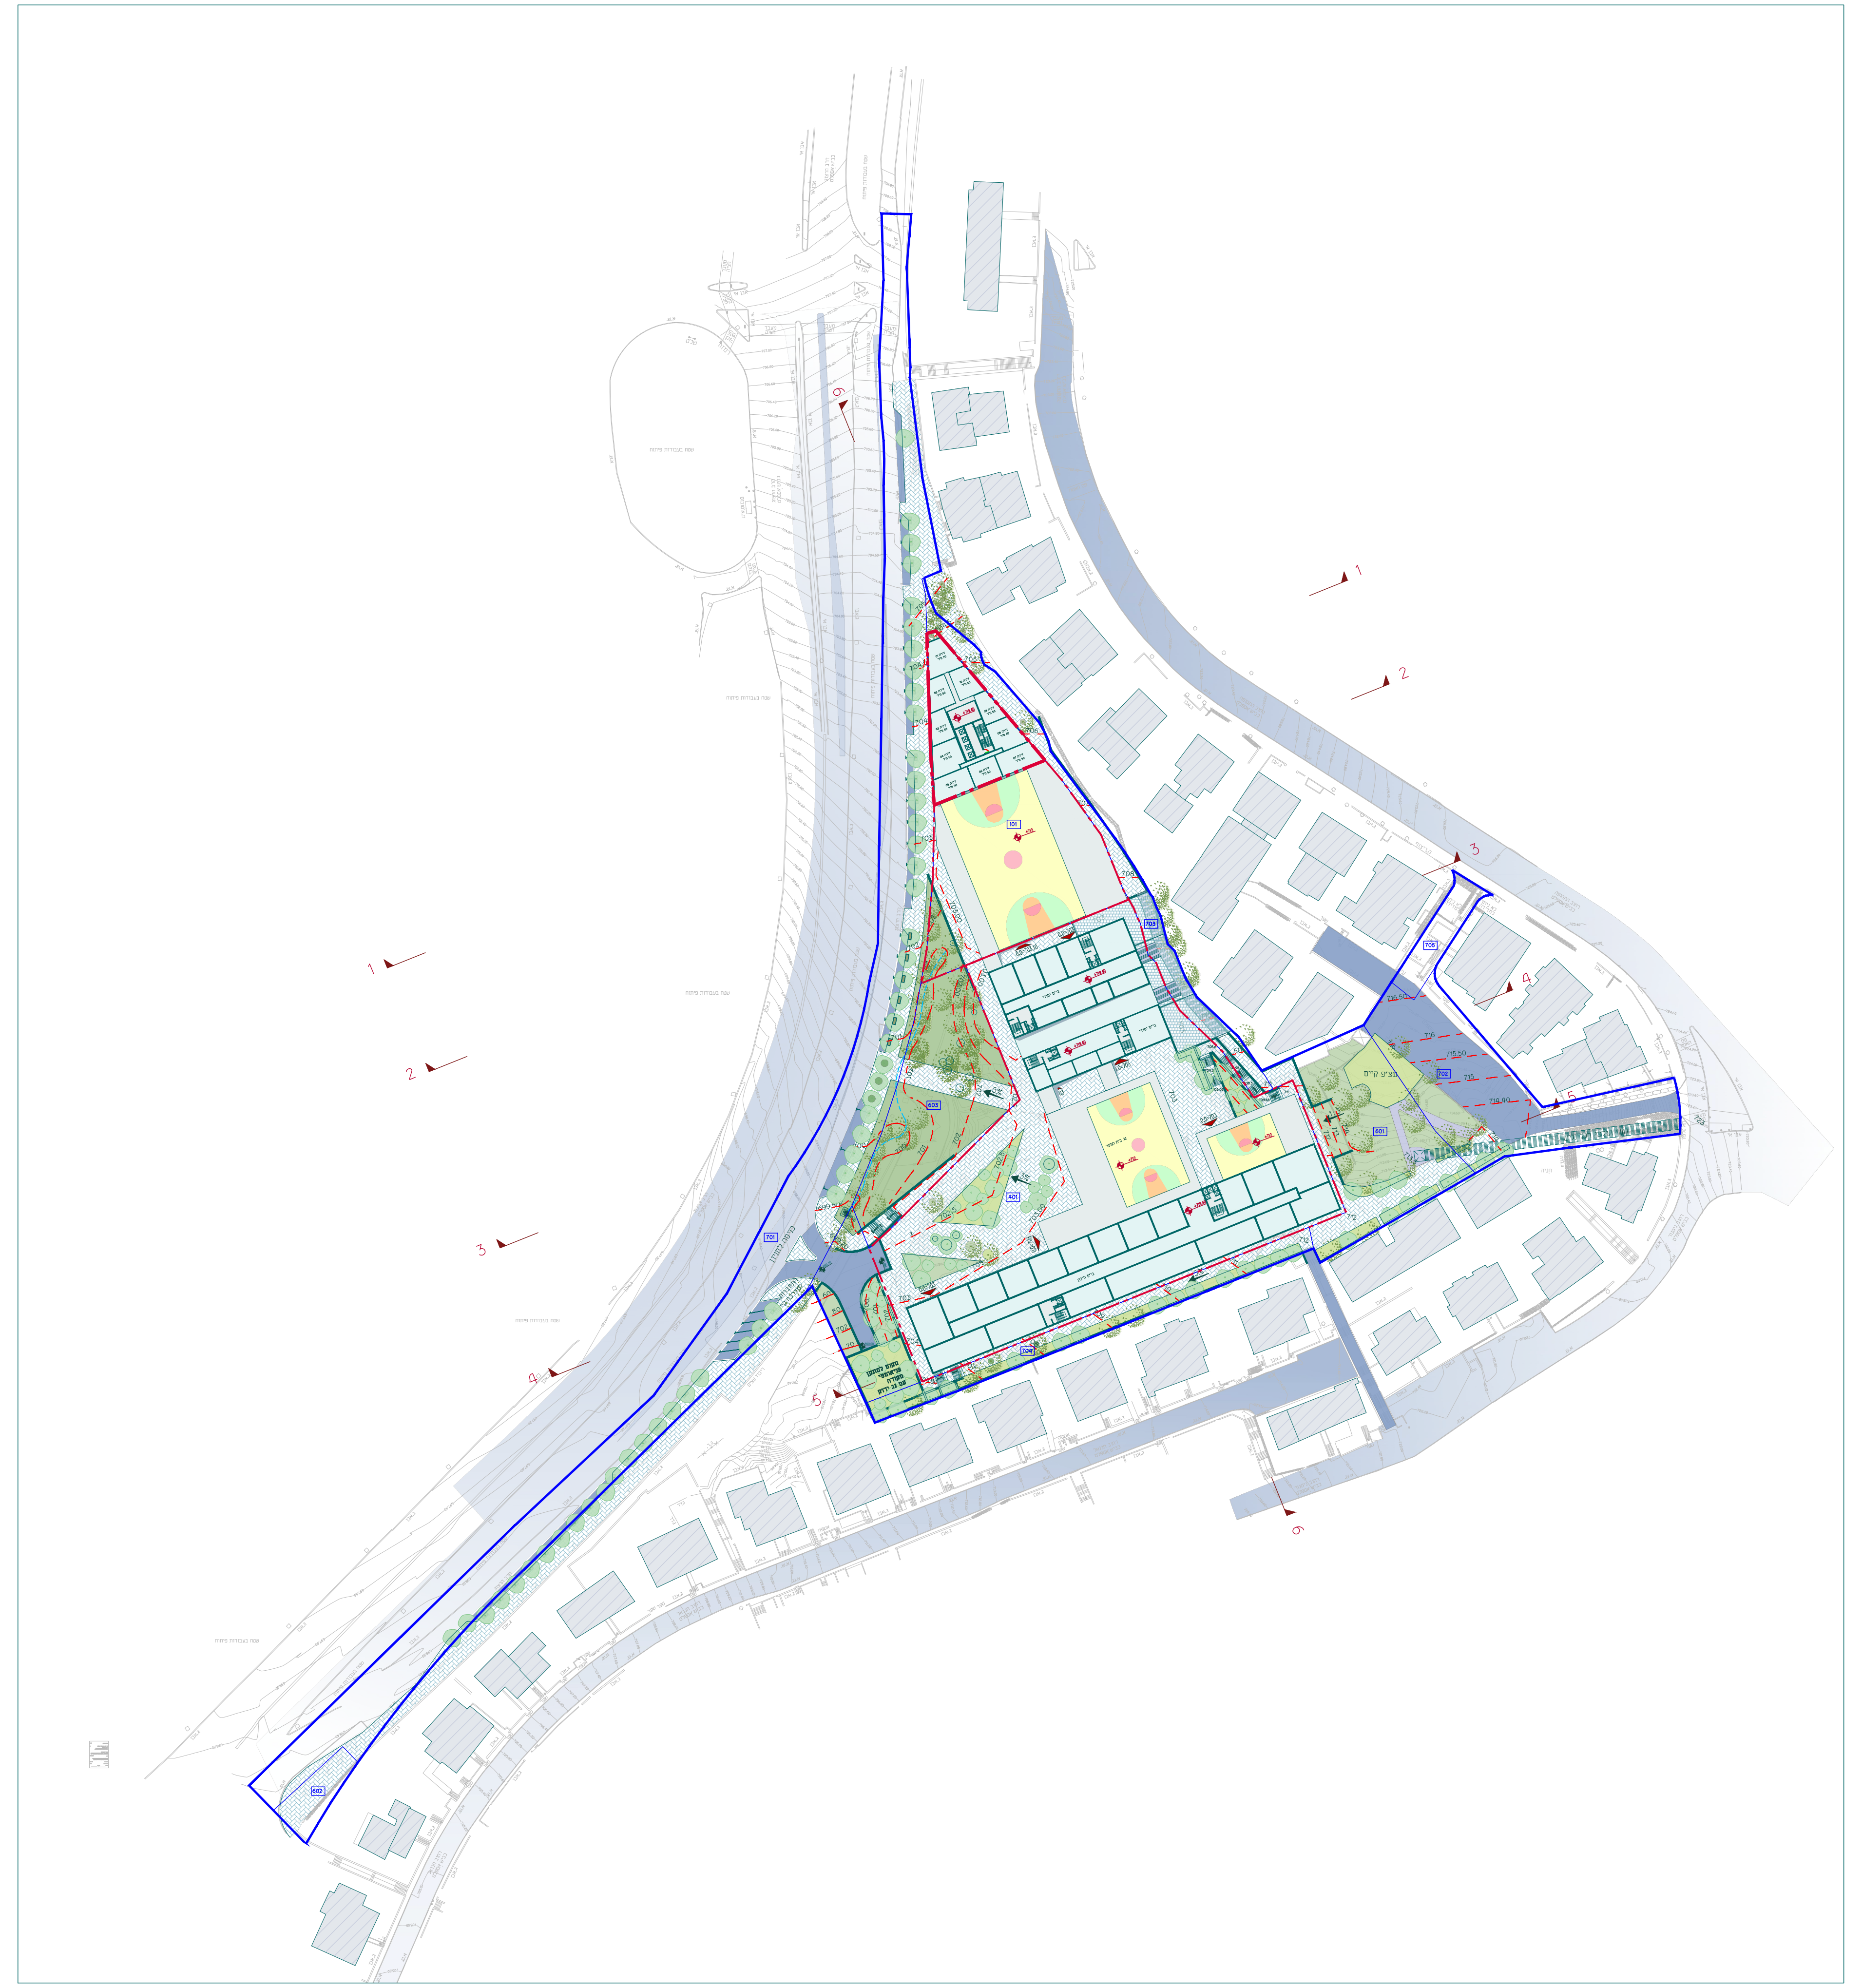

קומה טיפוסית 1 : 750

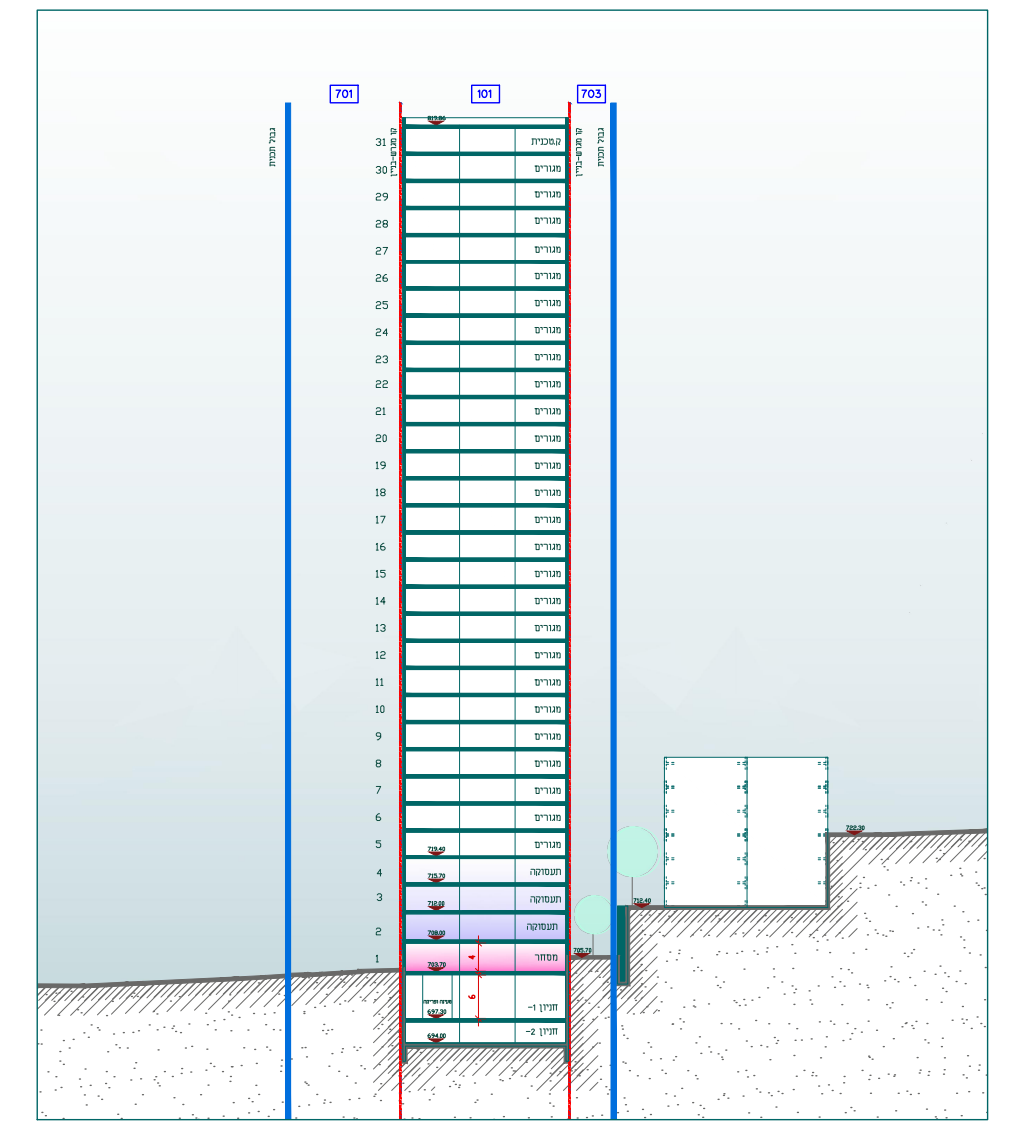

חתך 1-1 1 : 750

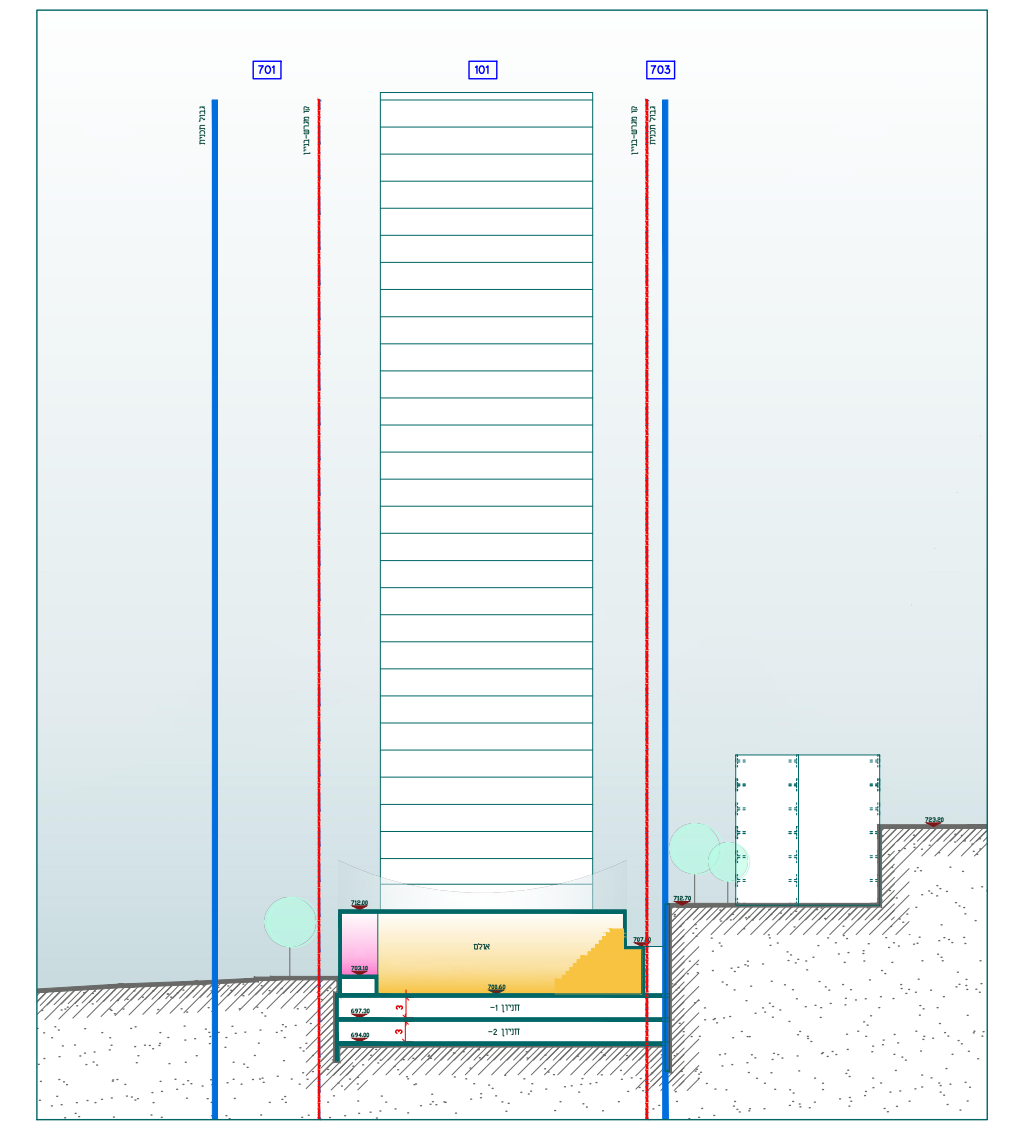

חתך 2-2 1 : 750

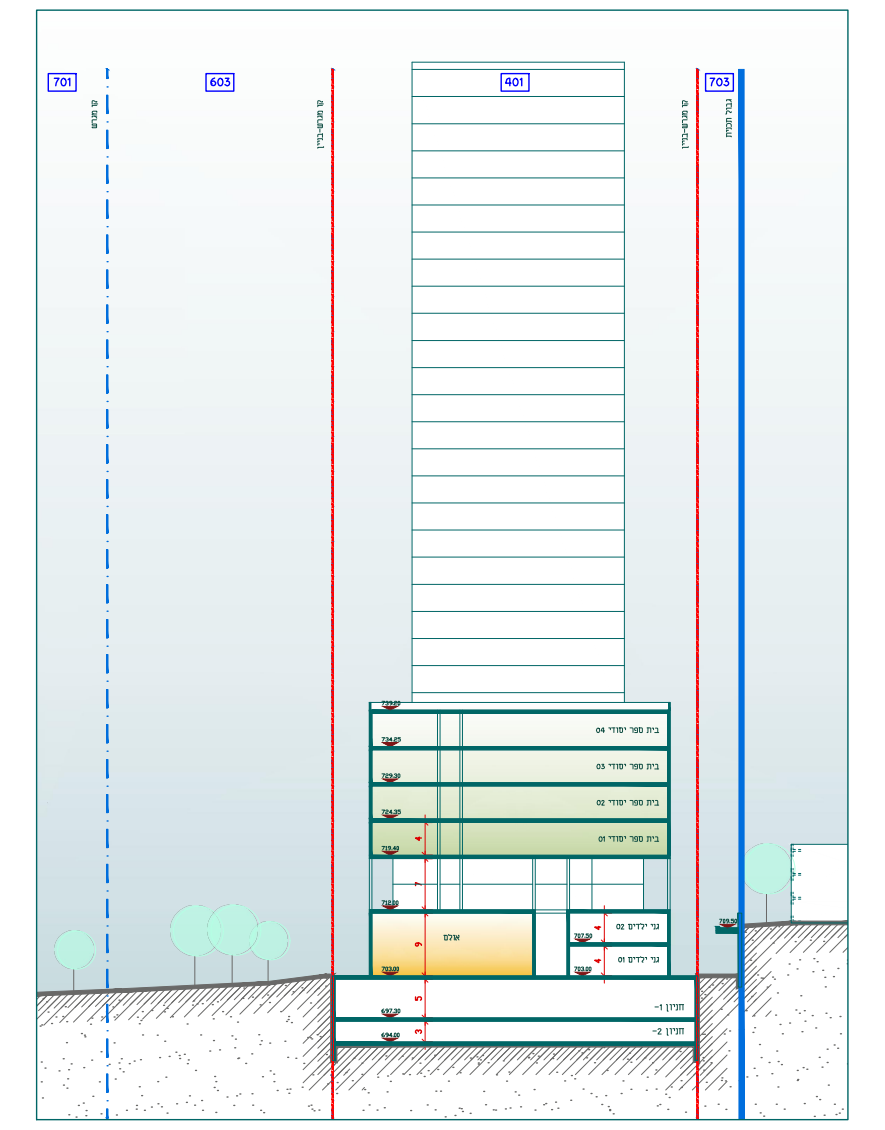

חתך 3-3 1 : 750

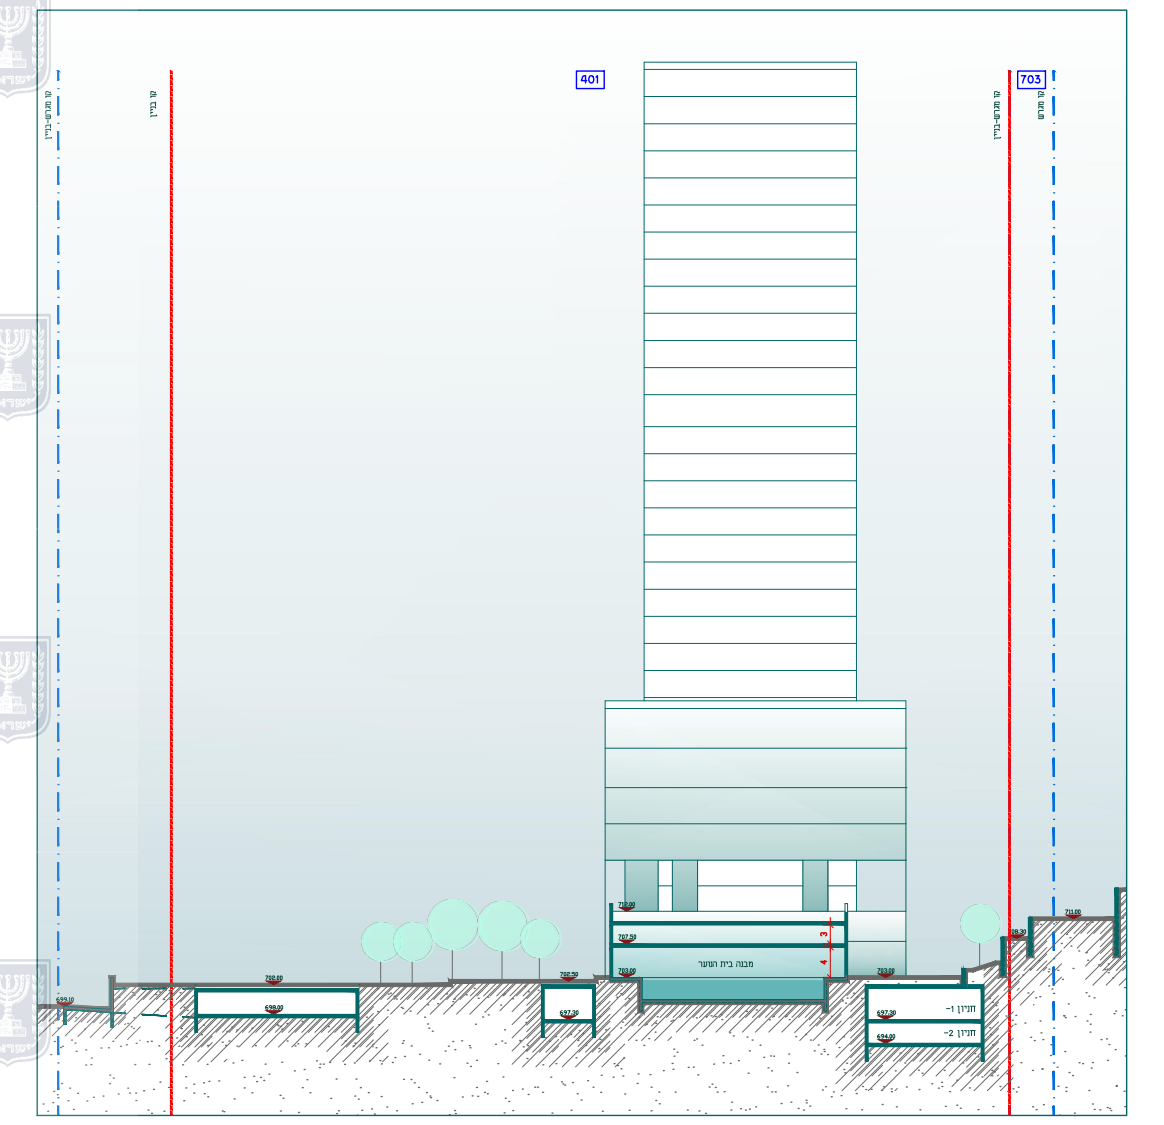

חתך 4-4 1 : 750

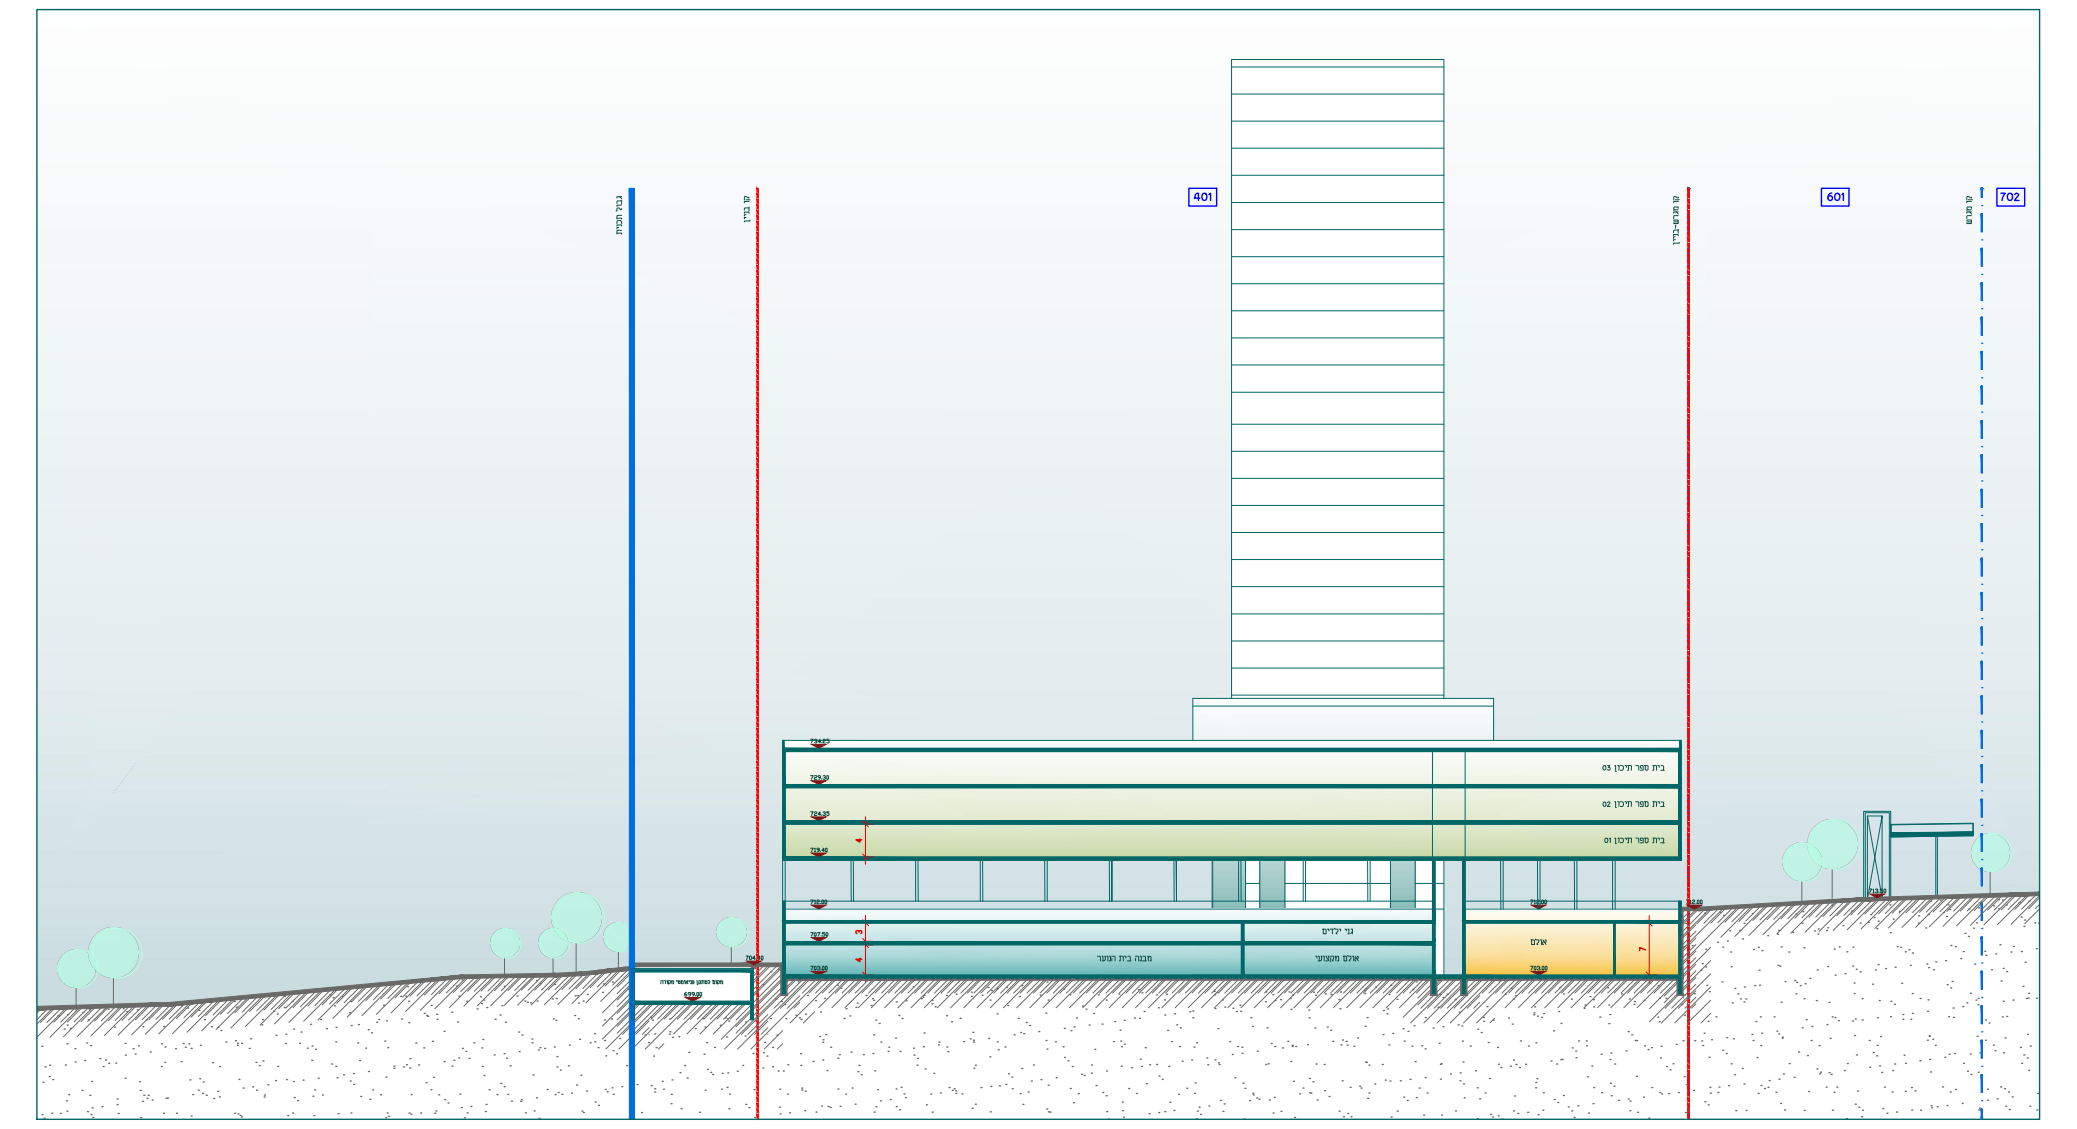

חתך 5-5 1 : 750

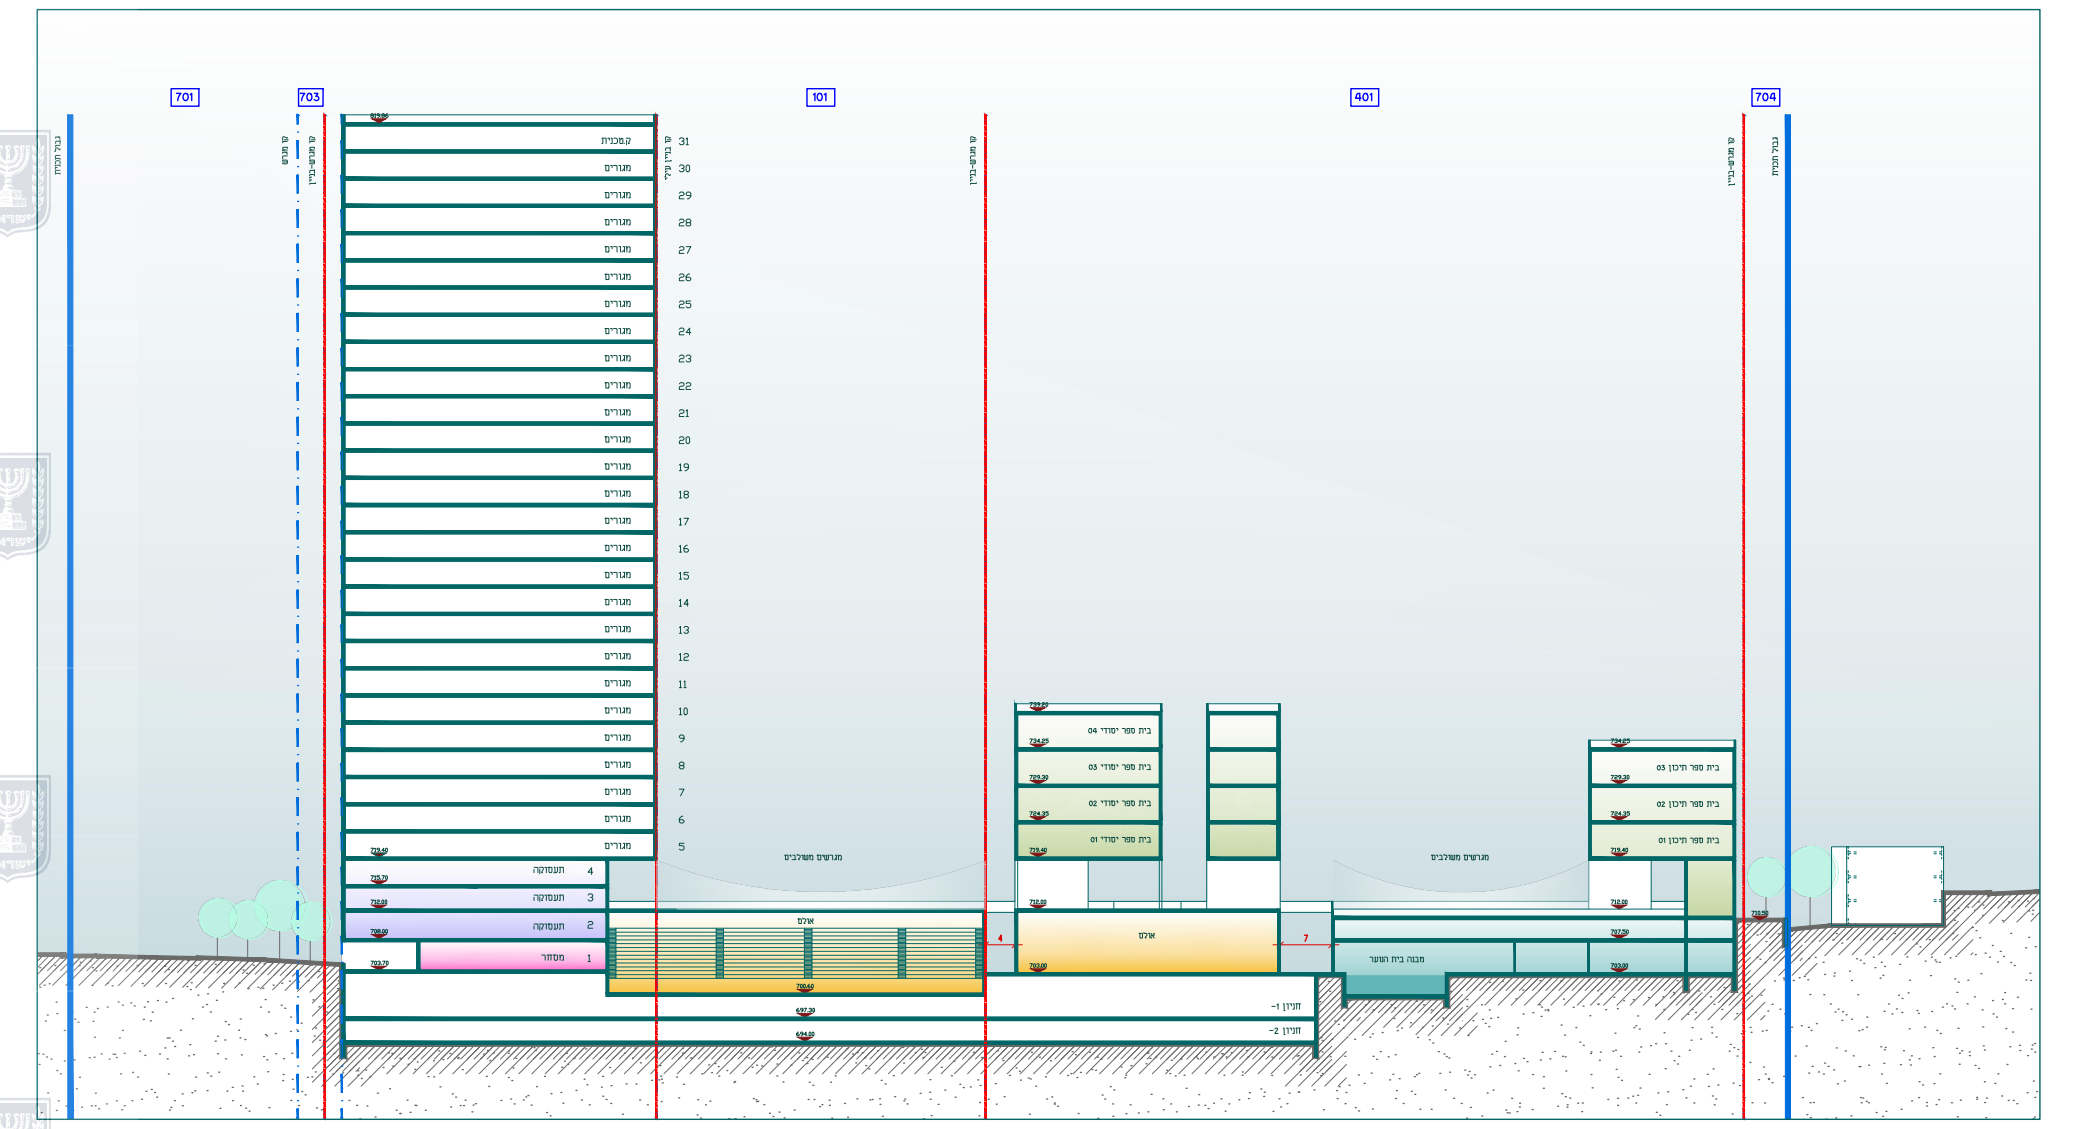

חתך 6-6 1 : 750