1312506_סט

מרחב תכנון מקומי ירושלים

תכנית מס' 9988

תכנית מתאר לשכונת רחביה וחלק משכונות קרית שמואל, טלביה ושערי חסד. ירושלים

תכנית מתאר מקומית הכוללת הוראות של תכנית מפורטת

נספח מס' 1 - בינוי ושימור

קנ"מ: 1 : 1250

חותמות מוסד התכנון :

מינהל התכנון - מחוז ירושלים
חוק התכנון והבנייה, תשכ"ה - 1965
אישור תכנית מס' ________
הועדה המחוזית לתכנון ולבניה החליטה
ביום ________ לאשר את התכנית
☐ התכנית לא נקבעה טעונה אישור שר
☐ התכנית נקבעה טעונה אישור שר
מנהל מינהל התכנון   יו"ר הועדה המחוזית

שלב: מילוי תנאים למתן תוקף   **מהדורה :** 10   **תאריך :** 28.09.2016

שמות וחתימות :

עורך התכנית	שם: נ.מלצר ג.איגרא א.כהן אדריכלים		חותמה:
	כתובת: ג.מ.י. הגן הטכנולוגי ירושלים		ג. מלצר ג. איגרא א. כהן אדריכלים שותפות מס' 540232387
	טלפון: 02-6797744	פקס: 02-6796640	דוא"ל: mic_arc@017.net.il

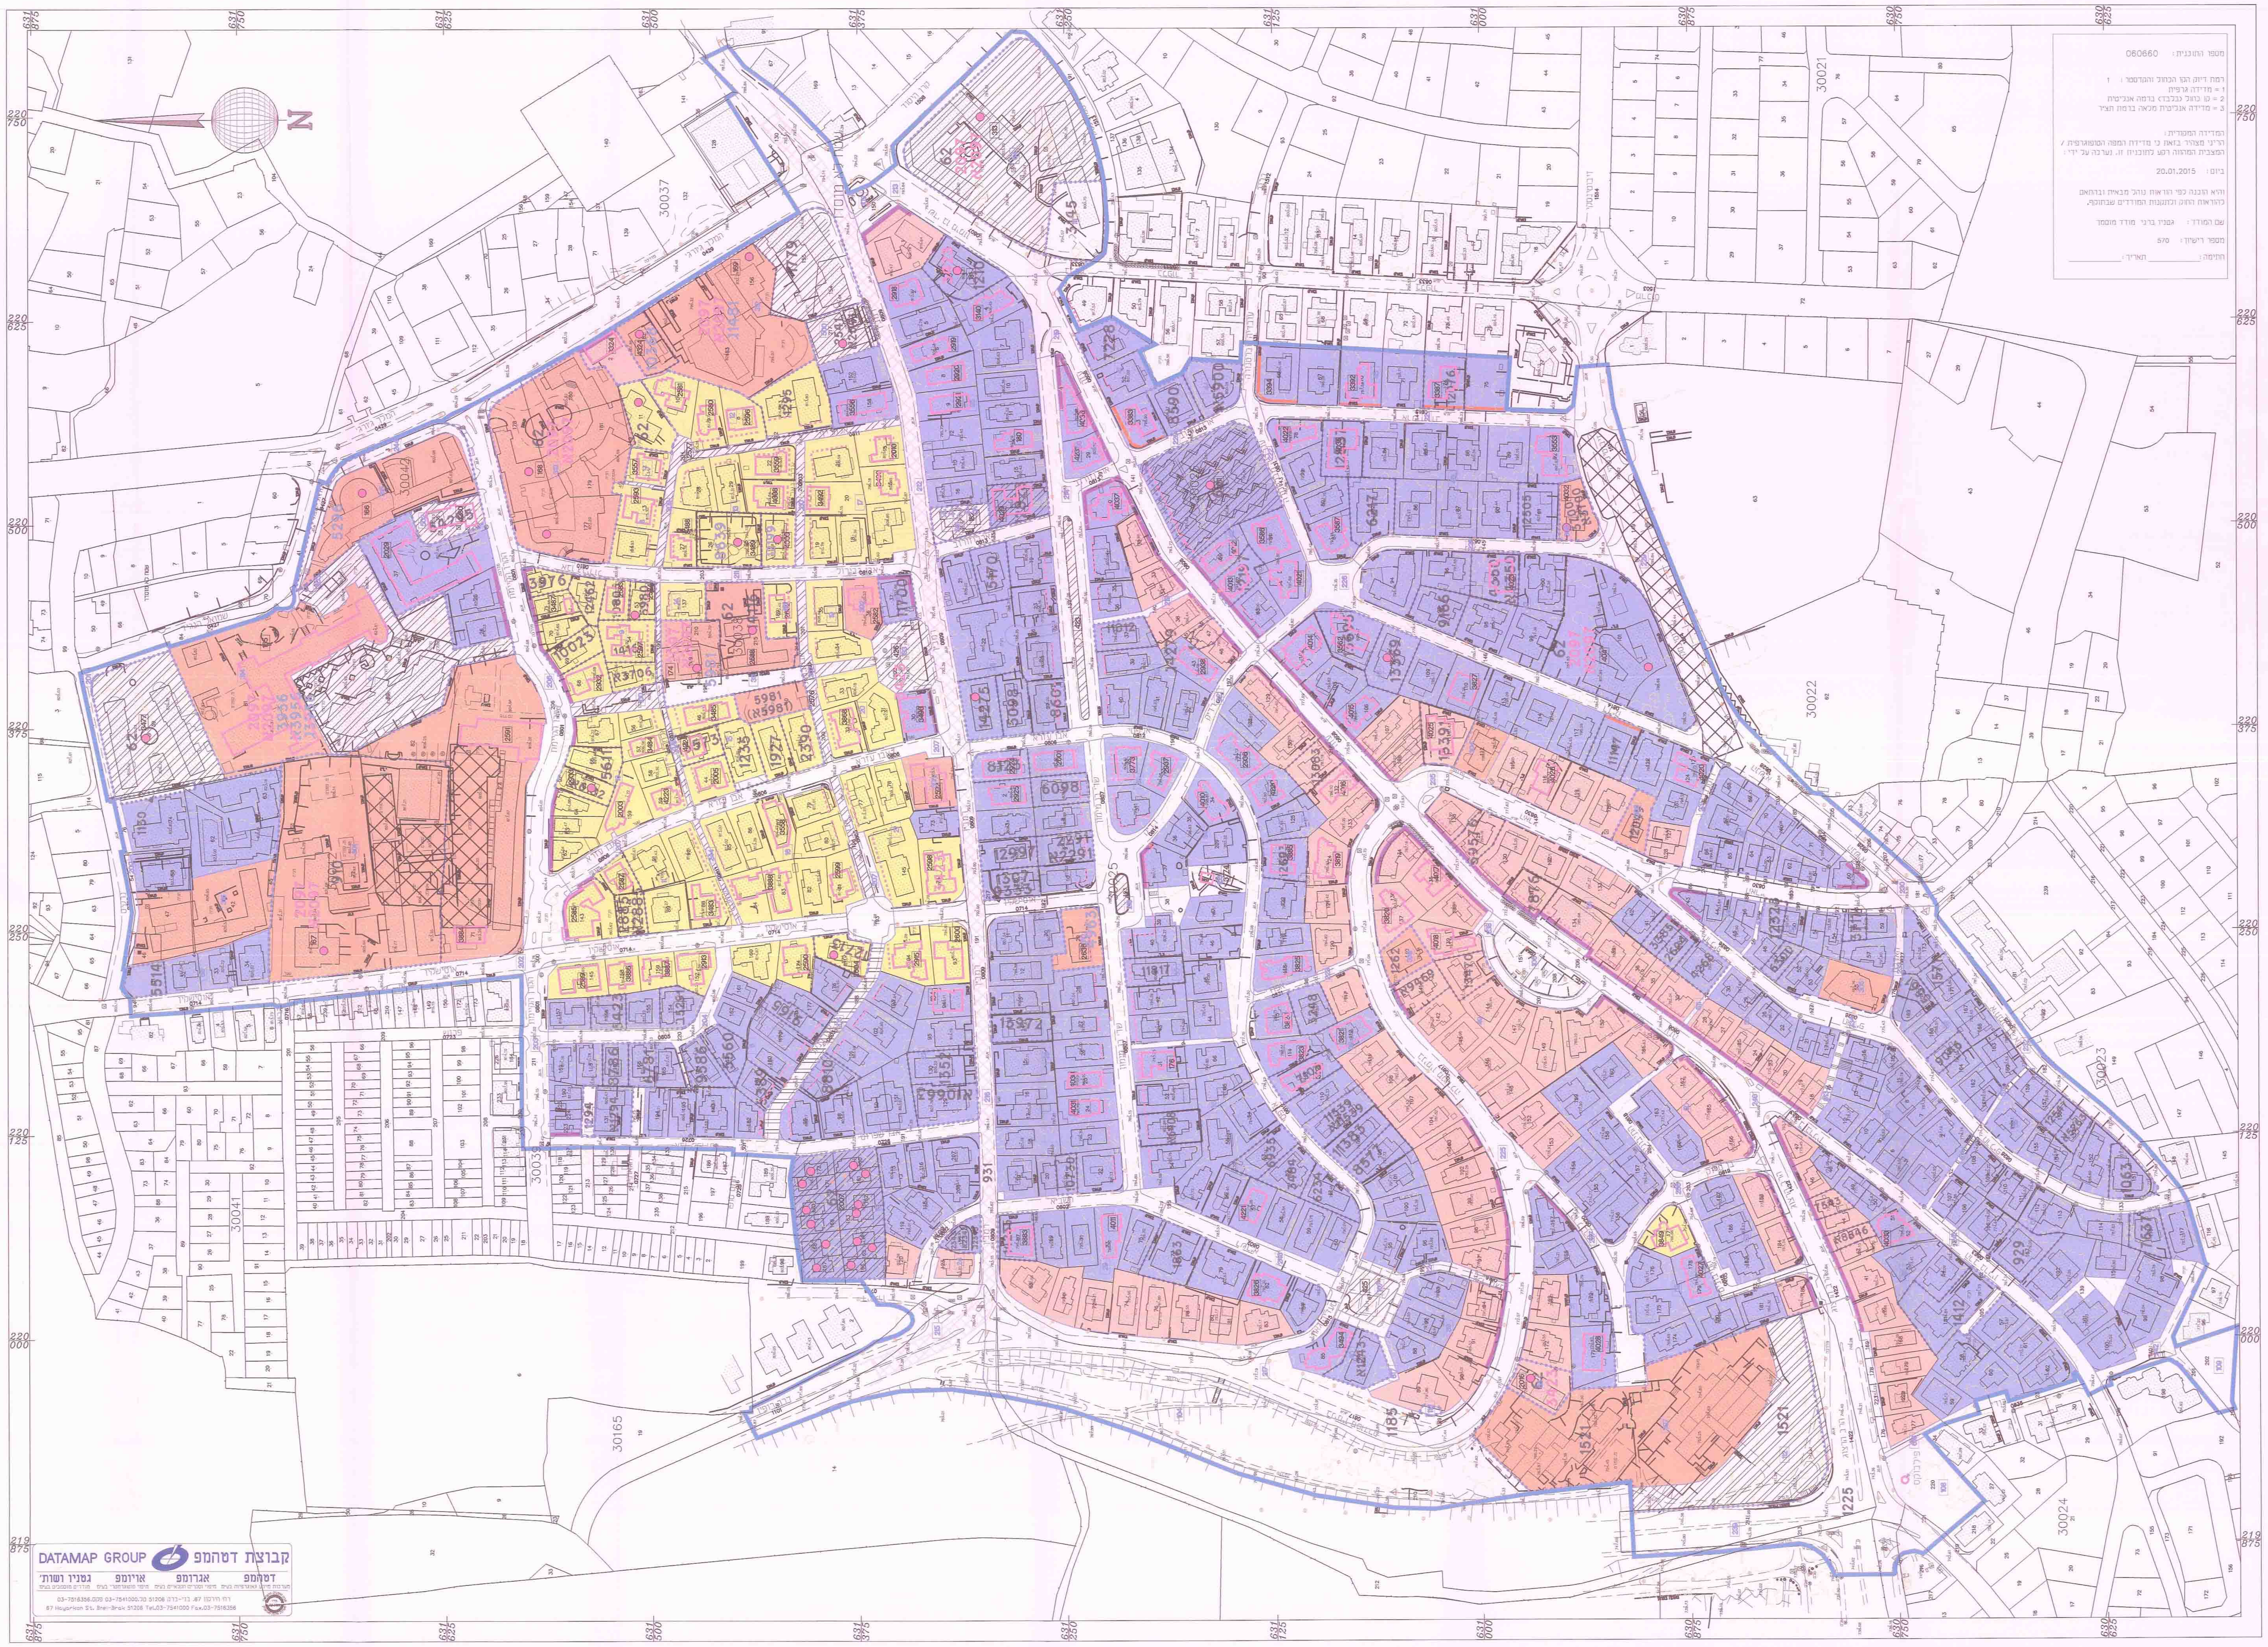

מספר התוכנית: 060660

רמת דיוק הקו הכחול והקדסטר : 1
1 = מדידה גרפית
2 = קו כחול (בלבד) ברמה אנליטית
3 = מדידה אנליטית מלאה ברמת תציר

המדידה המקורית:
הריני מצהיר בזאת כי מדידת המפה הטופוגרפית / המצבית המהווה רקע לתוכניות זו, נערכה על ידי:

ביום: 20.01.2015

והיא הוכנה כפי הוראות נוהל מבאית ובהתאם כהוראות החוק ולתקנות המודדים שבתוקף.

שם המודד: גטניו ברני מודד מוסמך

מספר רישיון: 570

חתימה: ________ תאריך: ________

קבוצת דטהמפ DATAMAP GROUP

דטהמפ — מערכות מידע גאוגרפיות בע"מ
אגרומפ — מיפוי וסקרים חקלאיים בע"מ
אוירומפ — מיפוי פוטוגרמטרי בע"מ
גטניו ושות' — מודדים מוסמכים בע"מ

רח' הירקון 67, בני-ברק 51206 טל.03-7541000 פקס.03-7516356
67 Hayarkon St. Bnei-Brak 51206 Tel.03-7541000 Fax.03-7516356

מקרא:

גבול התכנית	▭
גבול תכנית מאושרת שתכנית זו משנה	┈
מספר תכנית קודמת שתכנית זו משנה	4321א
מספר תכנית קודמת שתכנית זו משנה הכוללת הוראות שימור	2097
אזור מגורים חדש א'	🟨
אזור מגורים חדש ב'	🟪
אזור מגורים חדש ג'	▭
מבנים ומוסדות ציבור	🟧
הוראות מיוחדות	▨
בניין קיים ומספרו ברחוב	▱
מספר גוש	גוש 30025
גבול גוש	▲▼▲
מספר חלקה	10
גבול חלקה	—
גבול תא שטח	▭
מספר תא שטח	000
חזית רחוב לשימור	┈
בנין לשימור הכולל אפשרות לתוספות בניה	▱
בניין / מתחם עם הוראות מיוחדות לשימור	●
מס' בניין לשימור	3492
גדר לשימור	━
חזית מסחרית	━
חניה תת קרקעית	⊠