תכנית מס' 9988

מרחב תכנון מקומי ירושלים

משרד הפנים
לשכת התכנון
06-2015
נתקבל

תכנית מתאר לשכונת רחביה וחלק משכונות קרית שמואל, טלביה ושערי חסד. ירושלים

תכנית מתאר מקומית הכוללת הוראות של תכנית מפורטת

תשריט

איחוד וחלוקה	סמכות ראשית	אופי התכנית
-	ועדה מחוזית	תכנית שניתן מכוחה להוציא היתרים

מחוז : ירושלים
מרחב תכנון מקומי : ירושלים
רשות מקומית : ירושלים

שטח התכנית : 647.28 דונם
קנה מידה: 1 : 1,250

גושים וחלקות בתכנית:

גוש	סוג הגוש	חלקות בשלמותן	חלקי חלקות
30022	מוסדר (רשום)	25	-
30023	מוסדר (רשום)	1,2,5-32,35-71,151-175, 177-180,182,185-207	181,208
30024	מוסדר (רשום)	40-54,57-58,60-62 98-102,105-117,132, 139-140,165-169,176-179, 181-182,201-202,220-223	24,34,59,133, 157,158,216
30025	מוסדר (רשום)	1-4,6-48,51-130,132-189 191-206,208-209,213 216-218,220	212-210
30026	מוסדר (רשום)	1-48,51-55,59-64,66-67, 70-71,74-75,78-124, 127-142,144-148,150-151	49,143,149
30027	מוסדר (רשום)	1	90
30036	לא מוסדר (גוש שומא)	-	107
30037	לא מוסדר (גוש שומא)	-	60,130
30038	לא מוסדר (גוש שומא)	2,8-23,25-37,40-46,50-59, 62-74,77-89,91-95,98-104 115-116,118-120,122-123 129-130,137,143-145 149-152,154-156,158-165 168-172,176-183,188-189 191,193-210,212-218	166,167
30039	לא מוסדר (גוש שומא)	131,143,145,152,169-154 174-182,190,194-195 218-220,223-225,227-228 300-301	211 (חלקת דרך)
30041	לא מוסדר (גוש שומא)	-	94
30042	לא מוסדר (גוש שומא)	25-26,31-34,36-37 39,42,44-47,54,57-59 62-64,71-77,80-83	41,84
30042	מוסדר (רשום)	2,3	-
30145	מוסדר (רשום)	-	37
30165	מוסדר (רשום)	-	2,14,16

חותמות מוסד התכנון :

חוק התכנון והבניה, התשכ"ה - 1965
משרד הפנים - מחוז ירושלים
הוועדה המחוזית החליטה ביום: 30.12.14
לאשר את התכנית
☐ התכנית לא נקבעה טעונה אישור השר
☒ התכנית נקבעה טעונה אישור השר

1965

שלב: מילוי תנאים למתן תוקף 24.6.15 **מהדורה :** 9 **תאריך :** 04.06.2015

שמות וחתימות :

	שם	כתובת	טלפון	פקס	דוא"ל	חתימה
יוזם התכנית	עיריית ירושלים, אגף תכנון עיר	כיכר ספרא 1, ירושלים	02-6297679			עיריית ירושלים עופר גרידינגר מנהל אגף תכנון עיר
מגיש התכנית	עיריית ירושלים, אגף תכנון עיר	כיכר ספרא 1, ירושלים	02-6297679			עיריית ירושלים עופר גרידינגר מנהל אגף תכנון עיר
עורך התכנית	נ.מלצר ג.איגרא א.כהן אדריכלים	ג.ת.י. הגן הטכנולוגי ירושלים	02-6797744	02-6796640	mlc_arc@017.net.il	נ. מלצר ג. איגרא א. כהן אדריכלים שותפות מס' 540222387
מודד	קבוצת דטהמפ מערכות מידע גאוגרפיות בע"מ	רח' הירקון 67 בני ברק 51206	03-7541000	03-7516356	orenb@datamap.com	

טבלת שטחים :

יעוד	במ"ר	ב- %	יעוד	במ"ר	ב- %
מצב מאושר			**מצב מוצע**		
אזור מגורים מיוחד	9,544	1.48%	דרך מאושרת	145,964	22.71%
אזור מגורים 1	979	0.15%	מגורים	389,813	60.64%
אזור מגורים 2	323,569	50.33%	שטח ציבורי פתוח	28,771	4.48%
אזור מגורים 2 מיוחד	27,591	4.29%	מבנים ומוסדות ציבור	74,535	11.59%
אזור מגורים 3	8836	1.37%	שביל	1,162	0.18%
אזור מגורים 3 מיוחד	3,363	0.52%	אזור מסחרי מיוחד	1,632	0.25%
מגורים ב'	9,204	1.43%	משרדים	895	0.14%
מגורים ב'2	641	0.10%	שטח למתקנים הנדסיים	75	0.01%
מגורים ב'3	869	0.14%			
מגורים ג'	4,992	0.78%			
מגורים ג'1	851	0.13%			
מגורים ג'2	865	0.13%			
מגורים ומסחר	580	0.09%			
שטח לבנין ציבורי	48,494	7.54%			
שטח לבניין ציבורי להשלמה	1,204	0.19%			
שטח למוסד	15,016	2.34%			
מבנים ומוסדות ציבור	2,654	0.41%			
מבנים ומוסדות ציבור לחינוך	713	0.11%			
שטח ציבורי פתוח	22,931	3.57%			
שטח פרטי פתוח	1,548	0.24%			
שטח למתקנים הנדסיים	75	0.01%			
אזור מסחרי מיוחד	1,632	0.25%			
משרדים	895	0.14%			
דרך קיימת ומאושרת	154,994	24.11%			
דרך פרטית	167	0.03%			
מעבר ציבורי להולכי רגל	640	0.10%			
סה"כ	**642,847**	**100**	**סה"כ**	**642,847**	**100**

תשריט סביבה קנ"מ 1: 20,000

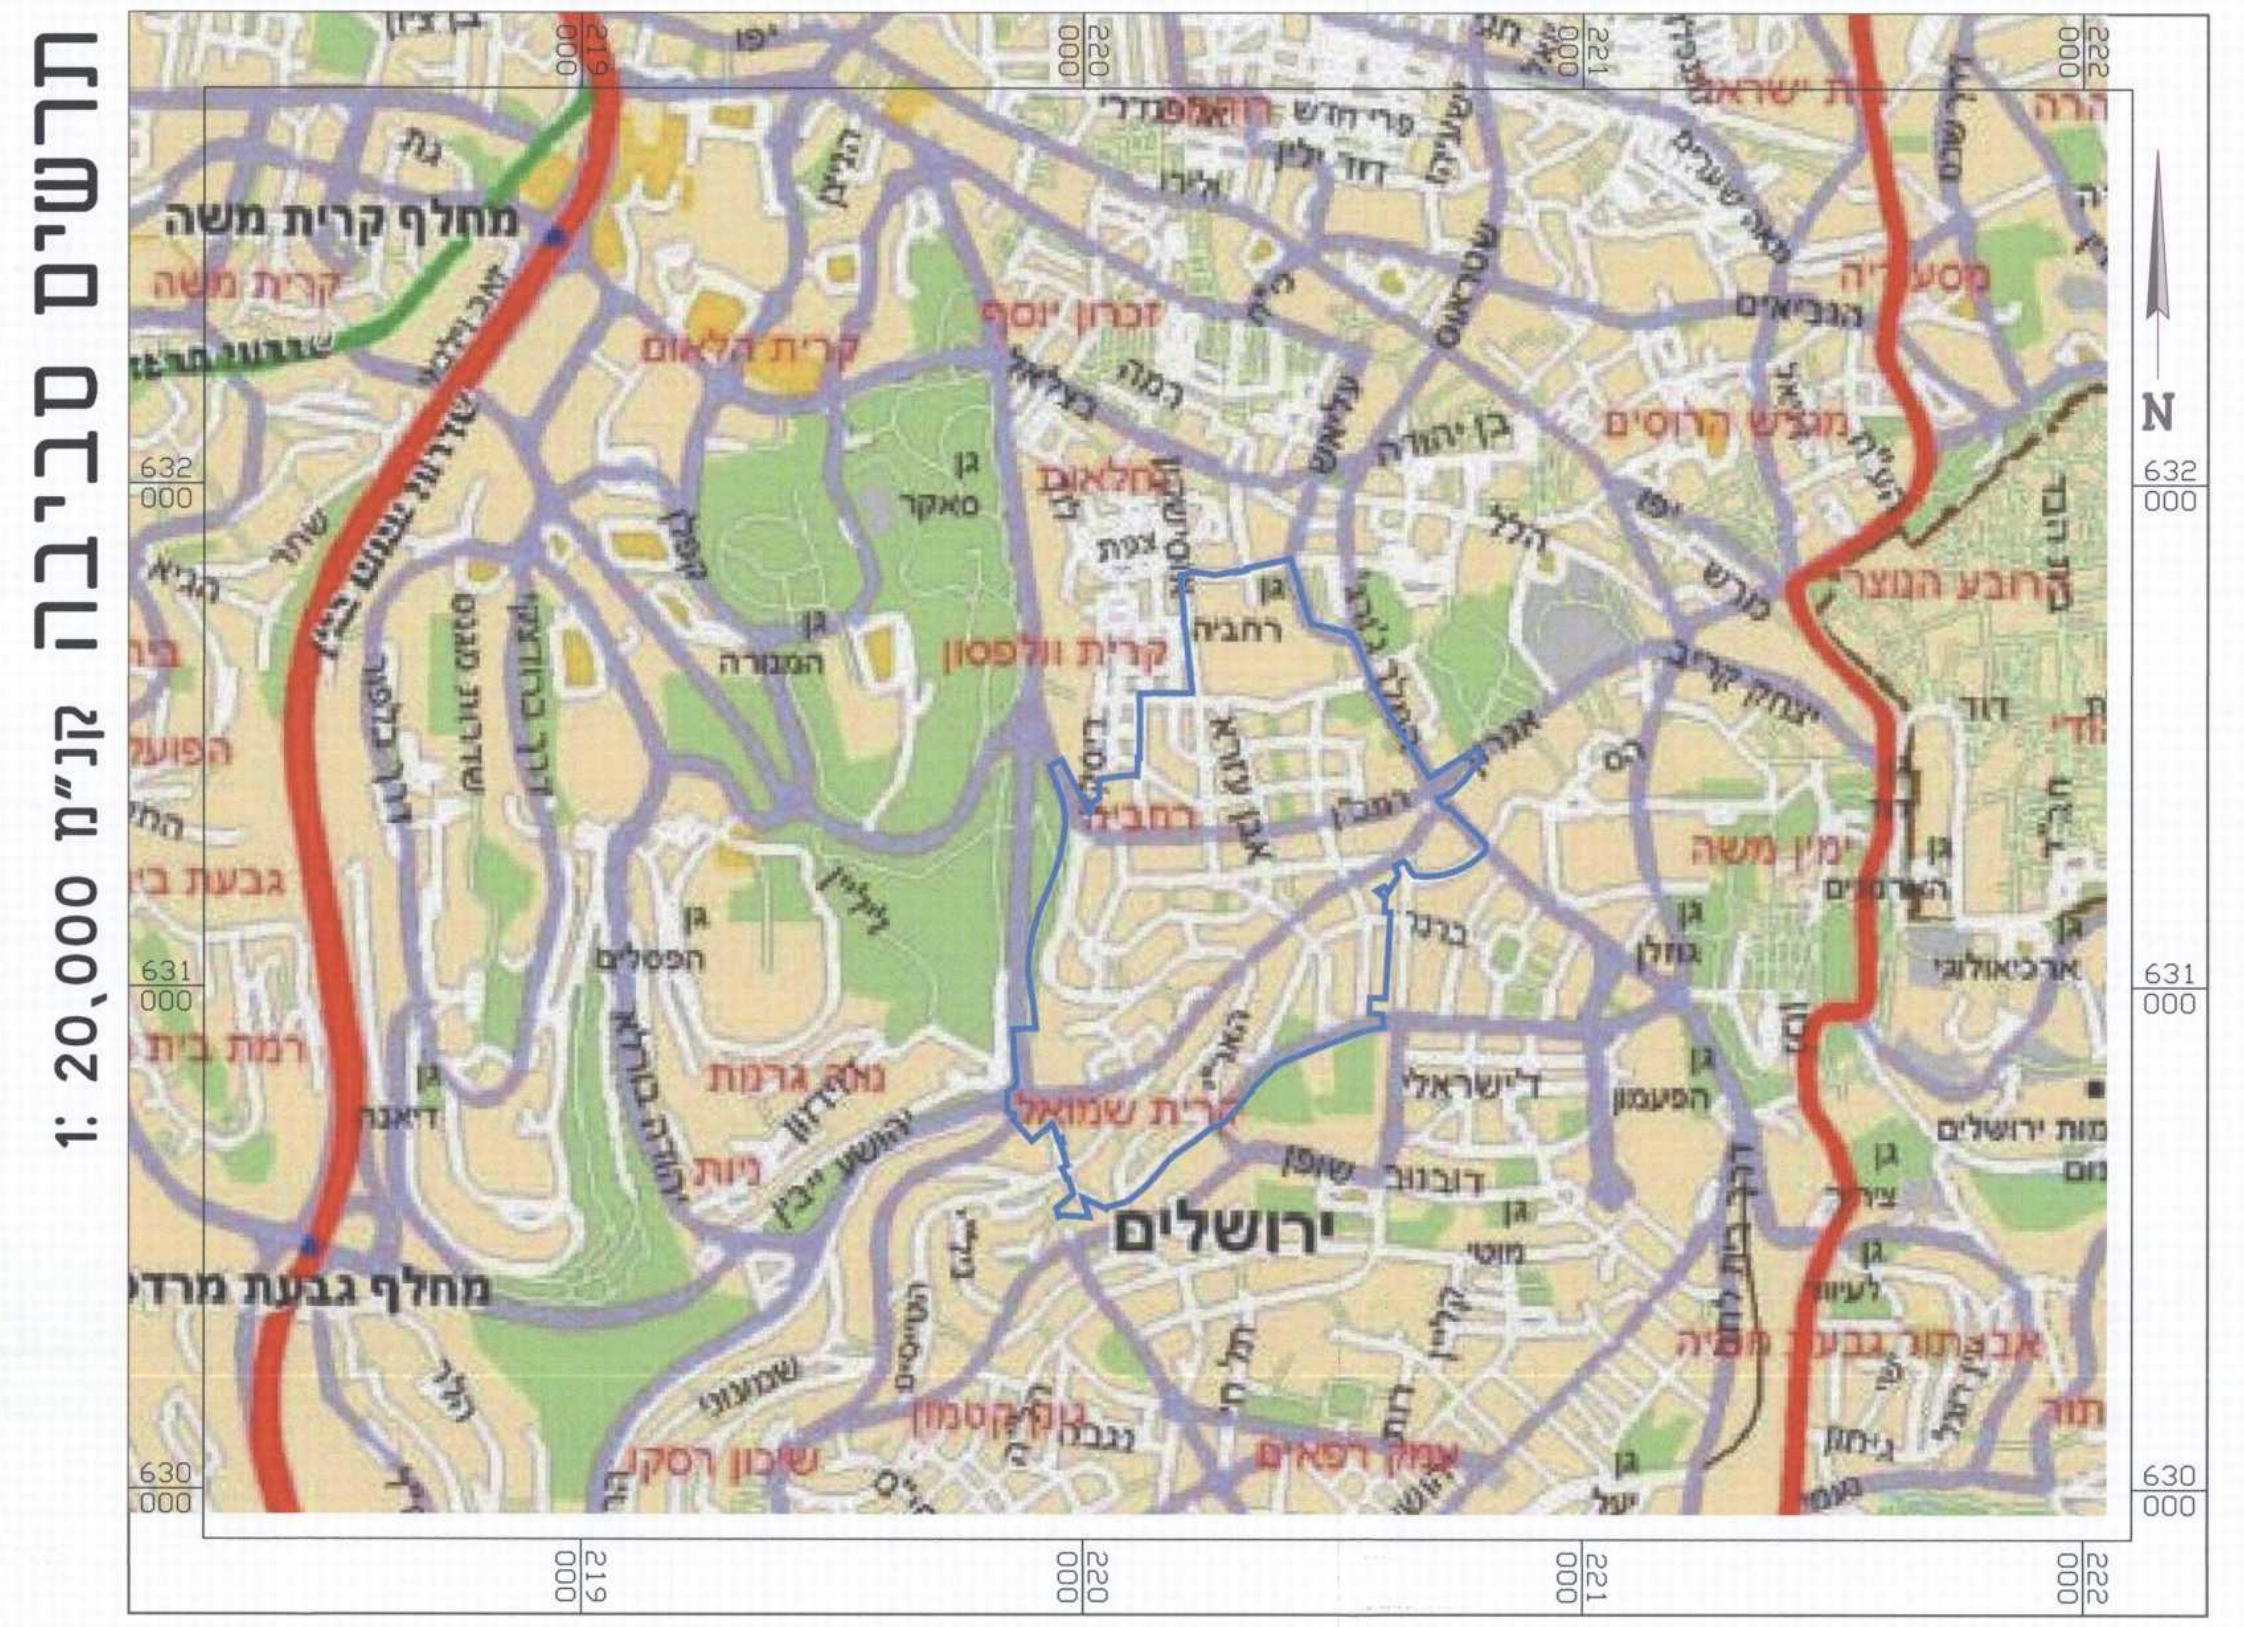

תשריט המקום קנ"מ 1: 5,000

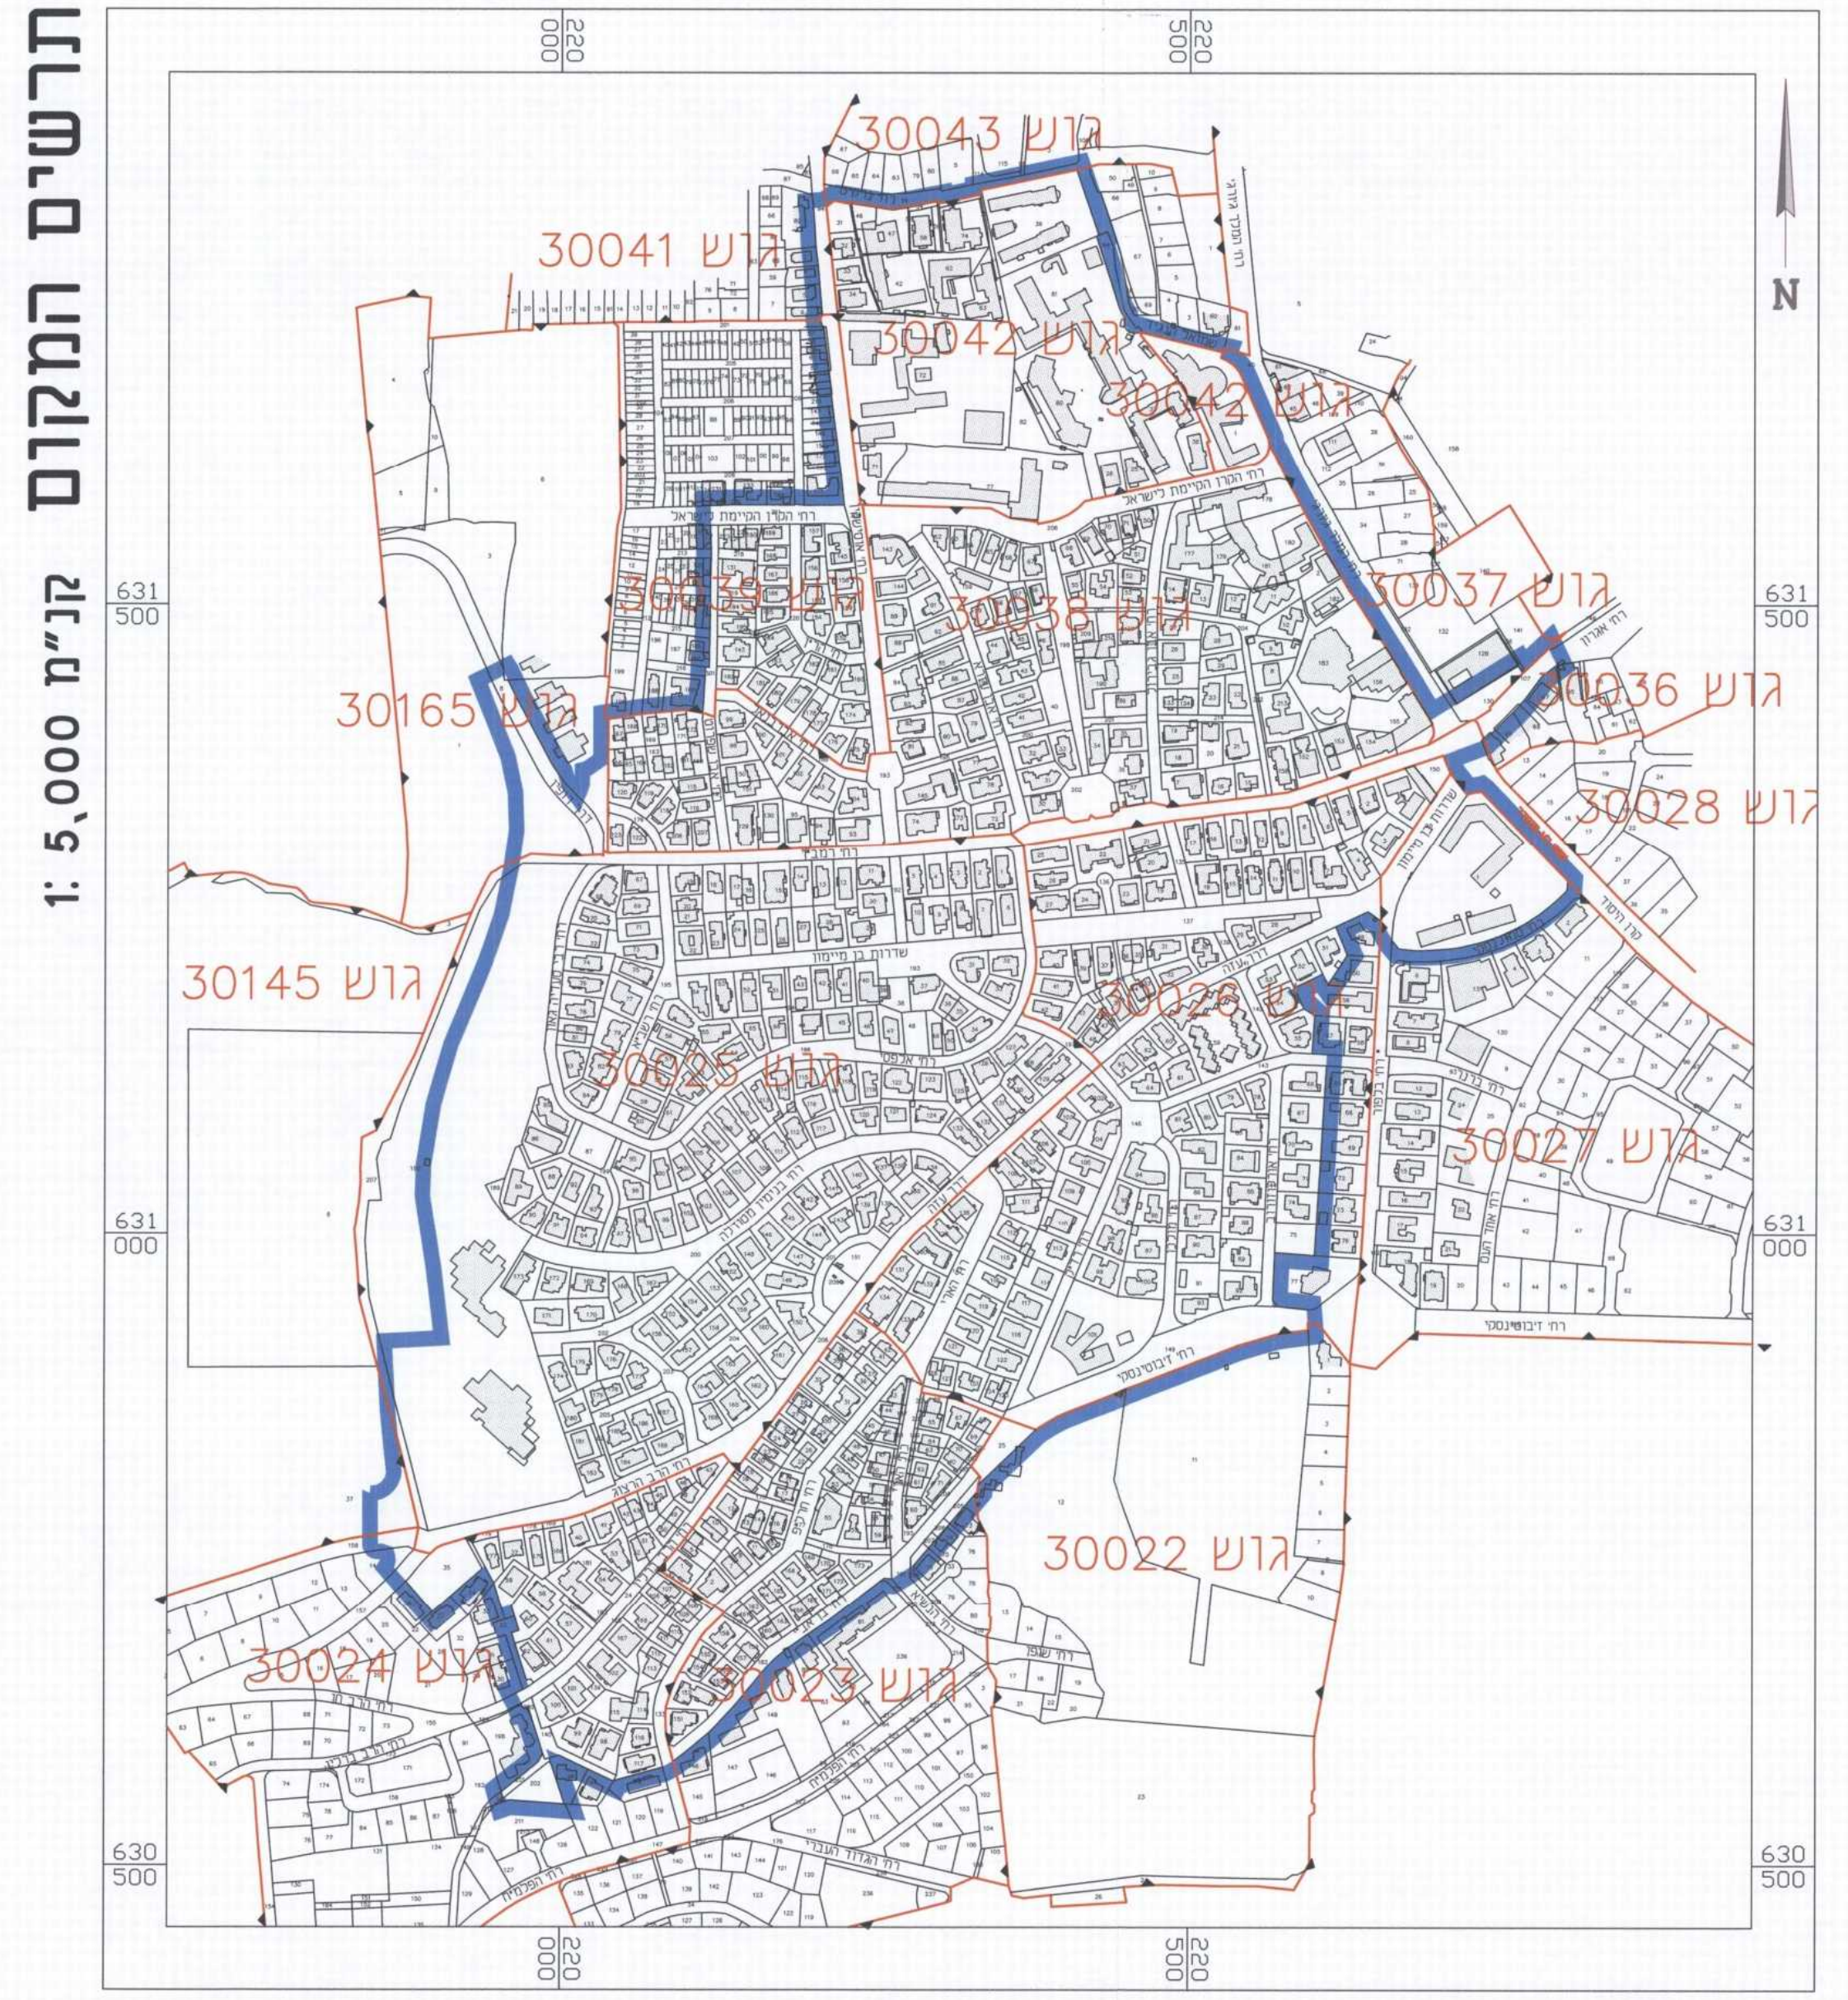

מקרא, מצב מאושר

גבול תכנית	
גבול תכנית מאושרת ומספרה	א4321
דרך קיימת ומאושרת	
מעבר ציבורי להולכי רגל	
דרך פרטית	
שטח פרטי פתוח	
שטח ציבורי פתוח	
אזור מגורים מיוחד	
אזור מגורים 1	
אזור מגורים 2	
אזור מגורים 2 מיוחד	
אזור מגורים 3	
אזור מגורים 3 מיוחד	
אזור מגורים 4 מיוחד	
מגורים ב'	
מגורים ב'2	
מגורים ב'3	
מגורים ג'	
מגורים ג'1	
מגורים ג'2	
מגורים ומסחר	
שטח למתקנים הנדסיים	
אזור מסחרי	
אזור מסחרי מיוחד	
משרדים	
שטח לבנין ציבורי	
שטח לבניני ציבור להשלמה	
שטח למוסד	
מבנים ומוסדות ציבור	
מבנים ומוסדות ציבור לחינוך	
שטח לבית מלון	
דרך גישה פרטית לחניה פרטית לפי תכנית 5886	
חניה פרטית	
זיקת הנאה למעבר רגלי	
מספר הדרך קו בניין רוחב הדרך	000 5 5 00
מספר חלקה	10
גבול חלקה	
מספר גוש	גוש 30025
גבול גוש	
בנין לשימור ע"פ תכנית מאושרת	●
בנין אופייני על פי תכנית מאושרת	●
עץ לשימור ע"פ תכנית מאושרת	⊙
בנין להריסה	
גדרות ושערים לשימור	
חזית בניין לשימור על פי תכנית 8639	
חזית מסחרית	
חזית לשימור	
הוראות מיוחדות	

מצב מאושר קנ"מ 1: 1,250

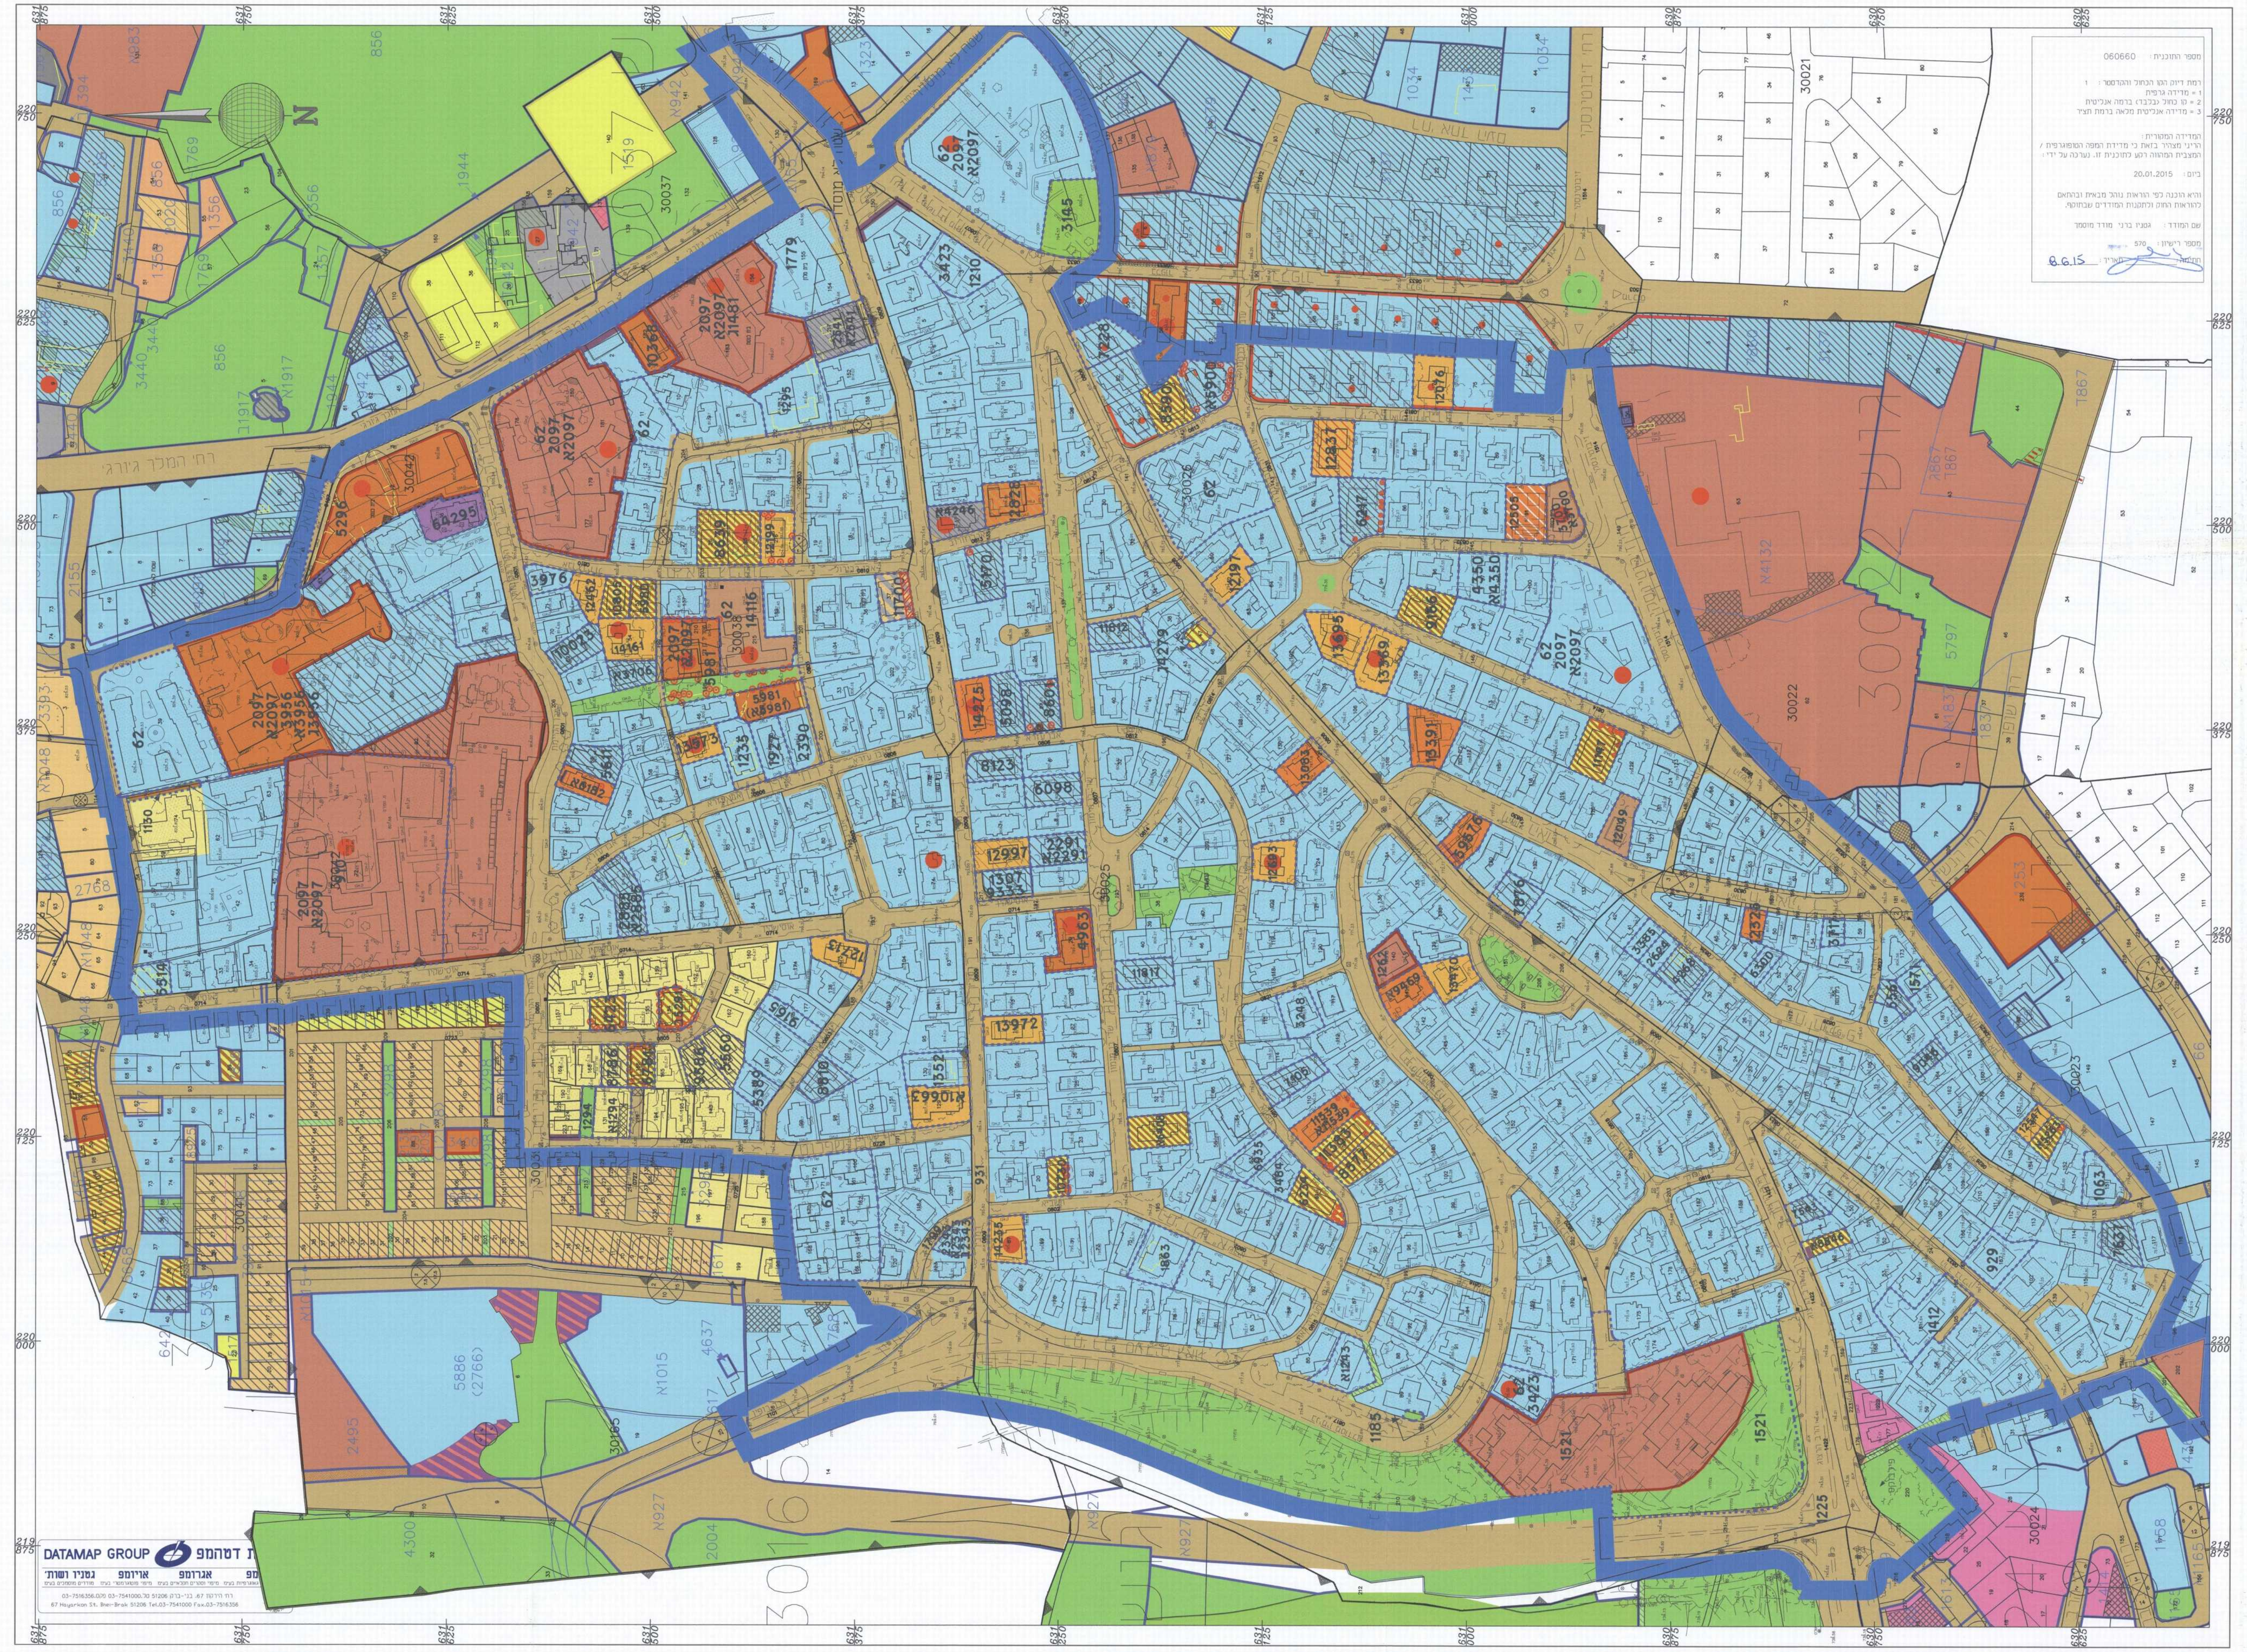

מספר התוכנית: 060660

רמת דיוק הקו הכחול והקדסטר : 1
1 = מדידה גרפית
2 = קו כחול (בלבד) ברמה אנליטית
3 = מדידה אנליטית מלאה ברמת תציר

המדידה המקורית :
הריני מצהיר בזאת כי מדידת המפה הטופוגרפית / המצבית המהווה רקע לתוכנית זו, נערכה על ידי :

ביום: 20.01.2015

והיא הוכנה לפי הוראות נוהל מבאית ובהתאם להוראות החוק ולתקנות המודדים שבתוקף.

שם המודד : גטניו ברני מודד מוסמך

מספר רישיון : 570

חתימה: ______ תאריך: ______

DATAMAP GROUP קבוצת דטהמפ

מקרא, מצב מוצע

גבול תכנית	
גבול תכנית קודמת שתכנית זו משנה	
מספר תכנית קודמת שתכנית זו משנה	א4321
דרך מאושרת	
דרך לביטול	
מגורים	
מבנים ומוסדות ציבור	
מסחר	
שטח ציבורי פתוח	
משרדים	
שביל	
מתקנים הנדסיים	
הוראות מיוחדות	
חניה תת קרקעית	
מנהרה / מעבר תחתי	
בניין קיים ומספרו ברחוב	6
חזית מסחרית	
גדר לשימור	
מבנה עם הוראות שימור	
עץ לשימור	
מספר גוש	גוש 30025
גבול גוש	
מספר חלקה	10
גבול חלקה	
גבול תא שטח	
מספר תא שטח	33

מצב מוצע קנ"מ 1: 1,250

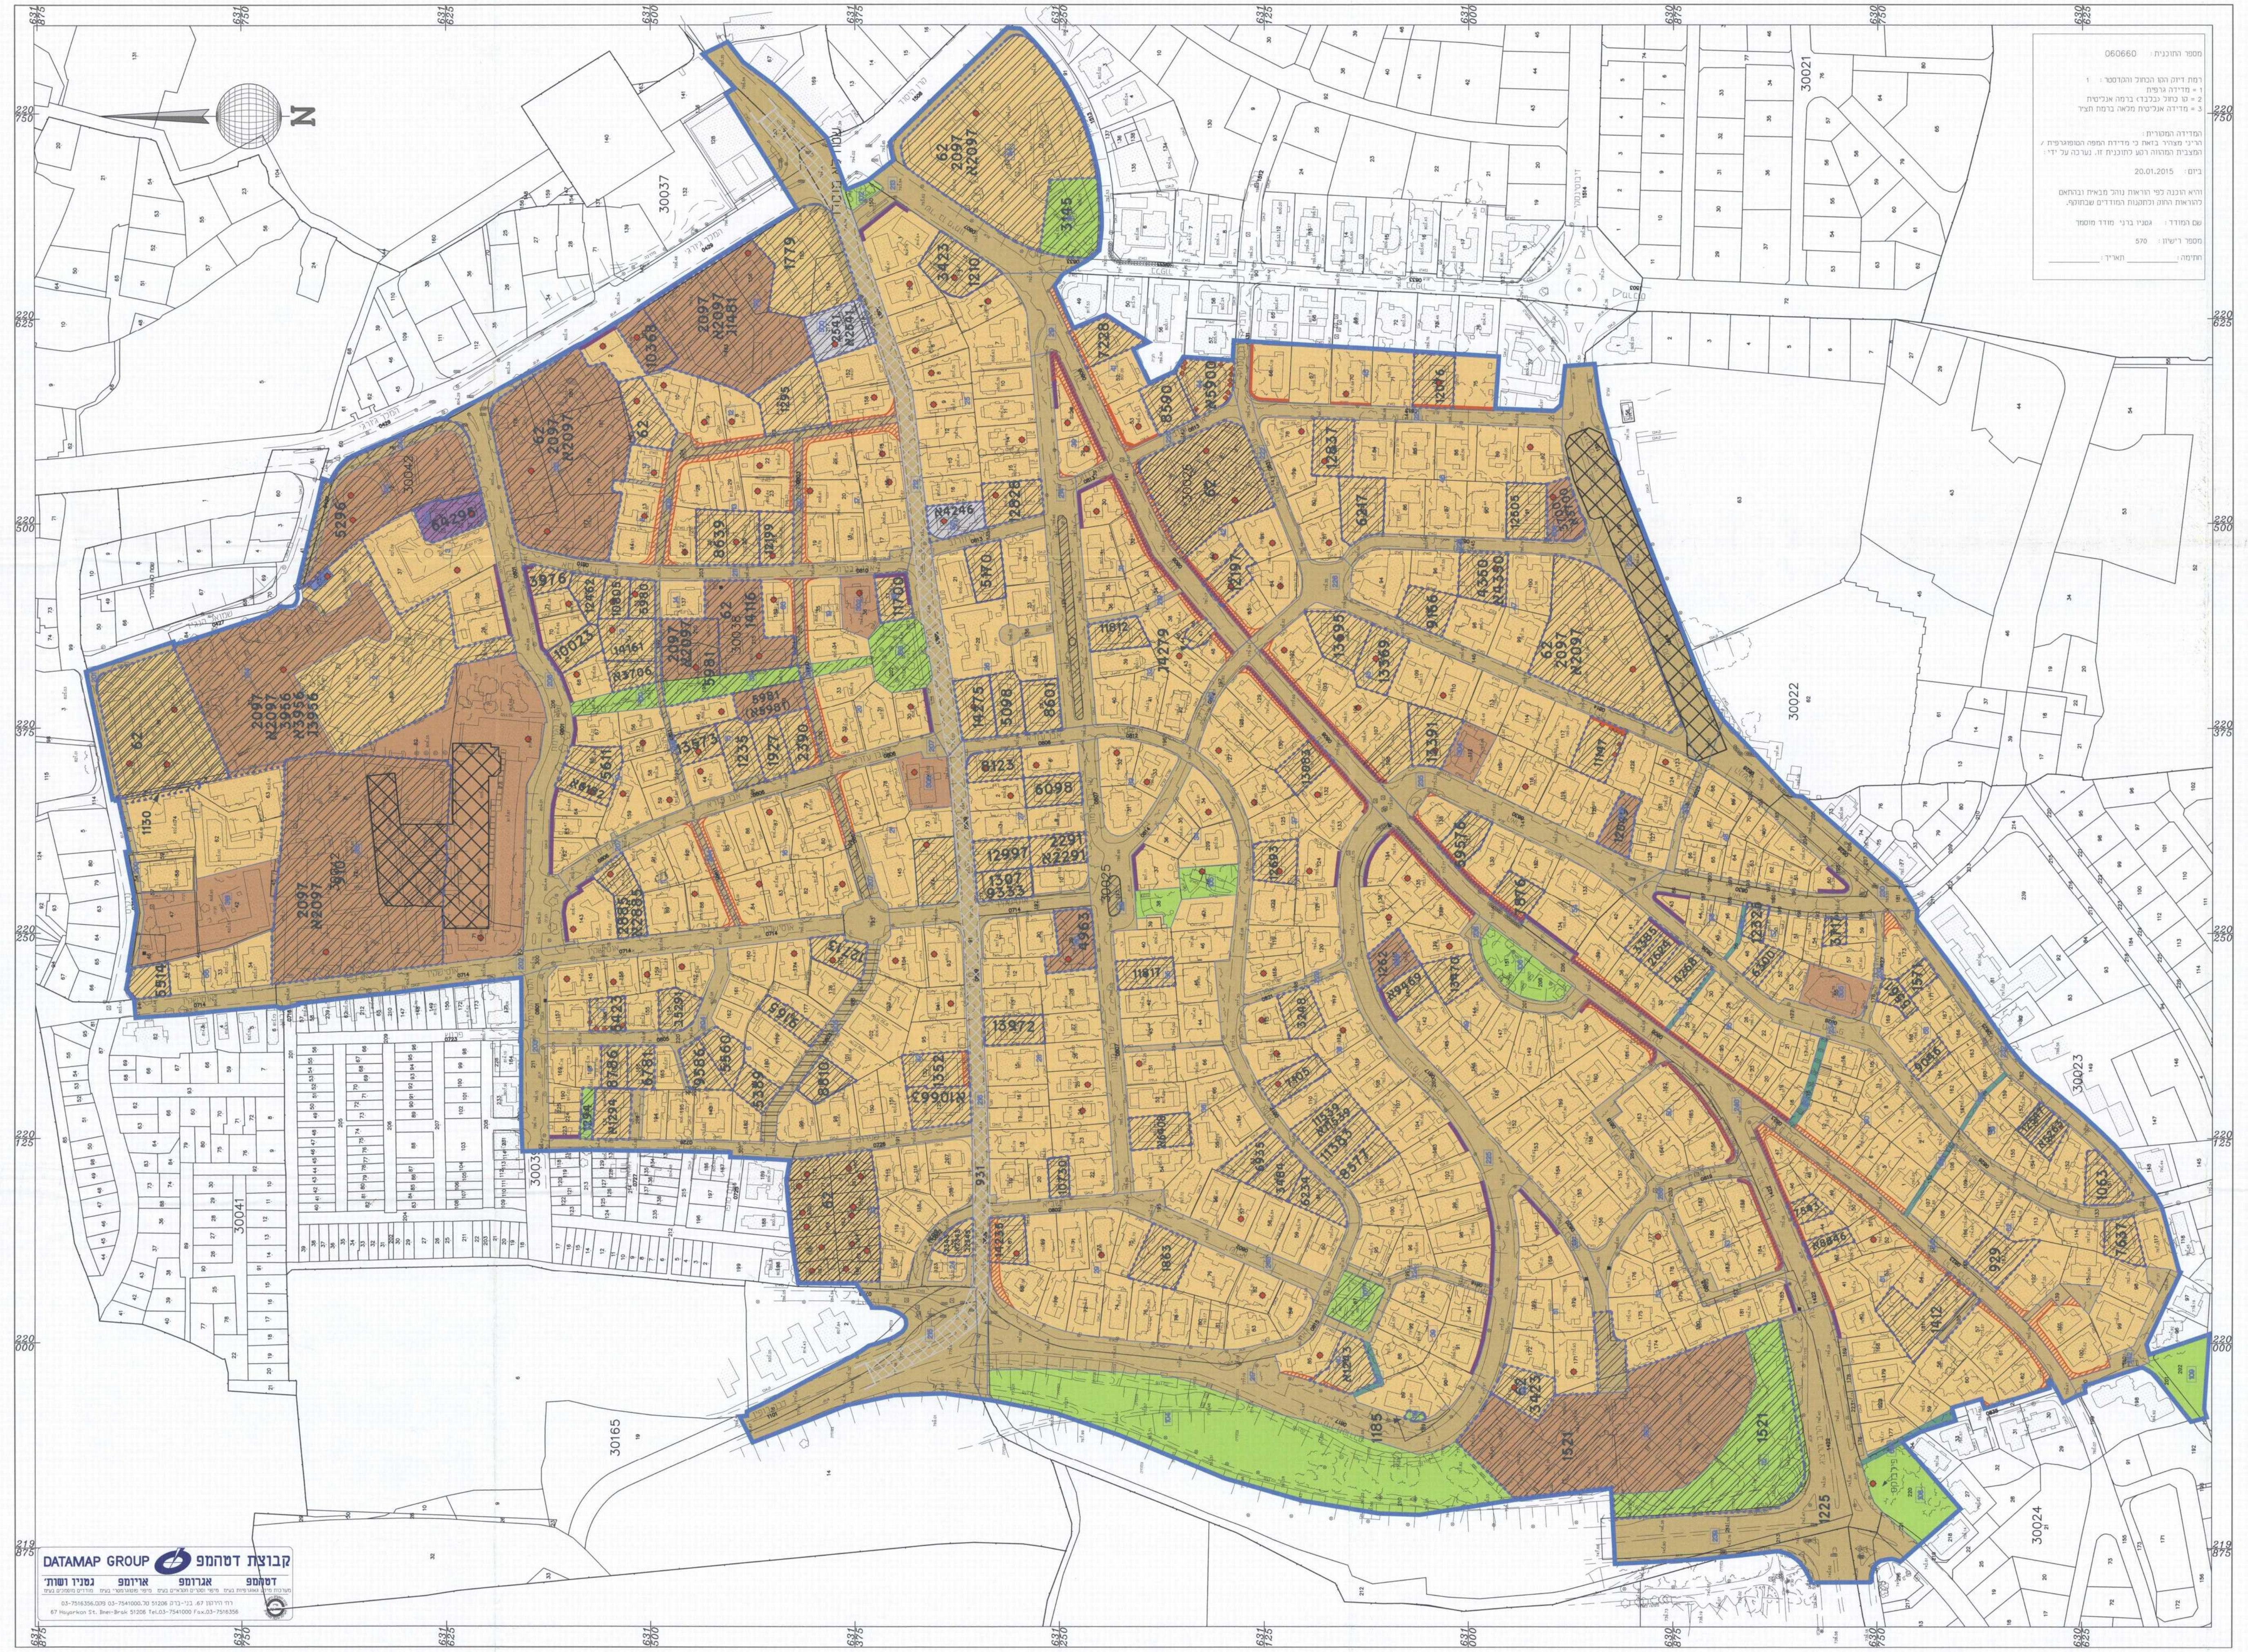

מספר התוכנית: 060660

רמת דיוק הקו הכחול והקדסטר : 1
1 = מדידה גרפית
2 = קו כחול (בלבד) ברמה אנליטית
3 = מדידה אנליטית מלאה ברמת תציר

המדידה המקורית :
הריני מצהיר בזאת כי מדידת המפה הטופוגרפית / המצבית המהווה רקע לתוכנית זו, נערכה על ידי :

ביום: 20.01.2015

והיא הוכנה לפי הוראות נוהל מבאית ובהתאם להוראות החוק ולתקנות המודדים שבתוקף.

שם המודד : גטניו ברני מודד מוסמך

מספר רישיון : 570

חתימה: ______ תאריך: ______

DATAMAP GROUP קבוצת דטהמפ