מינהל התכנון
חוק התכנון והבניה, התשכ"ה - 1965
מחוז ירושלים
הוועדה המחוזית החליטה ביום :
12/06/2025
להפקיד את התכנית
19/08/2026
יו"ר הוועדה המחוזית
תאריך
תכנית 101-1215656 15/07/2026 13:05:35 נספח סקר עצים ד"ם סקר עצים

סקר עצים - בני בתירא 7-9

מספר סקר	11-190
שם פרויקט	בני בתירא 7-9
שנה	2023
עיר	ירושלים
מקום	קטמונים
תכנית	סקר עצים
כתובת	בני בתירא 7-9
הוכן עבור	COSYCASA
איש קשר	ישראל חברת היתר
מייל	yisrael@heter.co.il



מבוא:

סקר העצים תועד ב- 27/03/2023 בכתובת בני בתירא 7-9, ירושלים.

סקר העצים הוכן לצורך היתר בניה.

חוות דעת זו הוכנה עלי ידי כמומחה המוכר ומאושר על ידי משרד החקלאות ועל פי תיקון 89 לחוק התכנון והבנייה ובהתאם להנחיית פקיד היערות.

תכניות הסקר מוגשות בקנ"מ על רקע מדידה (מצב קיים) ועל רקע בינוי (מצב מתוכנן).

סה"כ עצים שנסקרו	16		
	%	כמות	שווי בש"ח
שימור	13%	2	9,851
כריתה	56%	9	53,206
העתקה	0%	0	0

תכולת הסקר:

טבלת סקר עצים הכוללת המלצות להמשך טיפול
סיכום המלצות
טבלת פיצוי נופי
תכנית הסקר על רקע מדידה - מצב קיים (קנ"מ 1:250)
תכנית הסקר על רקע מצב מתוכנן (קנ"מ 1:250)


ארז קפלן
תכנון נוף | ליווי פרויקטים

תצ"א - מיקום האתר



ארז קפלן
תכנון נוף | ליווי פרויקטים

תכנית העמדה כללית ע"ג בינוי מתוכנן - להגדלת פרטים ראה תכניות מצורפות בקנה מידה

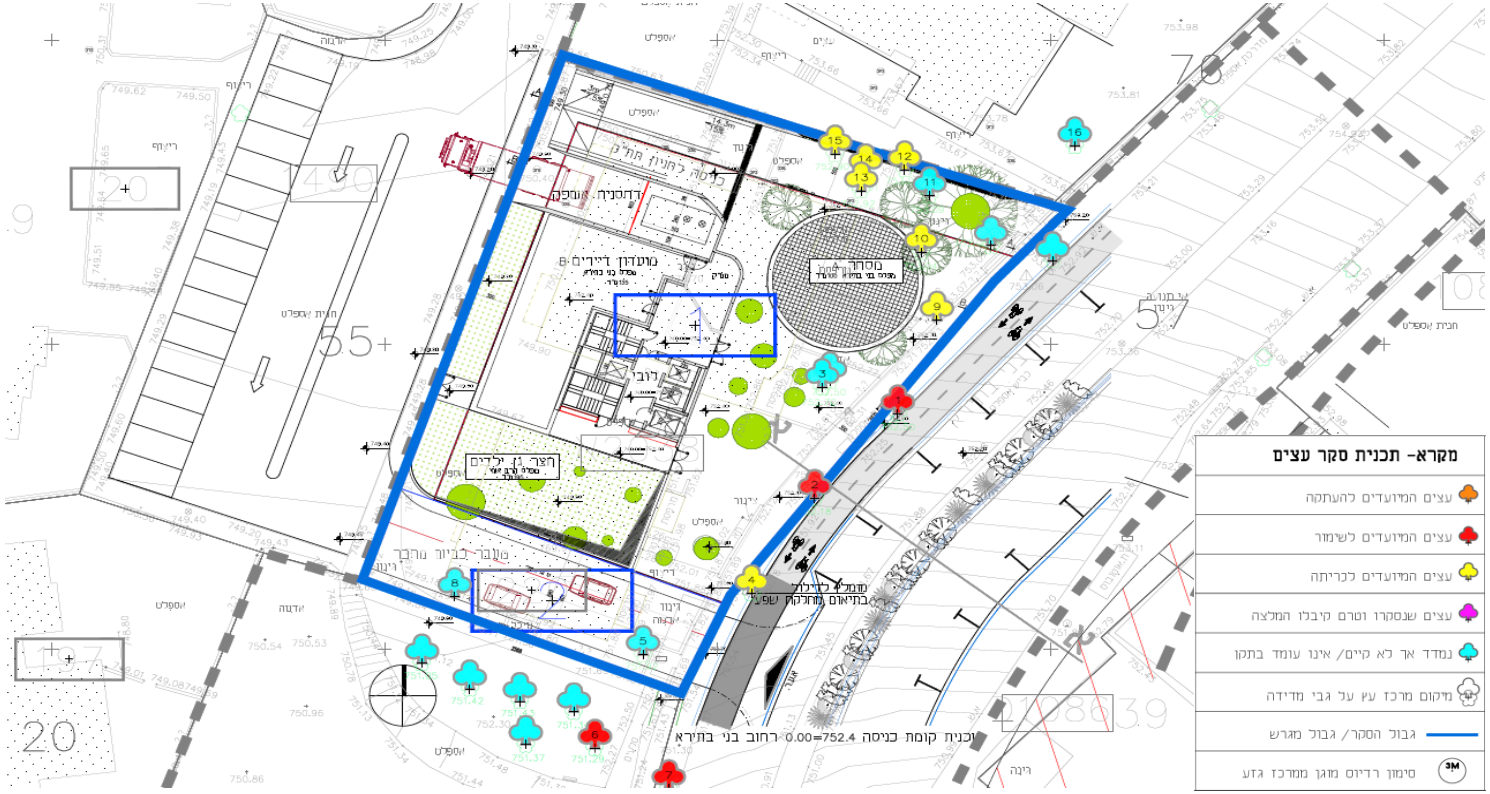

טבלת סקר עצים

מספר העץ/פוליגון	מין העץ/תיאור הפוליגון	כמות עצים	גובה העץ (מ')	קוטר גזע מרכזי (ס"מ)	מצב בריאותי (0-5)	מיקום העץ (0-5)	ערך מין העץ (0-5)	חופת העץ (0-5)	סך ערכיות העץ/פוליגון (0-20)	ערכיות העץ	אזור שורשים מוגן רדיוס במ'	שווי העץ (₪) ליחידה/פוליגון	הערות	המלצות	הסבר
1	Platanus orientalis - דולב מזרחי	1	12	60	3	5	4	3	15	ערכיות גבוהה	4.00	₪ 26,451	התחלת ריקבון בחתך גירדום ענף שלד.	כריתה	צמוד לדיפון חניון תת קרקעי
2	Platanus orientalis - דולב מזרחי	1	10	40	3	5	4	3	15	ערכיות גבוהה	3.00	₪ 11,756	על גבול מגרש, מעוצב 2ל ענפי שלד פיצול על בסיס גירדום הגזע, רקבונות	כריתה	צמוד לדיפון חניון תת קרקעי
3	Washingtonia - וושינגטוניה חסונה Robusta	1	15	50	4	4	2	2	12	ערכיות בינונית	3.00	₪ 6,048	הגזע מכוסה בקיסוס	לא נדרש ברישיון	
4	Platanus orientalis - דולב מזרחי	1	3	20	1	5	4	1	11	ערכיות בינונית	2.00	₪ 980	מחוץ לגבולות מגרש, הגזע גורדם בגובה 1.5 מ'.	כריתה	מולמץ להוצאה והחלפה בעץ בריא, ברדיוס כניסה לחניון. בתיאום מחקלת שפע

מספר העץ/פוליגון	מין העץ/תיאור הפוליגון	כמות עצים	גובה העץ (מ')	קוטר גזע מרכזי (ס"מ)	מצב בריאותי (0-5)	מיקום העץ (0-5)	ערך מין העץ (0-5)	חופת העץ (0-5)	סך ערכיות העץ/פוליגון (0-20)	ערכיות העץ	אזור שורשים מוגן רדיוס במ'	שווי העץ (₪) ליחידה/פוליגון	הערות	המלצות	הסבר
5	וושינגטוניה חסונה - Washingtonia Robusta	1	7	40	4	4	2	2	12	ערכיות בינונית	3.00	₪ 2,822	צמוד לגדר	לא נדרש ברישיון	
6	ברכיכיטון אוסטרלי - Brachychiton australis	1	4	25	3	5	3	1	12	ערכיות בינונית	2.00	₪ 3,238	מחוץ לגבולות מגרש, נוף דליל	שימור	
7	דולב מזרחי - Platanus orientalis	1	5	30	3	5	4	1	13	ערכיות בינונית	2.00	₪ 6,613	מחוץ לגבולות מגרש, גורדם בגובה 2 מ'	שימור	
8	בוקיצה נמוכה - Ulmus pumila	1	9	15	2	4	2	2	10	ערכיות בינונית	2.00	₪ 475	ספיח, גדל בחניה מתוך אספלט, גדל בנטייה.	לא נדרש ברישיון	
9	שסק יפני - Eriobotrya japonica	1	3	25	3	4	3	1	11	ערכיות בינונית	2.00	₪ 2,355	ספיח, גדל בין גדר לארון שירות.	כריתה	בחניון תת קרקעי מתוכנן
10	שסק יפני - Eriobotrya japonica	1	4	25	4	3	3	2	12	ערכיות בינונית	2.00	₪ 2,355	מעוצב על 2 גזעי שלד	כריתה	בחניון תת קרקעי מתוכנן
11	וושינגטוניה חסונה - Washingtonia Robusta	1	2	30	4	3	2	2	11	ערכיות בינונית	2.00	₪ 605	זריע צעיר	לא נדרש ברישיון	
12	שקד מצוי - Amygdalus communis	1	6	30	3	3	3	3	12	ערכיות בינונית	2.50	₪ 3,357	צמוד לגדר, גדל בנטייה	כריתה	בחניון תת קרקעי מתוכנן

מספר העץ/פוליגון	מין העץ/תיאור הפוליגון	כמות עצים	גובה העץ (מ')	קוטר גזע מרכזי (ס"מ)	מצב בריאותי (0-5)	מיקום העץ (0-5)	ערך מין העץ (0-5)	חופת העץ (0-5)	סך ערכיות העץ/פוליגון (0-20)	ערכיות העץ	אזור שורשים מוגן רדיוס במ'	שווי העץ (₪) ליחידה/פוליגון	הערות	המלצות	הסבר
13	Citrus limon - הדר הלימון	1	4	20	3	3	3	3	12	ערכיות בינונית	2.00	₪ 1,266	גדל בצפיפות לעץ שסק, עלווה דלילה	כריתה	בחניון תת קרקעי מתוכנן
14	Eriobotrya japonica - שסק יפני	1	7	25	4	3	3	2	12	ערכיות בינונית	2.00	₪ 2,355	חיוני	כריתה	בחניון תת קרקעי מתוכנן
15	Amygdalus communis - שקד מצוי	1	4	25	3	3	3	2	11	ערכיות בינונית	2.00	₪ 2,331	גדל בנטייה בזוית חדה, בחצר מגודרת נסקר מרחוק	כריתה	בחניון תת קרקעי מתוכנן
16	Washingtonia - וושינגטוניה חסונה Robusta	1	13	40	4	4	2	3	13	ערכיות בינונית	2.00	₪ 5,242	מחוץ לגבולות מגרש, בנטייה קלה	לא נדרש ברישיון	

סיכום המלצות

ערכיות גבוהה מאוד – עצים/פוליגונים בעלי נקוד ערכיות 17-20 נקודות, אשר בשל ערכיותם הגבוהה יש לשמרם במסגרת התכנון בכל דרך אפשרית.

ערכיות גבוהה– עצים/פוליגונים בעלי נקוד ערכיות 14-16 נקודות, אשר יש לבחון את היכולת לשמרם במסגרת התכנון העתידי.

ערכיות בינונית– עצים/פוליגונים בעלי נקוד ערכיות 7-13 נקודות, אשר ניתן לשמרם במסגרת התכנון העתידי ובלבד שאינם פוגעים במטרות התכנית ובתכליתה. לחילופין יומלץ לכרתם.

ערכיות נמוכה– עצים/פוליגונים בעלי נקוד ערכיות 0-6 נקודות, שהינם עצים מתים, מסוכנים, בתהליך ניווני או שאינם חייבים ברישיון כריתה, אשר מומלץ לכרתם באופן מיידי וללא קשר ו/או תלות בתכנון העתידי.

טבלת ריכוז ערכים לפי מיני העצים

מין העץ/פוליגון	ערכיות נמוכה	ערכיות בינונית	ערכיות גבוהה	ערכיות גבוהה מאוד	סה"כ עצים
דולב מזרחי - Platanus orientalis	0	2	2	0	4
וושינגטוניה חסונה - Washingtonia Robusta	0	4	0	0	4
ברכיכיטון אוסטרלי - Brachychiton australis	0	1	0	0	1
בוקיצה נמוכה - Ulmus pumila	0	1	0	0	1
שסק יפני - Eriobotrya japonica	0	3	0	0	3
שקד מצוי - Amygdalus communis	0	2	0	0	2
הדר הלימון - Citrus limon	0	1	0	0	1
סה"כ עצים	**0**	**14**	**2**	**0**	**16**

טבלת ריכוז ערכים לפי מיני העצים					
מין העץ/פוליגון	ערכיות נמוכה	ערכיות בינונית	ערכיות גבוהה	ערכיות גבוהה מאוד	סה"כ עצים
אחוז מסה"כ	**0%**	**88%**	**13%**	**0%**	**100%**

טבלת ריכוז המלצות לפי מיני העצים				
מין העץ/פוליגון	שימור	כריתה	העתקה	סה"כ עצים
דולב מזרחי - Platanus orientalis	1	3	0	4
וושינגטוניה חסונה - Washingtonia Robusta	0	0	0	0
ברכיכיטון אוסטרלי - Brachychiton australis	1	0	0	1
בוקיצה נמוכה - Ulmus pumila	0	0	0	0
שסק יפני - Eriobotrya japonica	0	3	0	3
שקד מצוי - Amygdalus communis	0	2	0	2
הדר הלימון - Citrus limon	0	1	0	1
סה"כ עצים	**2**	**9**	**0**	**11**
אחוז מסה"כ	**13%**	**56%**	**0%**	**69%**

סה"כ כריתות - פיצוי נופי		
מין העץ/תיאור הפוליגון	כמות עצים	שווי העץ (₪ ליחידה/פוליגון)
דולב מזרחי - Platanus orientalis	3	₪ 39,187
שסק יפני - Eriobotrya japonica	3	₪ 7,065
שקד מצוי - Amygdalus communis	2	₪ 5,688

סה"כ כריתות - פיצוי נופי		
מין העץ/תיאור הפוליגון	כמות עצים	שווי העץ (₪ ליחידה/פוליגון)
הדר הלימון - Citrus limon	1	₪ 1,266
סה"כ	**9**	**₪ 53,206**
אחוז מכל העצים	**56%**	**68%**


סה"כ שווי שימור עצים		
מין העץ/תיאור הפוליגון	כמות עצים	שווי העץ (₪ ליחידה/פוליגון)
ברכיכיטון אוסטרלי - Brachychiton australis	1	₪ 3,238
דולב מזרחי - Platanus orientalis	1	₪ 6,613
סה"כ	**2**	**₪ 9,851**
אחוז מכל העצים	**13%**	**13%**


סה"כ שווי העתקות		
מין העץ/תיאור הפוליגון	כמות עצים	שווי העץ (₪ ליחידה/פוליגון)
סה"כ	**0**	**0**
אחוז מכל העצים	**0%**	**0%**

הערות והנחיות

- אין לבצע עבודות בקרבת עצים לשימור. מילוי או חפירה במרחק הקטן 3 מטר מהגזע יהיה באישור הליווי הנופי.
- אין לבצע פעולות בעצים המיועדים לשימור כגון גיזום נוף, גיזום שורשים, הרמת נוף, חיגור או פגיעה בגזע.
- פעולות כמו גיזום נוף, גיזום סניטציה או הרמת נוף יהיו בתיאום הגוף המלווה ובהתאם למפרטי שימור עצים. ביצוע העבודה תעשה ע"י גוזם מומחה עם תעודה מטעם משרד החקלאות.
- חיתוך שורשים, פגיעה בגזע או כל פעולה אחרת שתגרום מוות לעץ תיחשב ע"פ חוק כריתה ללא היתר.
- מספור וסימון העצים בשטח ע"פ המלצות המצורפות יישום עם כניסת הקבלן לביצוע.
- גידור עצים לשימור יישום עם כניסת הקבלן לביצוע וטרם כניסת כלים כבדים לאתר. הגידור יהיה ע"פ פרט מצורף הכולל גדר איסכורית סביב הגזע בכל החזיתות בהם העץ חשוף עם שלט מנוילן המצורף " עץ לשימור".
- כריתה או העתקת עצים ללא רישיון בתוקף מפקיד יערות עירוני הינה עבירה פלילית והאחריות תהיה על המבצע או מי שמטעמו.
- יש לחכות שבועיים מרגע קבלת אישורי כריתה והעתקה לתוקף הביצוע בפועל.
- הכנת עצים להעתקה תהיה ע"פ מפרט אגרונומי שישלח לפי הצורך. ביצוע הכנה הכולל גיזומים להקטנת נוף יבוצעו ע"י גוזם מומחה מאושר.
- הסקר תקף לשנה מיום תיעוד העצים וסקירתם בשטח- ע"פ הנחיית הרשויות.
- מפרטים, פרטים והנחיות נוספות לשימור, העתקה וכריתת עצים ישלחו ע"פ הצורך.

פרטים מצורפים ע"פ הגדרות משרד החקלאות:

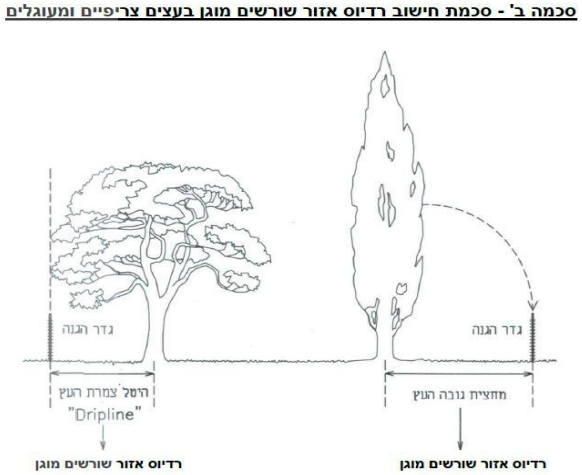

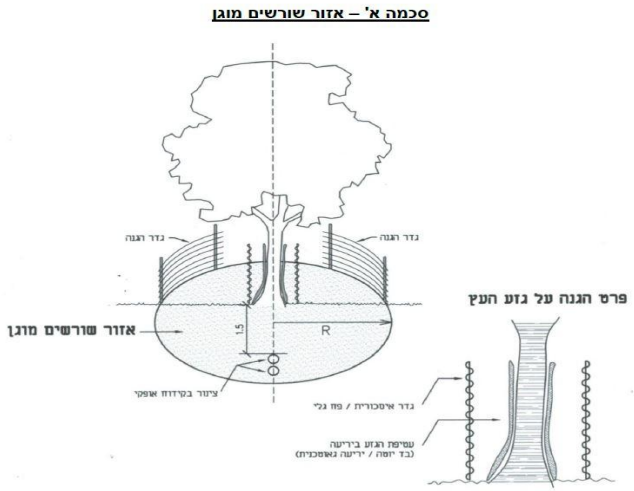

עץ לשימור
الشجر للحفظ

תמונות עצים

6



5



4



3



2



1



12



11




10



9



8

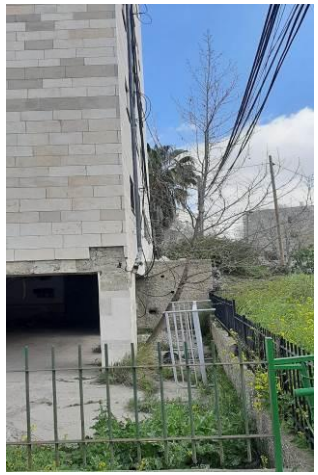

7




דוד מרכוס 5 ירושלים נייד: 0526408054 משרד: 02-6271190 מייל: erez@eklp.co.il

תמונות עצים

16



15

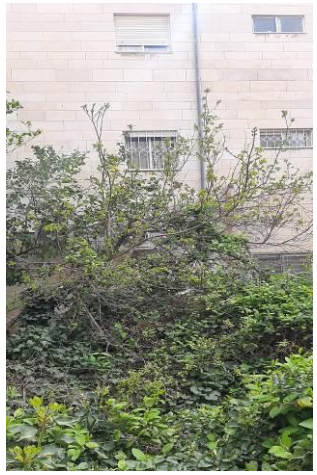

14



13



דוד מרכוס 5 ירושלים נייד: 0526408054 משרד: 02-6271190 מייל: erez@eklp.co.il