מינהל התכנון
חוק התכנון והבניה, התשכ"ה - 1965
מחוז ירושלים
הוועדה המחוזית החליטה ביום :
12/06/2025
להפקיד את התכנית
19/08/2026
יו"ר הוועדה המחוזית
תאריך

תכנית 101-1215656 12:24:06 07/06/2026 נספח שמירה על עצים בוגרים סקר עצים על רקע בינוי מוצע

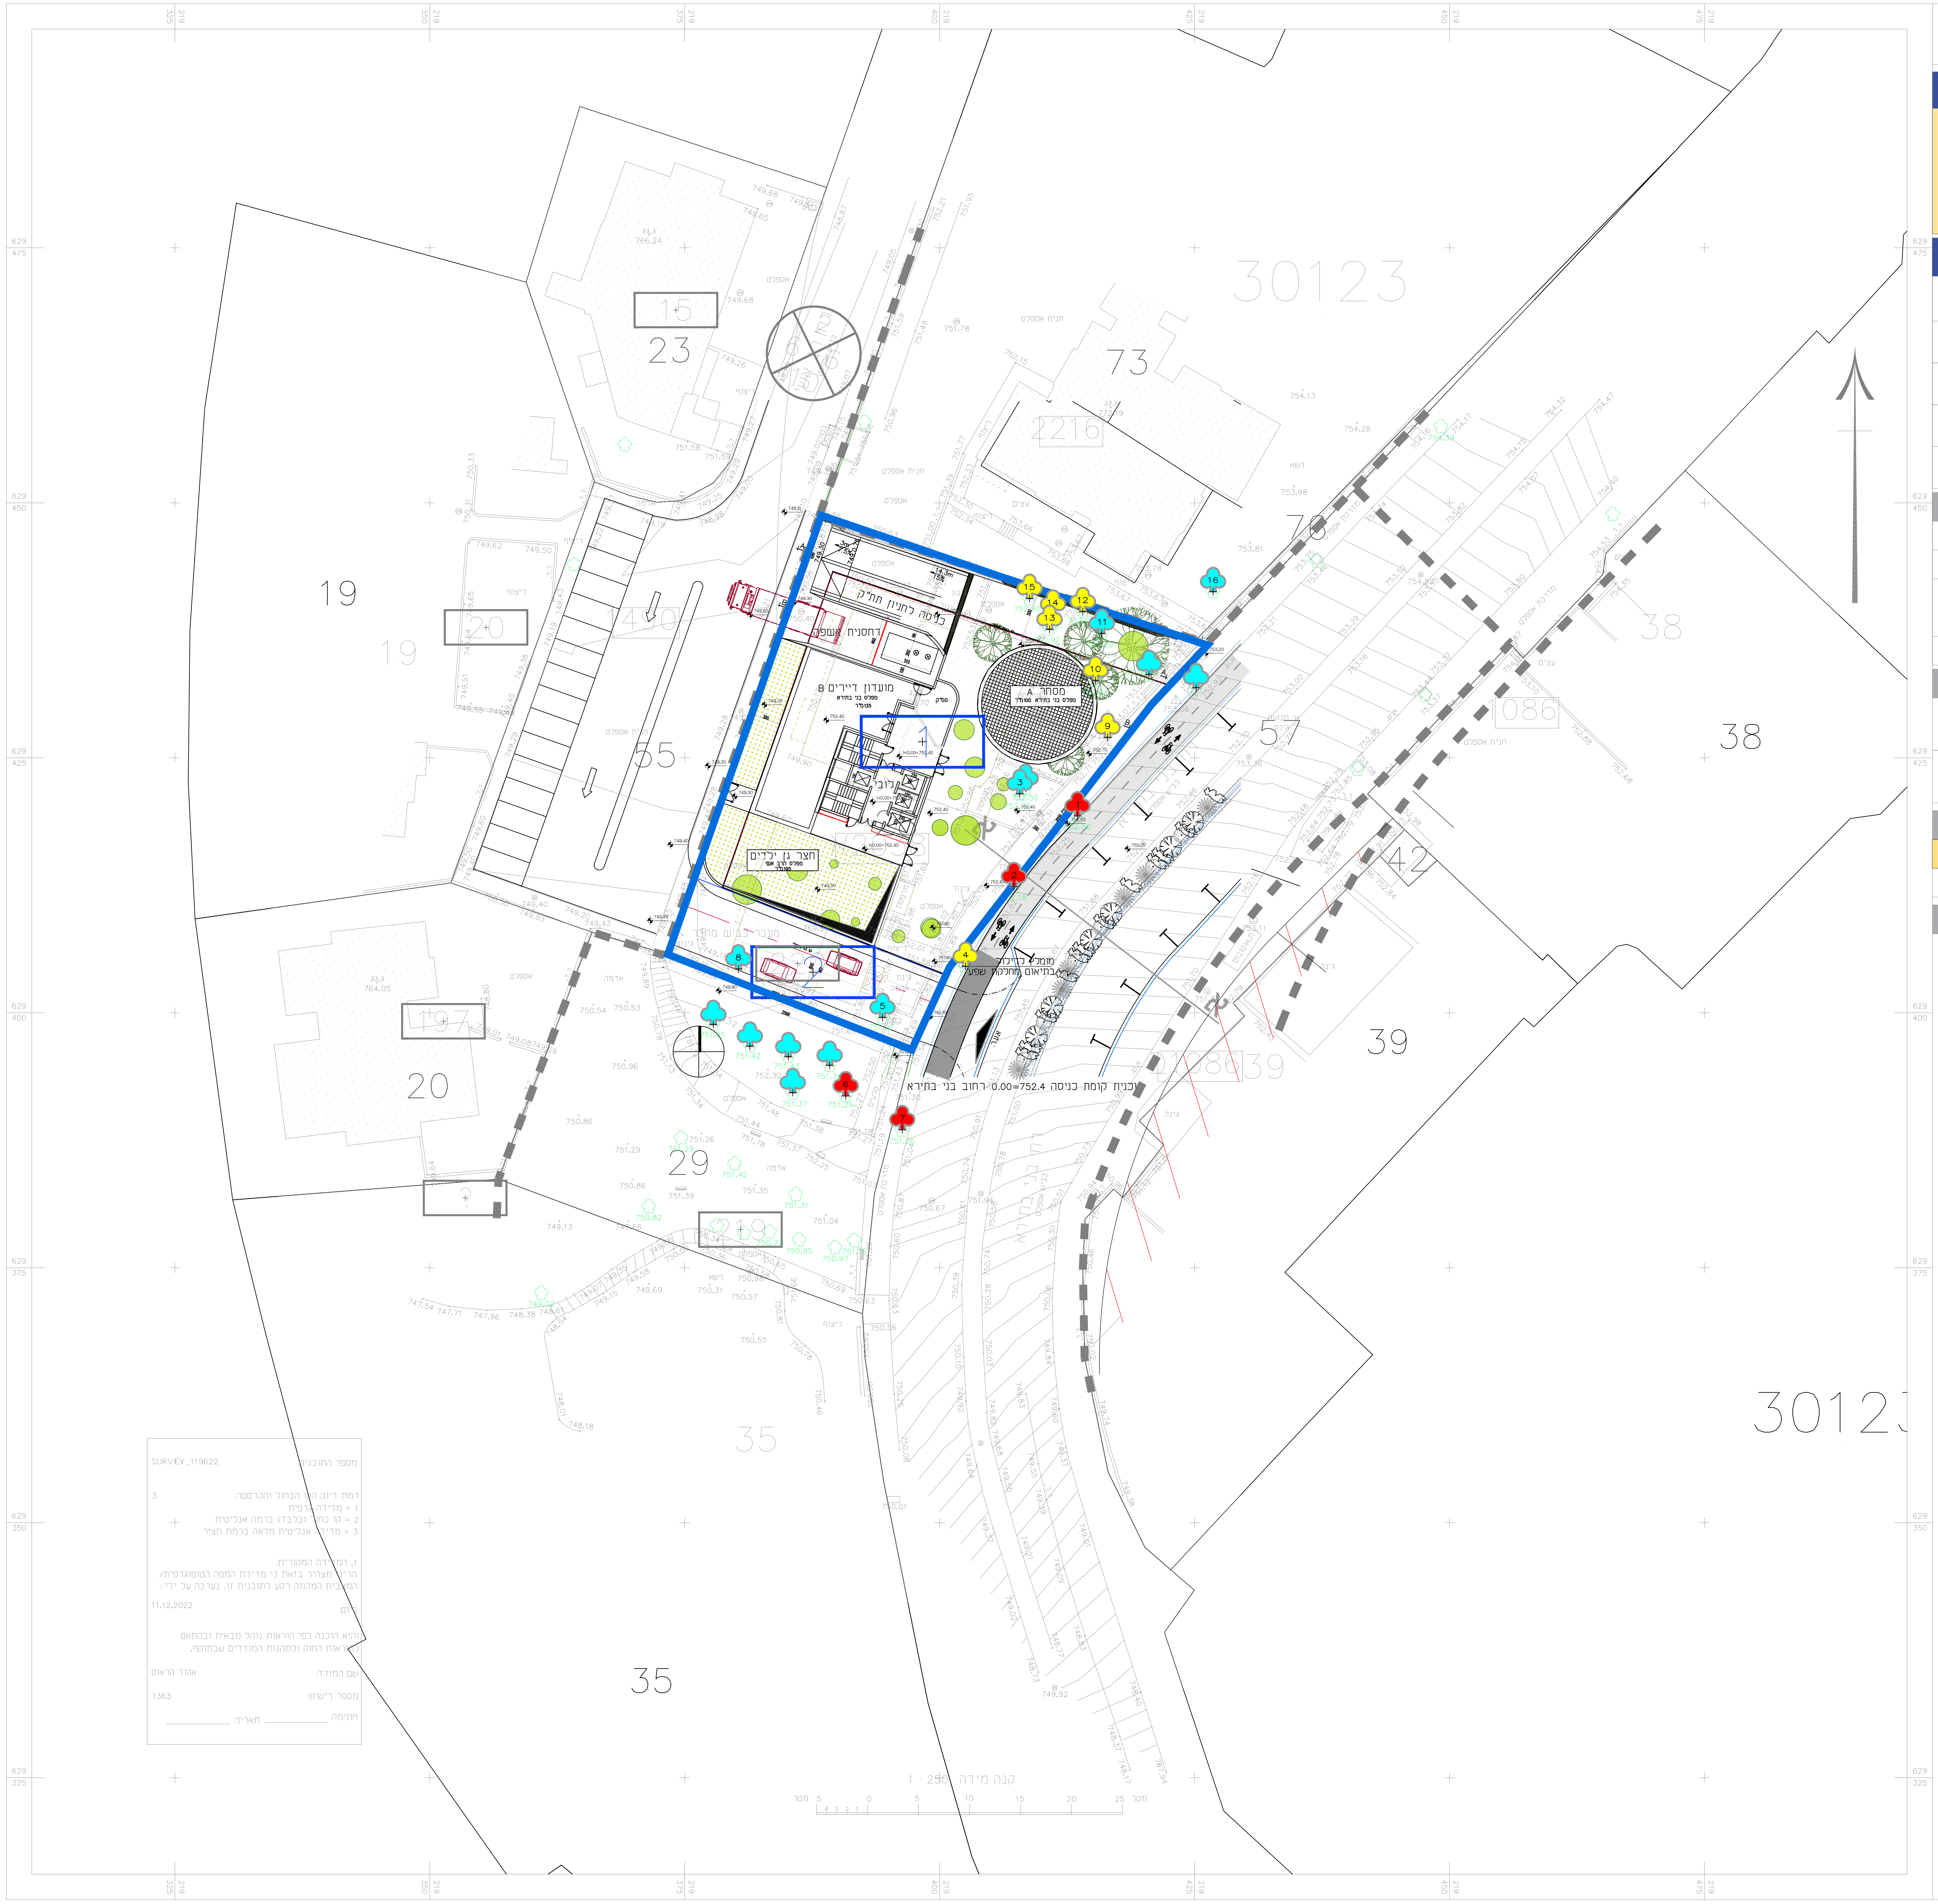

SURVEY_119622 :מספר התוכנית

רמת דיוק הקו הכחול והקדסטר: 3
1 = מדידה גרפית
2 = קו כחול (בלבד) ברמה אנליטית
3 = מדידה אנליטית מלאה ברמת תצ"ר

1. המדידה המקורית:
הריני מצהיר בזאת כי מדידת המפה הטופוגרפית/המצבית המהווה רקע לתוכנית זו, נערכה על ידי :

ביום: 11.12.2022

והיא הוכנה לפי הוראות נוהל מבא"ת ובהתאם להוראות החוק ולתקנות המודדים שבתוקף.

שם המודד: אהוד קראוס
מספר רישיון: 1363
חתימה: ____________ תאריך: ____________

חוק התכנון והבנייה, התשכ"ה - 1965
תכנית מתאר מקומית

101-1215656

בני בתירא 7-9 התחדשות עירונית

תשריט מצב מאושר גליון 1 מתוך

מחוז	ירושלים
מרחב תכנון מקומי	ירושלים
רשות מקומית	ירושלים
ישוב	ירושלים
תאריך	11.12.2022

שם הנספח	קנ"מ
מצב מאושר	1:250
תרשים סביבה	–
תרשים נוסף	–
תרשים נוסף	–
תמונה נוספת	–

שמות וחתימות:

עורך התוכנית	שם: תאגיד:	חתימה:
מודד	שם: אהוד קראוס תאגיד: קראוס חברה למדידות	חתימה:

גושים וחלקות בתכנית:

גוש	חלק/כל הגוש	חלקות בשלמותן	חלקי חלקות
30123	חלק	28	

מקרא מצב מאושר

גבול תכנית מוצעת	▬
גבול תכנית מאושרת ומספרה	101-0051854
דרך מאושרת/מוצעת	☐
אזור מגורים 1	■
שטח ציבורי פתוח	▩
דרך לביטול	▨
תא שטח	106
רוזטה	רוחב דרך מספר דרך קווי בניין

תכנית מספר -

בני בתירא 7-9
ירושלים

נספח שמירה על עצים בוגרים

תחולה	מנחה
תיאור	מהדורה 1
תאריך הגשה	

רשימת תרשימים	קנ"מ
קנה מידה	250
ייעודי קרקע	
שם תרשים	–
שם תרשים	–

שמות וחתימות

עורך הנספח	שם: ארז קפלן תאגיד: ארז קפלן תכנון נוף ליווי פרויקטים

מקרא- תכנית סקר עצים

🟧	עצים המיועדים להעתקה
🟥	עצים המיועדים לשימור
🟨	עצים המיועדים לכריתה
🟪	עצים שנסקרו וטרם קיבלו המלצה
🟦	נמדד אך לא קיים/ אינו עומד בתקן
♣	מיקום מרכז עץ על גבי מדידה
▬	גבול הסקר/ גבול מגרש
3M	סימון רדיוס מוגן ממרכז גדע

רקע בינוי/ מתוכנן ● רקע מדידה/ מצב קיים ○

○ לעיון ● לאישור ○ למכרז ○ לביצוע

פרויקט: בני בתירא 7-9
ירושלים

סקר עצים

קנה מידה: **1:250**	מס גליון: **1**
תאריך מקור:	**29/03/23**
תאריך עדכון:	**20/05/26**

ארז קפלן
תכנון נוף | ליווי פרויקטים
דוד מרכוס 5 ירושלים
משרד: 02-6271190
מייל: EREZ@EKLP.CO.IL
נייד: 052-6408054

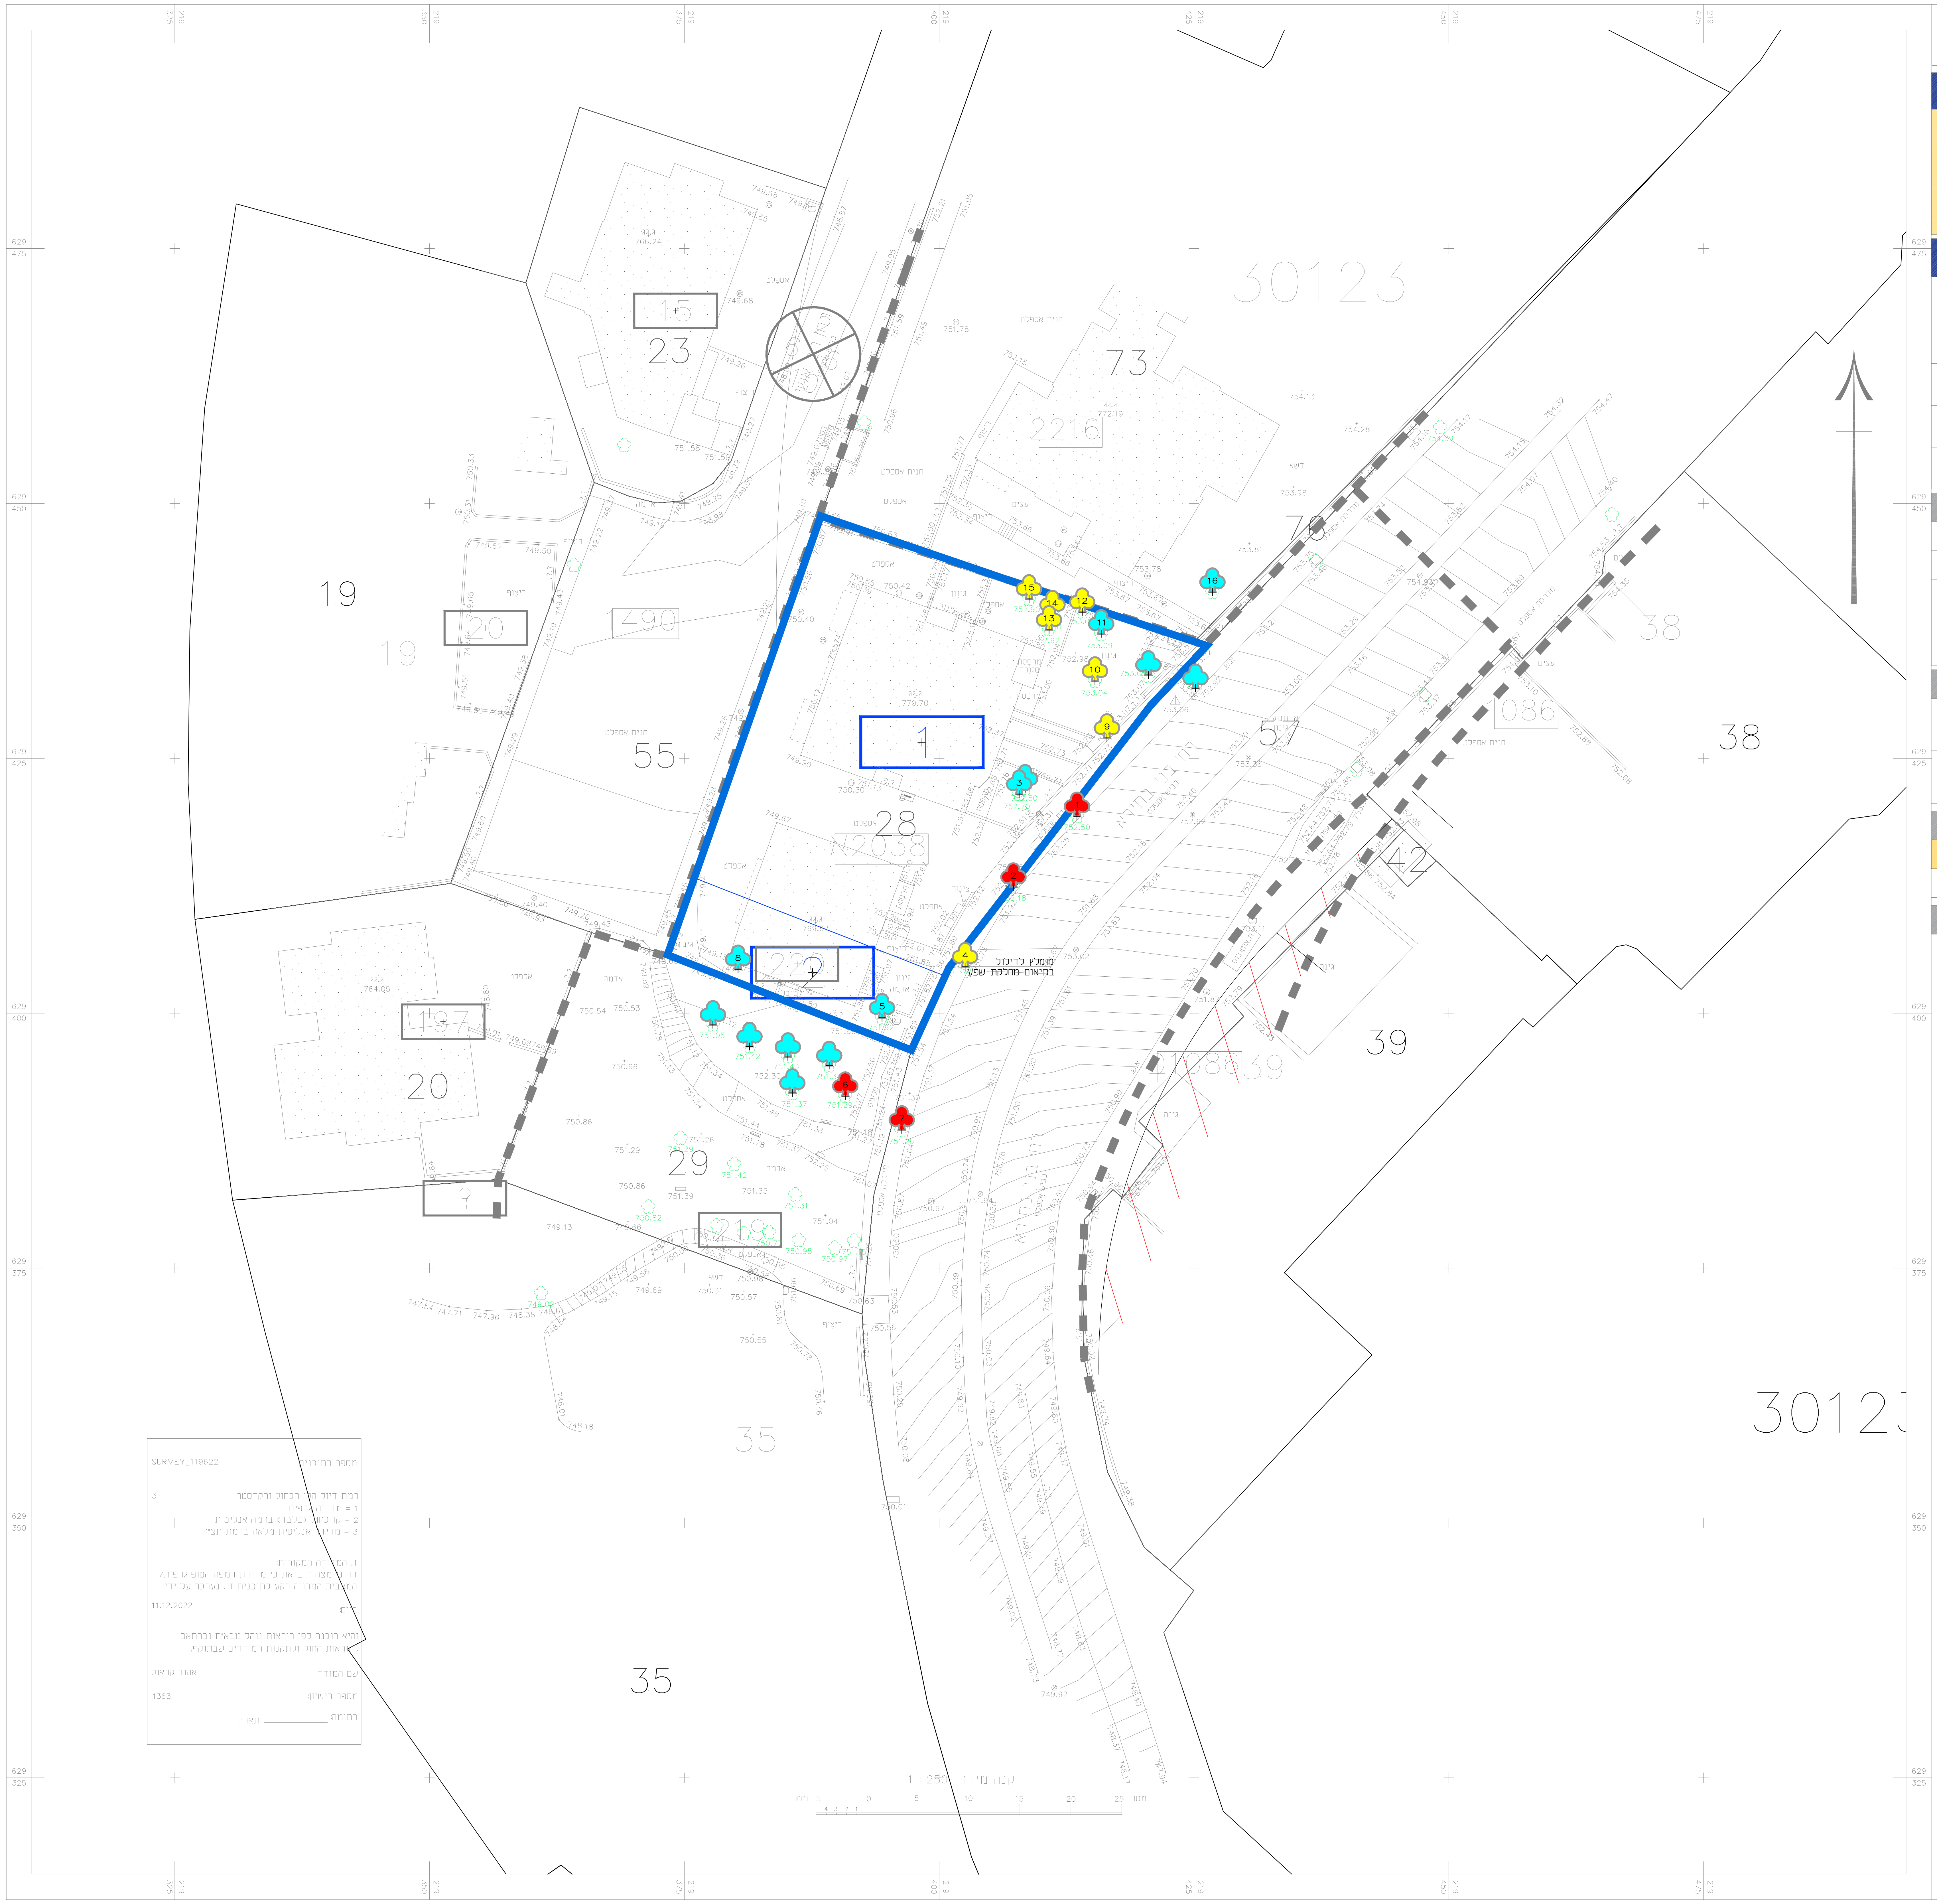

חוק התכנון והבנייה, התשכ"ה – 1965
תכנית מתאר מקומית

101-1215656

בני בתירא 7-9 התחדשות עירונית

תשריט מצב מאושר | גליון 1 מתוך

מחוז	ירושלים
מרחב תכנון מקומי	ירושלים
רשות מקומית	ירושלים
ישוב	ירושלים
תאריך	11.12.2022

שם הנספח	קנ"מ
מצב מאושר	1:250
תרשים סביבה	–
תרשים נוסף	–
תרשים נוסף	–
תמונה נוספת	–

שמות וחתימות:

עורך התוכנית	שם: תאגיד:	חתימה:
מודד	שם: אהוד קראוס תאגיד: קראוס חברה למדידות	חתימה:

גושים וחלקות בתכנית:

גוש	חלק/כל הגוש	חלקות בשלמותן	חלקי חלקות
30123	חלק	28	

מקרא מצב מאושר

- גבול תכנית מוצעת
- 101-0051854 גבול תכנית מאושרת ומספרה
- דרך מאושרת/מוצעת
- ■ אזור מגורים 1
- ■ שטח ציבורי פתוח
- ▨ דרך לביטול
- 106 תא שטח
- רוזטה: רוחב דרך, מספר דרך, קוי בניין

תכנית מספר -

בני בתירא 7-9
ירושלים

נספח שמירה על עצים בוגרים

תחולה	מנחה
תיאור	מהדורה 1
תאריך הגשה	

רשימת תרשימים	קנ"מ
קנה מידה	250
ייעודי קרקע	
שם תרשים	–
שם תרשים	–

שמות וחתימות

עורך הנספח	שם:	ארז קפלן
	תאגיד:	ארז קפלן תכנון נוף ליווי פרויקטים

מקרא- תכנית סקר עצים

- ♣ עצים המיועדים להעתקה
- ♣ עצים המיועדים לשימור
- ♣ עצים המיועדים לכריתה
- ♣ עצים שנסקרו וטרם קיבלו המלצה
- ♣ נמדד אך לא קיים/ אינו עומד בתקן
- ♣ מיקום מרכז עץ על גבי מדידה
- ━ גבול הסקר/ גבול מגרש
- 3M סימון רדיוס מוגן ממרכז גזע

רקע בינוי/ מתוכנן ○ רקע מדידה/ מצב קיים ●

לעיון ○ | לאישור ● | למכרז ○ | לביצוע ○

פרויקט: בני בתירא 7-9
ירושלים

סקר עצים

קנה מידה: **1:250**	מס גליון: **3**
תאריך מקור:	**29/03/23**
תאריך עדכון:	**20/05/26**

ארז קפלן
תכנון נוף | ליווי פרויקטים

דוד מרכוס 5 ירושלים
משרד: 02-6271190
מייל: EREZ@EKLP.CO.IL
נייד: 052-6408054

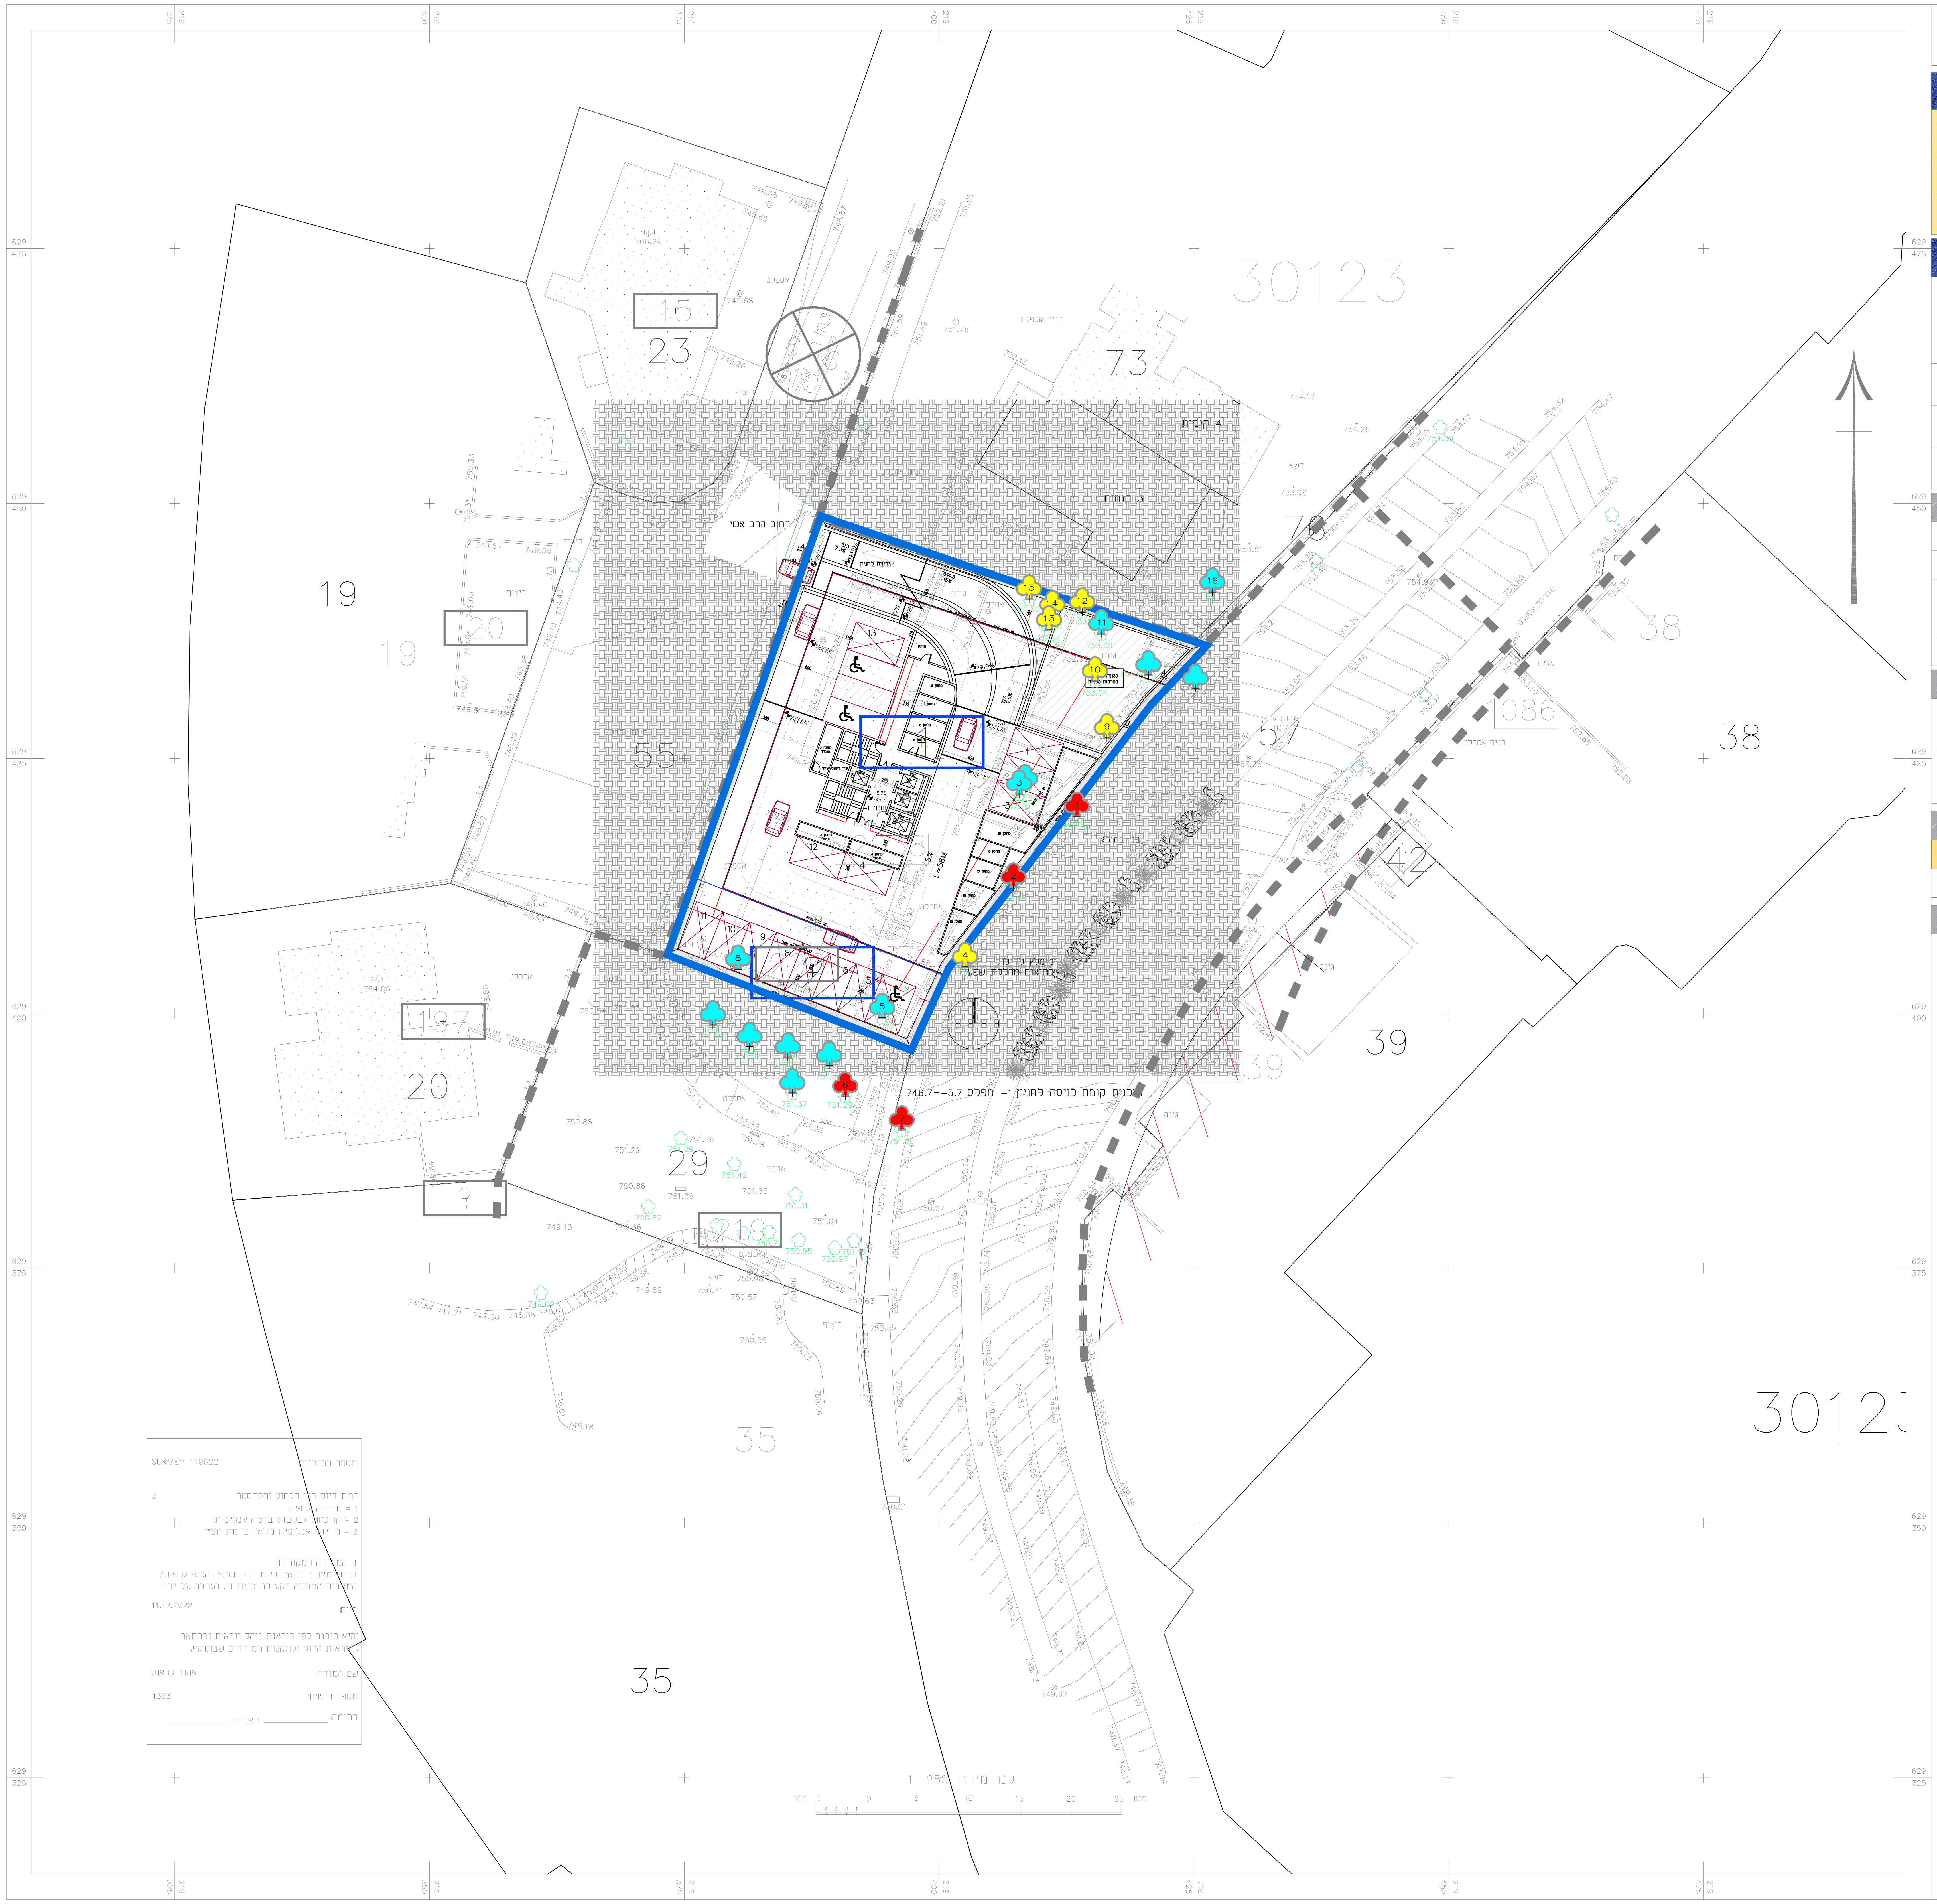

חוק התכנון והבנייה, התשכ"ה – 1965
תכנית מתאר מקומית

101-1215656

בני בתירא 7-9 התחדשות עירונית

תשריט מצב מאושר גליון 1 מתוך

מחוז	ירושלים
מרחב תכנון מקומי	ירושלים
רשות מקומית	ירושלים
ישוב	ירושלים
תאריך	11.12.2022

שם הנספח	קנ"מ
מצב מאושר	1: 250
תרשים סביבה	–
תרשים נוסף	–
תרשים נוסף	–
תמונה נוספת	–

שמות וחתימות:

עורך התוכנית	שם: תאגיד:	חתימה:
מודד	שם: אהוד קראוס תאגיד: קראוס חברה למדידות	חתימה:

גושים וחלקות בתכנית:

גוש	חלק/כל הגוש	חלקות בשלמותן	חלקי חלקות
30123	חלק	28	

מקרא מצב מאושר

גבול תכנית מוצעת	▬
גבול תכנית מאושרת ומספרה	101-0051854 ╍
דרך מאושרת/מוצעת	☐
אזור מגורים 1	■
שטח ציבורי פתוח	■
דרך לביטול	▨
תא שטח	106
רוזטה	רוחב דרך / מספר דרך / קווי בניין

תכנית מספר -

בני בתירא 7-9
ירושלים

נספח שמירה על עצים בוגרים

תחולה	מנחה
תיאור	מהדורה 1
תאריך הגשה	

רשימת תרשימים	קנ"מ
קנה מידה	250
ייעודי קרקע	
שם תרשים	–
שם תרשים	–

שמות וחתימות

עורך הנספח	שם: ארז קפלן תאגיד: ארז קפלן תכנון נוף ליווי פרויקטים

מקרא- תכנית סקר עצים

●	עצים המיועדים להעתקה
●	עצים המיועדים לשימור
●	עצים המיועדים לכריתה
●	עצים שנסקרו וטרם קיבלו המלצה
●	נמדד אך לא קיים/ אינו עומד בתקן
○	מיקום מרכז עץ על גבי מדידה
▬	גבול הסקר/ גבול מגרש
3M	סימון רדיוס מוגן ממרכז גזע

רקע בינוי/ מתוכנן ● רקע מדידה/ מצב קיים ○

לעיון ○ לאישור ● למכרז ○ לביצוע ○

פרויקט: בני בתירא 7-9
ירושלים

סקר עצים

קנה מידה: **1:250**	מס גליון: **2**
תאריך מקור:	**29/03/23**
תאריך עדכון:	**20/05/26**

ארז קפלן
תכנון נוף | ליווי פרויקטים
דוד מרכוס 5 ירושלים
משרד: 02-6271190
מייל: EREZ@EKLP.CO.IL
נייד: 052-6408054