מינהל התכנון
חוק התכנון והבניה, התשכ"ה - 1965
מחוז ירושלים
הוועדה המחוזית החליטה ביום :
12/06/2025
להפקיד את התכנית
19/08/2026
יו"ר הוועדה המחוזית
תאריך

תכנית 101-1215656 נספח תנועה נספח תנועה 12:48:21 16/07/2026

תכנית מס' 101-1215656

בני בתירא 7-9
התחדשות עירונית

נספח תנועה גליון 1 מתוך 1

תחולה	מנחה
תיאור	
תאריך	16.07.2026
תכניות, חתכים וחזיתות	קנ"מ 1:250

מקרא

גבול מגרש	━
קו בניין תת"ק	━ ·· ━
קו בניין עילי	━ · ━
שביל אופניים	╌
גבול זכות דרך	🟦 🟦 🟦
זכות דרך חדשה	🟩 🟩 🟩
תלת ממד	🟧 🟧 🟧
כניסה לחניון	▲
חניה למבנה ציבור	▤
חניית אורחים	▤
זיקת הנאה	▨

המקום

תרשים סביבה:

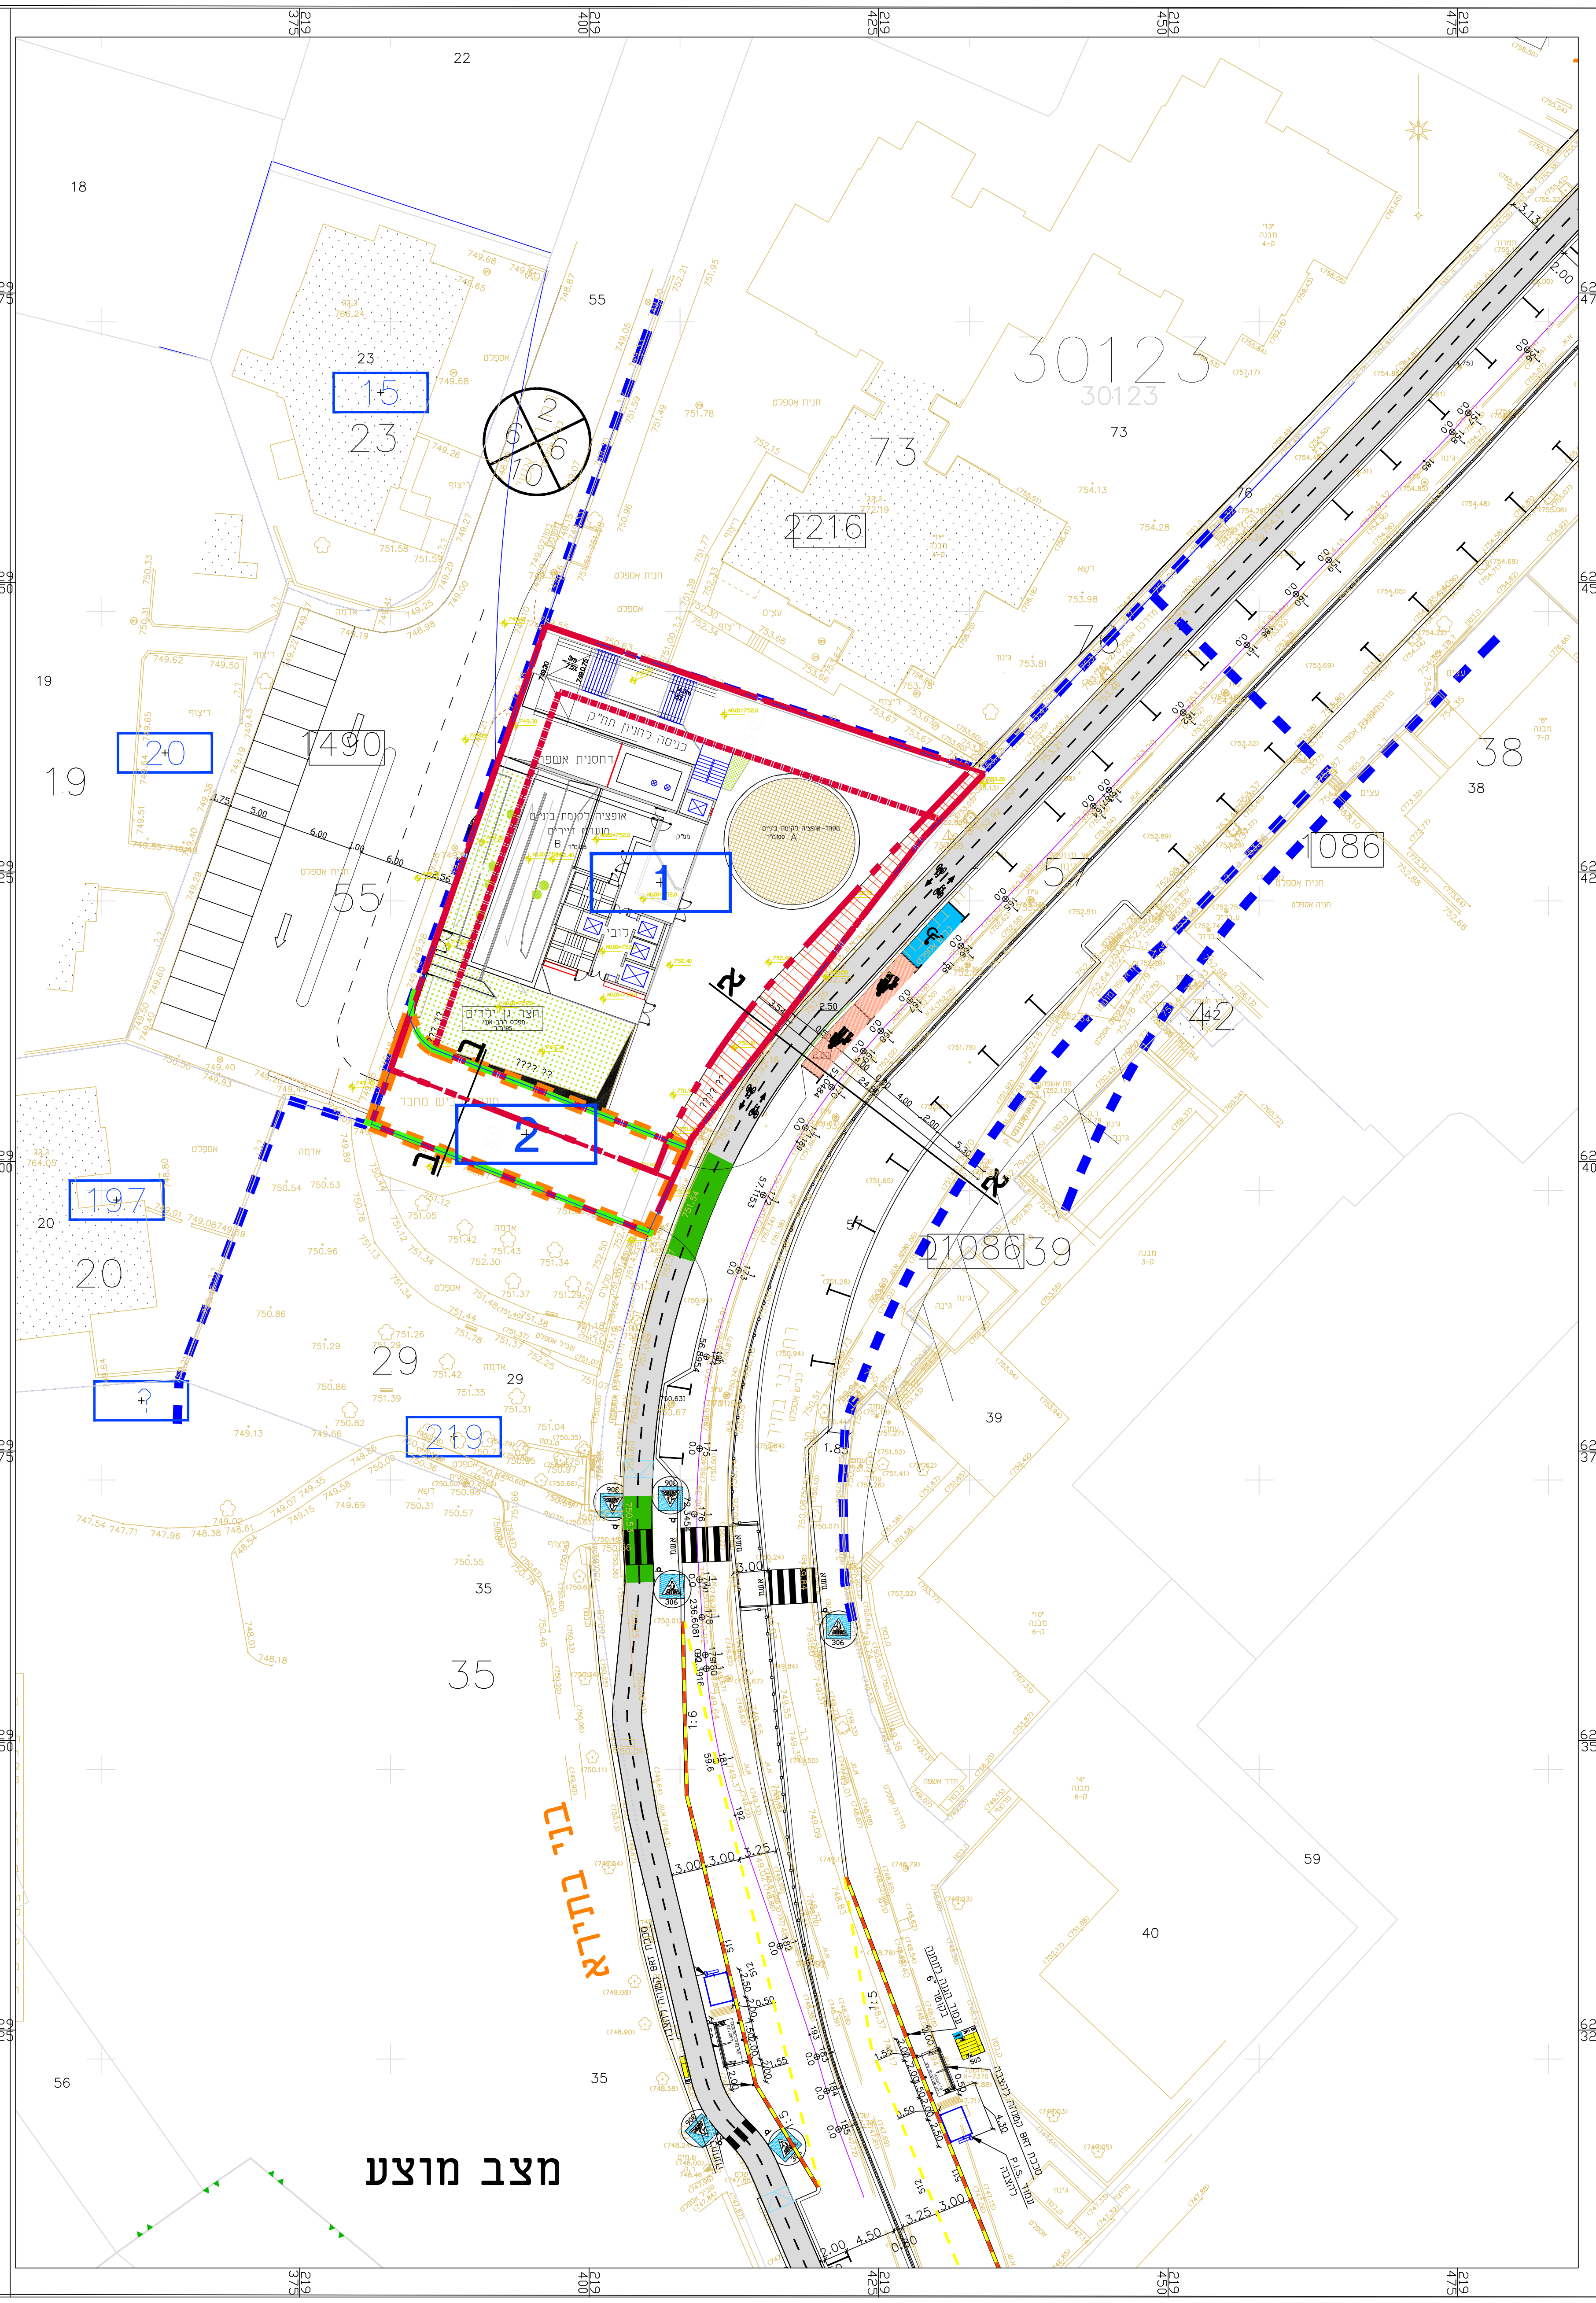

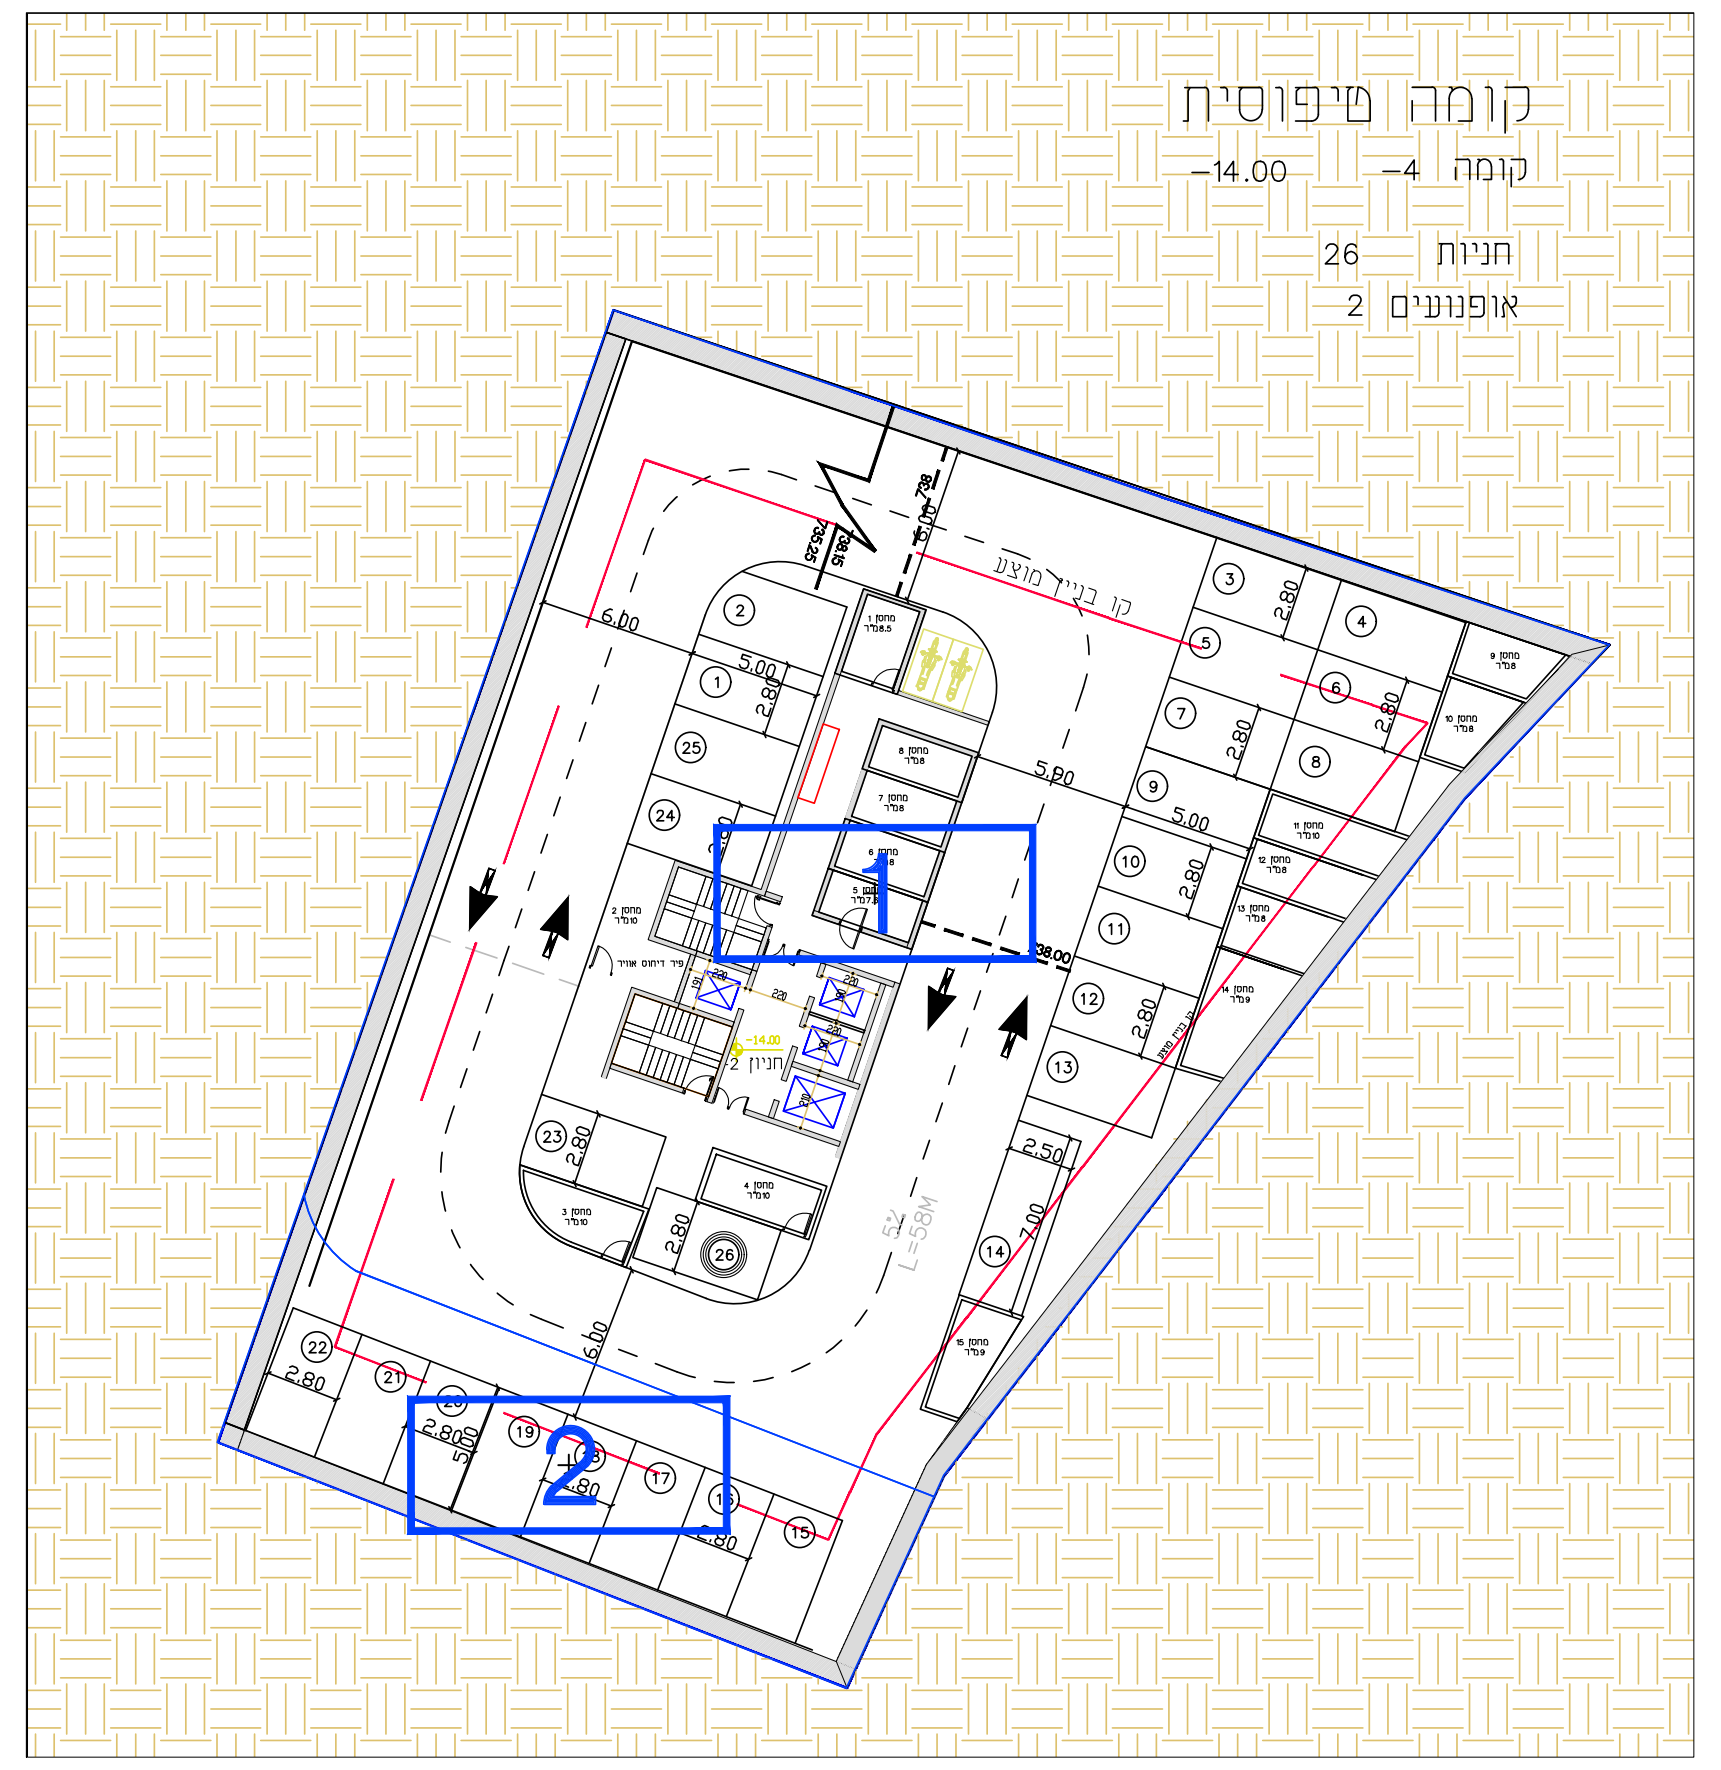

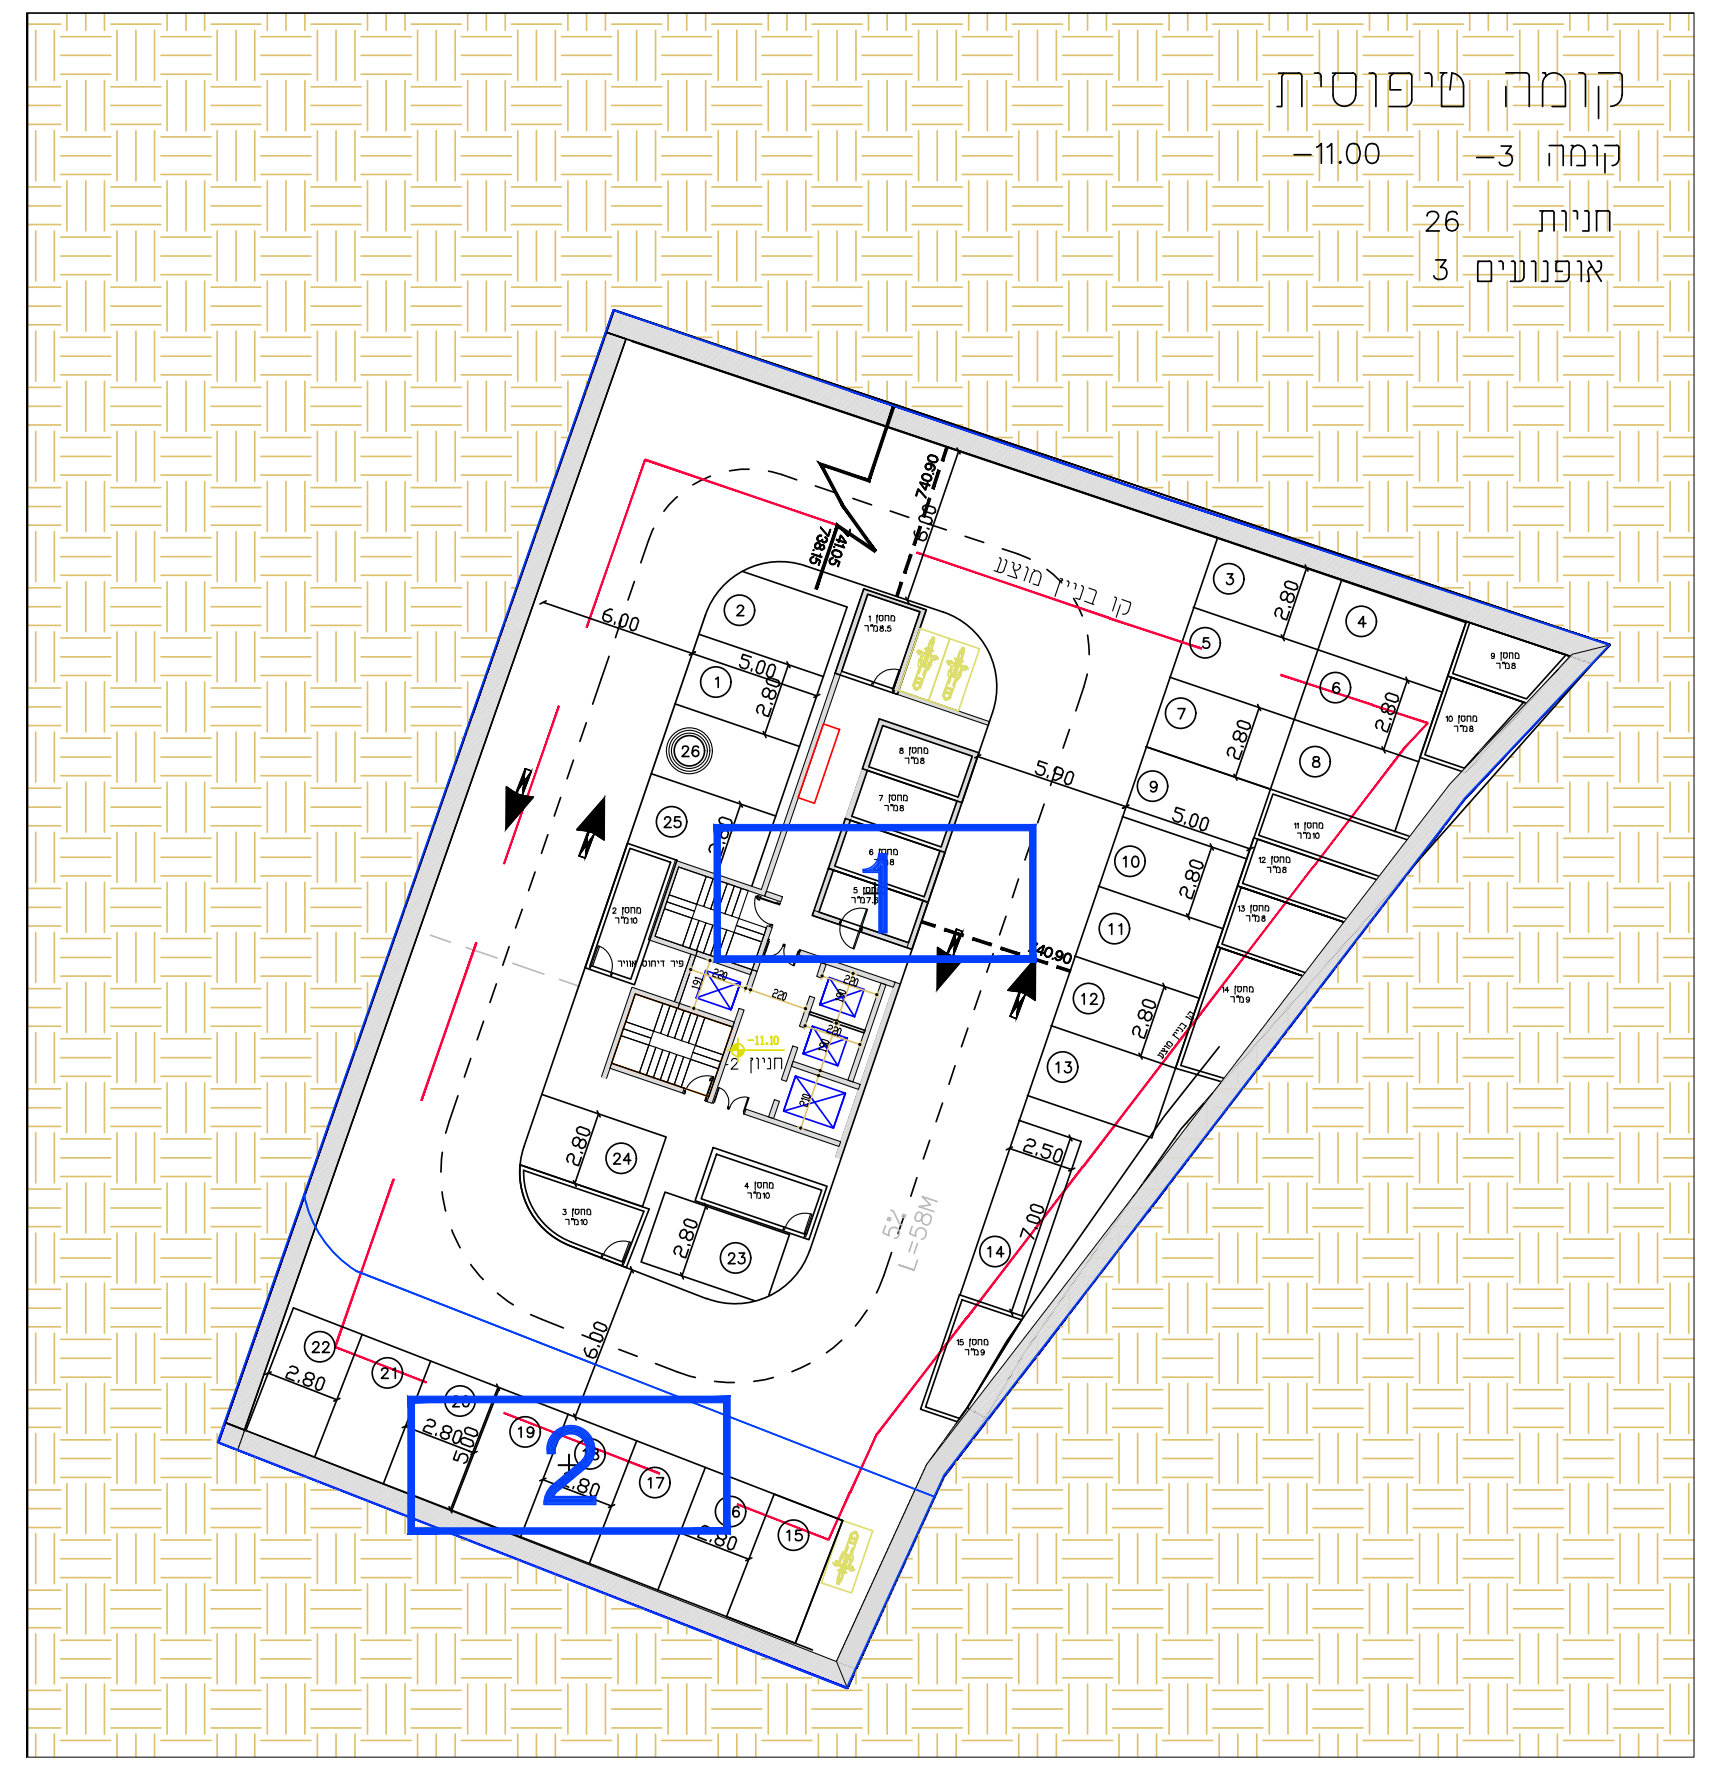

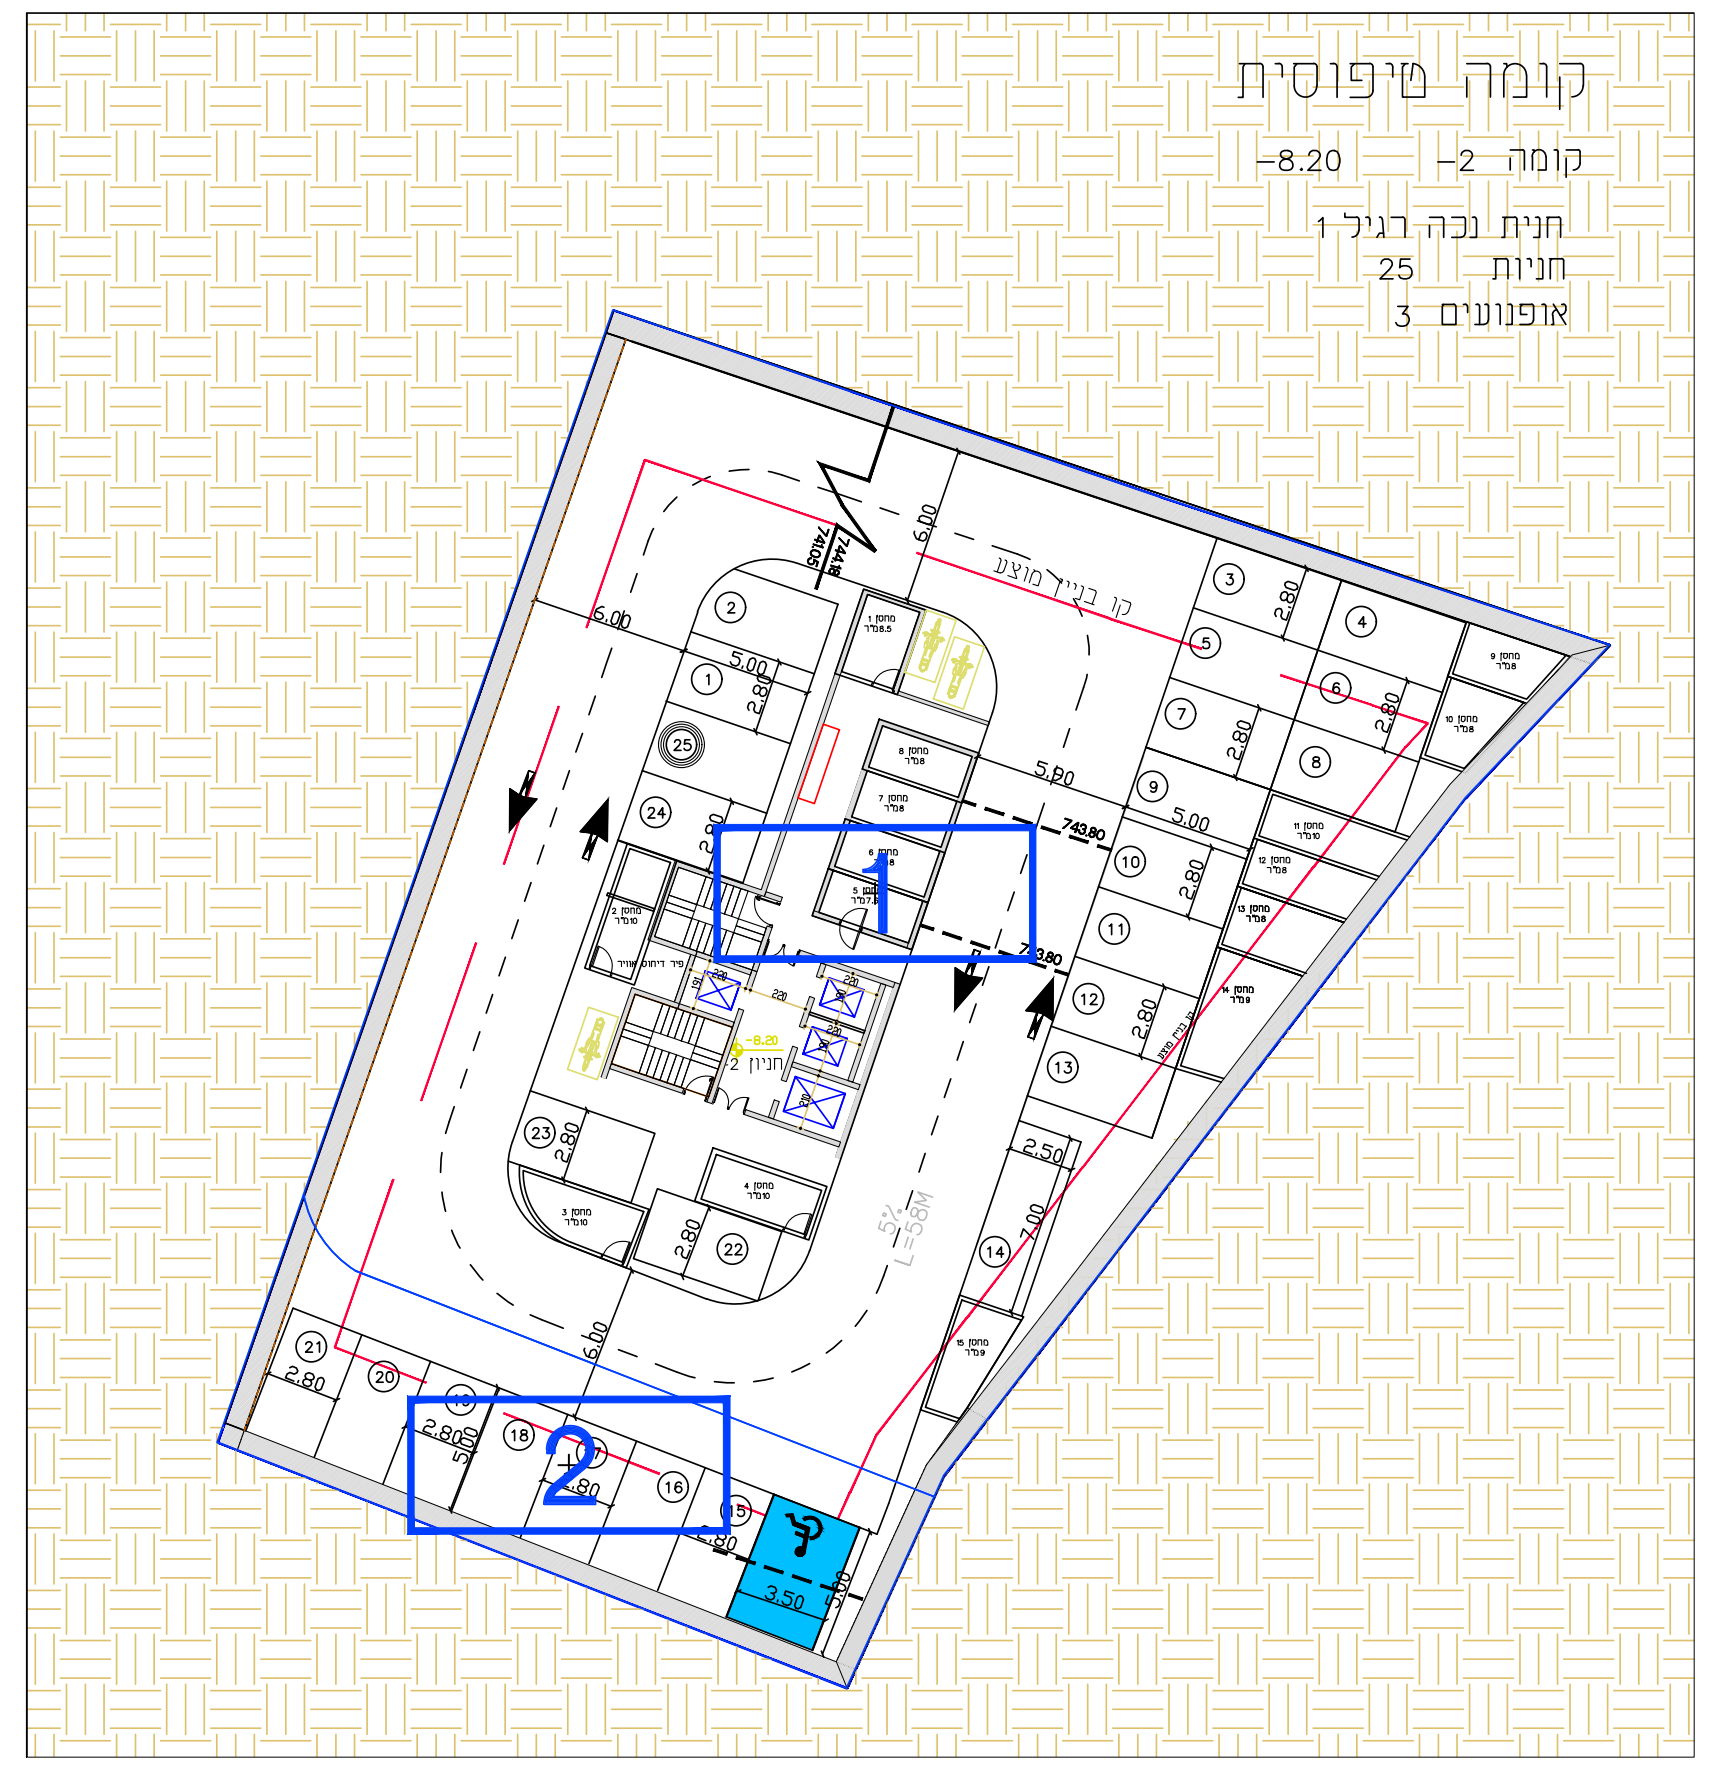

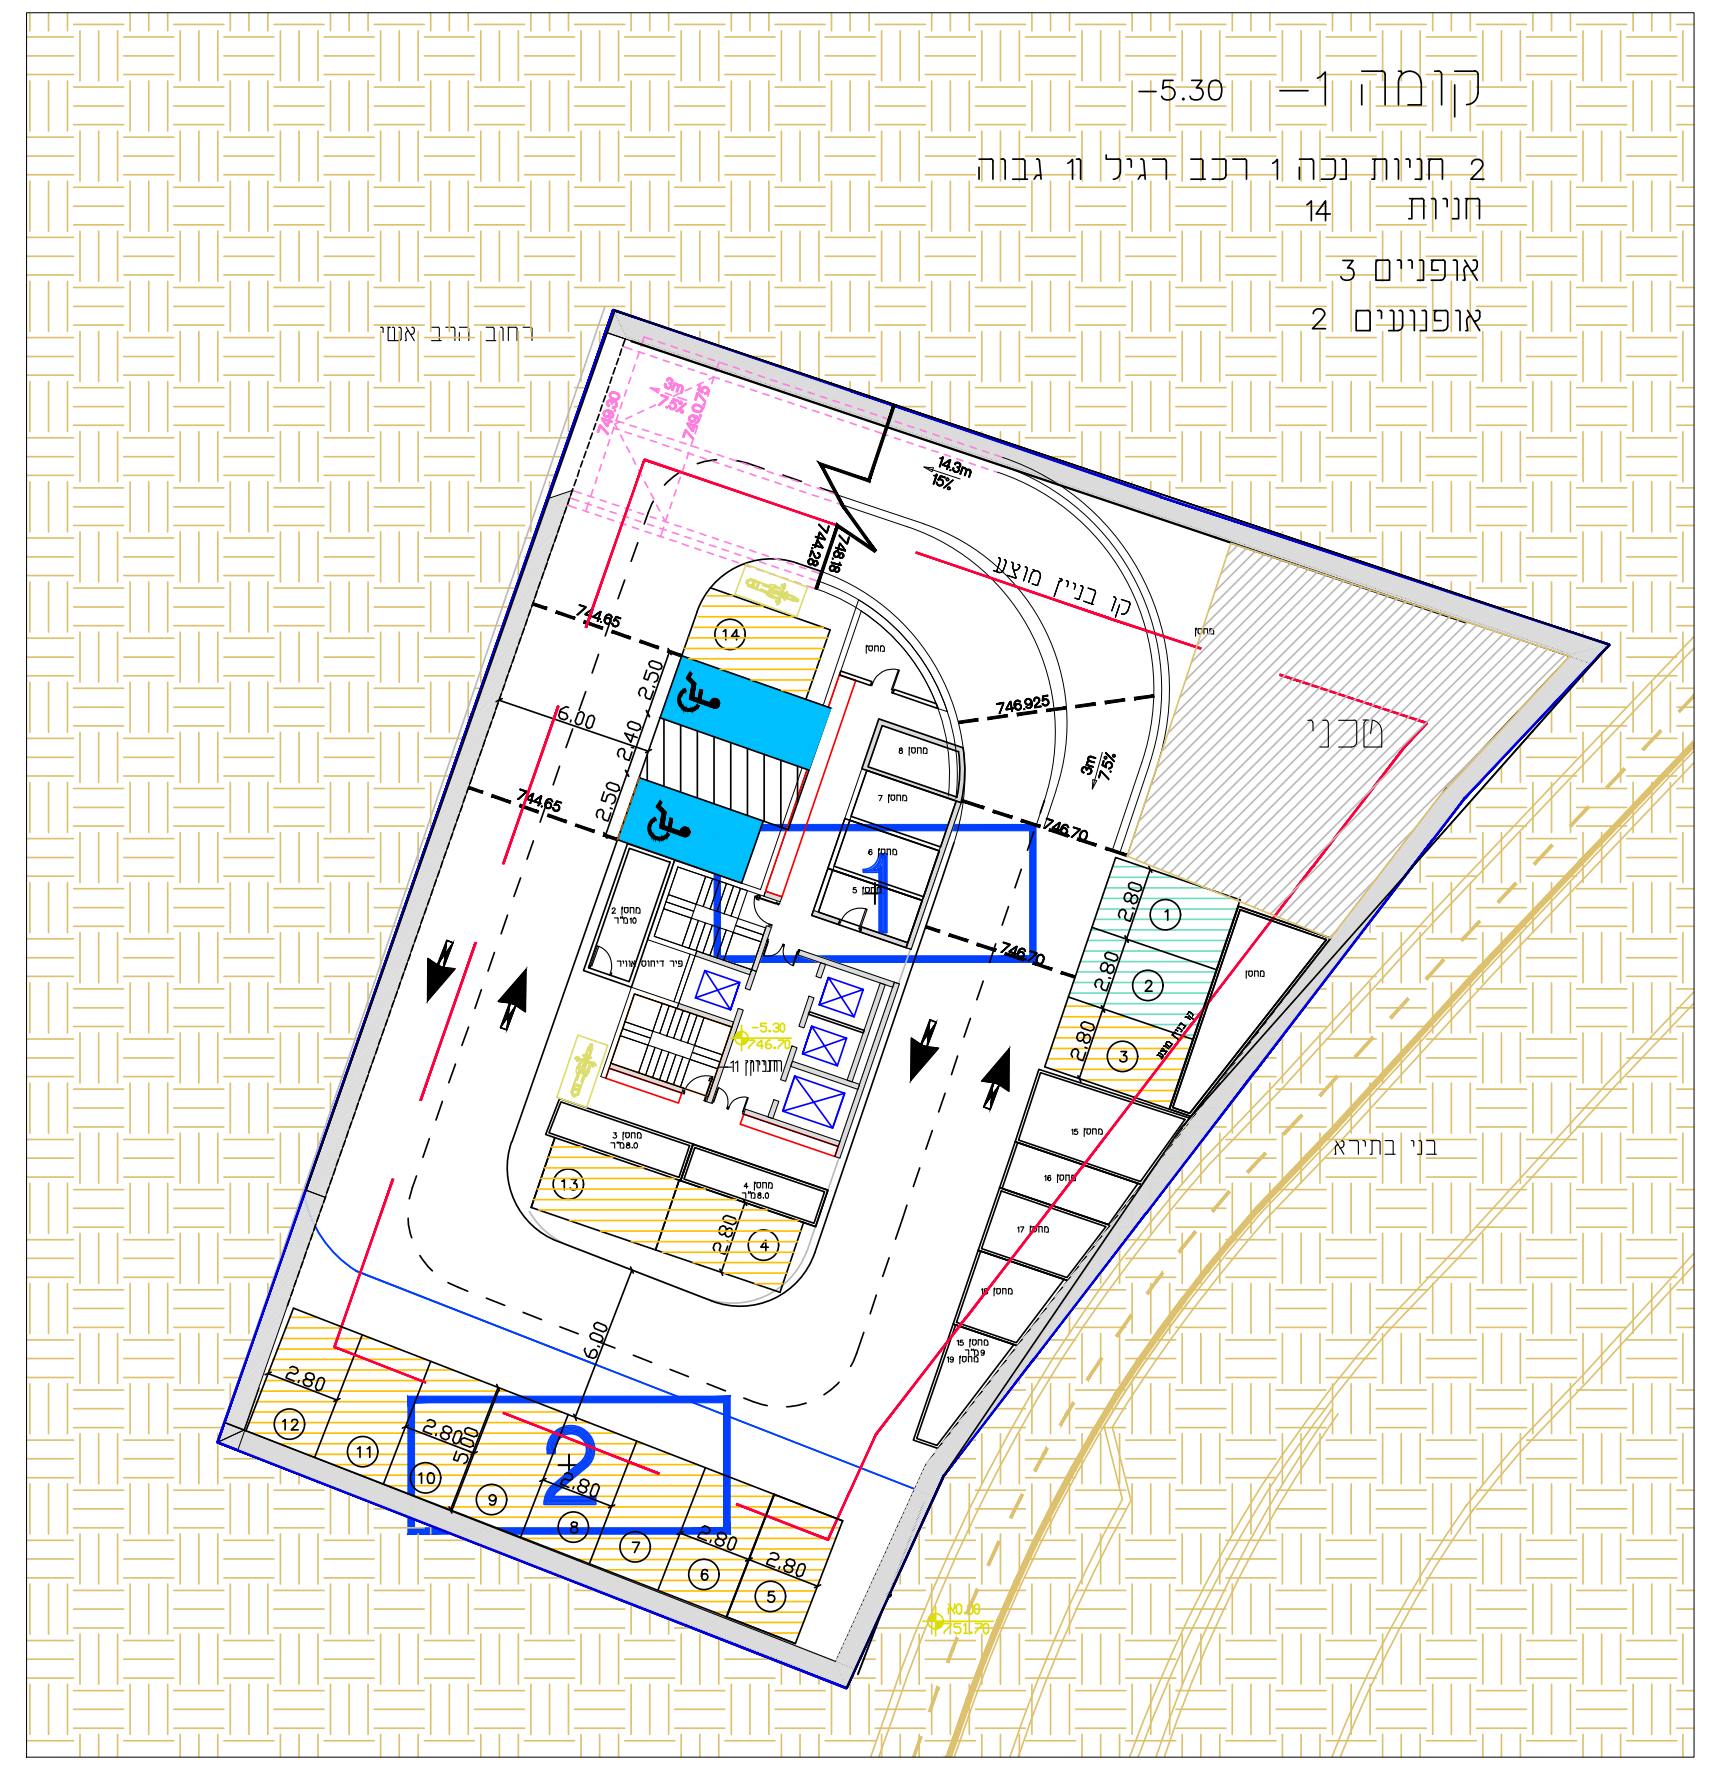

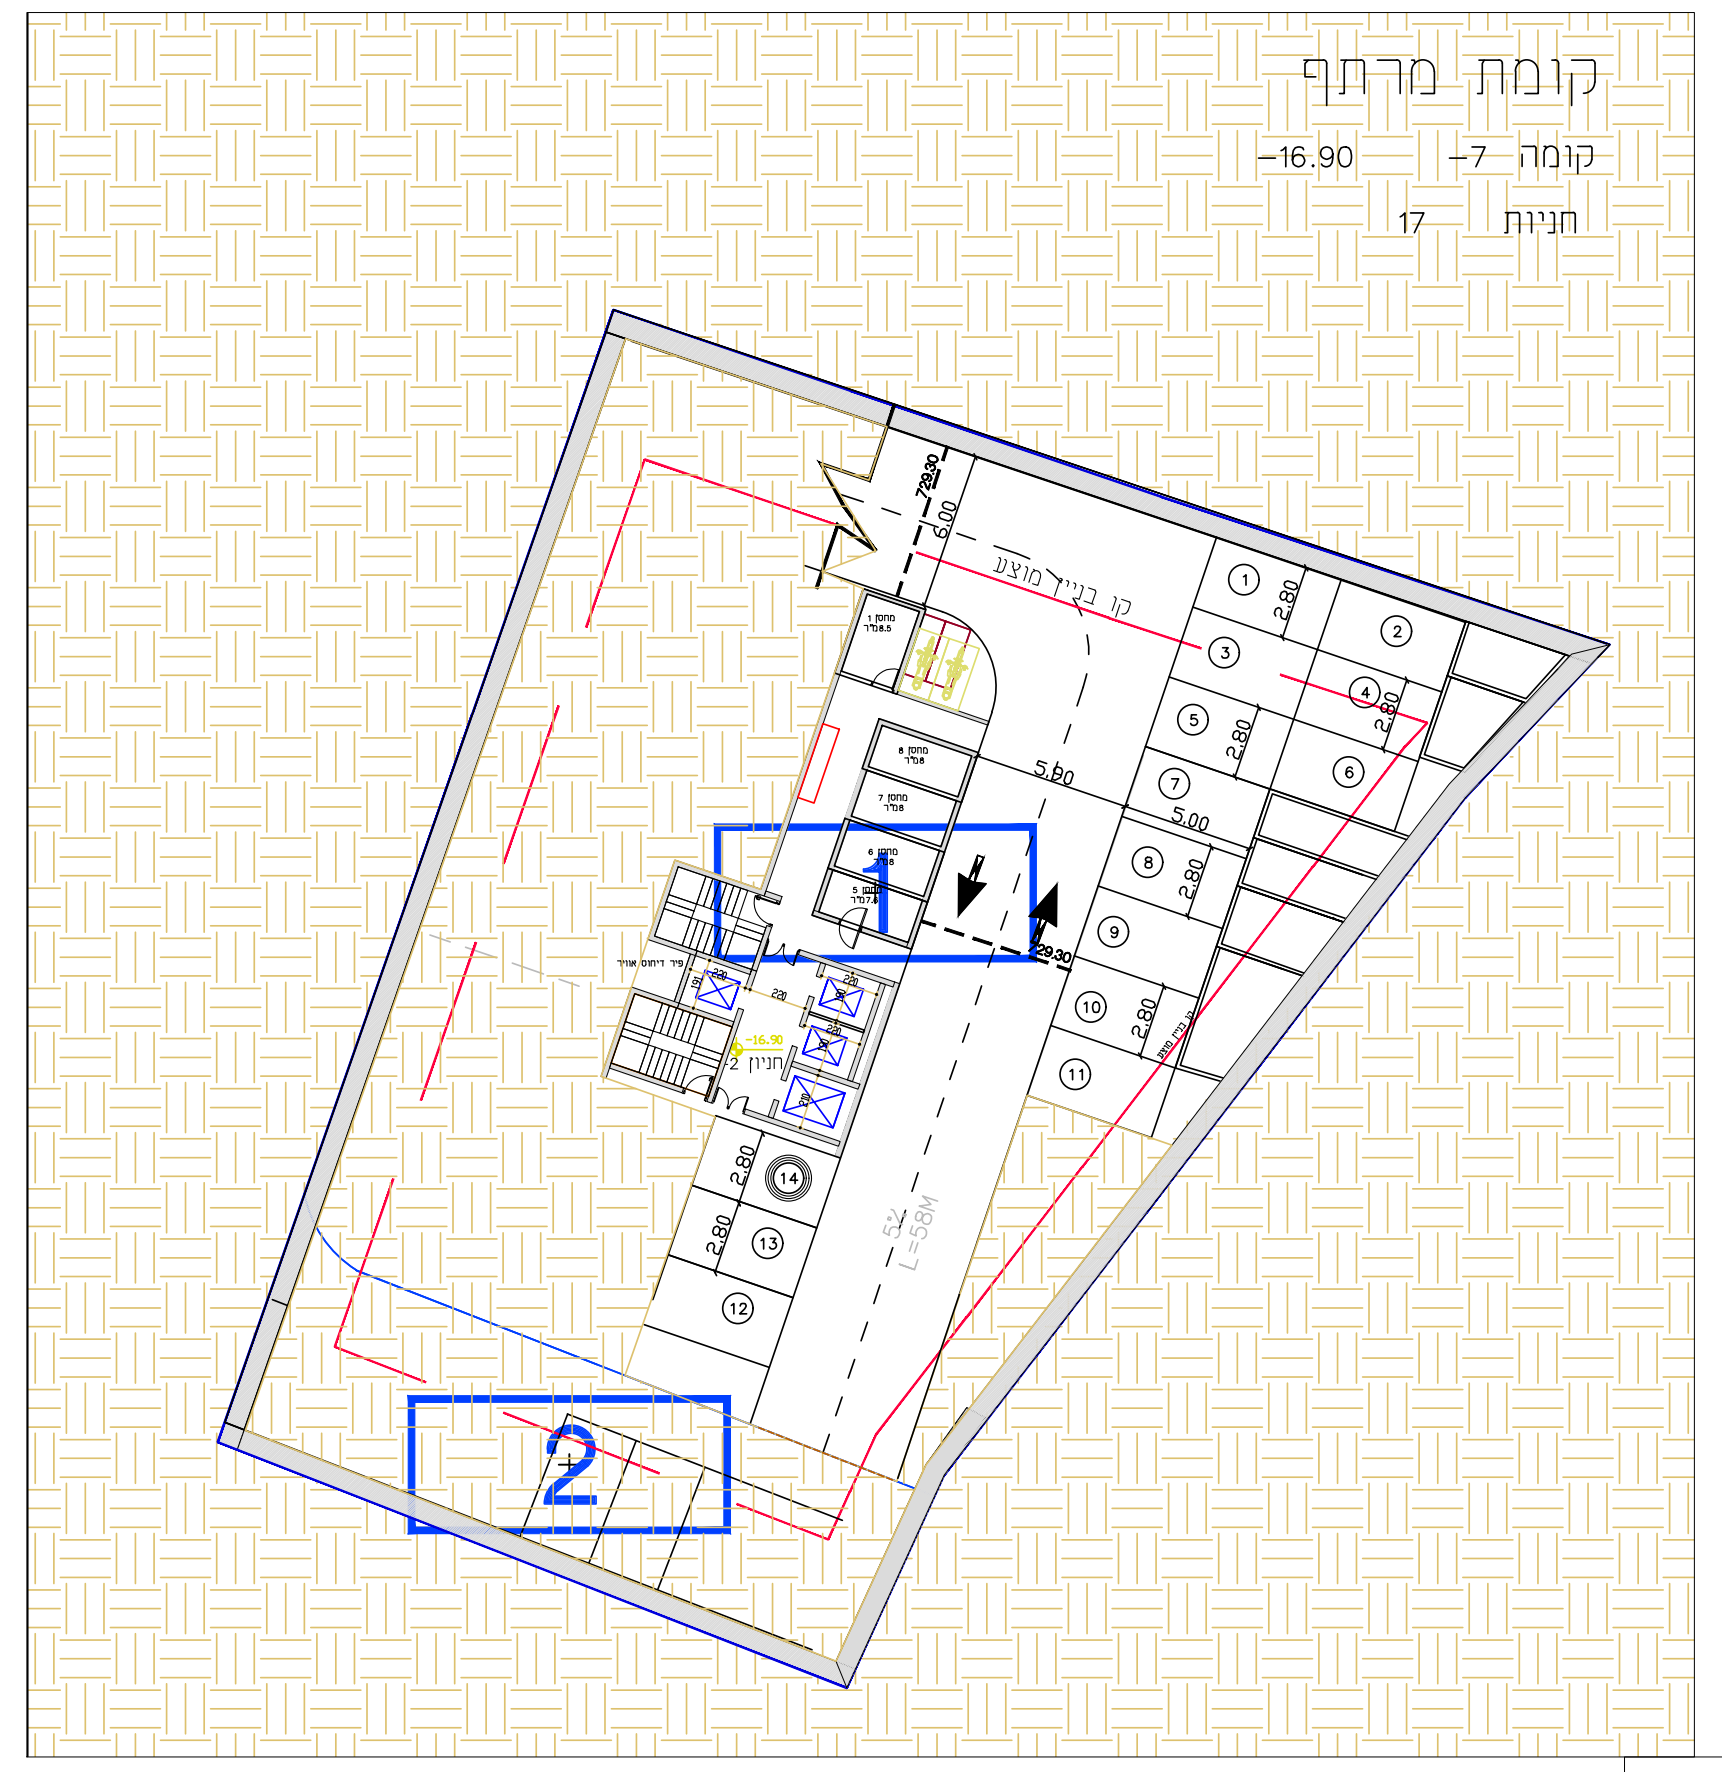

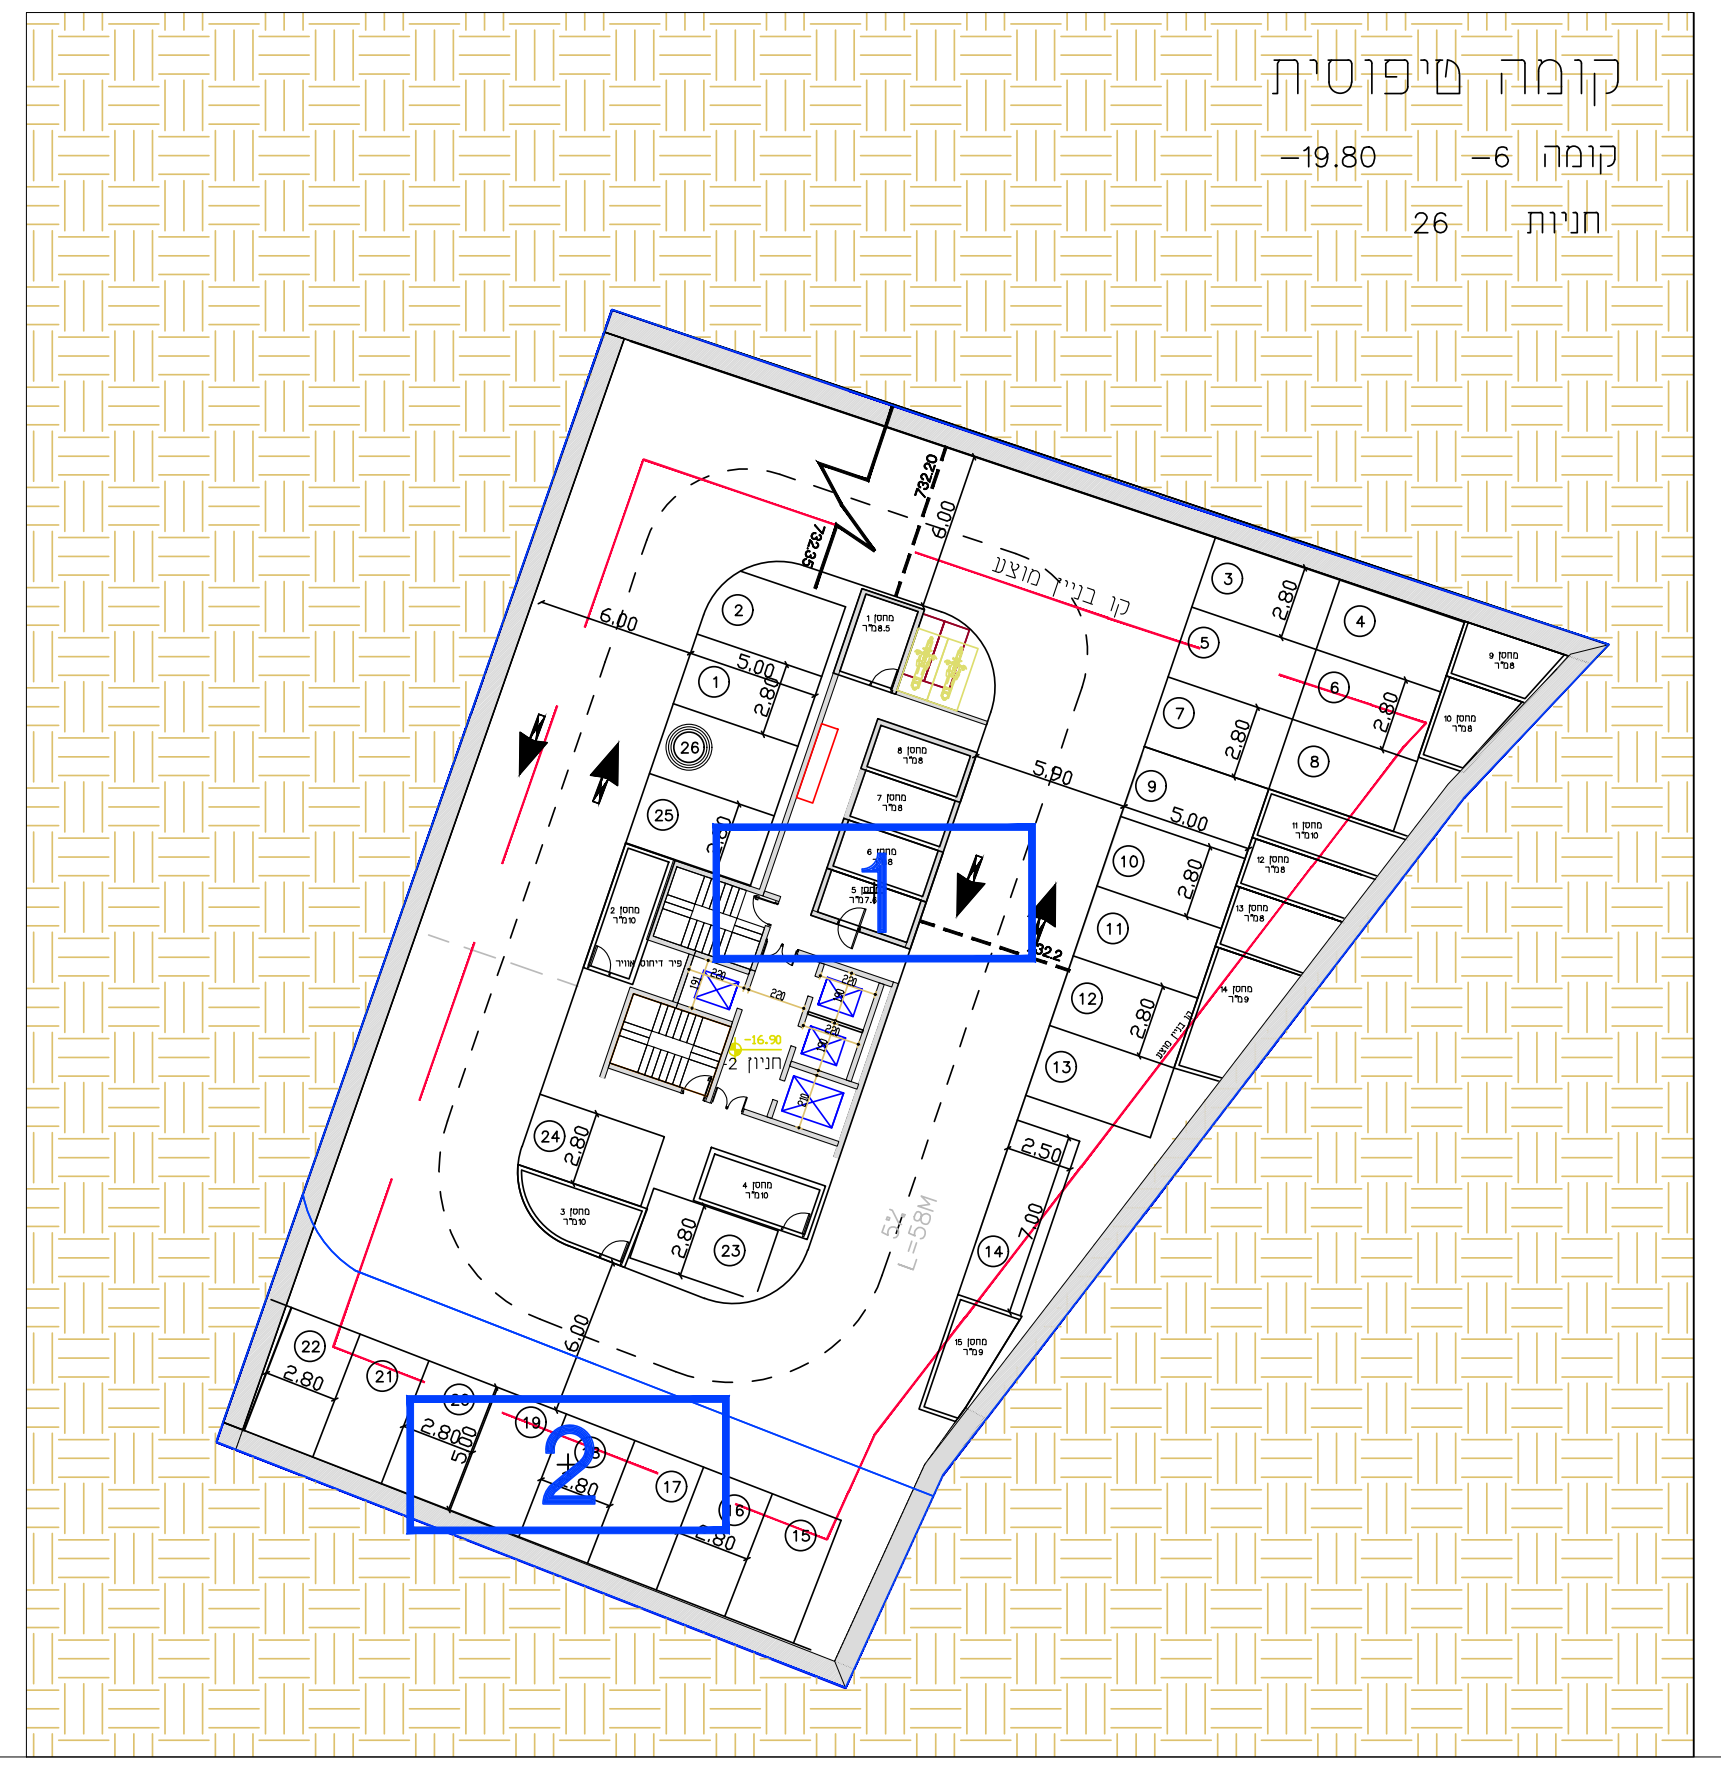

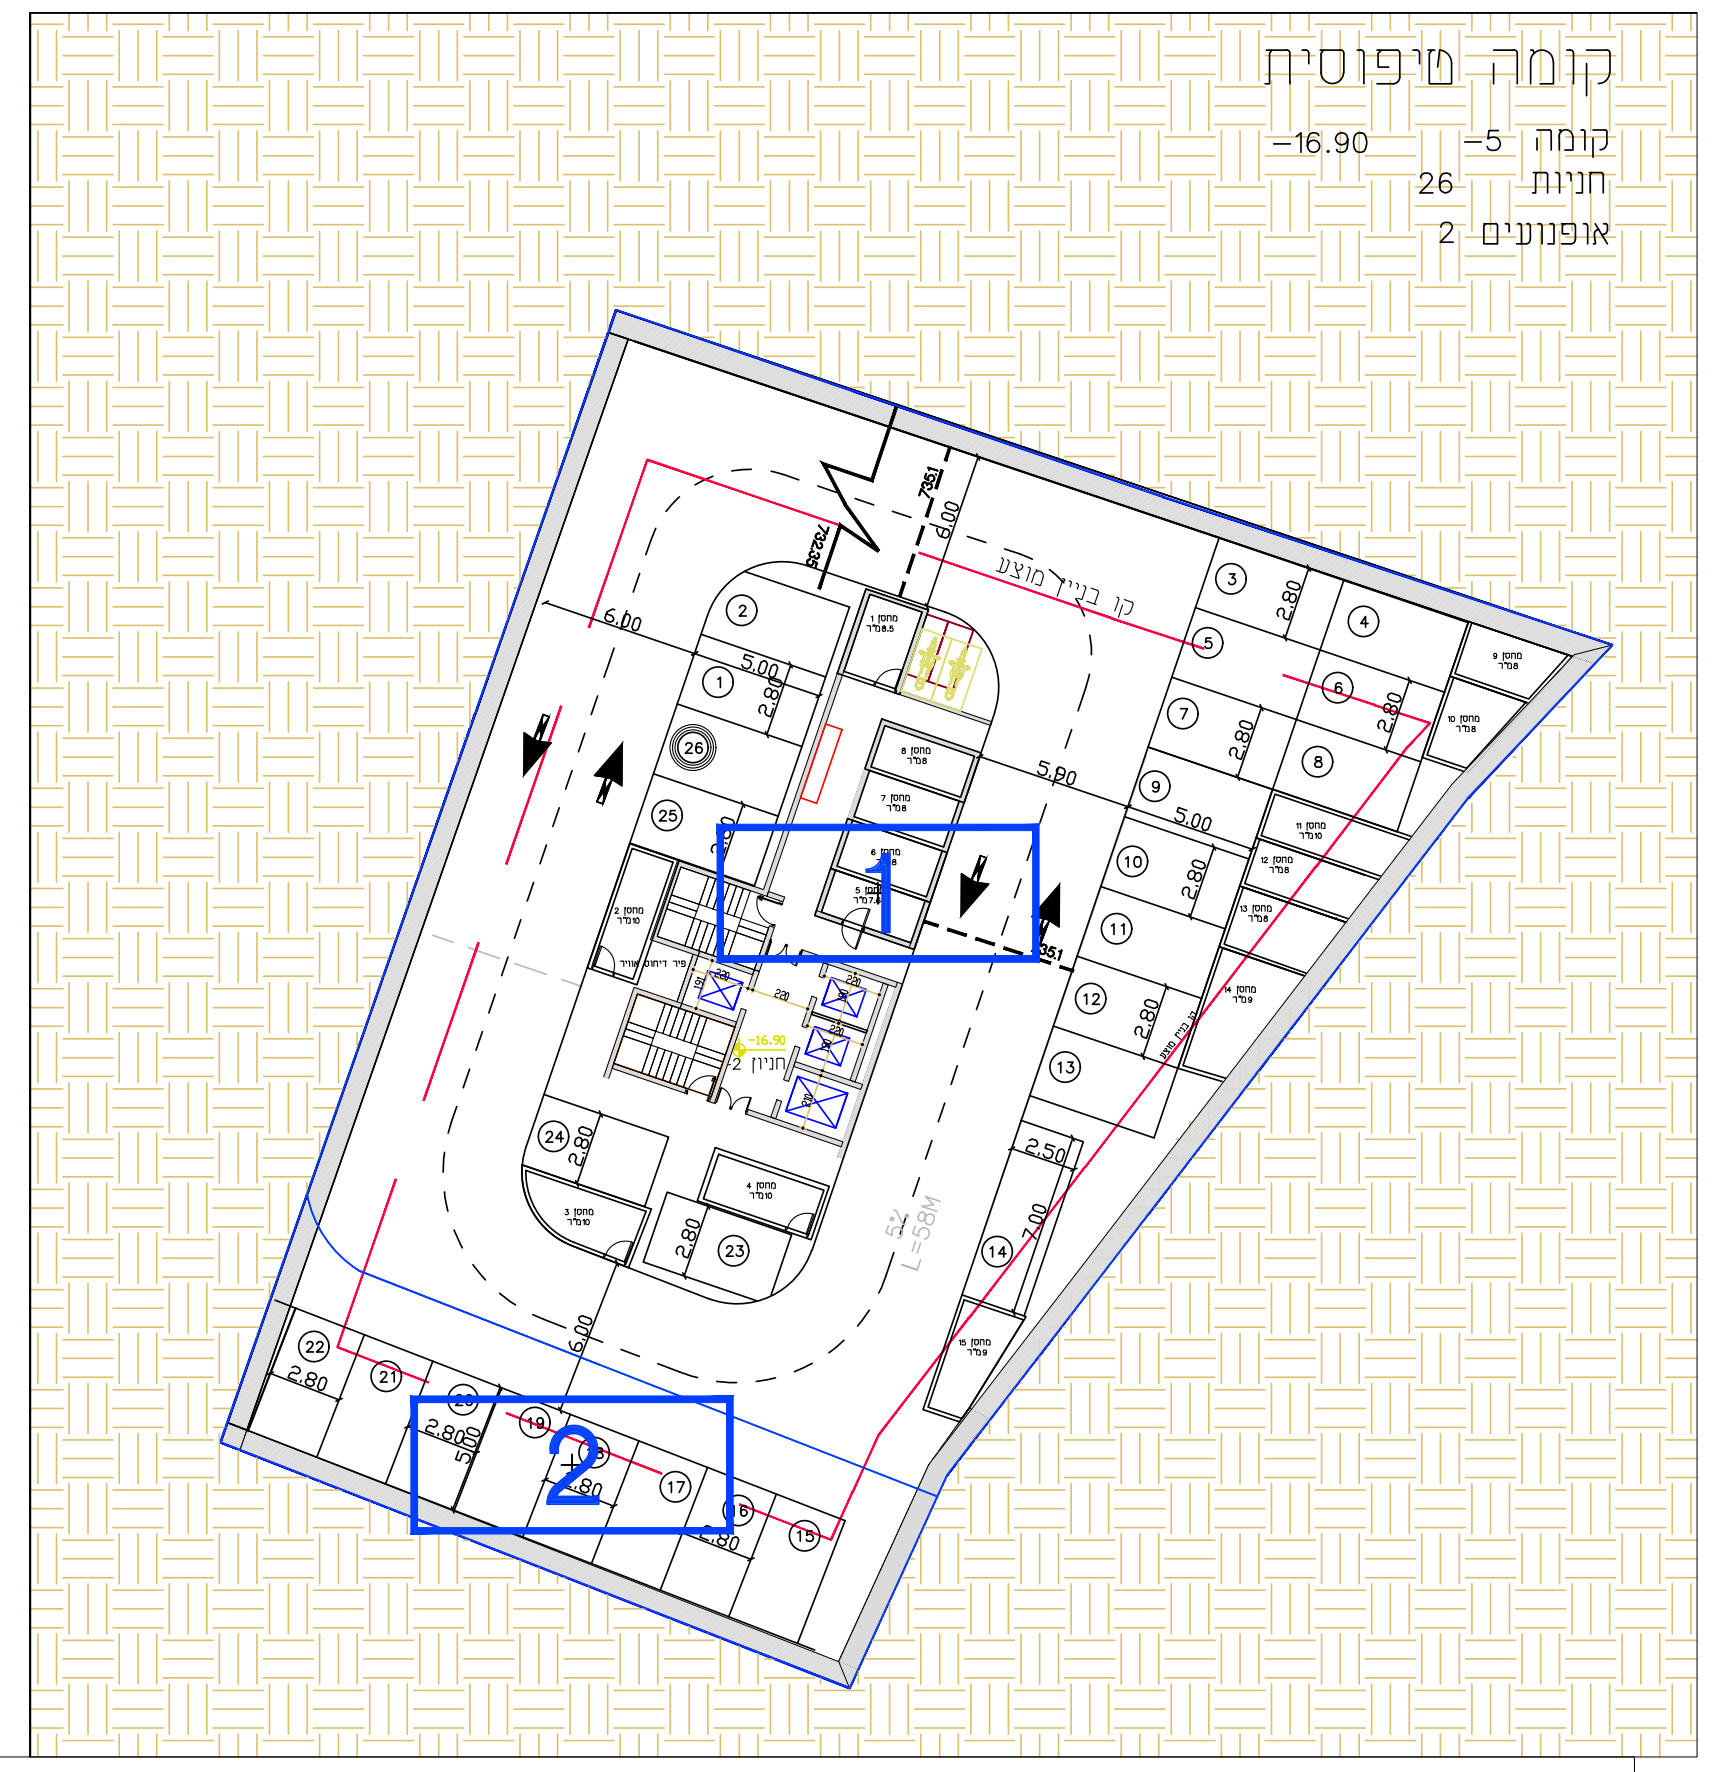

רחוב מחבר חדש
חתך ב-ב מוצע
קנ"מ 1:250

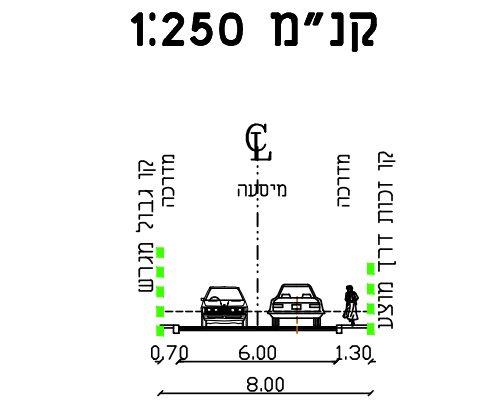

רחוב בני בתירא
חתך א-א
קנ"מ 1:250

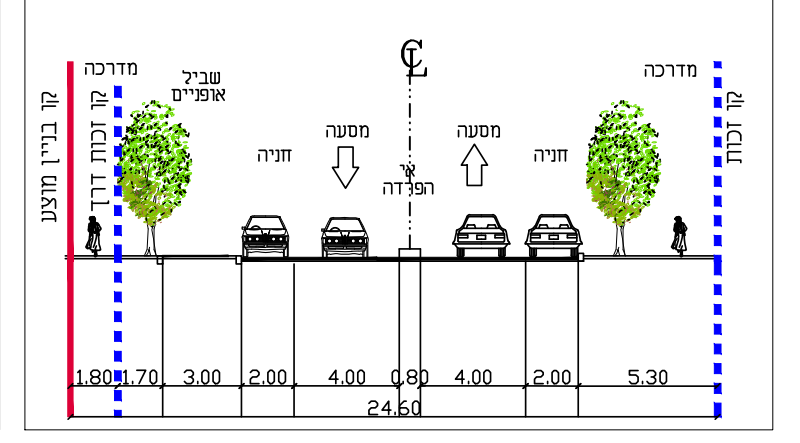

רחוב מחבר חדש
חתך ב-ב עתידי מוצע
קנ"מ 1:250

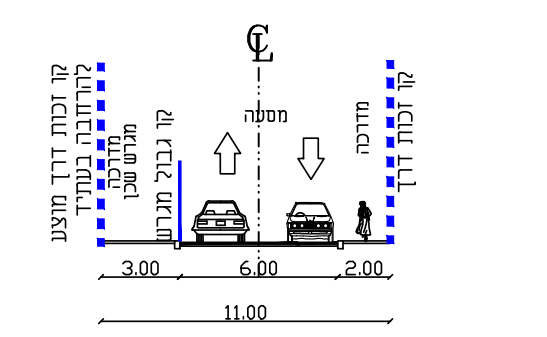

טבלת מאזן חניה - בני בתירא

שמוש קרקע	כמות תקן (שטח עיקרי)	חניית פרטית			חניה תפעולית	חניית אופניים		חניית אופנועים		חניה מתוכננת - תקן מופחת				
		דרישה לפי תקן רגיל	כמות לפי תקן רגיל	כמות לפי תקן בנוני (1.33:1)	דרישה לפי תקן רגיל	דרישה	כמות	דרישה	כמות	מפלס	רכב פרטי	נכים	אופניים	אופנועים
מגורים עד 55 מ"ר	8 יח"ד	1:1	8	0.2 לדירה 2		1:1	123	1:10	12	קומה -1 קומה -2 קומה -3 קומה -4 קומה -5 קומה -6 קומה -7	25 26 26 26 26 14	2 1	3 בפיתוח במחסנים 123	2 3 3 2 2
מגורים בין 55 ל95 מ"ר	39 יח"ד	1:1	39	39										
מגורים מעל 95 מ"ר	76 יח"ד	2:1	152	102										
גני ילדים	195 מ"ר	1:40 מ"ר	4	2		1:10 תלמידים	3			קומה -1	2			
אורחים	10%	10%	12	12						קומה -1	12			
סה"כ			215	157			126		12		160	126	12	
סה"כ כולל נכים				160										

מפת מרחקי הליכה מציר רק"ל

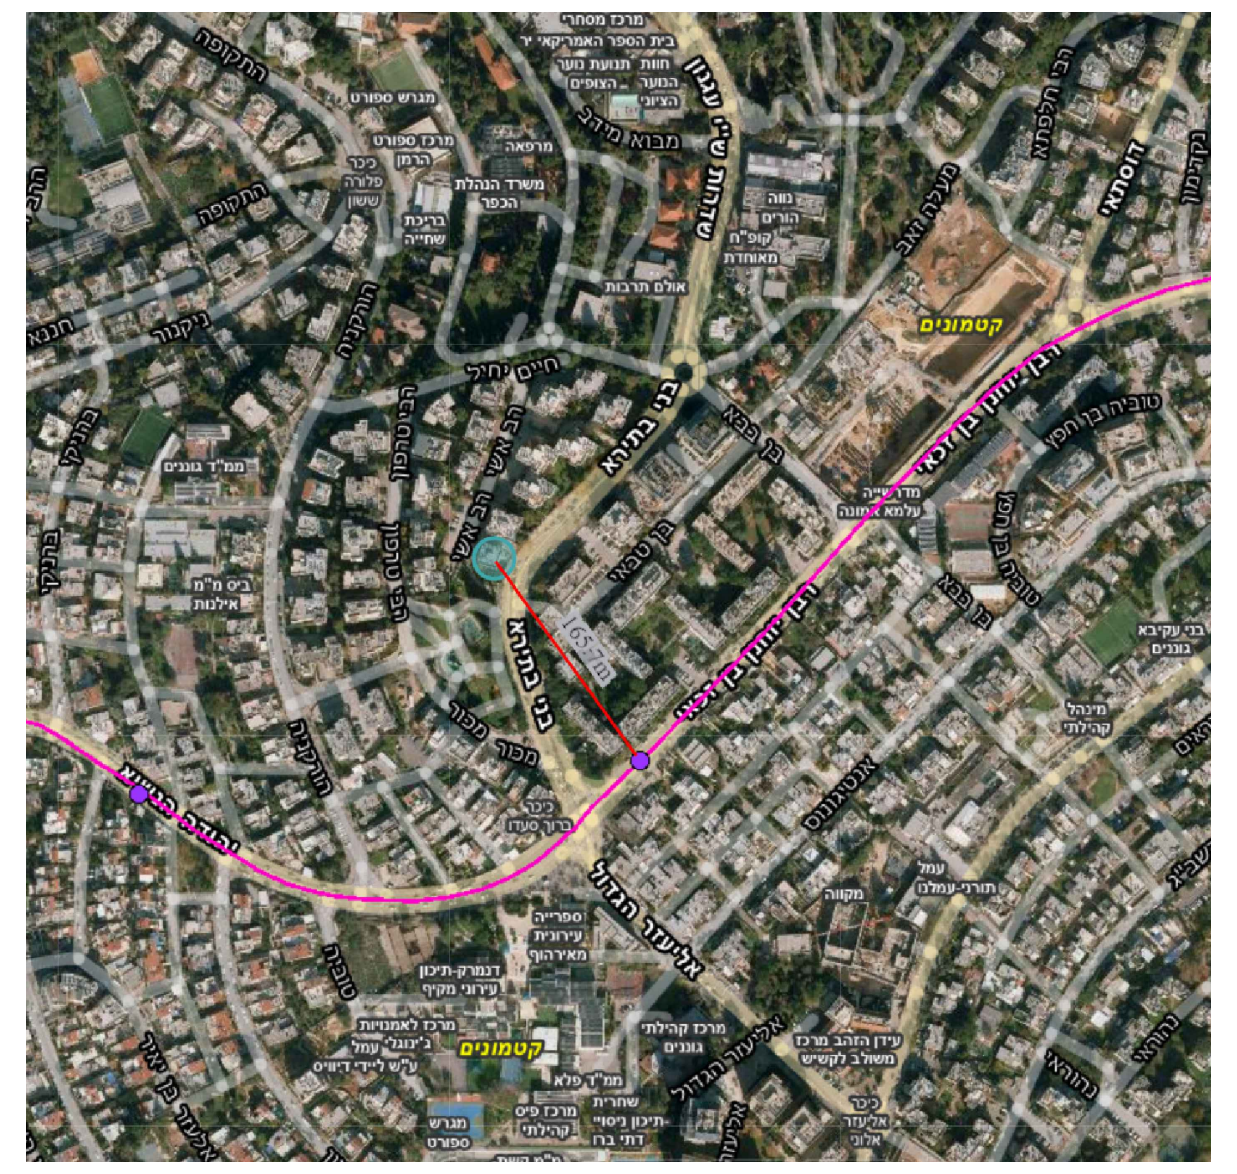

שמות וחתימות:

עורך הנספח	שם: כ.דוד תאגיד: **אמאב תחבורה ותנועה בע"מ**	חתימה:

אמאב
תחבורה ותנועה (2012) בע"מ
AMAV Transportation & Traffic Ltd