
תכנית 101-1386671 נספח ביוב נספח ביוב - תכנית
05/08/2026 20:27:19

מינהל התכנון
חוק התכנון והבניה, התשכ"ה - 1965
מחוז ירושלים
הוועדה המחוזית החליטה ביום :
30/11/2025
להפקיד את התכנית
05/10/2026
תאריך
יו"ר הוועדה המחוזית

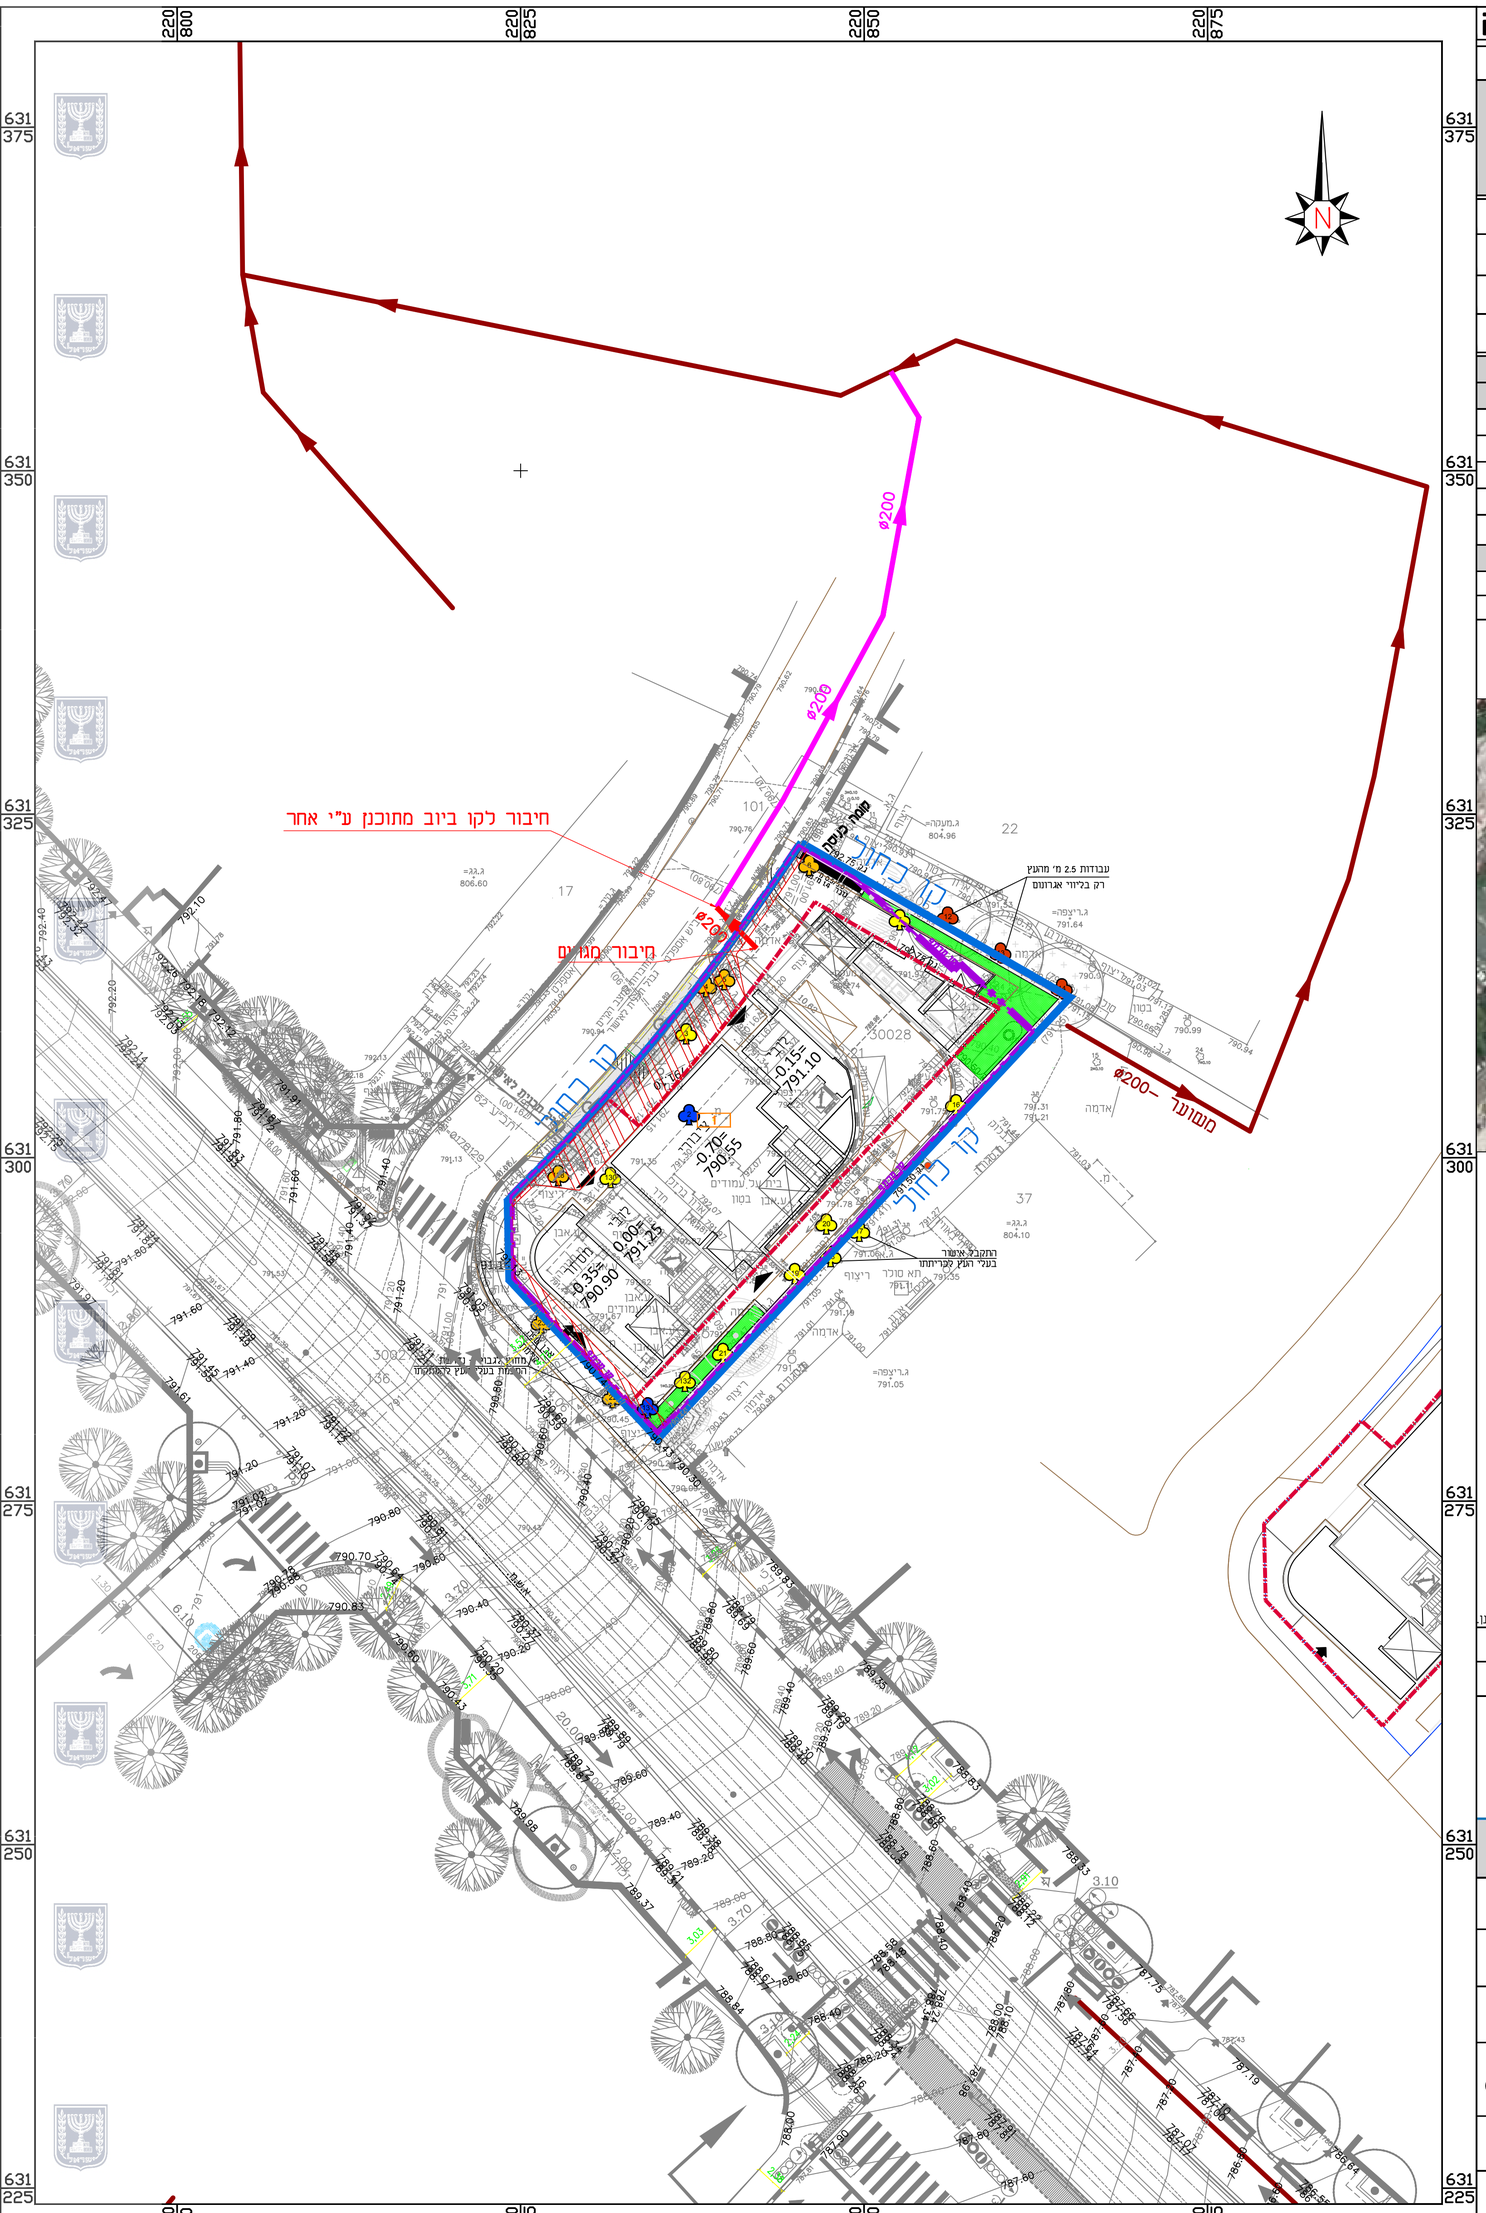

נספח ביוב - תנוחה

נספח לתכנית מס' 101-1386671

התחדשות עירונית-לינקולן 13

גליון 2 מתוך 3


תחולה	מנחה
תיאור	נספח ביוב
תאריך עריכת הנספח	05.08.2026
קנ"מ	1:250

תרשימים נוספים	קנ"מ

שמות וחתימות:

עורך הנספח	שם:	אורן גבעון
	תאגיד:	י.לבל מהנדסים יועצים בע"מ

מפת הסביבה

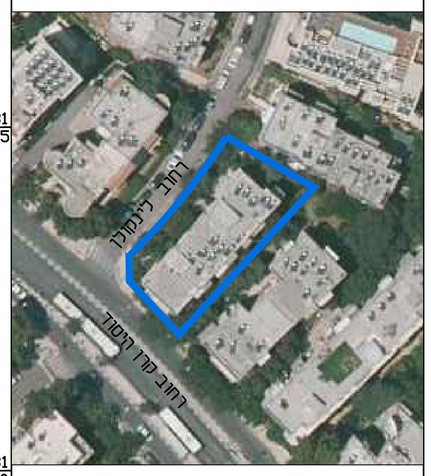

מקרא :

- קו כחול
- גבול מרתף
- קו בניין
- שטחי גינון
- זיקת הנאה
- קו ביוב מתוכנן
- קו ביוב מתוכנן ע"י אחר
- קו ביוב קיים

הקבלן אחראי לבדיקת המידות שבתכנית. על כל טעות, סתירהאו אי התאמה עליו להודיע למתכנן. אין לקבוע מידות ע"י מדידה בשרטוט אלא באישור המתכנן.
התכנית הנה רכושו הבלעדי של המתכנן ובעבלותו מוגנת ע"י חוק זכויות היוצרים.
אין לעשות כל שימוש בתכנית זו ובהרעיונות הגלומים בה ללא אישור מראש ובכתב של המתכנן.

לעיון	למכרז	לביצוע
●	○	○

י.לבל
Y.LEBEL
מהנדסים יועצים בע"מ
CONSULTING ENGINEERS LTD
נחלת יצחק 32א' ת"א, 67448
טל': 03-6952418 פקס: 03-6916647
lebel@lebel.co.il www.lebel.co.il
32a Nahlat Yitzhak st. Tel Aviv, 67448 tel:03- 6952418 fax:03-6916647

שם הפרויקט:
התחדשות עירונית-לינקולן 13

שם המזמין:
תמייא טופ בעיים

שם הגליון:
נספח ביוב - תנוחה

מס' הפרויקט:	מס' הגליון:	תאריך:
3220	02	08.10.24

ק.מ.:	מהדורה:	תאריך עדכון:	סה"כ גיליונות:	מידות הגליון:
1:250	2	05.08.26	3	65x55

תכנן:	שרטט:	בדק:	אשר:	תאריך:
אדהם.ח	הדסה.א	מיתר.ק	אורן.ג	

שם הקובץ C:\Users\inna\2PLAN Dropbox\LEBEL TEAM\3220\TICHNUN\MAIN_3220.dwg