מינהל התכנון
חוק התכנון והבניה, התשכ"ה - 1965
מחוז ירושלים
הוועדה המחוזית החליטה ביום :
30/11/2025
להפקיד את התכנית
05/10/2026
יו"ר הוועדה המחוזית　　　תאריך

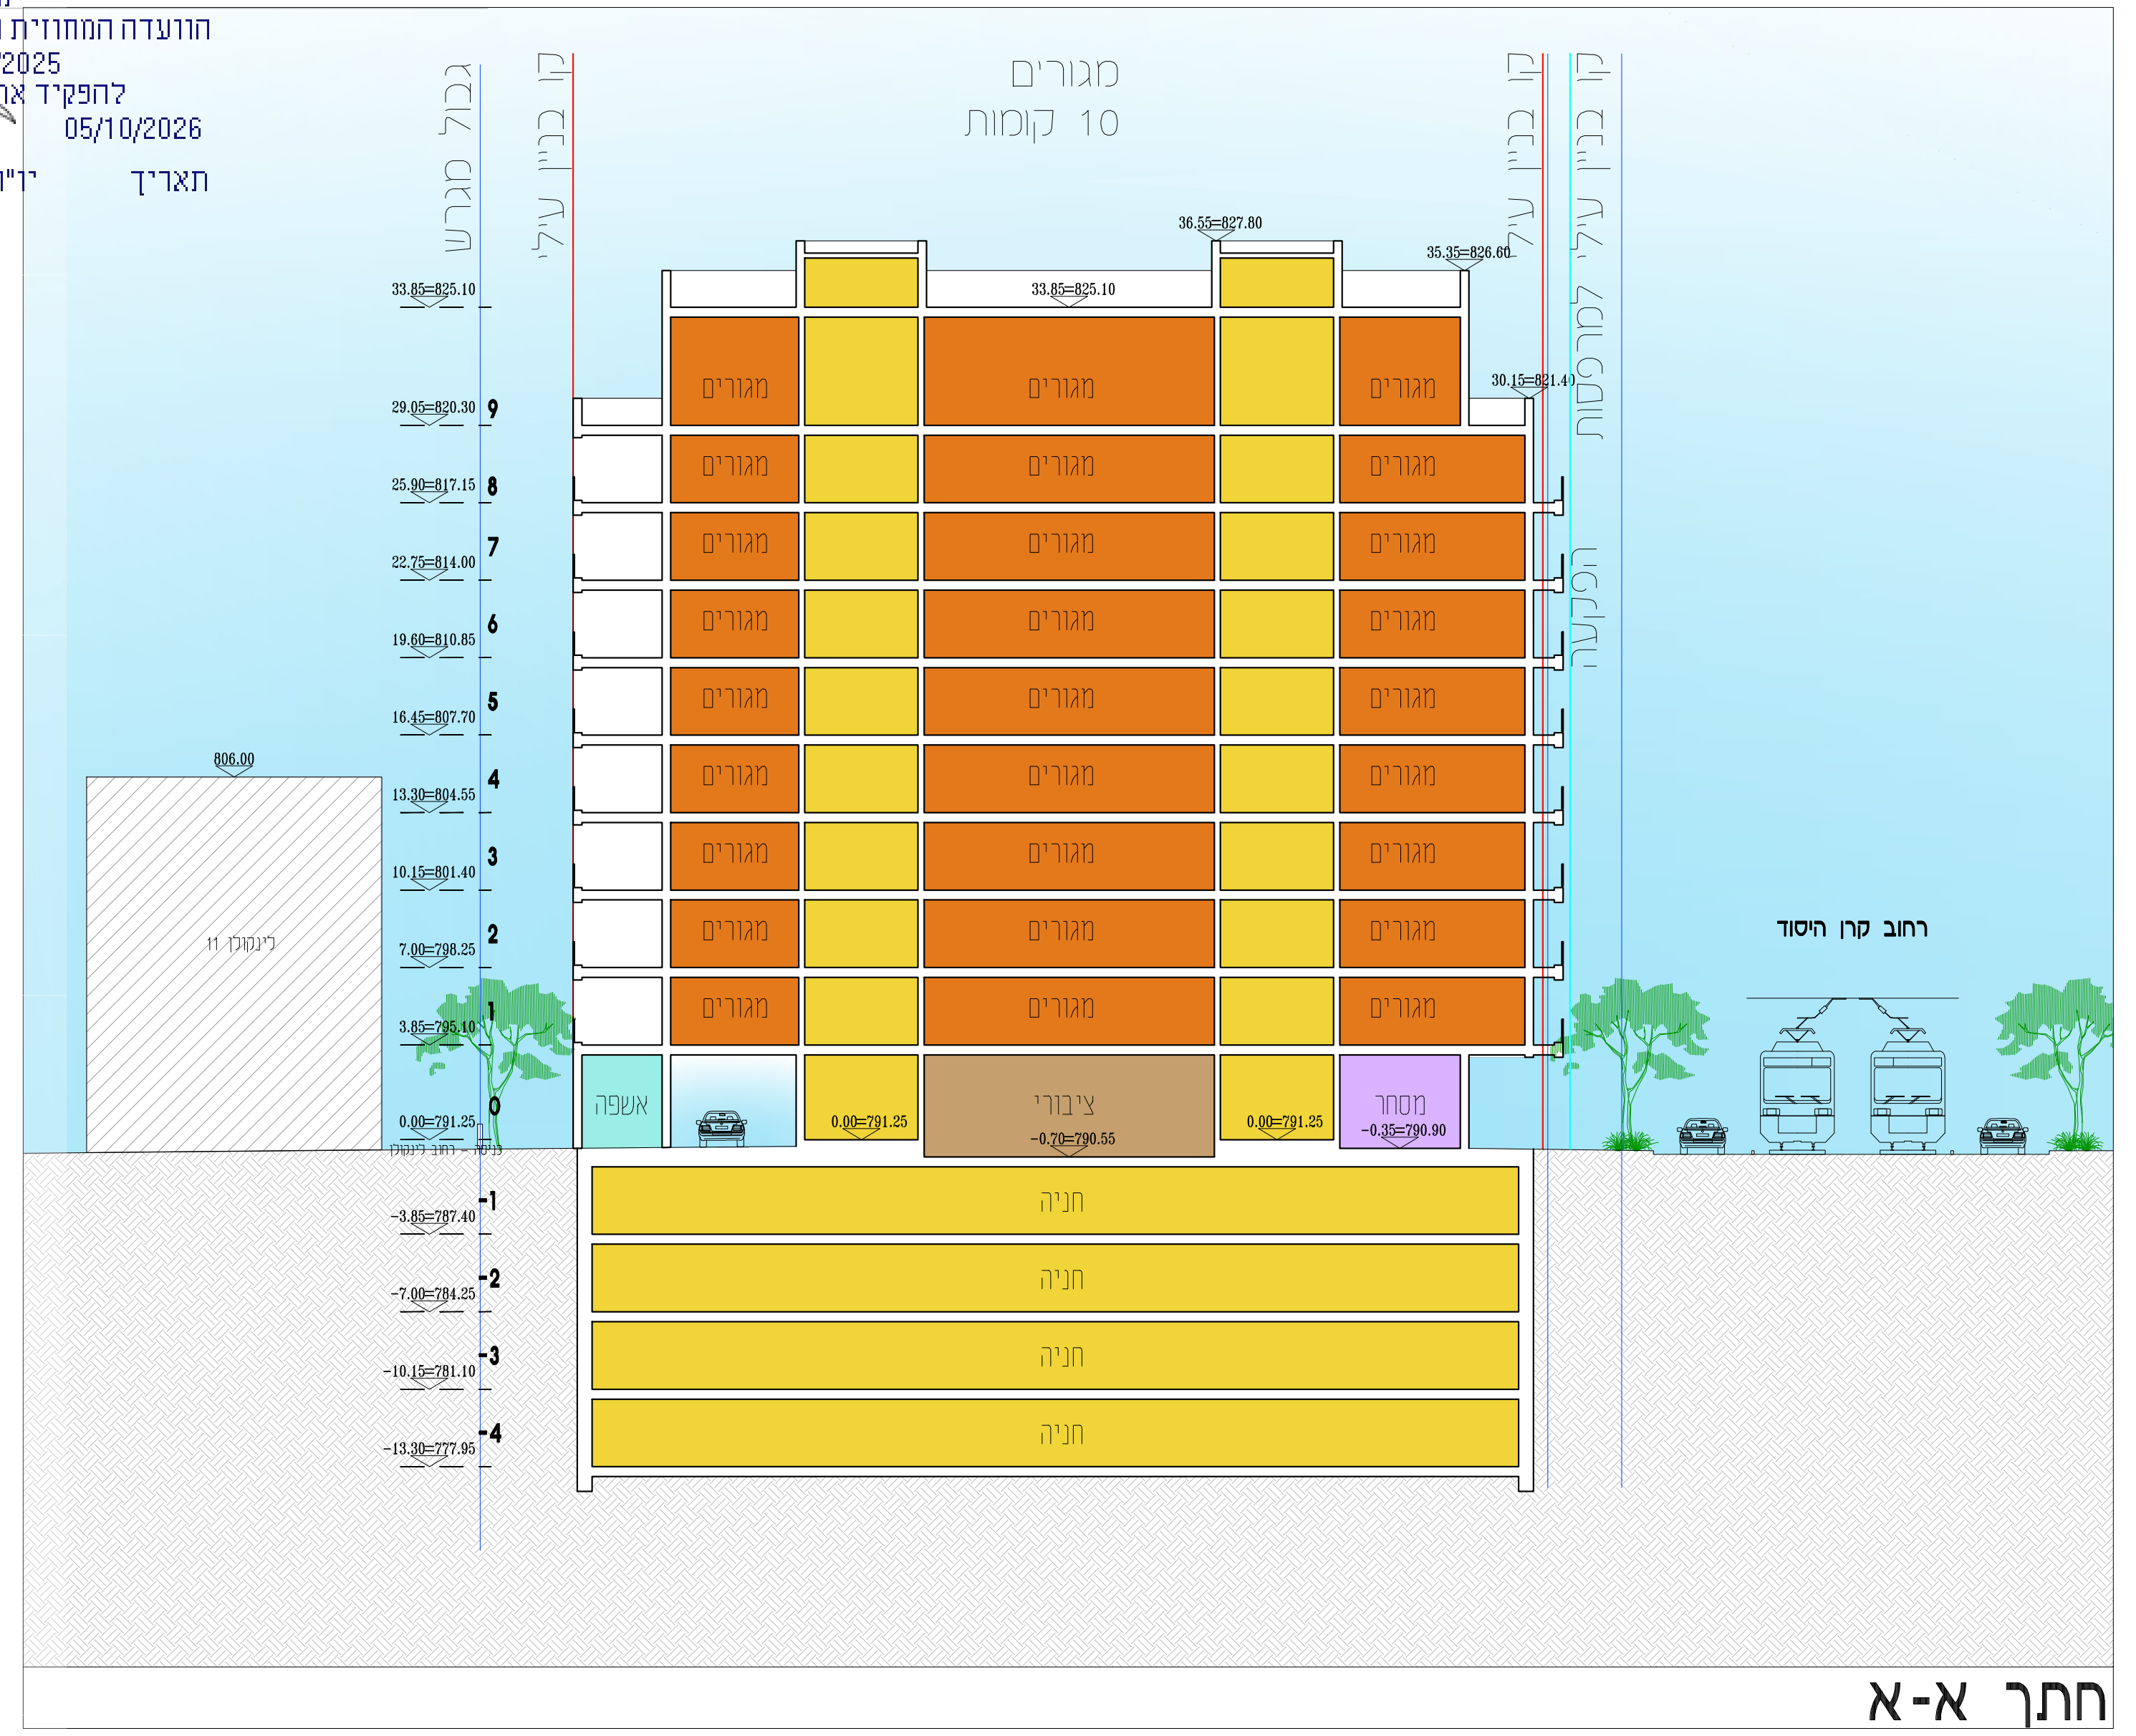

חתך א-א

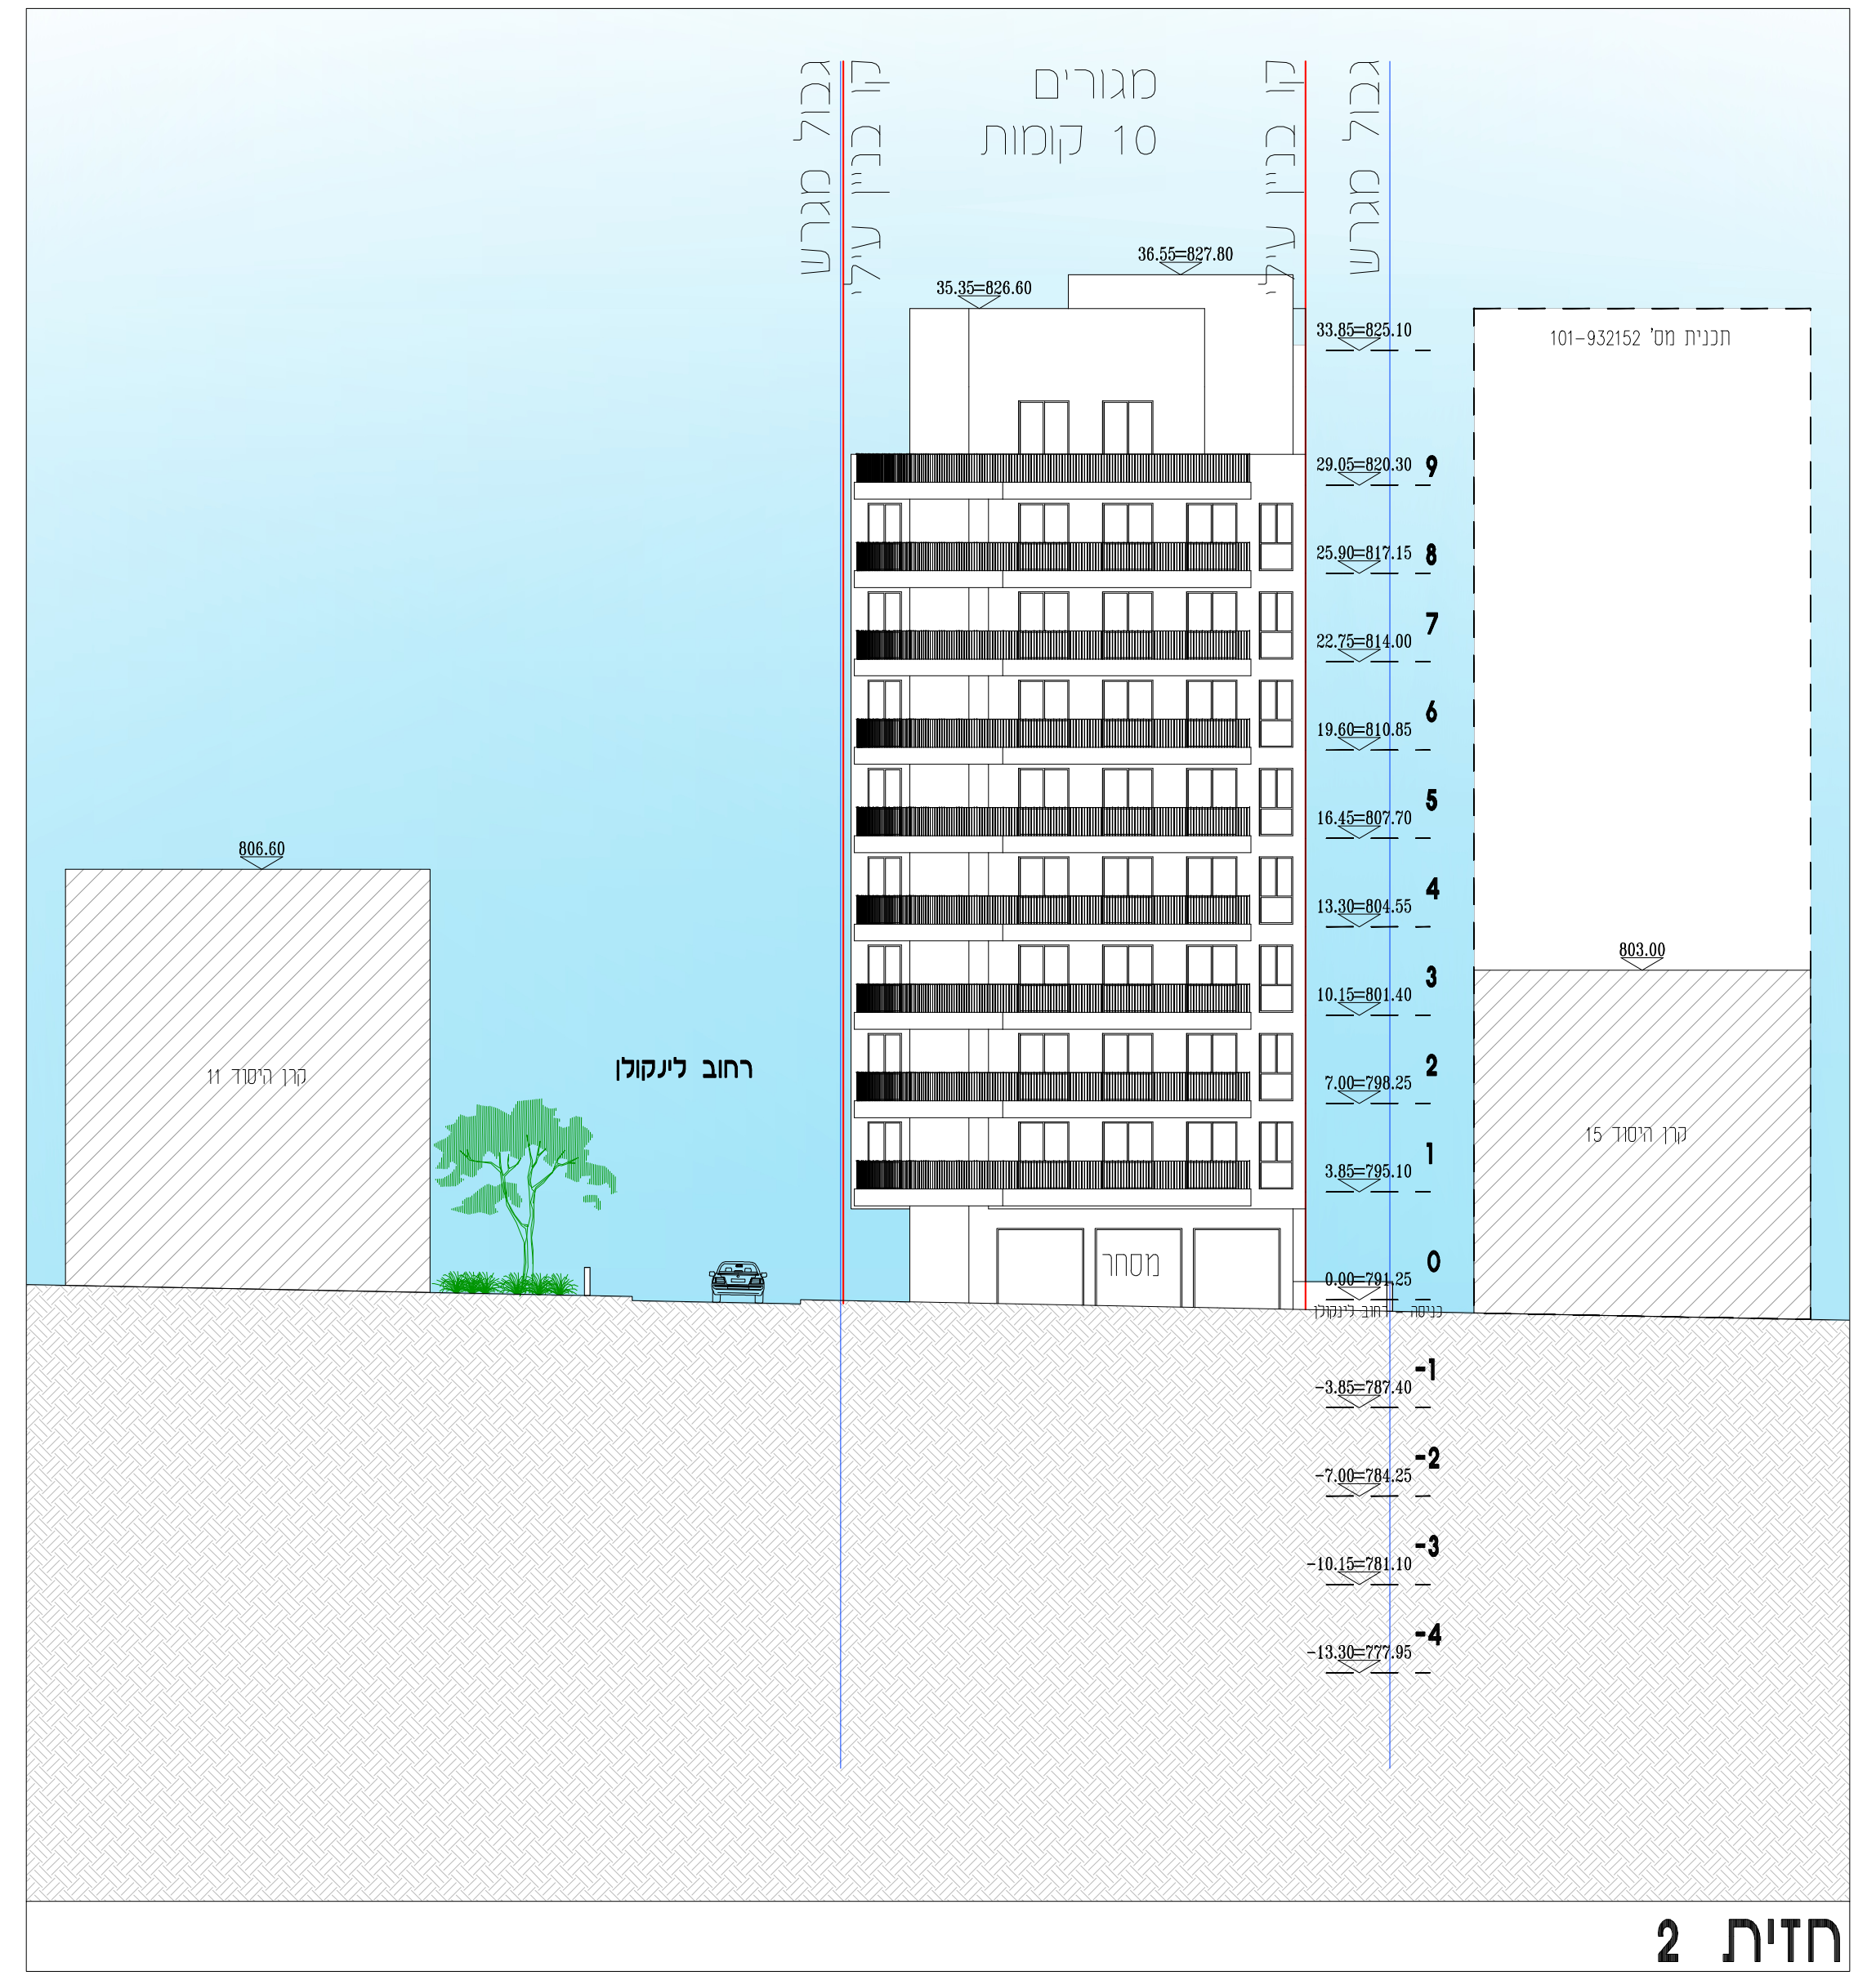

חזית 2

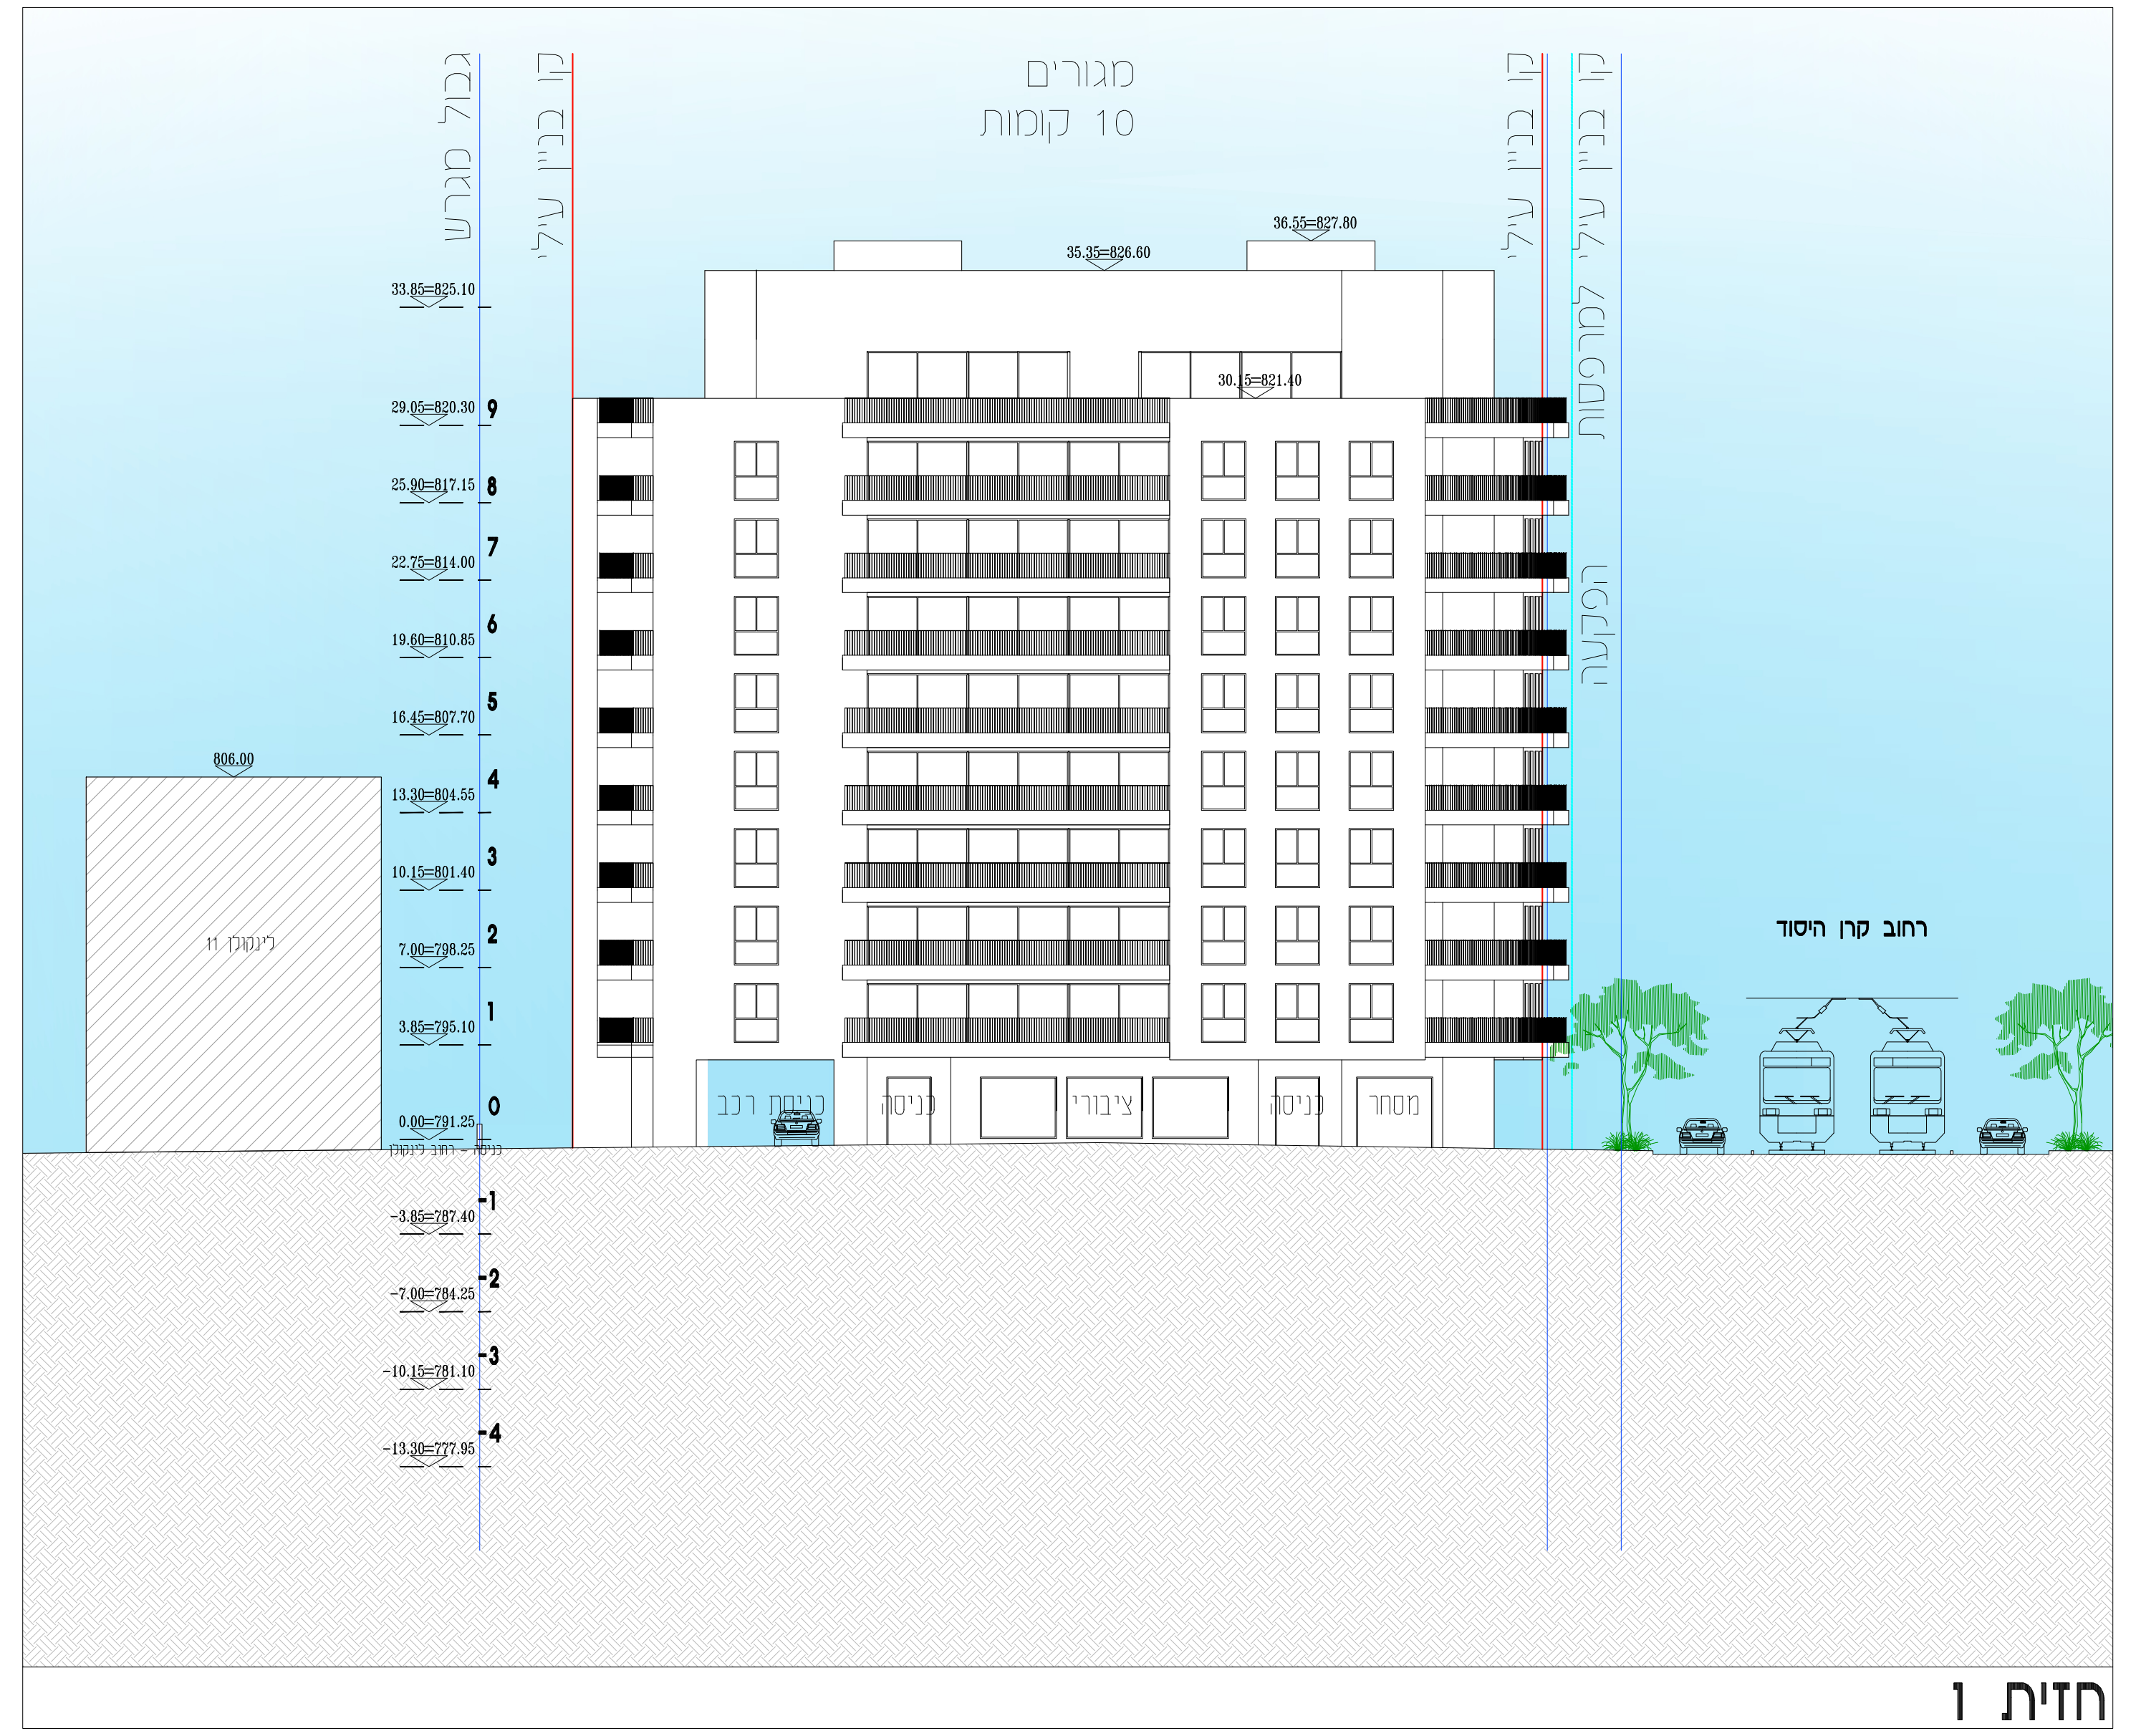

חזית 1

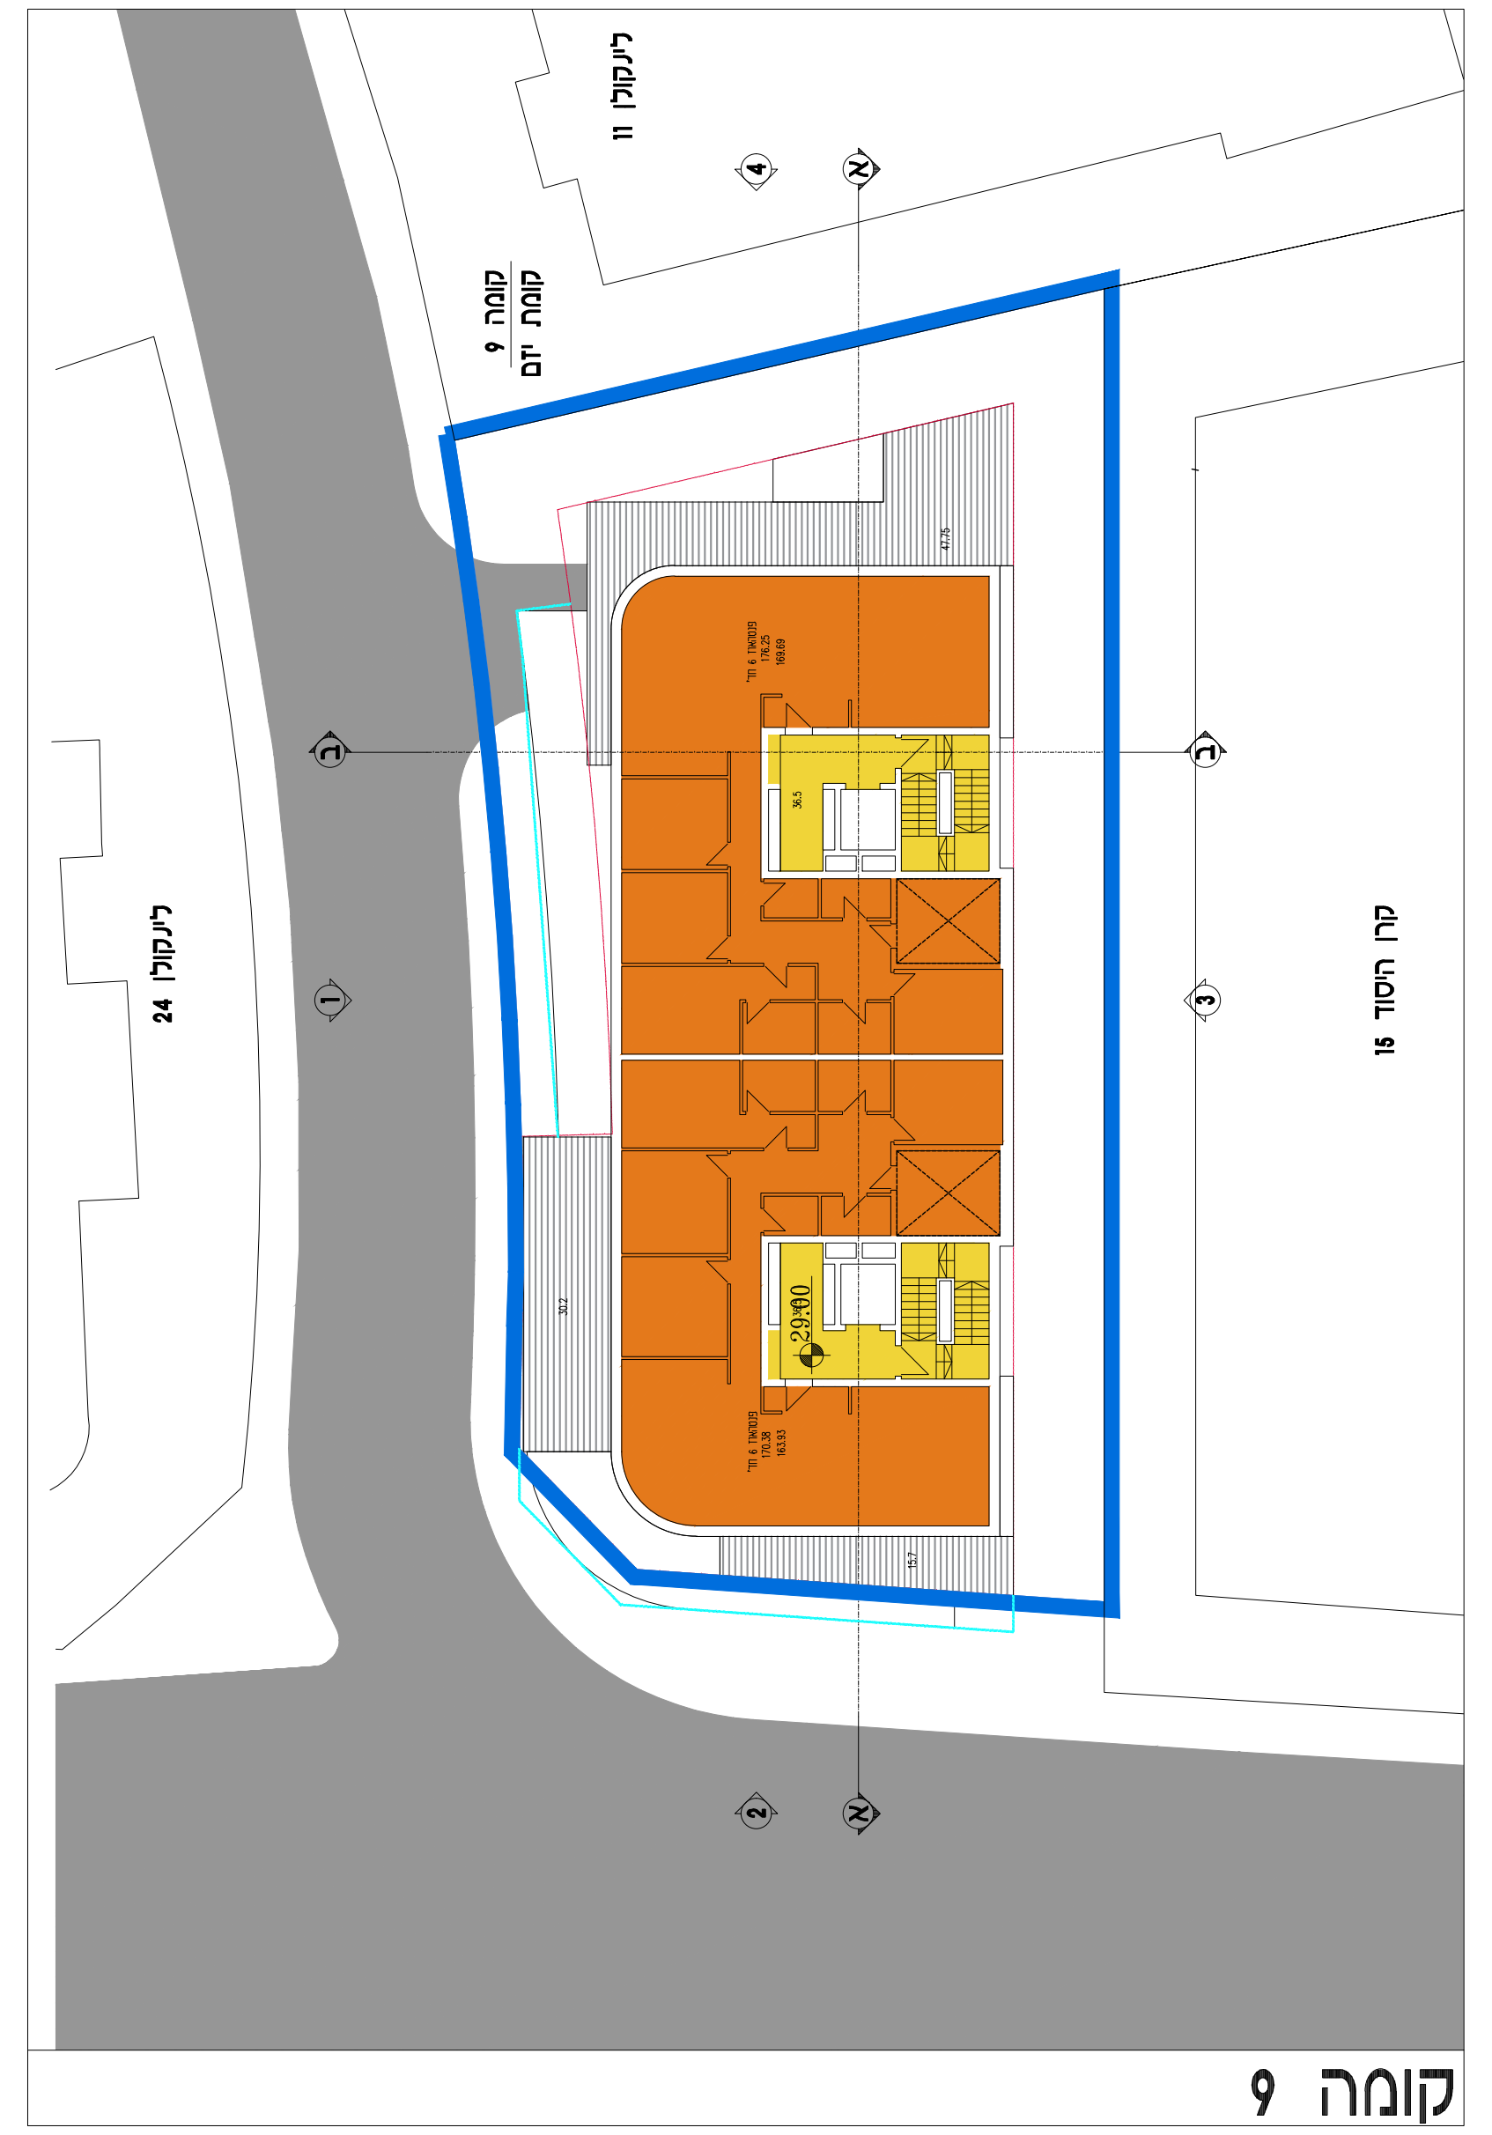

קומה 9

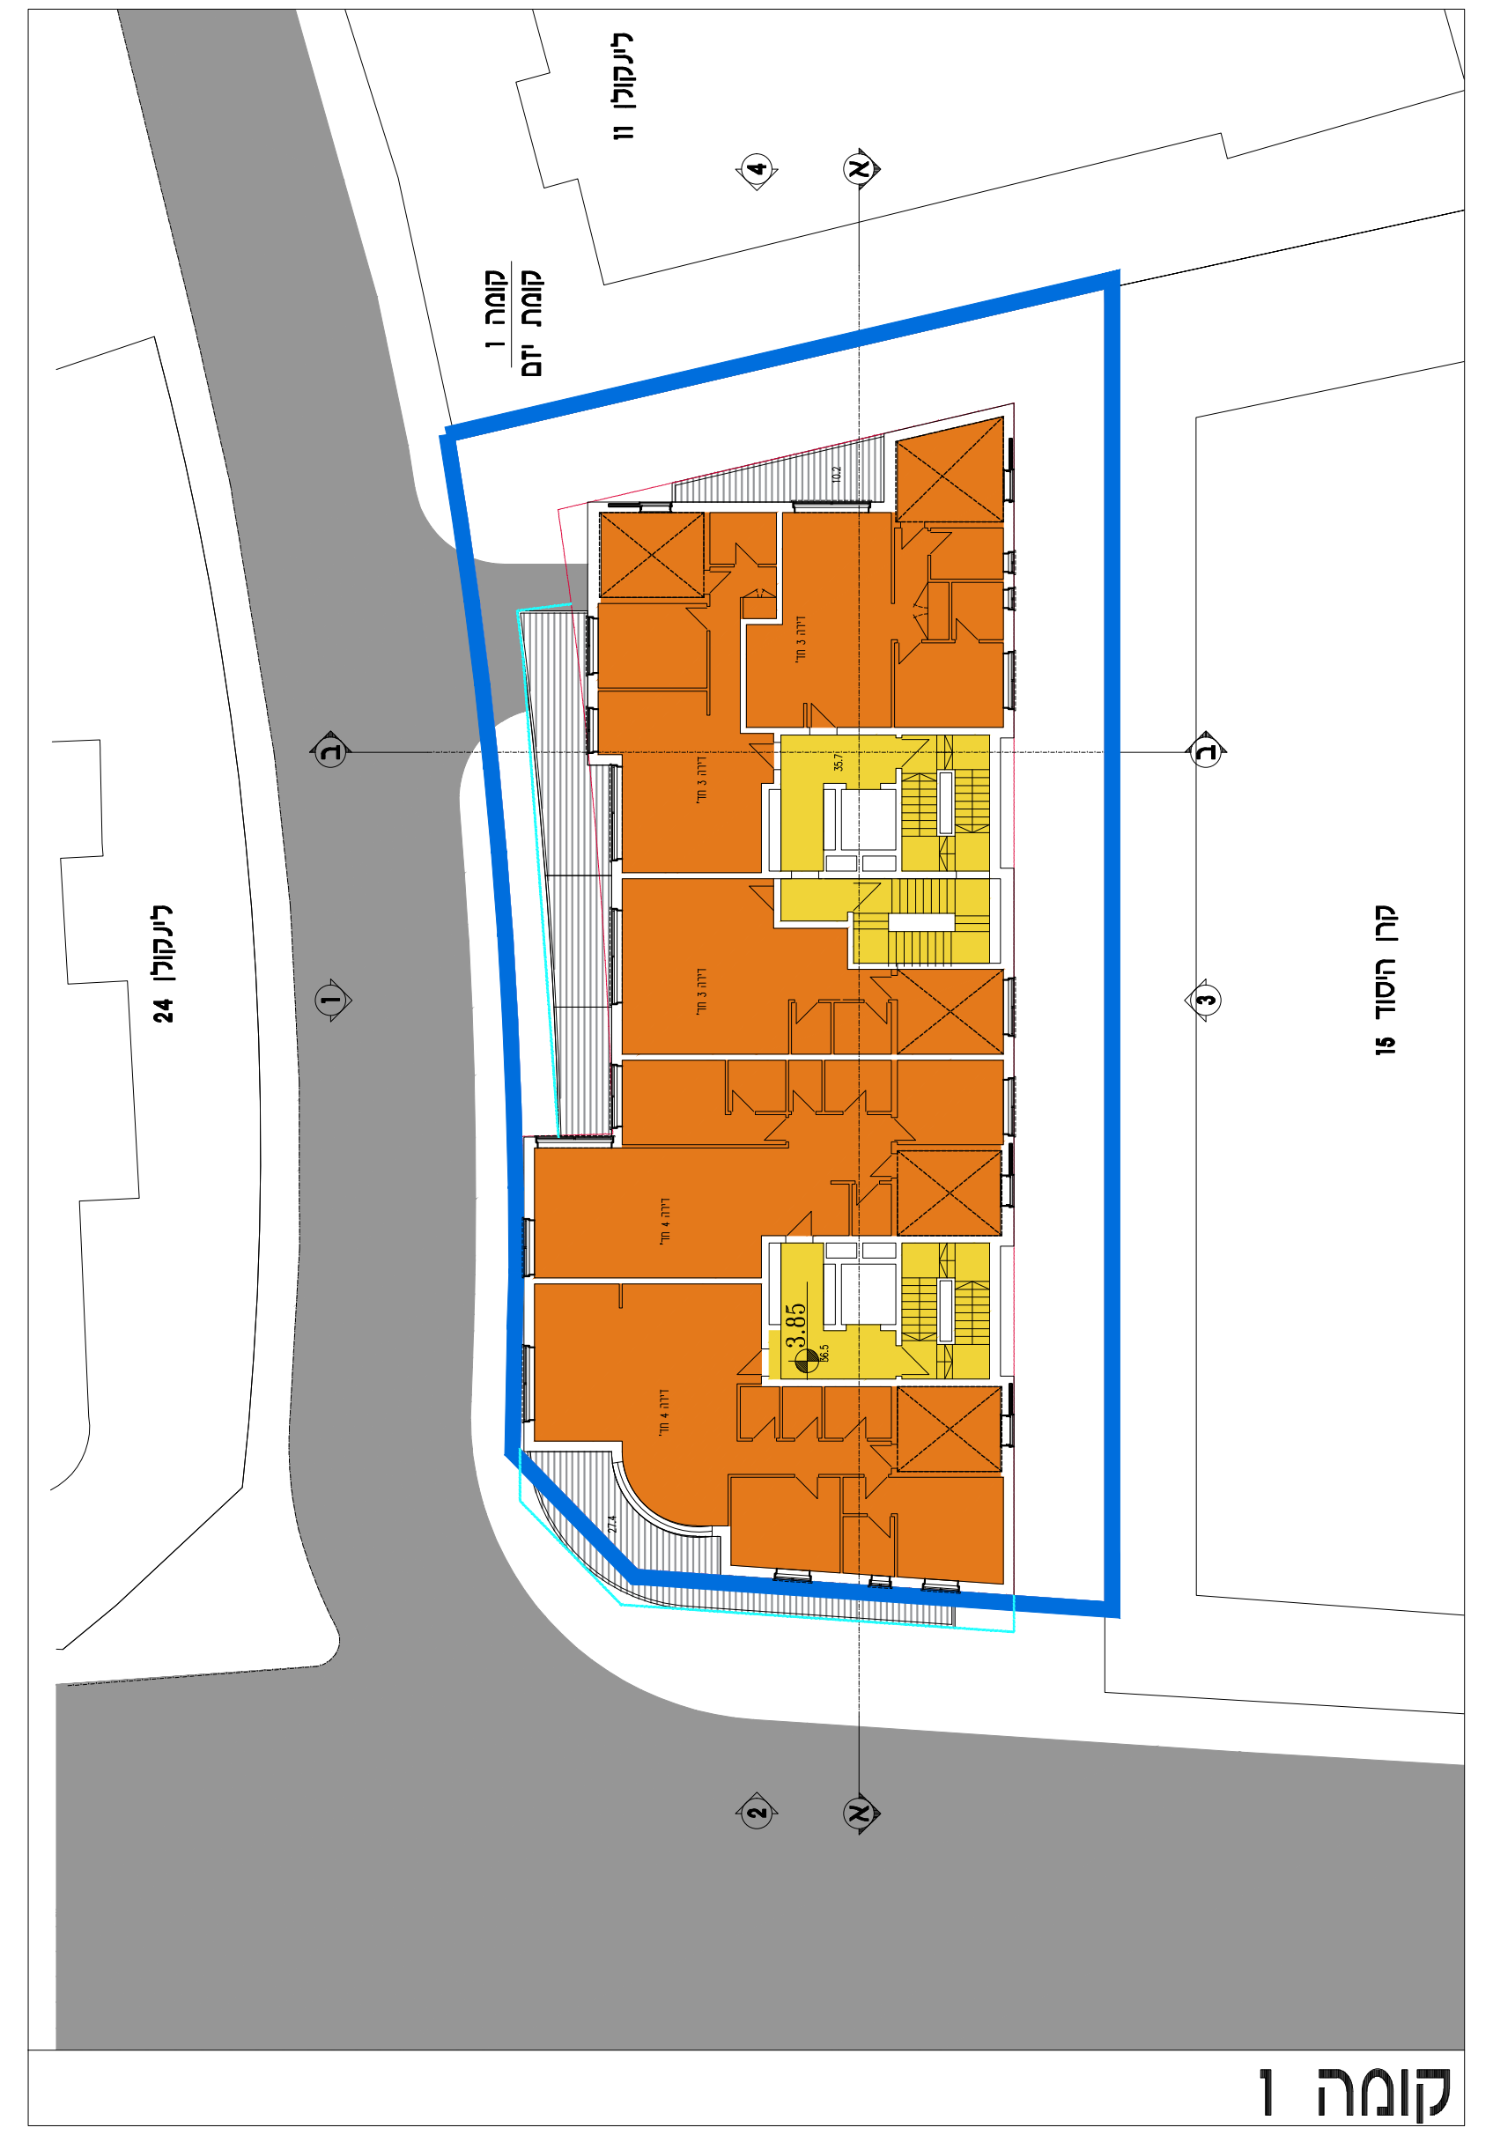

קומה 1

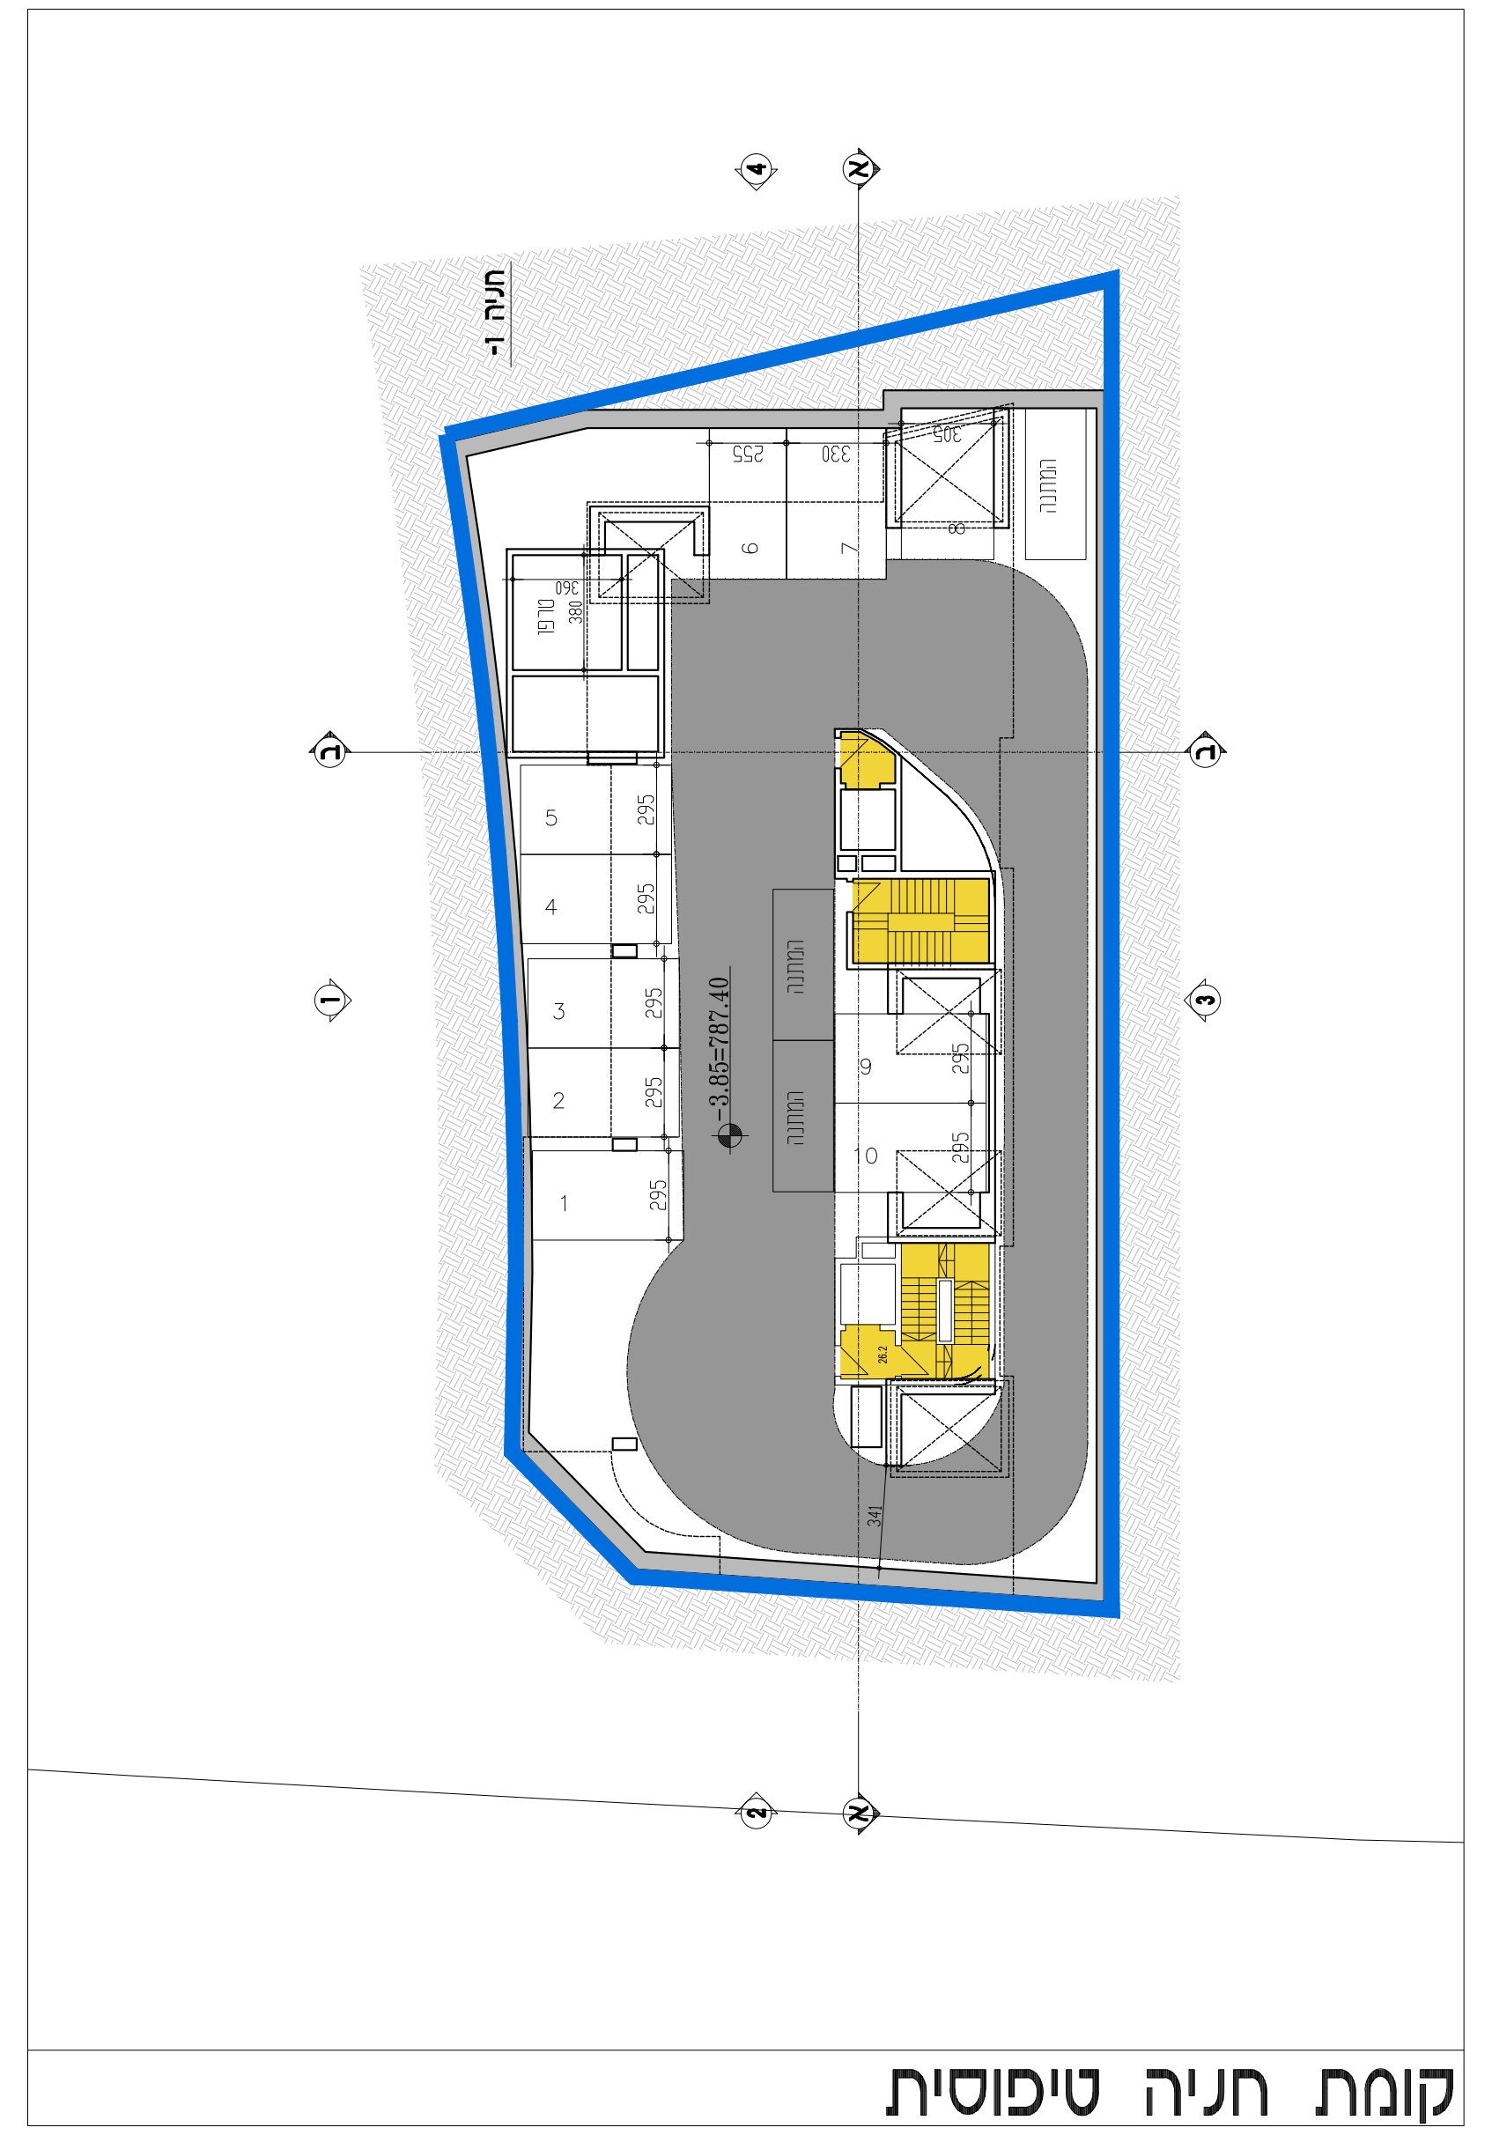

קומת חניה טיפוסית

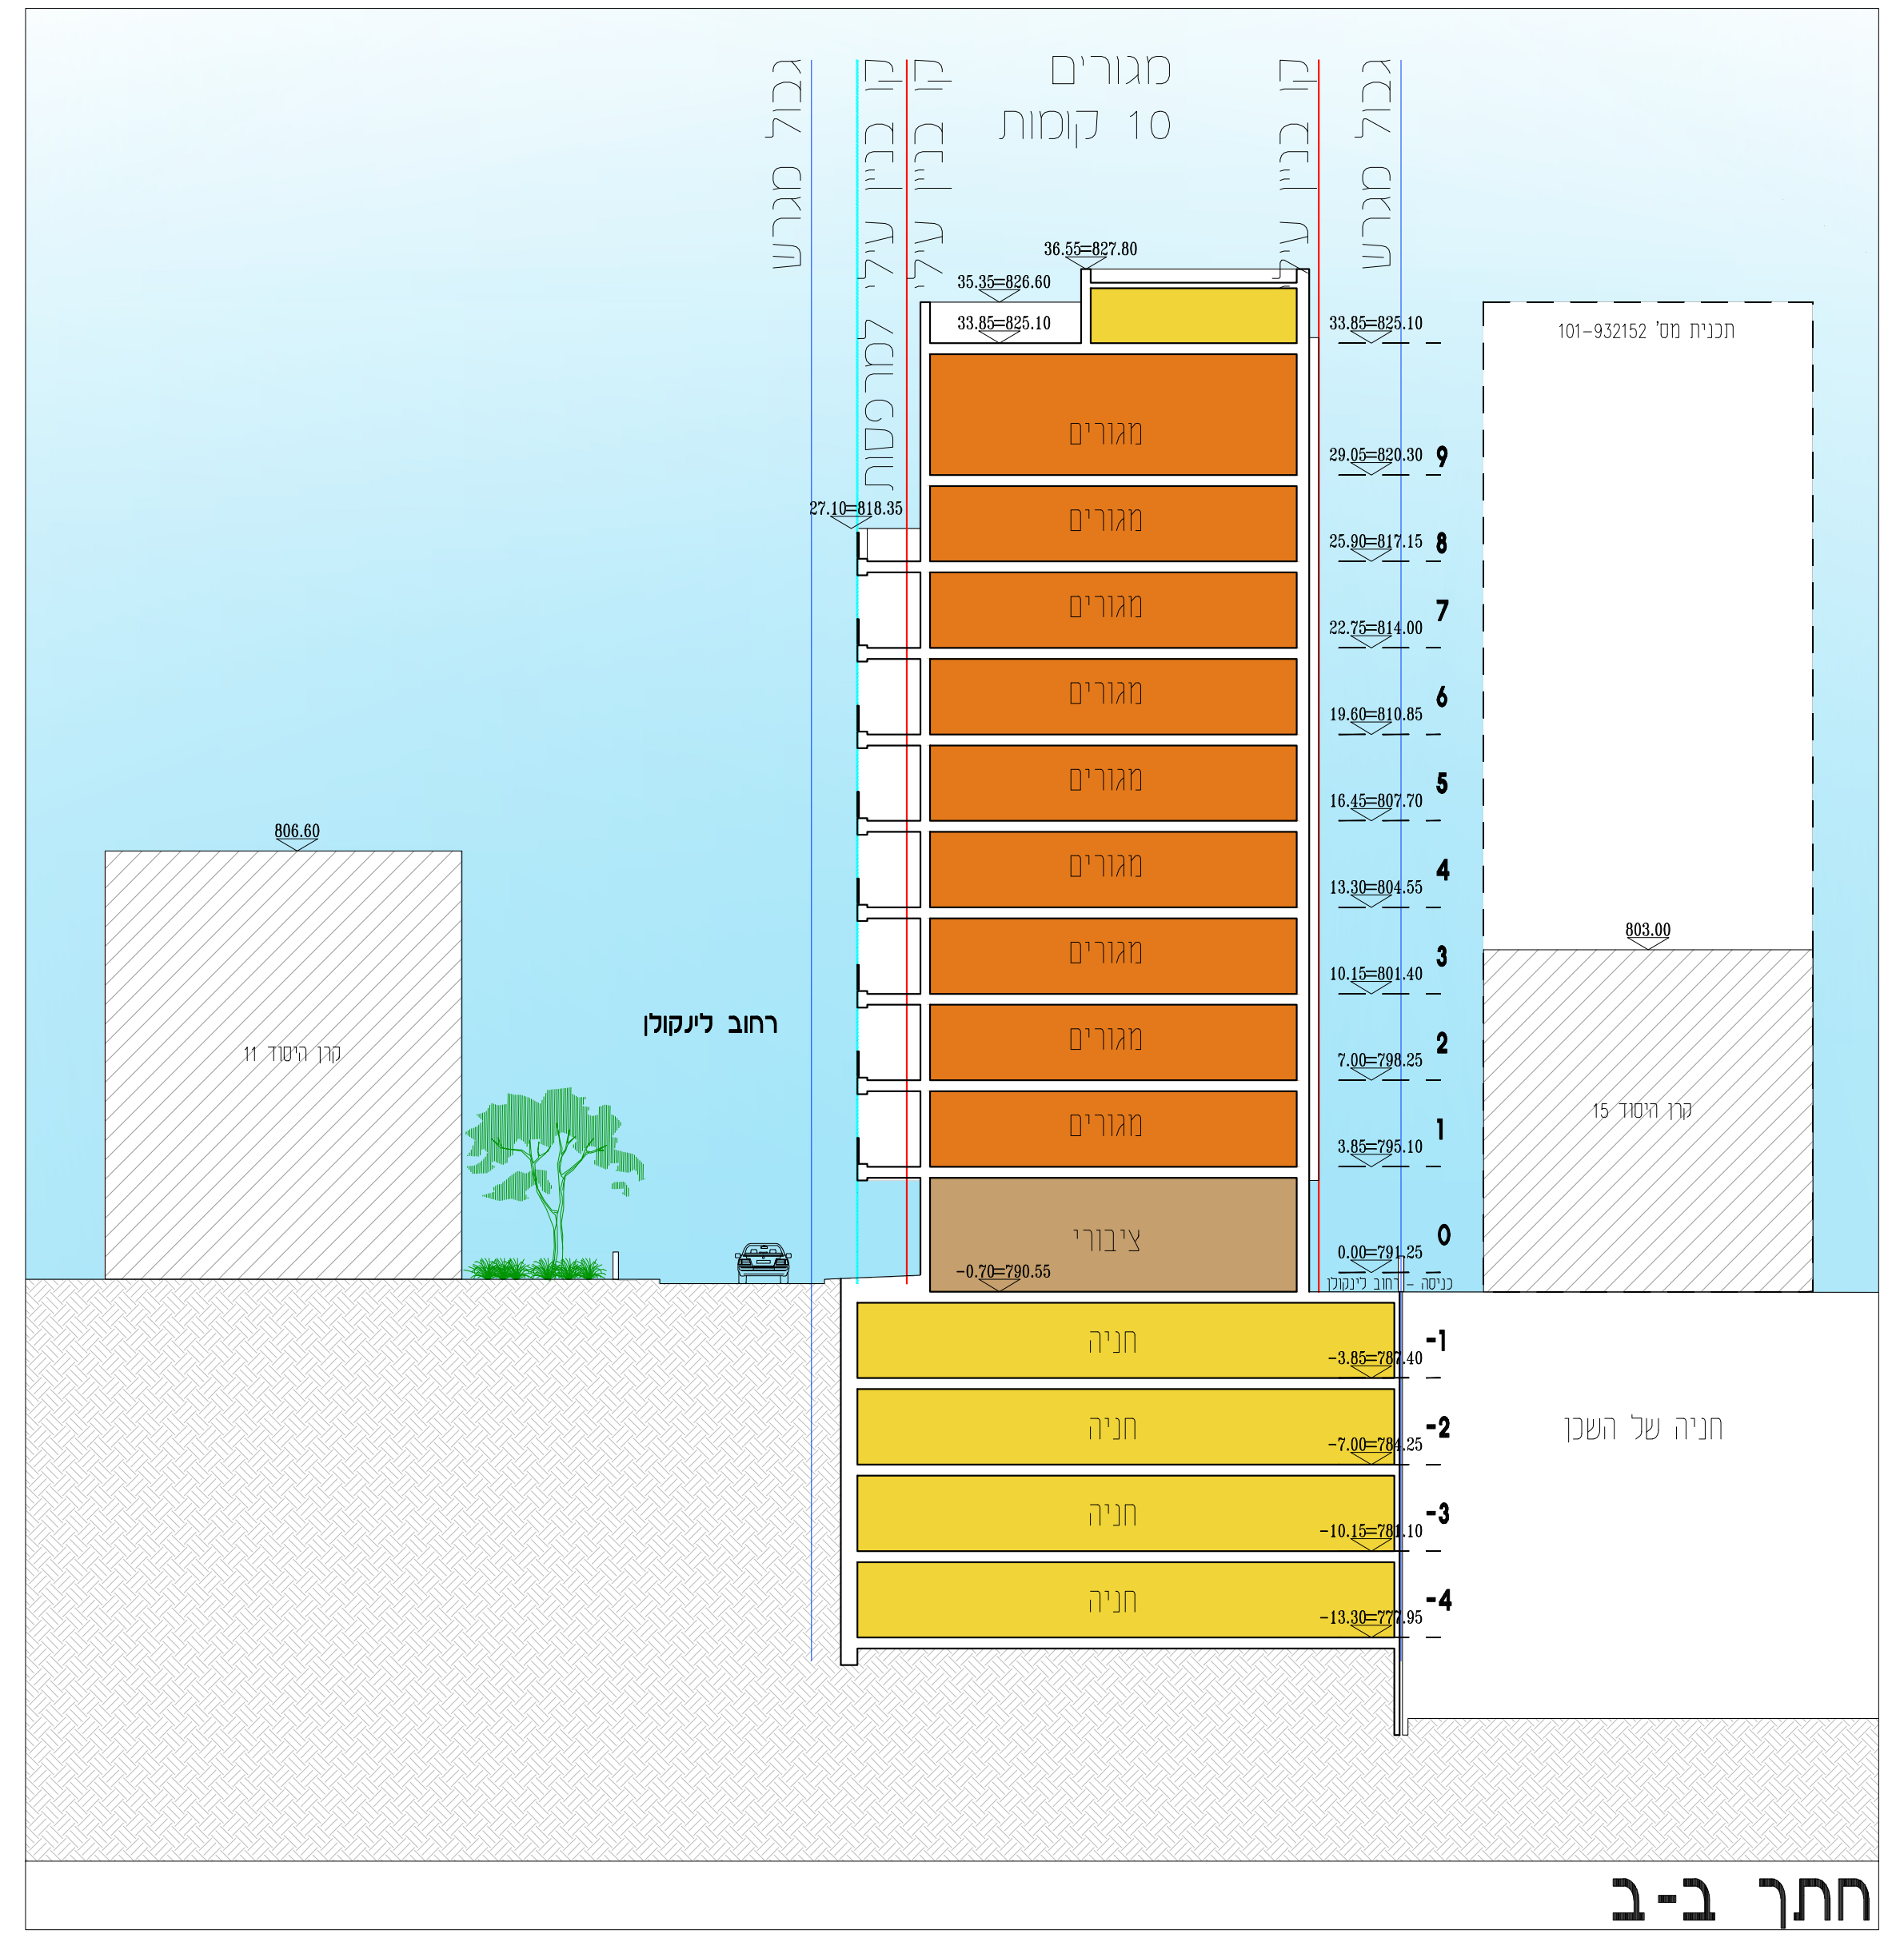

חתך ב-ב

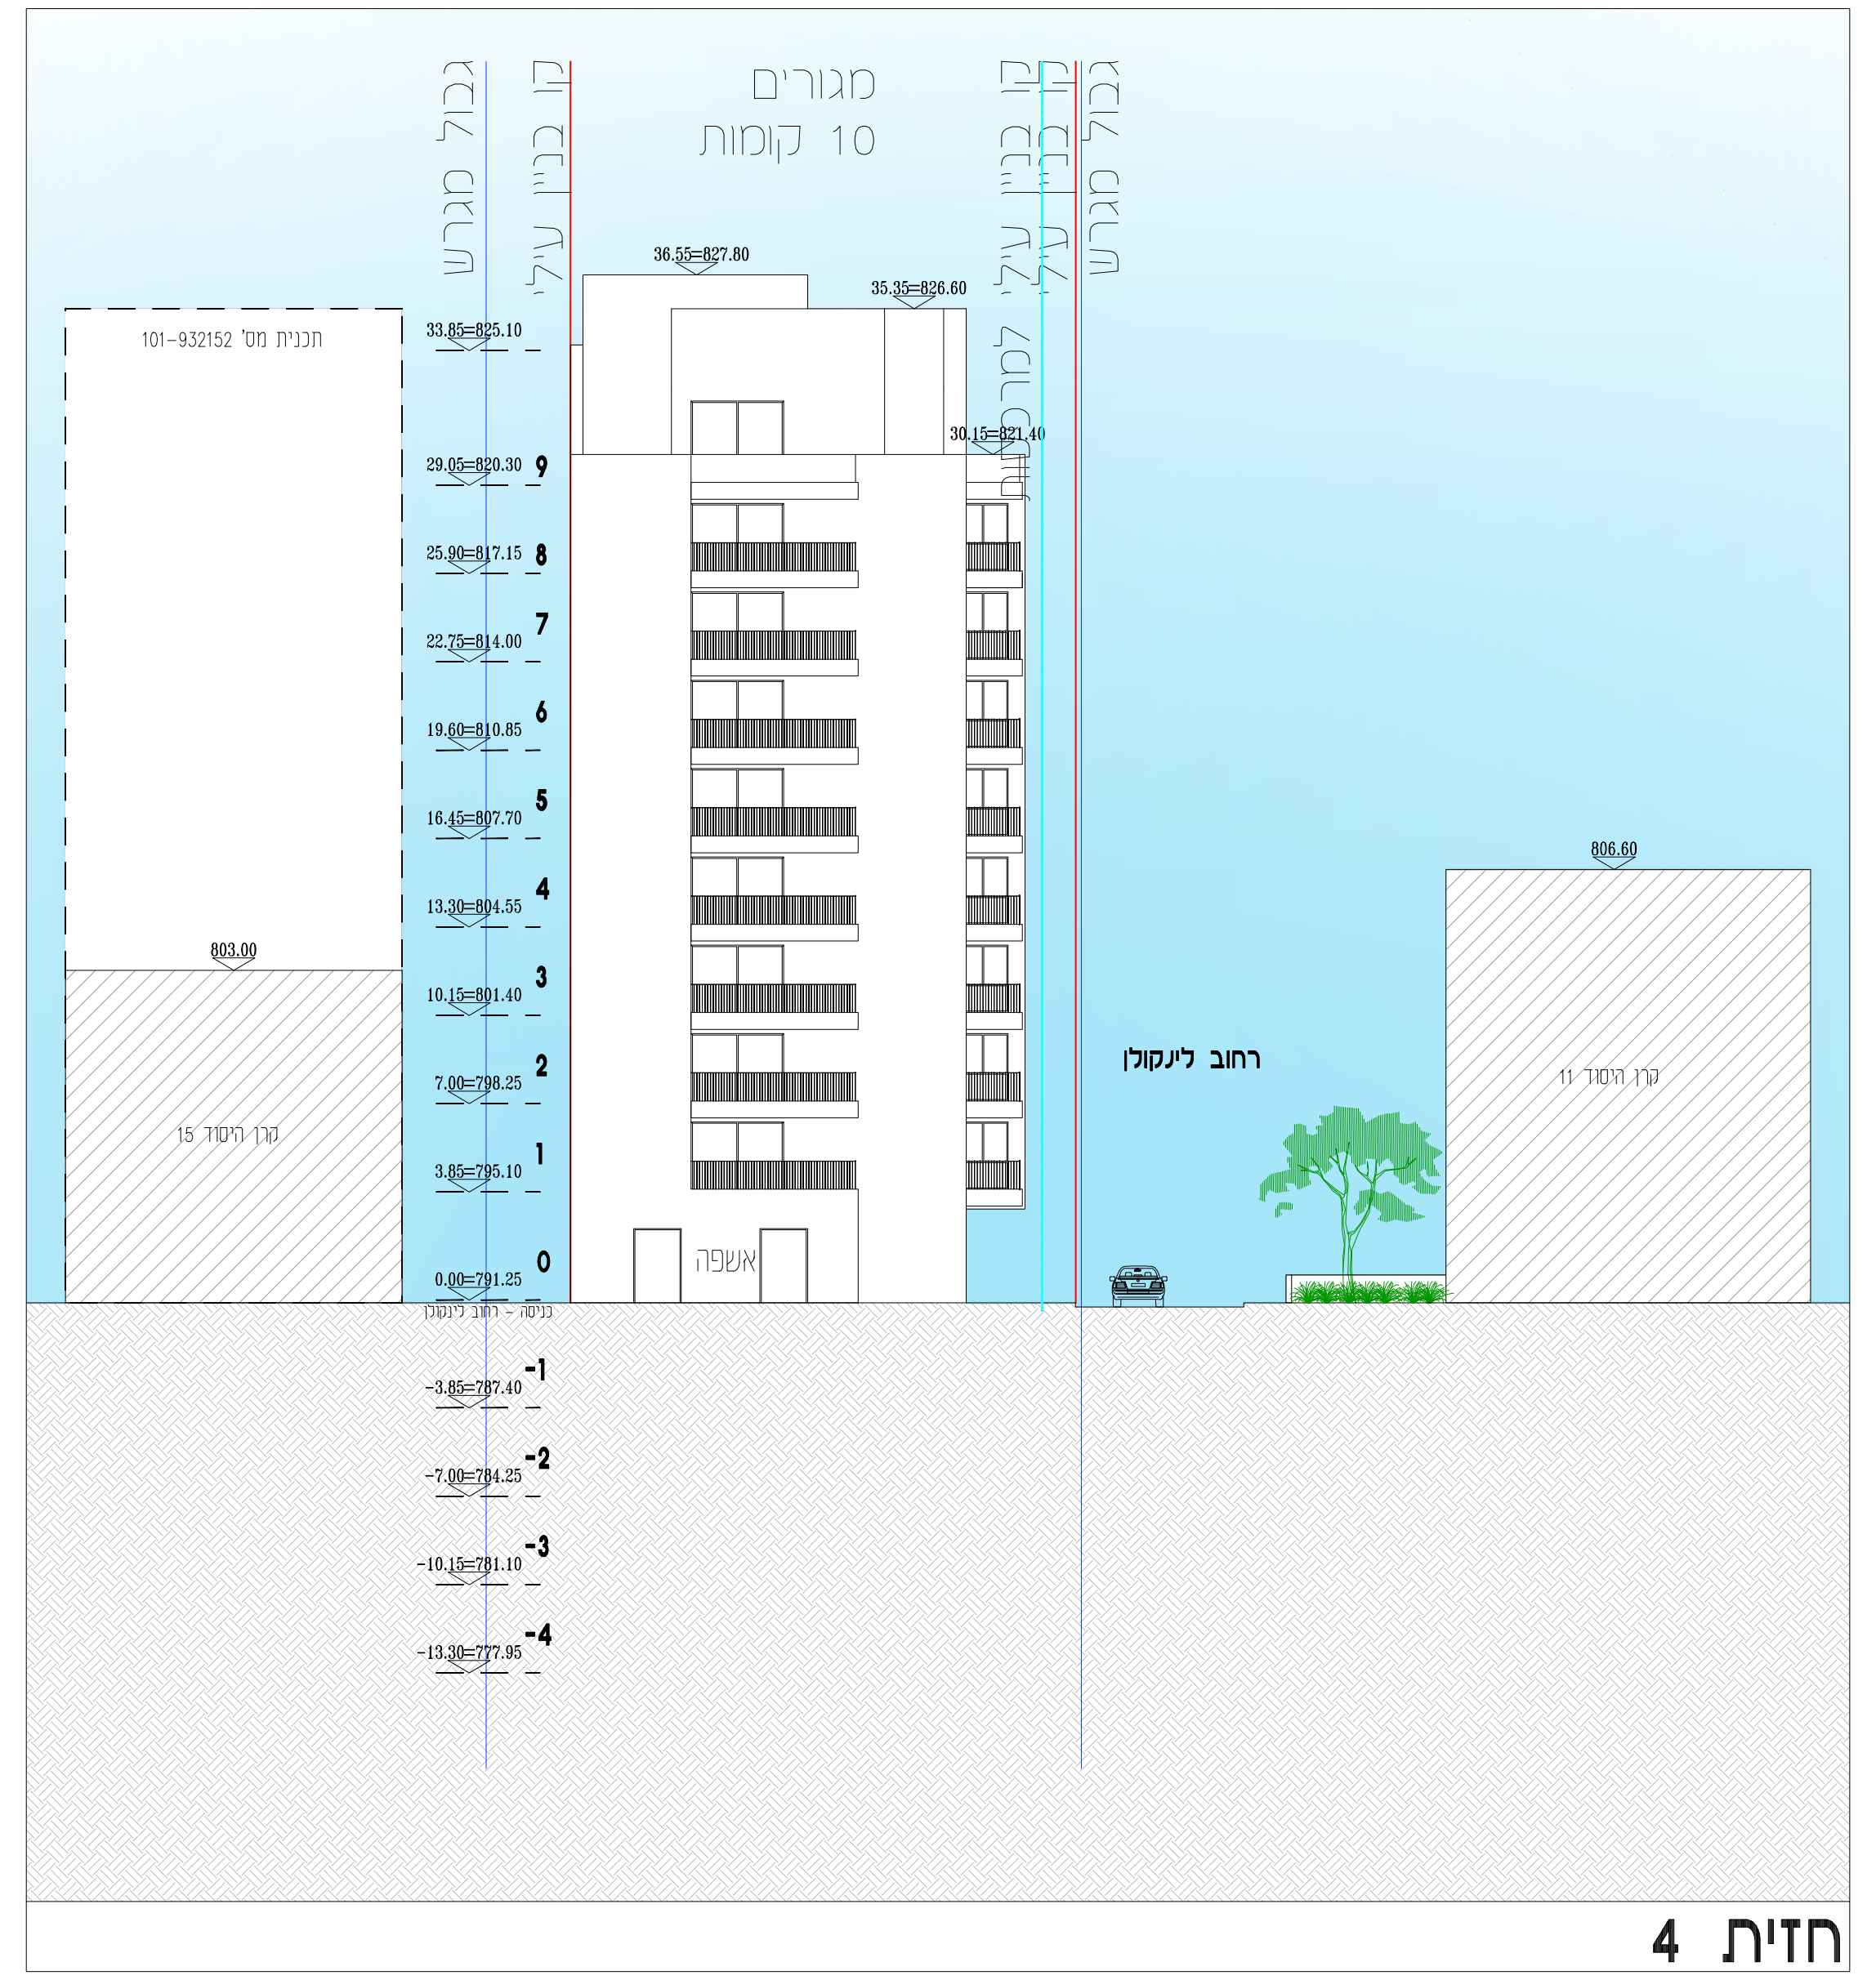

חזית 4

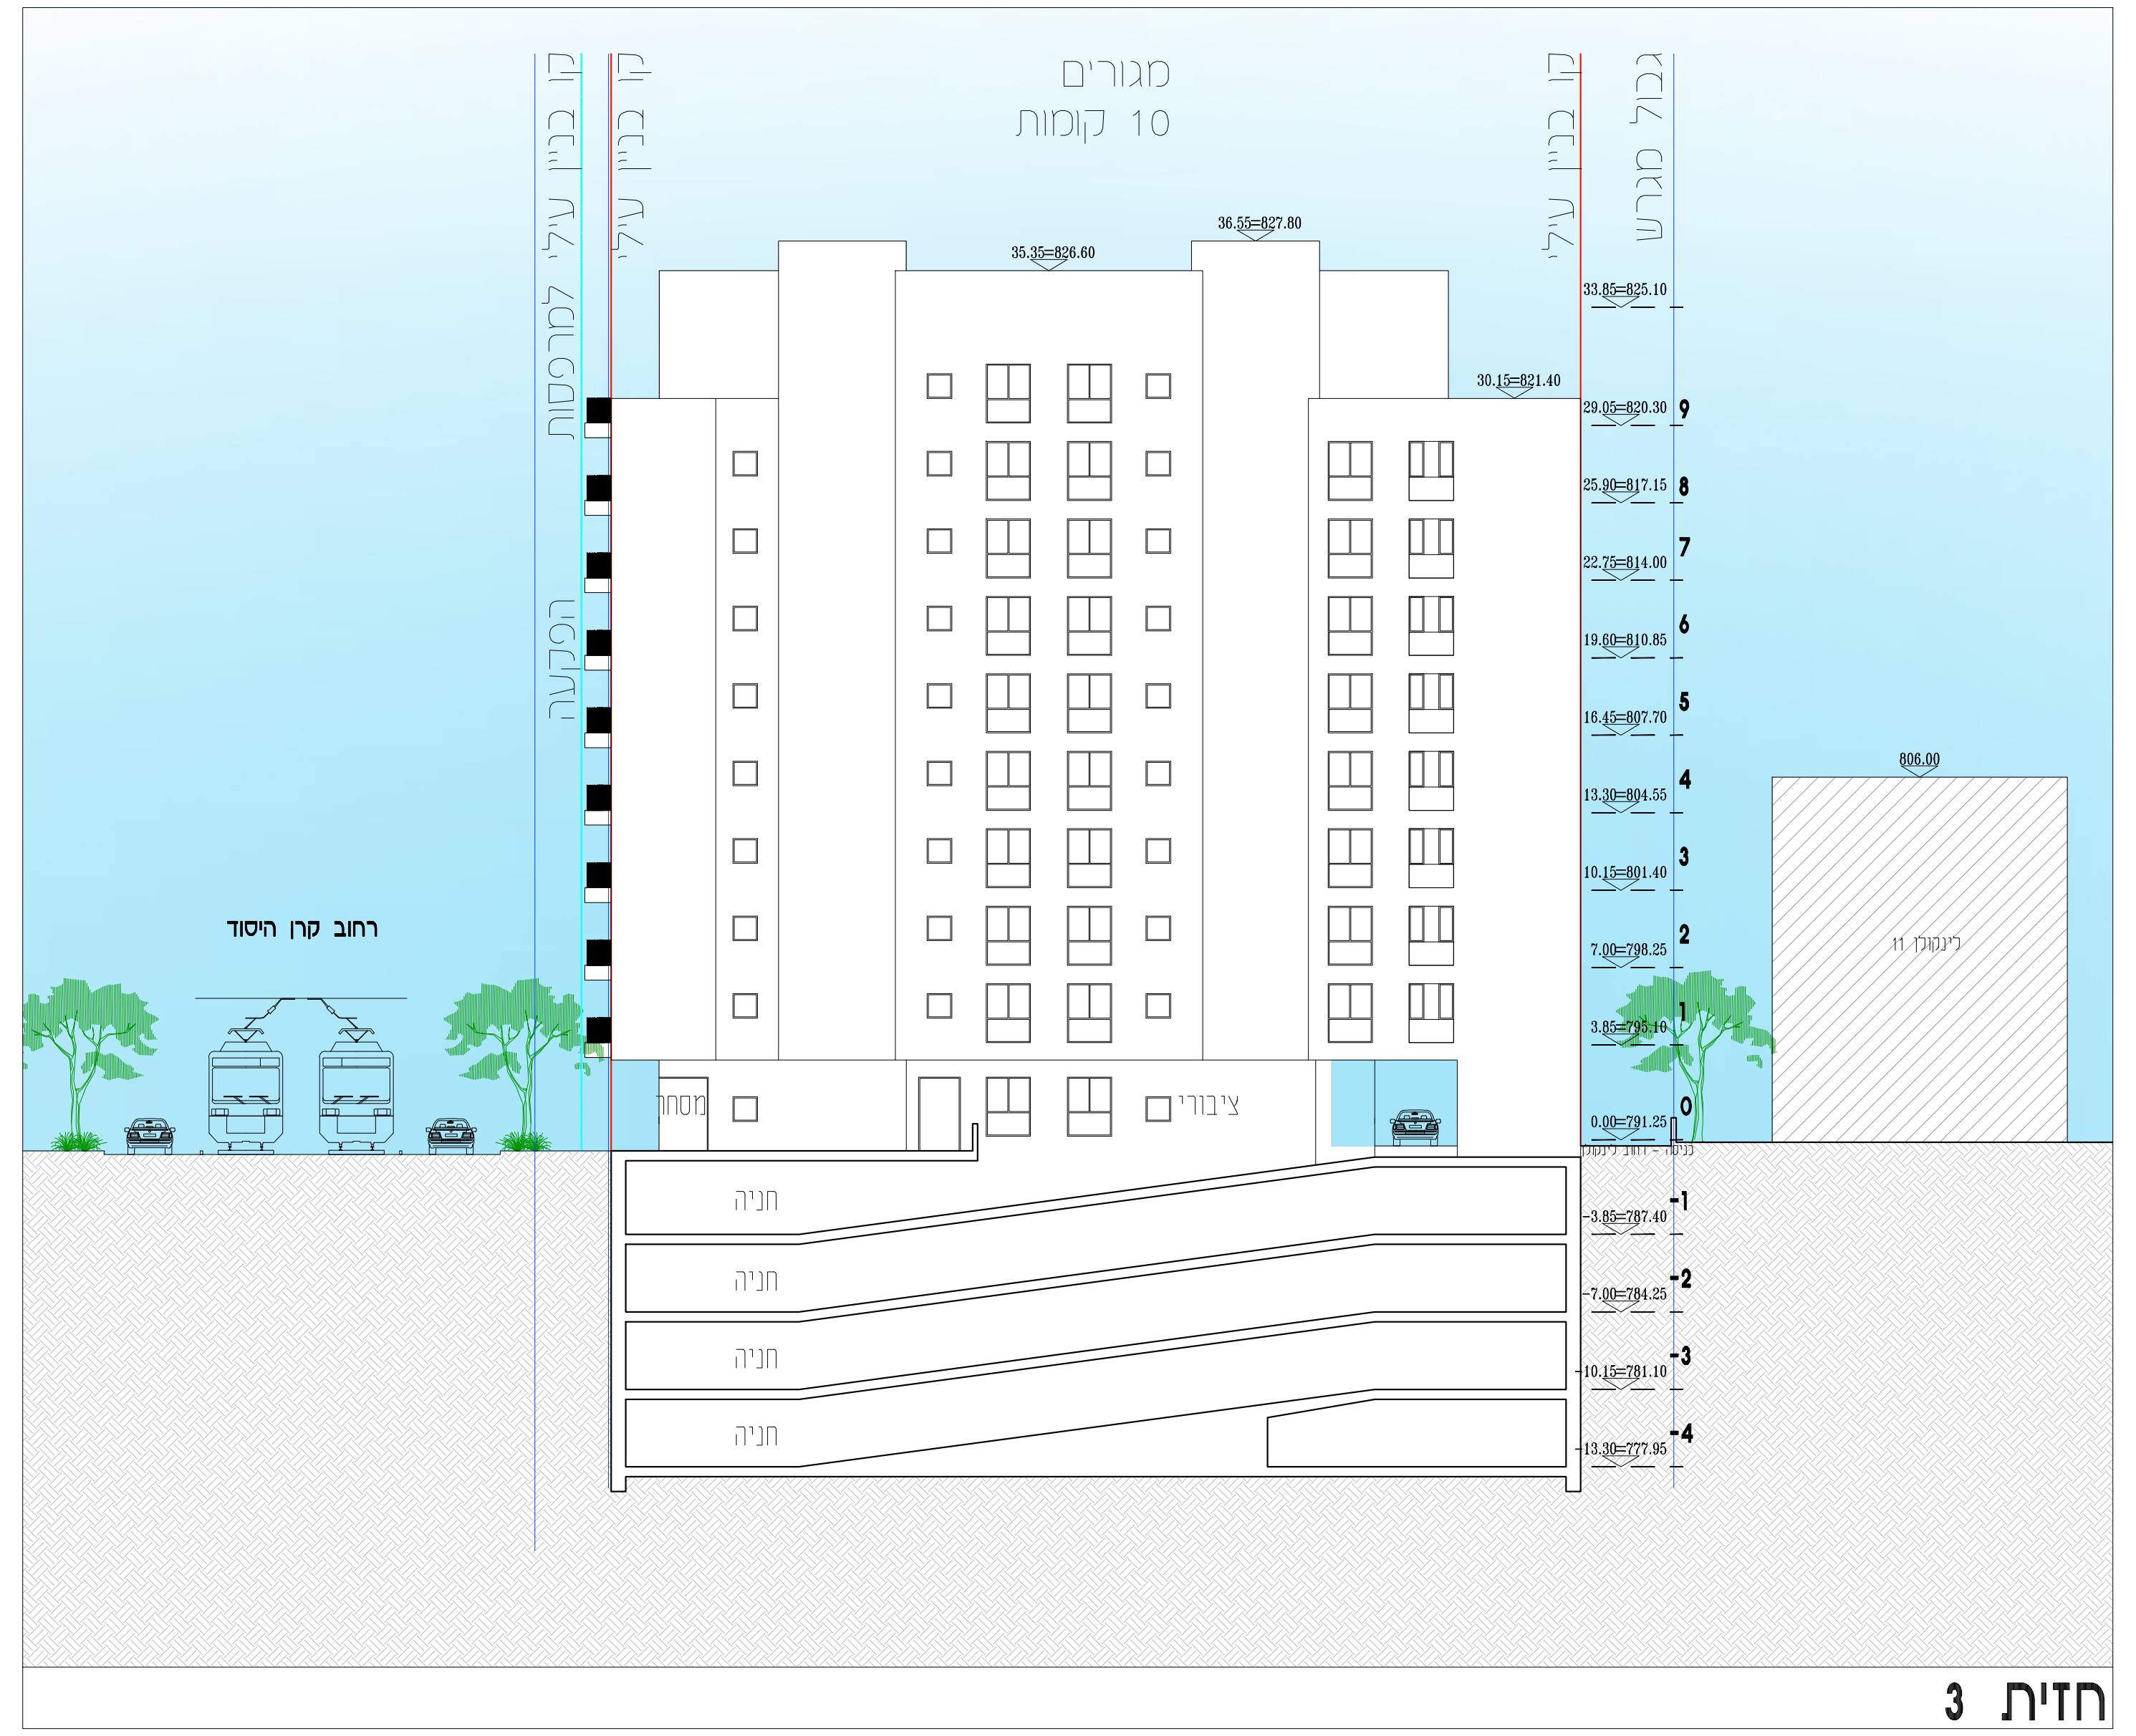

חזית 3

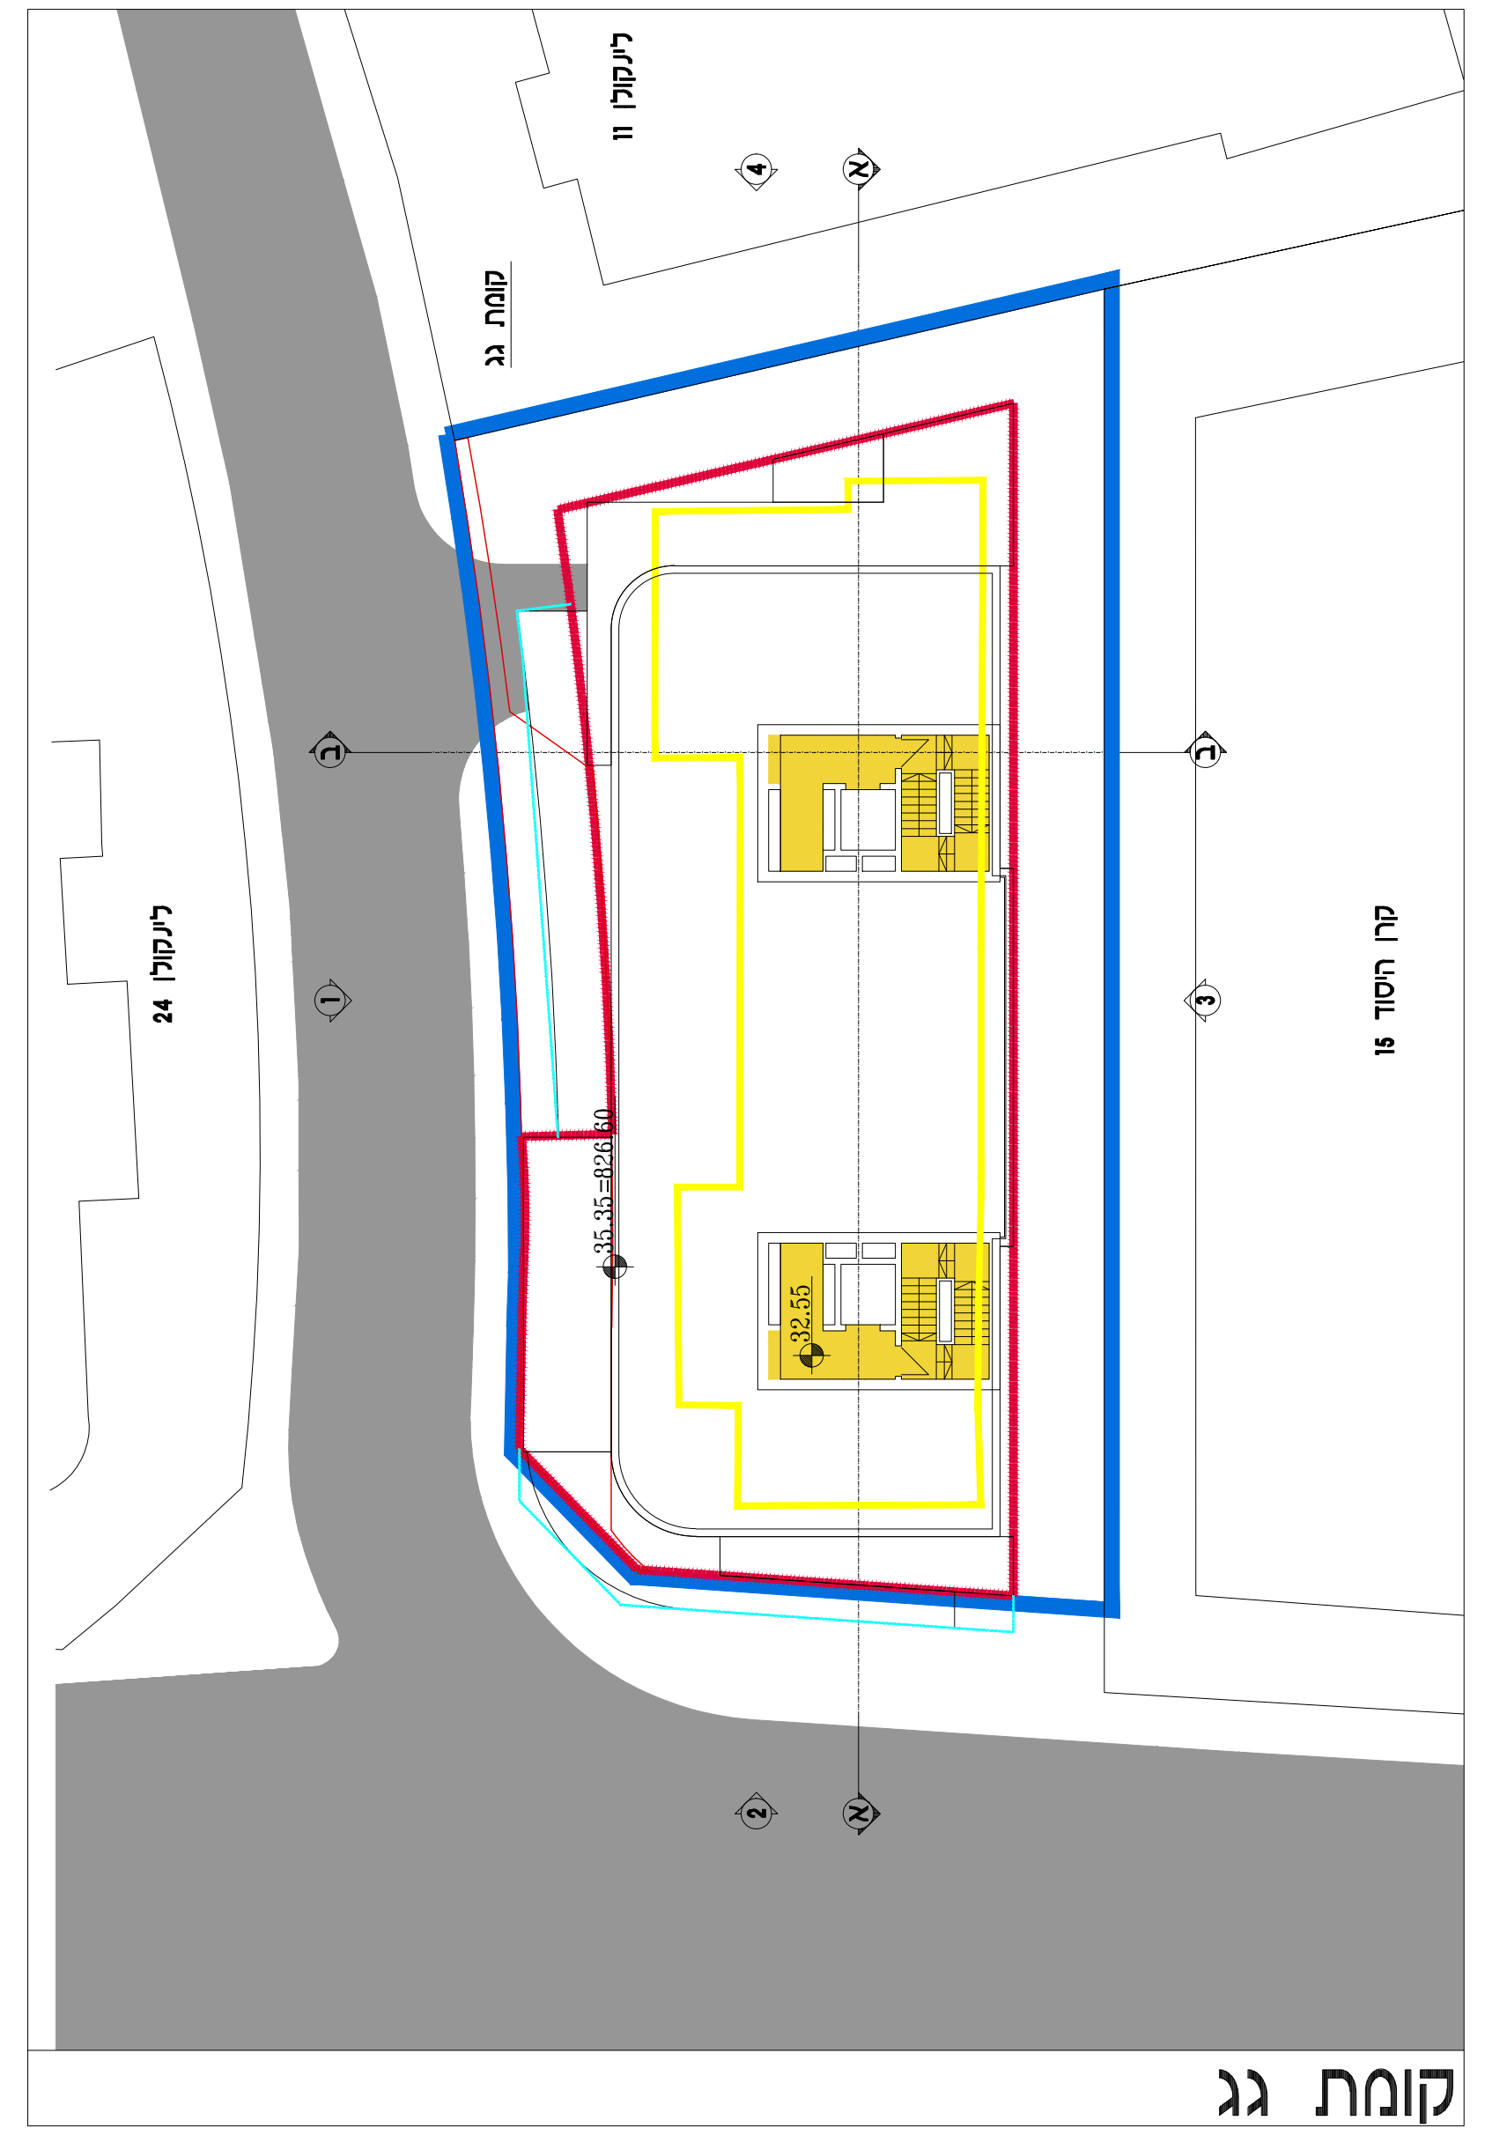

קומת גג

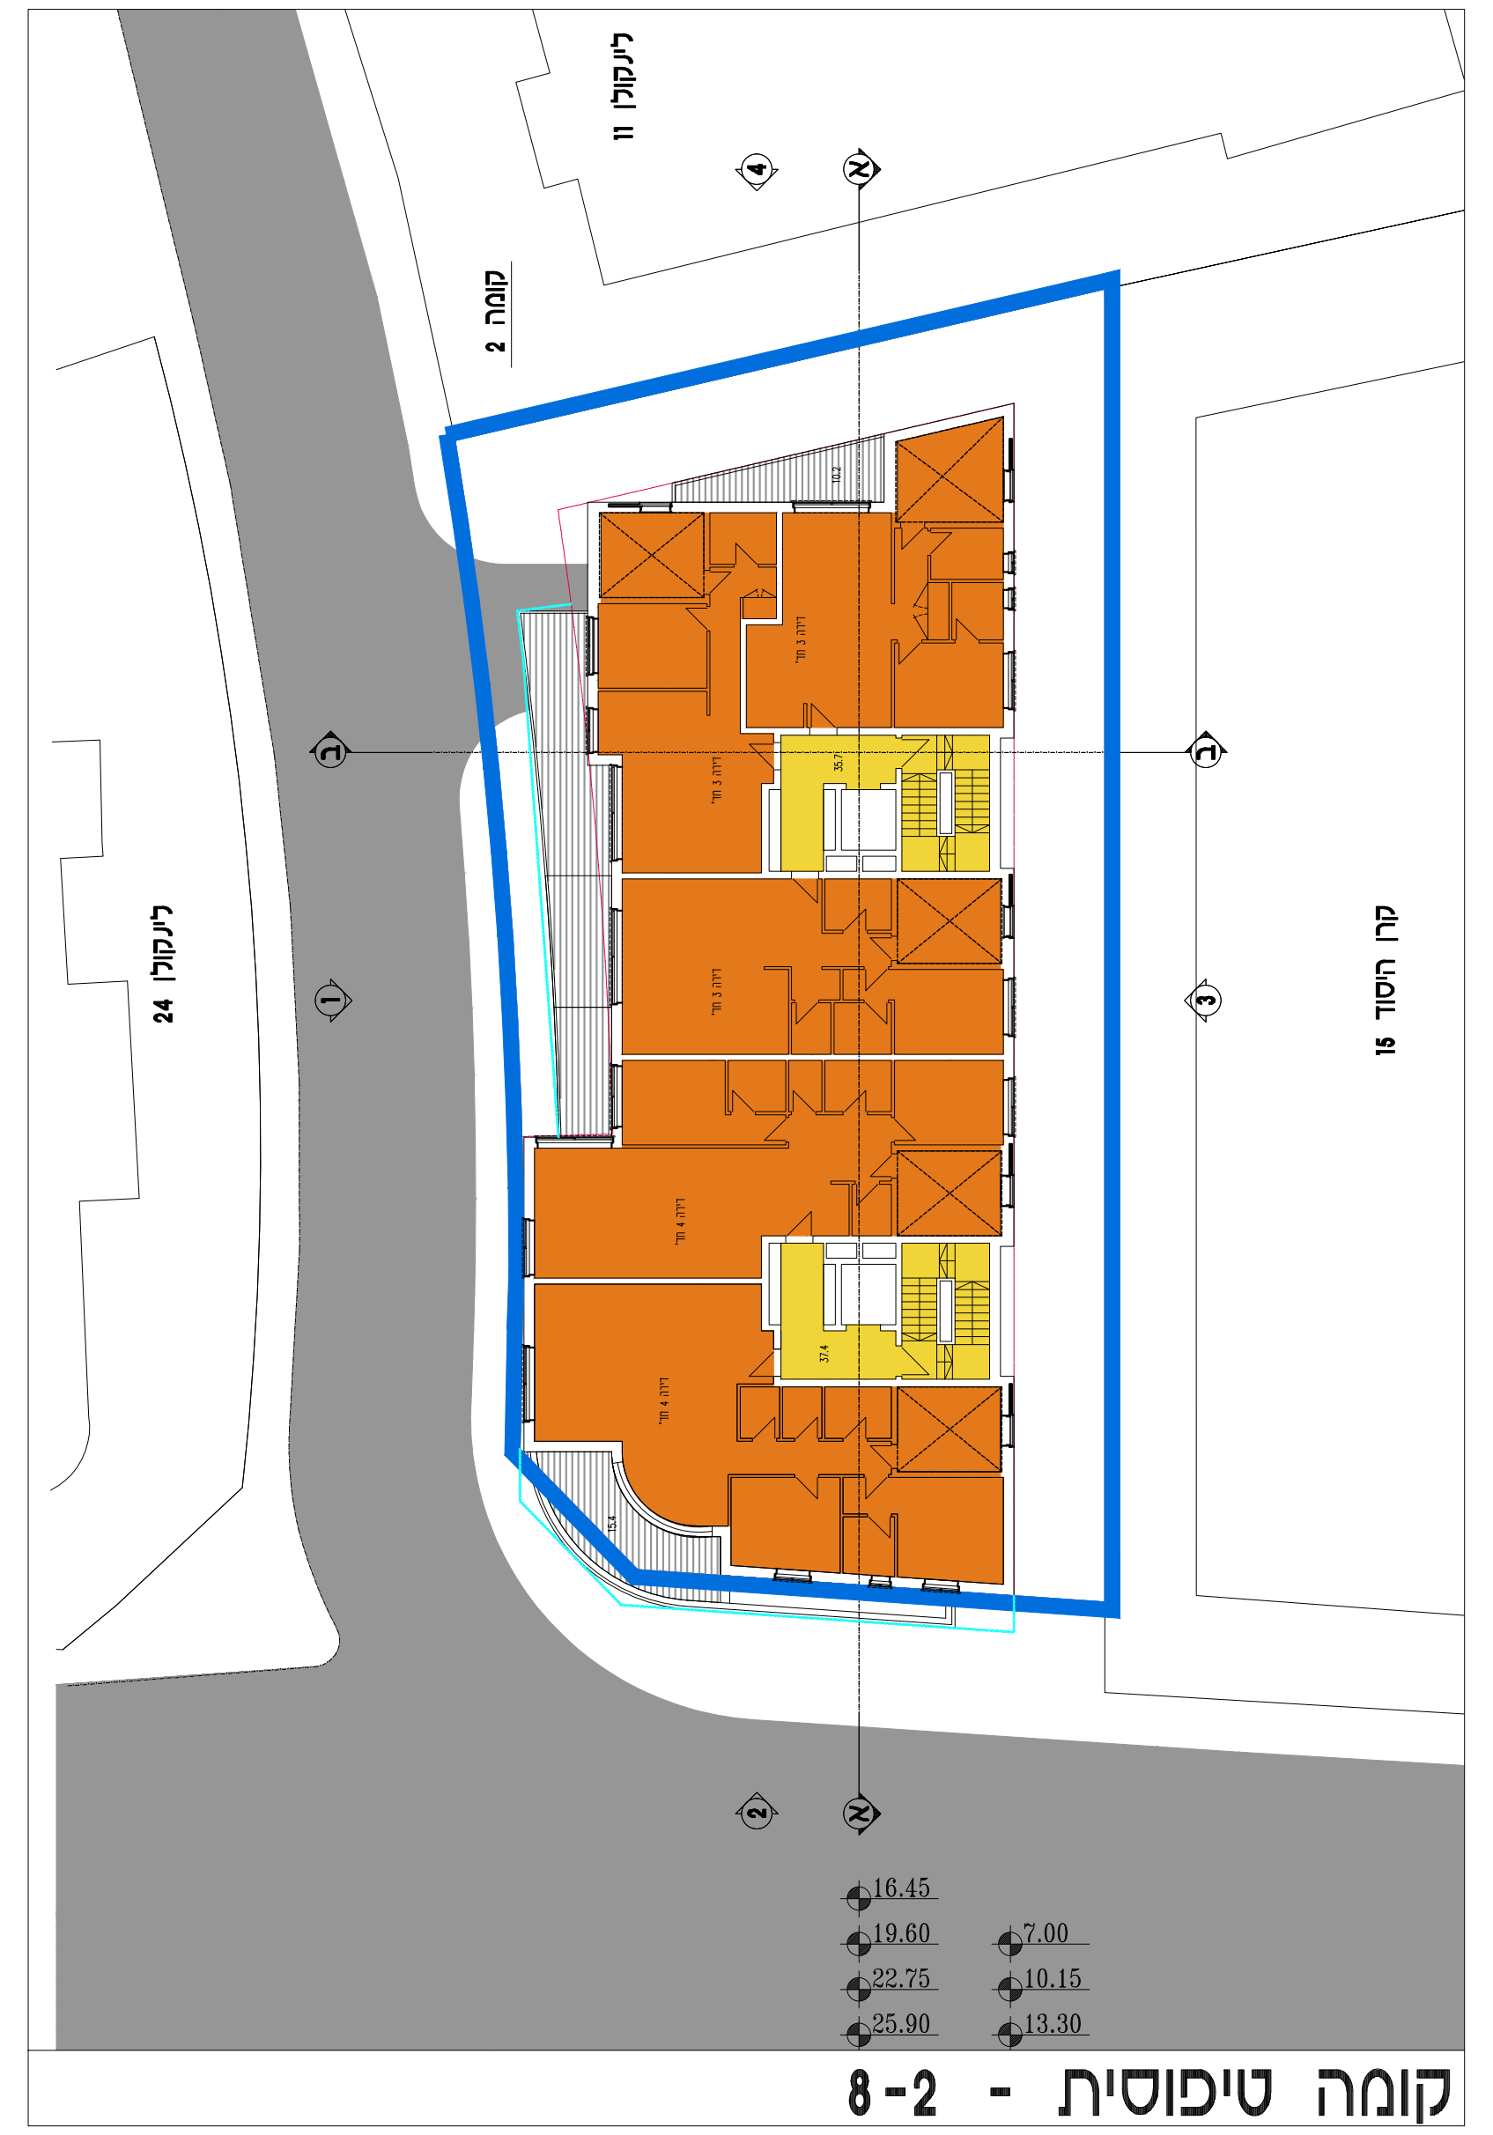

קומה טיפוסית - 2-8

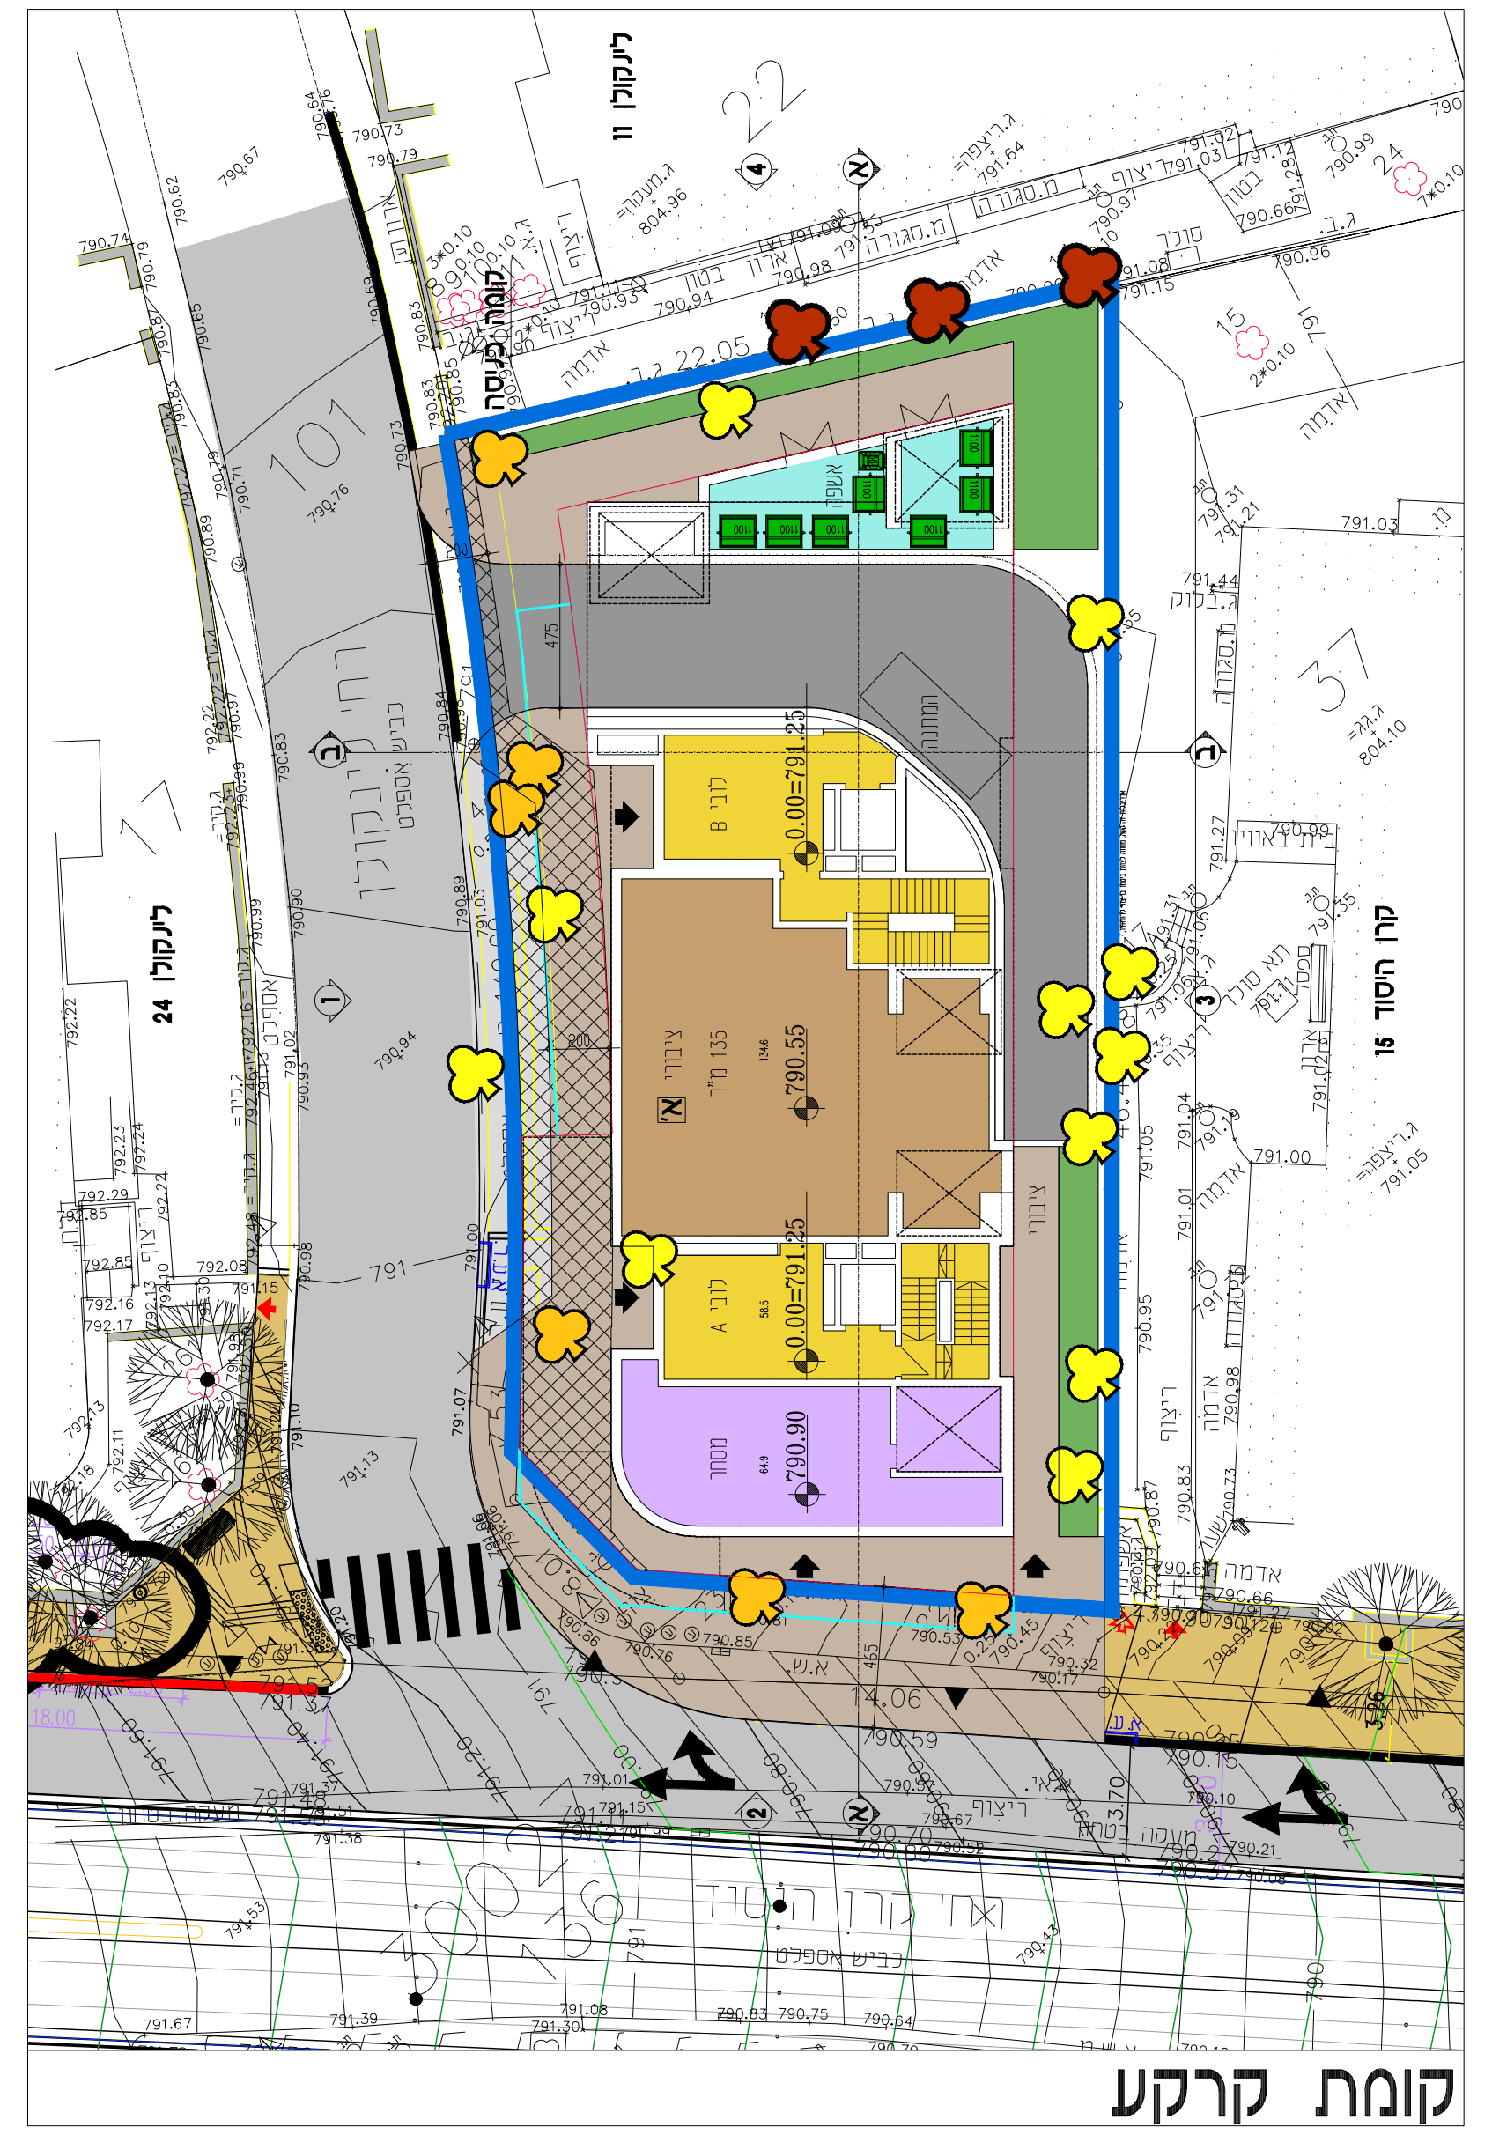

קומת קרקע

תכנית מס' 101-1386671

התחדשות עירונית - לינקולן 13

נספח מס' 1

נספח בינוי

מחוז	ירושלים
מרחב תכנון מקומי	ירושלים
רשות מקומית	ירושלים
ישוב	ירושלים
קנה מידה	1:250

מקרא שימושים

🟪	מסחר
🟧	מגורים
🟨	שירות מגורים
🟫	מבנה ציבור
🟦	אשפה
▨	זיקת הנאה להולכי רגל

הדמיה להמחשה בלבד

שמות

מגיש התכנית	תמ"א טופ נדל"ן + קרסו התחדשות עירונית	
עורך ראשי	בעז ביטמן - ביטמן בן צור אדריכלים	
	טלפון : 02-5700181	פקס : 02-5700181
	boaz@bitman-bentzur.co.il dinai@bitman-bentzur.co.il	

מהדורה: 3　　תאריך: 23.09.2026