מינהל התכנון
חוק התכנון והבניה, התשכ"ח - 1965
מחוז ירושלים
הוועדה המחוזית החליטה ביום :
30/11/2025
להפקיד את התכנית
05/10/2026
יו"ר הוועדה המחוזית
תאריך

תכנית 101-1386671 10:38:49 24/09/2026

מספר סידורי : 1150TREE24-18.02.24

מחוז : ירושלים
נפה : ירושלים
עיר : ירושלים
שכונה : טלביה/המוגרבים
רחוב לינקולן 13
גוש 30028 : חלקה:21
שטח החלקה: 0.845 ד'
נספח עצים
קנ"מ 1:250

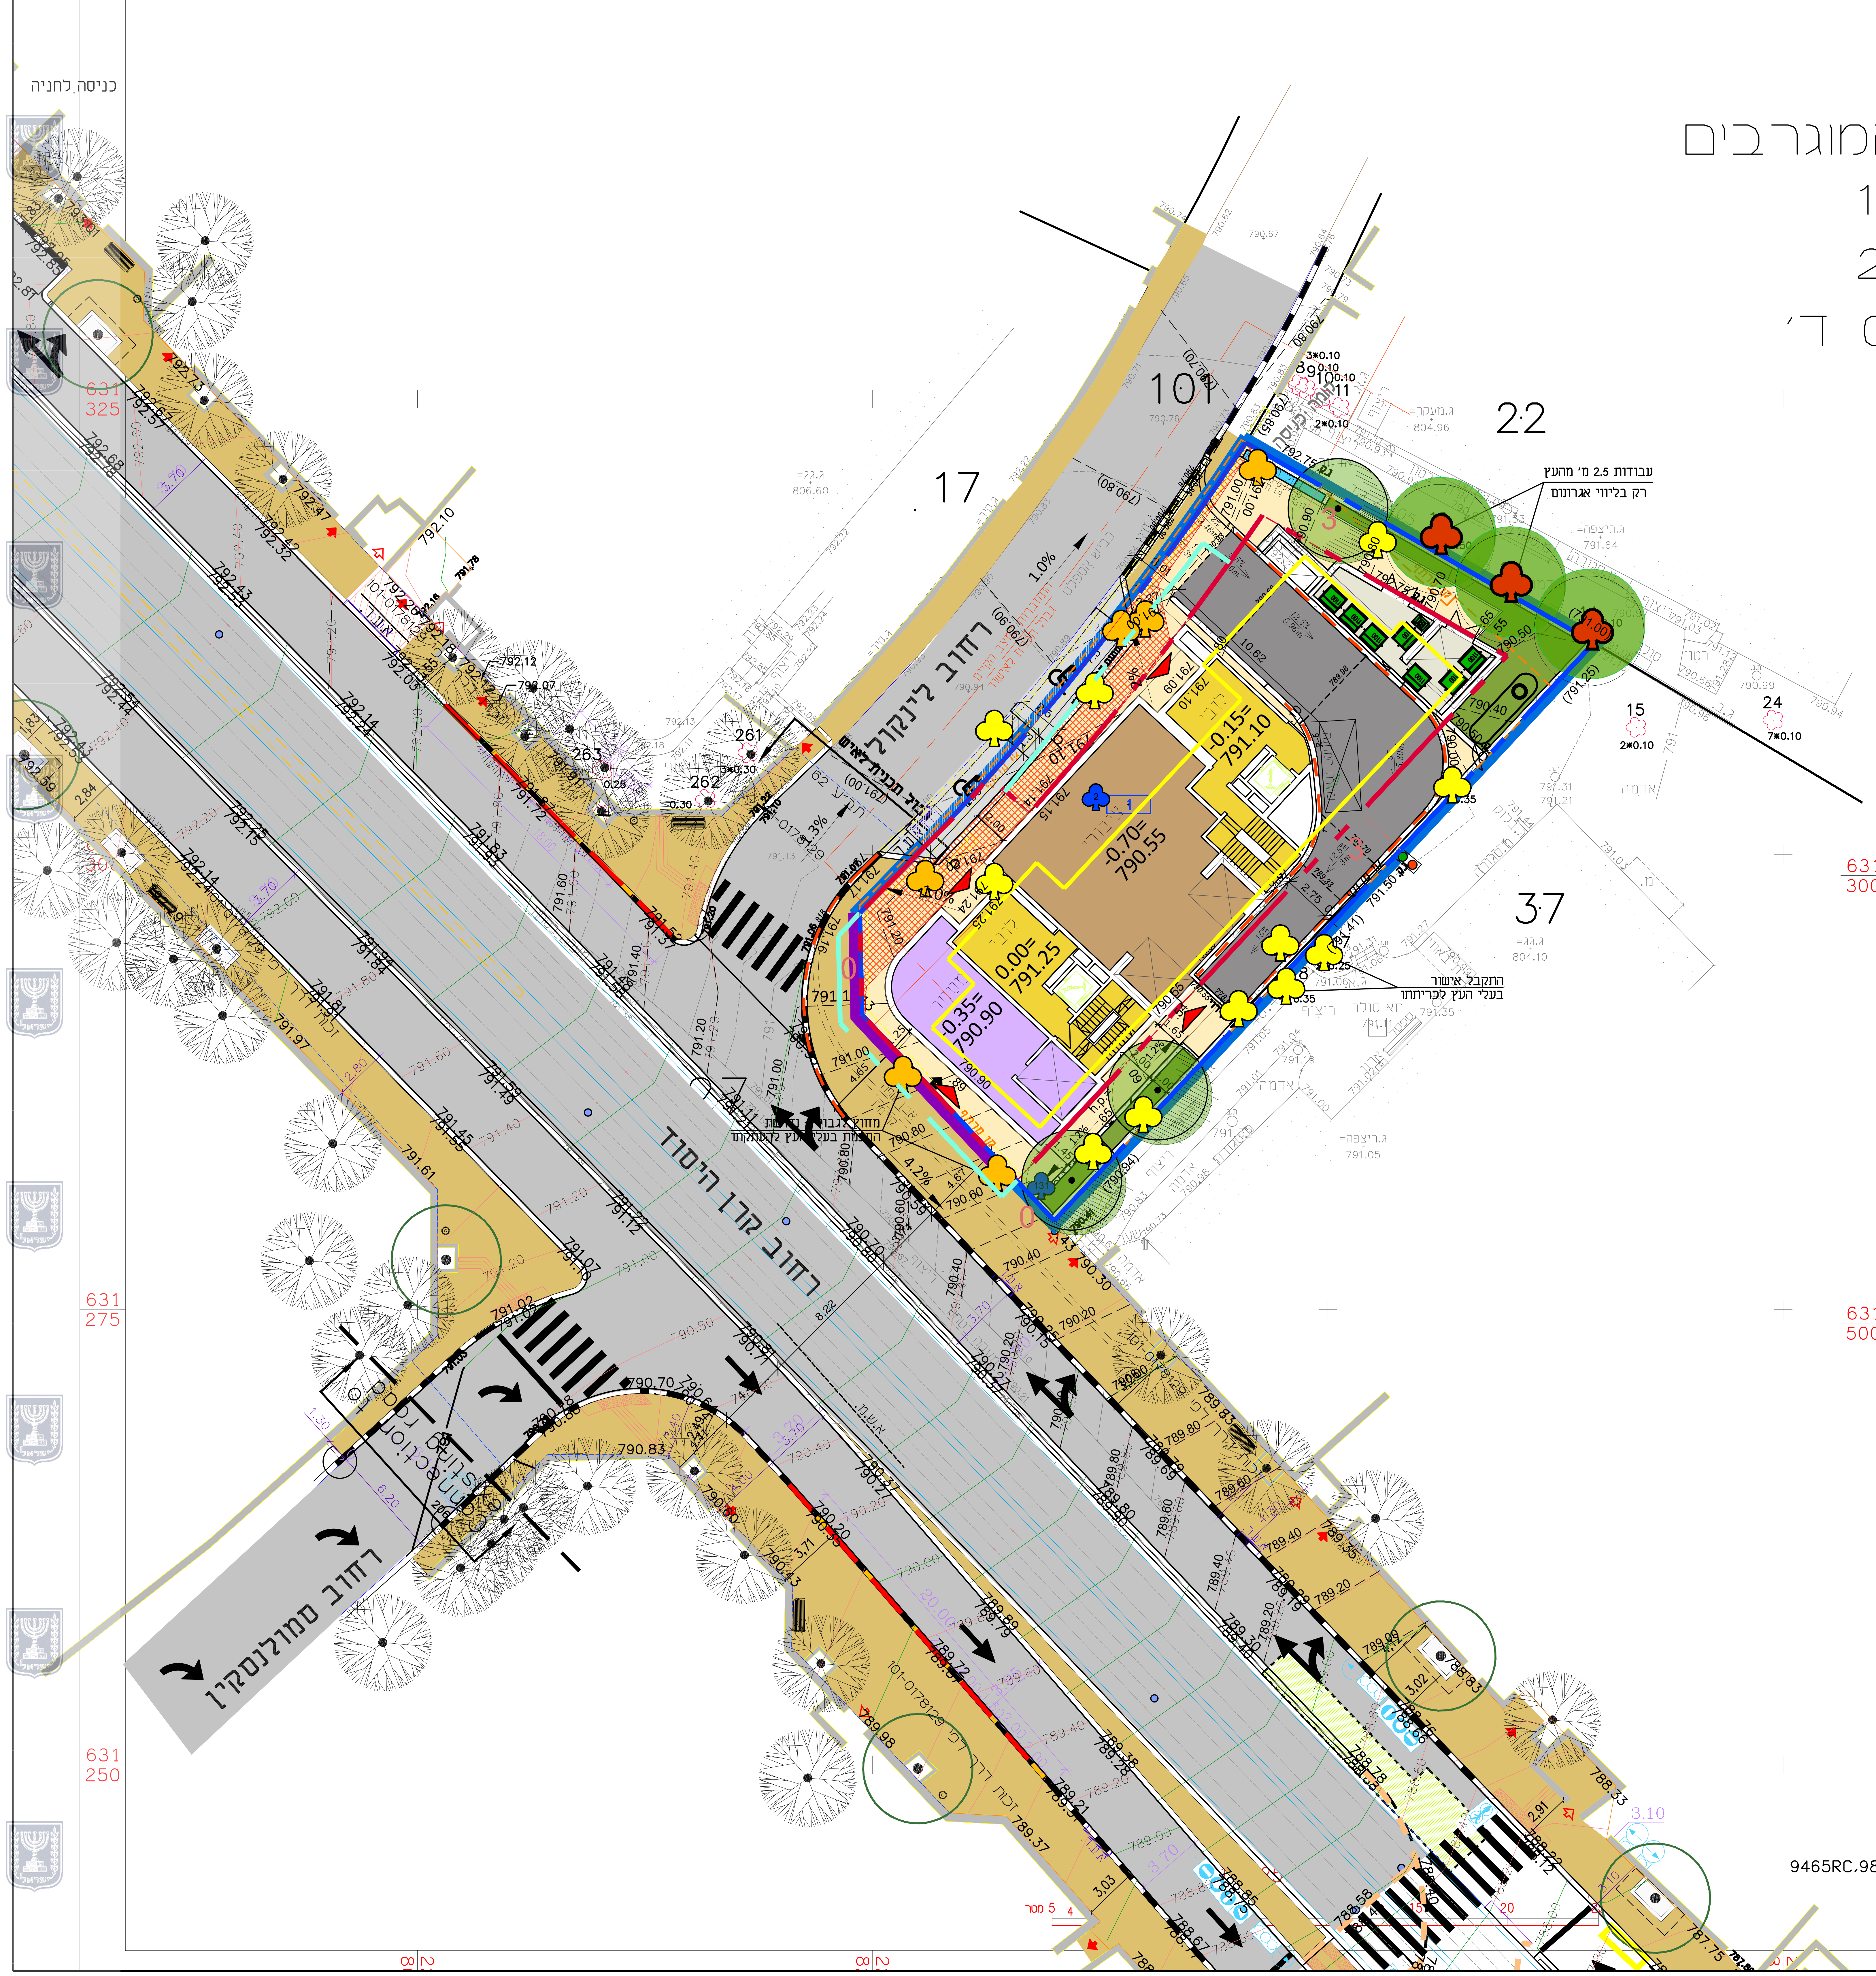

תרשים המקום: קנ"מ 1:1250

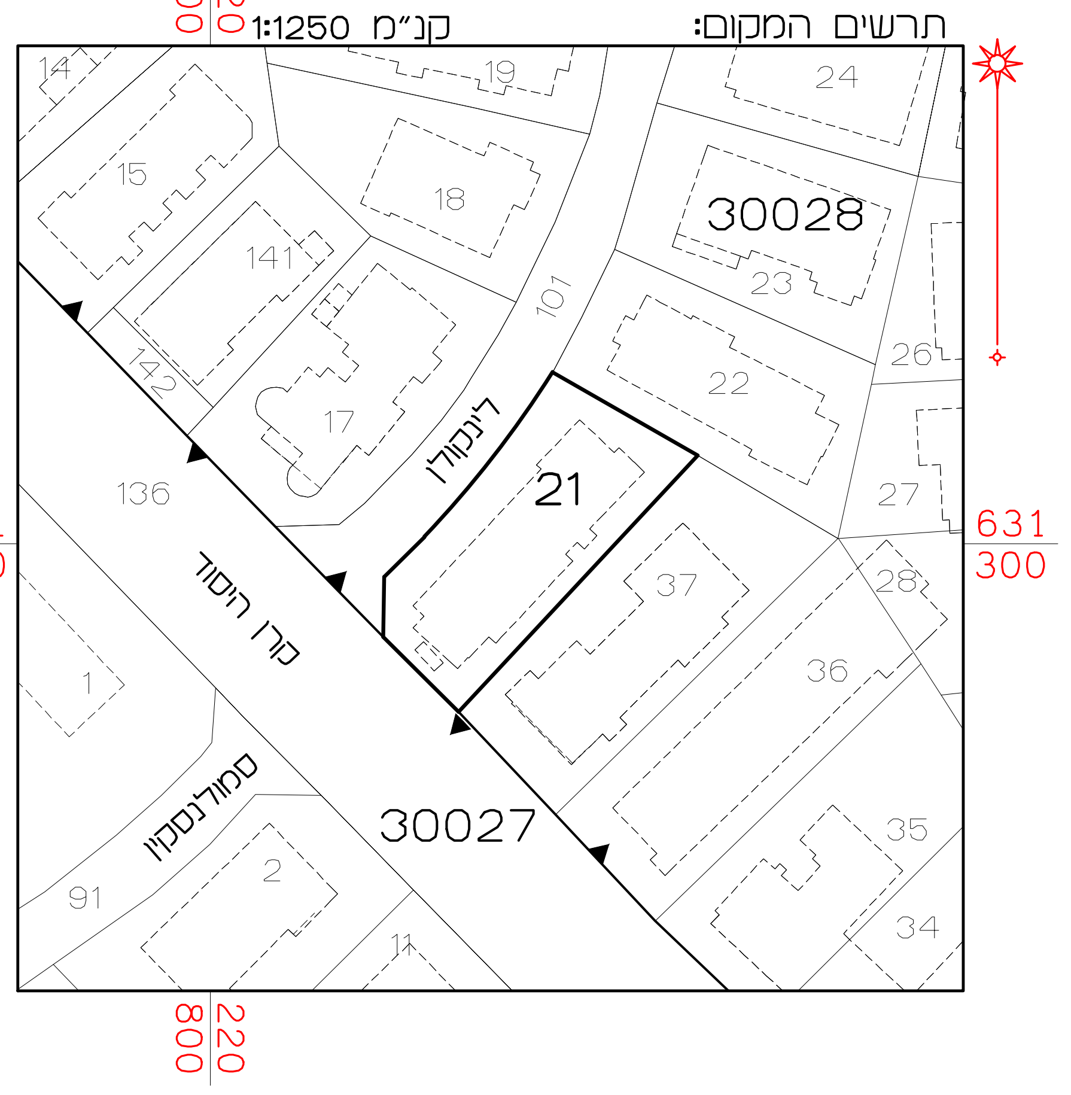

תרשים הסביבה: קנ"מ 1:5000

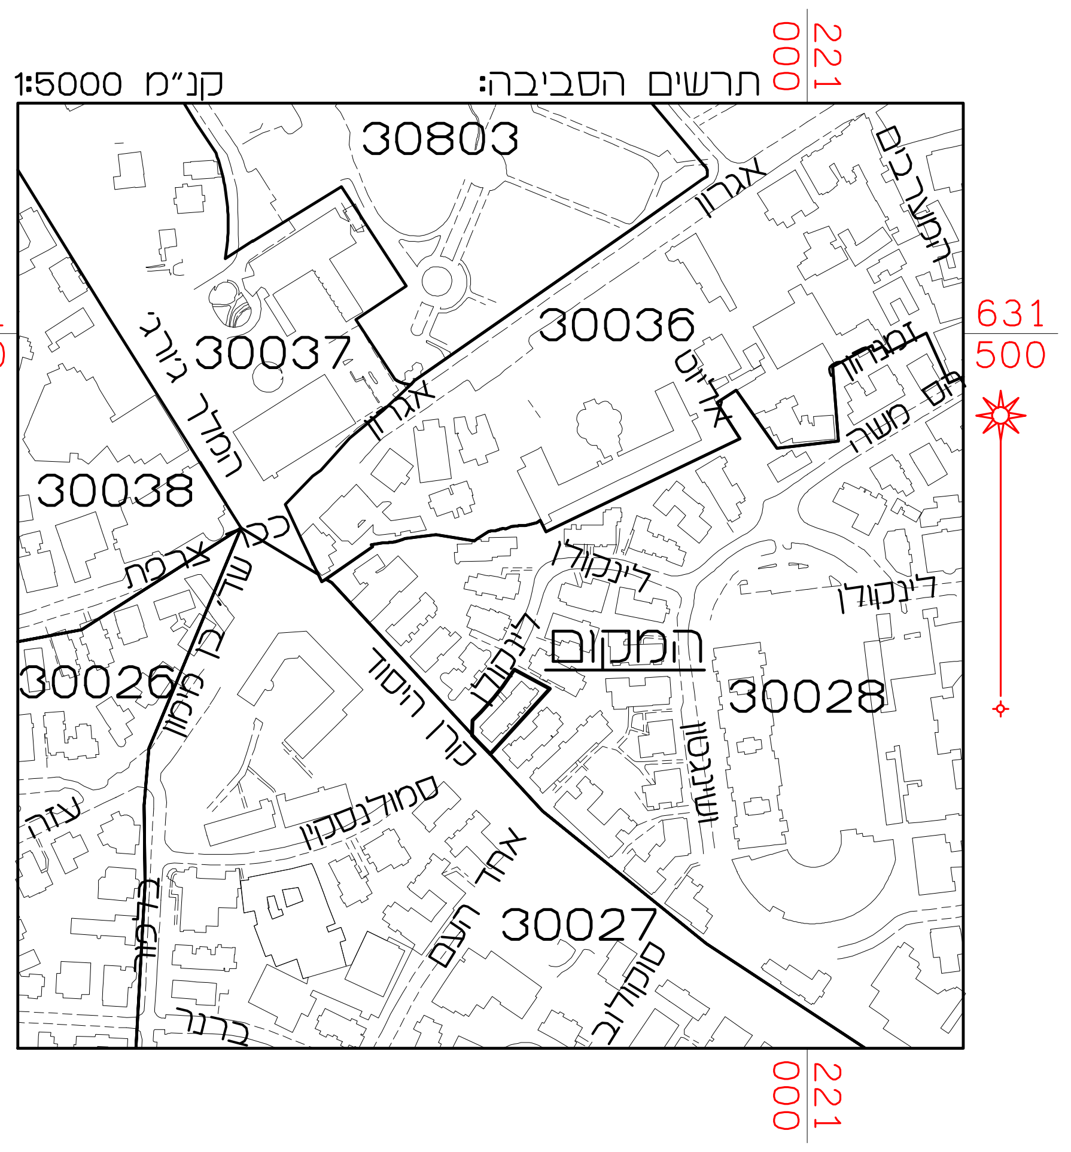

תכנית מס' 101-1386671

התחדשות עירונית - רחוב לינקולן 13

נספח נופי

מחוז	ירושלים
מרחב תכנון מקומי	ירושלים
רשות מקומית	ירושלים
ישוב	ירושלים
קנה מידה	1:200

מקרא שימושים

מקרא:

גבול תוכנית	🟦
קו בניין	— · — · —
גבול מרתף	– – – –
גובה קיים	(825.50)
גובה מתוכנן	825.50
קיר	═
ריצוף מדרכות שבילים ורחבות	🟨
גינון	🟩
עץ קיים	●
עץ מתוכנן	●

♣	עץ להעתקה
♣	עץ לשימור
♣	עץ לכריתה
♣	עץ להעתקה שלא סומן ע"י מודד אלא בסימון עצמי במיקום משוער
♣	עץ לשימור שלא סומן ע"י מודד אלא בסימון עצמי במיקום משוער
♣	עץ לכריתה שלא סומן ע"י מודד אלא בסימון עצמי במיקום משוער
♣	עץ פולשני/ממשפחת הדקליים/צעיר/לא קיים שאין צורך לסקור ולא נדרש רישיון לכריתתו
♣	עץ פולשני/ממשפחת הדקליים, שסומן בסימון עצמי שאין צורך לסקור ולא נדרש רישיון לכריתתו

הערות:

1. המדידה קשורה לרשת קואורדינטות ארצית ע"י נקודותGPS 9465RC,988RS
2. המדידה קשורה לרשת גבהים ארצית 788.23=988RS
3. גבולות החלקה 21 נלקחו לפי תצ"ר מתיק 1153/30.

שמות

עורך ראשי	ביטמן בן צור אדריכלים
	טלפון 077-2018275 פקס : boaz@bitman-bentzur.co.il

מהדורה: 1 תאריך: 24.09.2026

אמדו אדריכלות נוף בע"מ 077-2018275 077-2018274 office@amado-la.co.il המייסדים 19, זכרון יעקב 3091053