מינהל התכנון
חוק התכנון והבניה, התשכ"ה - 1965
מחוז ירושלים
הוועדה המחוזית החליטה ביום :
30/11/2025
להפקיד את התכנית
05/10/2026
תאריך יו"ר הוועדה המחוזית

נספח ניקוז - תנוחה

נספח לתכנית מס' 101-1386671

התחדשות עירונית-לינקולן 13

גליון 3 מתוך 3

תחולה	מנחה
תיאור	נספח ניקוז
תאריך עריכת הנספח	05.08.2026
קנ"מ	1:250

תרשימים נוספים	קנ"מ

שמות וחתימות:

עורך הנספח	שם:	אורן גבעון
	תאגיד:	י.לבל מהנדסים יועצים בע"מ

מפת הסביבה

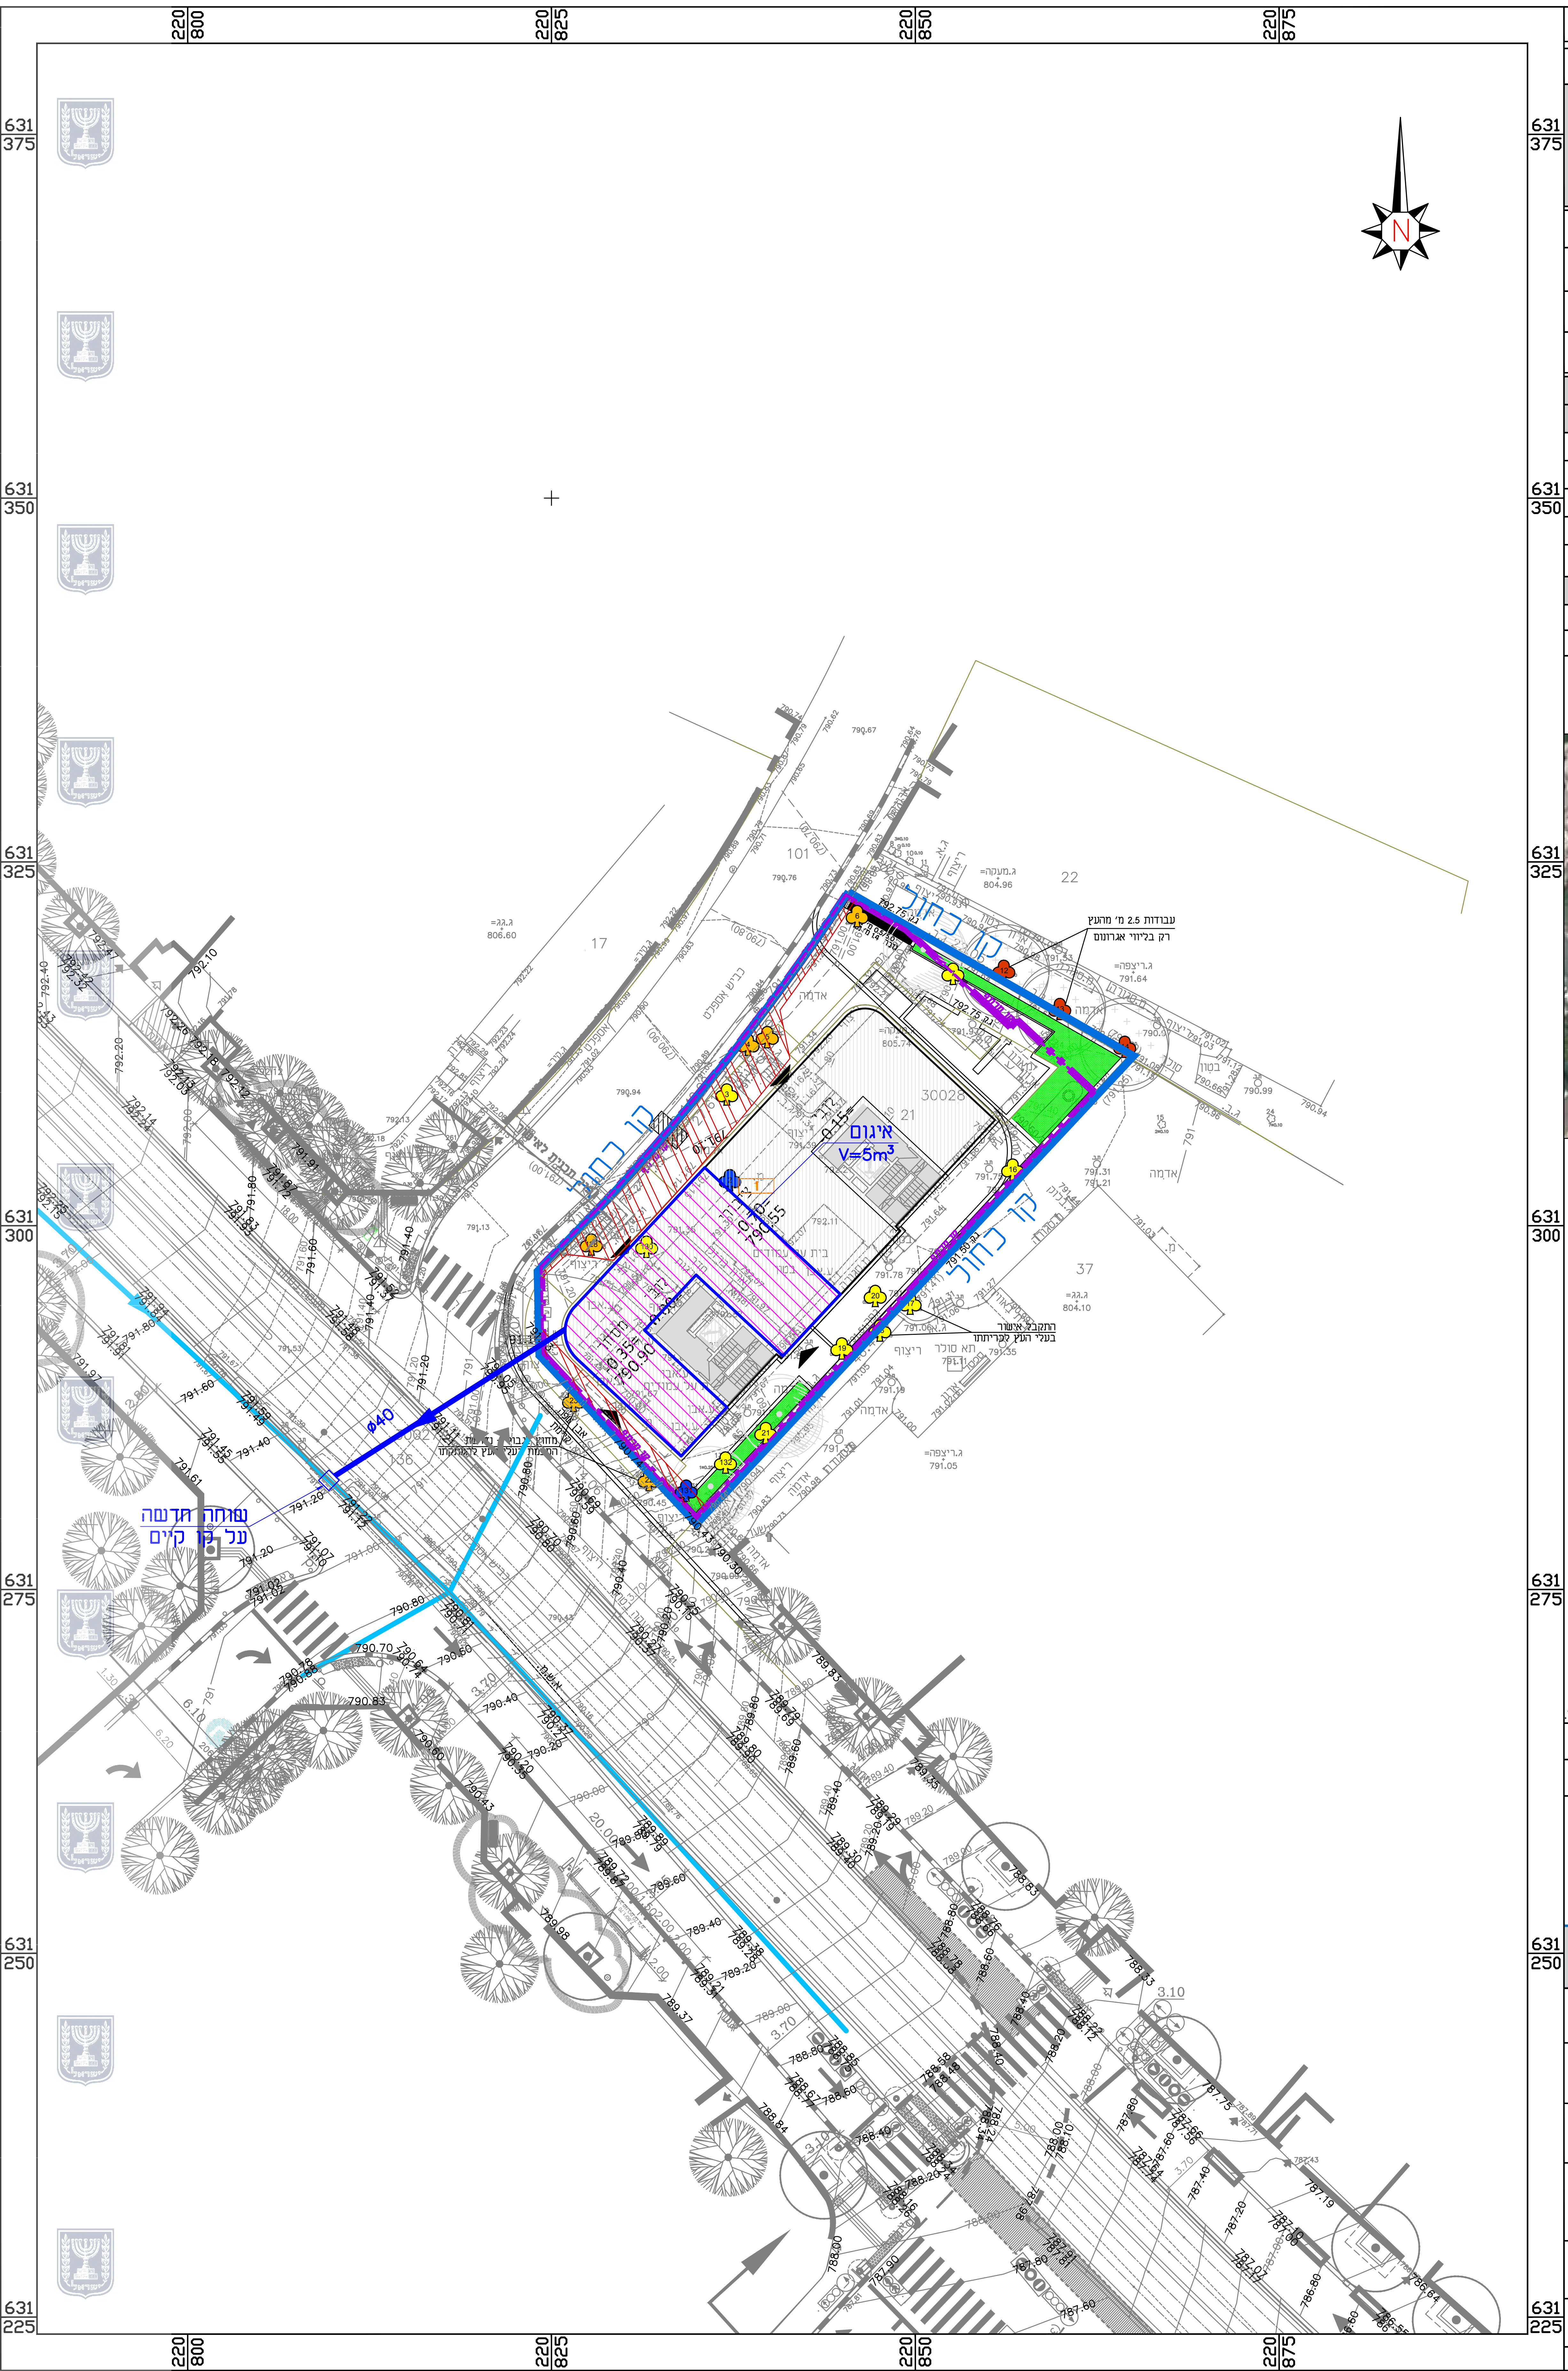

מקרא :

- קו כחול
- גבול מרתף
- קו בניין
- זיקת הנאה ▨
- איגום בגג ▨
- גבול אגן ניקוז
- קו ניקוז קיים
- קו ניקוז מתוכנן

הקבלן אחראי לבדיקת המידות שבתכנית. על כל טעות, סטייהאו אי התאמה עליו להודיע למתכנן. אין לקבוע מידות ע"י מדידה בשרטוט אלא באישור המתכנן.
התכנית הנה רכוש הבלעדי של המתכנן ובעלותו מוגנת ע"י חוק זכויות היוצרים.
אין לעשות כל שימוש בתכנית זו וברעיונות הגלומים בה ללא אישור מראש ובכתב של המתכנן.

לעיון	למכרז	לבצוע
●	○	○

י.לבל
Y.LEBEL
מהנדסים יועצים בע"מ
CONSULTING ENGINEERS LTD
נחלת יצחק 32א' ת"א, 67448
טל': 03-6952418 פקס: 03-6916647
lebel@lebel.co.il www.lebel.co.il
32a Nahlat Yitzhak st. Tel Aviv, 67448 tel:03- 6952418 fax:03-6916647

שם הפרויקט :
התחדשות עירונית-לינקולן 13

שם המזמין :
תמ״א טופ בע״מ

שם הגליון :
נספח ניקוז - תנוחה

מס' הפרויקט :	מס' הגליון :	תאריך :
3220	03	08.10.24

ק.מ. :	מהדורה :	תאריך עדכון :	סה"כ גליונות :	מידות הגליון :
1:250	2	05.08.26	3	65x55

תכנן :	שרטט :	בקר :	אישר :	תאריך :
אדהם.ח	הדסה.א	מיתר.ק	אורן.ג	

שם הקובץ C:\Users\inna\2PLAN Dropbox\LEBEL TEAM\3220\TICHNUN\MAIN_3220.dwg