נספח שמירה על עצים בוגרים 10:12:47 11/05/2026 101-1386671

מינהל התכנון
חוק התכנון והבניה, התשכ"ה - 1965
מחוז ירושלים
הוועדה המחוזית החליטה ביום : 30/01/2025
להפקיד את התכנית
05/10/2026
תאריך יו"ר הוועדה המחוזית

מספר סידורי : 3150TREE24-18.02.24

מחוז : ירושלים
נפה : ירושלים
עיר : ירושלים
שכונה : טלביה\המוגרבים
רחוב לינקולן 13
גוש: 30028 חלקה: 21
שטח החלקה: 0.845 ד,
נספח עצים
קנ"מ 1:250

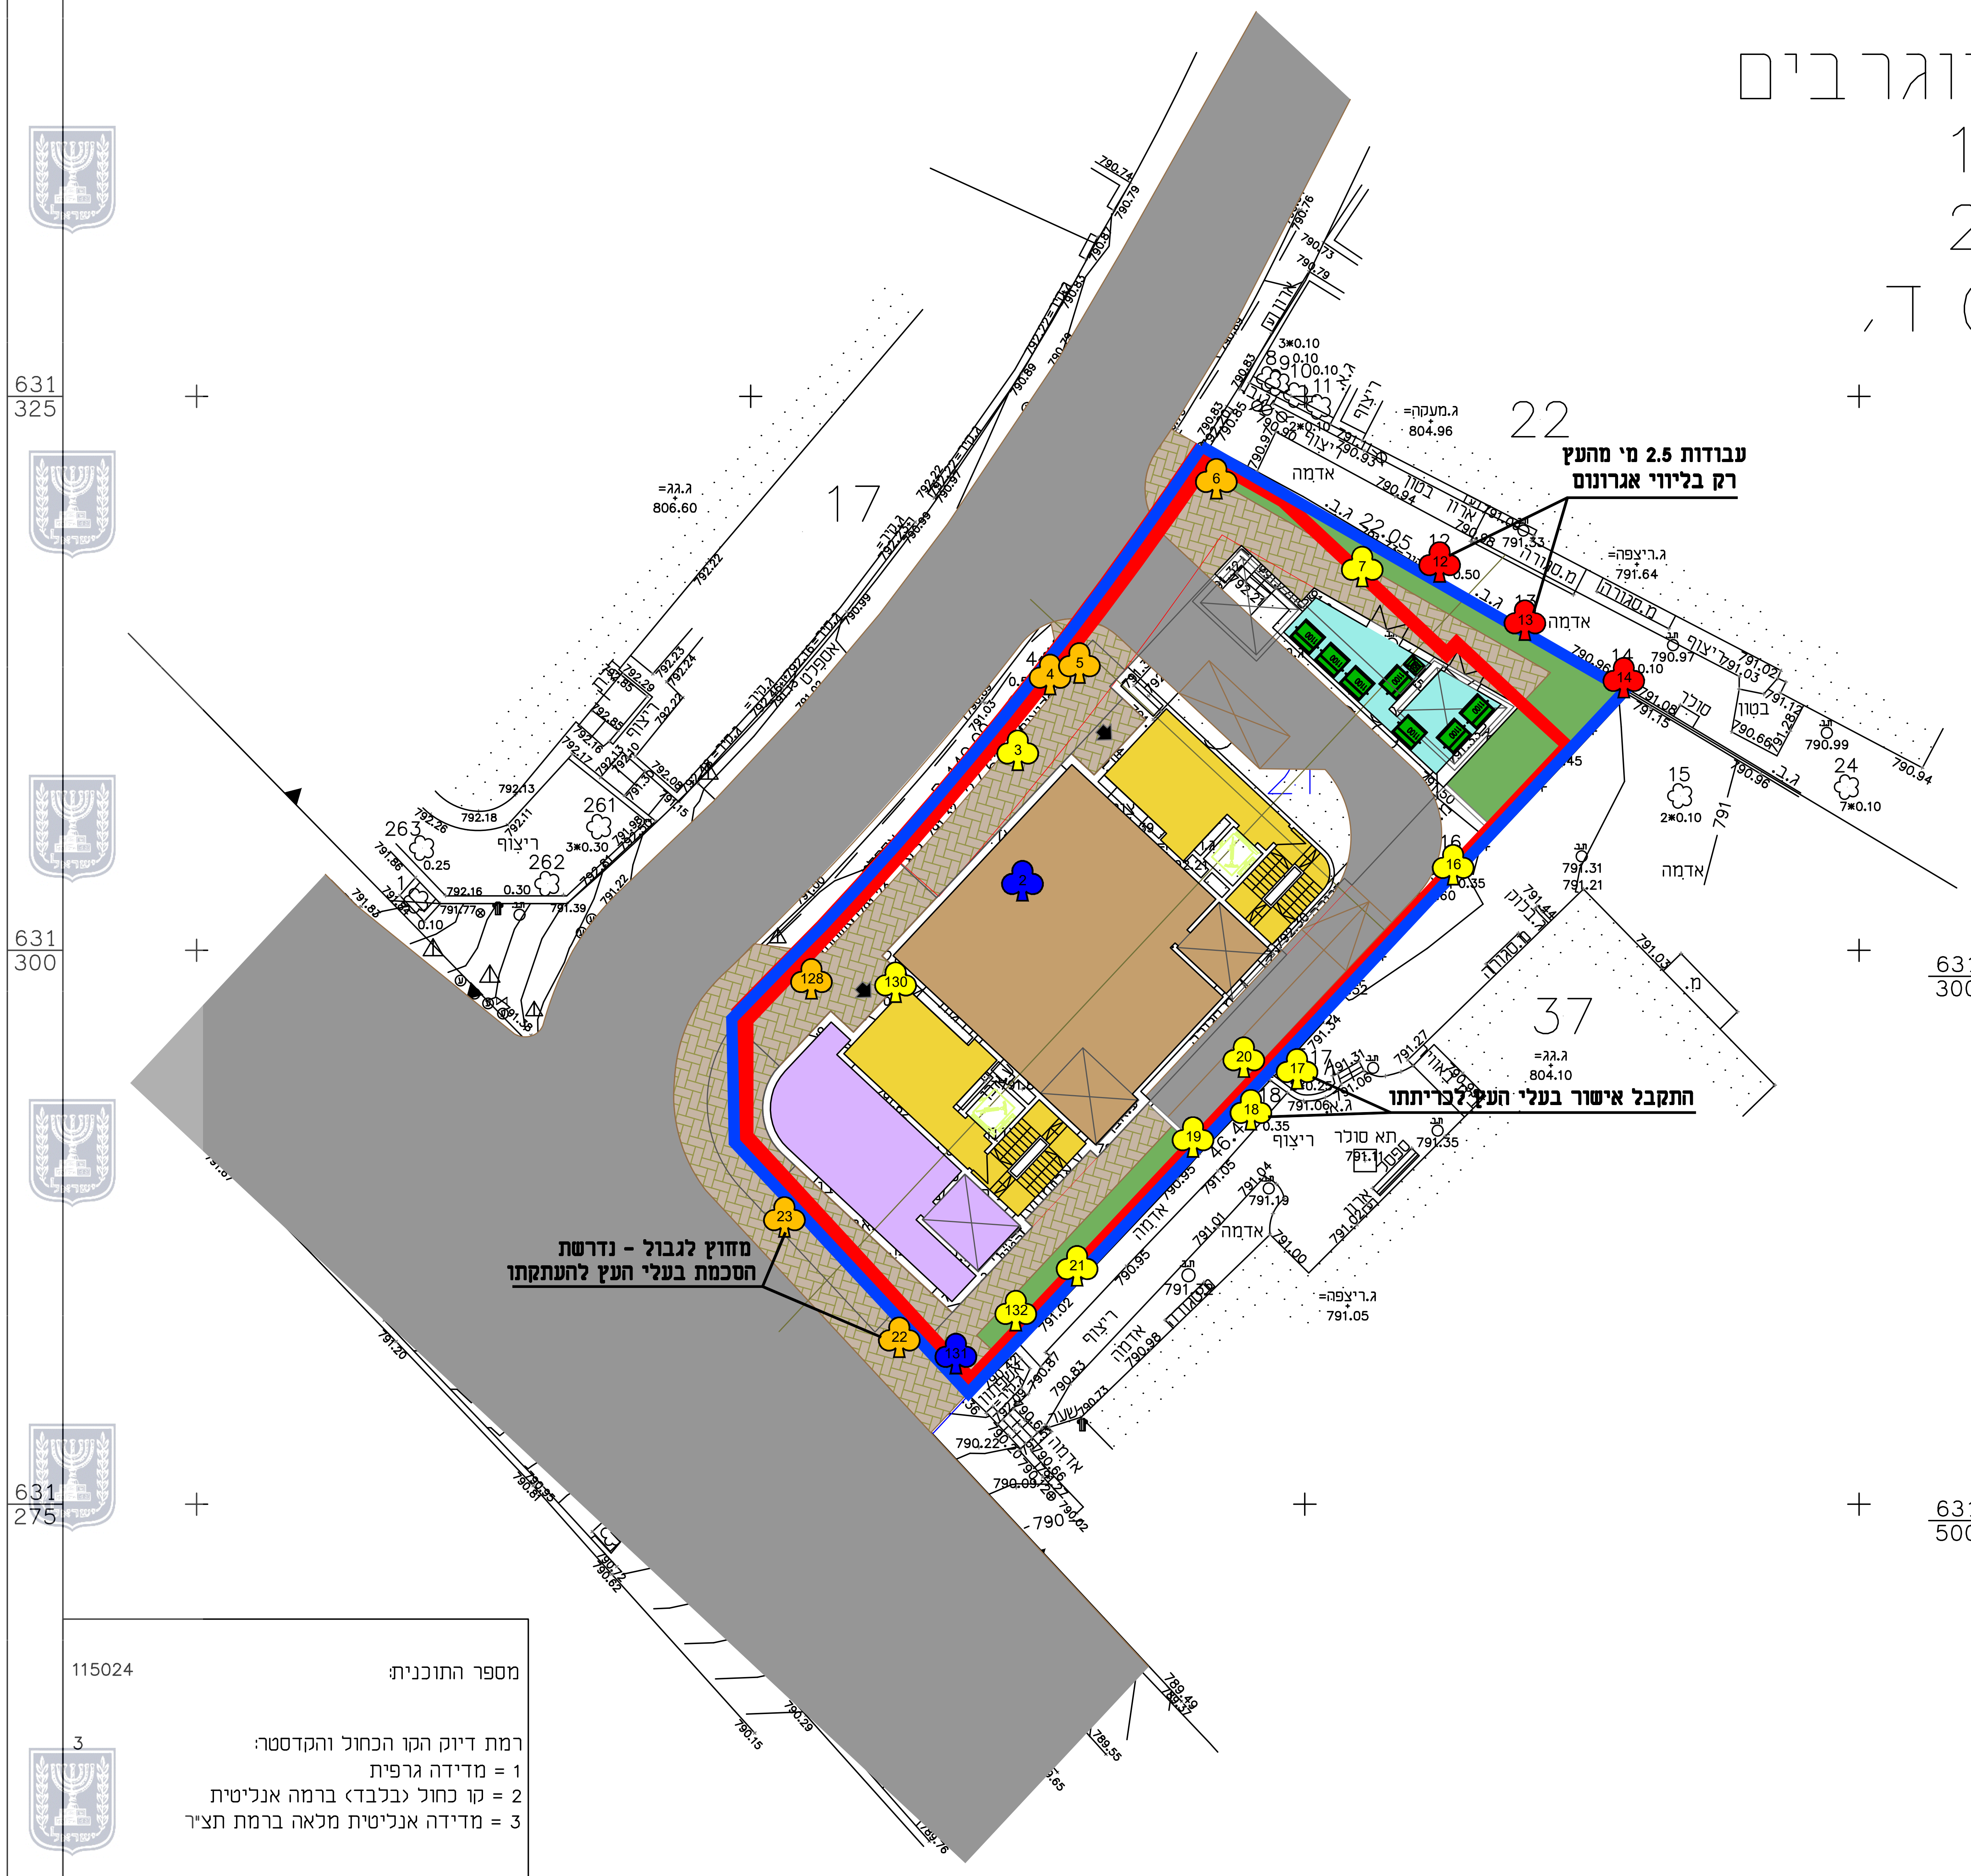

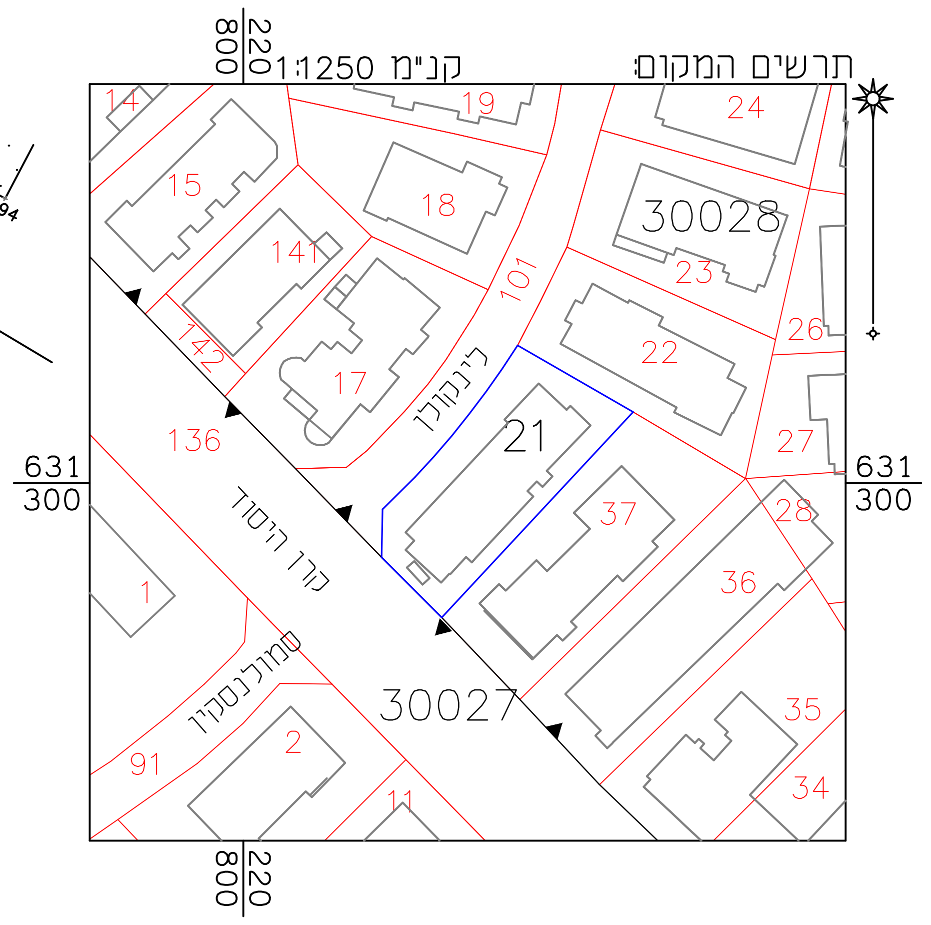

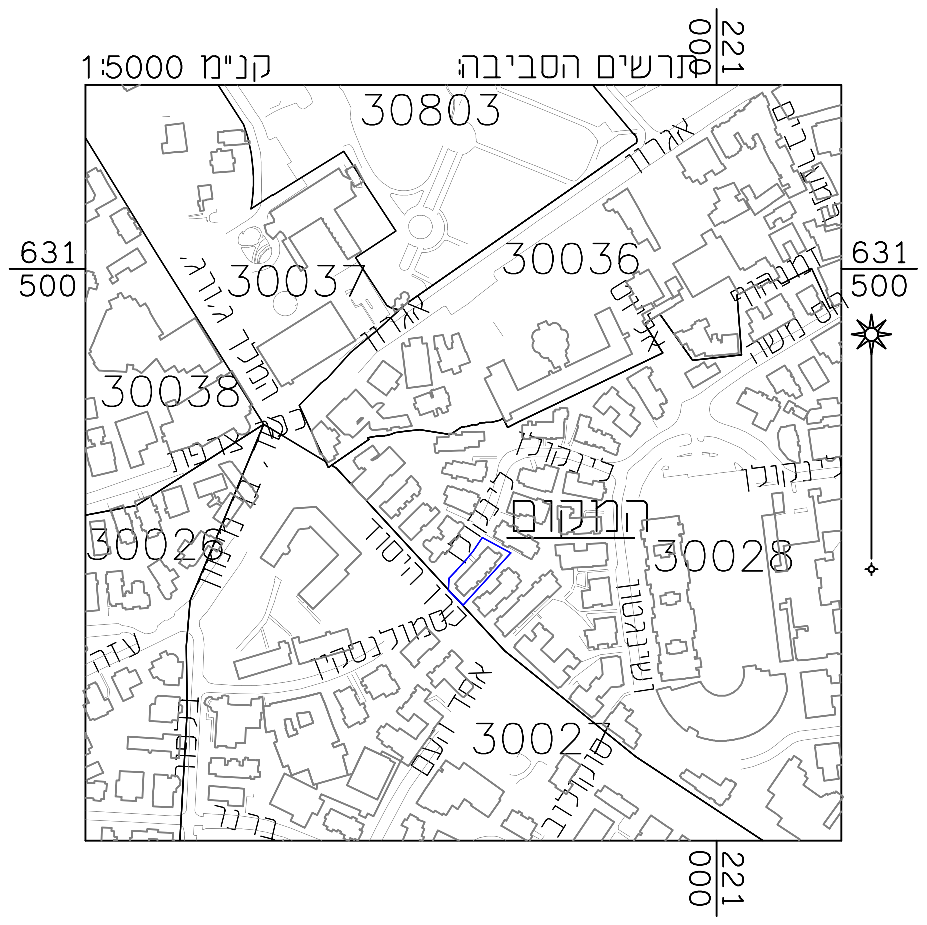

מספר התוכנית: 115024

רמת דיוק הקו הכחול והקדסטר: 3
1 = מדידה גרפית
2 = קו כחול (בלבד) ברמה אנליטית
3 = מדידה אנליטית מלאה ברמת תצ"ר

1. המדידה המקורית:
הריני מצהיר בזאת כי מדידת המפה הטופוגרפית/המצבית המהווה רקע לתוכנית זו, נערכה על ידי :

ביום: 18.02.24

והיא הוכנה לפי הוראות נוהל מבא"ית ובהתאם להוראות החוק ולתקנות המודדים שבתוקף.

שם המודד: אלסטר ראובן

מספר רישיון: 502

חתימה: ____________ תאריך: ____________

קנה מידה 1 : 250

מטר 5 4 3 2 1 0 5 10 15 20 25 מטר

הערות:
1. המדידה קשורה לרשת קואורדינטות ארצית ע"י נקודות GPS 988RS,9465RC
2. המדידה קשורה לרשת גבהים ארצית 988RS=788.23
3. גבולות החלקה 21 נלקחו לפי תצ"ר מתיק 1153/30.

שמירה על עצים בוגרים

לינקולן 13
ירושלים

נספח לתכנית גליון 1 מתוך 1

תחולה	מנחה
תאריך עריכת הנספח	10/05/26
רשימת התרשימים	קנ"מ
שמירה על עצים בוגרים	1:250

עורך הנספח	שם: אדיר אלווס	חתימה:
	תאגיד: אדיר יעוץ ופקוח נופי בע"מ	

🟧	עץ להעתקה
🟥	עץ לשימור
🟨	עץ לכריתה
🟧	עץ להעתקה שלא סומן ע"י מודד אלא בסימון עצמי במיקום משוער
🟥	עץ לשימור שלא סומן ע"י מודד אלא בסימון עצמי במיקום משוער
🟨	עץ לכריתה שלא סומן ע"י מודד אלא בסימון עצמי במיקום משוער
🟦	עץ פולשני/ממשפחת הדקליים/צעיר/לא קיים שאין צורך לסקור ולא נדרש רישיון לכריתתו
🟦	עץ פולשני/ממשפחת הדקליים, שסומן בסימון עצמי שאין צורך לסקור ולא נדרש רישיון לכריתתו
🟦	גבול התוכנית
🟥	קו מרתף מתוכנן
△	קבוצת עצים להעתקה
△	קבוצת עצים לשימור
△	קבוצת עצים לכריתה
▽	קבוצת עצים צעירים/פולשניים/דקליים ואין צורך ברשיון לכריתתם/העתקתם

רקע פיתוח ●	**רקע מדידה** ○
בקר: אדיר אלווס	**[✓ לעיון] \ לביצוע**

תאריך	שרטט	שינויים
19/03/2024	דור	**חומר לעיון**
18/07/2024	יחיעם נ.	**הגשה ראשונה**
10/10/2024	יחיעם נ.	**עדכון פיתוח**
07/11/2024	יחיעם נ.	**עדכון עצים 22-23**
10/05/2026	יחיעם נ.	**עדכון פיתוח וגבול**

אדיר
יעוץ ופקוח נופי בע"מ
טל': 09-8357777, דוא"ל: office@adir-nof.co.il, נייד: 052-2333555

הערות:
1. סקר זה הינו סקר נופי אגרונומי ואינו סקר הערכת סיכונים/סקר בטיחות.
2. אין לבצע את כריתת/העתקת העצים המומלצים אלא לאחר קבלת רישיון כריתה כחוק-מפקיד היערות העירוני.
3. עץ המוגדר לשימור - אין לבצע עבודות גיזום נוף/גיזום שורשים, ללא תיאום עם החו"מ.
4. עץ המוגדר לשימור - אין לבצע עבודות חפירה ו/או מילוי במרחק הקטן מפי 10 מקוטר מגזע העץ, ללא תיאום עם החו"מ.
5. תוקף הסקר 6 חודשים מביצוע הסקר בשטח.
6. עצים המאושרים לכריתה, יינטעו תמורתם עצים באותו הערך-כפיצוי נופי.
7. כל פעולה העלולה לגרום למות העץ - כולל פגיעה/חיתוך שורשיו, הרעלה , הסרת קליפה, שרפת העץ - נחשבת עפ"י חוק ככריתה ללא היתר.
8. מיספור העצים בהתאם לתכנית הסקר, יבוצע מייד עם הכניסה לביצוע העבודות באתר - הסימון יאושר ע"י המפקח והאגרונום.

10. אין לבצע עירום פסולת/אחסנת חומרים בתחום שטח הגנת העצים.

פרט עץ לשימור ללא קנ"מ

פירוט:
- גידור פח איסכורית/גלי בגובה מינימלי 2 מ' מהקרקע ובמרחק פי 10 מקוטר הגזע בבסיסו.
- מיקום סופי של הגדר יקבע ע"י המפקח בשטח.
- הגידור יהיה היקפי סביב העץ ע"ג הגדר יותקן שלט ברור "עץ מוגן לשימור" עפ"י הדוגמא שלהלן, בגודל A4 בכל החזיתות

דוגמת המדבקה

עץ
לשימור
אין לפגוע בעץ ואין לחפור בסביבתו
يمنع الإضرار بالشجرة أو الحفر حولها
אדיר
יעוץ ופקוח נופי בע"מ