מינהל התכנון
חוק התכנון והבניה, התשכ"ה - 1965
מחוז ירושלים
הוועדה המחוזית החליטה ביום :
10/02/2025
להפקיד את התכנית
09/08/2026
יו"ר הוועדה המחוזית תאריך

תכנית 101-1185578 13/05/2026 08:04:24 נספח בינוי ופיתוח נספח בינוי חתכים וחזיתות. מחייב לעניין מספר הקומות ומיקום

מרחב תכנון ירושלים

תכנית מס' 101-1185578

התחדשות עירונית חזקיהו המלך 39-45
קטמון הישנה, ירושלים

בינוי ופיתוח - חתכים וחזיתות

קנ"מ: 1:250

מקרא

גבול תכנית	▬
מספר תא שטח	000
קו בניין	‒ · ‒
קו בניין תחתי (תת-קרקעי)	‒ · ‒
חזית מסחרית	─
ציבורי	●
מסחר	●
לובי מגורים	●
ציבורי-דיירים	●
חצר פרטית	●
חצר ציבורית	●
עץ לשימור	♣
עץ לכריתה	♣

שלב: הפקדה **מהדורה :** 01 **תאריך :** 12/May/2026

עורך התכנית	שם: איגרא-שקד אדריכלים		חתימה :
	כתובת : גן טכנולוגי, בנין 1, מלחה, ירושלים		
	טלפון : 02-6521350	פקס :	דוא"ל office@mic-arc.com

חתך 1-1

קנ"מ 1:250

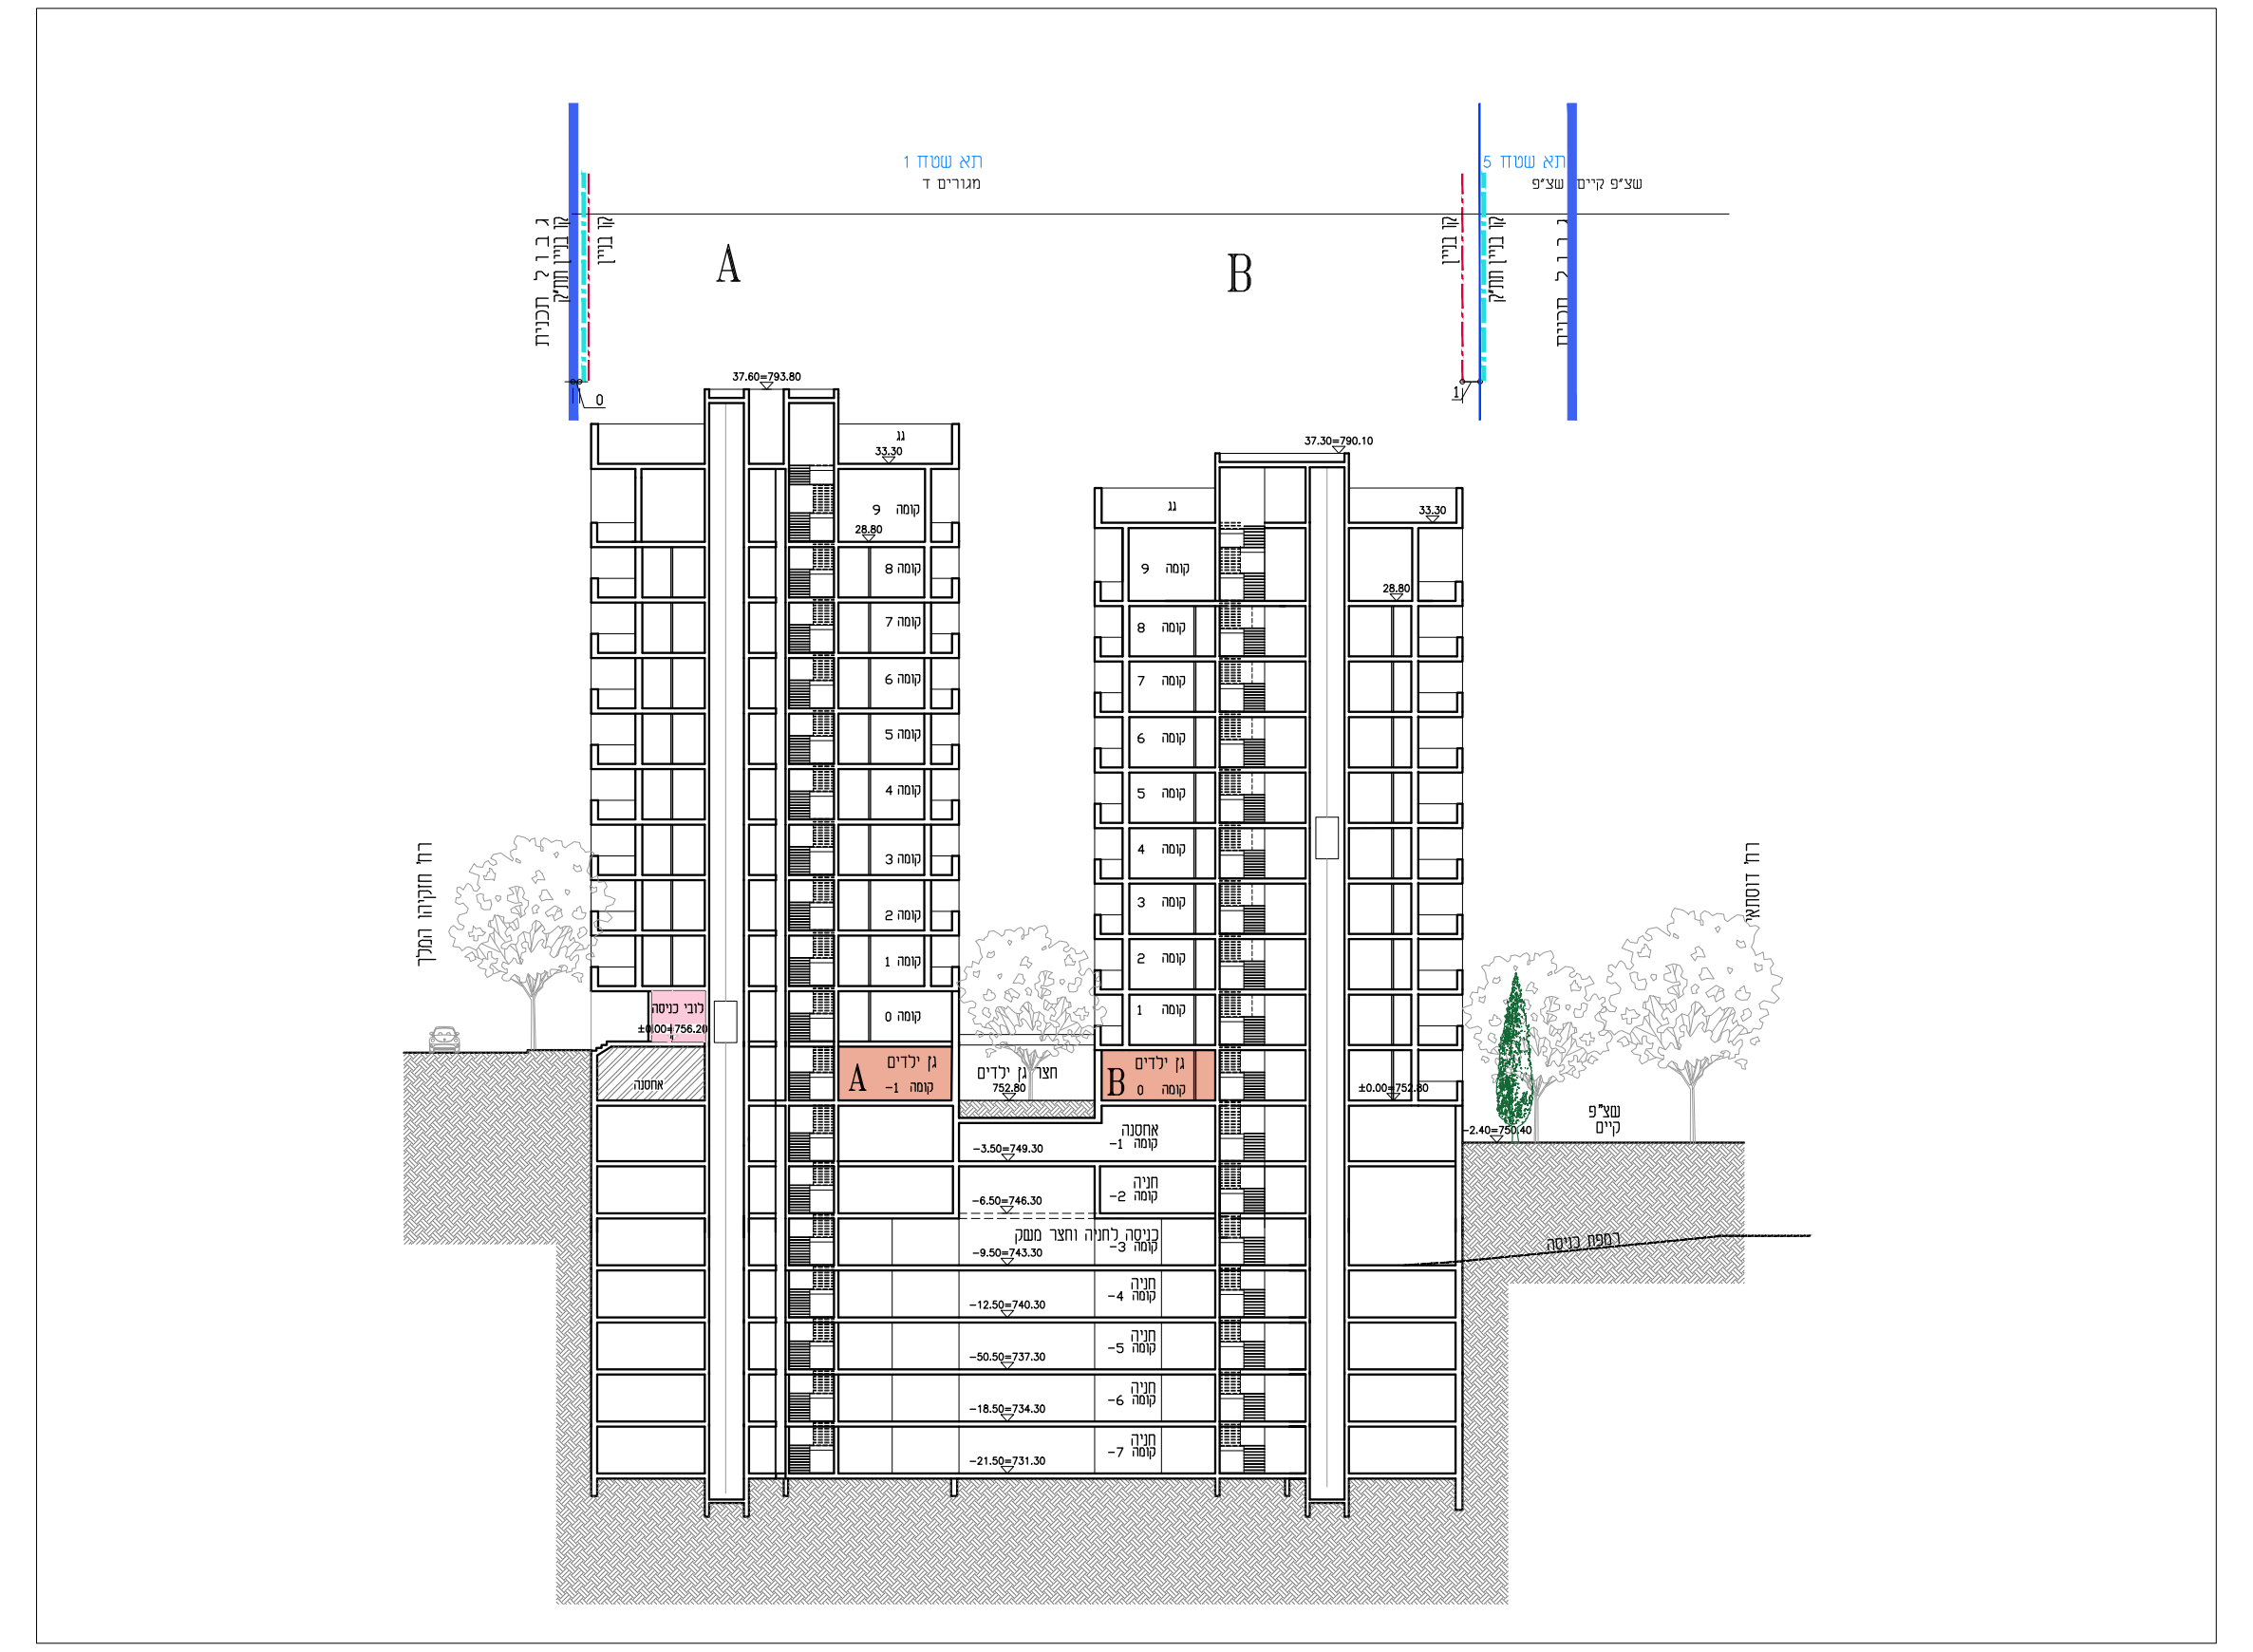

חתך 2-2

קנ"מ 1:250

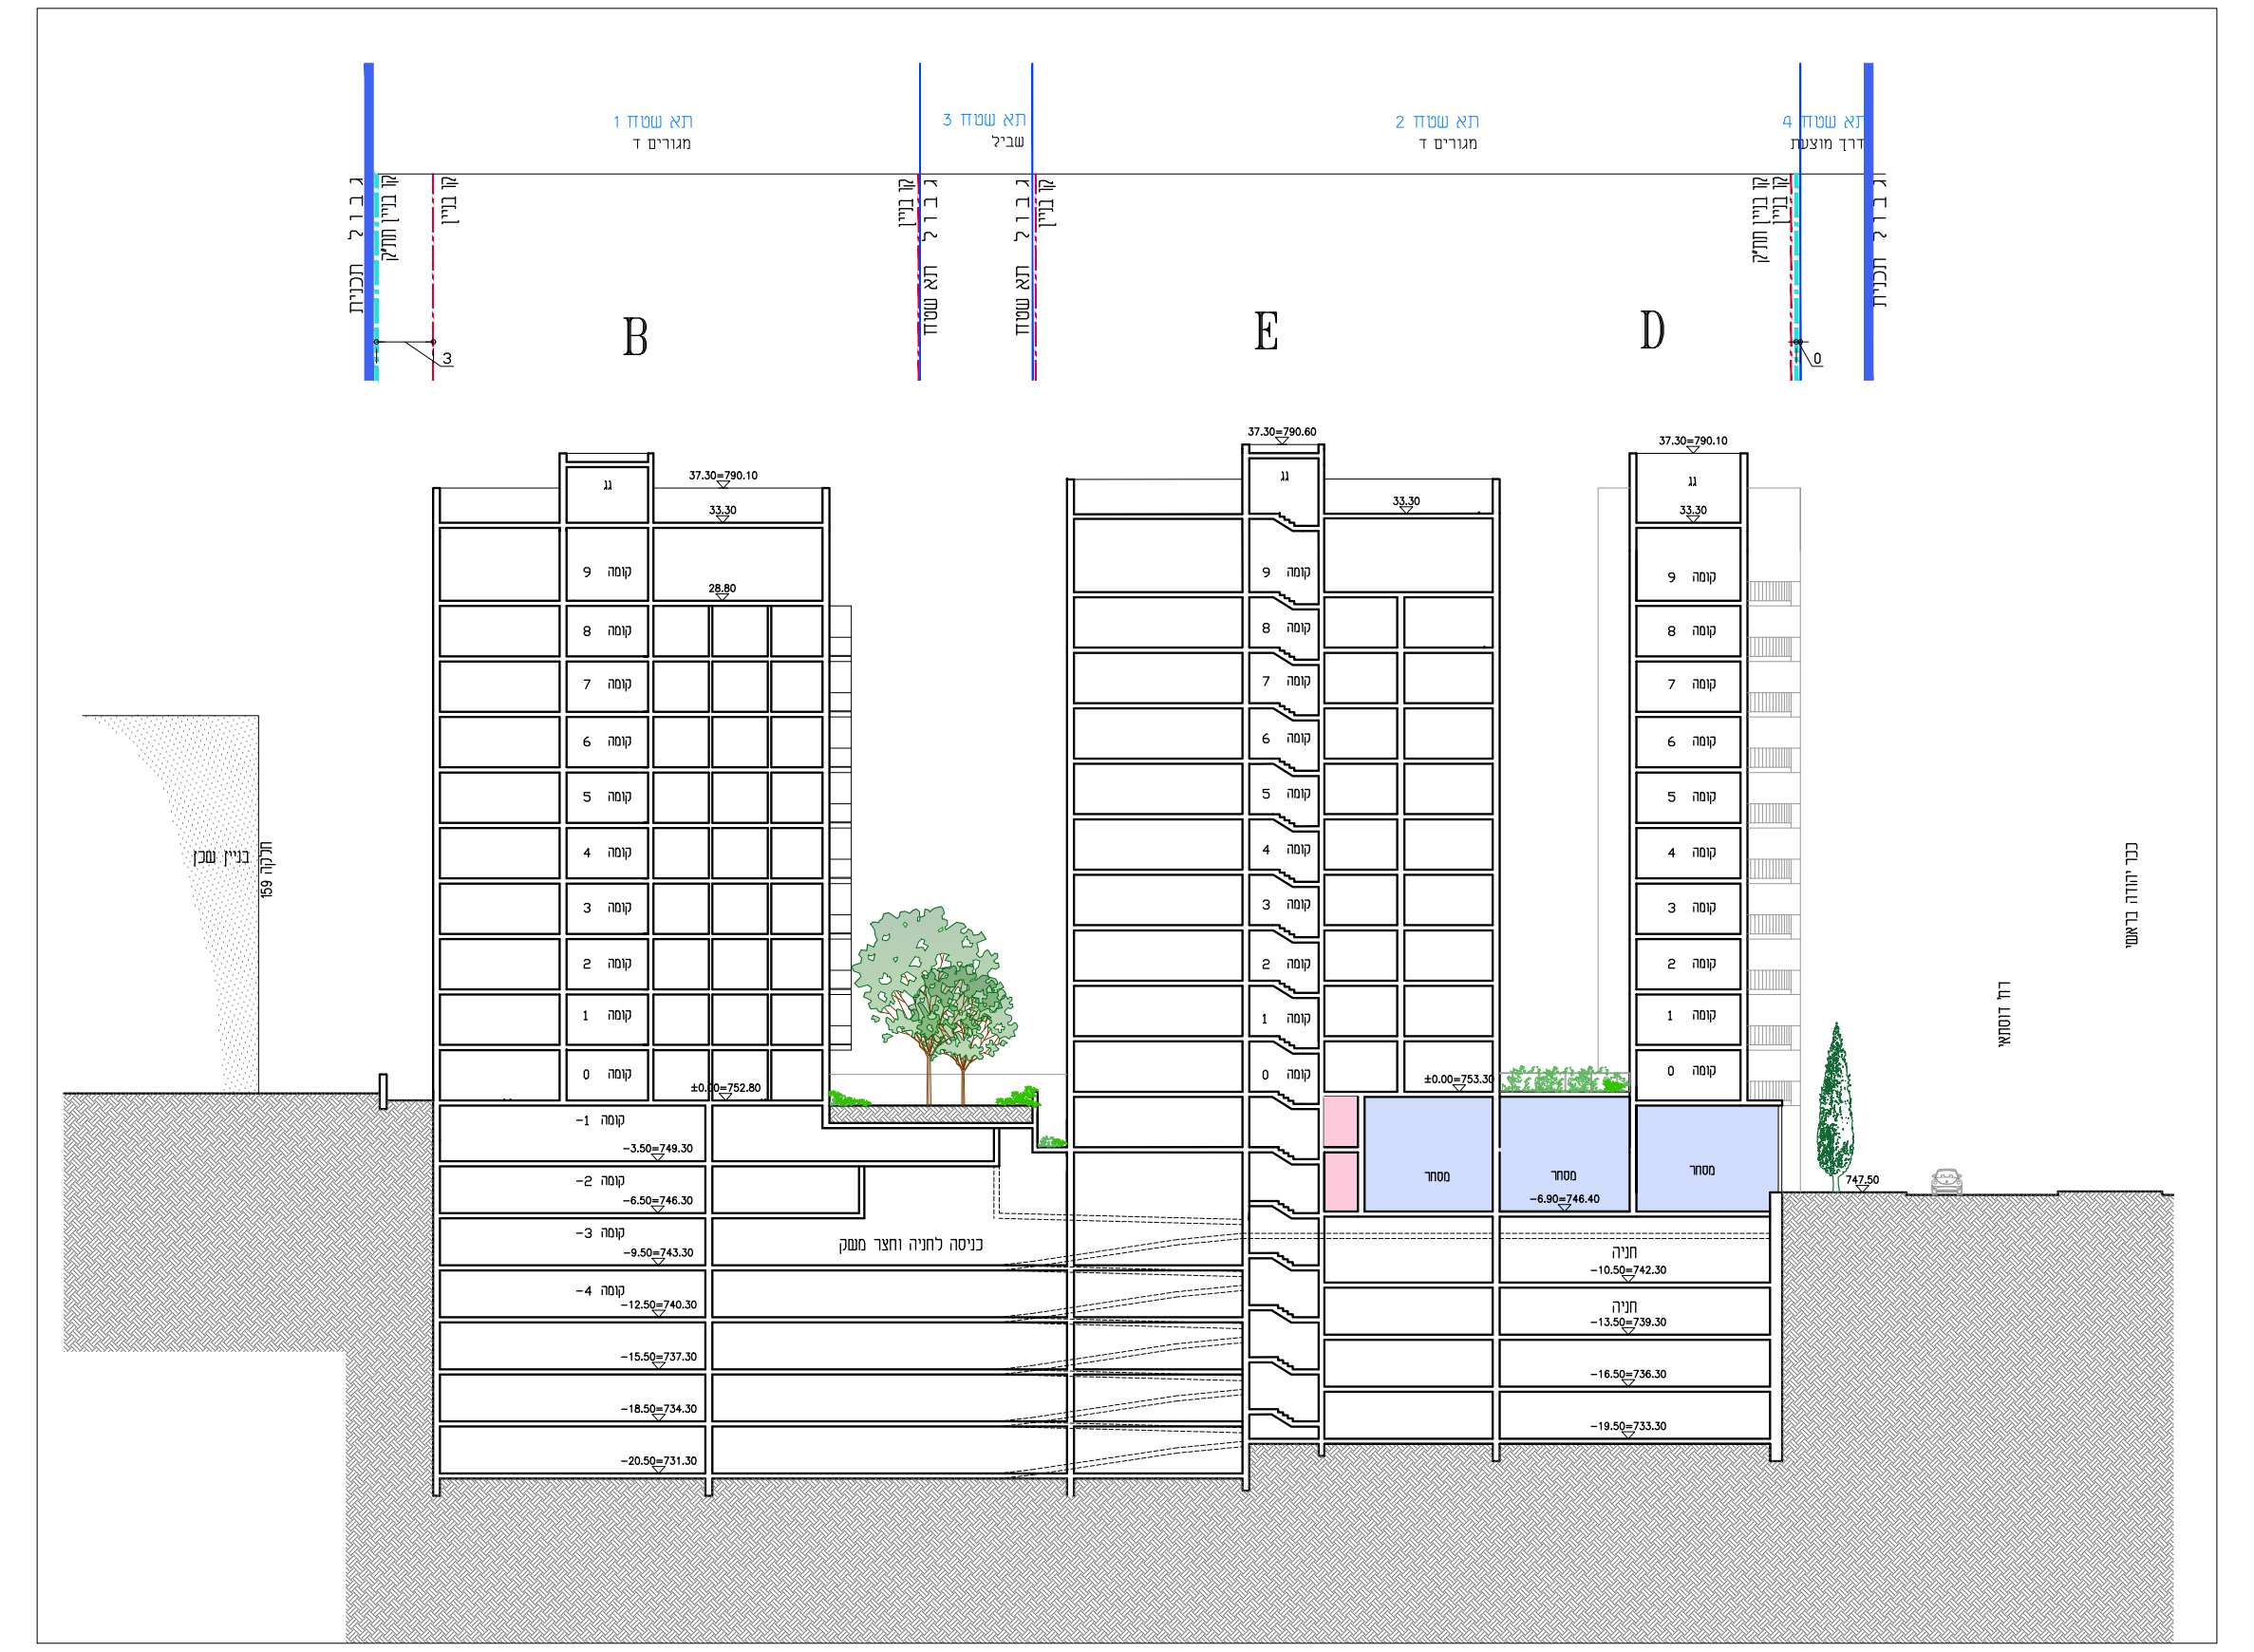

חזית רחוב חזקיהו

קנ"מ 1:250

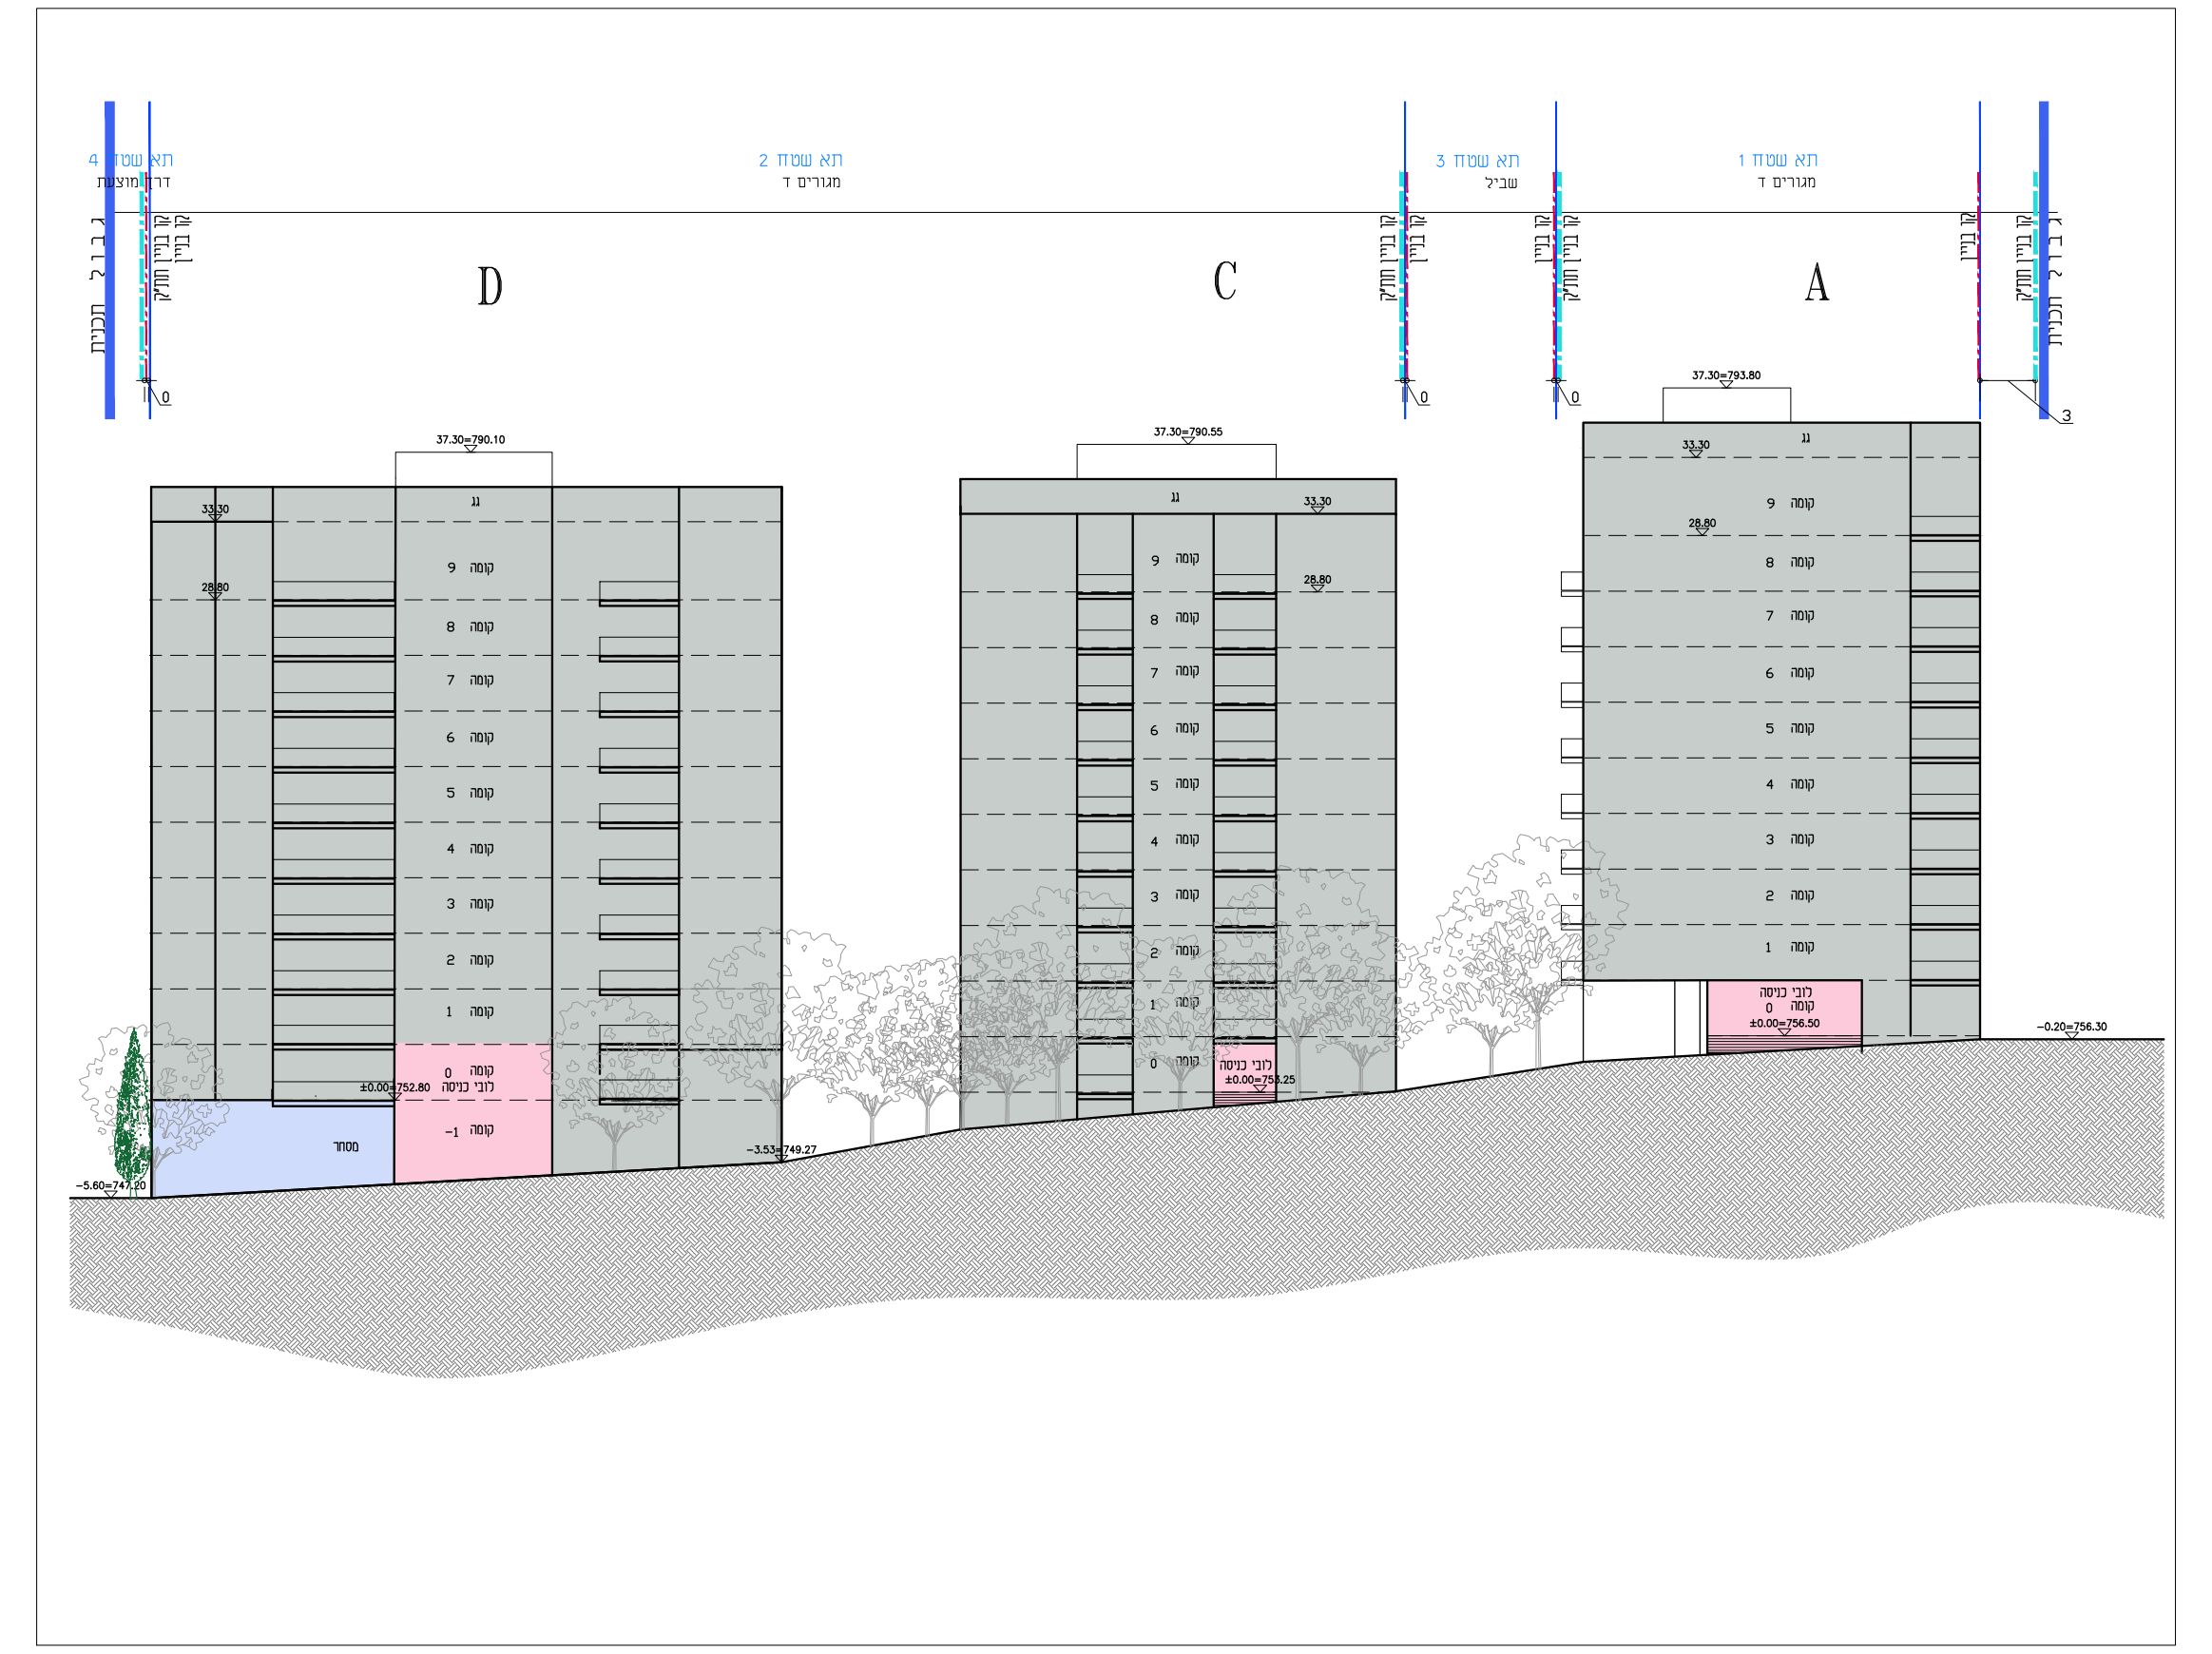

חזית מערבית

קנ"מ 1:250

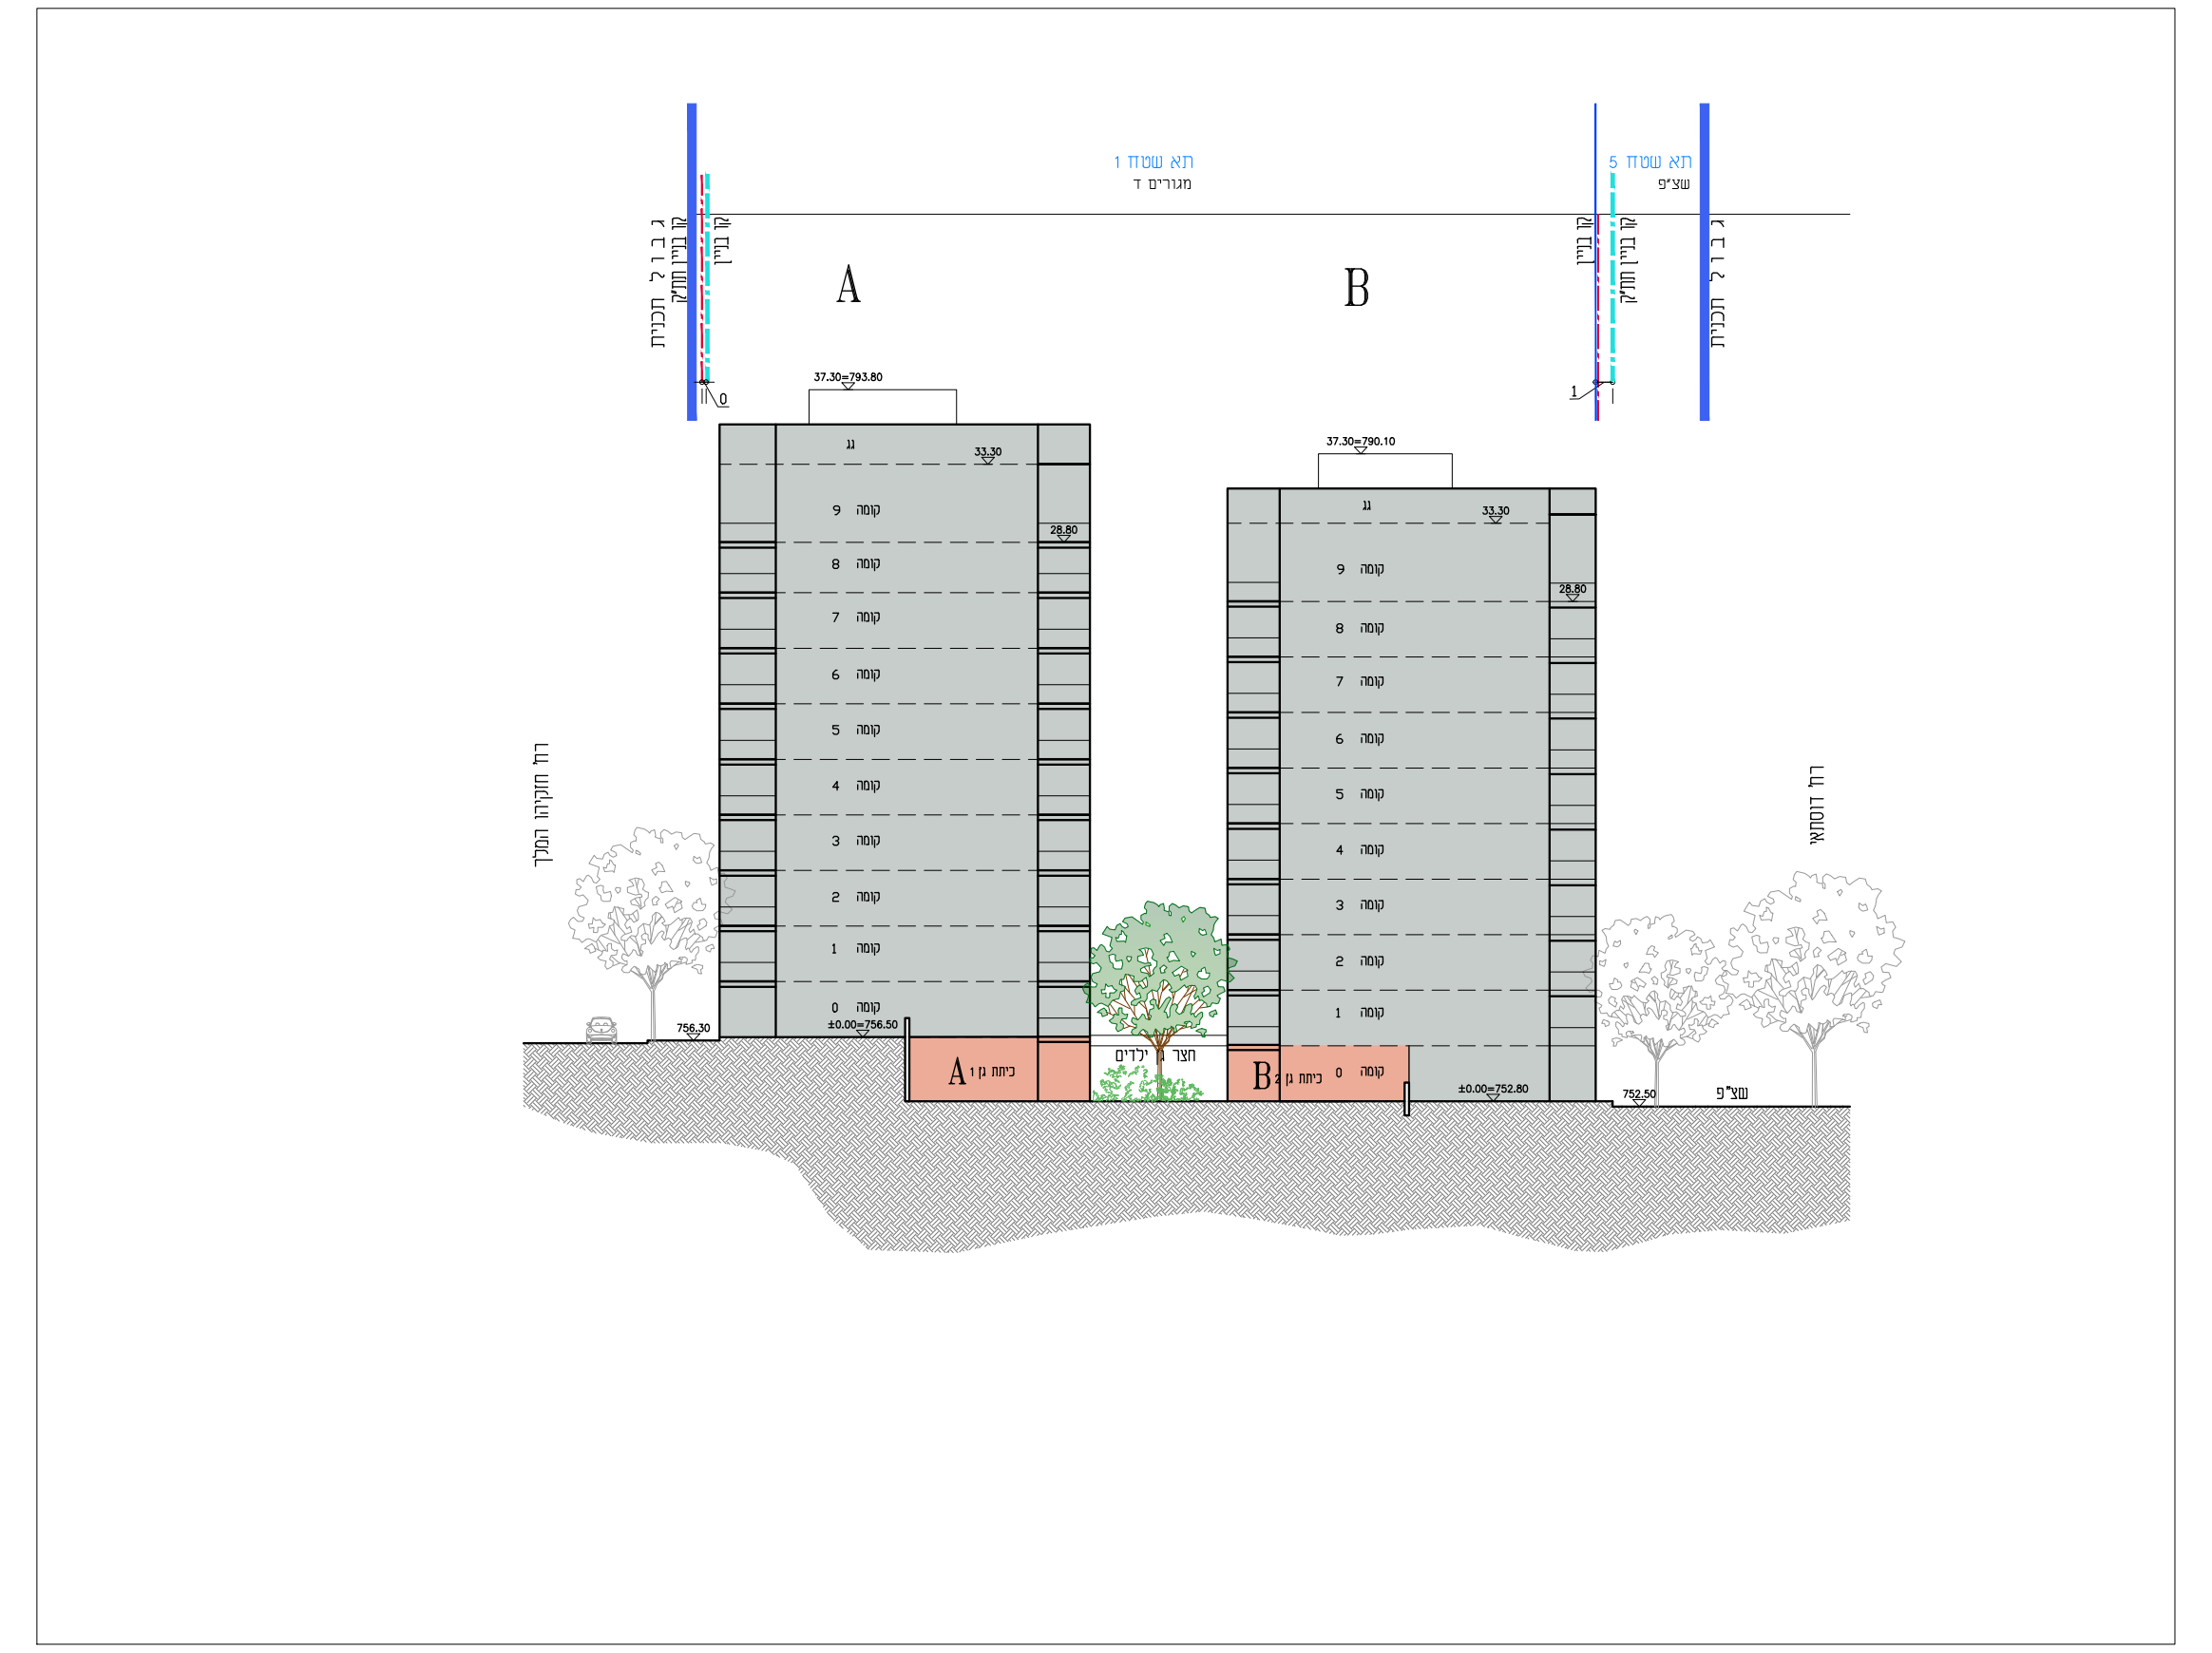

חזית דרומית

קנ"מ 1:250