מינהל התכנון
חוק התכנון והבניה, התשכ"ה - 1965
מחוז ירושלים
הוועדה המחוזית החליטה ביום :
10/02/2025
להפקיד את התכנית
09/08/2026
תאריך יו"ר הוועדה המחוזית

תכנית 101-1185578 13/05/2026 08:02:49 נספח בינוי ופיתוח נספח בינוי, תוכניות. מחייב לעניין מספר קומות מיקום

מרחב תכנון ירושלים

תכנית מס' 101-1185578

התחדשות עירונית חזקיהו המלך 39-45
קטמון הישנה, ירושלים

נספח בינוי ופיתוח

קנ"מ: 1:250

מקרא

גבול תכנית	▬
מספר תא שטח	000
קו בניין	▬ ▪ ▬
קו בניין תחתי (תת-קרקעי)	▬ ▪ ▬
חזית מסחרית	―
ציבורי	●
מסחר	●
לובי מגורים	●
ציבורי-דיירים	●
חצר פרטית	●
חצר ציבורית	●
עץ לשימור	♣
עץ לכריתה	♣

שלב: הפקדה **מהדורה :** 01 **תאריך :** 12/May/2026

עורך התכנית	שם: איגרא-שקד אדריכלים		חתימה :
	כתובת : גן טכנולוגי, בנין 1, מלחה, ירושלים		
	טלפון : 02-6521350	פקס :	דוא"ל office@mic-arc.com

תכנית גגות

קנ"מ 1:250

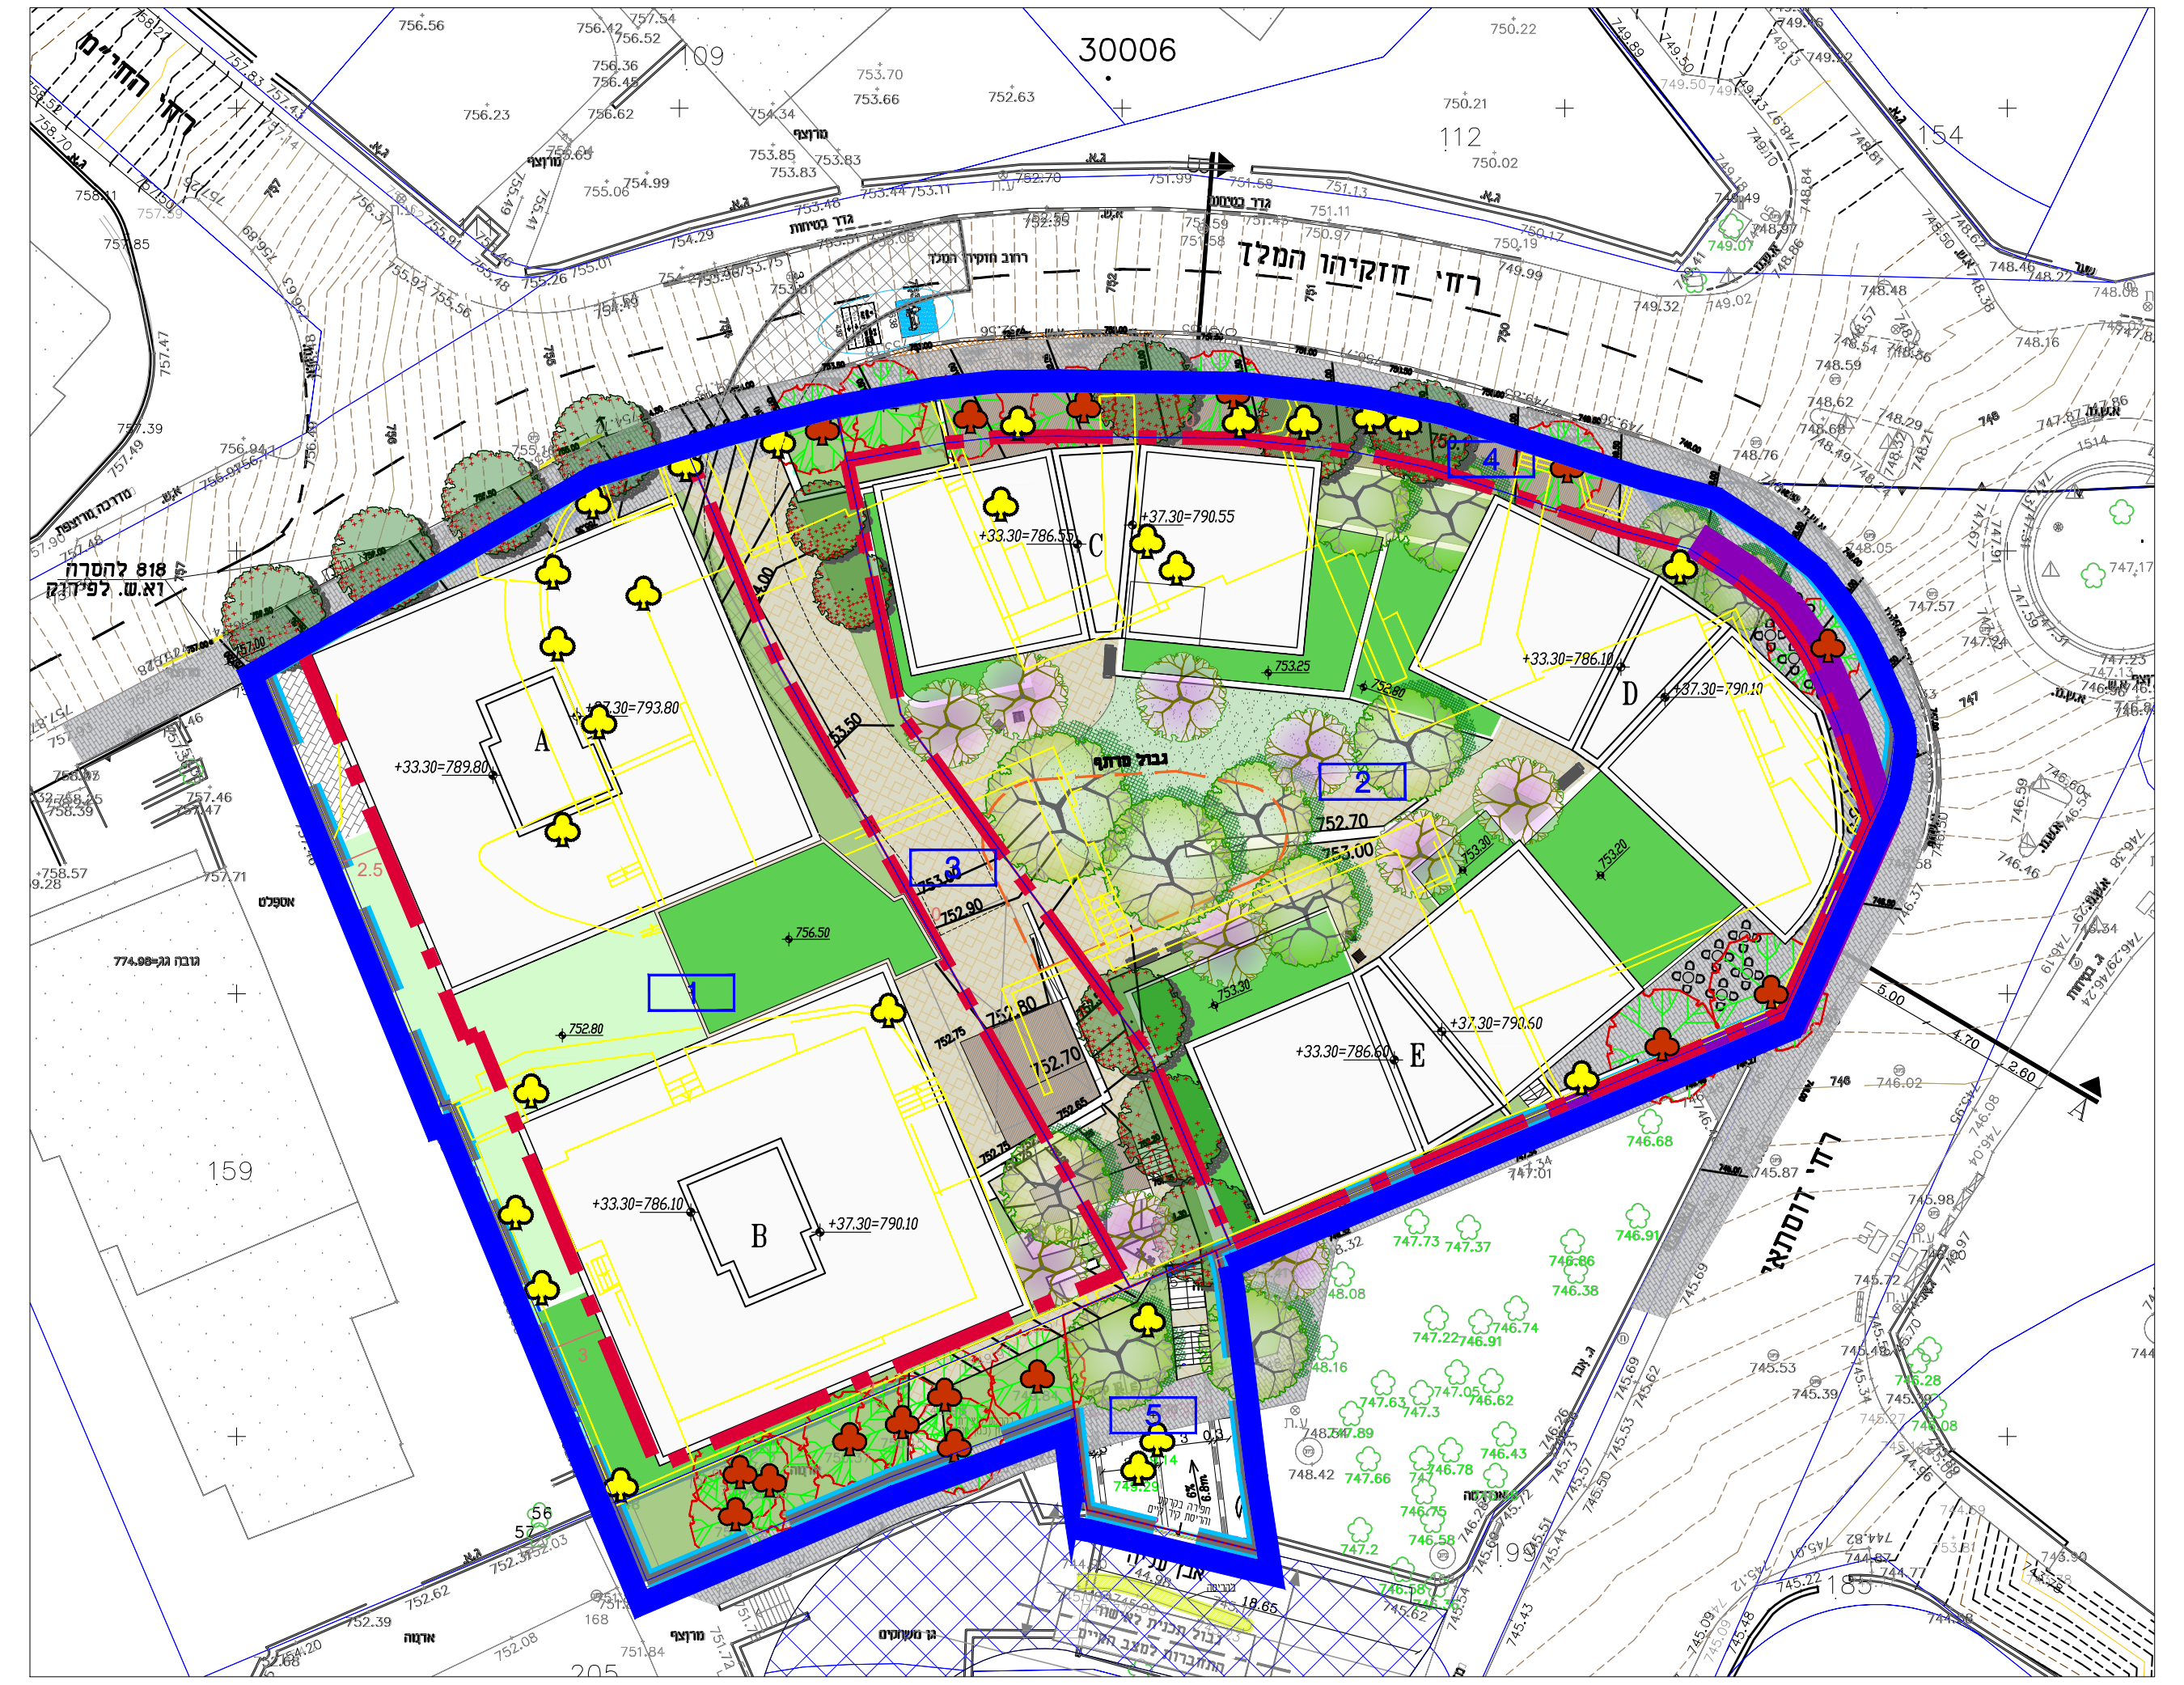

תכנית קומה טיפוסית

קנ"מ 1:250

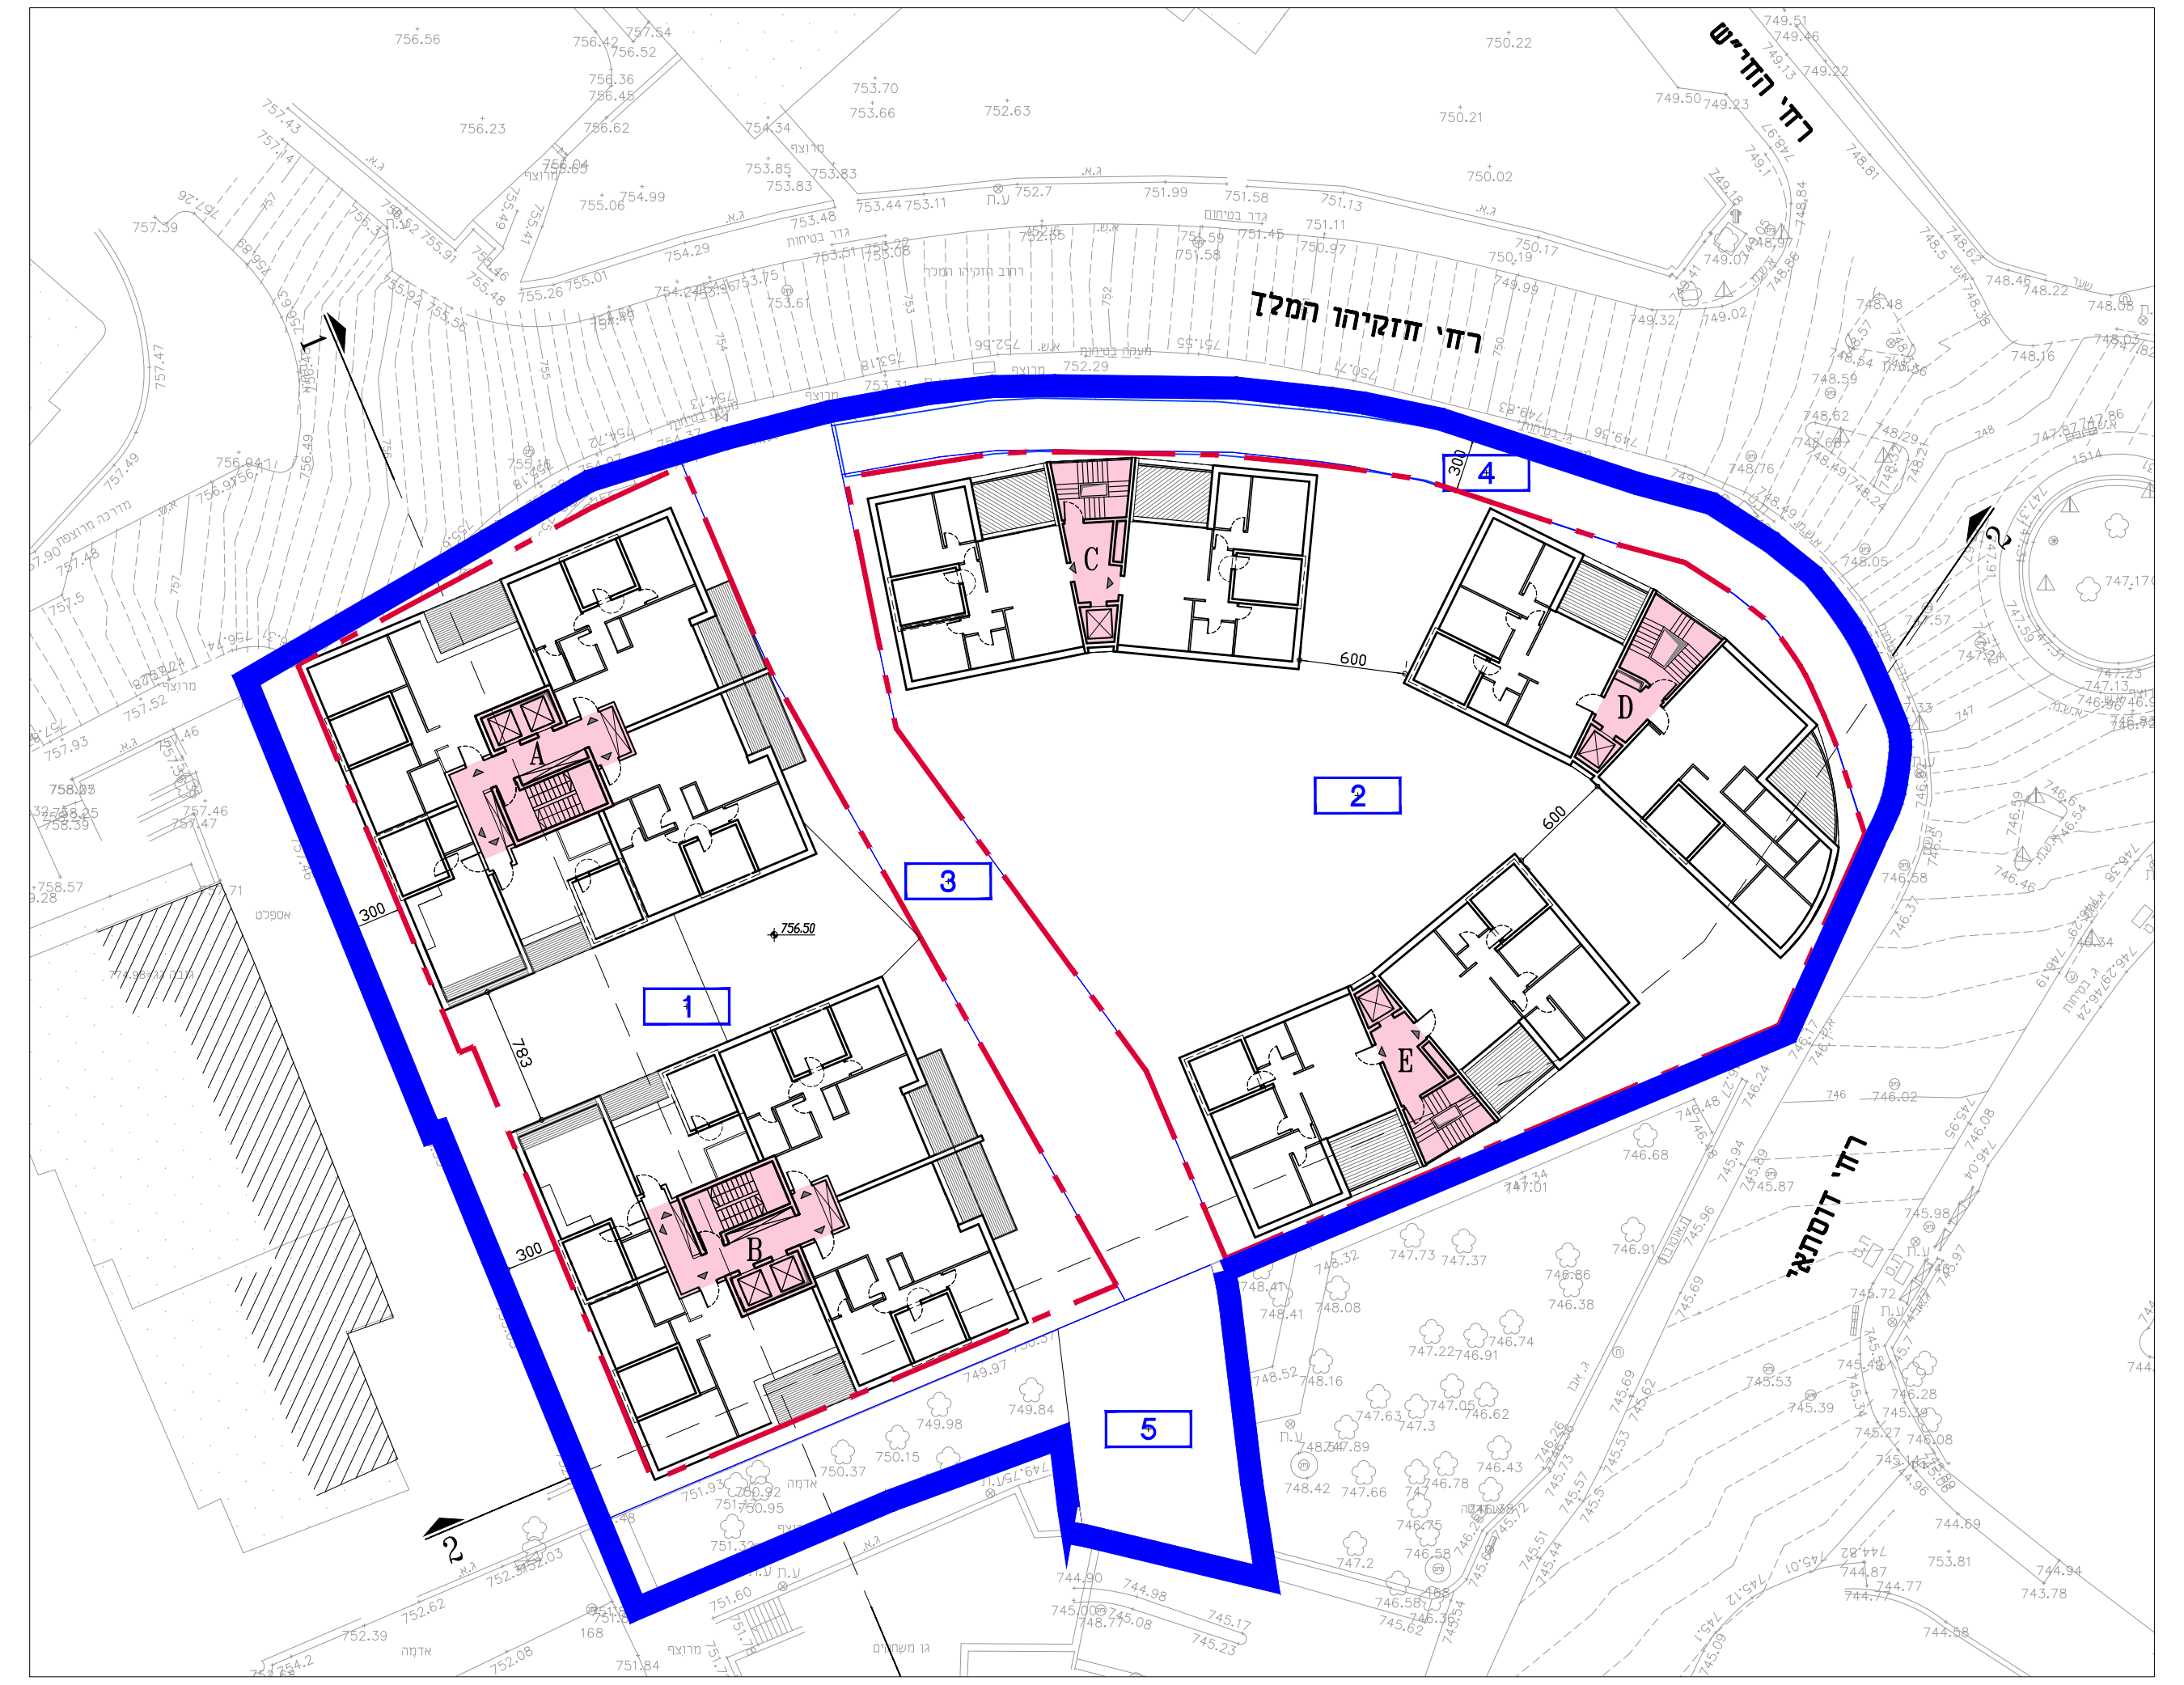

קומת כניסה למגורים

קנ"מ 1:250

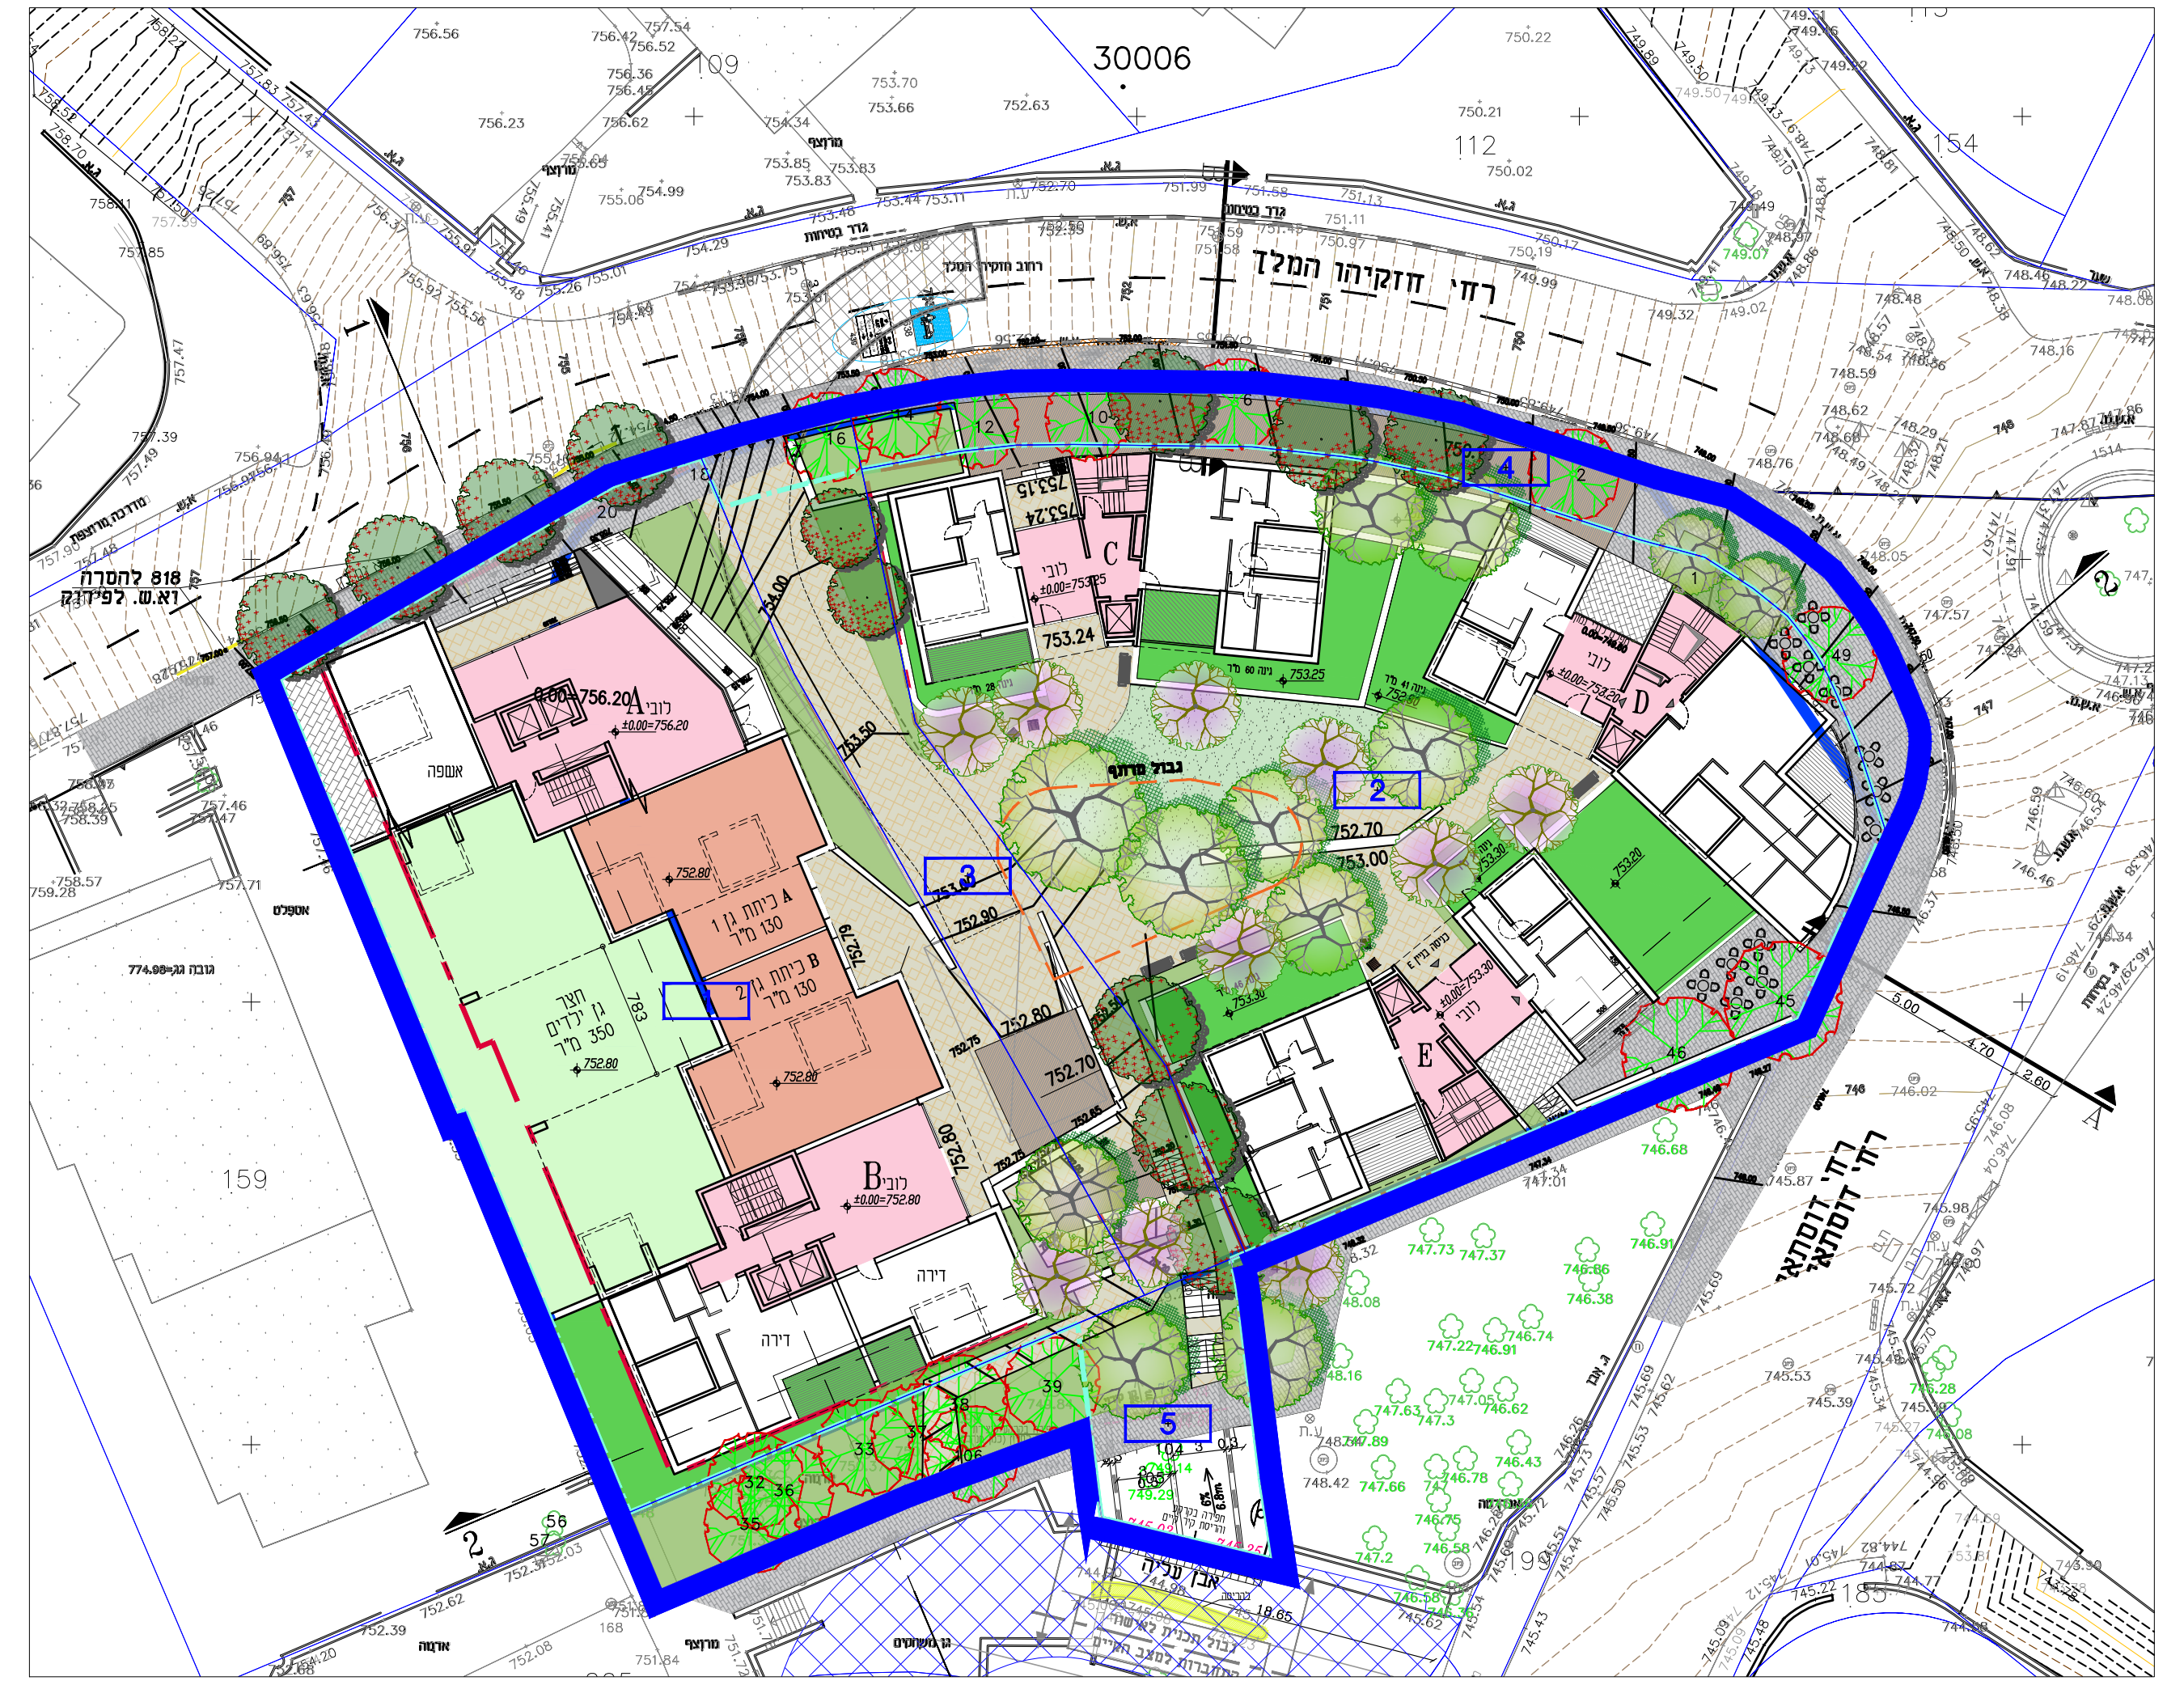

מפלס בניין A
±0.00=756.20

מפלס בניין B
±0.00=752.80

מפלס בניין C
±0.00=753.25

מפלס בניין D
±0.00=752.80

מפלס בניין E
±0.00=753.30

קומת כניסה לחניון + מסחר

קנ"מ 1:250

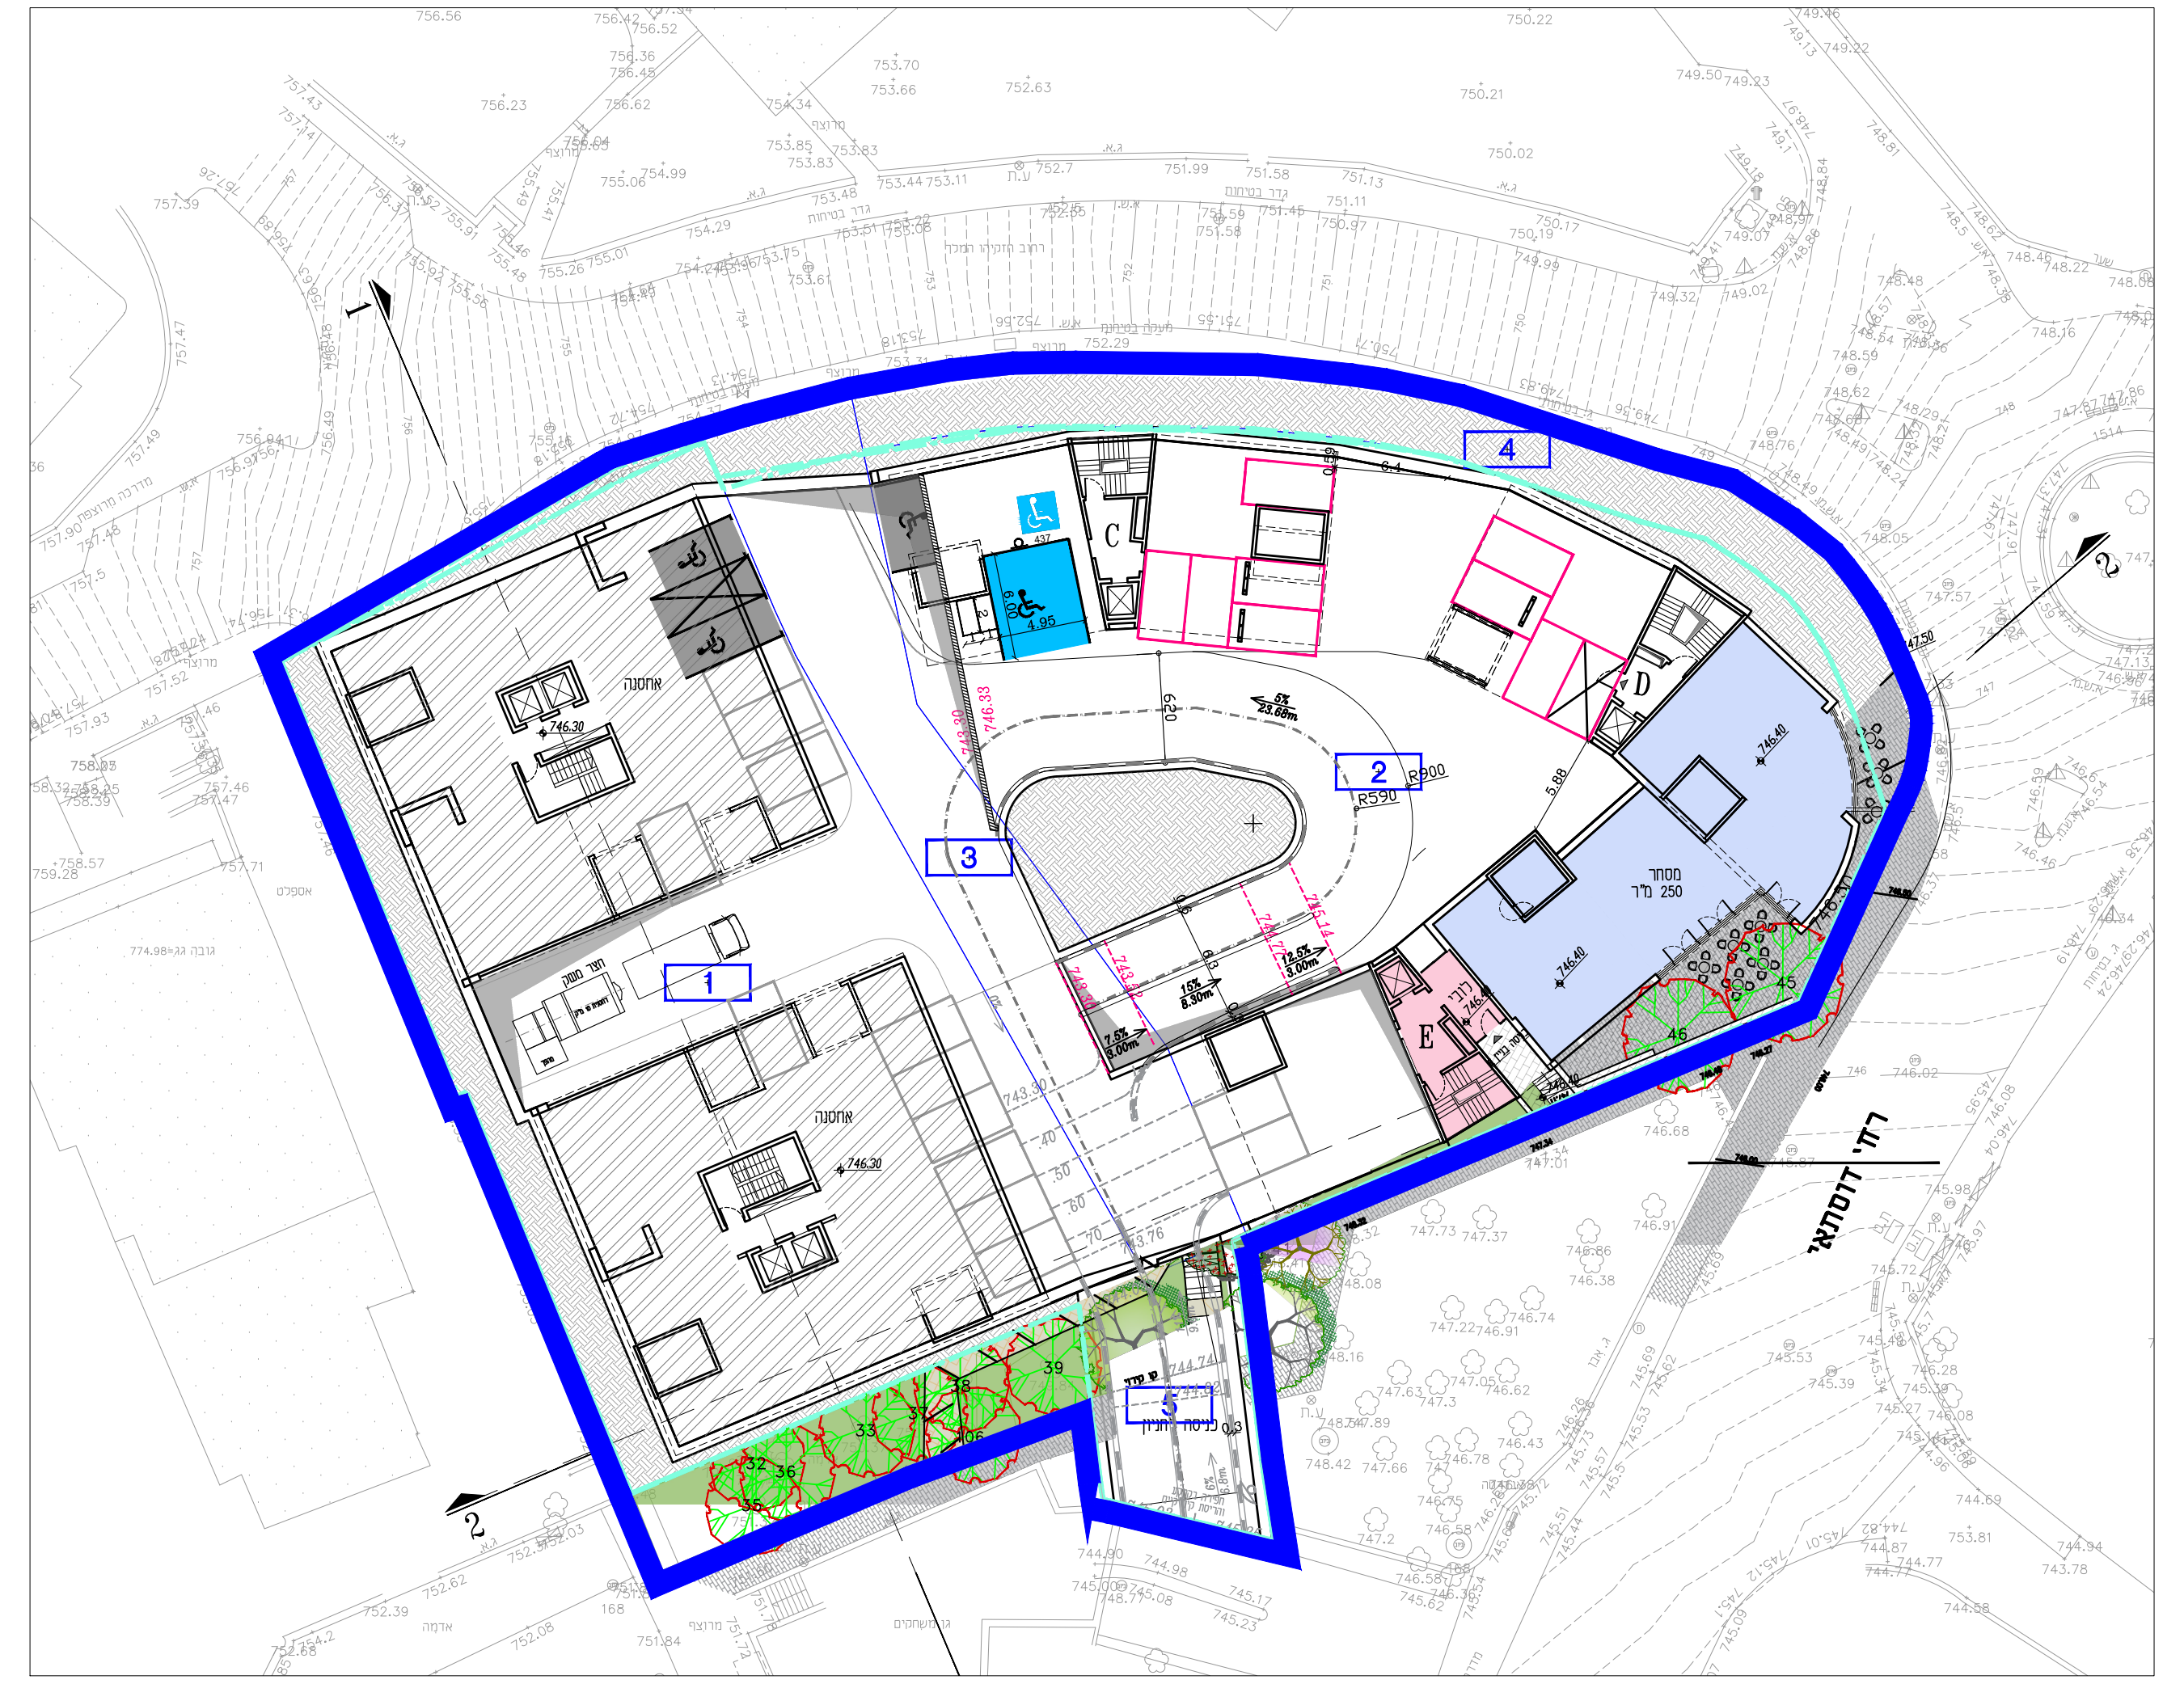

קומת חניון טיפוסית

קנ"מ 1:250