מינהל התכנון
חוק התכנון והבניה, התשכ"ה - 1965
מחוז ירושלים
הוועדה המחוזית החליטה ביום :
10/02/2025
להפקיד את התכנית
09/08/2026
תאריך יו"ר הוועדה המחוזית

תכנית 101-1185578 נספח ירושלים 16:28:25 12/05/2026

טבלת הקצאה לתכנית מפורטת מס' 101-1185578

נתוני המקרקעין										מצב יוצא				
מס"ד	גוש	חלקה	שטח החלקה רשום מ"ר	שטח החלקה הכלולה בחלוקה החדשה מ"ר	אזור מגורים	שצ"פ	דרך	החלקים בבעלות או בזכויות ב %	סה"כ	מס' מגרש תמורה	מס' מגרש מוקצה ארעי/סופי	יעוד המגרש המוקצה	שטח מגרש מוקצה	חלקים במגרש ב %
1	30005	105	3,355	90			90	2.68%	90		1	מגורים ד	1,510	לפי נספח הקצאה ואיזון
2		138	3,248	3,248	3,248			100.00%	3,248		2	מגורים ד	1,719	
3		160	444	444			444	100.00%	444		3	שביל	344	
4		205	3,393	258		258		7.60%	258		4	דרך	209	
											5	שצ"פ	258	
סה"כ				**4,040**	3,248	258	534		**4,040**				**4,040**	

1. יחס הבעלות של החלקות מפורט בטבלת ההקצאות ואיזון של השמאי המצורפת כנספח לתב"ע.
2. אני, אהוד קראוס מודד מוסמך, חתום מטה מאשר בזה כי חישוב השטחים שבטבלת איחוד וחלוקה נכונים, בדקתי החישוב פלנימטרית ובשיטה דיגיטלית

אהוד קראוס – מודד מוסמך
רשיון מס' 1363

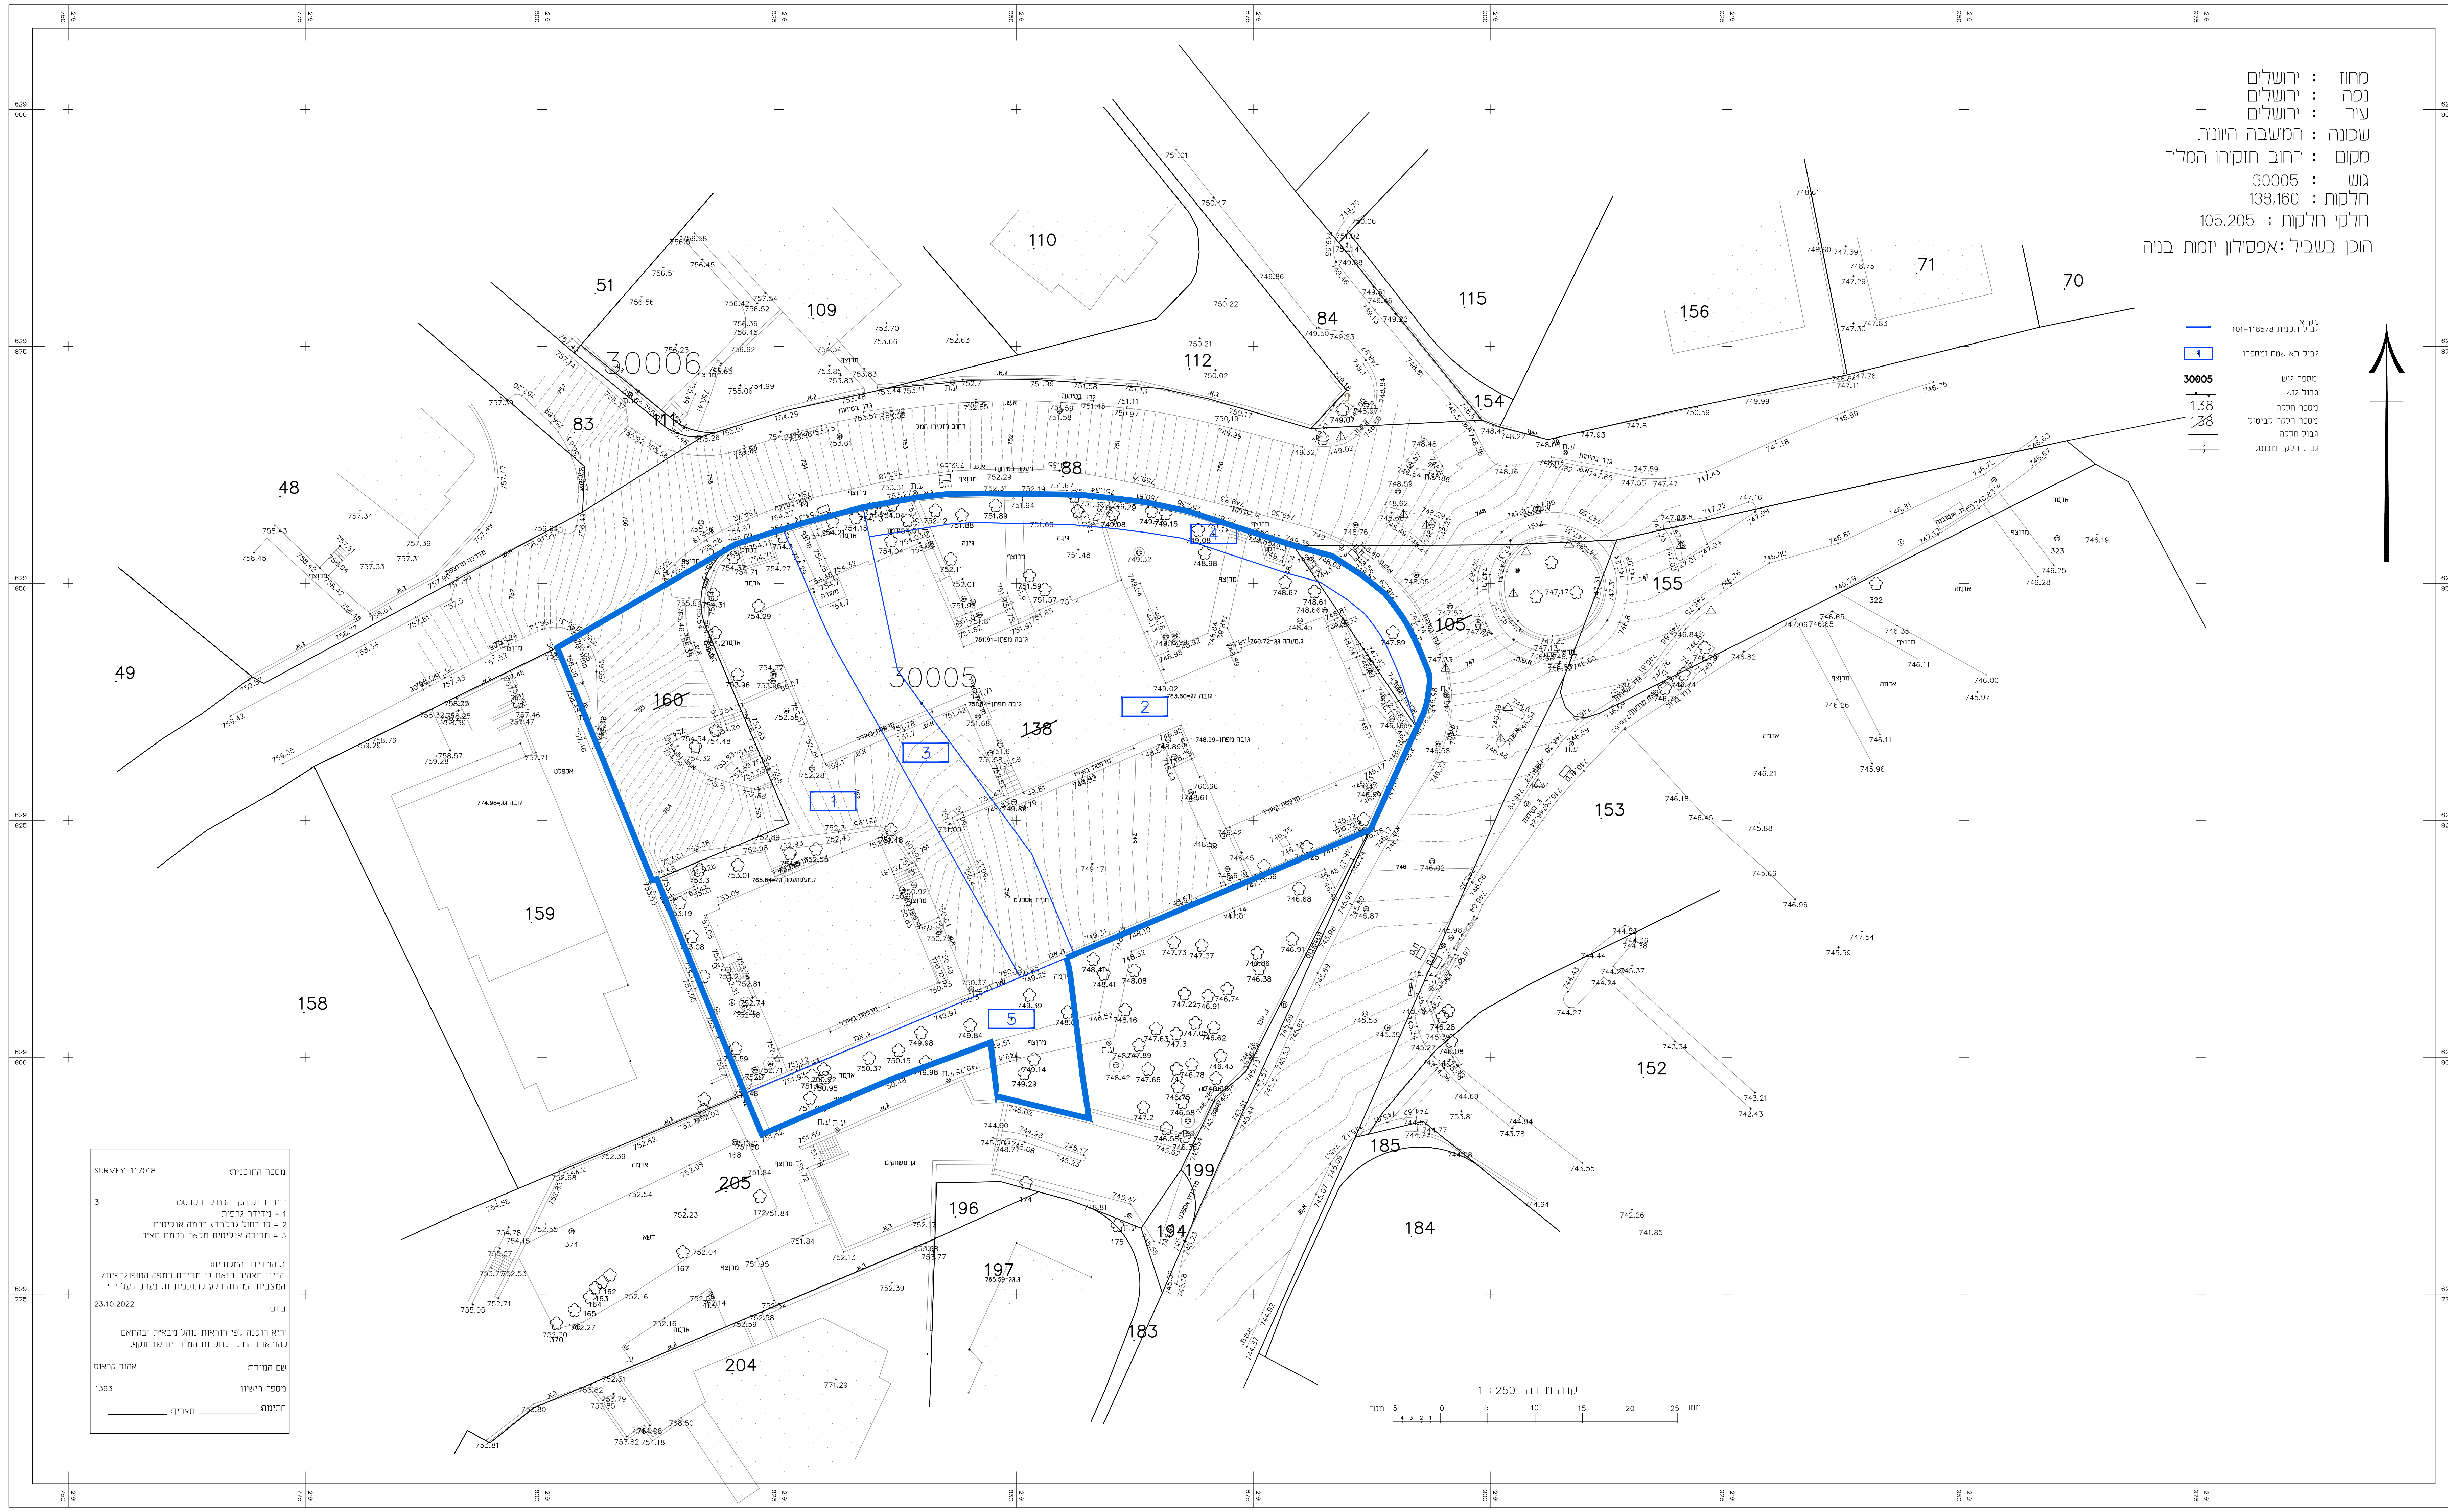

מחוז : ירושלים
נפה : ירושלים
עיר : ירושלים
שכונה : המושבה היוונית
מקום : רחוב חזקיהו המלך
גוש : 30005
חלקות : 138,160
חלקי חלקות : 105,205
הוכן בשביל: אפסילון יזמות בניה

מקרא
גבול תכנית 101-118578
גבול תא שטח ומספרו
מספר גוש 30005
גבול גוש
מספר חלקה 138
מספר חלקה לביטול 138
גבול חלקה
גבול חלקה מבוטל

מספר התוכנית: SURVEY_117018

רמת דיוק הקו הכחול והקדסטר: 3
1 = מדידה גרפית
2 = קו כחול (בלבד) ברמה אנליטית
3 = מדידה אנליטית מלאה ברמת תצ"ר

1. המדידה המקורית:
הריני מצהיר בזאת כי מדידת המפה הטופוגרפית/המצבית המהווה רקע לתוכנית זו, נערכה על ידי :
ביום: 23.10.2022
והיא הוכנה לפי הוראות נוהל מבא"ת ובהתאם להוראות החוק ולתקנות המודדים שבתוקף.
שם המודד: אהוד קראוס
מספר רישיון: 1363
חתימה: ________ תאריך: ________

קנה מידה 1 : 250

חוק התכנון והבנייה, התשכ"ה – 1965
תכנית מתאר מקומית

מס' 101-1185578

התחדשות עירונית ברחוב חזקיהו המלך 39-45

נספח איחוד וחלוקה

איחוד וחלוקה	סמכות ראשית	אופי התכנית
בהסכמת כל הבעלים	ועדה מחוזית	תכנית שניתן מכוחה להוציא היתרים או הרשאות

מחוז: ירושלים
מרחב תכנון מקומי: ירושלים
רשות מקומית: ירושלים

שטח התכנית: 4.040 ד'
קנה מידה: 1:250

חותמת מוסד התכנון:

שלב: הגשה מהדורה: 1 תאריך: 10.12.25

הריני מצהיר בזאת כי המפה הטופוגרפית/המצבית המהווה רקע לתכנית זו, נערכה על ידי ביו 21.2.23 והיא הוכנה לפי הוראות נוהל מבא"ת ובהתאם להוראות החוק ולתקנות המודדים שבתוקף. דיוק הקו הכחול והקדסטר:
מדידה אנליטית מלאה ברמת תצ"ר

שם המודד	מספר רשיון	חתימה	תאריך
אהוד קראוס	1363		