מינהל התכנון
חוק התכנון והבניה, התשכ"ה - 1965
מחוז ירושלים
הוועדה המחוזית החליטה ביום :
10/02/2025
להפקיד את התכנית
09/08/2026
יו"ר הוועדה המחוזית תאריך

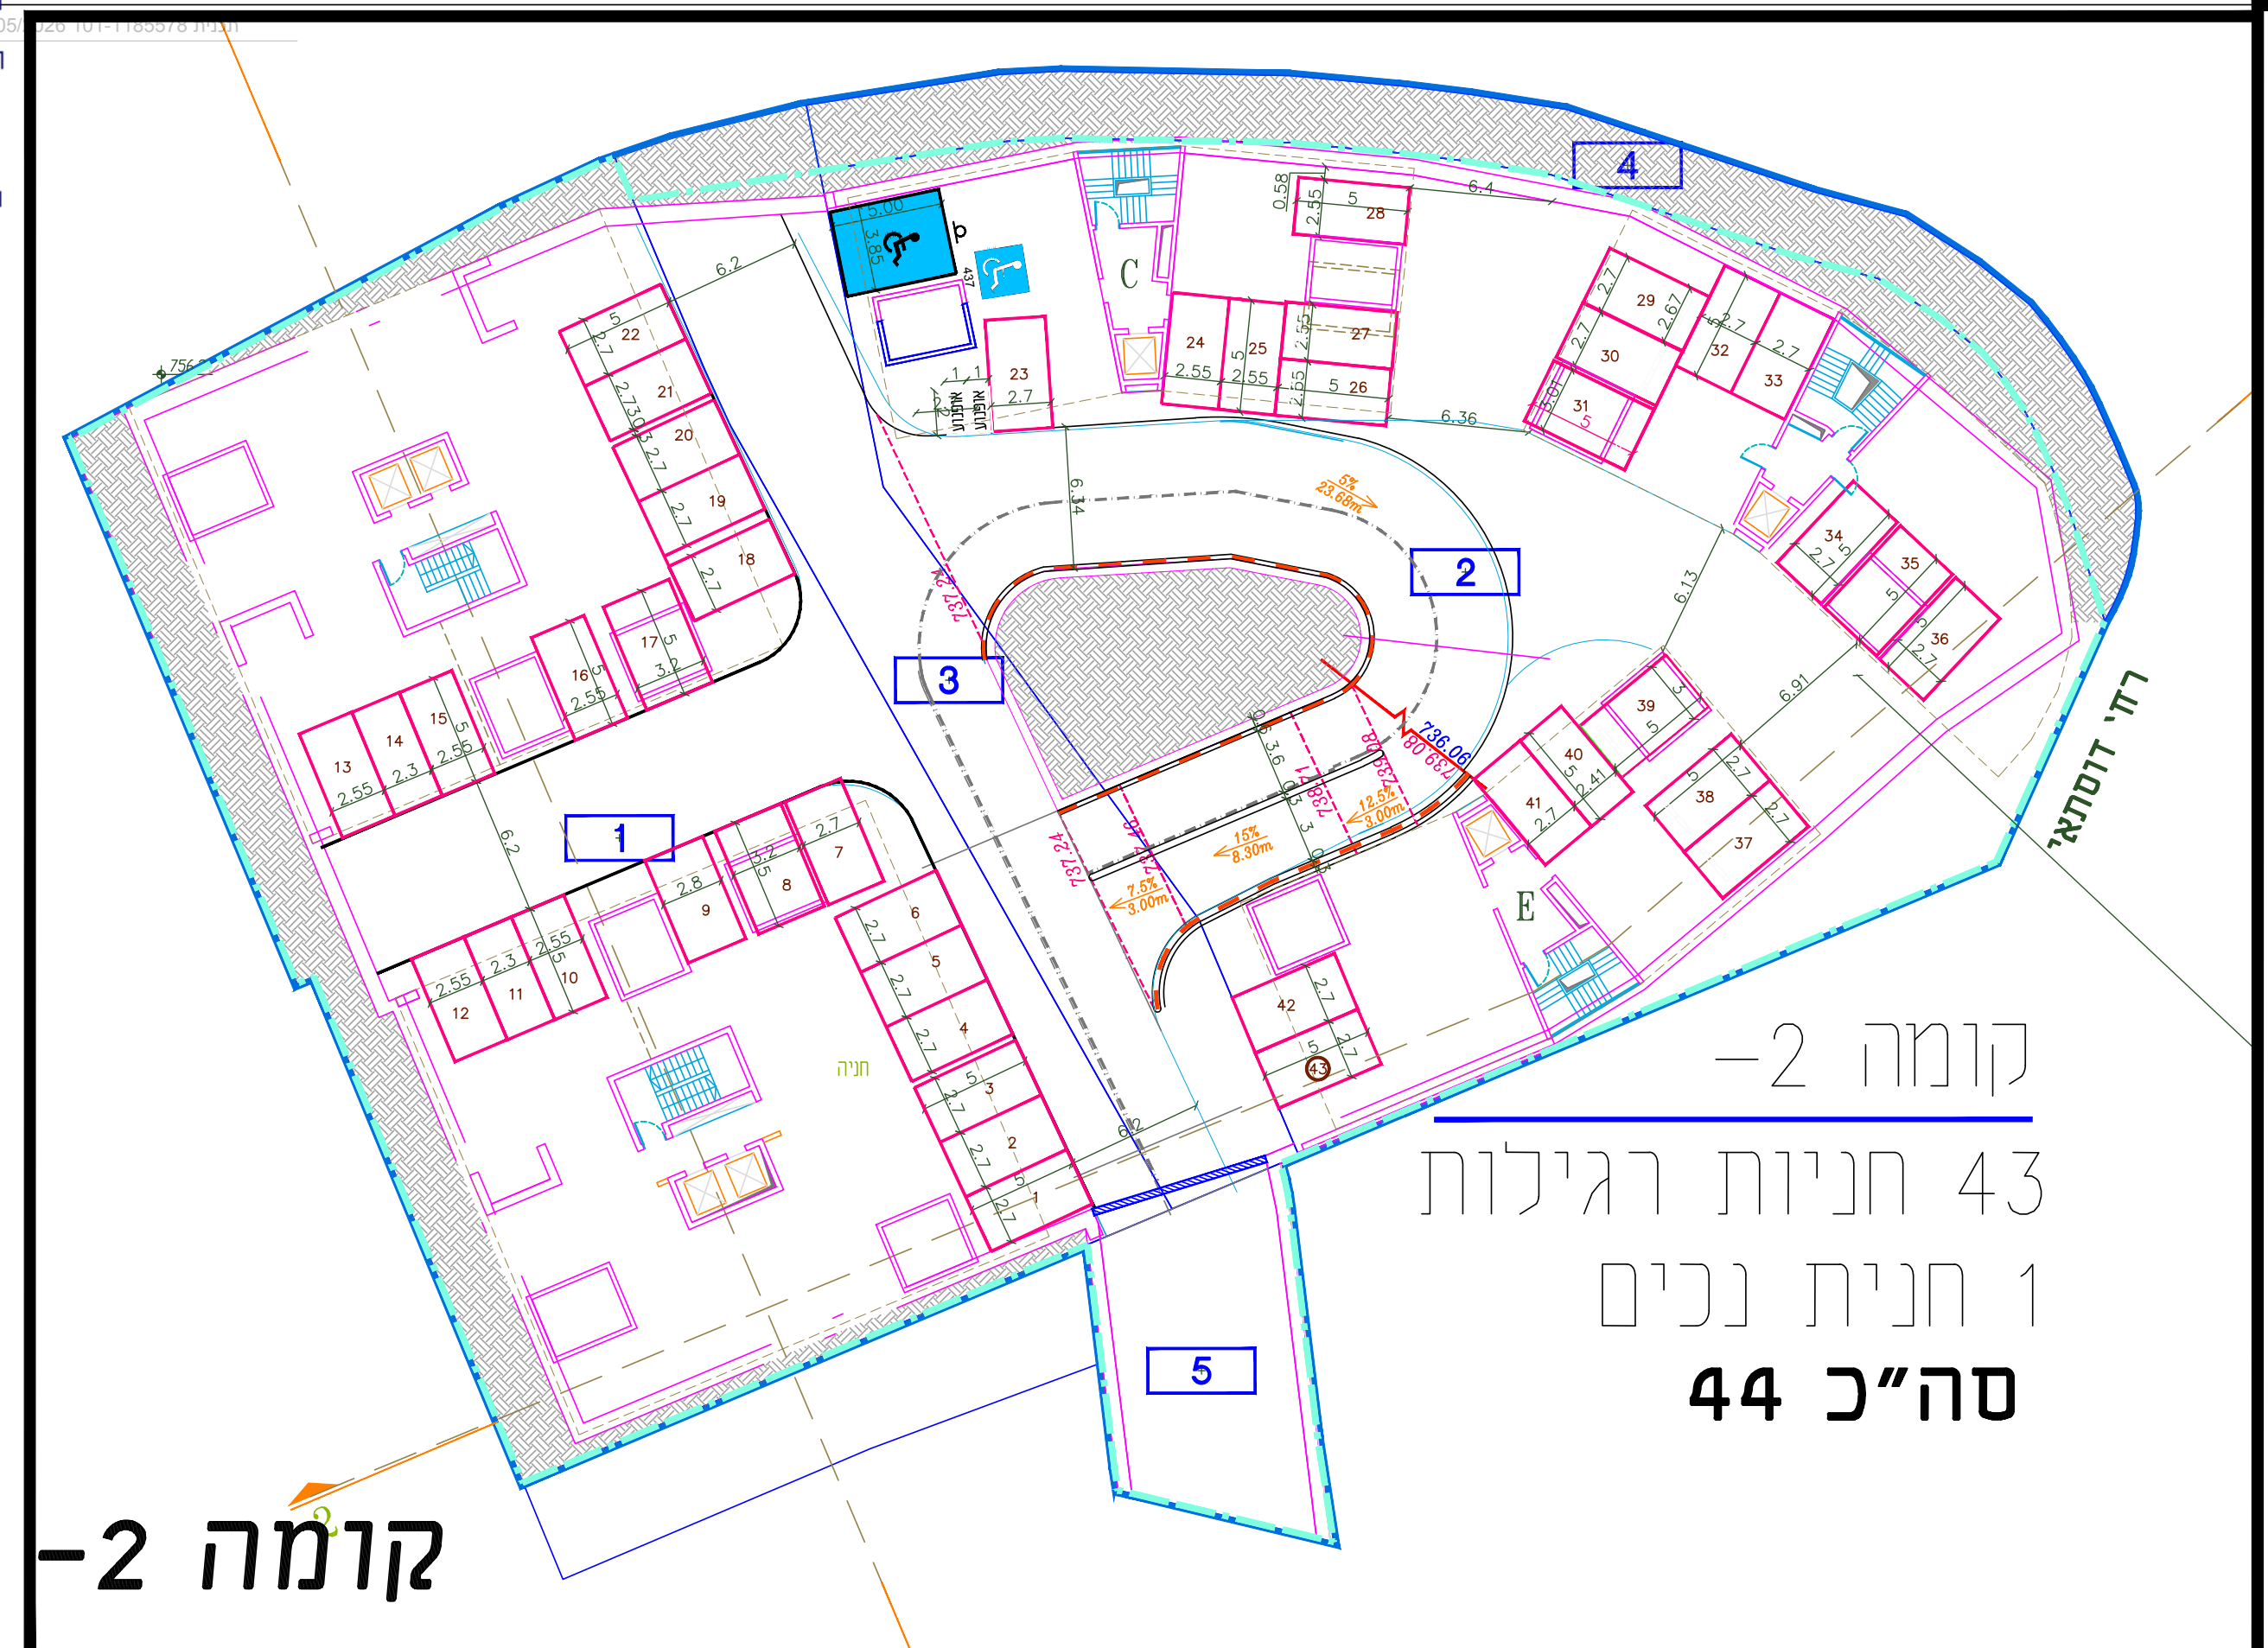

קומה -2

קומה -2
43 חניות רגילות
1 חנית נכים
סה"כ 44

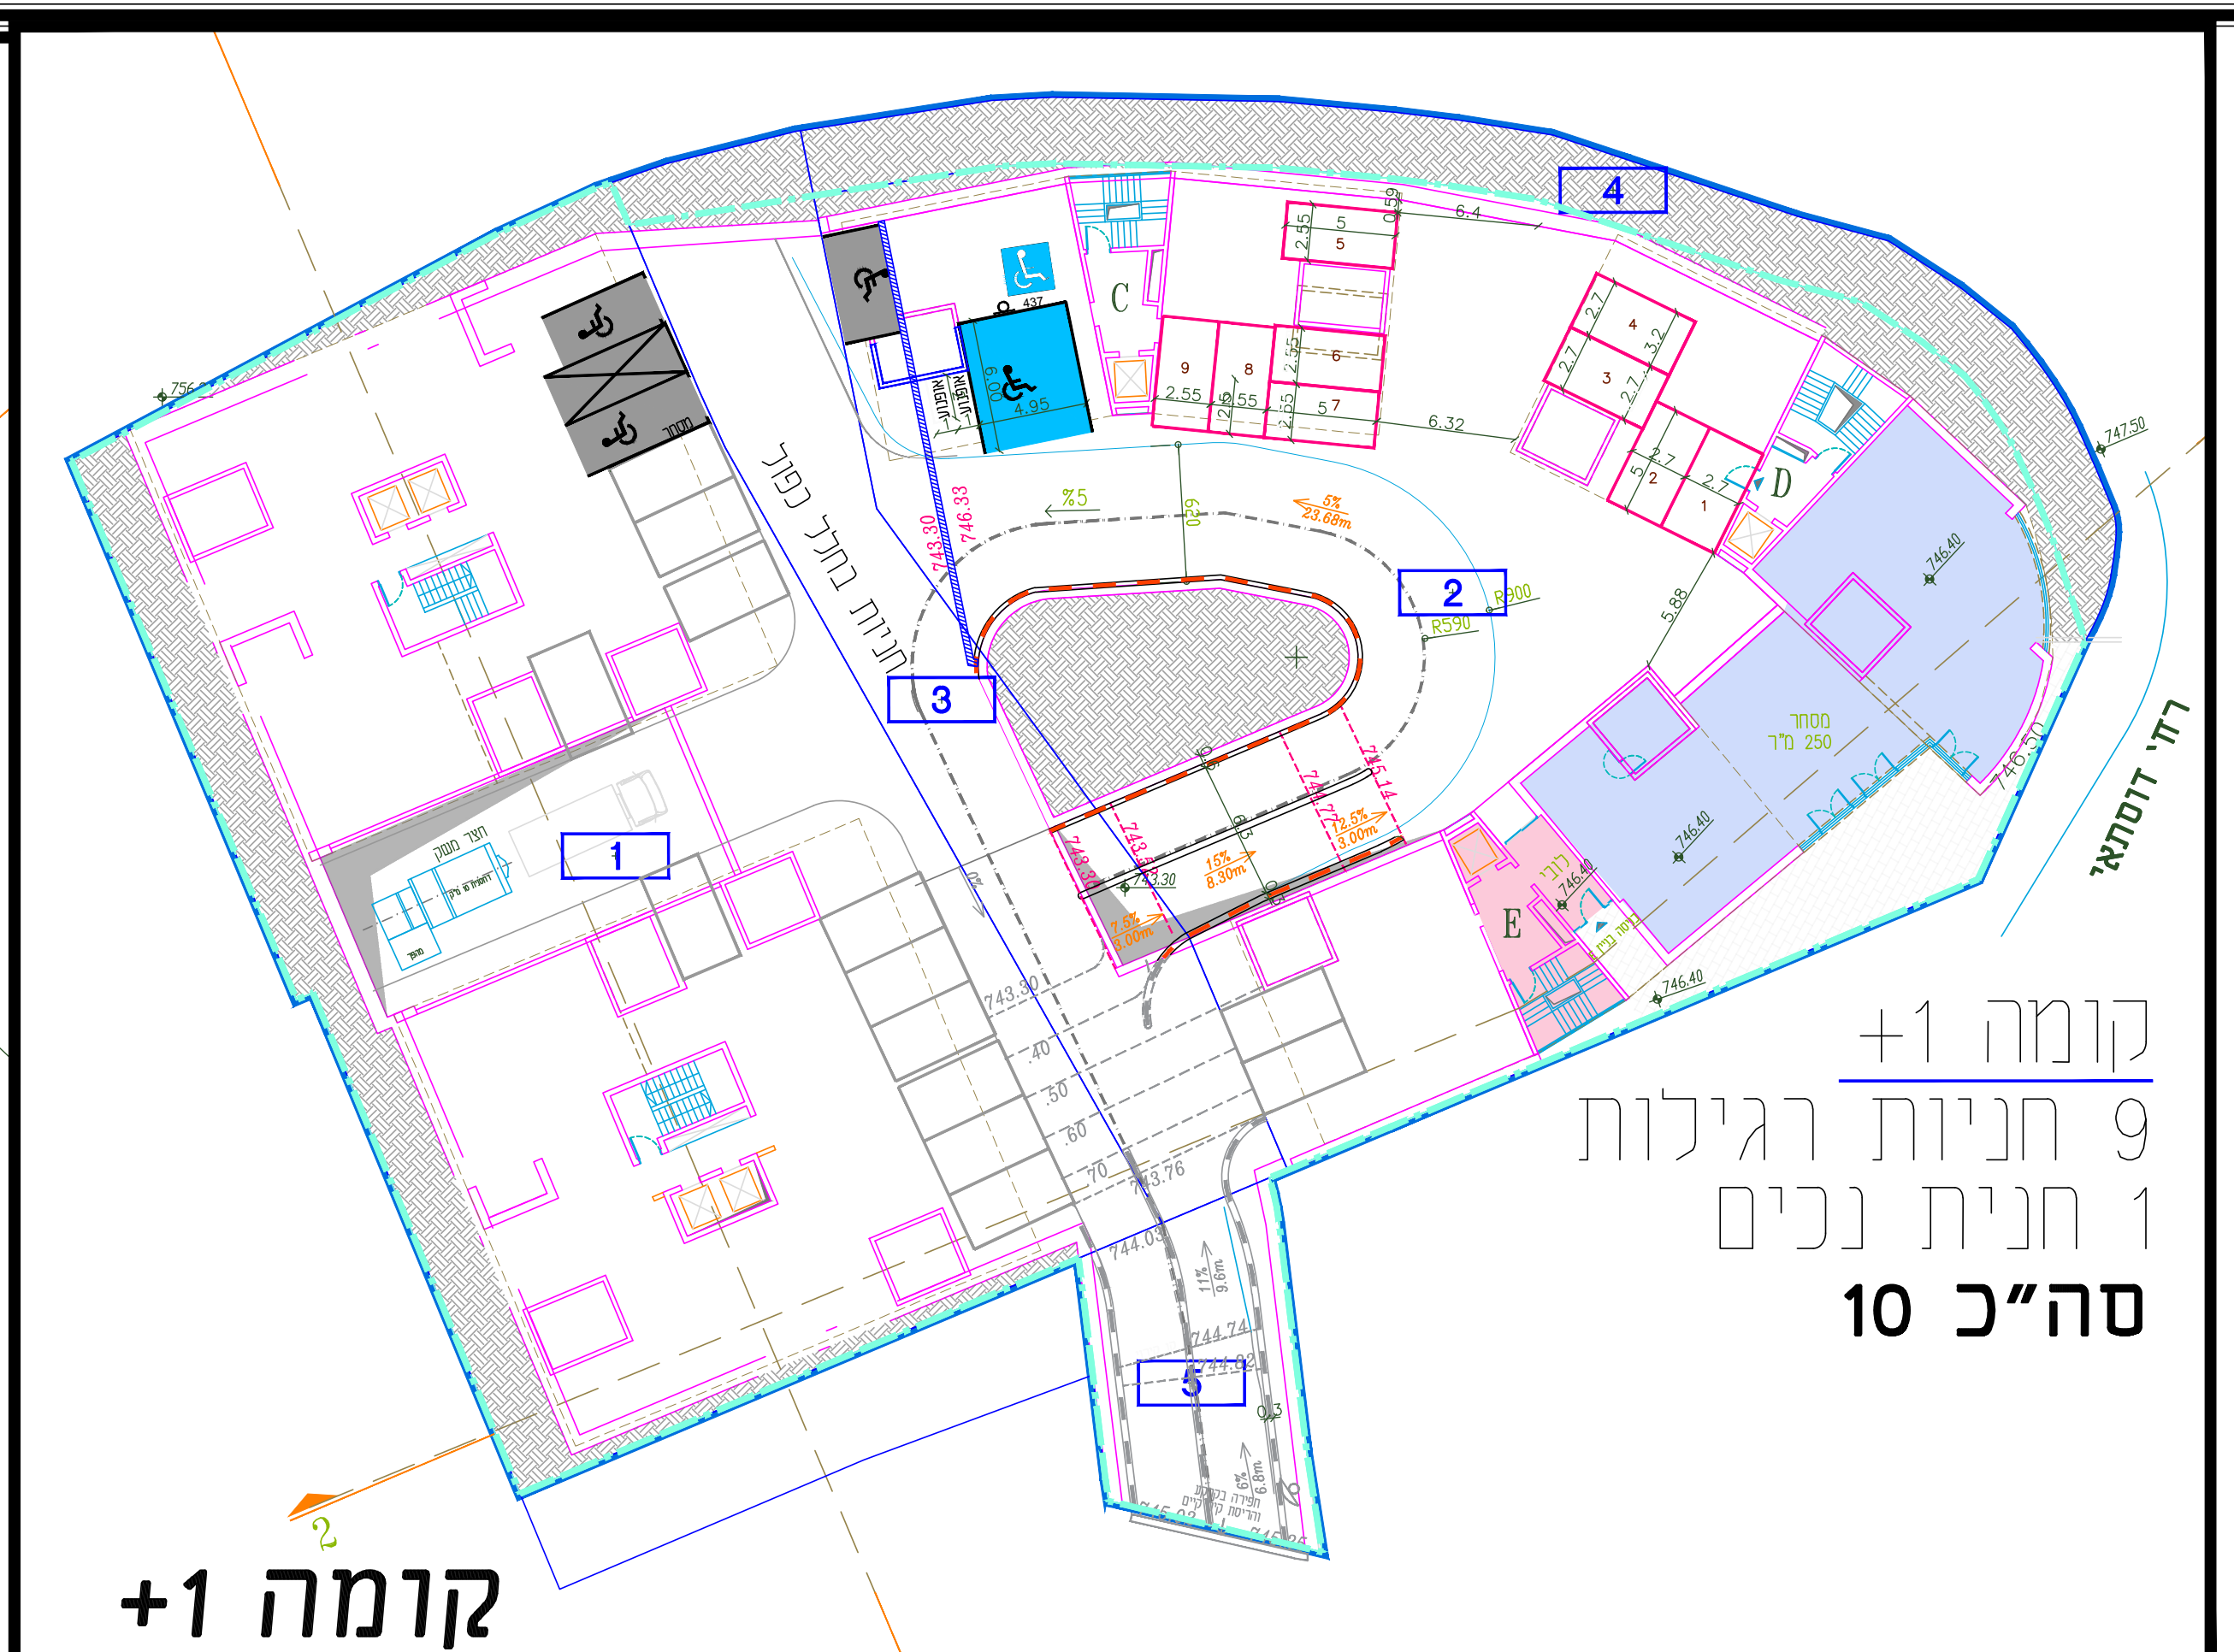

קומה +1

קומה +1
9 חניות רגילות
1 חנית נכים
סה"כ 10

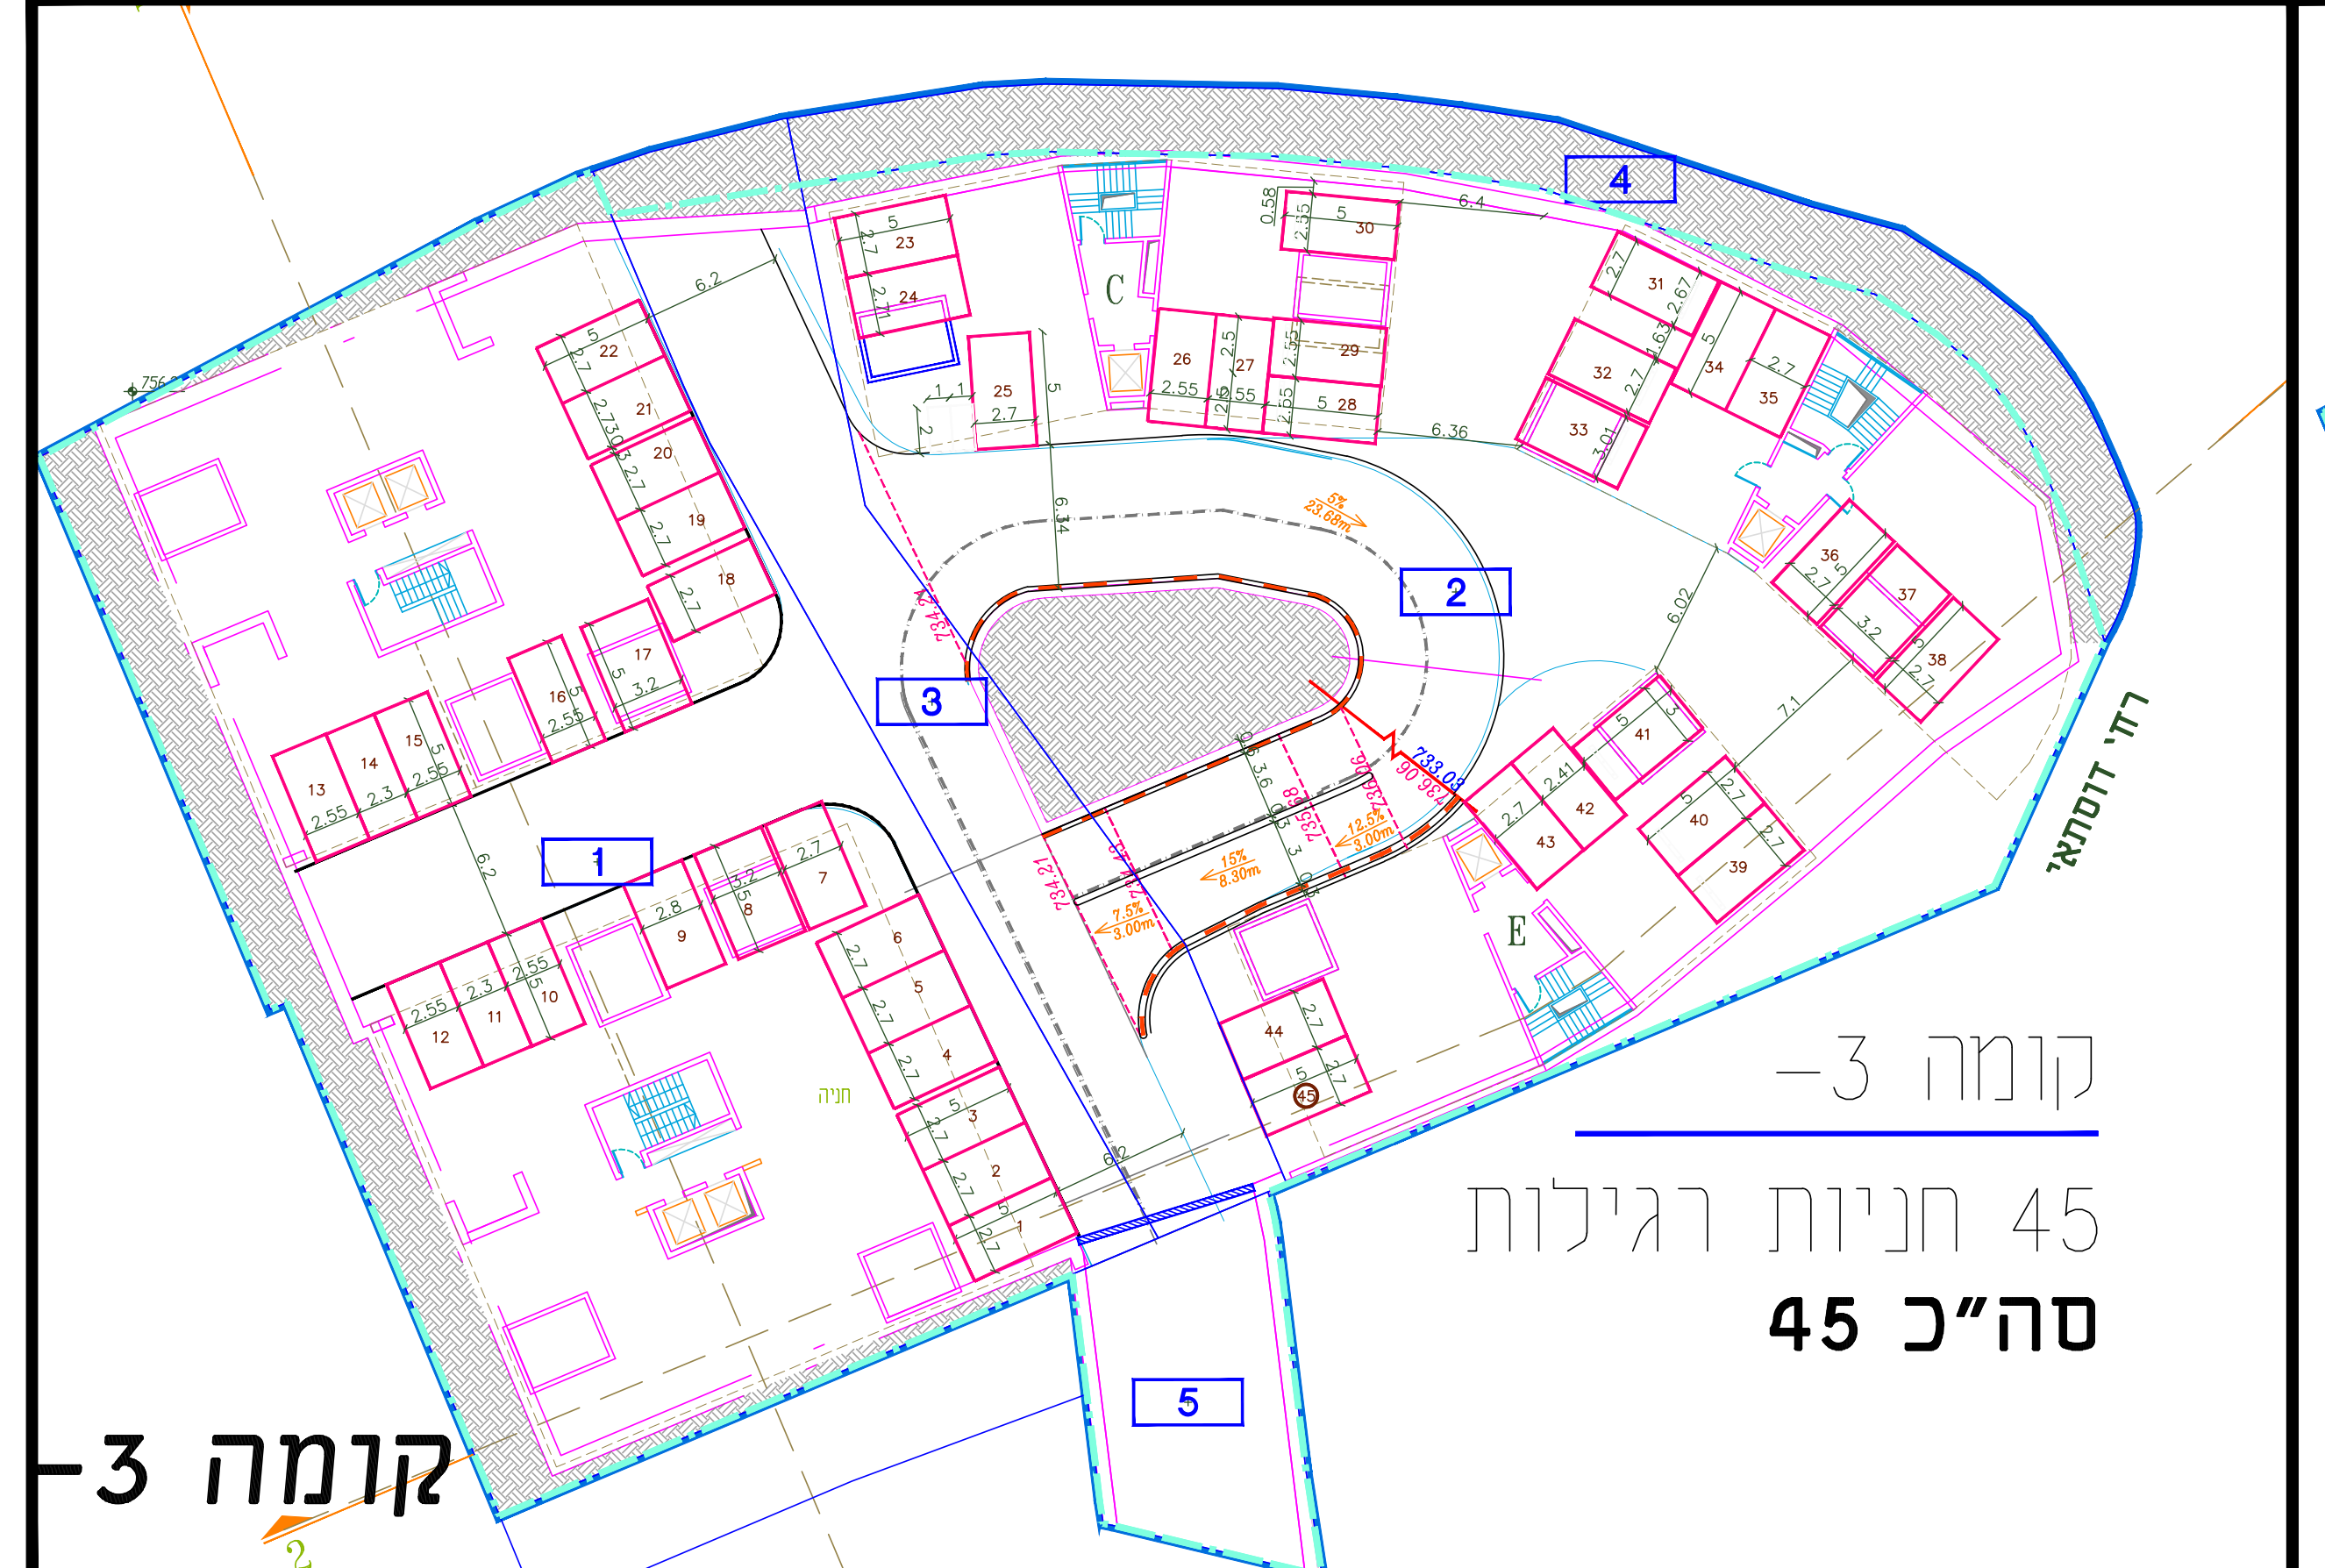

קומה -3

קומה -3
45 חניות רגילות
סה"כ 45

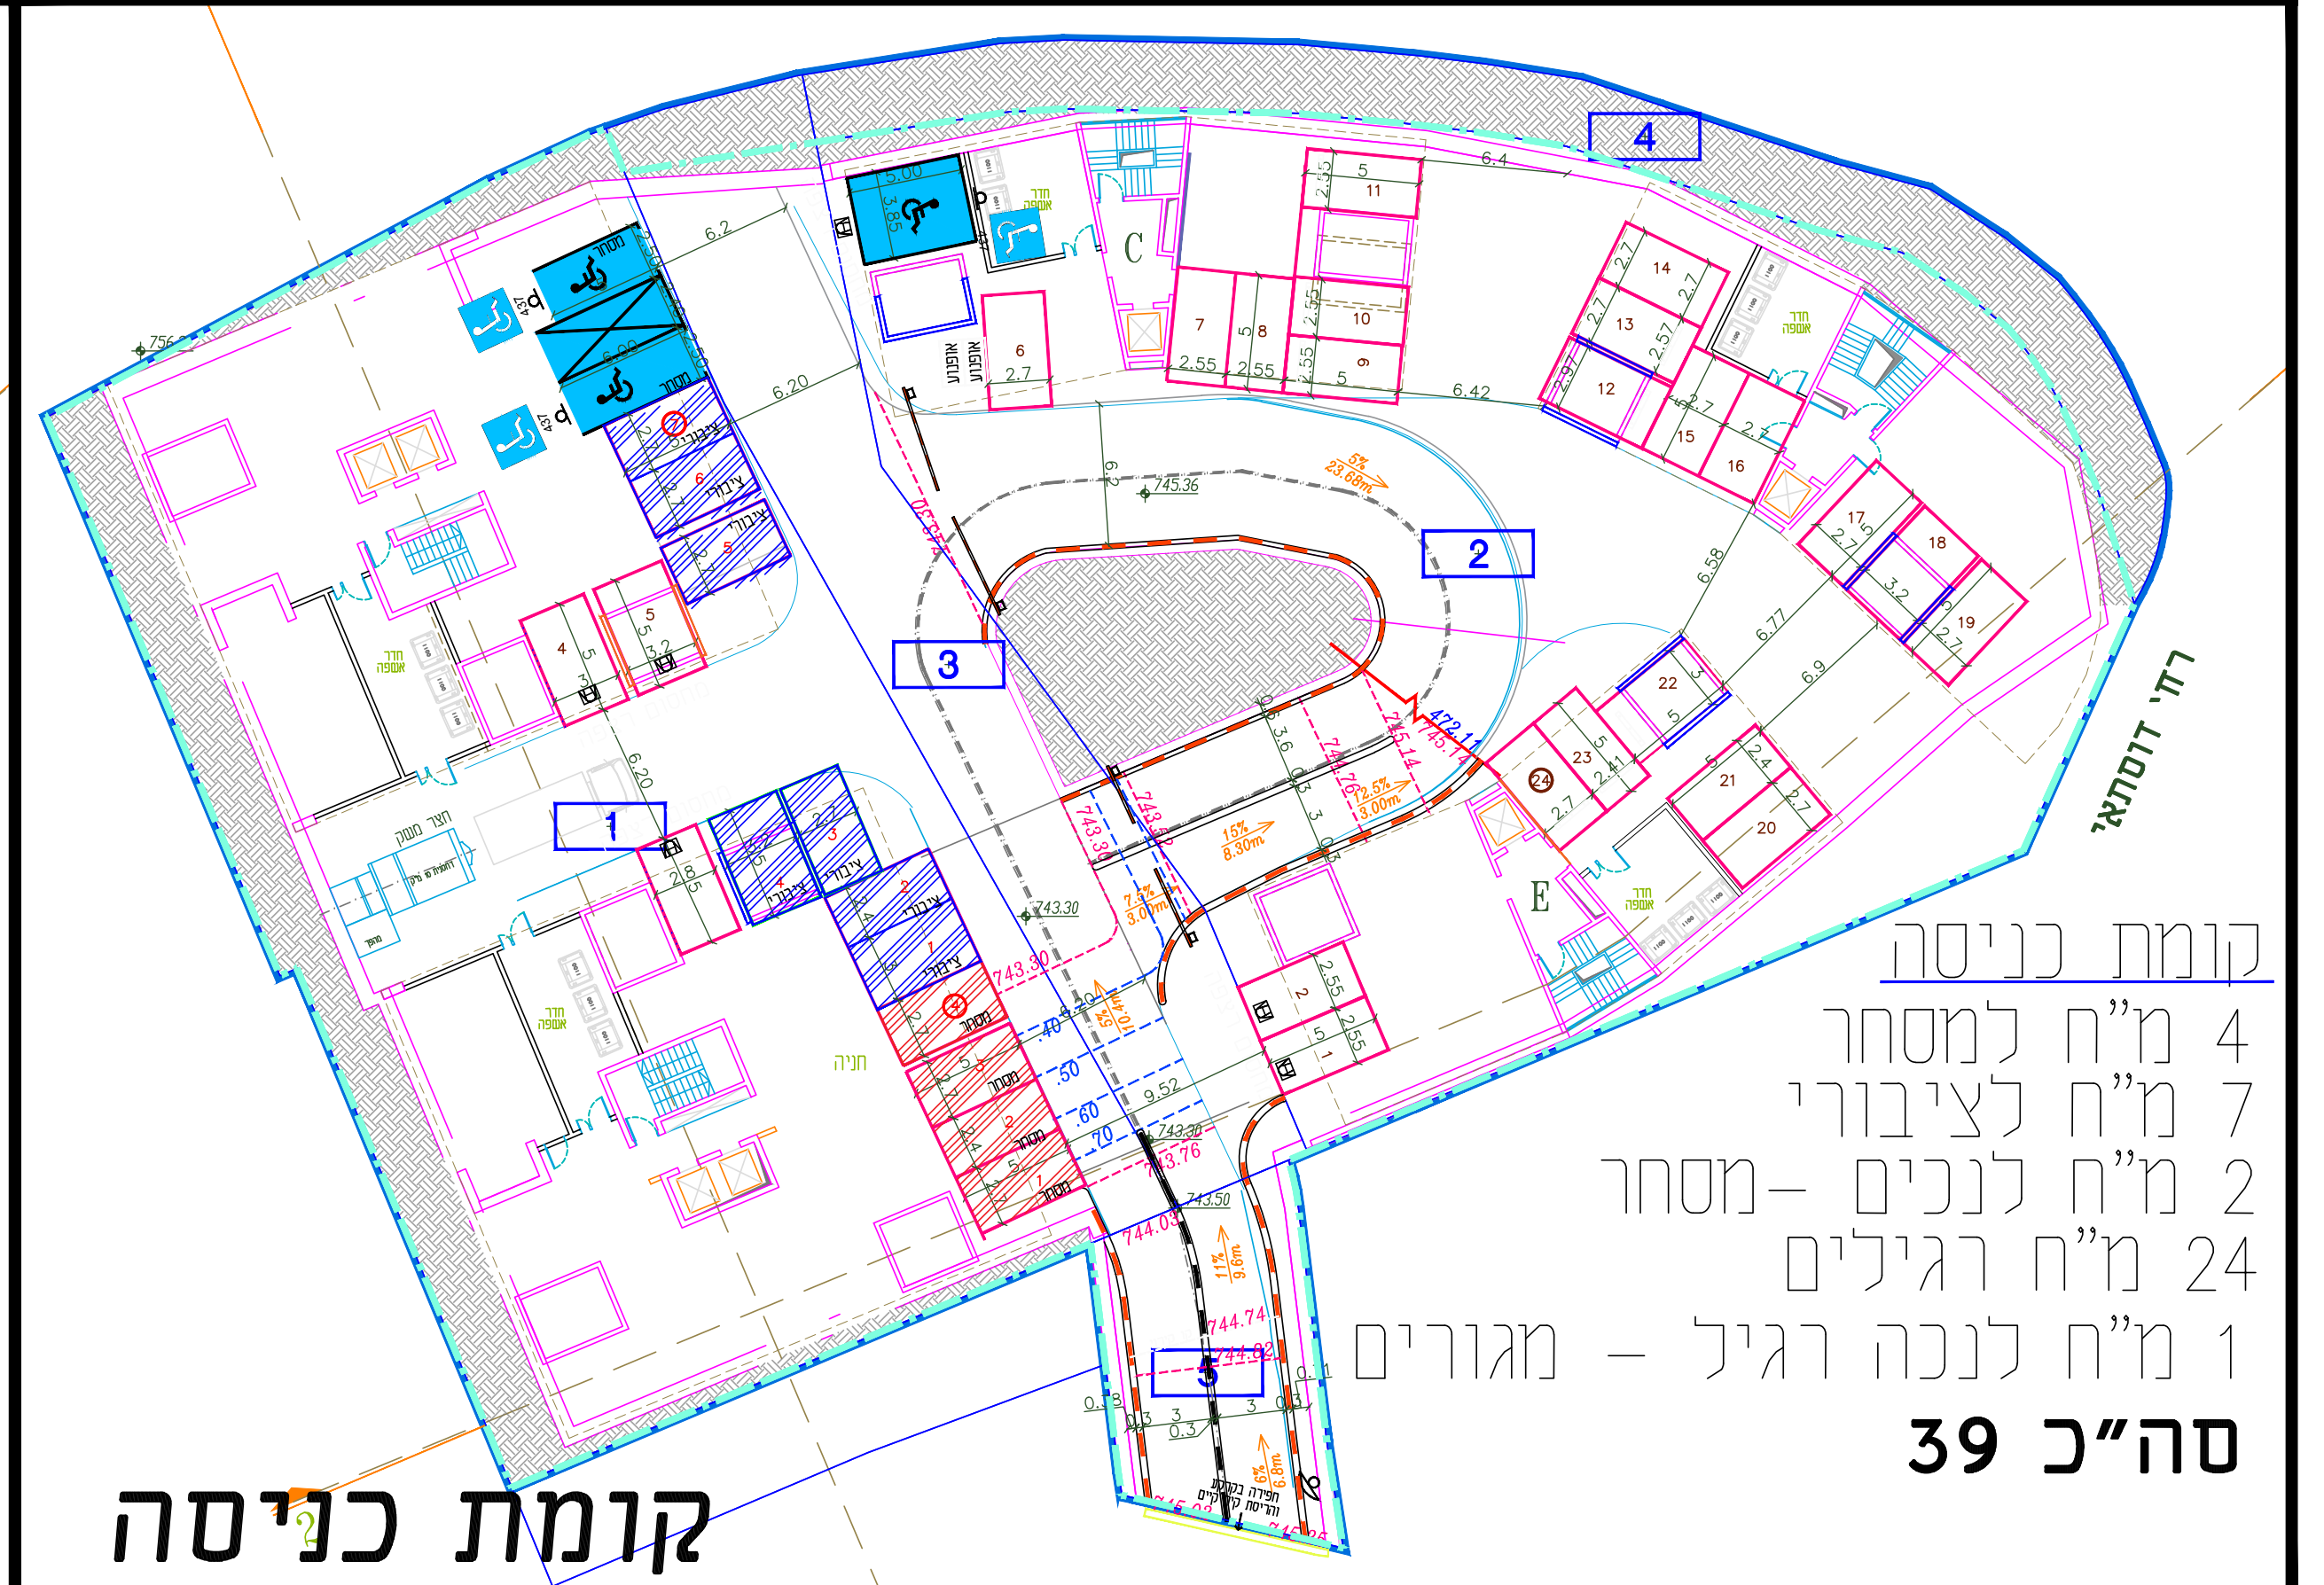

קומת כניסה

קומת כניסה
4 מ"ח למסחר
7 מ"ח לציבורי
2 מ"ח לנכים -מסחר
24 מ"ח רגילים
1 מ"ח לנכה רגיל - מגורים
סה"כ 39

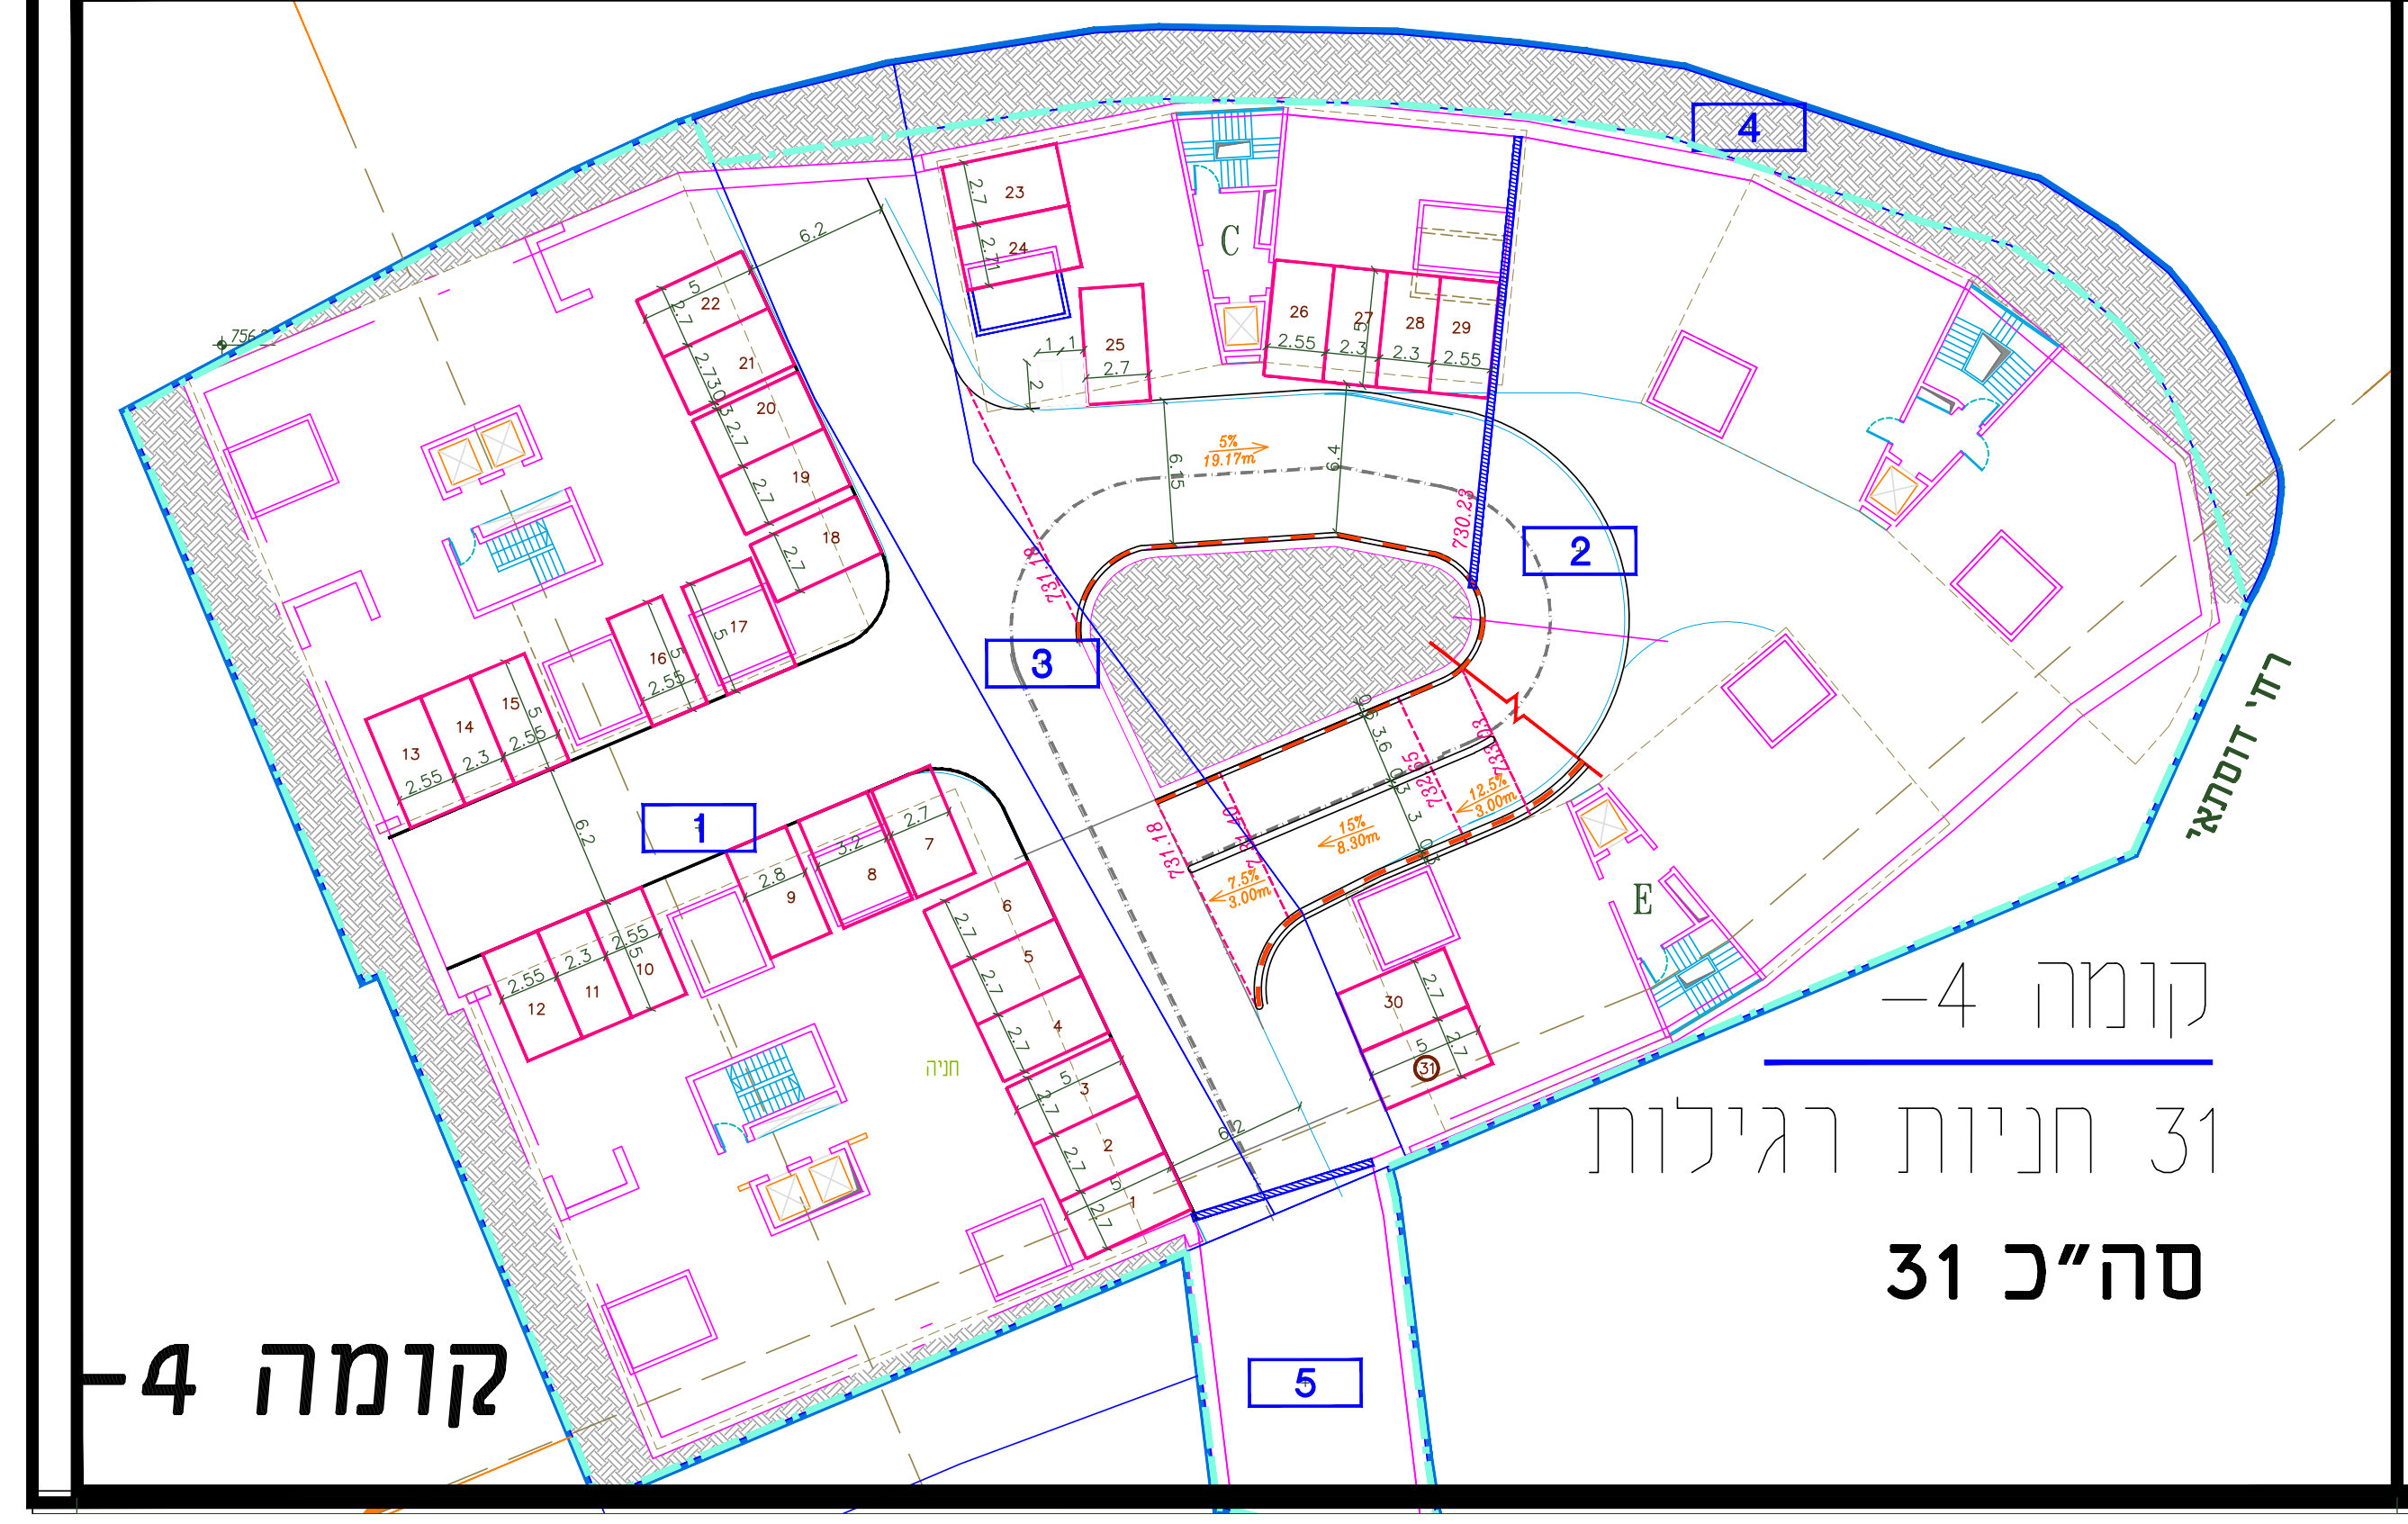

קומה -4

קומה -4
31 חניות רגילות
סה"כ 31

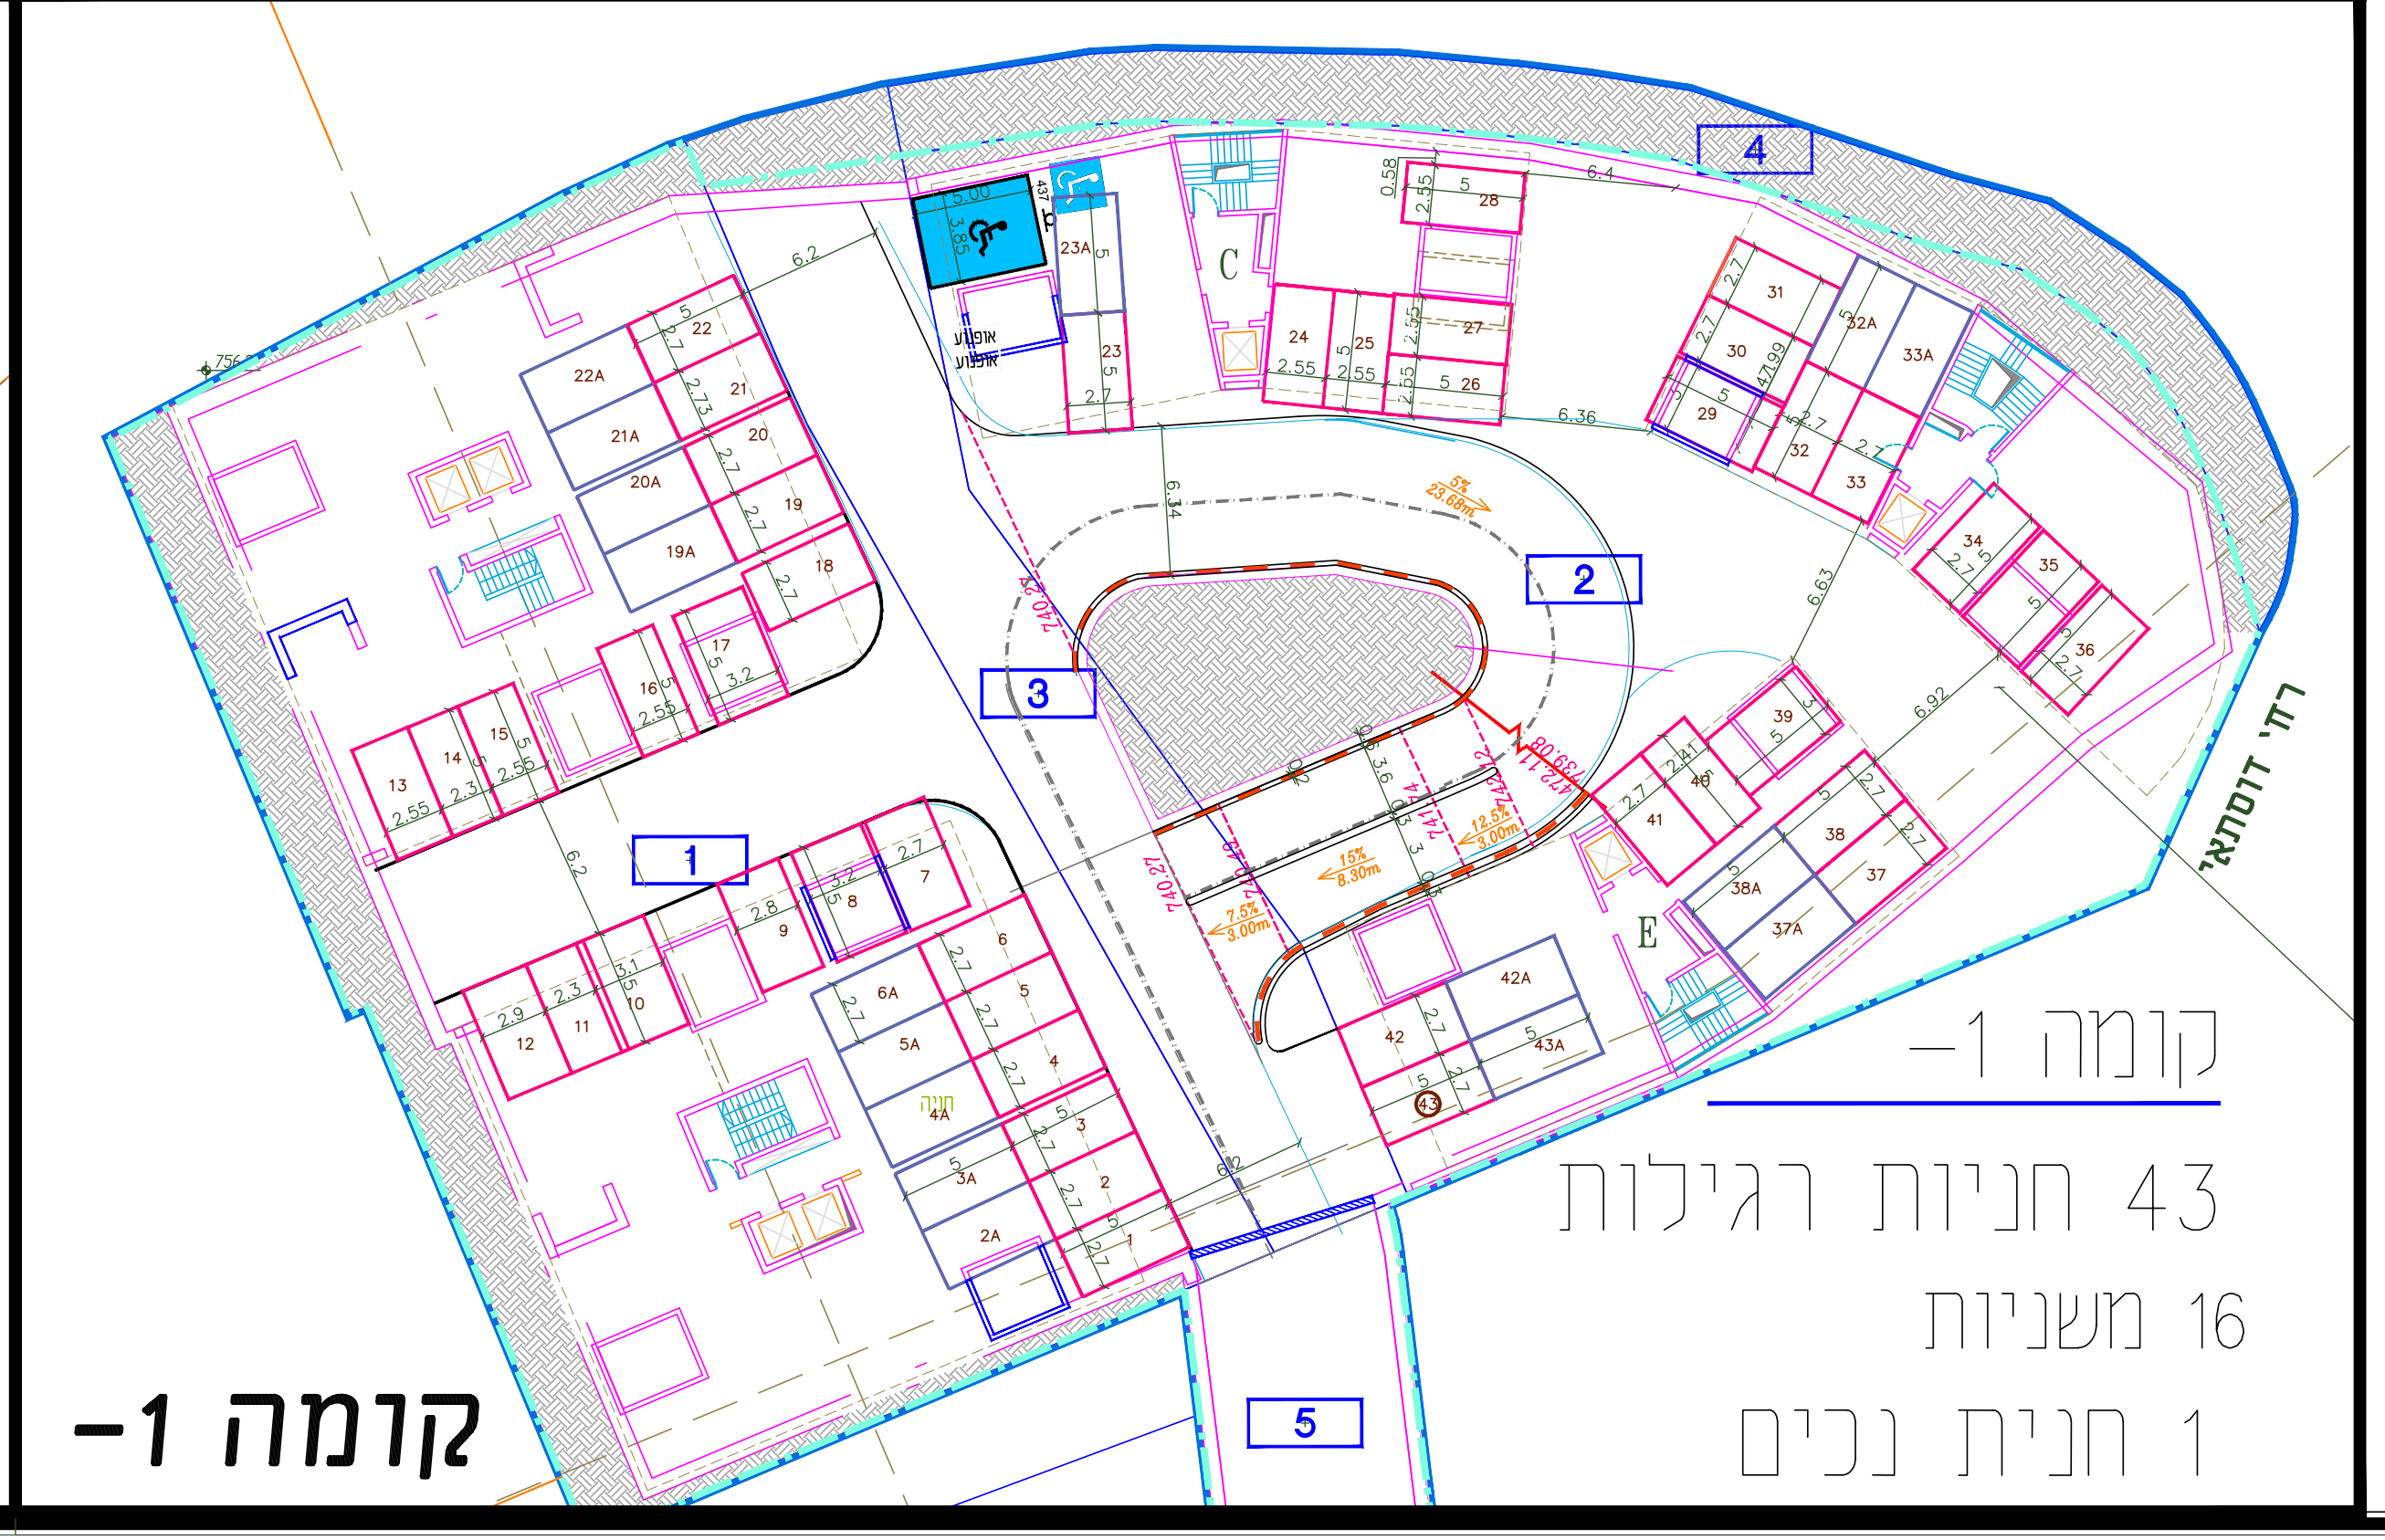

קומה -1

קומה -1
43 חניות רגילות
16 משניות
1 חנית נכים

קומת קרקע

תרשים סביבה ללא קנ"מ
מרחק מתחנת רק"ל

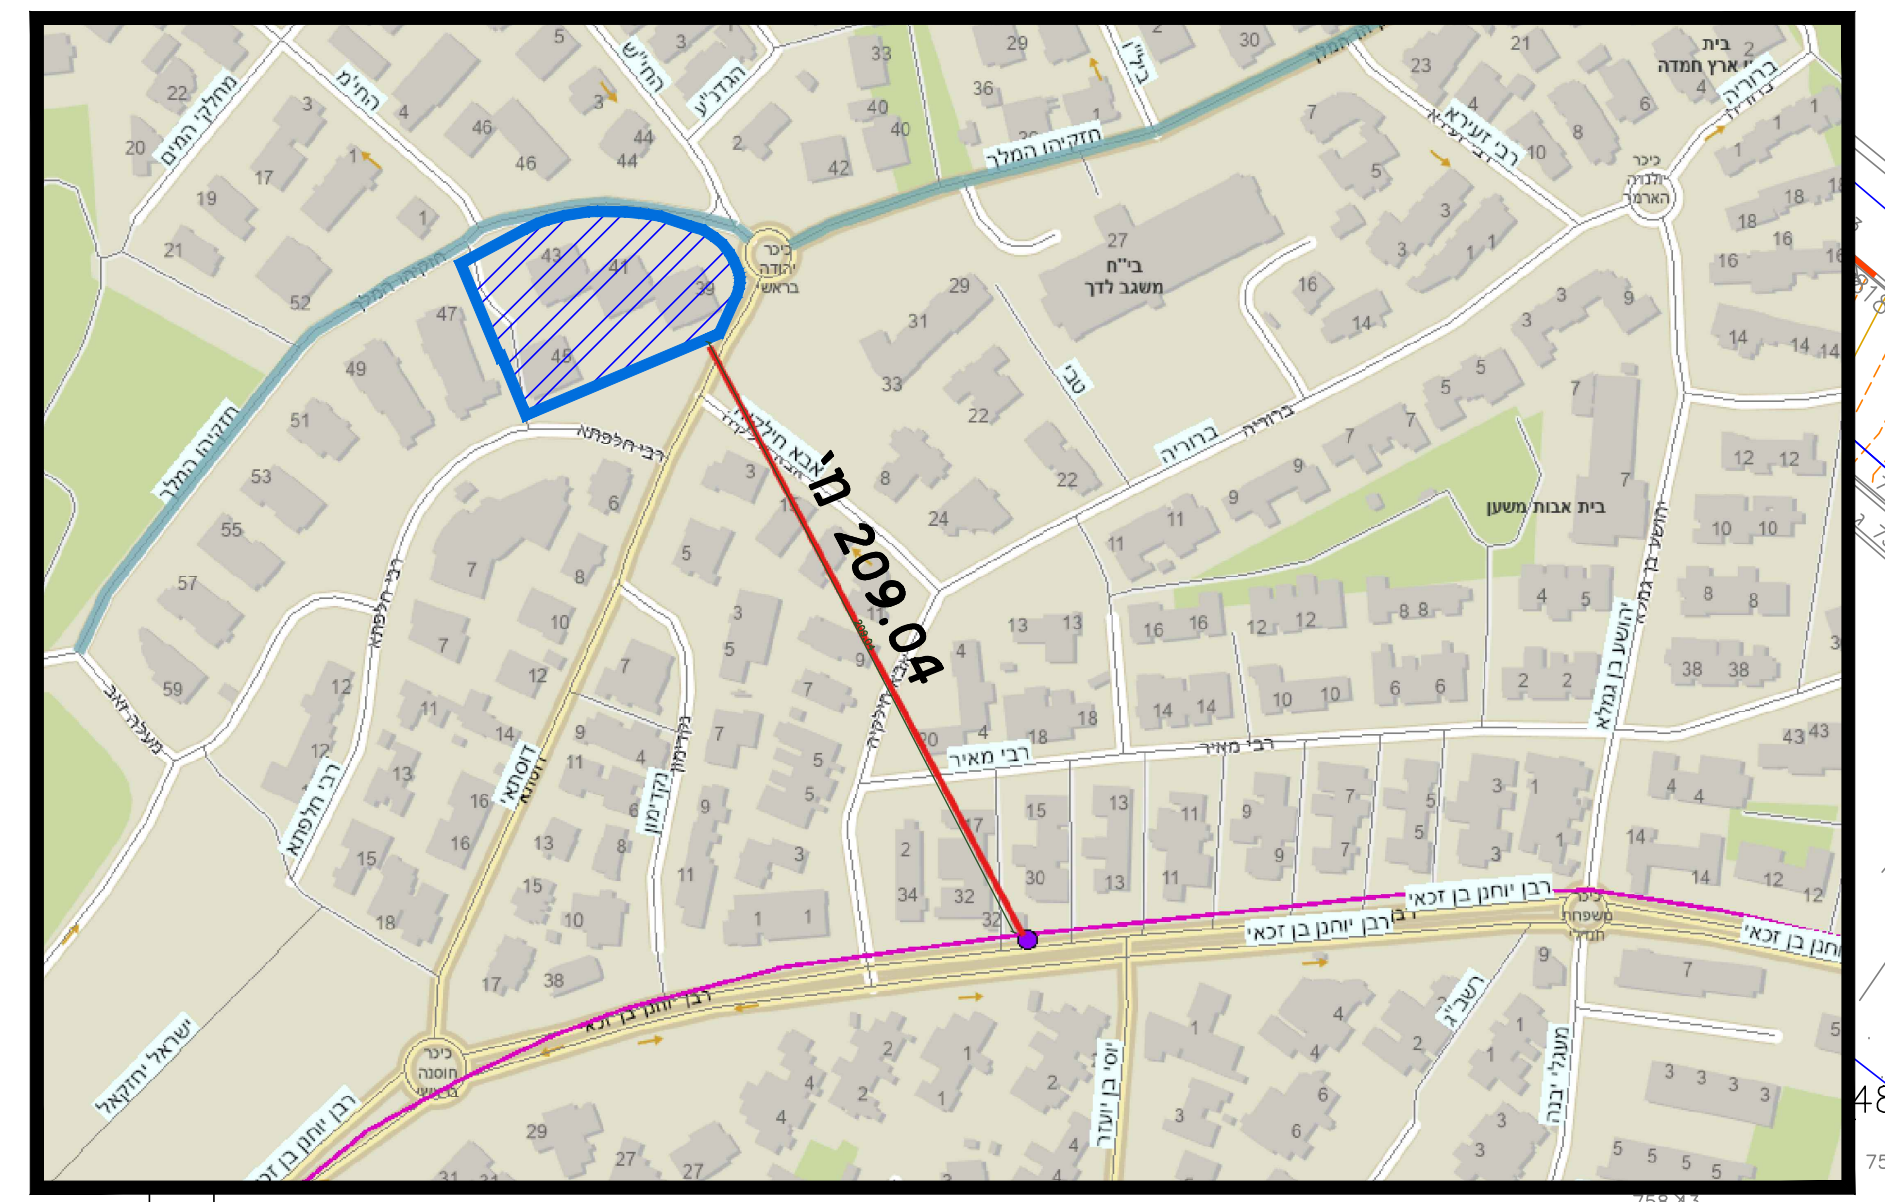

תמרון משאית אשפה

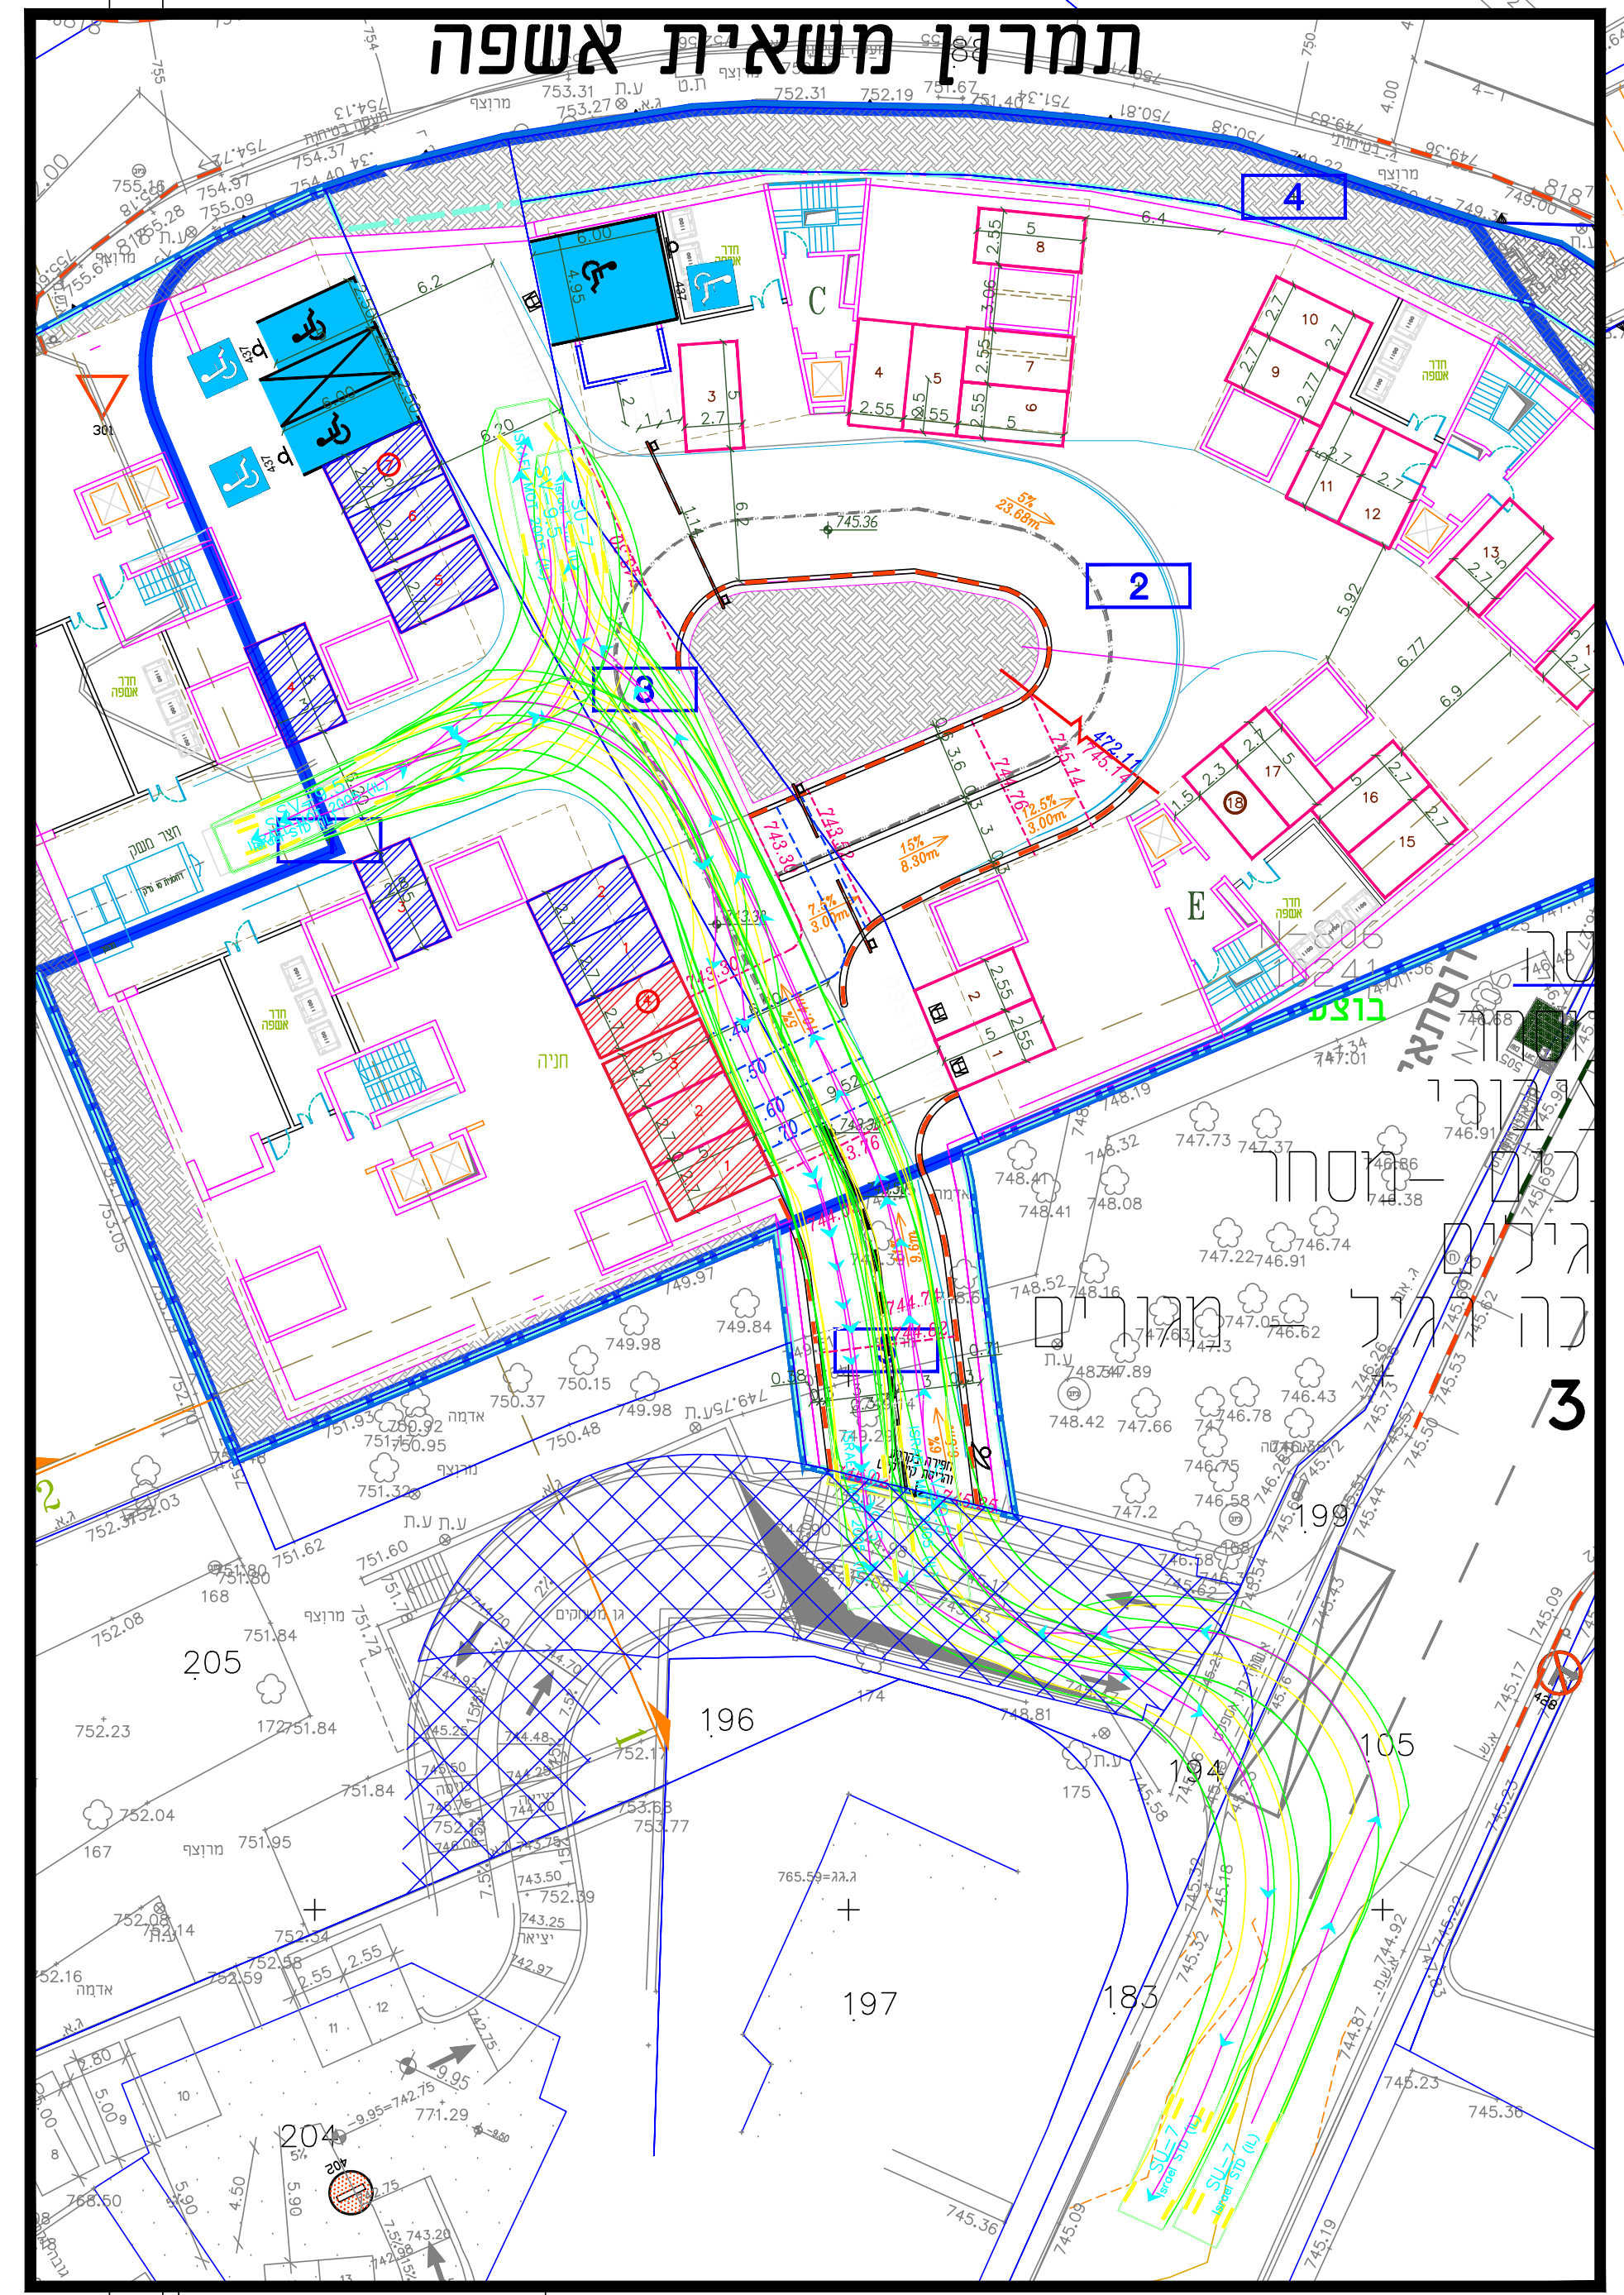

חניון מגרש שכן- 56 חניות

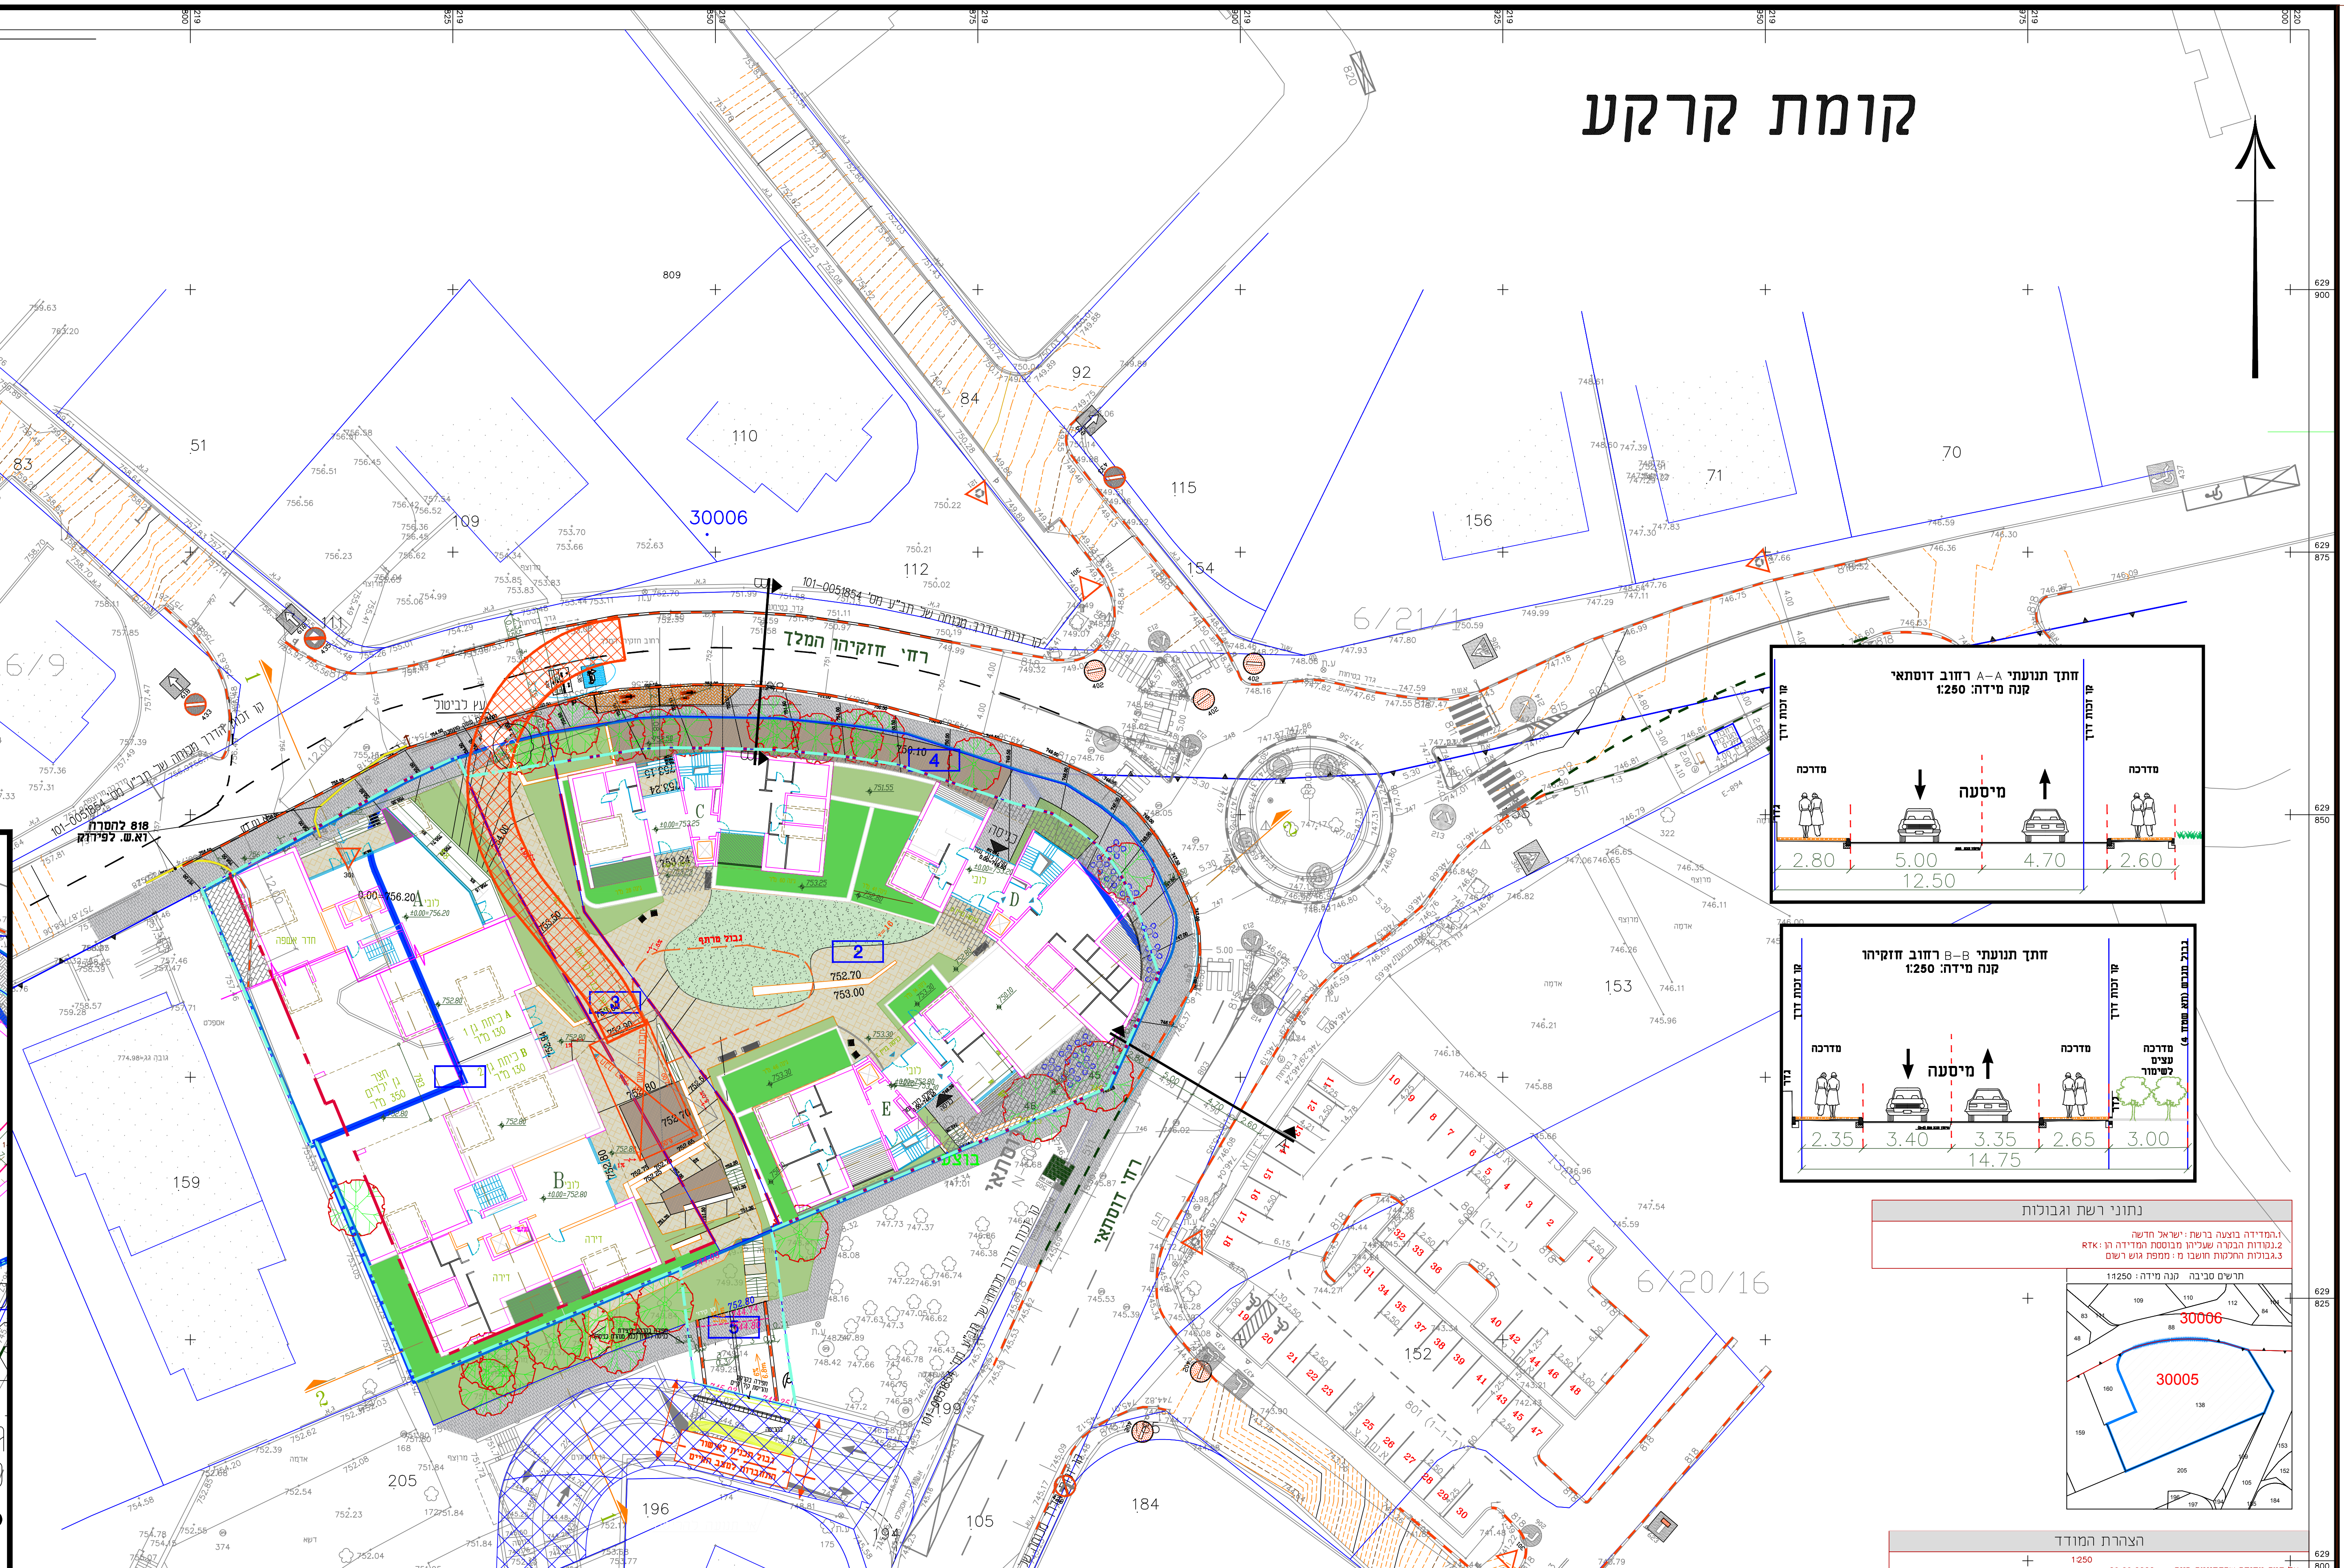

נתוני רשת וגבולות

1.המדידה בוצעה ברשת: ישראל חדשה
2.נקודות הבקרה שעליהן מבוססת המדידה הן: RTK
3.גבולות החלקות חושבו מ: ממפת גוש רשום

הצהרת המודד

1:250
על סמך מדידה שהסתיימה ביום: 29.09.2022

חזקיהו המלך 39-45 -תב"ע 101-1185578

טבלת מאזן חניה - ע"פ תקן ירושלים 5166ב' (אזור תקן גובה)

המגרש נמצא במרחק כ-240 מ' מקו הרכבת הקלה.

26.03.2026

יעוד	שטח	פרטי תקן	דרוש	דרוש נכים	מתוכנן נכים	סה"כ דרוש	אופניים תקן:	דרוש:	מתוכנן	אופנועים מינימום תקן:	דרוש:	מקסימום תקן:	דרוש:	מתוכנן
מגורים	139 יח"ד עד 95 מ"ר	1:1	139	2 רגיל 2 גבוה	2 רגיל 2 גבוה	208 + 4 נכים	1:1	170	170	1:10	17	1:5	34	24
	21 יח"ד מ 95 מ"ר עד 120 מ"ר	1.5:1	32 (31.5)											
	10 יח"ד גדולות מ 120 מ"ר	2:1	20											
אורחים	170 יח"ד	10% מיח"ד	17											
סה"כ מגורים	170 יח"ד		208	4	4	212								
כיתת גן	260 מ"ר	1:40 + נשק וסע	7 (6.5)	1 גבוה	1 גבוה	15 + 2 נכים	—	—		—	—	—	—	—
מסחר	195 מ"ר	1:25	8 (7.8)	1 רגיל	1 רגיל		—					1:200	2	2
סה"כ			223	6	6	229								
סה"כ כולל נכים						229								26

07.05.26

מרחב תכנון ירושלים

תכנית מס' 101-1185578

התחדשות עירונית חזקיהו המלך 39-45
קטמון הישנה, ירושלים

נספח תנועה וחניה

קנ"מ: 1:250

אלבוחר משה
office@albocher-eng.co.il